การประกอบเลขที่ ASSEMBLY NO. 3805

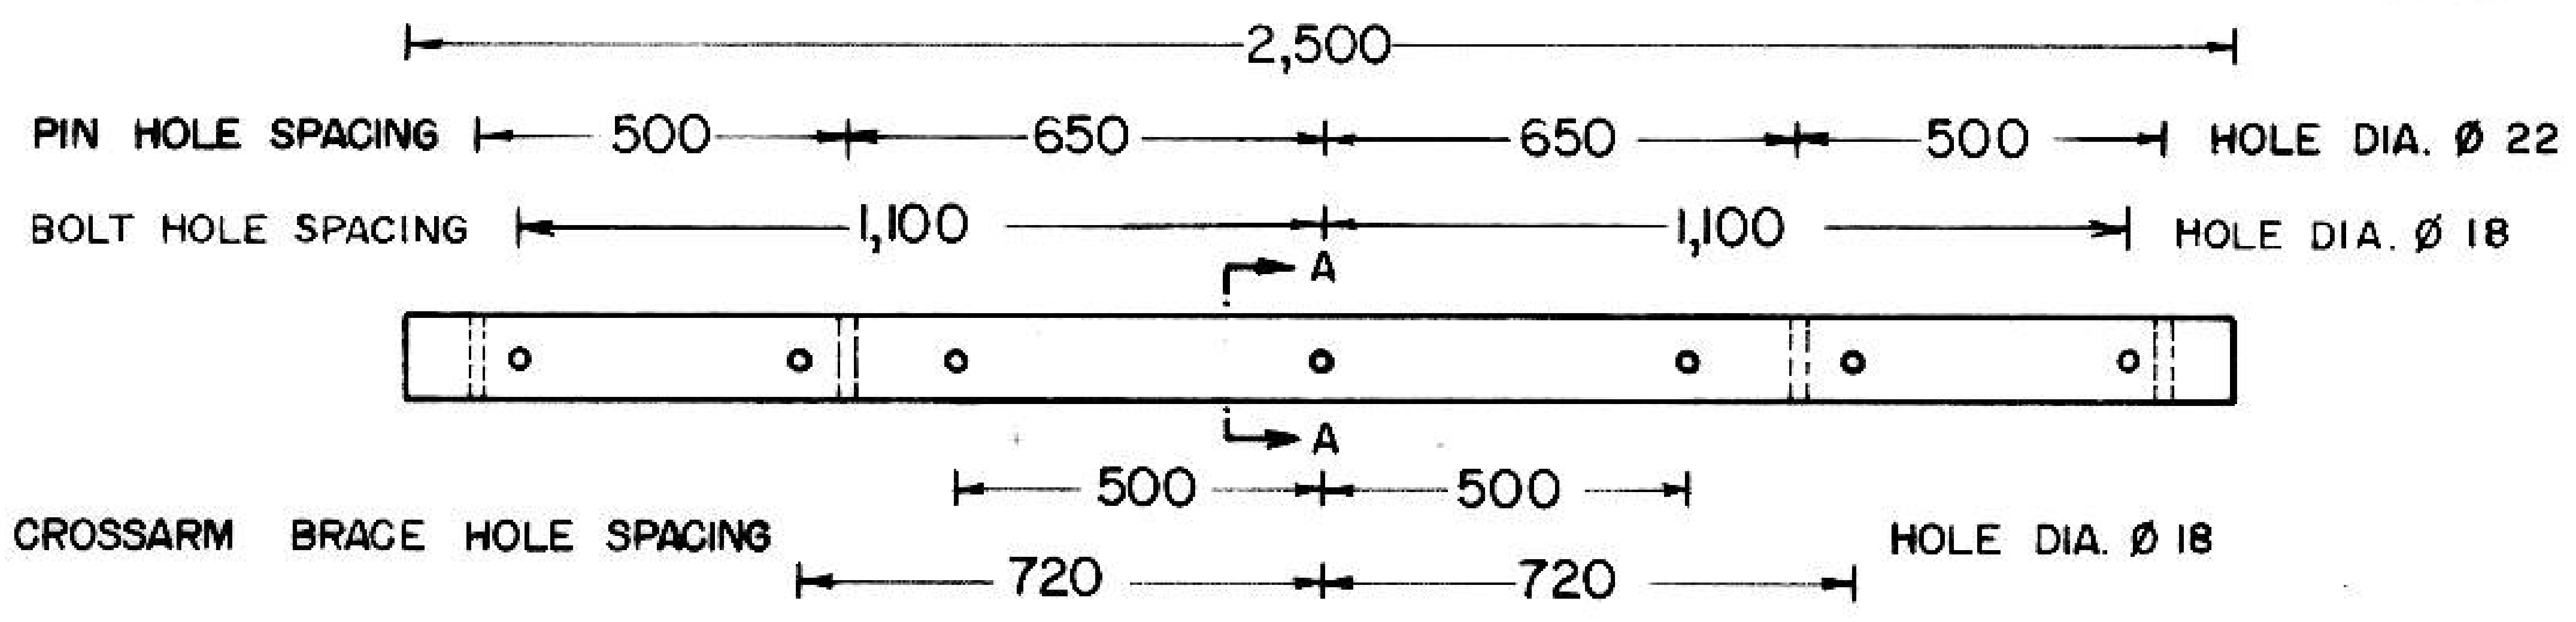

WORKING MOMENT 500 kg-M SAFETY FACTOR = 3

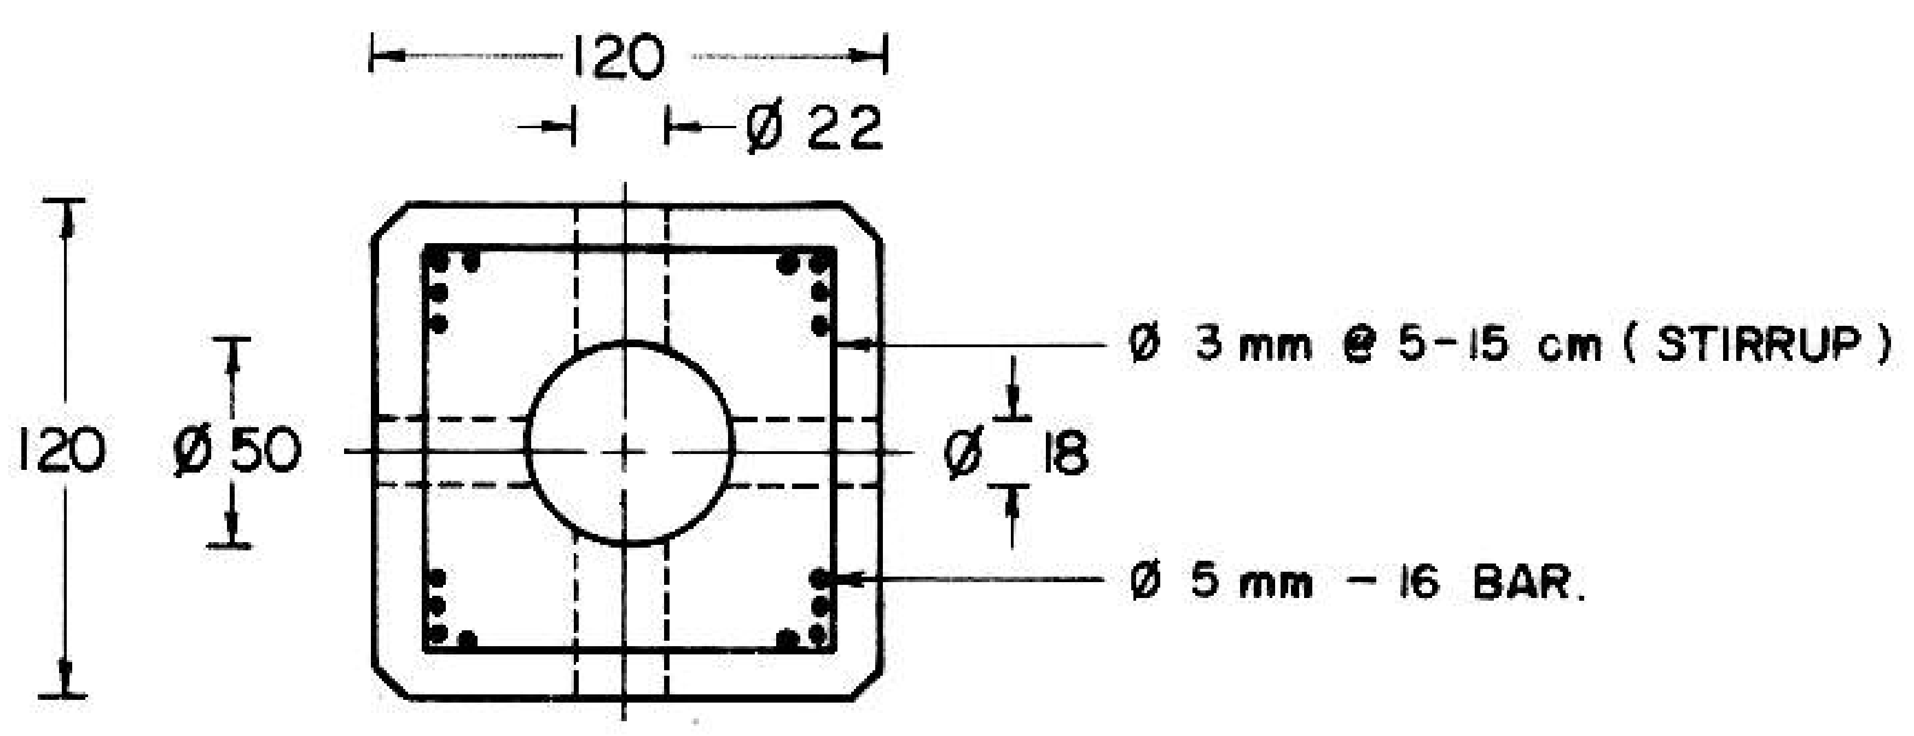

รูปตัด SECTION A - A

คอน คอนกรีตอัดแรงแบบสปัน (สำหรับเจ้าปลายสาย) 120 X 120 X 2,500 มม. (**วัสดุเลขที่ 0196**)

1 ประกอบคอนคู่ เพื่อติดตั้งลูกถ้วยแขวนบนเสาคอนกรีต สำหรับใช้งานในระบบจำหน่าย 33 kV

2 ใช้งานสำหรับโครงสร้างเจ้าปลายสาย , เจ้าปลายสายสองข้าง , ทางโค้งมากกว่า 30° (30° - 60°)

3 ข้อกำหนดการใช้งาน

ขนาดสายสูงสุด : อะลูมิเนียมเปลือย 185 ต.มม.

ระยะห่างระหว่างเสาสูงสุดไม่เกิน 80 ม.

SPUN PRESTRESSED CONCRETE CROSSARM (FOR DEADENDING) 120 X 120 X 2,500 mm (MAT. NO. 0196)

1 ASSEMBLY THE DOUBLE CROSSARMS FOR SUSPENSION-TYPE INSULATOR ON CONCRETE POLE. USING ON 33 kV DISTRIBUTION SYSTEM.

2 APPLICATION FOR DEADEND STRUCTURE, DOUBLE DEADEND STRUCTURE, AND ANGLE STRUCTURE MORE THAN 30° (30° - 60°)

3 RECOMMENDATION

MAXIMUM CONDUCTOR SIZE : BARE ALUMINIUM 185 mm^2

MAX. SPAN LENGTH NOT EXCEEDING 80 m

กองวิศวกรรมไฟฟ้าและเครื่องกล ฝ่ายวิศวกรรม	การไฟฟ้าส่วนภูมิภาค	ใช้แทนแบบ ถูกแทนโดยแบบ
ผู้เขียน ผู้สำรวจ วิศวกร หัวหน้าแผนก หัวหน้ากอง ผู้อำนวยการฝ่าย	ผู้ว่าการ 4 มิ.ย. 24	เขียนเสร็จวันที่ 8 พ.ค. 24 แก้แบบวันที่ 28 มิ.ย. 27 มิติเป็น มม. มาตราส่วน 1 : 5 , 1 : 25
	คอน คอร. สปัน (สำหรับเจ้าปลายสาย) 120 X 120 X 2,500 มม.	
รองผู้ว่าการฝ่ายเทคนิค	SPUN PRESTRESSED CONCRETE CROSSARM (FOR DEADENDING) 120 X 120 X 2,500 mm	แบบเลขที่ SAI-015/24011 แผ่นที่ 1 จองจำนวน 1 แผ่น

2524