



การประกอบเลขที่ 3238
ASSEMBLY NO.

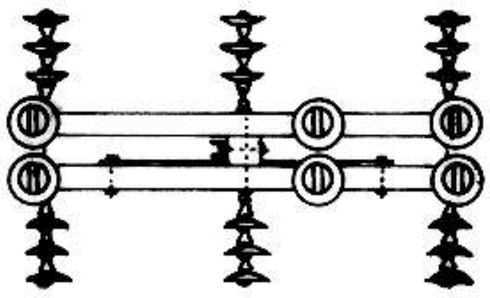


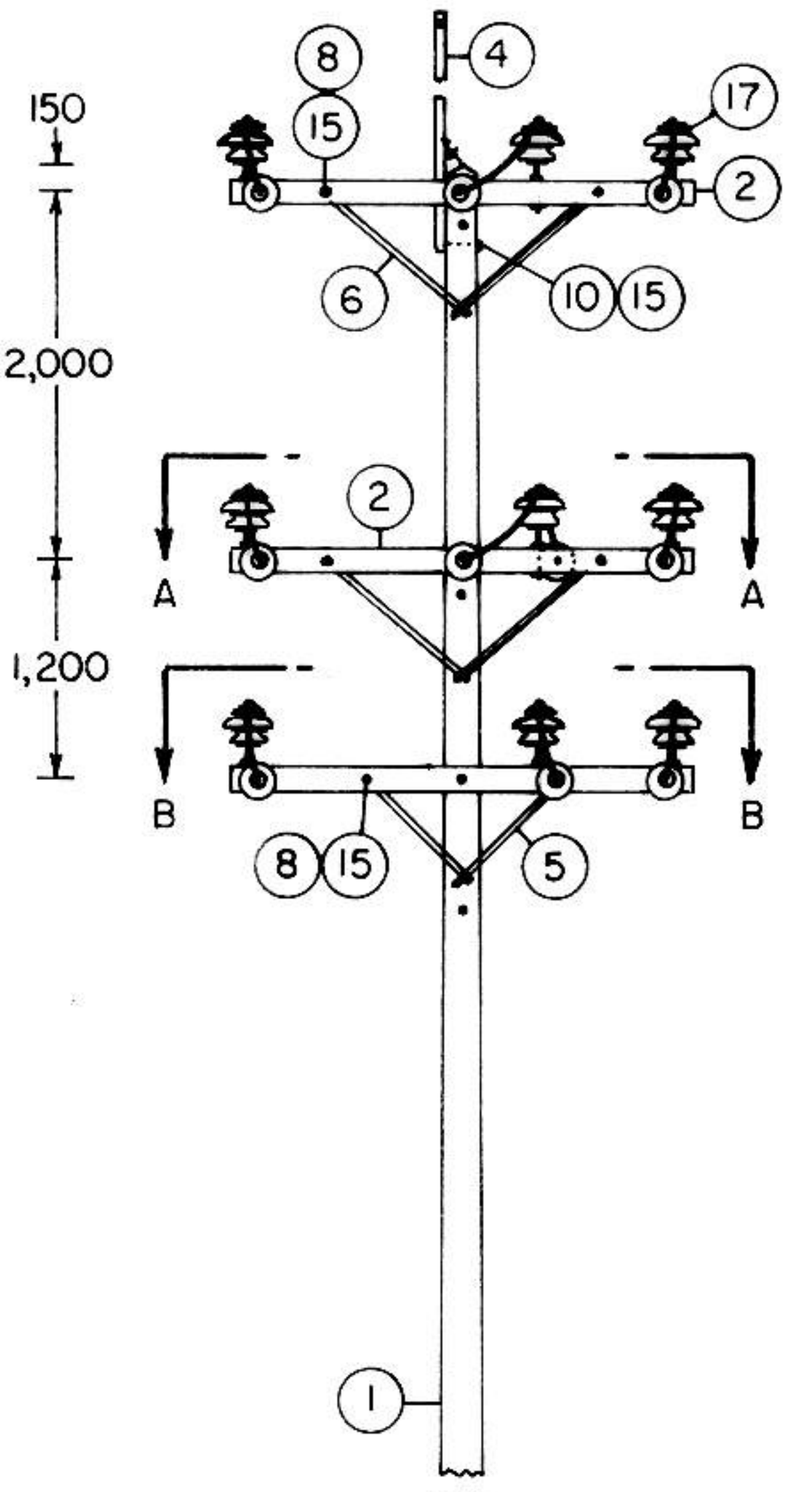

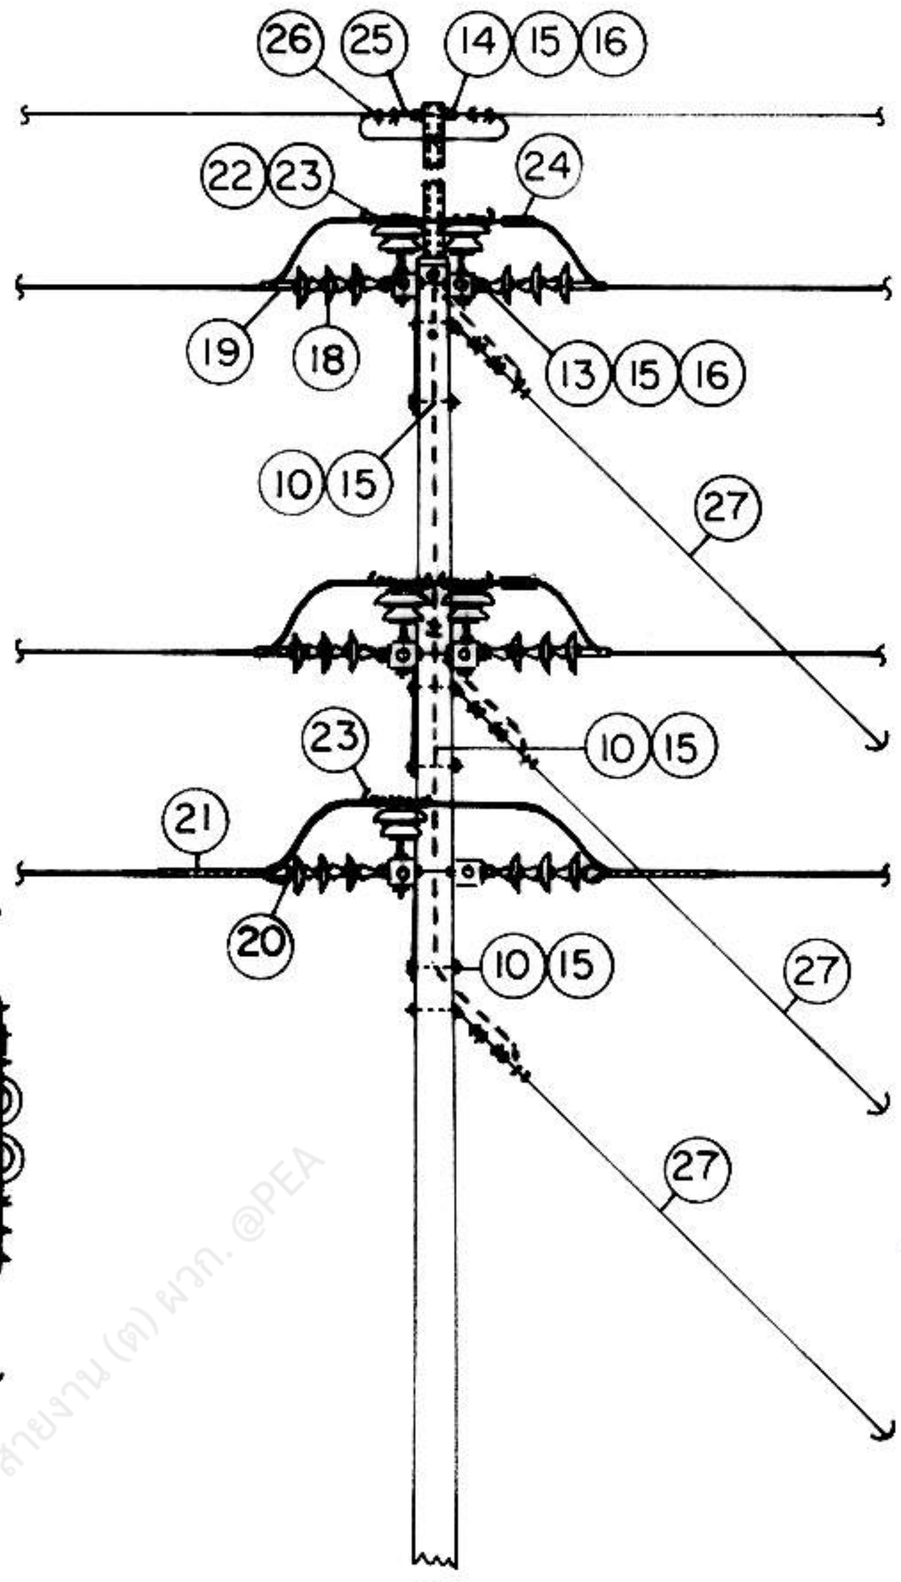

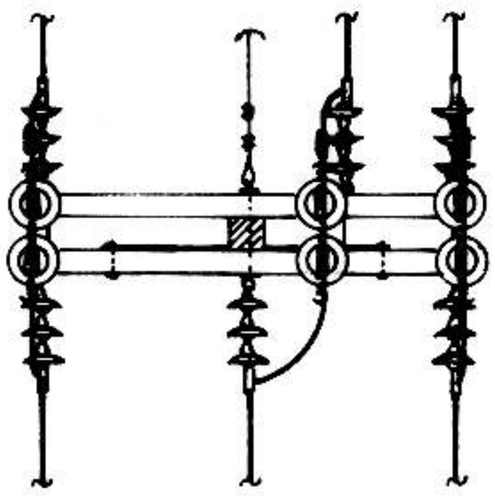

รูปตัด A – A
SECTION A – A

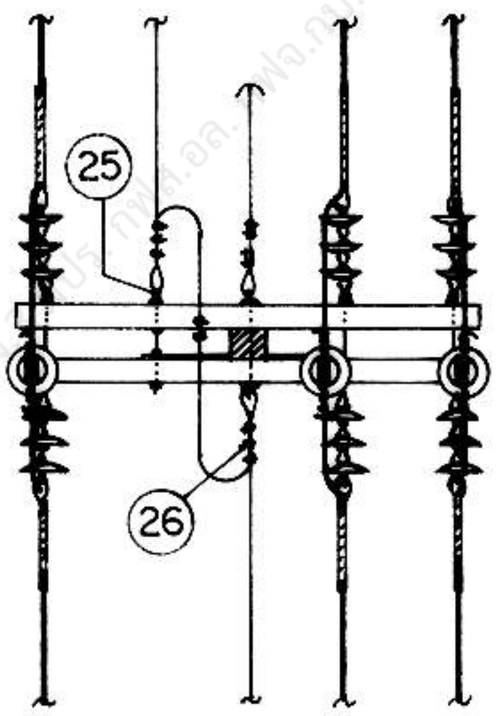


รูปตัด B – B
SECTION B – B

I สำหรับการติดตั้ง 3 วงจร (สายเปลือย 2 วงจร และเคเบิลอากาศ 1 วงจร)
FOR 3-CIRCUIT INSTALLATION (2-CIRCUIT BARE CONDUCTOR AND 1-CIRCUIT AERIAL CABLE)

กองวิศวกรรมไฟฟ้าและเครื่องกล ฝ่ายวิศวกรรม	การไฟฟ้าส่วนภูมิภาค	ใช้แทนแบบ ถูกแทนโดยแบบ
ผู้เขียน ผู้สำรวจ วิศวกร หัวหน้าแผนก ผู้อำนวยการกอง ผู้อำนวยการฝ่าย	ผู้ว่าการ โครงสร้างเสาต้นเข้าปลายสายส่องข้าง ระบบ 33 kV 3 – 4 วงจร	เขียนเสร็จวันที่ 9 ต.ค. 35 แก้แบบวันที่ มิติเป็น มิลลิเมตร มาตราส่วน 1 : 75
รองผู้ว่าการฝ่ายเทคนิค	33 kV DOUBLE DEADEND STRUCTURE 3 – 4 CIRCUIT	แบบเลขที่ SA4-015/35011 แผ่นที่ 1 ของจำนวน 7 แผ่น

26 ต.ค. 2535


การประกอบเลขที่ 3238
ASSEMBLY NO.

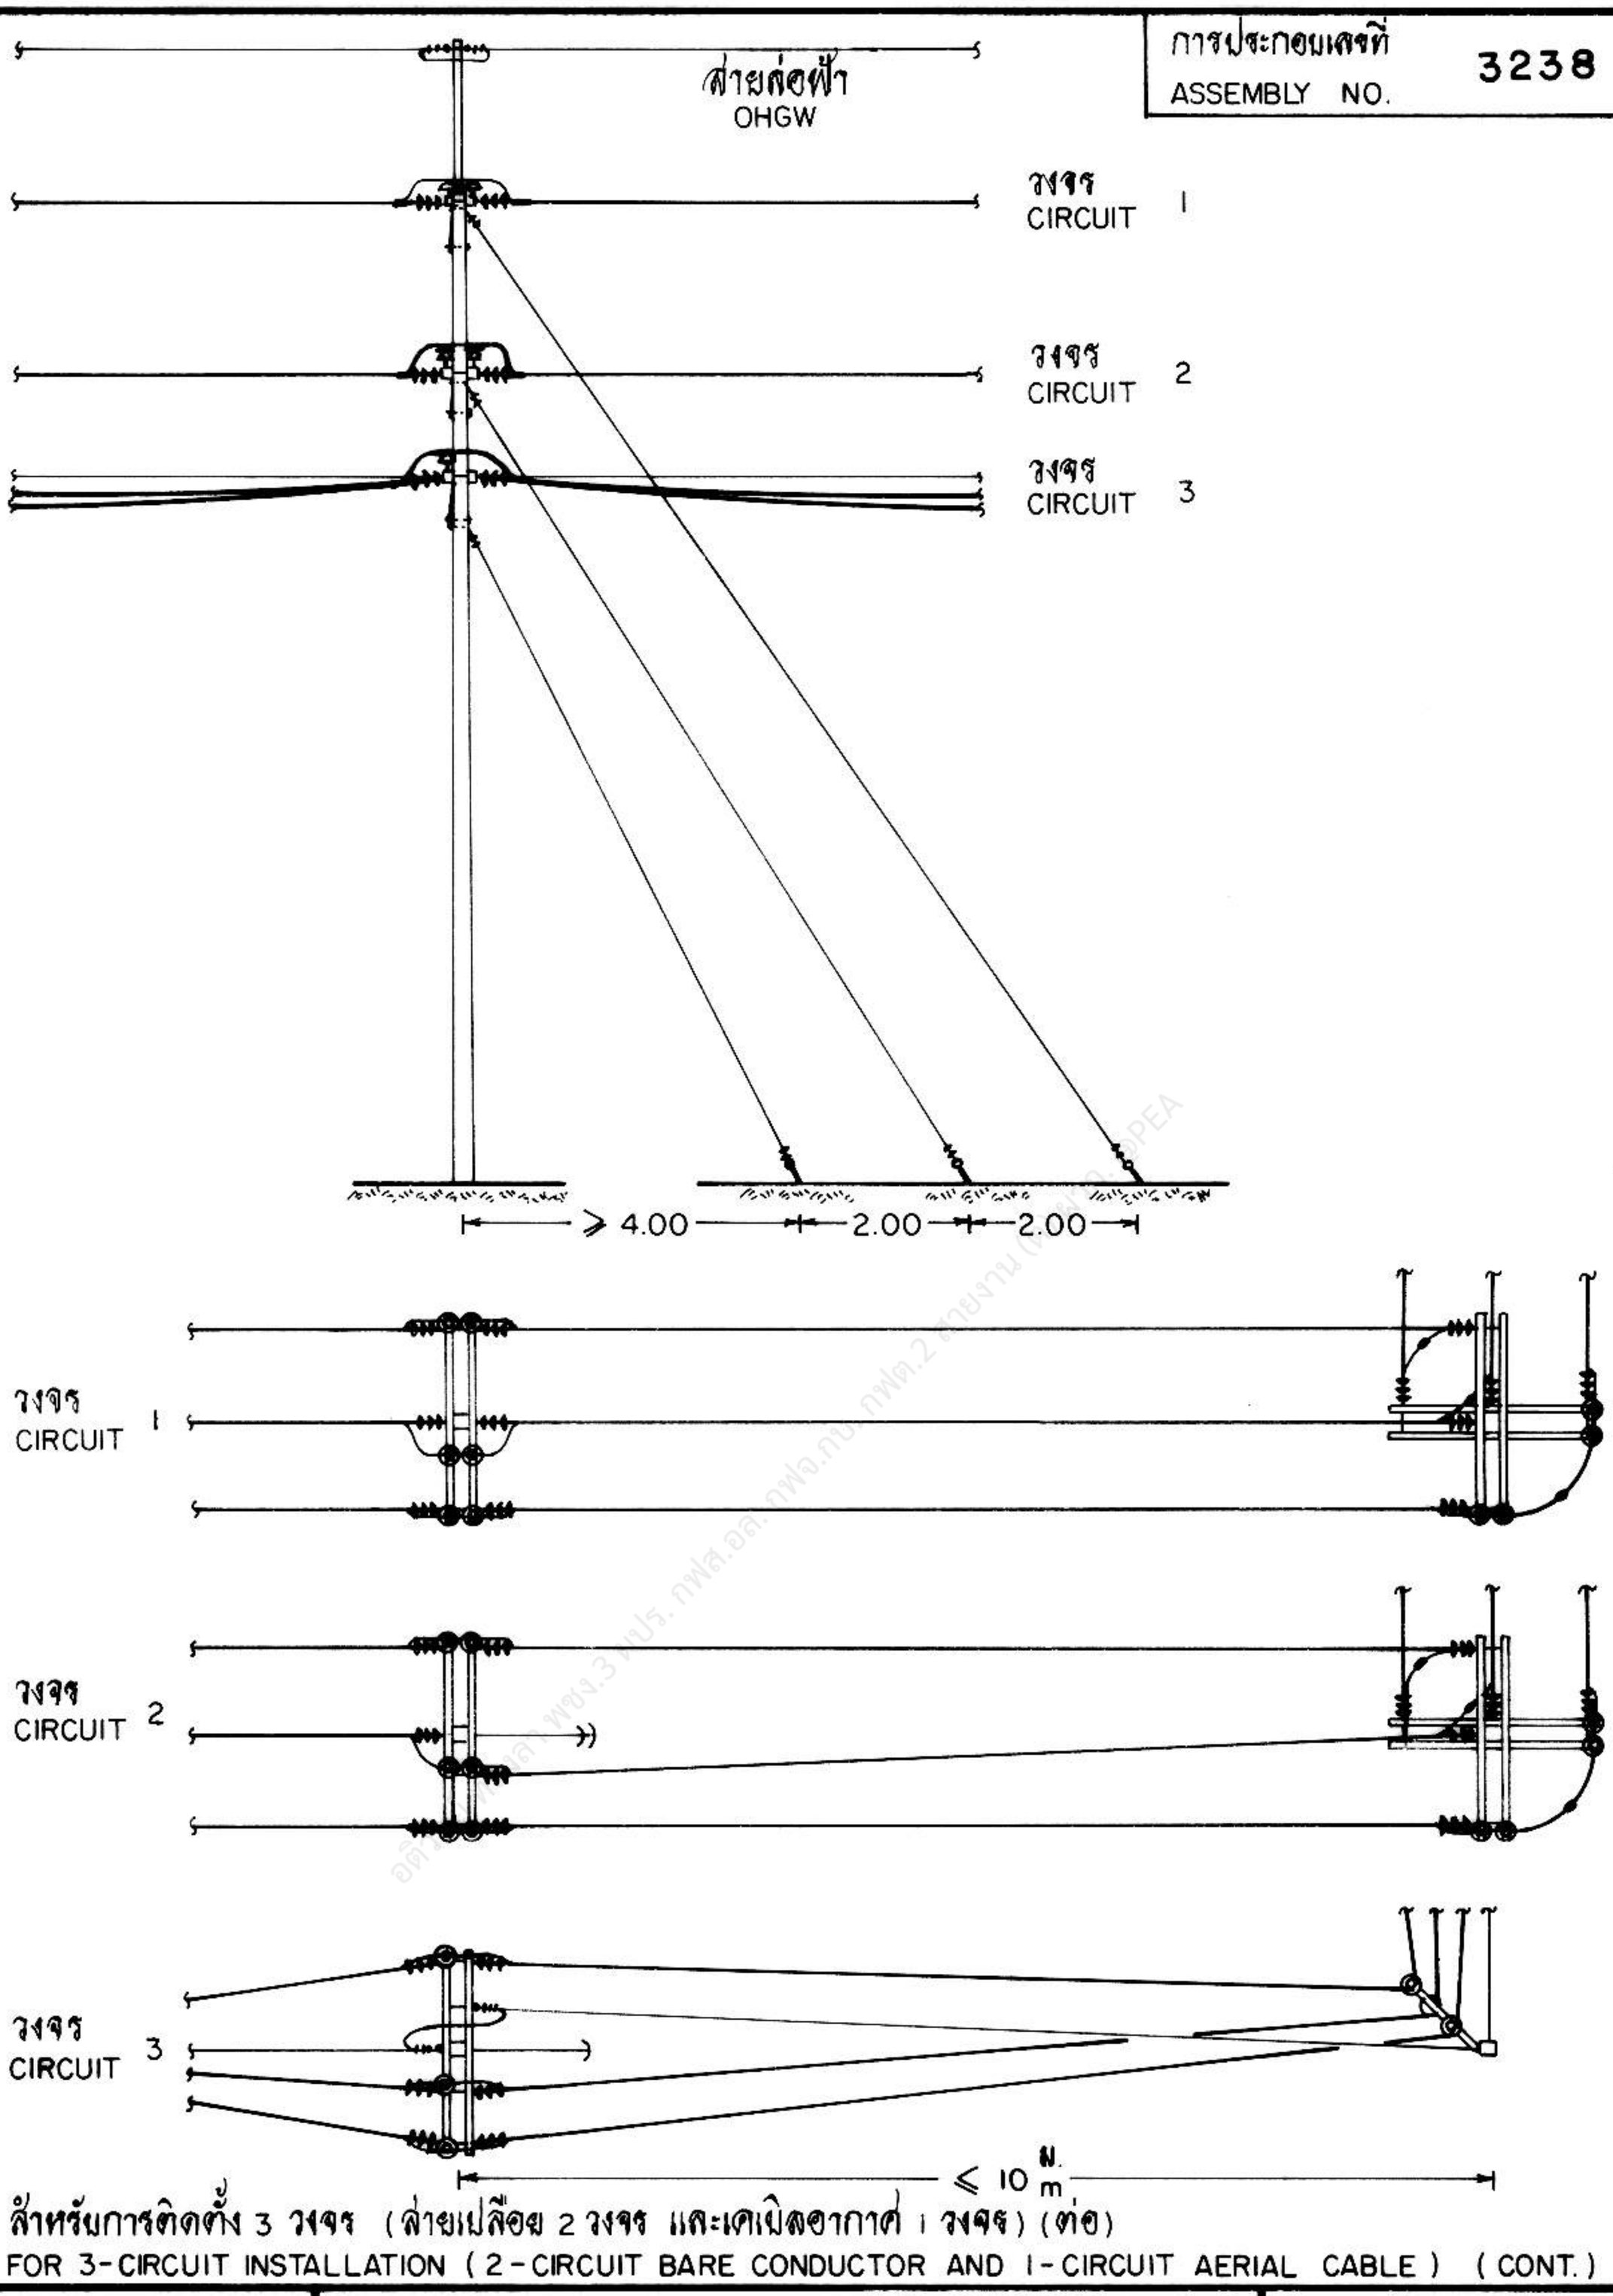

I สำหรับการติดตั้ง 3 วงจร (สายเปลือย 2 วงจร และเคเบิลอากาศ 1 วงจร) (ต่อ)
FOR 3-CIRCUIT INSTALLATION (2-CIRCUIT BARE CONDUCTOR AND 1-CIRCUIT AERIAL CABLE) (CONT.)

กองวิศวกรรมไฟฟ้าและเครื่องกล ฝ่ายวิศวกรรม	การไฟฟ้าส่วนภูมิภาค	ใช้แทนแบบ ถูกแทนโดยแบบ
ผู้เขียน ผู้สำรวจ วิศวกร หัวหน้าแผนก ผู้อำนวยการกอง ผู้อำนวยการฝ่าย	ผู้ว่าการ 29 ต.ค. 35	เขียนเสร็จวันที่ 9 ต.ค. 35 แก้แบบวันที่ มิติเป็น เมตร มาตราส่วน 1 : 125
รองผู้ว่าการฝ่ายเทคนิค	โครงสร้างเสาต้นเข้าปลายสายสองข้าง ระบบ 33 kV 3 – 4 วงจร 33 kV DOUBLE DEADEND STRUCTURE 3 – 4 CIRCUIT	แบบเลขที่ SA4-015/35011 แผ่นที่ 2 ของจำนวน 7 แผ่น

การประกอบเลขที่ 3238
ASSEMBLY NO.

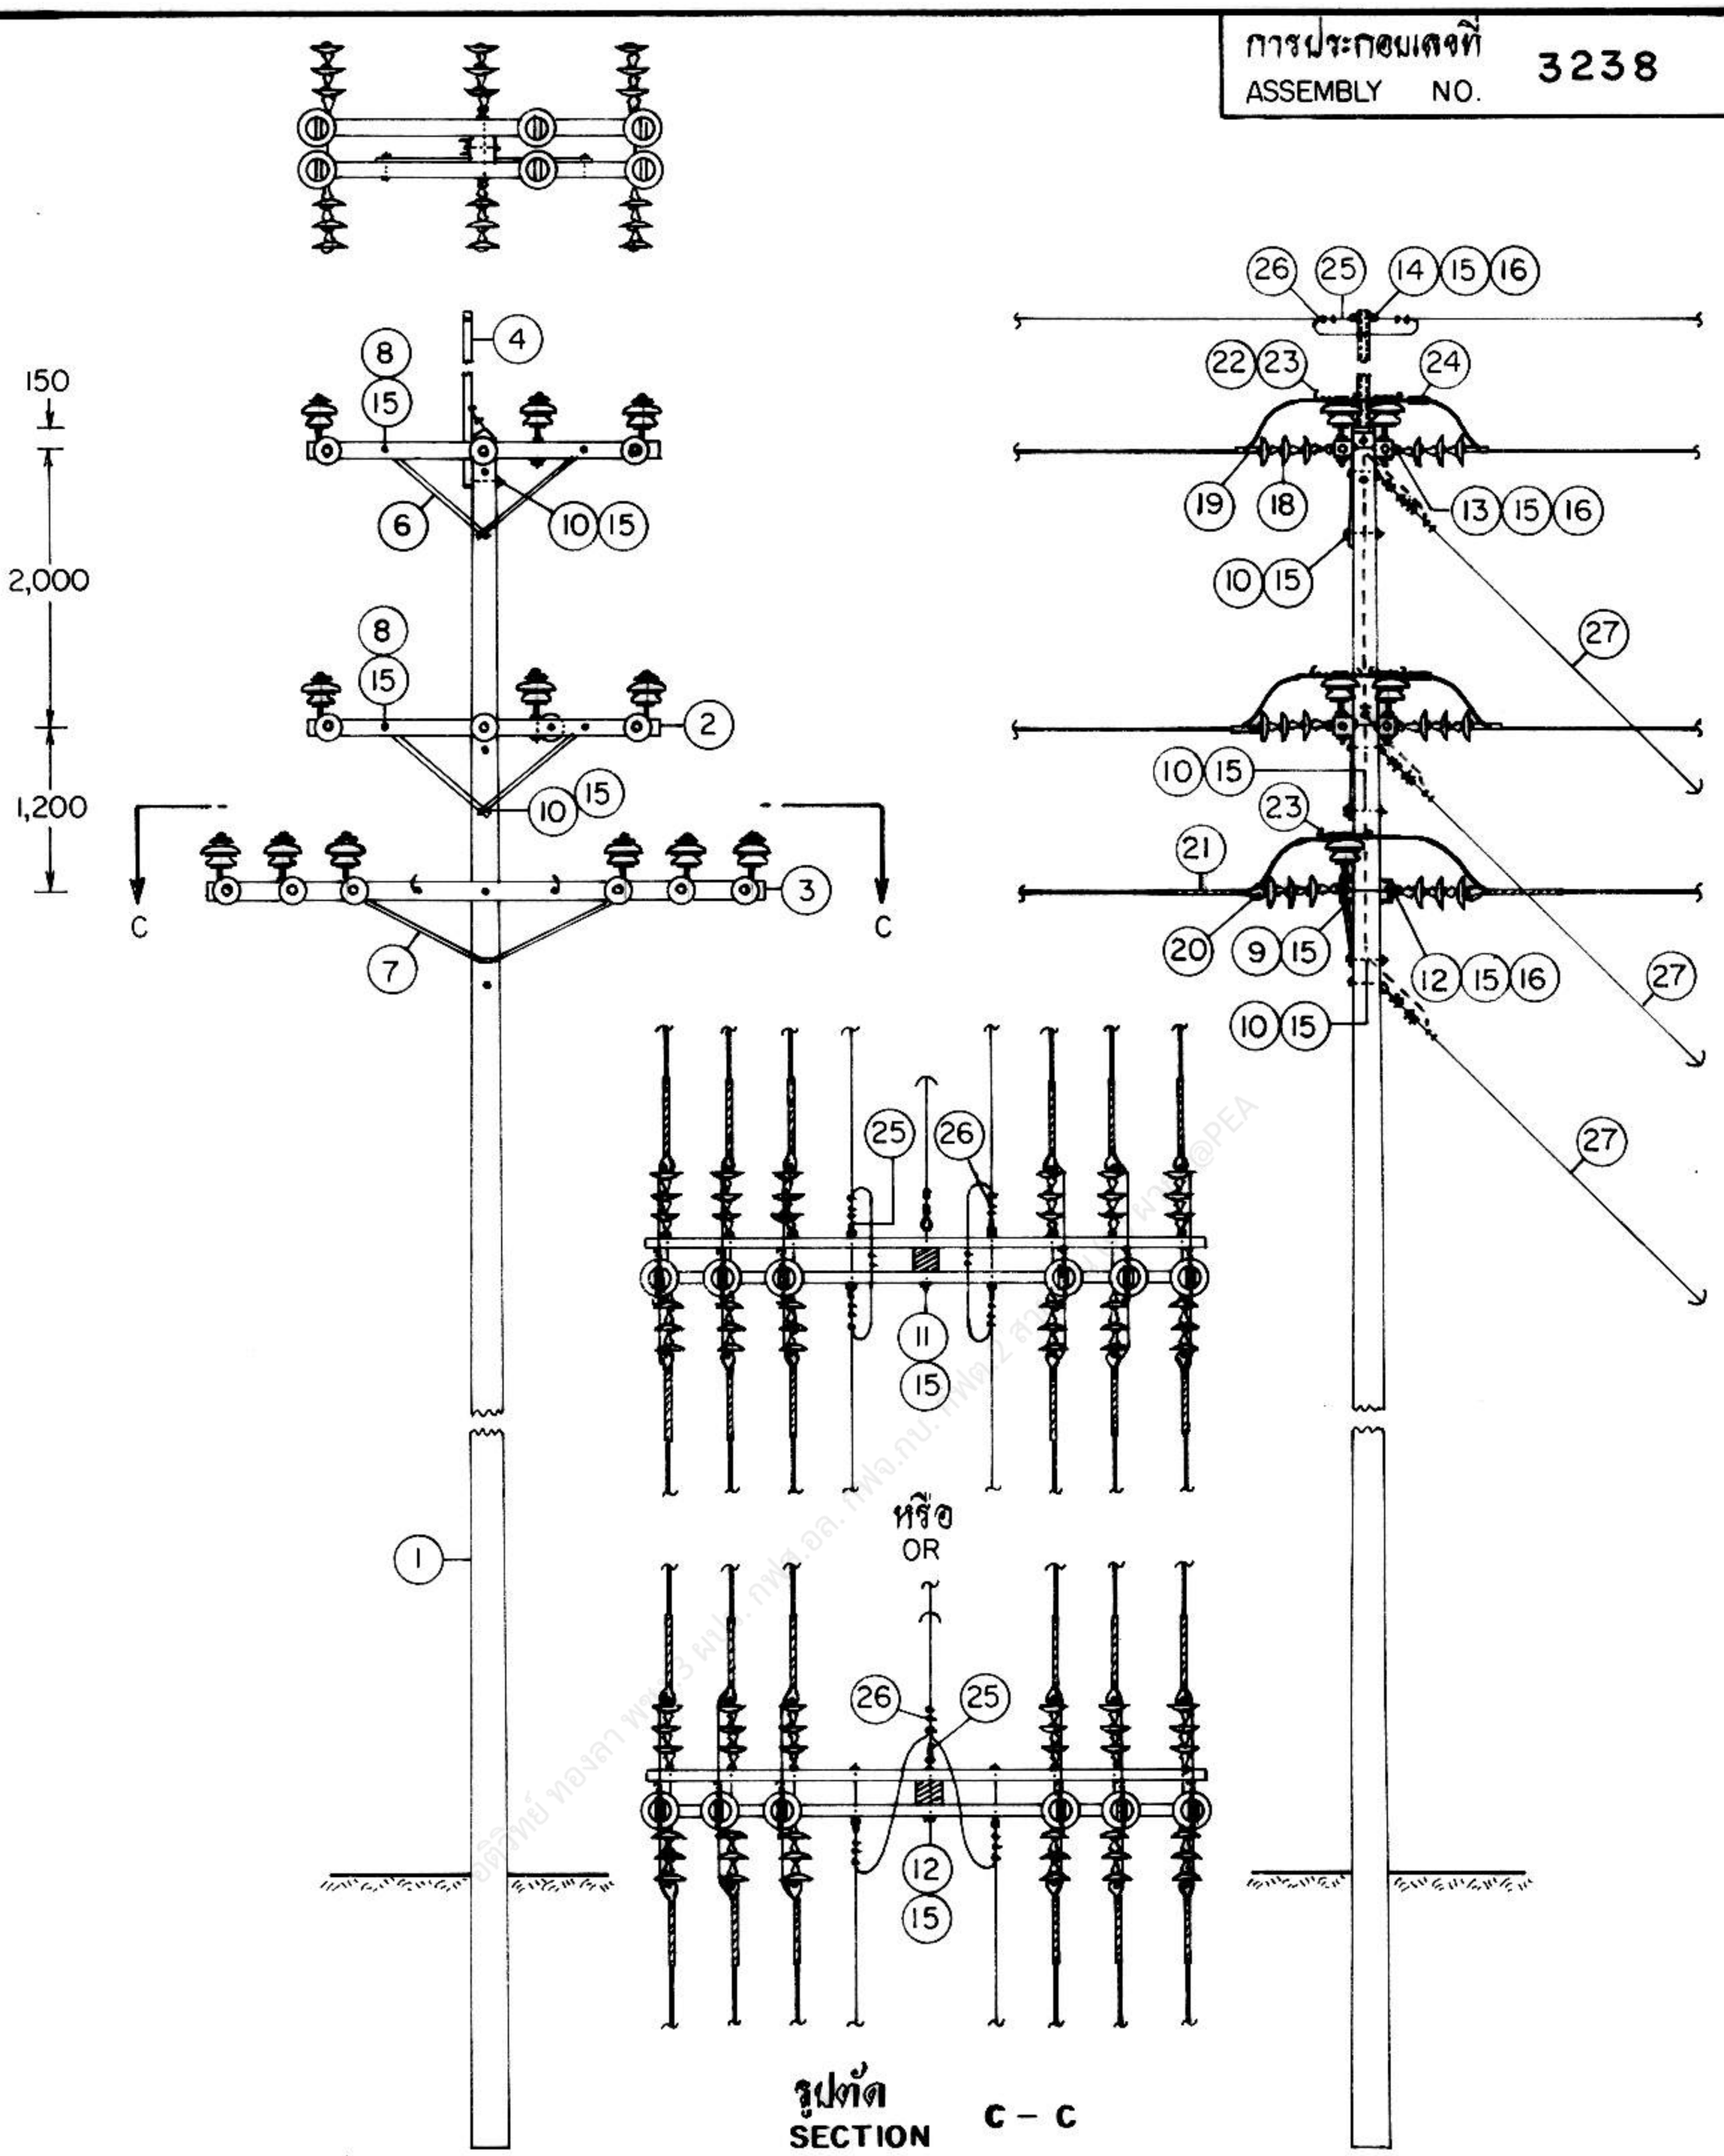



รูปตัด
SECTION C – C

II สำหรับการติดตั้ง 4 วงจร (สายเปลือย 2 วงจร และเคเบิลอากาศ 2 วงจร)
FOR 4-CIRCUIT INSTALLATION (2-CIRCUIT BARE CONDUCTOR AND 2-CIRCUIT AERIAL CABLE)

กองวิศวกรรมไฟฟ้าและเครื่องกล ฝ่ายวิศวกรรม	การไฟฟ้าส่วนภูมิภาค	ใช้แทนแบบ ถูกแทนโดยแบบ
ผู้เขียน ผู้สำรวจ วิศวกร หัวหน้าแผนก ผู้อำนวยการกอง ผู้อำนวยการฝ่าย	ผู้ว่าการ 29 ต.ค. 35 โครงสร้างเสาต้นเข้าปลายสายสองด้าน ระบบ 33 kV 3 – 4 วงจร	เขียนแล้วเสร็จวันที่ 9 ต.ค. 35 แก้แบบวันที่ มิติเป็น มิลลิเมตร มาตราส่วน 1 : 75
รองผู้ว่าการฝ่ายเทคนิค	33 kV DOUBLE DEADEND STRUCTURE 3 – 4 CIRCUIT	แบบเลขที่ SA4-015/35011 แผ่นที่ 3 ของจำนวน 7 แผ่น

การประกอบเลขที่ ASSEMBLY NO.	3238

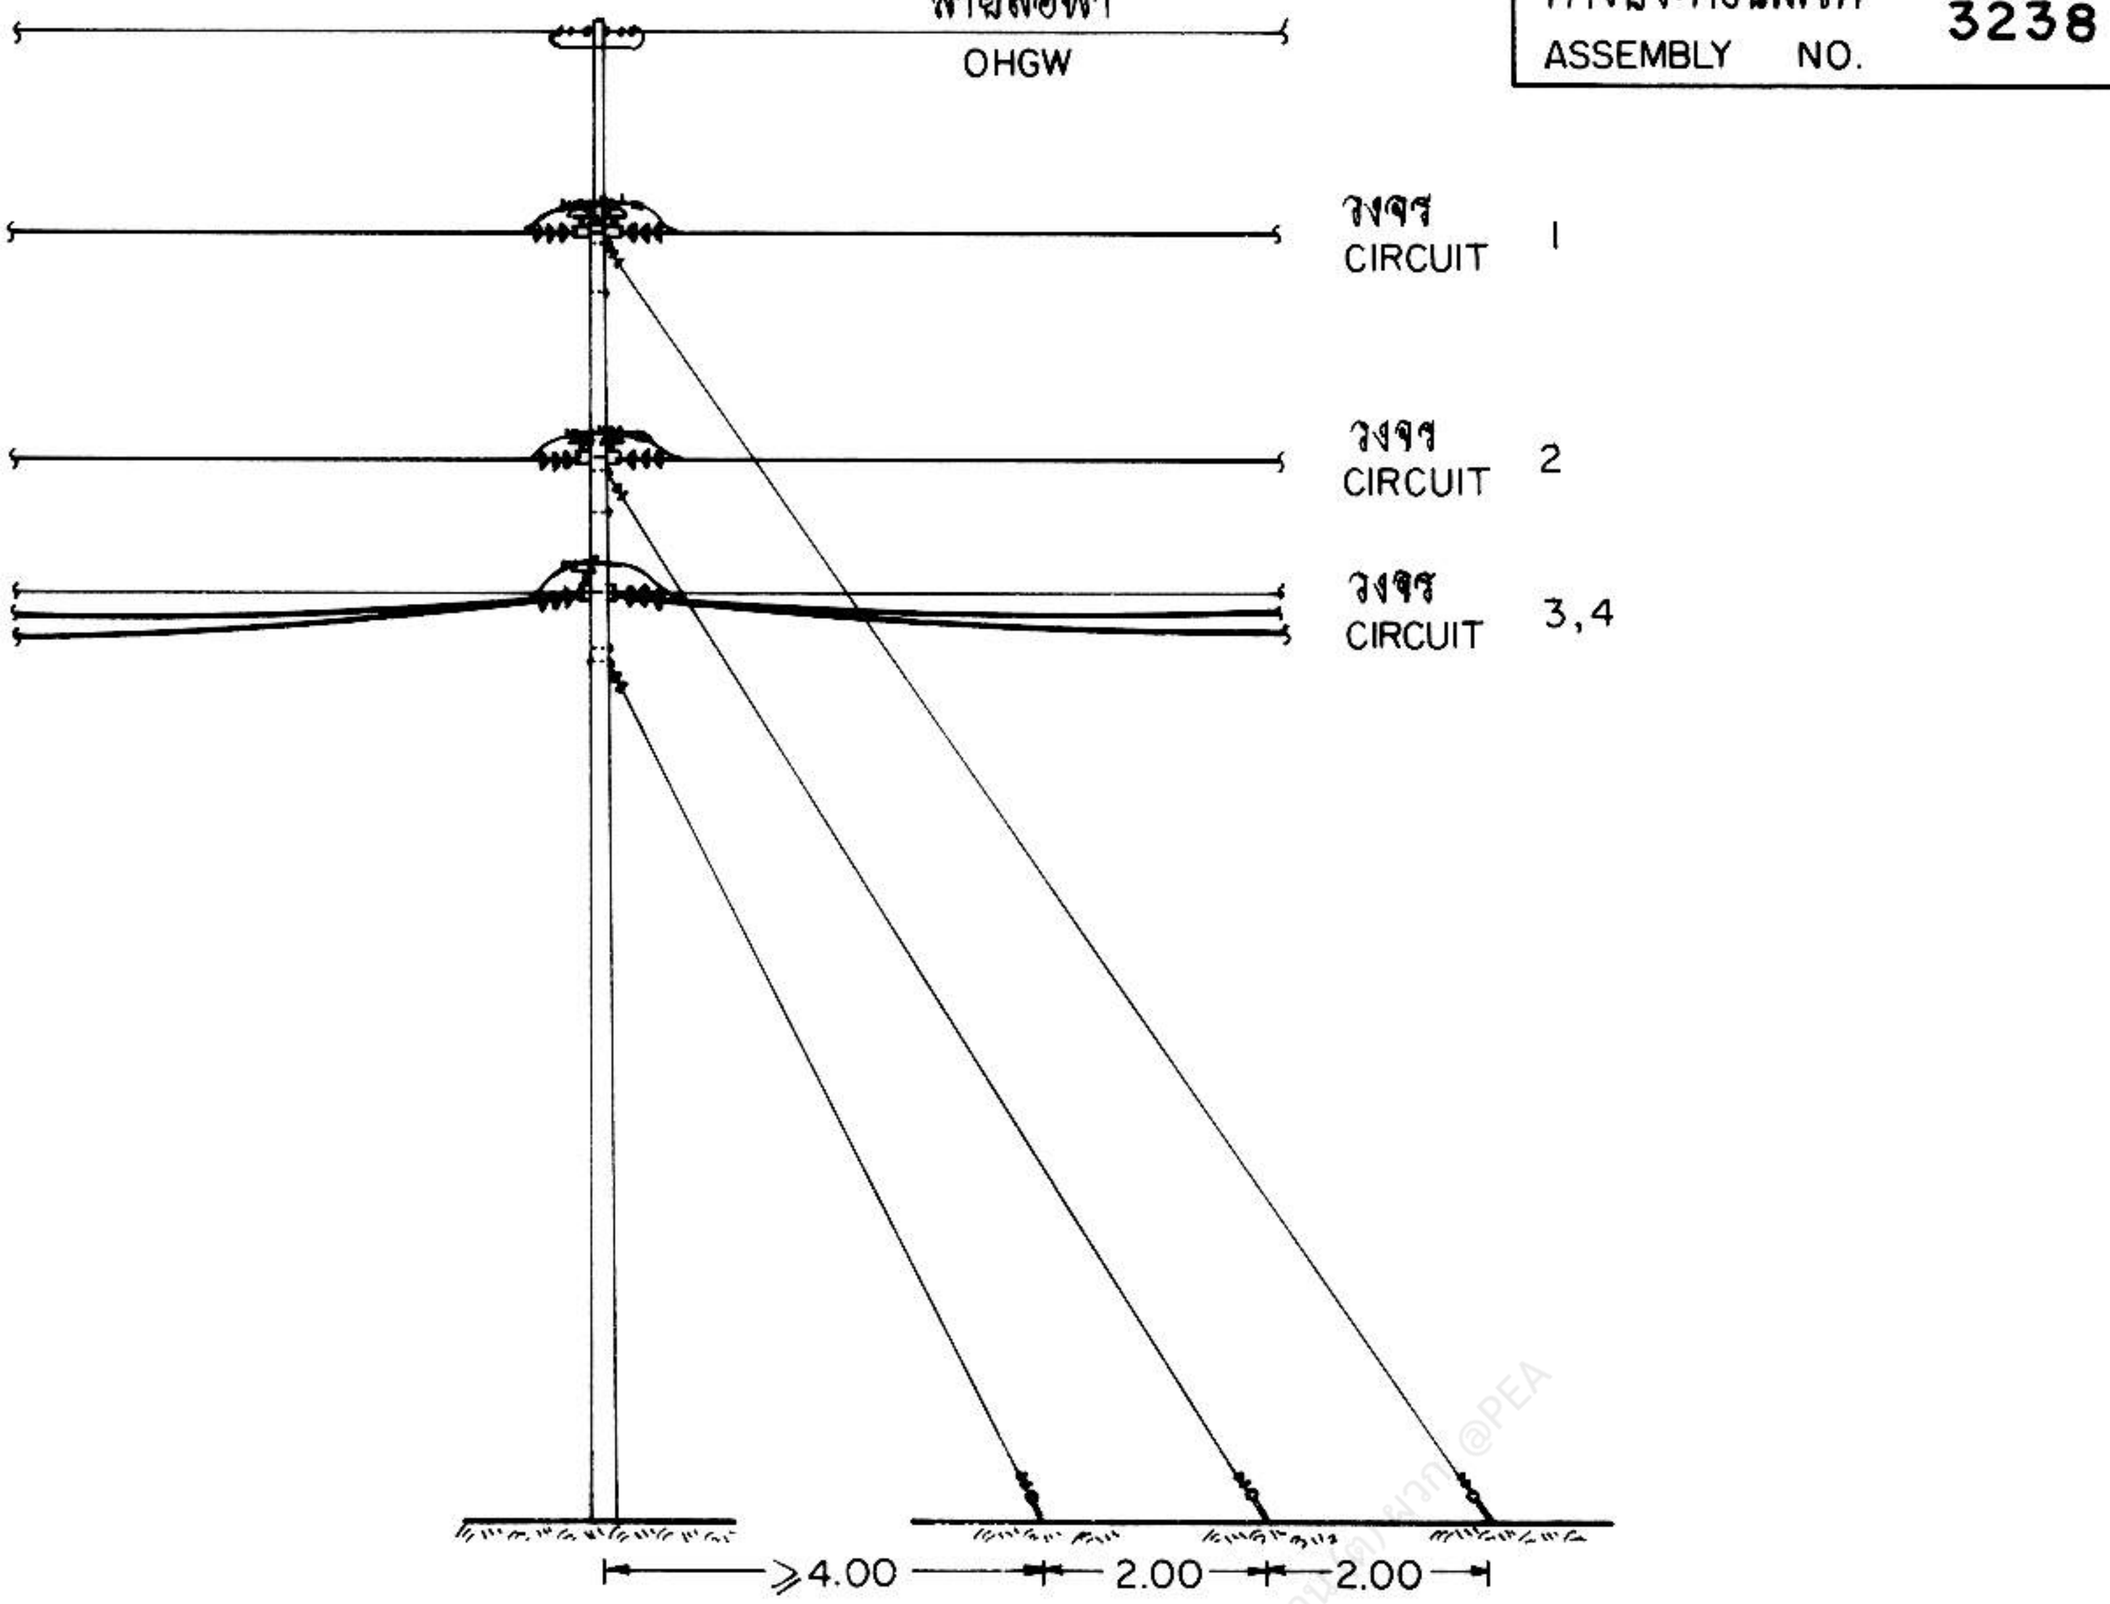

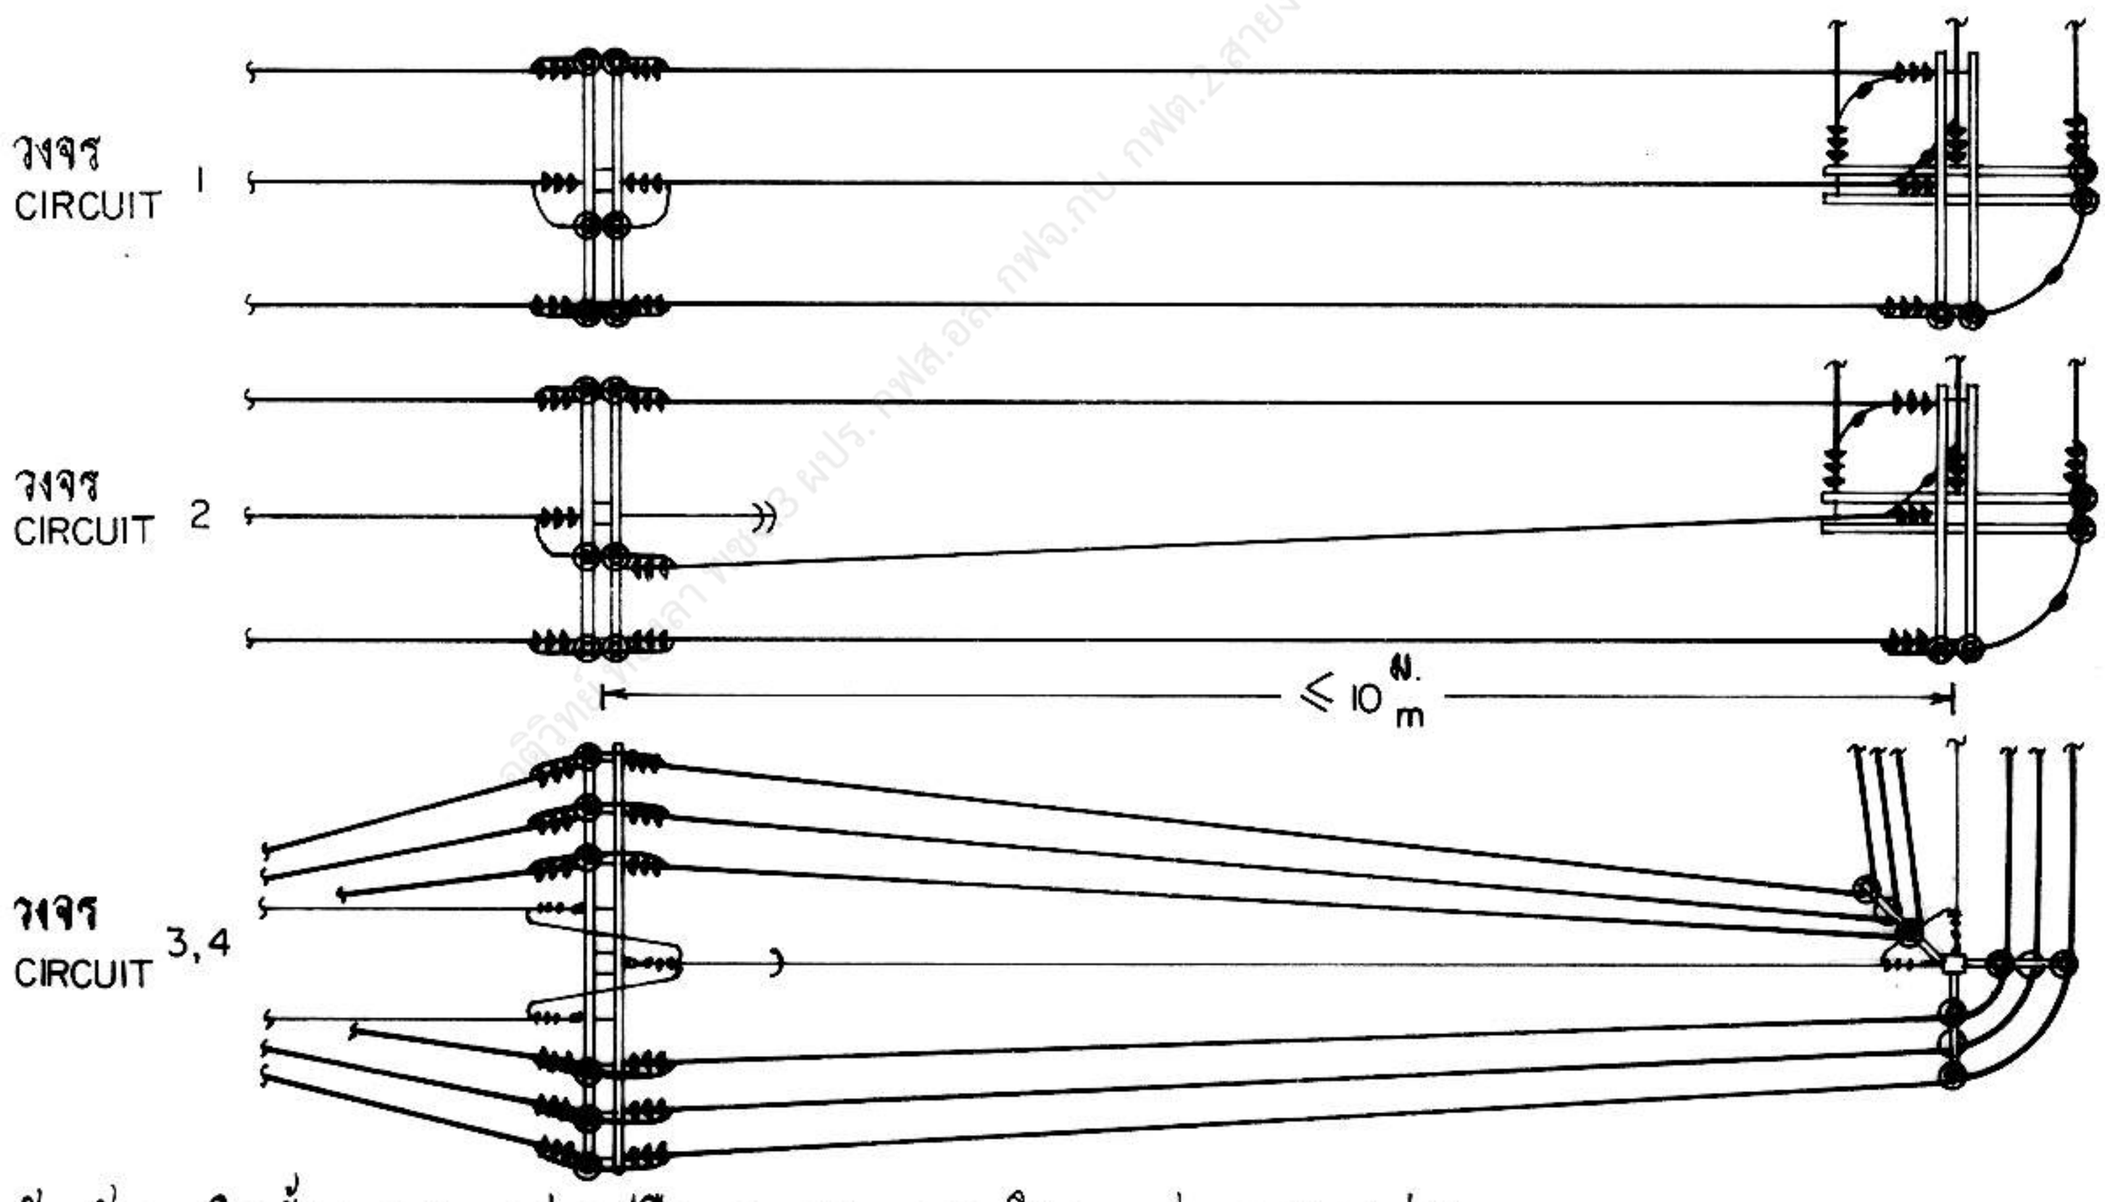


II สำหรับการติดตั้ง 4 วงจร (สายเปลือย 2 วงจร และเคเบิลอากาศ 2 วงจร) (ต่อ)
FOR 4-CIRCUIT INSTALLATION (2-CIRCUIT BARE CONDUCTOR AND 2-CIRCUIT AERIAL CABLE) (CONT.)

กองวิศวกรรมไฟฟ้าและเครื่องกล ฝ่ายวิศวกรรม	การไฟฟ้าส่วนภูมิภาค	ใช้แทนแบบ ถูกแทนโดยแบบ
ผู้เขียน ผู้สำรวจ วิศวกร หัวหน้าแผนก ผู้อำนวยการกอง ผู้อำนวยการฝ่าย	ผู้ว่าการ 27 ต.ค. 35 โครงสร้างเสาต้นเข้าปลายสายสองชั้น ระยม 33 kV 3 – 4 วงจร	เขียนเสร็จวันที่ 9 ต.ค. 35 แก้แบบวันที่ มิติเป็น เมตร มาตราส่วน 1 : 125
ของผู้ว่าการฝ่ายเทคนิค	33 kV DOUBLE DEADEND STRUCTURE 3 – 4 CIRCUIT	แบบเลขที่ SA4-015/35011 แผ่นที่ 4 ของจำนวน 7 แผ่น

26 ก.พ. 2535

การประกอบเลขที่ ASSEMBLY NO. 3238

วัสดุลำดับที่ MATERIAL ITEM (3)

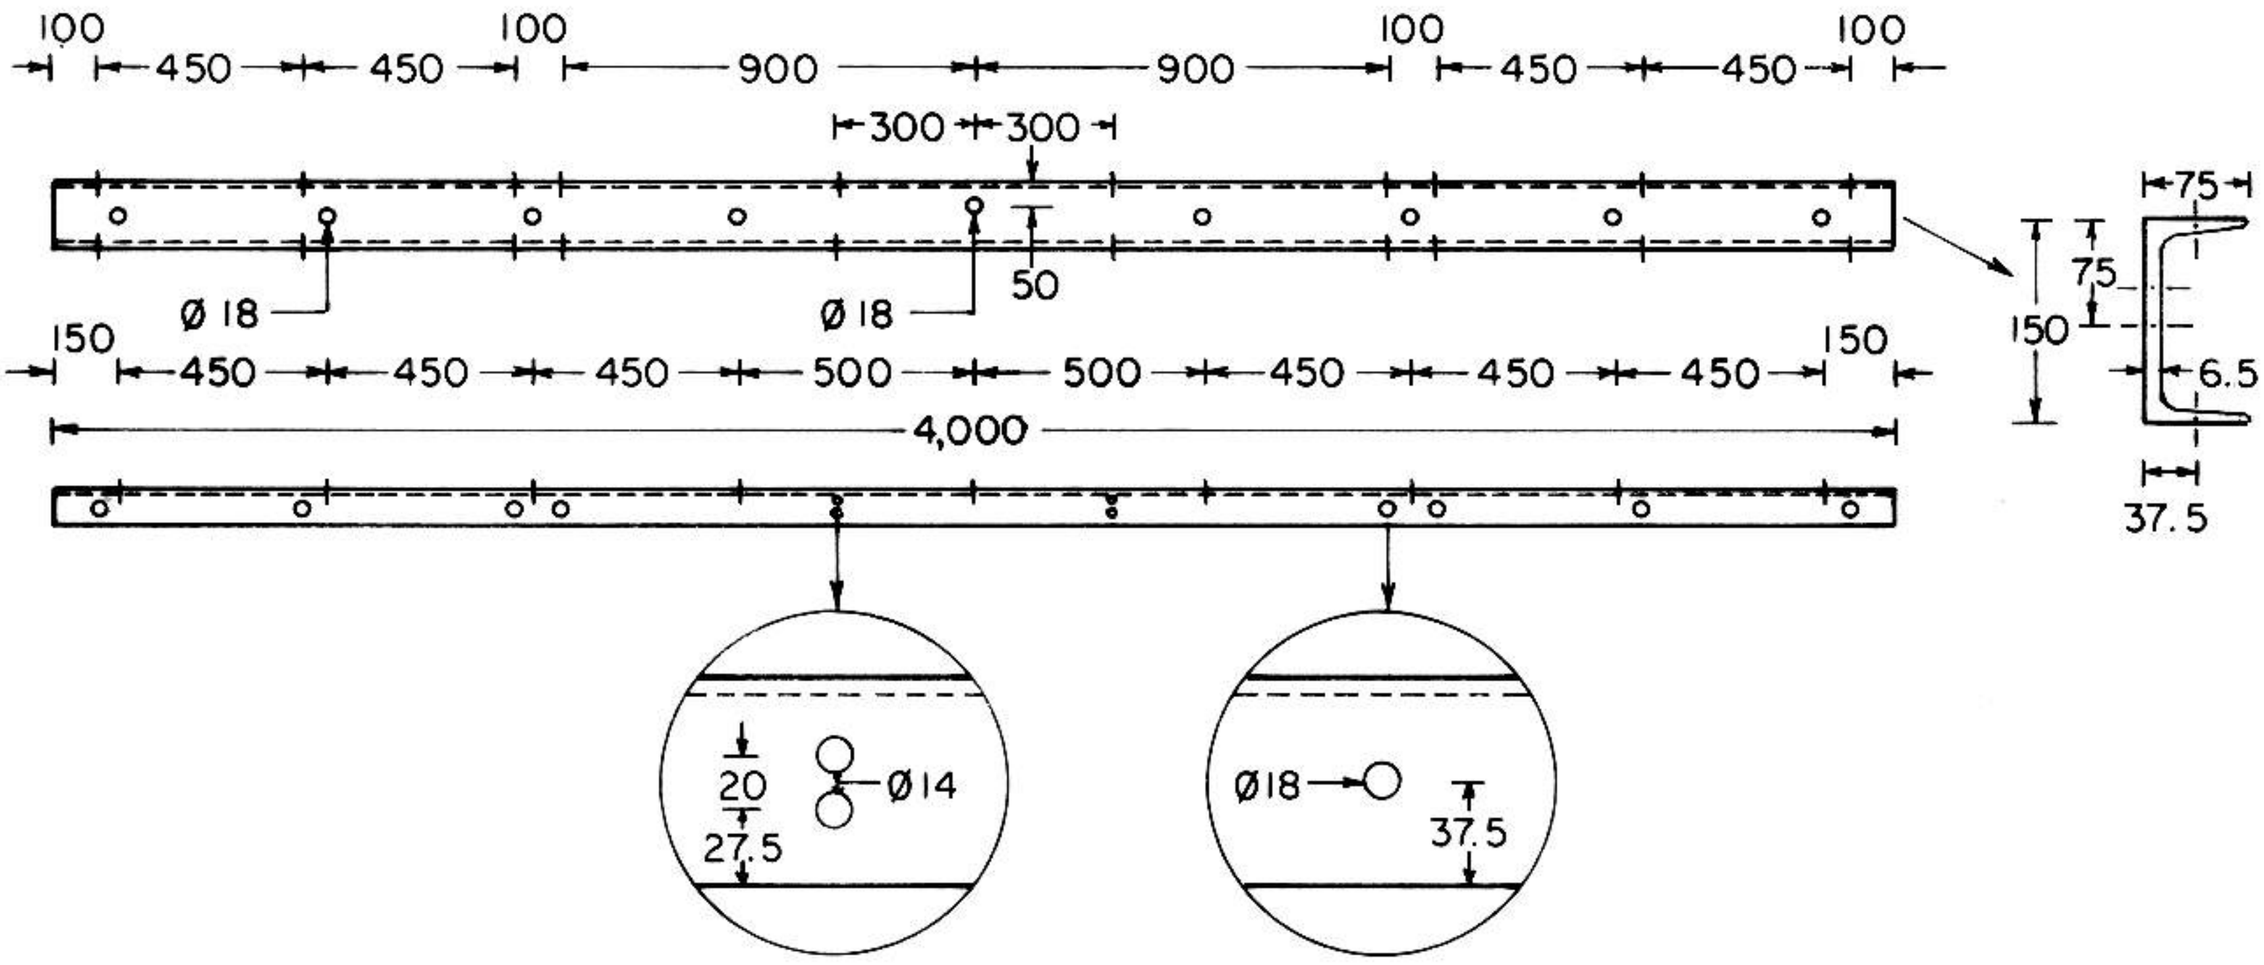

เหล็กรูปรางน้ำ ชนิดรีดร้อน ขนาด 150X75X6.5 มม. ยาว 4.00 ม. มอก. 116
STEEL, CHANNEL, 150 X 75 X 6.5 mm, 4.00 m LONG, TIS 116

รายละเอียด DETAIL A

บัญชีวัสดุ BILL OF MATERIAL

ลำดับที่ ITEM	รายละเอียด DESCRIPTION	จำนวน REQ'D I	จำนวน REQ'D II	วัสดุเลขที่ MAT. NO.
1	เสาคอนกรีต ขนาด 14 ม. POLE, CONCRETE, 14 m LONG	1	1	00010006 (0036)
2	คอน คอร. ส่ปัน (สำหรับเข้าปลายสาย) ขนาด 120 X 120 X 2,500 มม. CROSSARM, SPUN, PRESTRESSED CONCRETE (FOR DEADENDING), 120 X 120 X 2,500 mm	6	4	00110004 (0191)
3	เหล็กรูปรางน้ำ ขนาด 150 X 75 X 6.5 มม. ยาว 4.00 ม. มอก. 116 เจาะรูตามรายละเอียด A STEEL, CHANNEL, 150 X 75 X 6.5 mm, 4.00 m LONG, TIS 116; PUNCH HOLE AS DETAIL A	–	2	——
4	เหล็กรูปรางน้ำรับสายล่อฟ้า ขนาด 100 X 50 X 5 มม. ยาว 2.25 ม. OVERHEAD GROUND WIRE BAYONET, CHANNEL STEEL, 100 X 50 X 5 mm, 2.25 m LONG	1	1	01000100 (6012)
5	เหล็กประกับคอน ขนาด 30 X 6 X 760 มม. BRACE, FLAT, FOR CROSSARM, 30 X 6 X 760 mm	2	–	01200001 (0120)
6	เหล็กประกับคอน ขนาด 40 X 6 X 1,000 มม. BRACE, FLAT, FOR CROSSARM, 40 X 6 X 1,000 mm	4	4	01200002 (0121)
7	เหล็กฉากรับคอนสาย ขนาด 50 X 50 X 6 มม. ช่วงกว้าง 1,800 มม. ดรอพ 450 มม. BRACE, ANGLE STEEL, 50 X 50 X 6 mm, 1,800 mm WIDE, 450 mm DROP	–	1	01200007 (0119)
8	สลักเกลียว M 16 X 170 มม. BOLT, MACHINE, M 16 X 170 mm	4	4	01110201 (0221)

กองวิศวกรรมไฟฟ้าและเครื่องกล
ฝ่ายวิศวกรรม

ผู้เขียน ...
ผู้สำรวจ
วิศวกร ...
หัวหน้าแผนก ...
ผู้อำนวยการกอง ...
ผู้อำนวยการฝ่าย ...

รองผู้ว่าการฝ่ายเทคนิค ...

การไฟฟ้าส่วนภูมิภาค

ผู้ว่าการ ... 29 ต.ค. 35

โครงสร้างเสาต้นเข้าปลายสายสองชั้น ระบบ 33 kV
3 – 4 วงจร

33 kV DOUBLE DEADEND STRUCTURE
3 – 4 CIRCUIT

ใช้แทนแผ่น
ถูกแทนโดยแผ่น
เขียนเสร็จวันที่ 9 ต.ค. 35
แก้แผ่นวันที่
มิติเป็น มิลลิเมตร
มาตราส่วน 1 : 30

แผนเลขที่ SA4-015/35011
แผ่นที่ 5 ของจำนวน 7 แผ่น

26 ต.ค. 2535

กางปะกอบเลขที่ ASSEMBLY NO. 3238

บัญชีวัสดุ
BILL OF MATERIAL

ลำดับที่ ITEM	รายละเอียด DESCRIPTION	จำนวน REQ'D I	จำนวน REQ'D II	วัสดุเลขที่ MAT. NO.
9	สลักเกลียว M 16 X 200 มม. BOLT, MACHINE, M 16 X 200 mm	–	2	01110202 (0222)
10	สลักเกลียว M 16 X 250 มม. BOLT, MACHINE, M 16 X 250 mm	5	5	01110203 (0223)
11	สลักเกลียว M 16 X 400 มม. BOLT, MACHINE, M 16 X 400 mm	–	1 or –	01110206 (0226)
12	สลักเกลียวห่วงกลม M 16 X 450 มม. BOLT, DOUBLE ARMING, ROUND EYE, M 16 X 450 mm	–	8 or 9	01130000 (0246)
13	สลักเกลียวห่วงกลม M 16 X 500 มม. BOLT, DOUBLE ARMING, ROUND EYE, M 16 X 500 mm	12	7	01130002 (0248)
14	สลักห่วงกลม M 16 X 200 มม. BOLT, ROUND EYE, M 16 X 200 mm	1	1	01140001 (0253)
15	แหวนสี่เหลี่ยมแบน 52 X 52 X 4.5 มม. รู Ø 18 มม. มอก. 258 WASHER, SQUARE, FLAT, 52 X 52 X 4.5 mm, HOLE Ø 18 mm, TIS 258	51	71	01180100 (0355)
16	นัทรูปห่วง M 16, DIN 582 NUT, EYE, M 16, DIN 582	8	13 or 11	01180001 (0345)
17	ลูกถ้วยก้านตรง 33 kV มอก. 279 แบบ ค (แบบ 56-3) พร้อมก้าน INSULATOR, PIN TYPE, 33 kV, TIS 279, TYPE C (CLASS 56-3) COMP. WITH PIN	15	18	03000002. 03100001
18	ลูกถ้วยแขวน มอก. 354 แบบ ง (แบบ 52-4) INSULATOR, SUSPENSION TYPE, TIS 354, TYPE D (CLASS 52-4)	54	72	03020002 (0415)
19	สเตรนแคล้มป์ สำหรับสายอะลูมิเนียม ขนาดตามต้องการ CLAMP, STRAIN, FOR Al CONDUCTOR ; SIZE AS REQUIRED	12	12	03110000 - 03110101
20	ทิมเบิลเดลวิส สำหรับปรีฟอร์มเข้าปลายสาย CLEVIS, THIMBLE, FOR PREFORMED DEADEND	6	12	03140011 (0428)
21	ปรีฟอร์มเข้าปลายสาย สำหรับเคเบิลอากาศอะลูมิเนียม 33 kV ขนาดตามต้องการ PREFORMED DEADEND, FOR 33 kV Al AERIAL CABLE ; SIZE AS REQUIRED	6	12	02260100 - 5928
22	ลวดอะลูมิเนียมแบน 1 X 10 มม. ความยาวตามต้องการ TAPE, ARMOUR, Al, 1 X 10 mm ; LENGTH AS REQUIRED	ม. m	ม. m	02200000 (0700)
23	ลวดอะลูมิเนียมกลม 4.0 มม. ความยาวตามต้องการ TIE WIRE, Al, 4.0 mm ; LENGTH AS REQUIRED	ม. m	ม. m	02200002 (0704)
24	หลอดต่อสายชนิดบีบไม่รับแรงดึง สายอะลูมิเนียมขนาดตามต้องการ CONNECTOR, SPLICE, COMPRESSION TYPE, TENSIONLESS, Al ; SIZE AS REQ'D	6	6	02410001 - 5 02410007
25	กายทิมเบิล สำหรับสายยึดโยง 50 – 95 ต.มม. THIMBLE, GUY, FOR STEEL WIRE 50 – 95 mm^2	4	6 or 5	01210304 (0150)
26	ยูแคล้มป์ สลัก 1 ตัว M 8 CLAMP, SINGLE U-BOLT, M 8	14	22 or 17	01230000 (0165)
27	สายยึดโยงแบบ GY-32 GUY ASSEMBLY, GY-32	3	3	

กองวิศวกรรมไฟฟ้าและเครื่องกล
ฝ่ายวิศวกรรม

ผู้เขียน ...
ผู้สำรวจ
วิศวกร ...
หัวหน้าแผนก ...
ผู้อำนวยการกอง ...
ผู้อำนวยการฝ่าย ...

รองผู้ว่าการฝ่ายเทคนิค
...

การไฟฟ้าส่วนภูมิภาค

ผู้ว่าการ ...

โครงสร้างเสาต้นเข้าปลายสายสองชั้น ระยบ 33 kV

3 – 4 วงจร

33 kV DOUBLE DEADEND STRUCTURE
3 – 4 CIRCUIT

ใช้แทนแบบ.....
ถูกแทนโดยแบบ.....
เขียนเสร็จวันที่ 9 ต.ค. 35
แก้แบบวันที่.....
มิติเป็น.....
มาตราส่วน.....

แบบเลขที่ SA4-015/35011
แผ่นที่ 6 ของจำนวน 7 แผ่น

26 MAR 253

การประกอบเลขที่ ASSEMBLY NO.	3238

	แบบอ้างอิง REFERENCE DRAWING	แบบเลขที่ DWG. NO.	การประกอบเลขที่ ASSEMBLY NO.
1	โครงสร้างเสาระบบจำหน่าย 33 kV, 3-4 วงจร 33 kV DISTRIBUTION POLE STRUCTURE, 3-4 CIRCUIT	IBI-015/34071	8282
2	โครงสร้างเสาต้นทางโค้ง ระบบ 33 kV มุม 60°-90°, 3-4 วงจร 33 kV ANGLE STRUCTURE, LINE ANGLE 60°-90°, 3-4 CIRCUIT	SA4-015/35012	
3	หลักเกณฑ์การใช้ลูกถ้วยแรงสูง ในบริเวณใกล้ฝั่งทะเล RECOMMENDATION FOR H.T. INSULATOR INSTALLATION, NEAR THE SEA COAST	SAI-015/24019	9502
4	การต่อสายเคเบิลอากาศแรงสูง COMPRESSION SLEEVE, FOR H.T. AERIAL CABLE	SAI-015/22020	9562
5	การต่อฝสายลวดเหล็กตีเกลียว STEEL STRANDED WIRE SPLICING	SAI-015/23053 SAI-015/28010	9563 9563A

หมายเหตุ

บัญชีวัสดุ :—

สดมภ์ I : สำหรับการติดตั้ง 3 วงจร
(สายเปลือย 2 วงจร และเคเบิลอากาศ 1 วงจร)

สดมภ์ II : สำหรับการติดตั้ง 4 วงจร
(สายเปลือย 2 วงจร และเคเบิลอากาศ 2 วงจร)

NOTES

BILL OF MATERIAL :—

COLUMN I : FOR 3 CIRCUIT INSTALLATION
(2-CIRCUIT BARE CONDUCTOR AND 1-CIRCUIT AERIAL CABLE)

COLUMN II : FOR 4 CIRCUIT INSTALLATION
(2-CIRCUIT BARE CONDUCTOR AND 2-CIRCUIT AERIAL CABLE)

คำชี้แจง

เนื่องจากเป็นโครงสร้างสายประธาน จึงกำหนดให้ติดตั้งลูกถ้วยก้านตรงบนคอนทั้งสองด้าน ในวงจรสายเปลือย เพื่อแก้ปัญหาอันเกิดจากนก

EXPLANATION

BECAUSE IT IS THE MAIN LINE STRUCTURE, THE PIN TYPE INSULATORS ARE SPECIFIED INSTALL ON THE BOTH SIDES OF CROSSARM, IN BARE LINE CIRCUITS, TO AVOID THE PROBLEM DUE TO BIRDS, THEREFORE .

กองวิศวกรรมไฟฟ้าและเครื่องกล
ฝ่ายวิศวกรรม

ผู้เขียน ...
ผู้สำรวจ ...
วิศวกร ...
หัวหน้าแผนก ...
ผู้อำนวยการกอง ...
ผู้อำนวยการฝ่าย ...

ของผู้ว่าการฝ่ายเทคนิค ...

การไฟฟ้าส่วนภูมิภาค

ผู้ว่าการ ... 25 ต.ค. 35

โครงสร้างเสาต้นเข้าปลายสายสองข้าง ระบบ 33 kV
3 – 4 วงจร

33 kV DOUBLE DEADEND STRUCTURE
3 – 4 CIRCUIT

ใช้แทนแบบ ...
ถูกแทนโดยแบบ ...
เขียนเสร็จวันที่ 9 ต.ค. 35
แก้แบบวันที่ ...
มิติเป็น ...
มาตราส่วน ...

แบบเลขที่ SA4-015/35011
แผ่นที่ 7 ของจำนวน 7 แผ่น

26 ต.ค. 2535