
การประกอบเลขที่ ASSEMBLY NO. 5 2 5 9 A

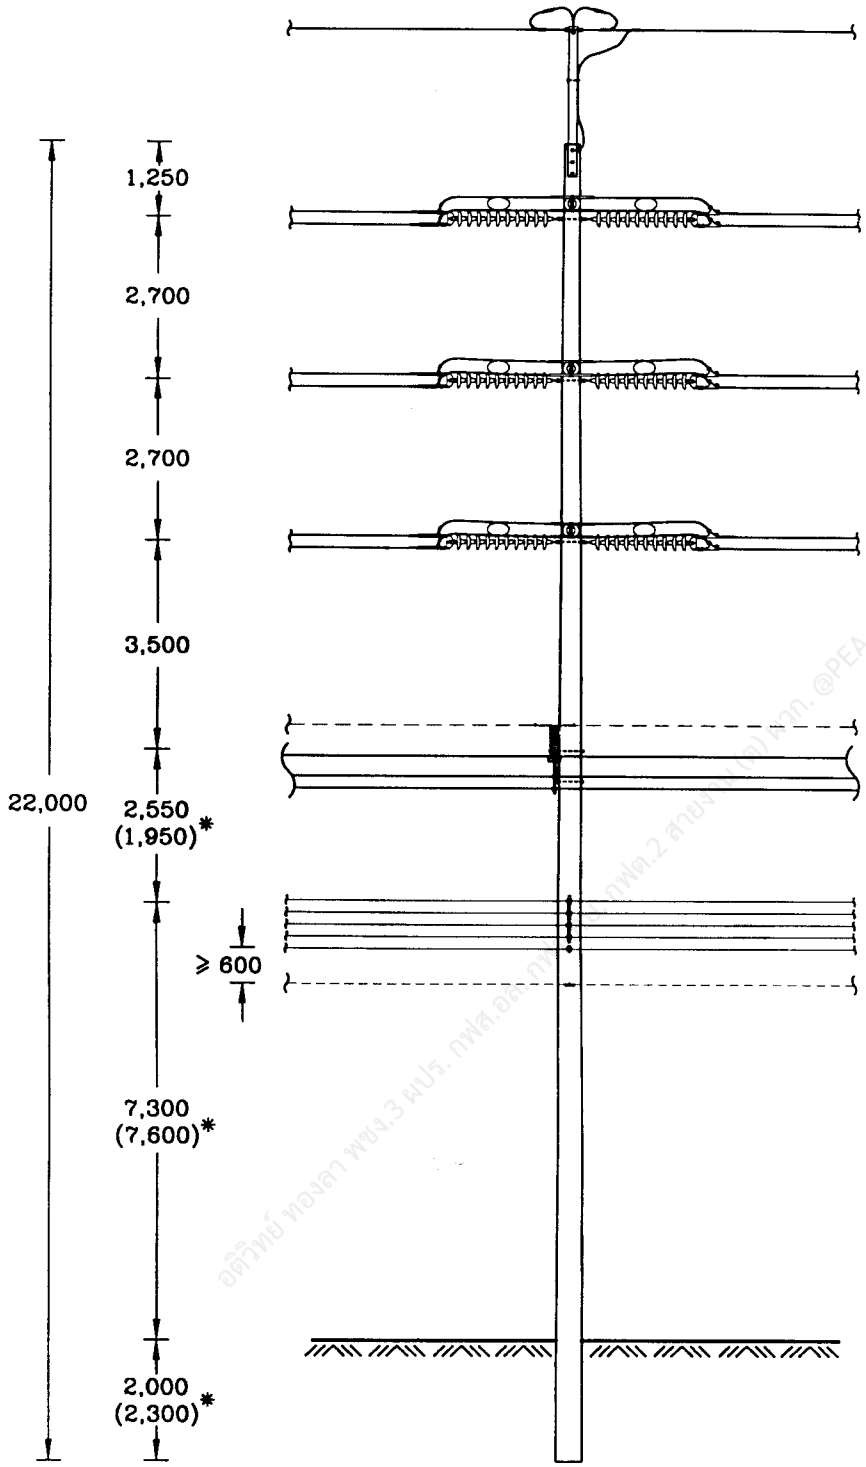


* ดูหมายเหตุ SEE NOTE 1

กองมาตรฐานระบบไฟฟ้า ฝ่ายมาตรฐานและความปลอดภัย	การไฟฟ้าส่วนภูมิภาค	ใช้แทนแบบ ..... ถูกแทนโดยแบบ .....
ผู้เขียน ...สมชาย..... ผู้สำรวจ ..... วิศวกร ..... หัวหน้าแผนก ..... ผู้อำนวยการกอง ..... ผู้อำนวยการฝ่าย	ผู้ว่าการ ..... 115 kV วงจรเดี่ยว สายไฟฟ้า 27 ส.ค. 2547 เสาเดี่ยว (ชนิดมีกราวด์เพลทในเสา) สำหรับแยกสาย แบบ SD-TL-1	เขียนเสร็จวันที่ 2 มิ.ย. 2547 แก้แบบวันที่ ..... มิติเป็น ...มิลลิเมตร..... มาตราส่วน ...1:125.....
รองผู้ว่าการฝ่ายวางแผนและพัฒนาระบบไฟฟ้า	115 kV SINGLE CIRCUIT DOUBLE CONDUCTOR SINGLE POLE (WITH GROUND PLATE IN POLE), TAP LINE STRUCTURE TYPE SD-TL-1	แบบเลขที่ SA1-015/47015 แผ่นที่ 1 ของจำนวน 3 แผ่น

27 ส.ค. 2547

การประกอบเลขที่ ASSEMBLY NO. 5 2 5 9 A

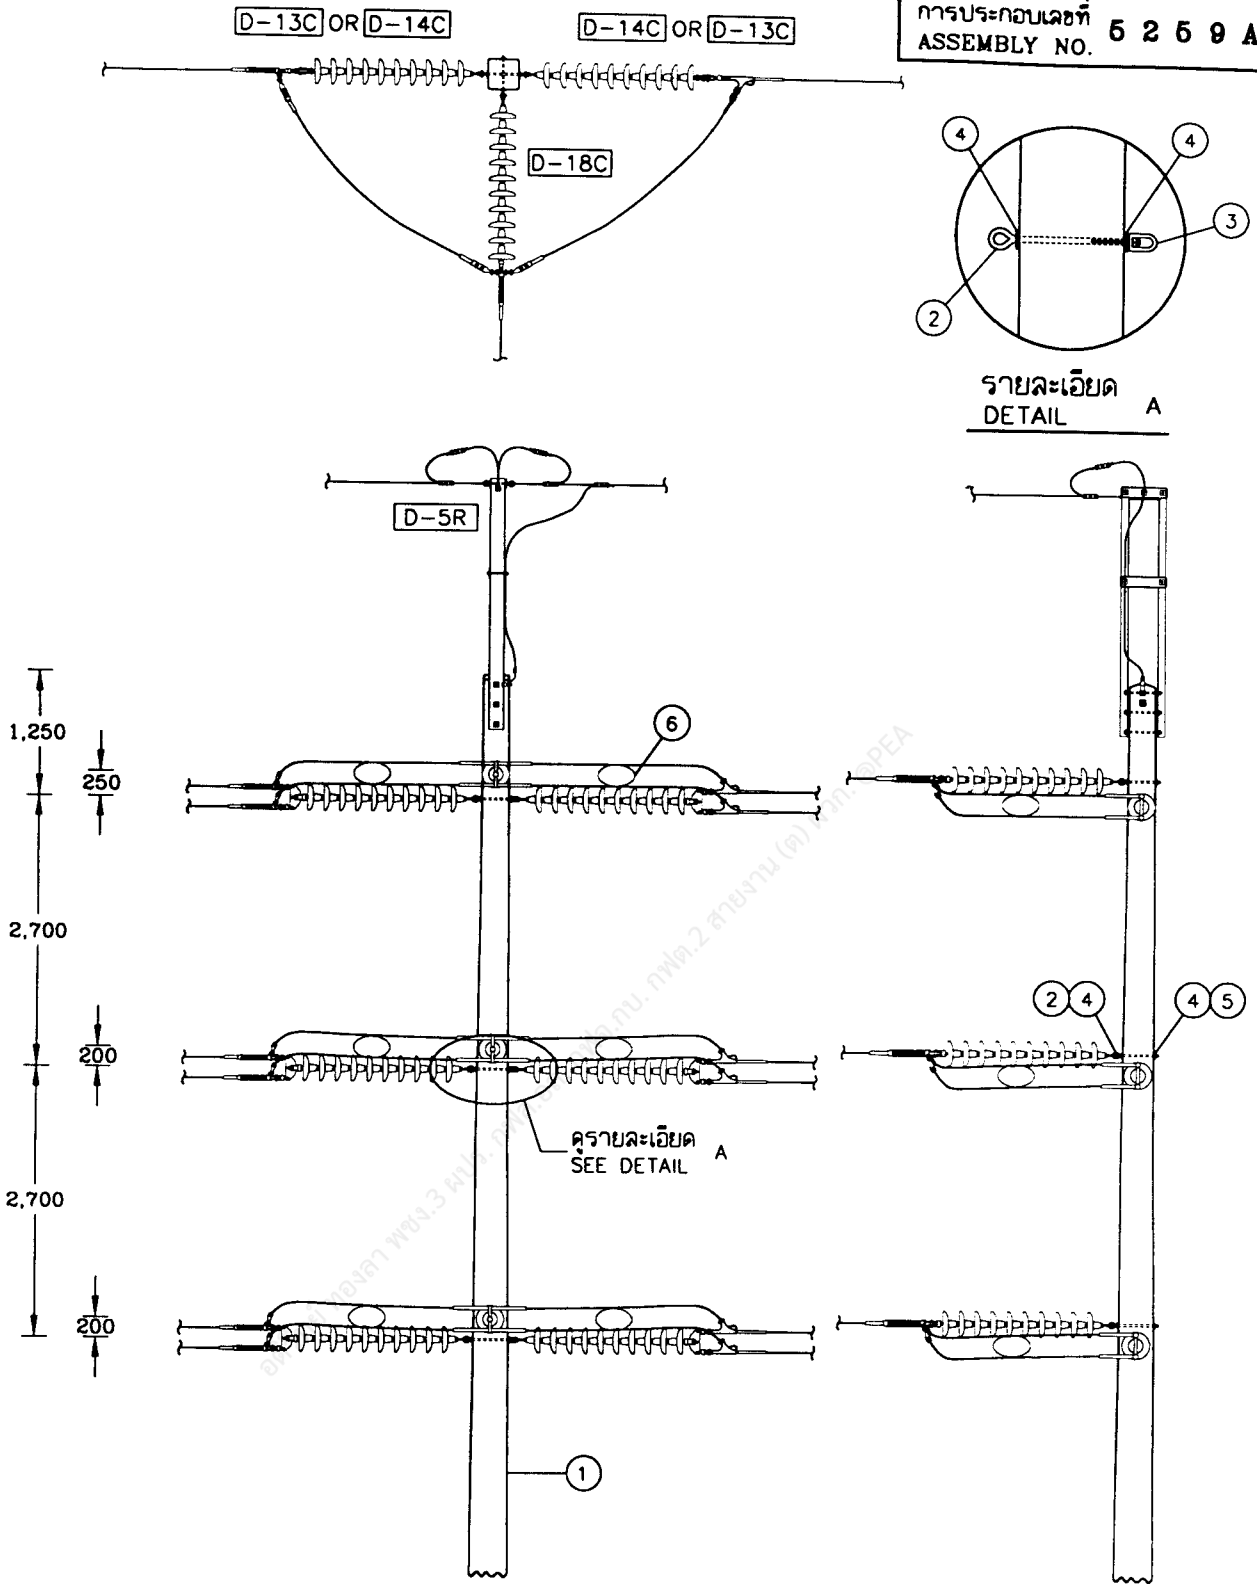

กองมาตรฐานระบบไฟฟ้า ฝ่ายมาตรฐานและความปลอดภัย	การไฟฟ้าส่วนภูมิภาค	ใช้แทนแบบ ..... ถูกแทนโดยแบบ .....
ผู้เขียน ...สมชาย..... ผู้สำรวจ ..... วิศวกร ..... หัวหน้าแผนก ..... ผู้อำนวยการกอง ..... ผู้อำนวยการฝ่าย	ผู้ว่าการ	เขียนเสร็จวันที่ 2 มิ.ย. 2547 แก้แบบวันที่ ..... มิติเป็น ...มิลลิเมตร..... มาตราส่วน ..1:75.....
รองผู้ว่าการฝ่ายวางแผนและพัฒนาระบบไฟฟ้า	115 kV วงจรเดี่ยว สายไฟฟ้าคู่ เสาเดี่ยว (ชนิดมีกราวด์เพลทในเสา) สำหรับแยกสาย แบบ SD-TL-1 115 kV SINGLE CIRCUIT DOUBLE CONDUCTOR SINGLE POLE (WITH GROUND PLATE IN POLE), TAP LINE STRUCTURE TYPE SD-TL-1	แบบเลขที่ SA1-015/47015 แผ่นที่ 2 ของจำนวน 3 แผ่น

27 ส.ค. 2547

การประกอบเลขที่ ASSEMBLY NO. 5259A

บัญชีวัสดุ
BILL OF MATERIAL

ลำดับที่ ITEM	รายละเอียด DESCRIPTION	จำนวน REQ.D	วัสดุเลขที่ MAT. NO.
1	เสา คอร. ยาว 22.00 ม. ชนิดมีกราวด์เพลทในเสา POLE, CONCRETE, 22.00 m LONG, WITH GROUND PLATE IN POLE	1	00010015
2	สลักหวงโอแวล M 20x350 มม. BOLT, OVAL EYE, M 20x350 mm	6	01150100
3	อายเล็ท สำหรับสลักเกลียว M 20 EYELET, FOR BOLT M 20	3	01180002
4	แหวนสี่เหลี่ยมแบน 62x62x6 มม. รู ø22 มม. มอก.258 WASHER, SQUARE, FLAT, 62x62x6 mm, HOLE ø22 mm, TIS 258	12	01180101
5	แหวนสปริง M 20 มอก. 259 WASHER, LOCK, M 20, TIS 259	3	01180302
6	บริฟอร์มแยกสาย SPACER, HELICAL ROD, PREFORMED	6	02240000
	รายละเอียด DETAIL		
D-13C	การประกอบลูกถ้วยแขวน SUSPENSION INSULATOR ASSEMBLY	3	
D-14C	การประกอบลูกถ้วยแขวน SUSPENSION INSULATOR ASSEMBLY	3	
D-18C	การประกอบลูกถ้วยแขวน SUSPENSION INSULATOR ASSEMBLY	3	
D-5R	การประกอบสายลอฟ้า OVERHEAD GROUND WIRE ASSEMBLY	1	
D-10A	ฐานรากเสา POLE FOUNDATION	1	
D-25	การต่อลงดิน GROUNDING	1	

หมายเหตุ

1.* กรณีก่อสร้างในพื้นที่เขตทางหลวง ให้ใช้ค่าระยะห่างตามแนวดิ่งในวงเล็บ โดยดูรายละเอียดเพิ่มเติมในแบบเลขที่ SA1-015/43012 (การประกอบเลขที่ 5687)

2. ระยะห่างระหว่างช่วงเสาของโครงสร้างสายส่ง 115 kV โครงสร้างเสาสำหรับแยกสาย ให้ดูแบบเลขที่ SA1-015/47010 (การประกอบเลขที่ 5162)

NOTES

1.* IN CASE OF CONSTRUCTION IN HIGHWAY AREA, USE A VERTICAL CLEARANCE VALUE IN THE PARENTHESIS, FOR ADDITIONAL DETAIL, SEE DWG NO. SA1-015/43012 (ASSEMBLY NO. 5687) .

2. SPAN LENGTHS FOR 115 kV CONSTRUCTION STRUCTURE, TAP LINE STRUCTURE, SEE DWG. NO. SA1-015/47010 (ASSEMBLY NO. 5162) .

กองมาตรฐานระบบไฟฟ้า ฝ่ายมาตรฐานและความปลอดภัย	การไฟฟ้าส่วนภูมิภาค	ใช้แทนแบบ ..... ถูกแทนโดยแบบ .....
ผู้เขียน สมชาย ..... ผู้สำรวจ ..... วิศวกร ..... หัวหน้าแผนก ..... ผู้อำนวยการกอง ..... ผู้อำนวยการฝ่าย	ผู้ว่าการ ..... 115 kV วงจรเดี่ยว สายไฟฟ้า 27 ส.ค. 2547 เสาเดี่ยว (ชนิดมีกราวด์เพลทในเสา) สำหรับแยกสาย แบบ SD-TL-1	เขียนเสร็จวันที่ 2 มิ.ย. 2547 แก้แบบวันที่ ..... มิติเป็น ..... มาตราส่วน .....
รองผู้ว่าการฝ่ายวางแผนและพัฒนาระบบไฟฟ้า	115 kV SINGLE CIRCUIT DOUBLE CONDUCTOR SINGLE POLE (WITH GROUND PLATE IN POLE), TAP LINE STRUCTURE TYPE SD-TL-1	แบบเลขที่ SA1-015/47015 แผ่นที่ 3 ของจำนวน 3 แผ่น

27 ส.ค. 2547