



กากประกอบเลขที่ 3229
ASSEMBLY NO.

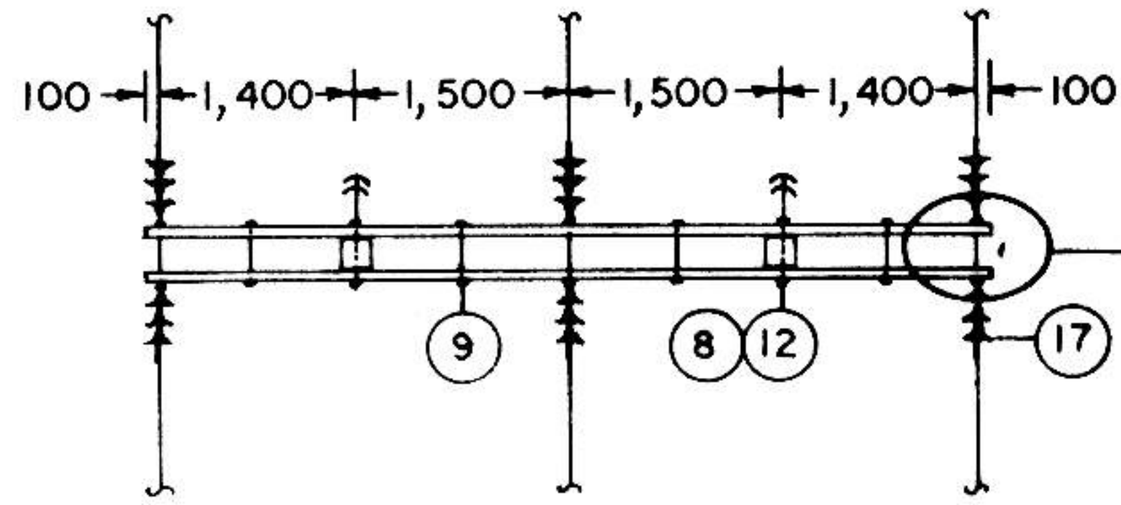

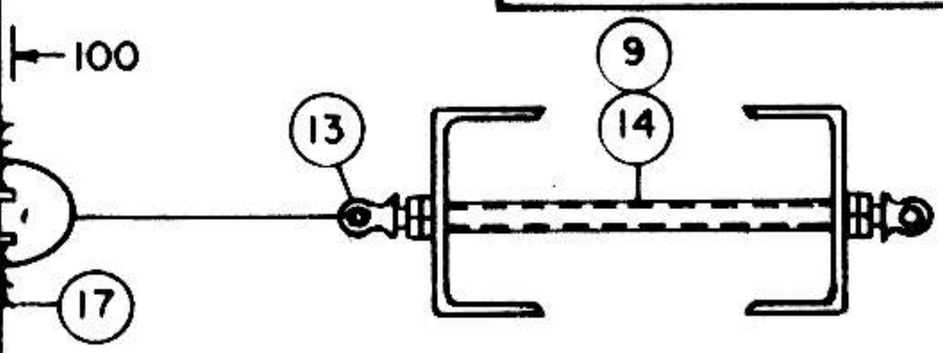


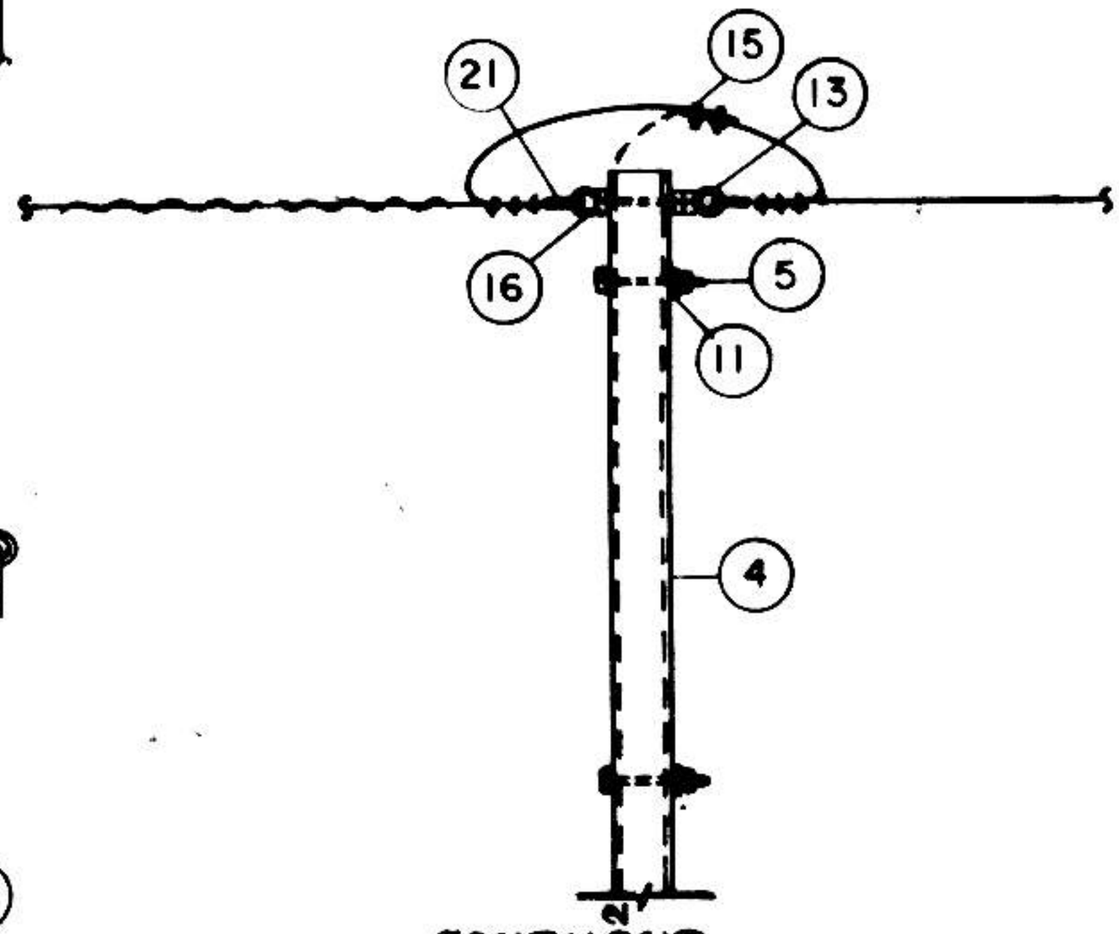


รายละเอียด A
DETAIL A

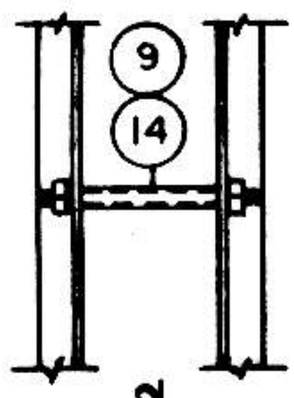

รายละเอียด B
DETAIL B

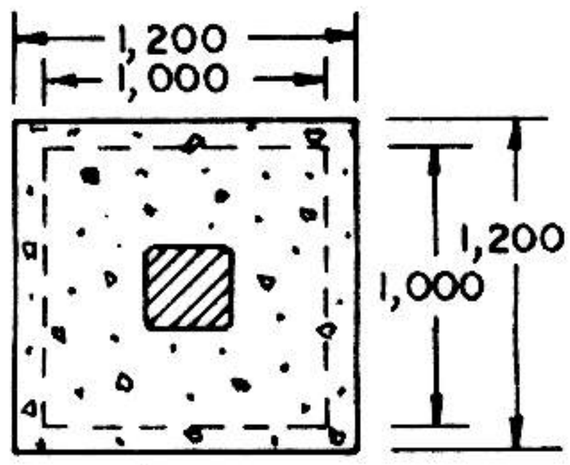

รูปตัด C–C
SECTION C–C

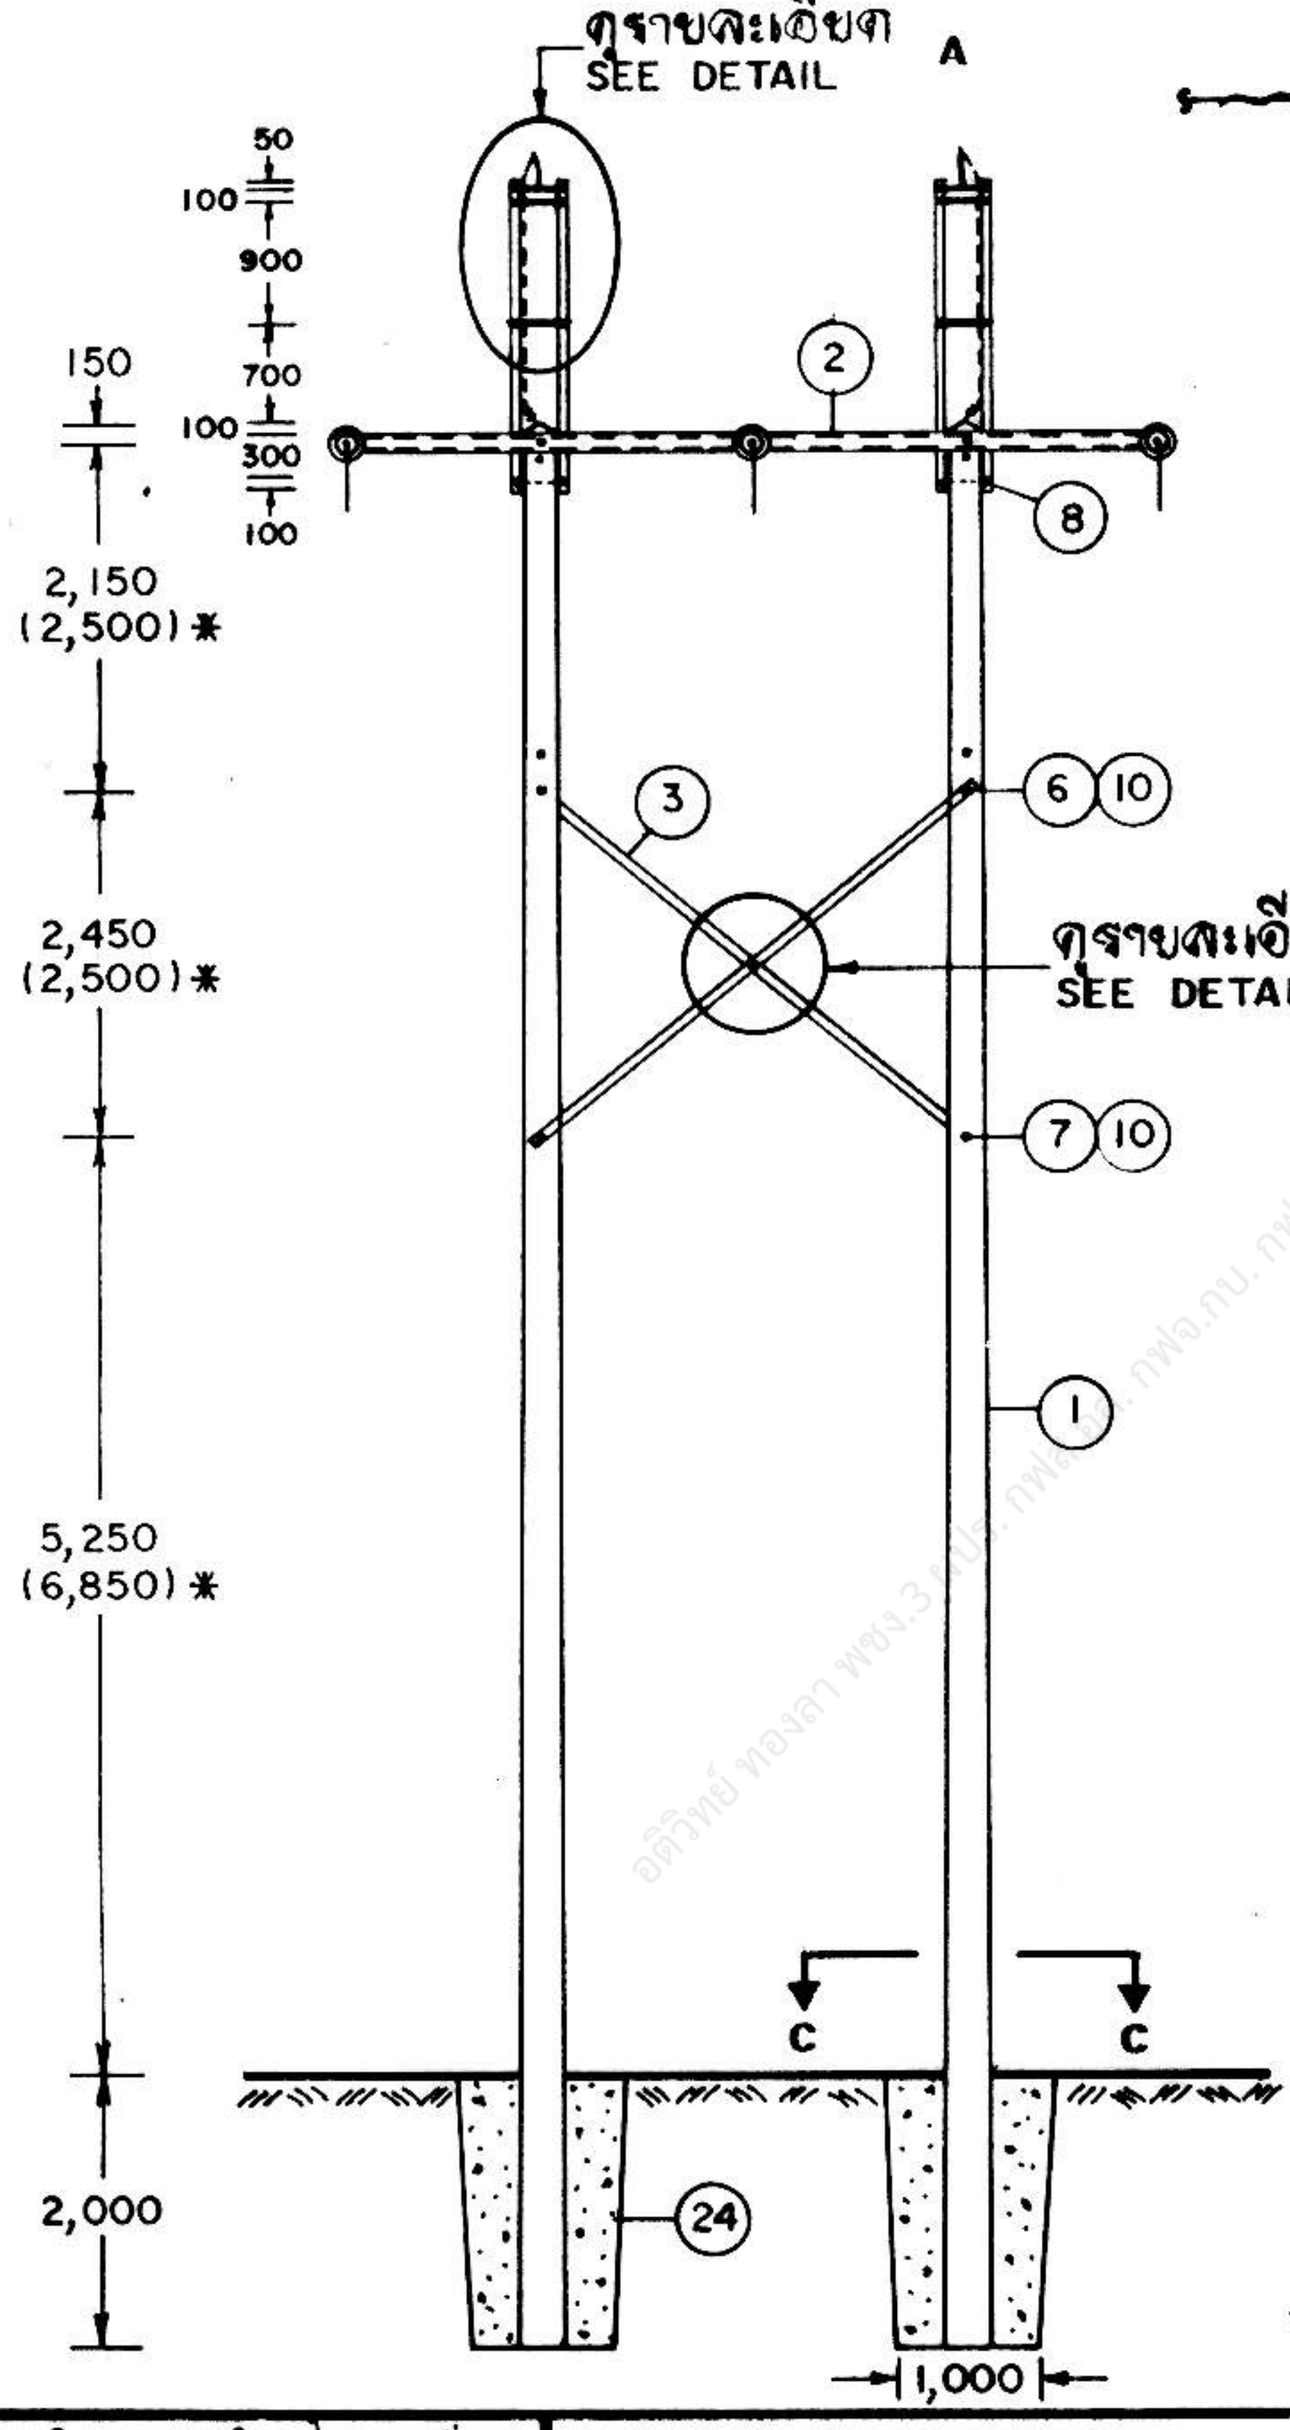



* สำหรับเสาคอนกรีต 14 ม.
FOR 14 m CONCRETE POLE

กองวิศวกรรมไฟฟ้าและเครื่องกล ฝ่ายวิศวกรรม	การไฟฟ้าส่วนภูมิภาค	ตัวแทนแบบ ลูกแทนโดยแบบ เขียนเสร็จวันที่ 8 มิ.ย. 33 แก้แบบวันที่
ผู้เขียน ผู้สำรวจ วิศวกร หัวหน้าแผนก ผู้อำนวยการกอง ผู้อำนวยการฝ่าย	ผู้จ่าการ 15 ก.ค. 33	มิติเป็น มิลลิเมตร มาตราส่วน 1:25, 1:50, 1:100
ของผู้จ่าการฝ่ายเทคนิค	มาตรฐานการก่อสร้าง ระบบ 22 kV และ 33 kV ระยะช่วงเสา 200 — 300 ม. 22 kV AND 33 kV STANDARD CONSTRUCTION SPAN OF 200 — 300 m	แบบเลขที่ SA1-015/33015 แผ่นที่ 1 ของจำนวน 5 แผ่น


30 ก.ค. 2533

การประกอบเลขที่ 3229
ASSEMBLY NO.

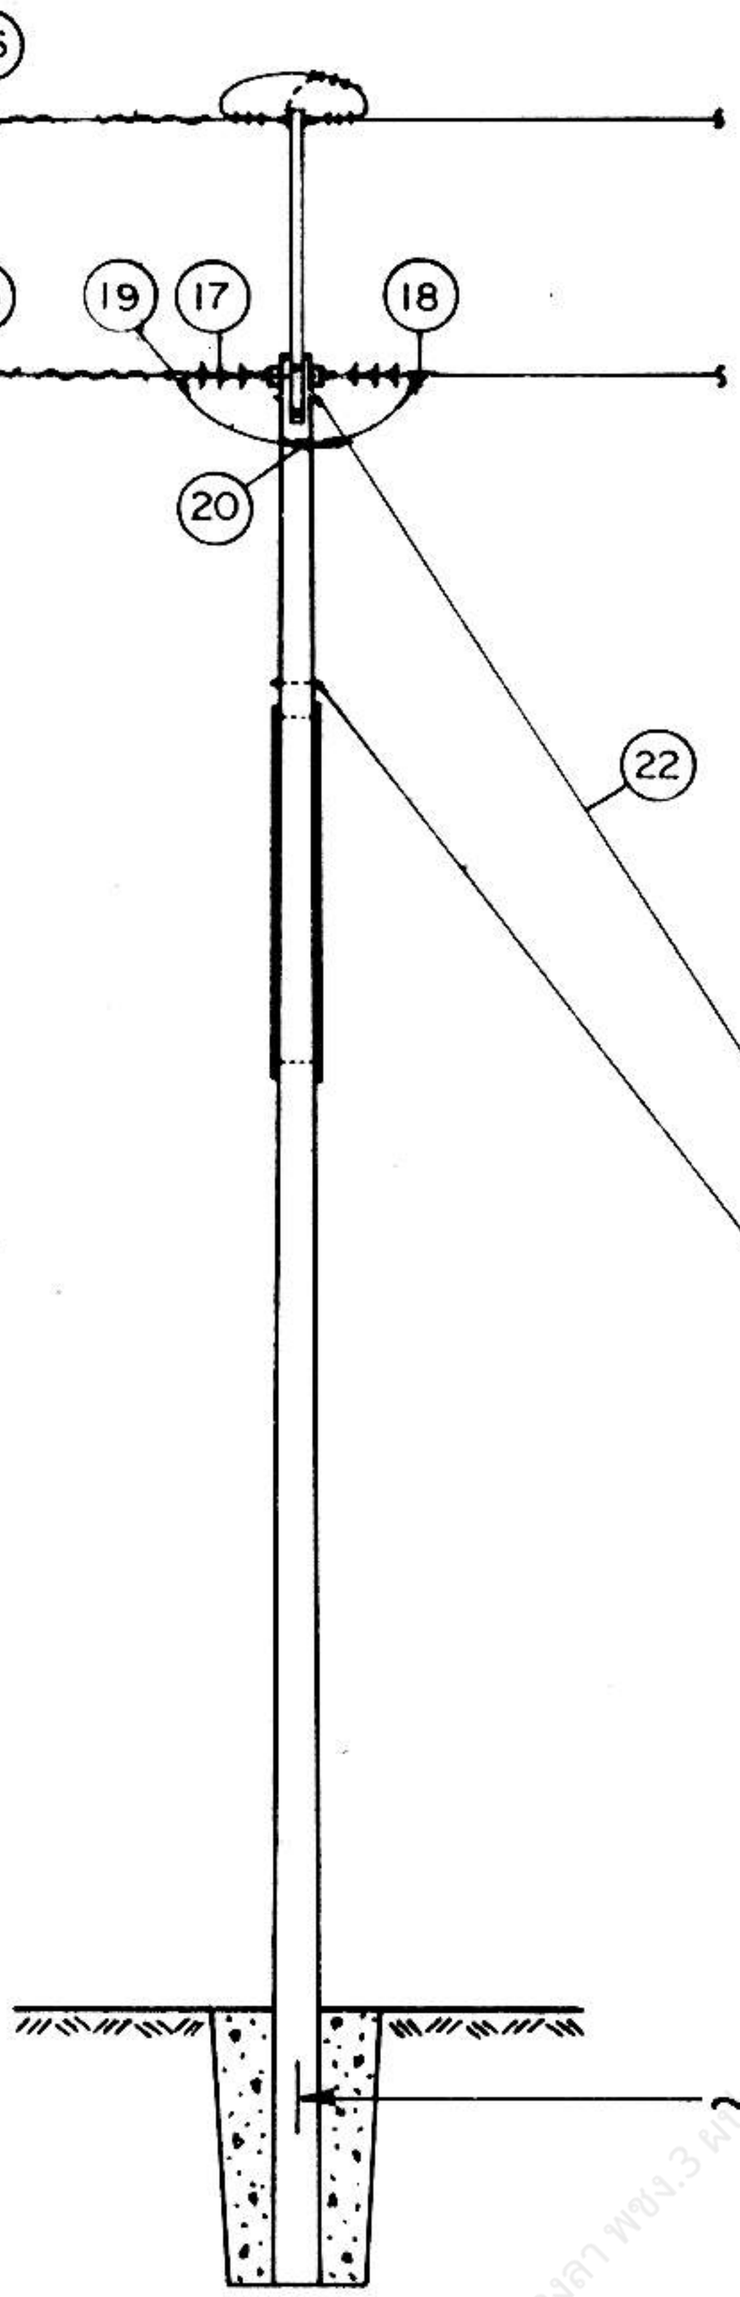

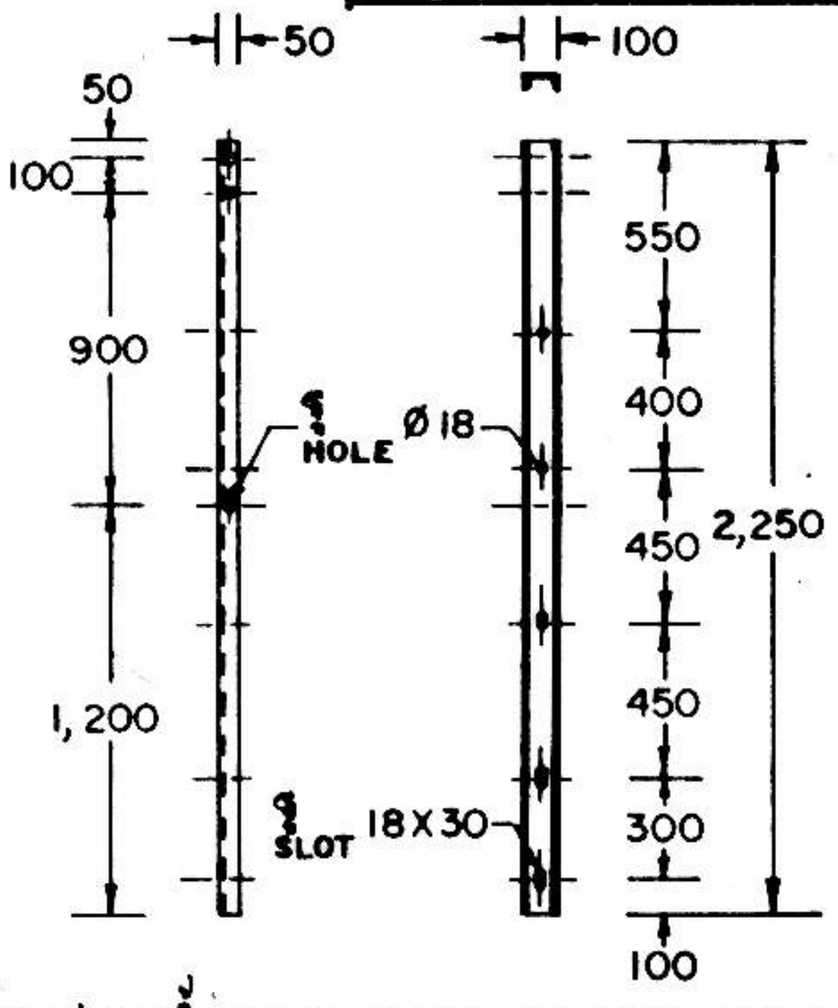

④ เหล็กรูปรางน้ำ ขนาด 100 x 50 x 5 มม. ยาว 2.25 ม.
(สามารถทำตากวัสดุเลขที่ 6012 ได้)
CHANNEL STEEL, 100 x 50 x 5 mm, 2.25 m LONG
(MAY BE MADE FROM MAT. NO. 6012)

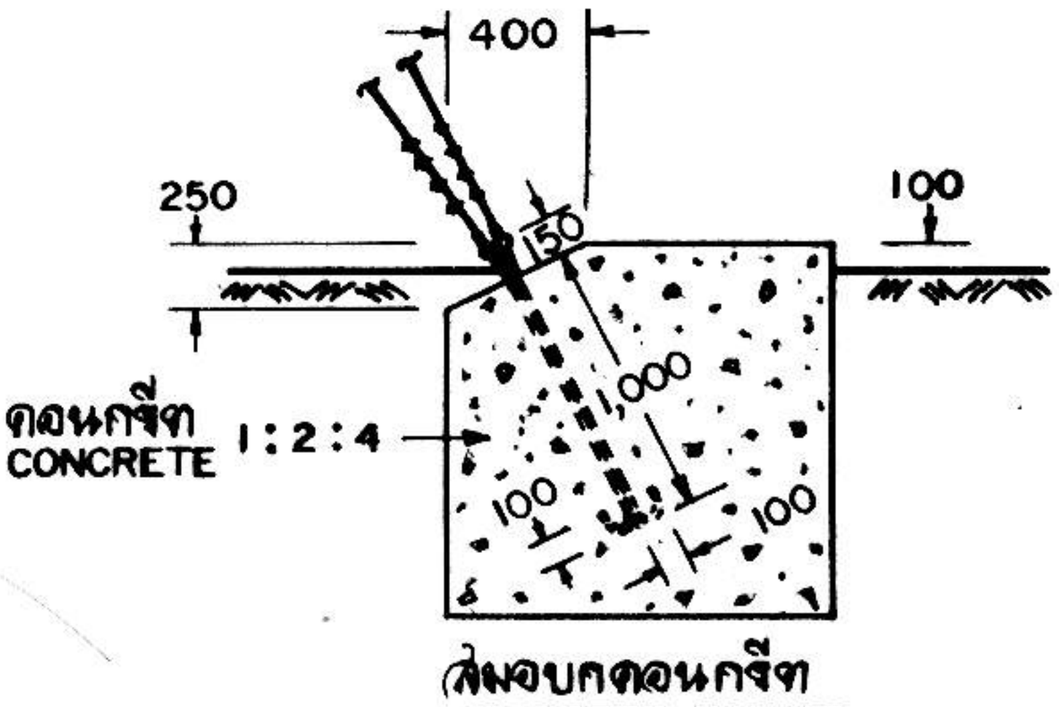

สมอบกคอนกรีต
CONCRETE ANCHOR

กองวิศวกรรมไฟฟ้าและเครื่องกล ฝ่ายวิศวกรรม	การไฟฟ้าส่วนภูมิภาค	ใช้แทนแบบ ..... ถูกแทนโดยแบบ .....
ผู้เขียน กฟภ. ผู้ตรวจ ..... วิศวกร สมศักดิ์ หัวหน้าแผนก ..... ผู้อำนวยการกอง ..... ผู้อำนวยการฝ่าย	ผู้จ่าการ ..... มาตรฐานการก่อสร้างระบบ 22 kV และ 33 kV ระยะช่วงเสา 200—300 ม.	เขียนเสร็จวันที่ 8 มิ.ย. 33 แก้แบบวันที่ ..... มิติเป็น มิลลิเมตร มาตราส่วน 1:40, 1:50, 1:100
ของผู้จ่าการฝ่ายเทคนิค	22 kV AND 33 kV STANDARD CONSTRUCTION SPAN OF 200 — 300 m	แบบเลขที่ SAI-015/33015 แผ่นที่ 2 จากจำนวน 5 แผ่น

30 ก.ค. 2533

การประกอบเลขที่ ASSEMBLY NO. 3229

บัญชีวัสดุ
BILL OF MATERIAL

ลำดับที่ ITEM	รายละเอียด DESCRIPTION	จำนวน REQ'D	วัสดุเลขที่ MAT. NO.
1	เสาคอนกรีต 12 ม. หรือ 14 ม. CONCRETE POLE, 12 m OR 14 m	2	00010004 or 00010006
2	เหล็กรูปรางน้ำ ขนาด 150 X 75 X 6.5 มม. ยาว 6.00 ม. STEEL, CHANNEL, 150 X 75 X 6.5 mm, 6.00 m LONG	2	01000303 (0117)
3	เหล็กฉาก ขนาด 75 X 75 X 6 มม. ยาว 4.10 ม. STEEL, ANGLE, 75 X 75 X 6 mm, 4.10 m LONG	2	01010101 (0122)
4	เหล็กรูปรางน้ำ ขนาด 100 X 50 X 5 มม. ยาว 2.25 ม. STEEL, CHANNEL, 100 X 50 X 5 mm, 2.25 m LONG	4	
5	สลักเกลียว M 16 X 130 มม. BOLT, MACHINE, M 16 X 130 mm	12	01110200 (0220)
6	สลักเกลียว M 16 X 250 มม. BOLT, MACHINE, M 16 X 250 mm	2	01110203 (0223)
7	สลักเกลียว M 16 X 300 มม. BOLT, MACHINE, M 16 X 300 mm	2	01110204 (0224)
8	สลักเกลียว M 16 X 350 มม. BOLT, MACHINE, M 16 X 350 mm	6	01110205 (0225)
9	สลักเกลียวตลอด M 16 X 400 มม. BOLT, DOUBLE ARMING, M 16 X 400 mm	8	01120000 (0243)
10	แหวนสี่เหลี่ยมแบน 52 X 52 X 4.5 มม. รู ø 18 มม. มอก. 258 WASHER, SQUARE, FLAT 52 X 52 X 4.5 mm HOLE ø 18 mm TIS 258	4	01180100 (0355)
11	เหล็กแผ่น ขนาด 40 X 6 มม. ยาว 320 มม. STEEL, PLATE, 40 X 6 mm, 320 mm LONG	12	
12	แหวนสปริง M 16 มอก. 259 WASHER, LOCK, M 16 TIS 259	2	01180301 (0365)
13	น๊อทรูปห่วง M 16 DIN 582 NUT, EYE M 16 DIN 582	8	01180001 (0345)
14	ท่อเหล็ก ขนาด ø 20 มม. ตามยาวตามต้องการ PIPE, STEEL ø 20 mm LENGTH AS REQ'D	8	01050005 01050008
15	ยูแคลมป์ สลัก 1 ด้าน M 8 CLAMP, SINGLE U-BOLT M 8	20	01230000 (0165)
16	สลักเกลียวห่วงกลม M 16 X 200 มม. BOLT, ROUND EYE, M 16 X 200 mm	2	01140001 (0253)
17	ลูกถ้วยแขวน มอก. 354 แบบ ก หรือ แบบ ง (แบบ 52-1 หรือ 52-4) INSULATOR, SUSPENSION, TIS 354, TYPE A OR TYPE D (CLASS 52-1 OR 52-4)	18	03020000 03020002
18	สเตรนแคลมป์ สำหรับสายอะลูมิเนียม CLAMP, STRAIN, FOR AI CONDUCTOR	3	03110000 - 03110101
19	สเตรนแคลมป์ สำหรับสายอะลูมิเนียมแกนเหล็ก และสายอะลูมิเนียมเกือ CLAMP, STRAIN, FOR ACSR AND AI-ALLOY	3	03110000 - 03110101
20	พีจี คอนเนคเตอร์ สำหรับสายอะลูมิเนียม อะลูมิเนียมผสมลอยและอะลูมิเนียมแกนเหล็ก CONNECTOR, PARALLEL GROOVE FOR AI, AI-ALLOY AND ACSR	6	02300103 - 02300104

กองวิศวกรรมไฟฟ้าและเครื่องกล ฝ่ายวิศวกรรม	การไฟฟ้าส่วนภูมิภาค	ใช้แทนแบบ ..... ถูกแทนโดยแบบ .....
ผู้เขียน ดมทอ. ผู้สำรวจ ..... วิศวกร ..... หัวหน้าแผนก ..... ผู้อำนวยการกอง ..... ผู้อำนวยการฝ่าย	ผู้จ่าการ ..... มาตรฐานการก่อสร้าง ระบบ 22 kV และ 33 kV ระยะช่วงเสา 200 — 300 ม.	เขียนเสร็จวันที่ 8 มิ.ย. 33 แก้แบบวันที่ ..... มิติเป็น ..... มาตราส่วน .....
ของผู้จ่าการฝ่ายเทคนิค	22 kV AND 33 kV STANDARD CONSTRUCTION SPAN OF 200 — 300 m	แบบเลขที่ SAI-015/33015 แผ่นที่ 3 จากจำนวน 5 แผ่น

3-0 ก.ค. 2533

การประกอบเลขที่ ASSEMBLY NO.	3229

บัญชีวัสดุ
BILL OF MATERIAL

ลำดับที่ ITEM	รายละเอียด DESCRIPTION	จำนวน REQ'D	วัสดุเลขที่ MAT. NO.
21	กายทิมเบิล สำหรับสายยึดโยง 50–95 ต.มม. THIMBLE, GUY, FOR STEEL WIRE 50–95 mm^2	4	01210304 (0150)
22	สายยึดโยง GY–21 หรือ GY–32 (ลวดเหล็กตีเกลียว 95 ต.มม. ไม่รวมสมอบก) GUY, GY–21 OR GY–32 (STEEL STRANDED WIRE 95 mm^2, ANCHOR NOT INCLUDED)	4	—
23	สมอบกคอนกรีต (คอนกรีต 1 : 2 : 4) CONCRETE ANCHOR (CONCRETE 1 : 2 : 4)	2	—
24	คอนกรีต 1 : 3 : 5 CONCRETE 1 : 3 : 5	ม.^{3} m^3	—
25	สไปเรลไวเบรชั่น แดมเปอร์ SPIRAL VIBRATION DAMPER	6	02200102 02200103
26	สไปเรลไวเบรชั่น แดมเปอร์ สำหรับลวดเหล็กตีเกลียว 25 ต.มม. SPIRAL VIBRATION DAMPER FOR 25 mm^2 STEEL STRANDED WIRE	2	02200100 (0903)

ข้อกำหนด
REGULATIONS

ชนิด และขนาด ของสายไฟฟ้า ต.มม. TYPE AND SIZE OF COND. mm^2	ระยะช่วงเสา สูงสุด ม. MAXIMUM SPAN LENGTH m	ระยะหย่อนยานต่ำสุด ของสายไฟฟ้าทุกเส้น ม. MINIMUN SAG OF ALL CONDUCTORS m	จำนวนสายยึดโยง (ลวดเหล็กตีเกลียว 95 ต.มม.) NO.OF GUY WIRE SETS (95 mm^2 STEEL STRANDED WIRE)	ขนาดของสมอบก คอนกรีต ม. SIZE OF CONCRETE ANCHOR m
ACSR 95/15	300	8	2	1.35 X 1.35 X 1.35
ACSR 120/20	260	7		
ACSR 185/30	240	6		1.50 X 1.50 X 1.50
AA 95	300	8		1.20 X 1.20 X 1.20
AA 120	260	7		
AA 185	240	6		1.35 X 1.35 X 1.35

กองวิศวกรรมไฟฟ้าและเครื่องกล ฝ่ายวิศวกรรม	การไฟฟ้าส่วนภูมิภาค	ใช้แทนแบบ ..... ถูกแทนโดยแบบ ..... เขียนแล้วเสร็จวันที่ 8 มิ.ย. 33 แก้แบบวันที่ ..... มิติเป็น ..... มาตราส่วน .....
ผู้เขียน .... ผู้ตรวจ .... วิศวกร .... หัวหน้าแผนก .... ผู้อำนวยการกอง .... ผู้อำนวยการฝ่าย	ผู้จ่ายการ .... 1 มิ.ย. 33	
ของผู้จ่ายการฝ่ายเทคนิค	มาตรฐานการก่อสร้างระบบ 22 kV และ 33 kV ระยะช่วงเสา 200 — 300 ม. 22 kV AND 33 kV STANDARD CONSTRUCTION SPAN OF 200 — 300 m	แบบเลขที่ SAI–015/33015 แผ่นที่ 4 ของจำนวน 5 แผ่น

30 ก.ค. 2533

กากบาทแสดงแบบเลขที่ ASSEMBLY NO.	3229

หมายเหตุ

1. สายล่อฟ้าใช้ลวดเหล็กตีเกลียว 25 ต.มม.
2. สายไฟฟ้าต้องมีระดับความสูงเหนือพื้นดินไม่น้อยกว่า 5.20 ม.
3. สายไฟฟ้าต้องมีระดับความสูงเหนือยอดของต้นไม้ ไม่น้อยกว่า 2.10 ม.
4. สำหรับระบบ 22 kV ที่ไม่มีสายล่อฟ้า ให้เปลี่ยนแปลงรายการวัสดุ ดังนี้ :
   - ตัดรายการวัสดุลำดับที่ 4, 5, 11, 15, 16 และ 21 ออก
   - ลดจำนวนรายการวัสดุลำดับที่ 8 เหลือ 2 ชุด
   - ลดจำนวนรายการวัสดุลำดับที่ 13 เหลือ 6 ชุด
5. ACSR หมายถึงสายอะลูมิเนียมแกนเหล็ก

   AA หมายถึงสายอะลูมิเนียมเจือ

NOTES

1. USE STEEL STRANDED WIRE 25 mm^2 AS OVERHEAD GROUND WIRE .
2. CONDUCTORS SHALL BE ABOVE GROUND OF NOT LESS THAN 5.20 m .
3. CONDUCTORS SHALL BE ABOVE TOP OF TREES OF NOT LESS THAN 2.10 m .
4. FOR 22 kV SYSTEM, WITHOUT OHGW, MUST CHANGED THE MATERIAL AS FOLLOWS :
   - OMIT THE MATERIAL ITEMS 4, 5, 11, 15, 16, AND 21 .
   - REDUCE THE MATERIAL ITEM 8 TO 2 SETS.
   - REDUCE THE MATERIAL ITEM 13 TO 6 SETS.
5. ACSR IS ALUMINIUM CONDUCTOR, STEEL REINFORCED .

   AA IS ALL ALUMINIUM ALLOY CONDUCTOR .

อดิวิทย์ ทองดา พชง.3 ผปร. กฟส.อด.

กองวิศวกรรมไฟฟ้าและเครื่องกล ฝ่ายวิศวกรรม	การไฟฟ้าส่วนภูมิภาค	ใช้แทนแบบ ถูกแทนโดยแบบ เขียนเสร็จวันที่ 8 มิ.ย. 33 แก้แบบวันที่ มิติเป็น มาตราส่วน
ผู้เขียน ONNO. ผู้สำรวจ วิศวกร สมพร หัวหน้าแผนก สิทธิพงษ์ ผู้อำนวยการกอง รักษ์ ผู้อำนวยการฝ่าย	ผู้จ่ากการ 1 ธ.ค. 33	มาตรฐานการก่อสร้างระบบ 22 kV และ 33 kV ระยะช่วงเสา 200—300 ม.
รองผู้จ่ากการฝ่ายเทคนิค	22 kV AND 33 kV STANDARD CONSTRUCTION SPAN OF 200 — 300 m	แบบเลขที่ SAI—015/33015 แผ่นที่ 5 ของจำนวน 5 แผ่น

30 ก.ค. 2533