การประกอบเลขที่
ASSEMBLY NO. 0214

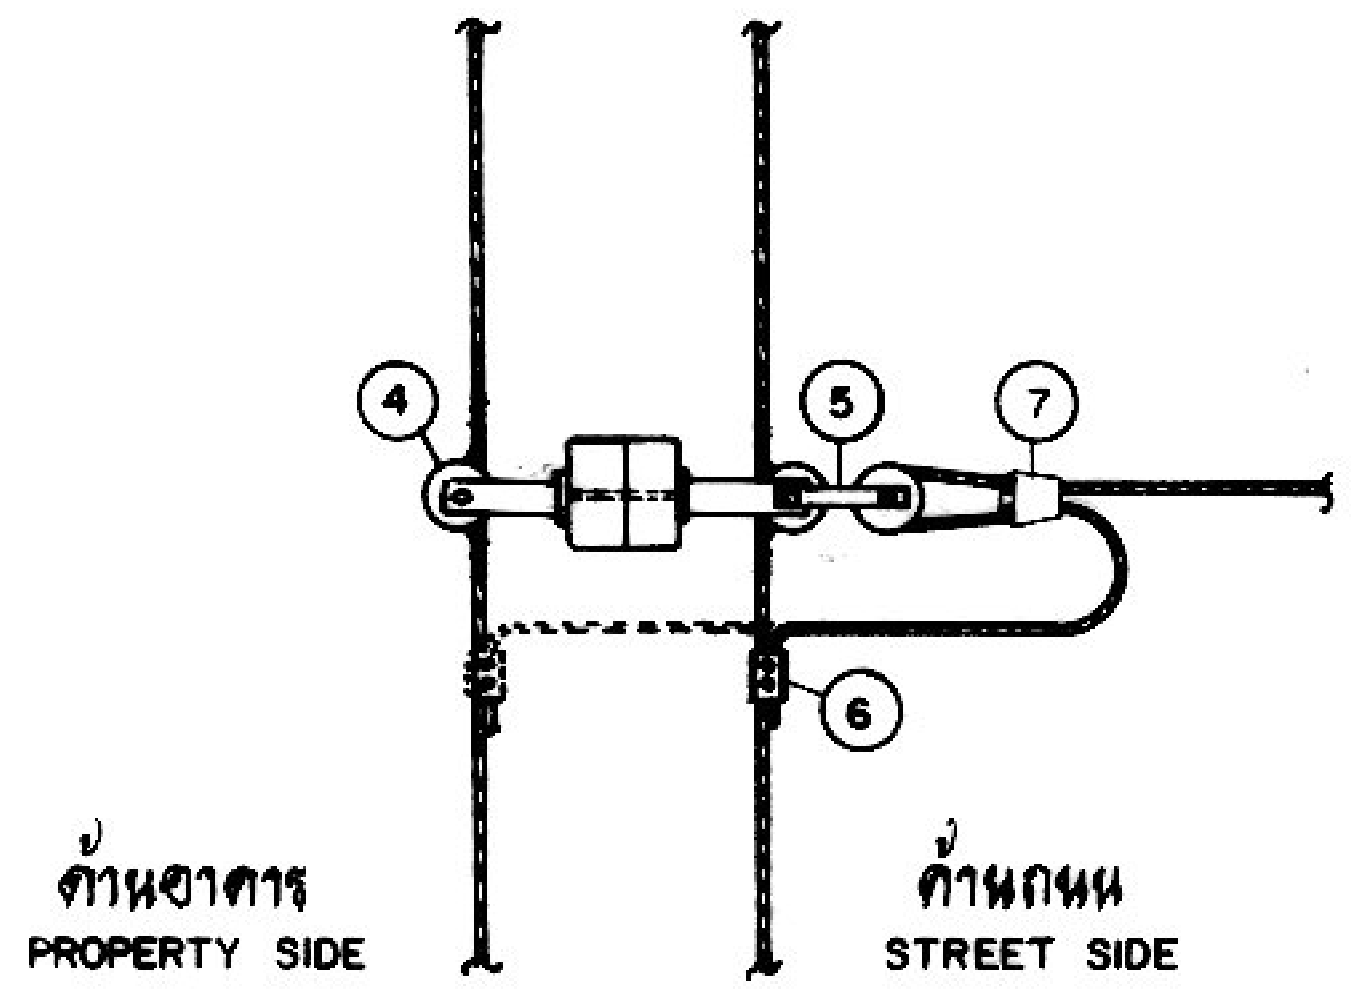

N – สายเป็นกลาง
NEUTRAL LINE

A,B,C – สายเฟส
PHASE LINE

L – สายดับไฟถนน
STREET LIGHTING LINE

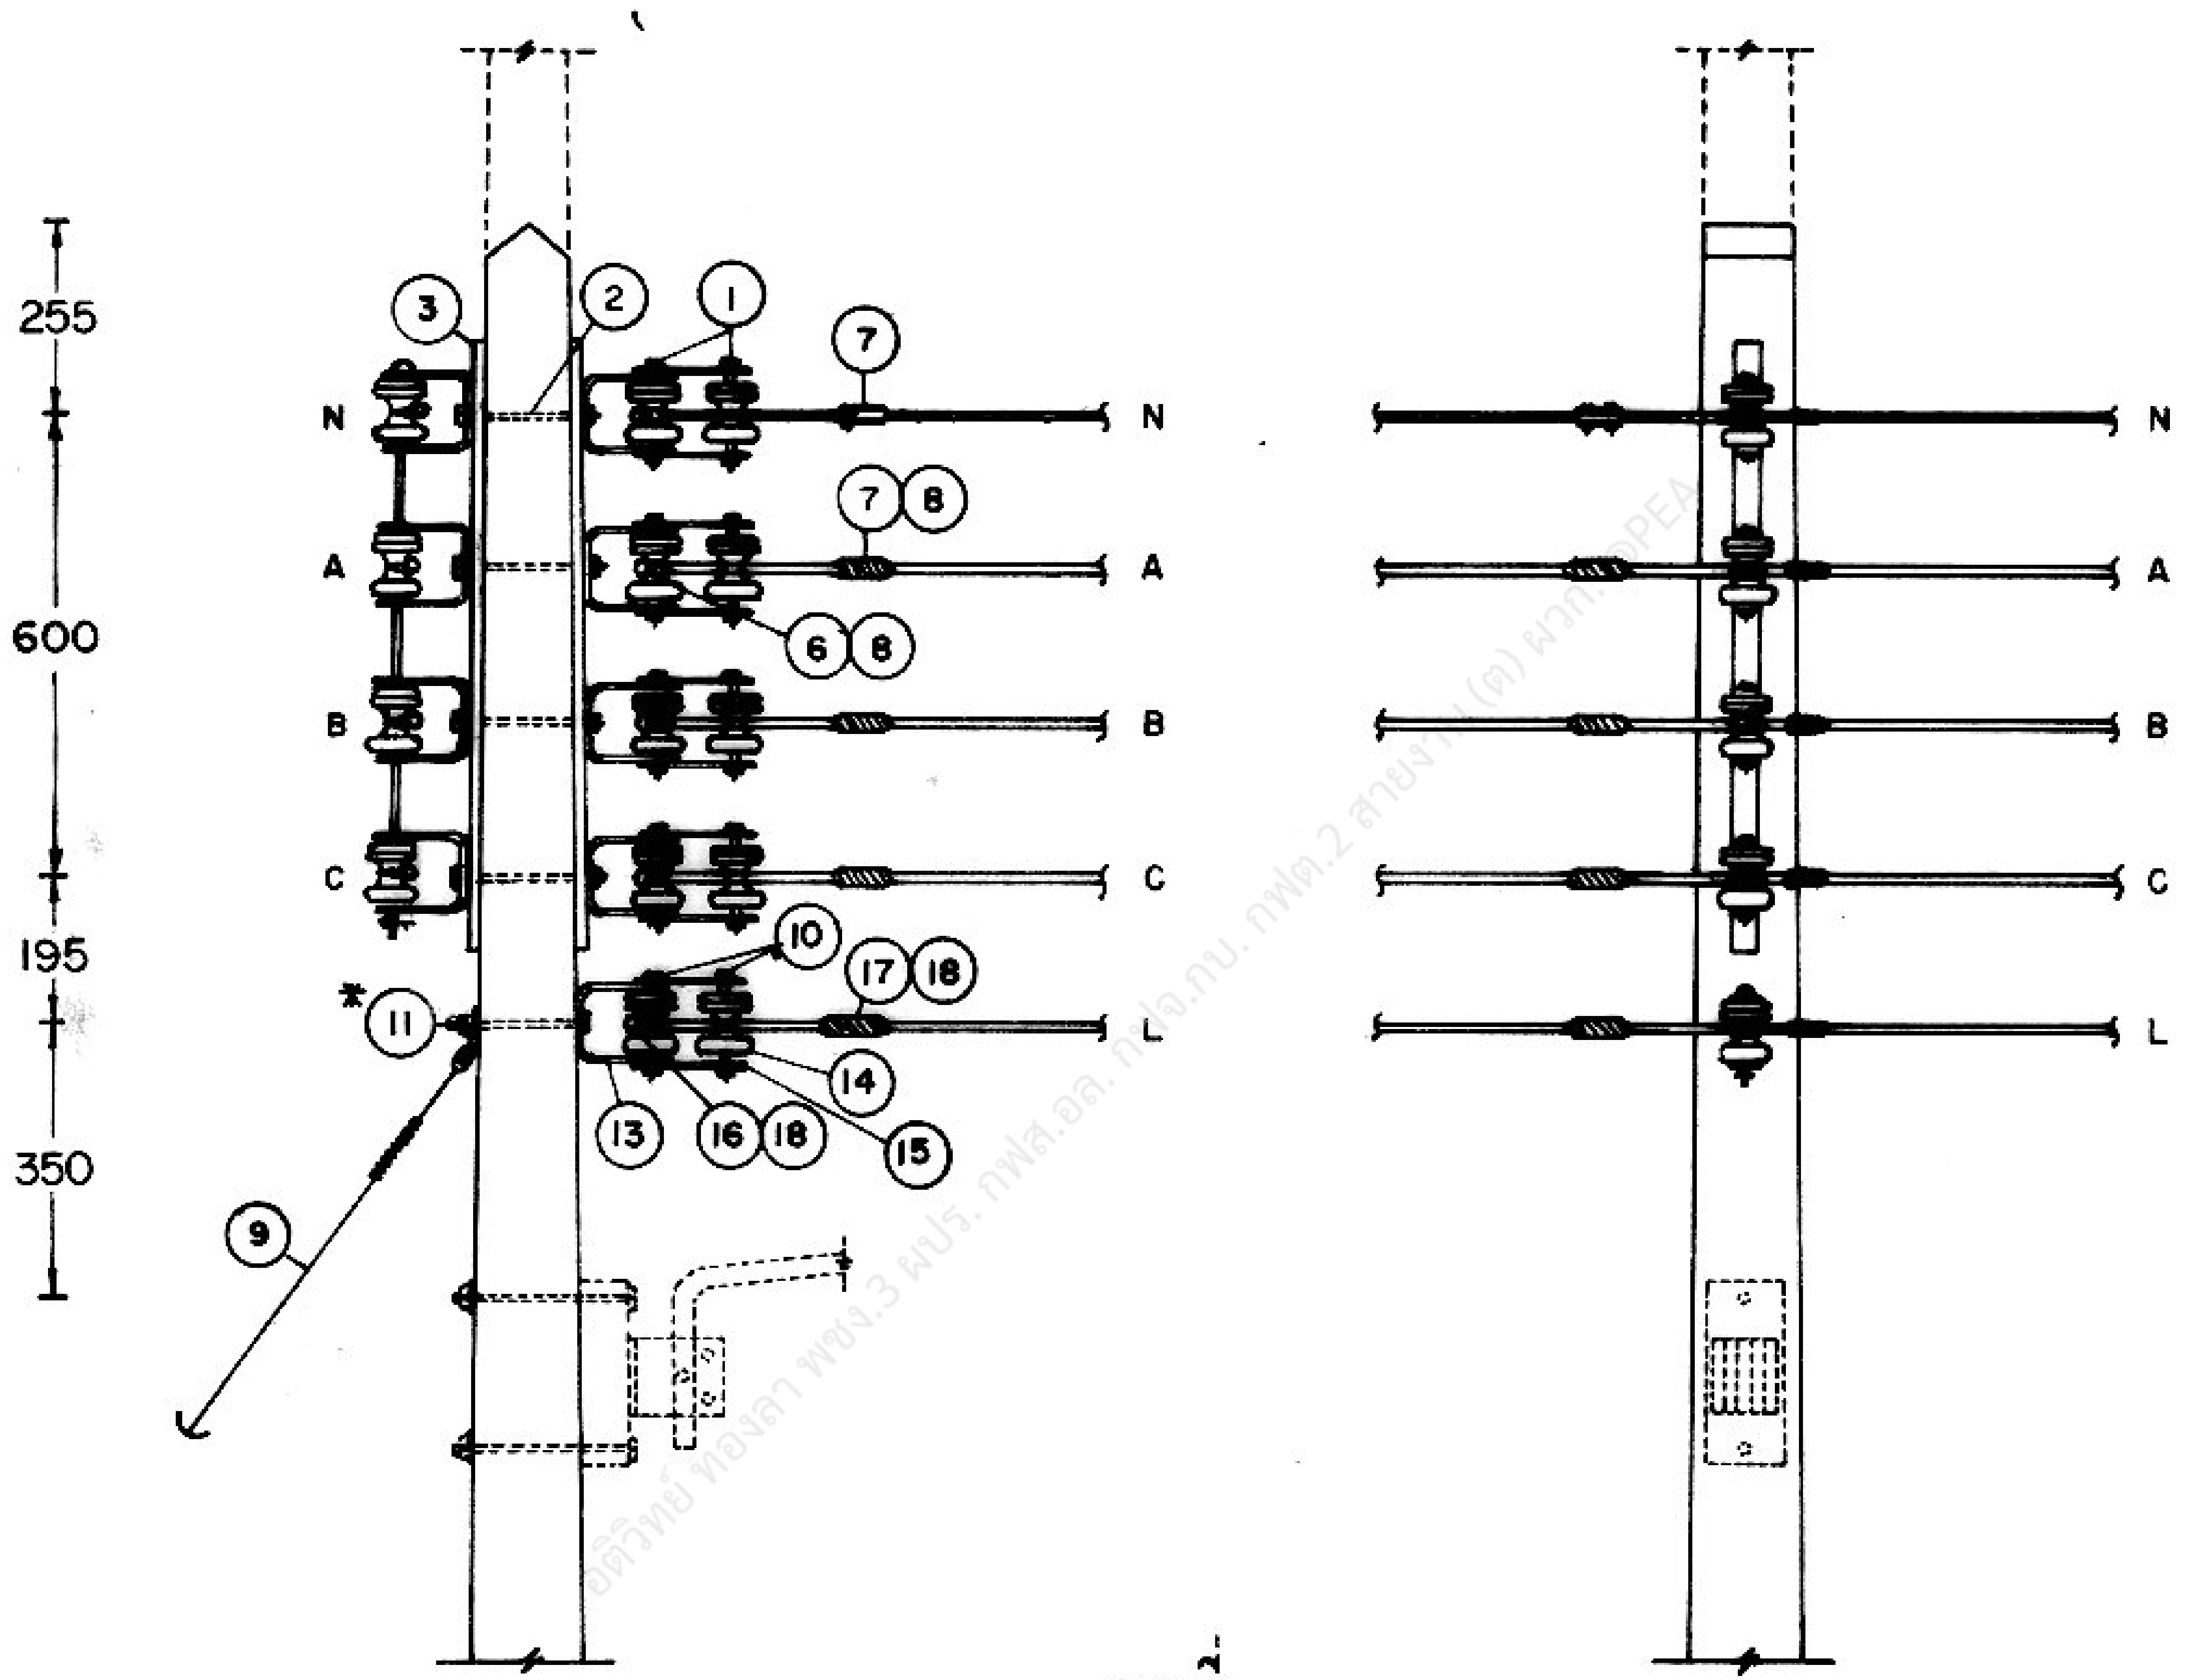

แบบที่ 1
TYPE 1

ในกรณีที่ไม่ติดตั้งสายดับไฟถนน การจัดทำสายยึดโยง ต้องเพิ่มสลักเกลียวรายการที่ 11 หนึ่งชุด และแหวนสี่เหลี่ยมในรายการที่ 12 หนึ่งตัว

* IF THE STREET LIGHTING LINE IS NOT INSTALLED, ONE MACHINE BOLT ITEM 11 AND ONE SQUARE WASHER ITEM 12 SHALL BE ADDED FOR GUY ASSEMBLY.

กองวิศวกรรมไฟฟ้าและเครื่องกล ฝ่ายวิศวกรรม	**การไฟฟ้าส่วนภูมิภาค**	ใช้แทนแบบ ถูกแทนโดยแบบ
ผู้เขียน ผู้สำรวจ วิศวกร หัวหน้าแผนก หัวหน้ากอง ผู้อำนวยการฝ่าย	ผู้ว่าการ 1 ก.ย. 2524	เขียนเสร็จวันที่ 12 เม.ย. 22 แก้แบบวันที่
	การติดตั้งแร็คแรงต่ำกับเสาคอนกรีต 9 ม. 2 วงจร สำหรับการต่อแยกสาย 1 วงจร	มิติเป็น มม. มาตราส่วน 1 : 20
รองผู้ว่าการฝ่ายเทคนิค	SECONDARY RACK INSTALLATION ON 9 m CONCRETE POLE 2-CIRCUITS FOR 1-CIRCUIT TAP LINE	แบบเลขที่ SAI-015/22024 แผ่นที่ 1 ของจำนวน 6 แผ่น

อิติวิทย์ ทองลา พชง.3 ผปร. กฟส.อล. กฟจ.กบ. กฟต.2 สายงาน(ต) ผวก.@PEA

การประกอบเลขที่
ASSEMBLY NO. 0214

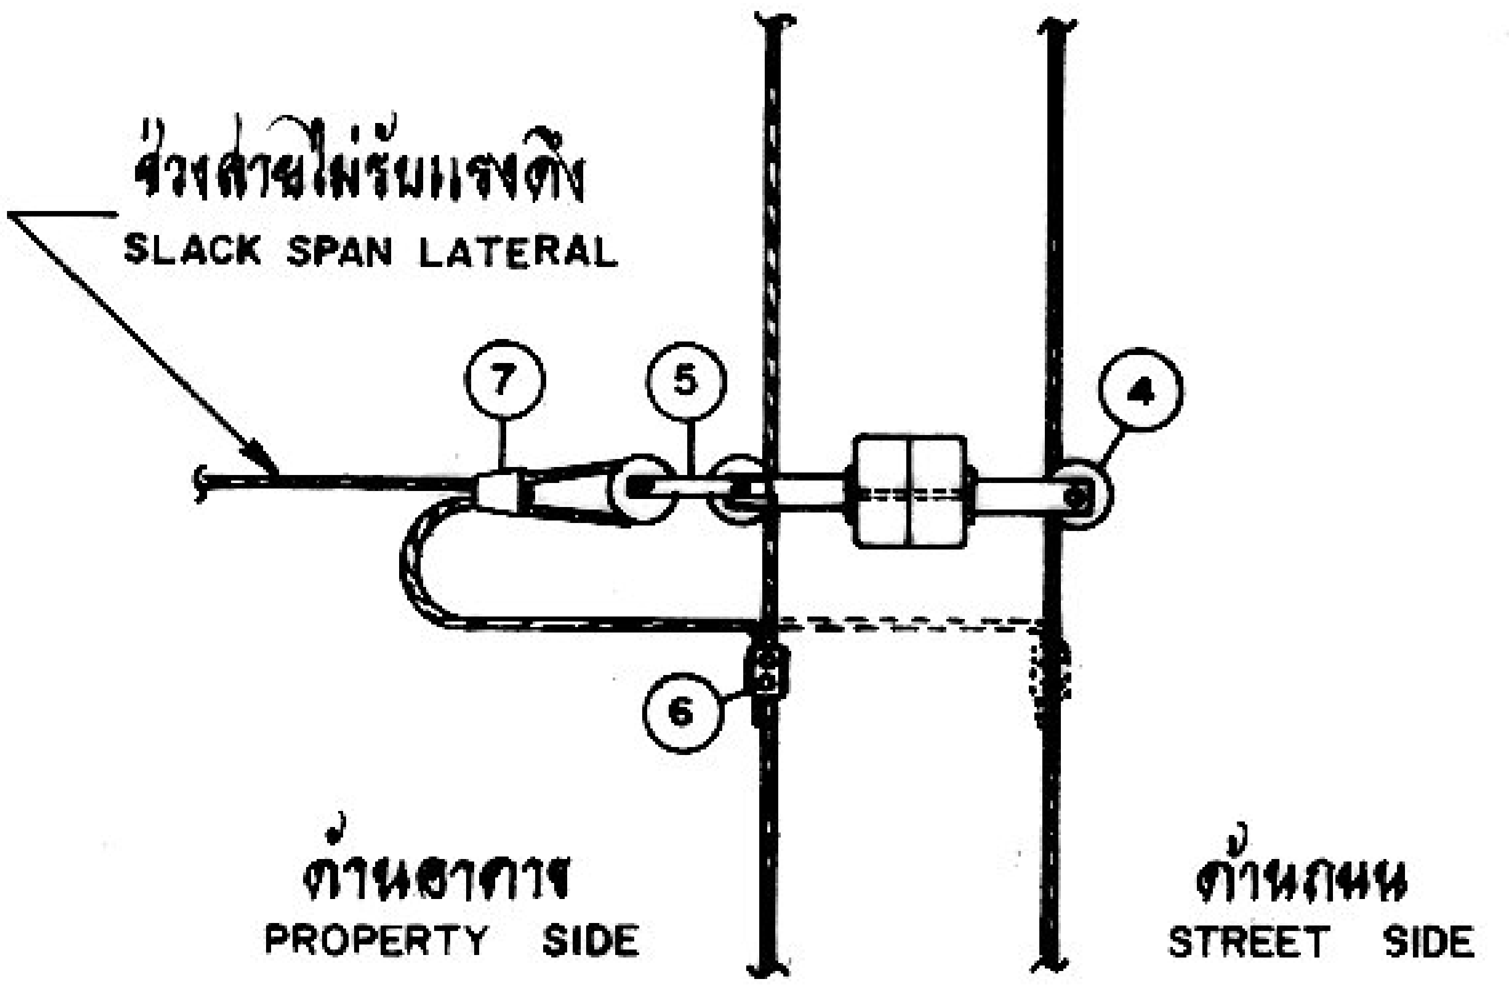

N - สายเป็นกลาง
NEUTRAL LINE

A, B, C - สายเฟส
PHASE LINE

L - สายคุมไฟถนน
STREET LIGHTING LINE

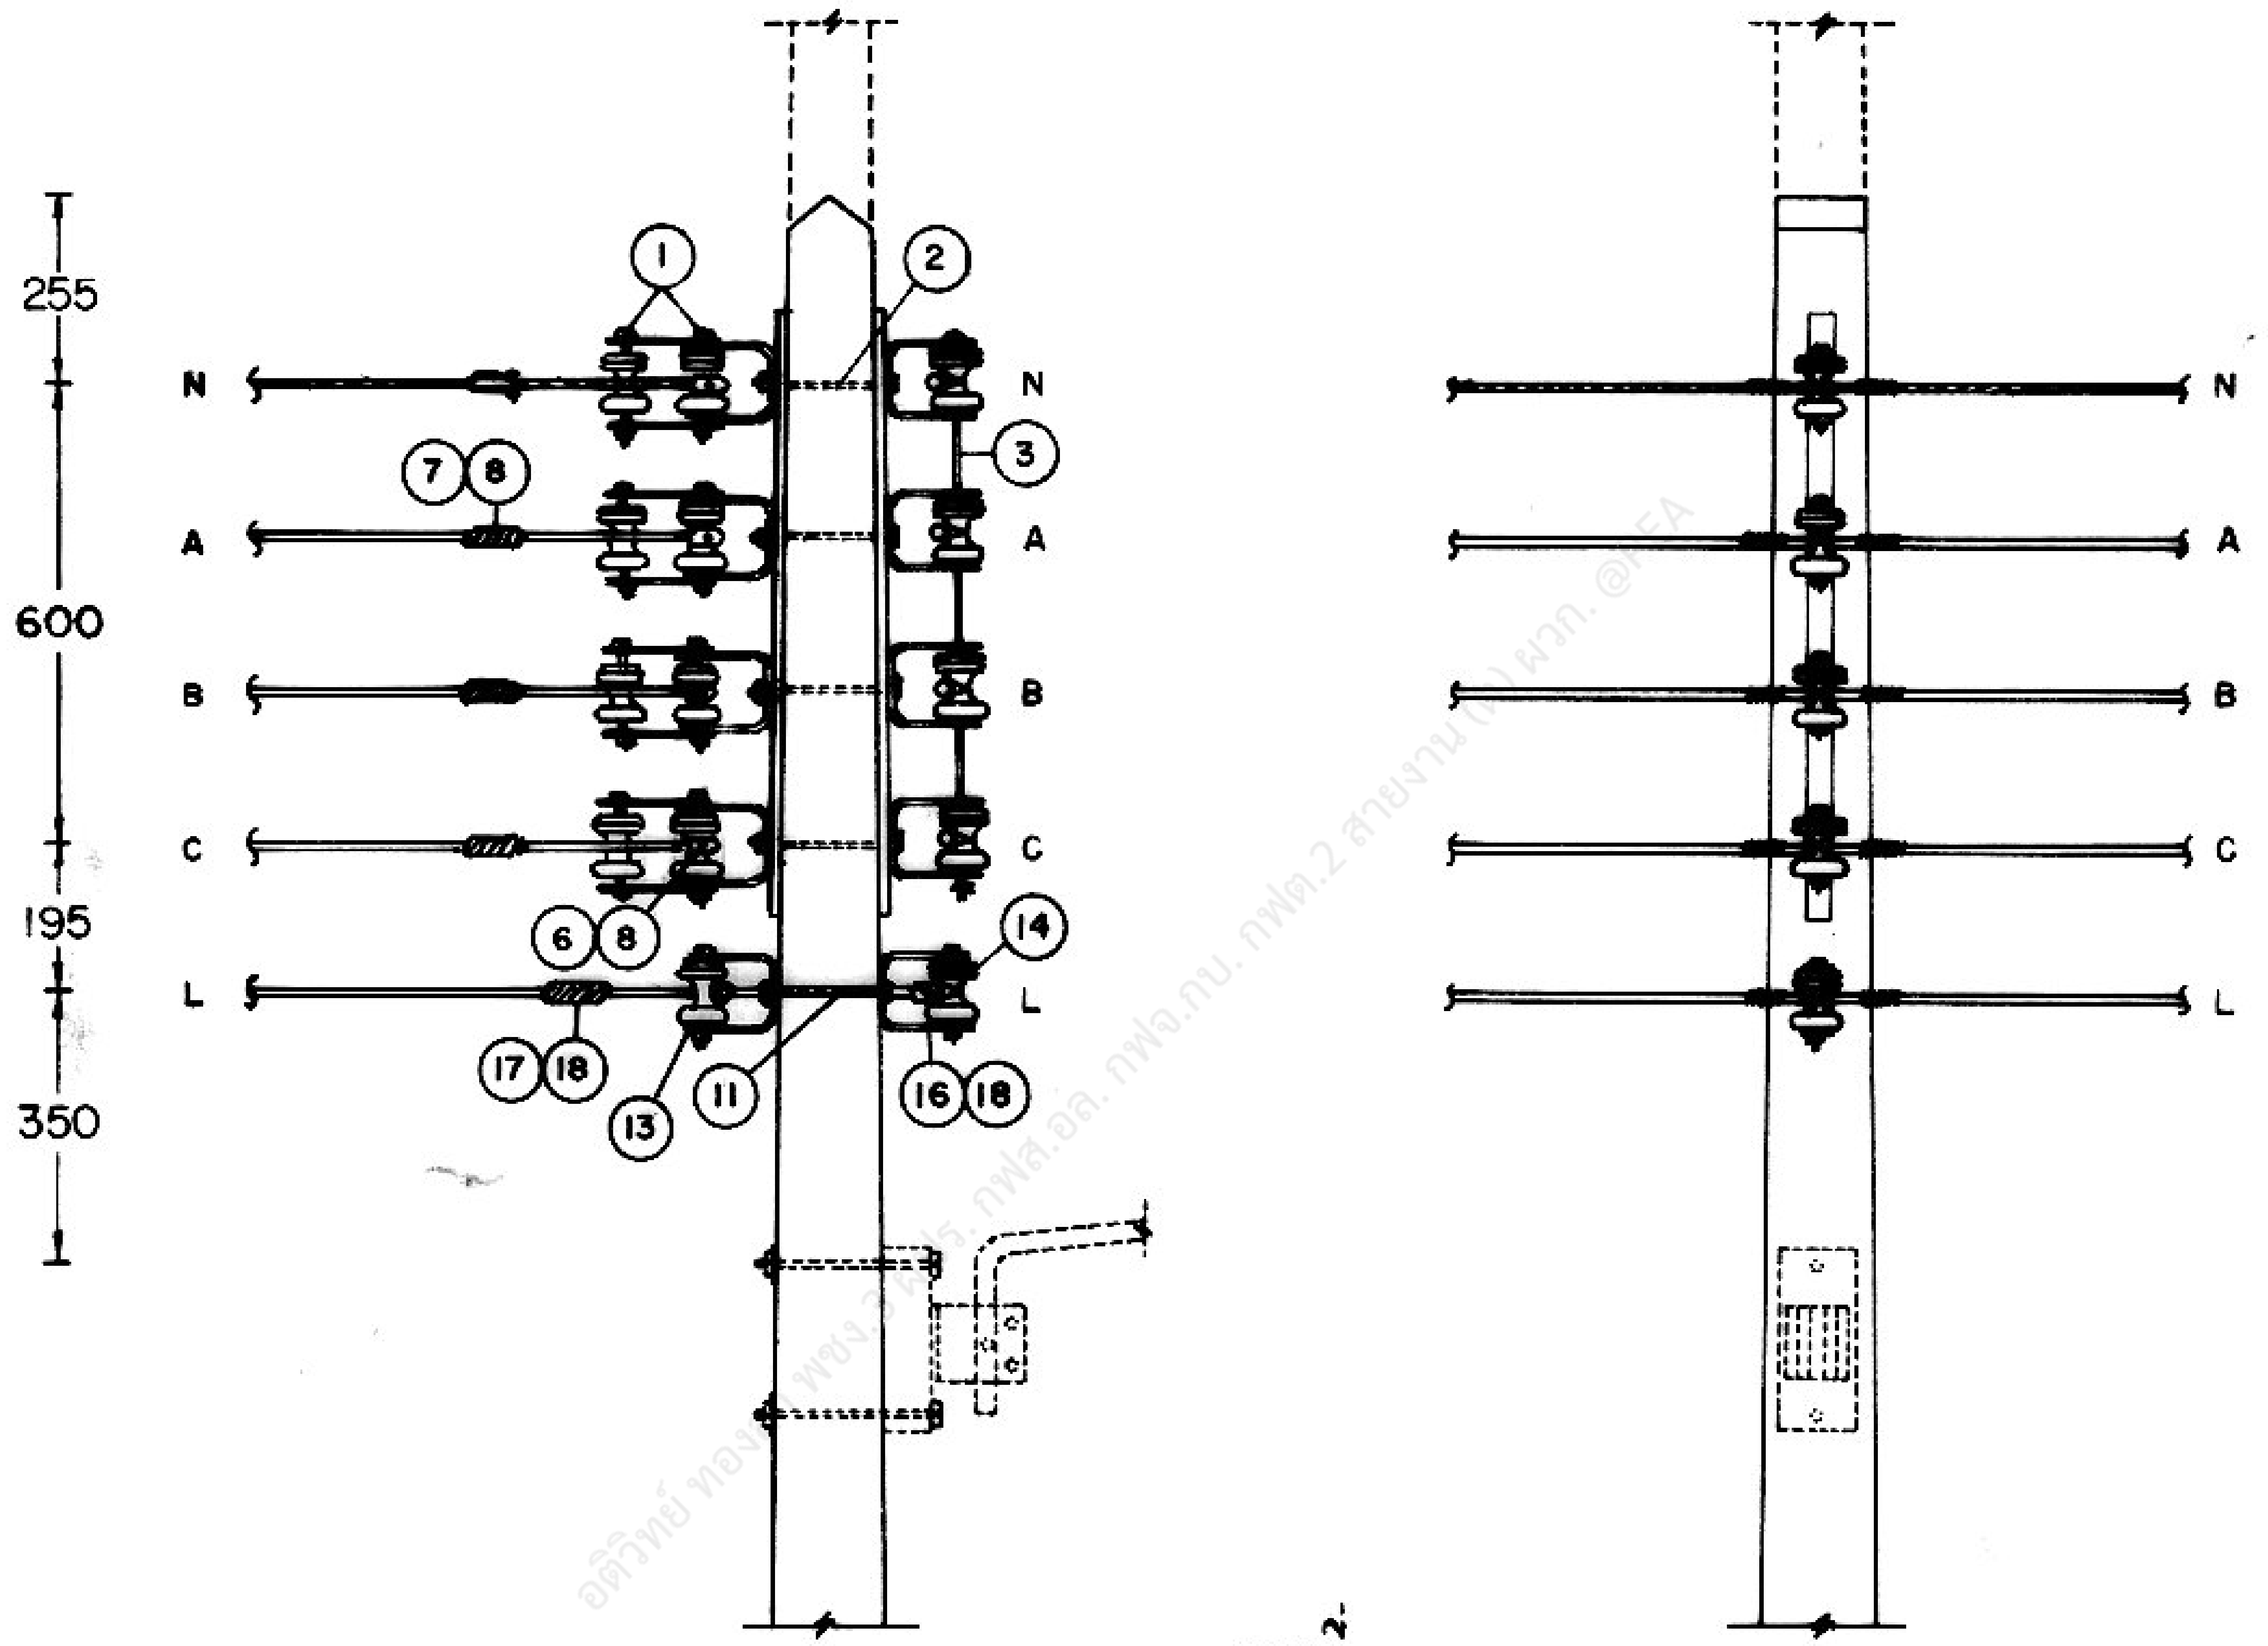

แบบที่
TYPE 2

ข้อแนะนำในการขึงสายระบบจำหน่ายแรงต่ำ

1. ระยะช่วงสายไม่รับแรงดึง ไม่เกิน 20 ม.
2. ระยะหย่อนยานต่ำสุดของสาย 50 ต.มม.,70 ต.มม. เท่ากับ 0.50 ม. และสาย 95 ต.มม. เท่ากับ 0.60 ม.

L.T. DISTRIBUTION LINE ERECTION SUGGESTION

1. MAXIMUM SLACK SPAN LATERAL 20 m.
2. MINIMUM SAG OF 50,70 mm^2 CONDUCTOR SHALL BE 0.50 m AND 95 mm^2 LINE SHALL BE 0.60 m.

กองวิศวกรรมไฟฟ้าและเครื่องกล
ฝ่ายวิศวกรรม

ผู้เขียน
ผู้สำรวจ
วิศวกร
หัวหน้าแผนก
หัวหน้ากอง
ผู้อำนวยการฝ่าย
รองผู้ว่าการฝ่ายเทคนิค

- 1 ก.ย. 2523

การไฟฟ้าส่วนภูมิภาค

ผู้ว่าการ
1 ก.ย. 2523

การติดตั้งแร็คแรงต่ำกับเสาคอนกรีต 9 ม.
2 วงจร
สำหรับการต่อแยกสาย 1 วงจร

SECONDARY RACK INSTALLATION ON 9 m CONCRETE POLE
2-CIRCUITS
FOR 1-CIRCUIT TAP LINE

ใช้แทนแบบ
ถูกแทนโดยแบบ
เขียนเสร็จวันที่ 12 เม.ย. 22
แก้แบบวันที่
มิติเป็น มม.
มาตราส่วน 1 : 20
แบบเลขที่ SAI-015/22024
แผ่นที่ 2 ของจำนวน 6 แผ่น

การประกอบเลขที่ ASSEMBLY NO. 0 214

N - สายเป็นกลาง NEUTRAL LINE

A,B,C - สายเฟส PHASE LINE

L - สายต้นไฟถนน STREET LIGHTING LINE

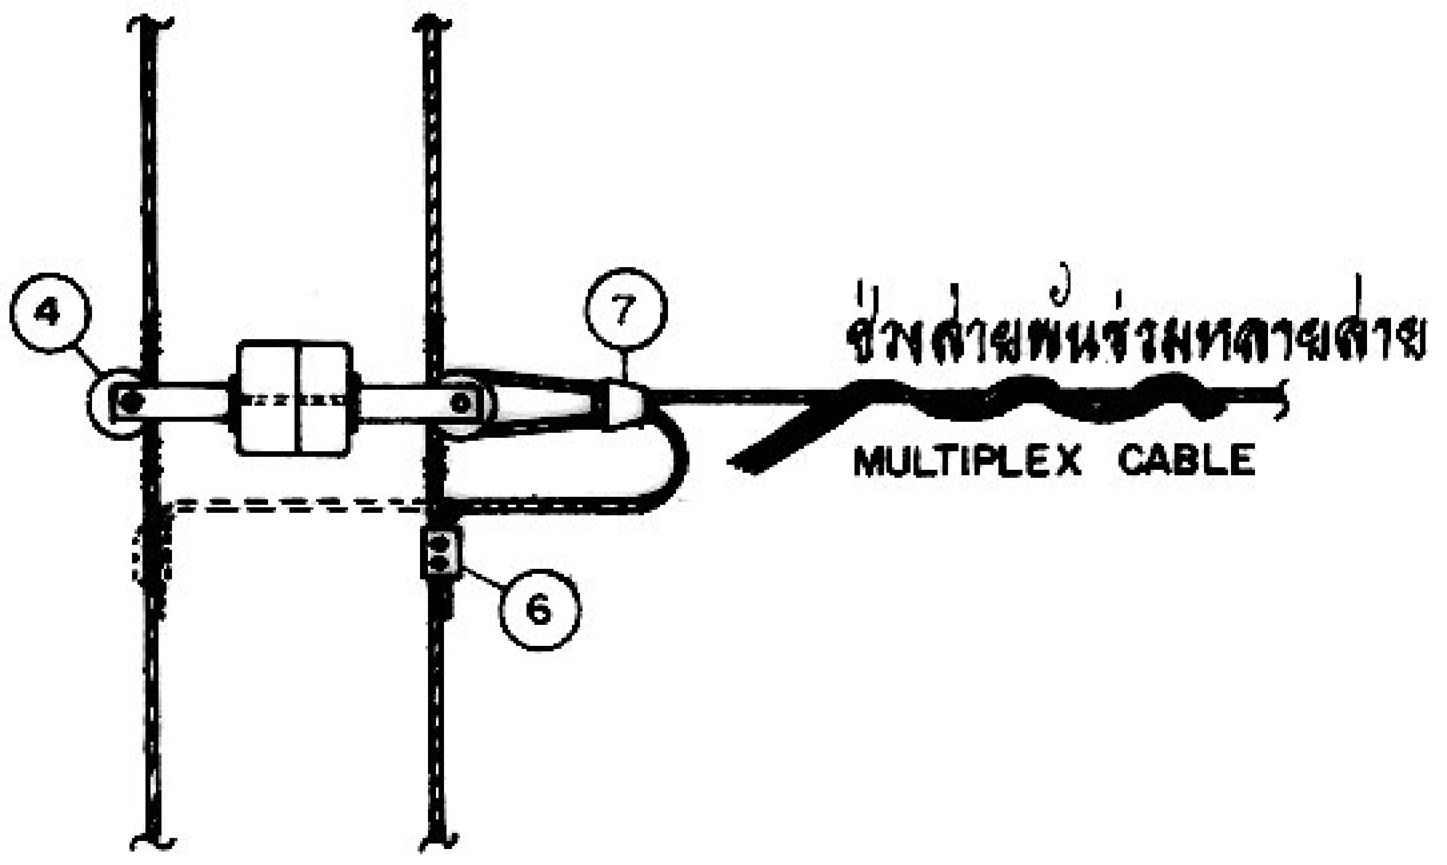

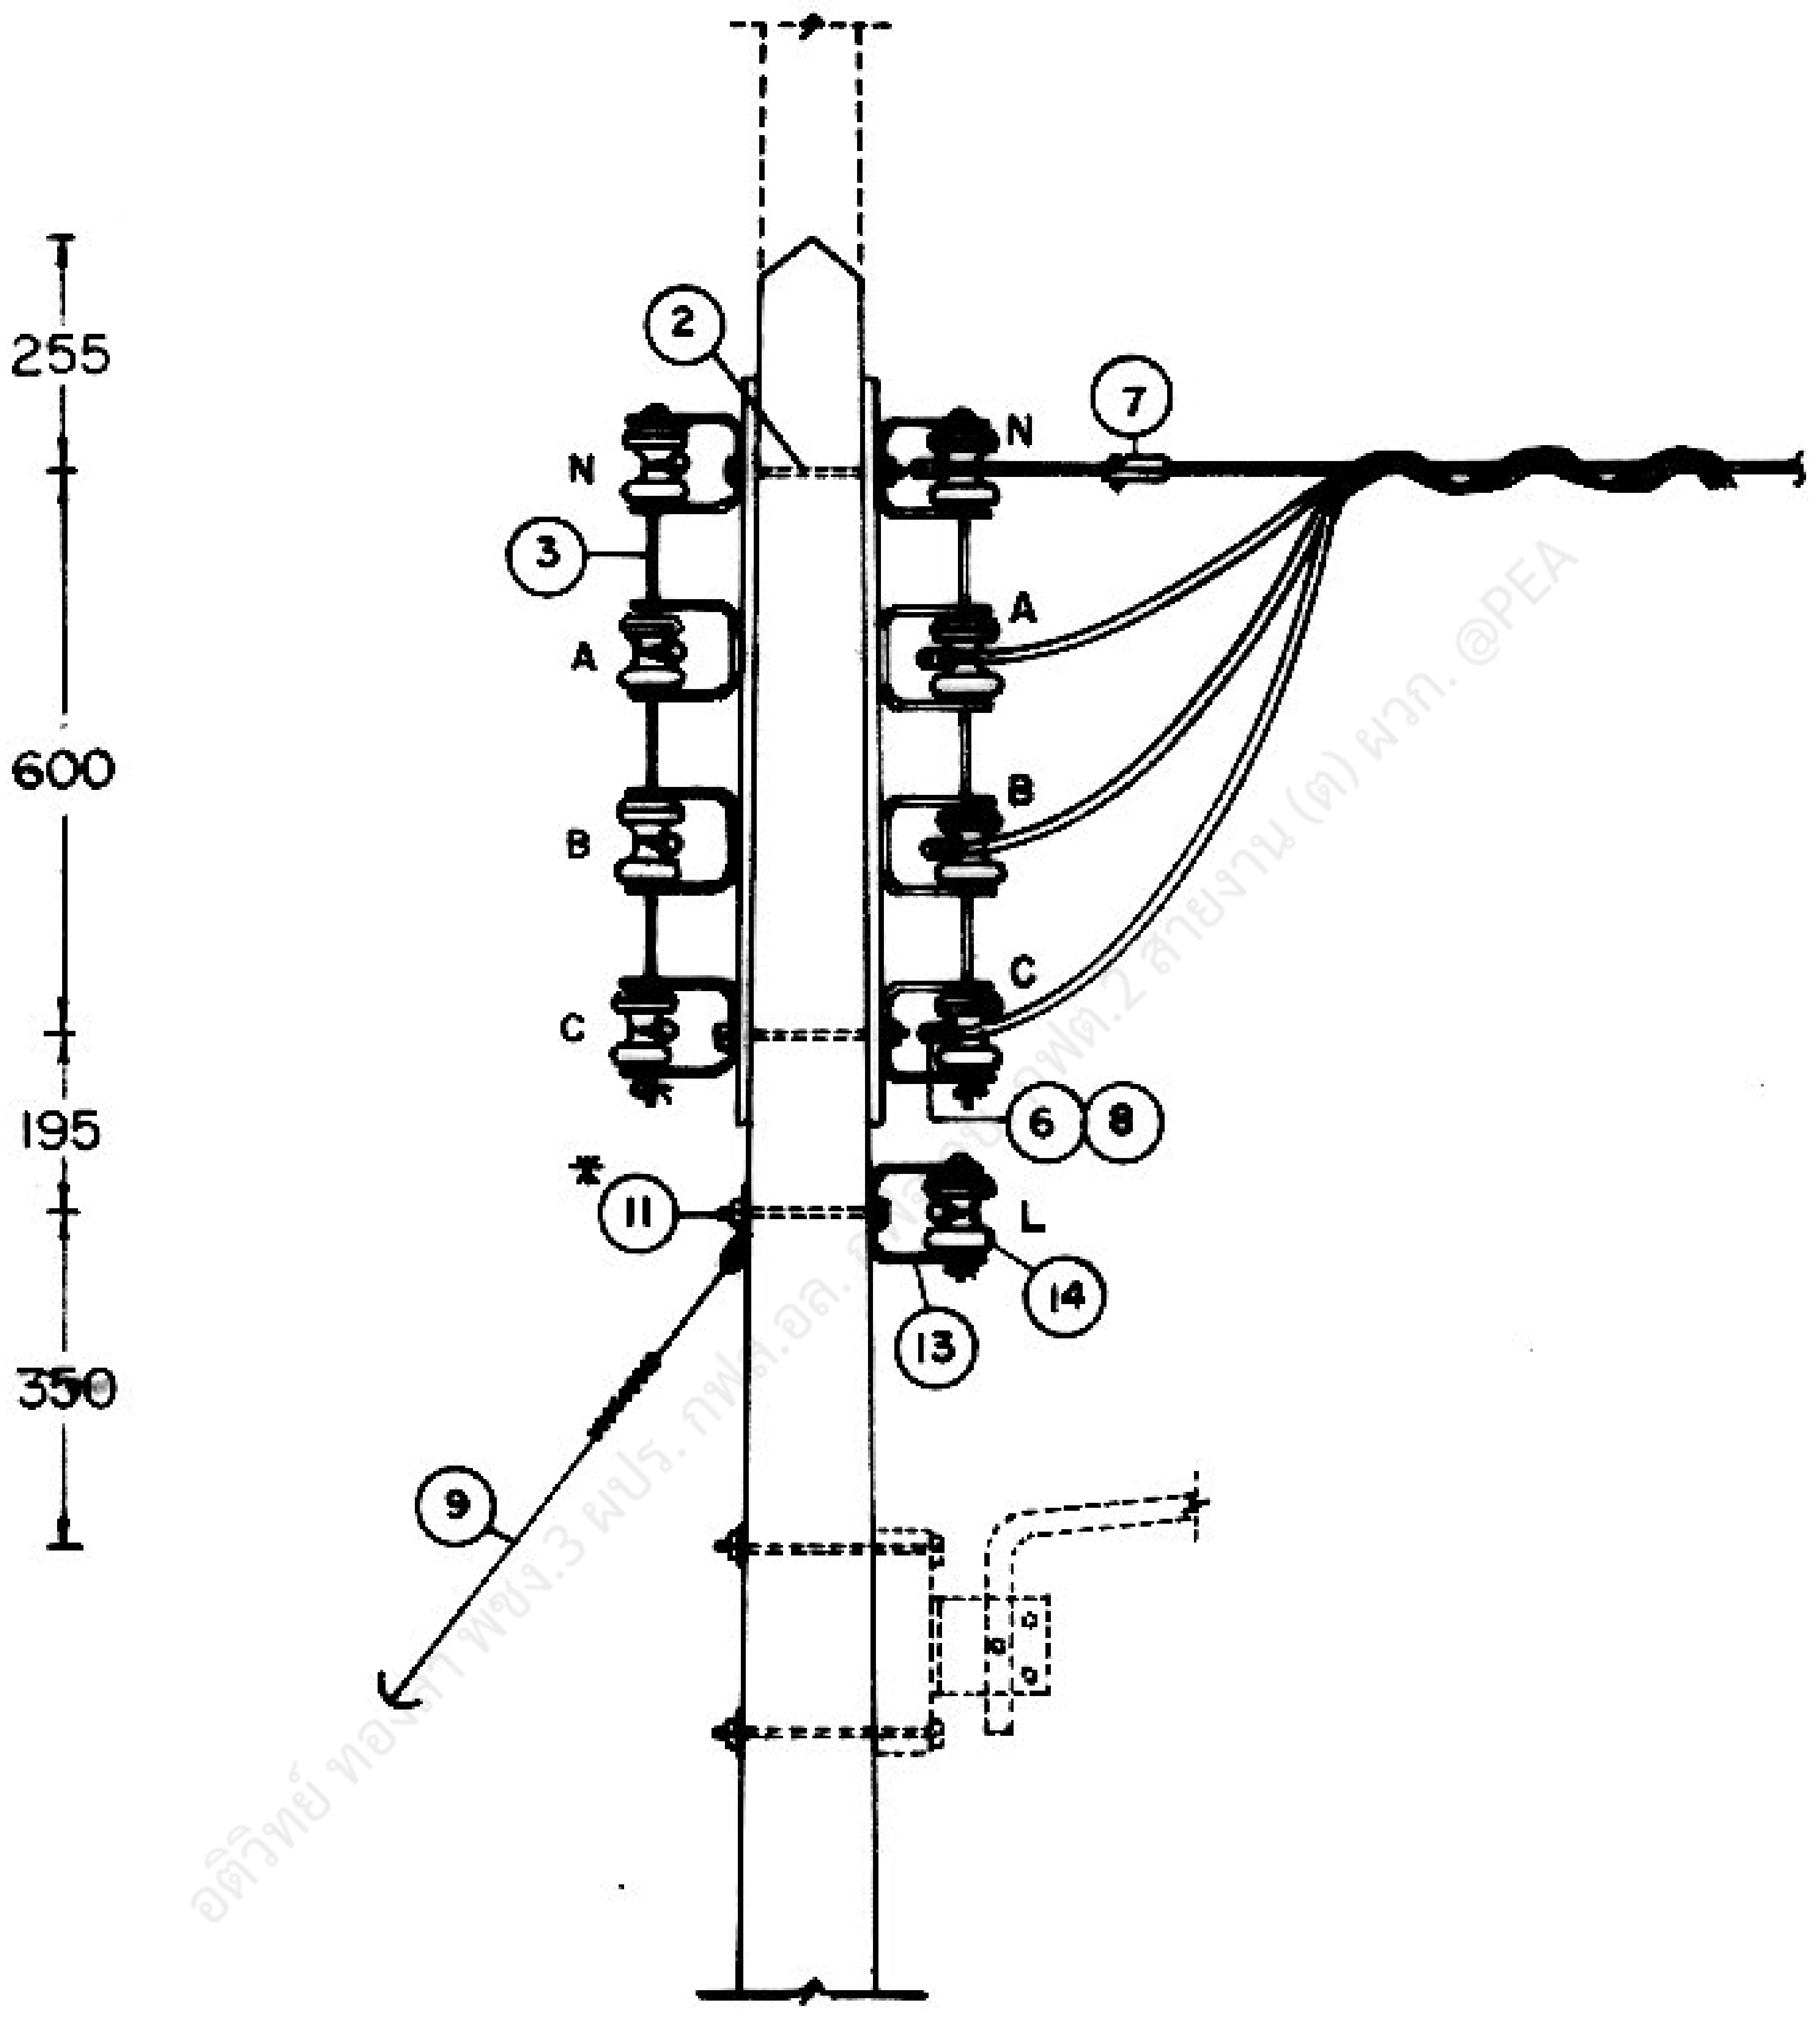

แบบที่ TYPE 3

ในกรณีที่ไม่ติดตั้งสายต้นไฟถนน การจัดทำสายยึดโยงต้องเพิ่มสลักเกลียว รายการที่ 11 หนึ่งชุด และแหวนสี่เหลี่ยมในรายการที่ 12 หนึ่งตัว

* IF THE STREET LIGHTING LINE IS NOT INSTALLED, ONE MACHINE BOLT ITEM 11 AND ONE SQUARE WASHER ITEM 12 SHALL BE ADDED FOR GUY ASSEMBLY.

กองวิศวกรรมไฟฟ้าและเครื่องกล
ฝ่ายวิศวกรรม

ผู้เขียน
ผู้สำรวจ
วิศวกร กิตติพงษ์
หัวหน้าแผนก
หัวหน้ากอง
ผู้อำนวยการฝ่าย

รองผู้ว่าการฝ่ายเทคนิค

การไฟฟ้าส่วนภูมิภาค

ผู้ว่าการ

การติดตั้งแร็คแรงต่ำบนเสาคอนกรีต 9 ม.
2 วงจร
สำหรับการต่อแยกสาย 1 วงจร

SECONDARY RACK INSTALLATION ON 9 m CONCRETE POLE
2- CIRCUITS
FOR 1-CIRCUIT TAP LINE

ใช้แทนแบบ
ถูกแทนโดยแบบ
เขียนเสร็จวันที่ 12 เม.ย. 22
แก้แบบวันที่
มิติเป็น มม.
มาตราส่วน 1 : 20
แบบเลขที่ SAI-015/22024
แผ่นที่ 3 ของจำนวน 6 แผ่น

7 ก.ย. 2522

การประกอบเลขที่ ASSEMBLY NO. 0214

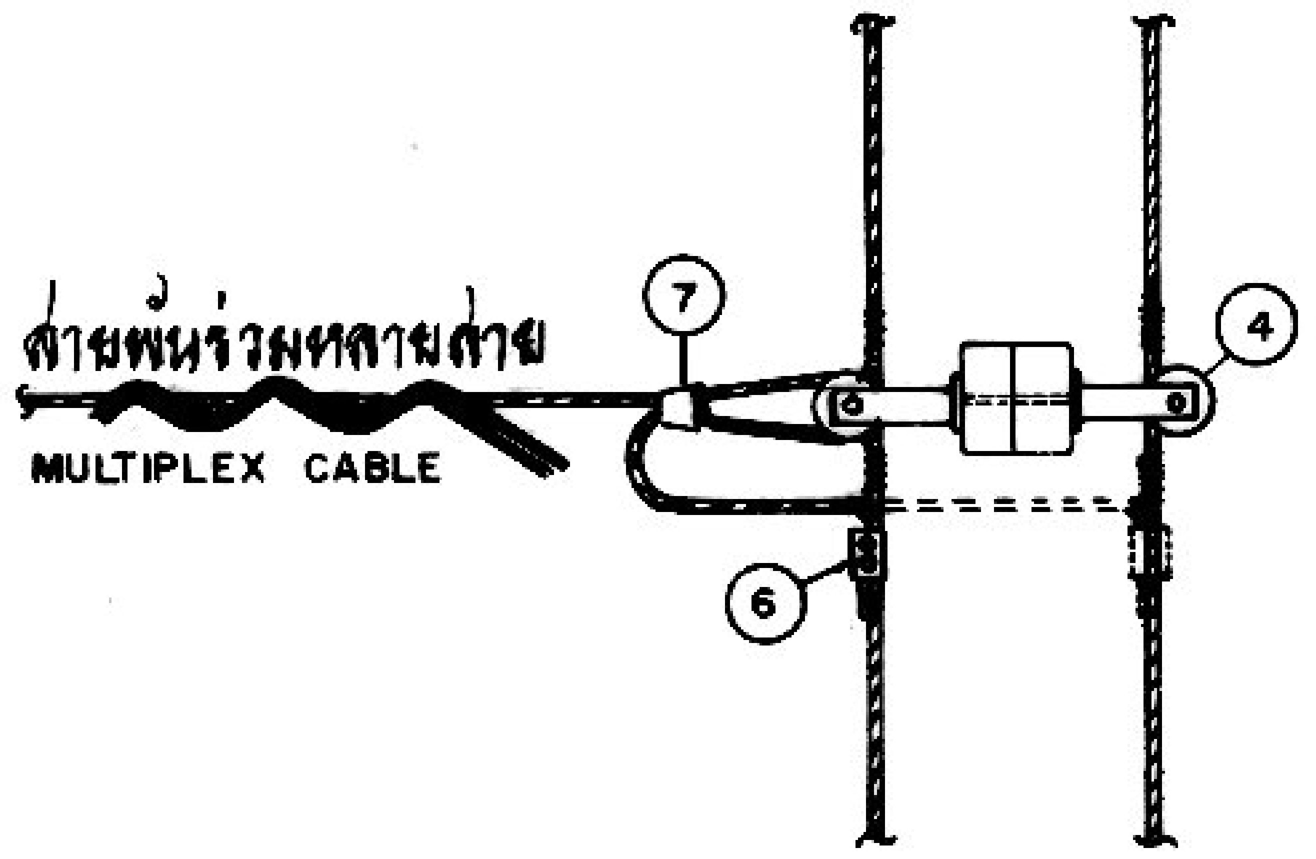

N - สายเป็นกลาง NEUTRAL LINE

A,B,C - สายเฟส PHASE LINE

L - สายดับไฟถนน STREET LIGHTING LINE

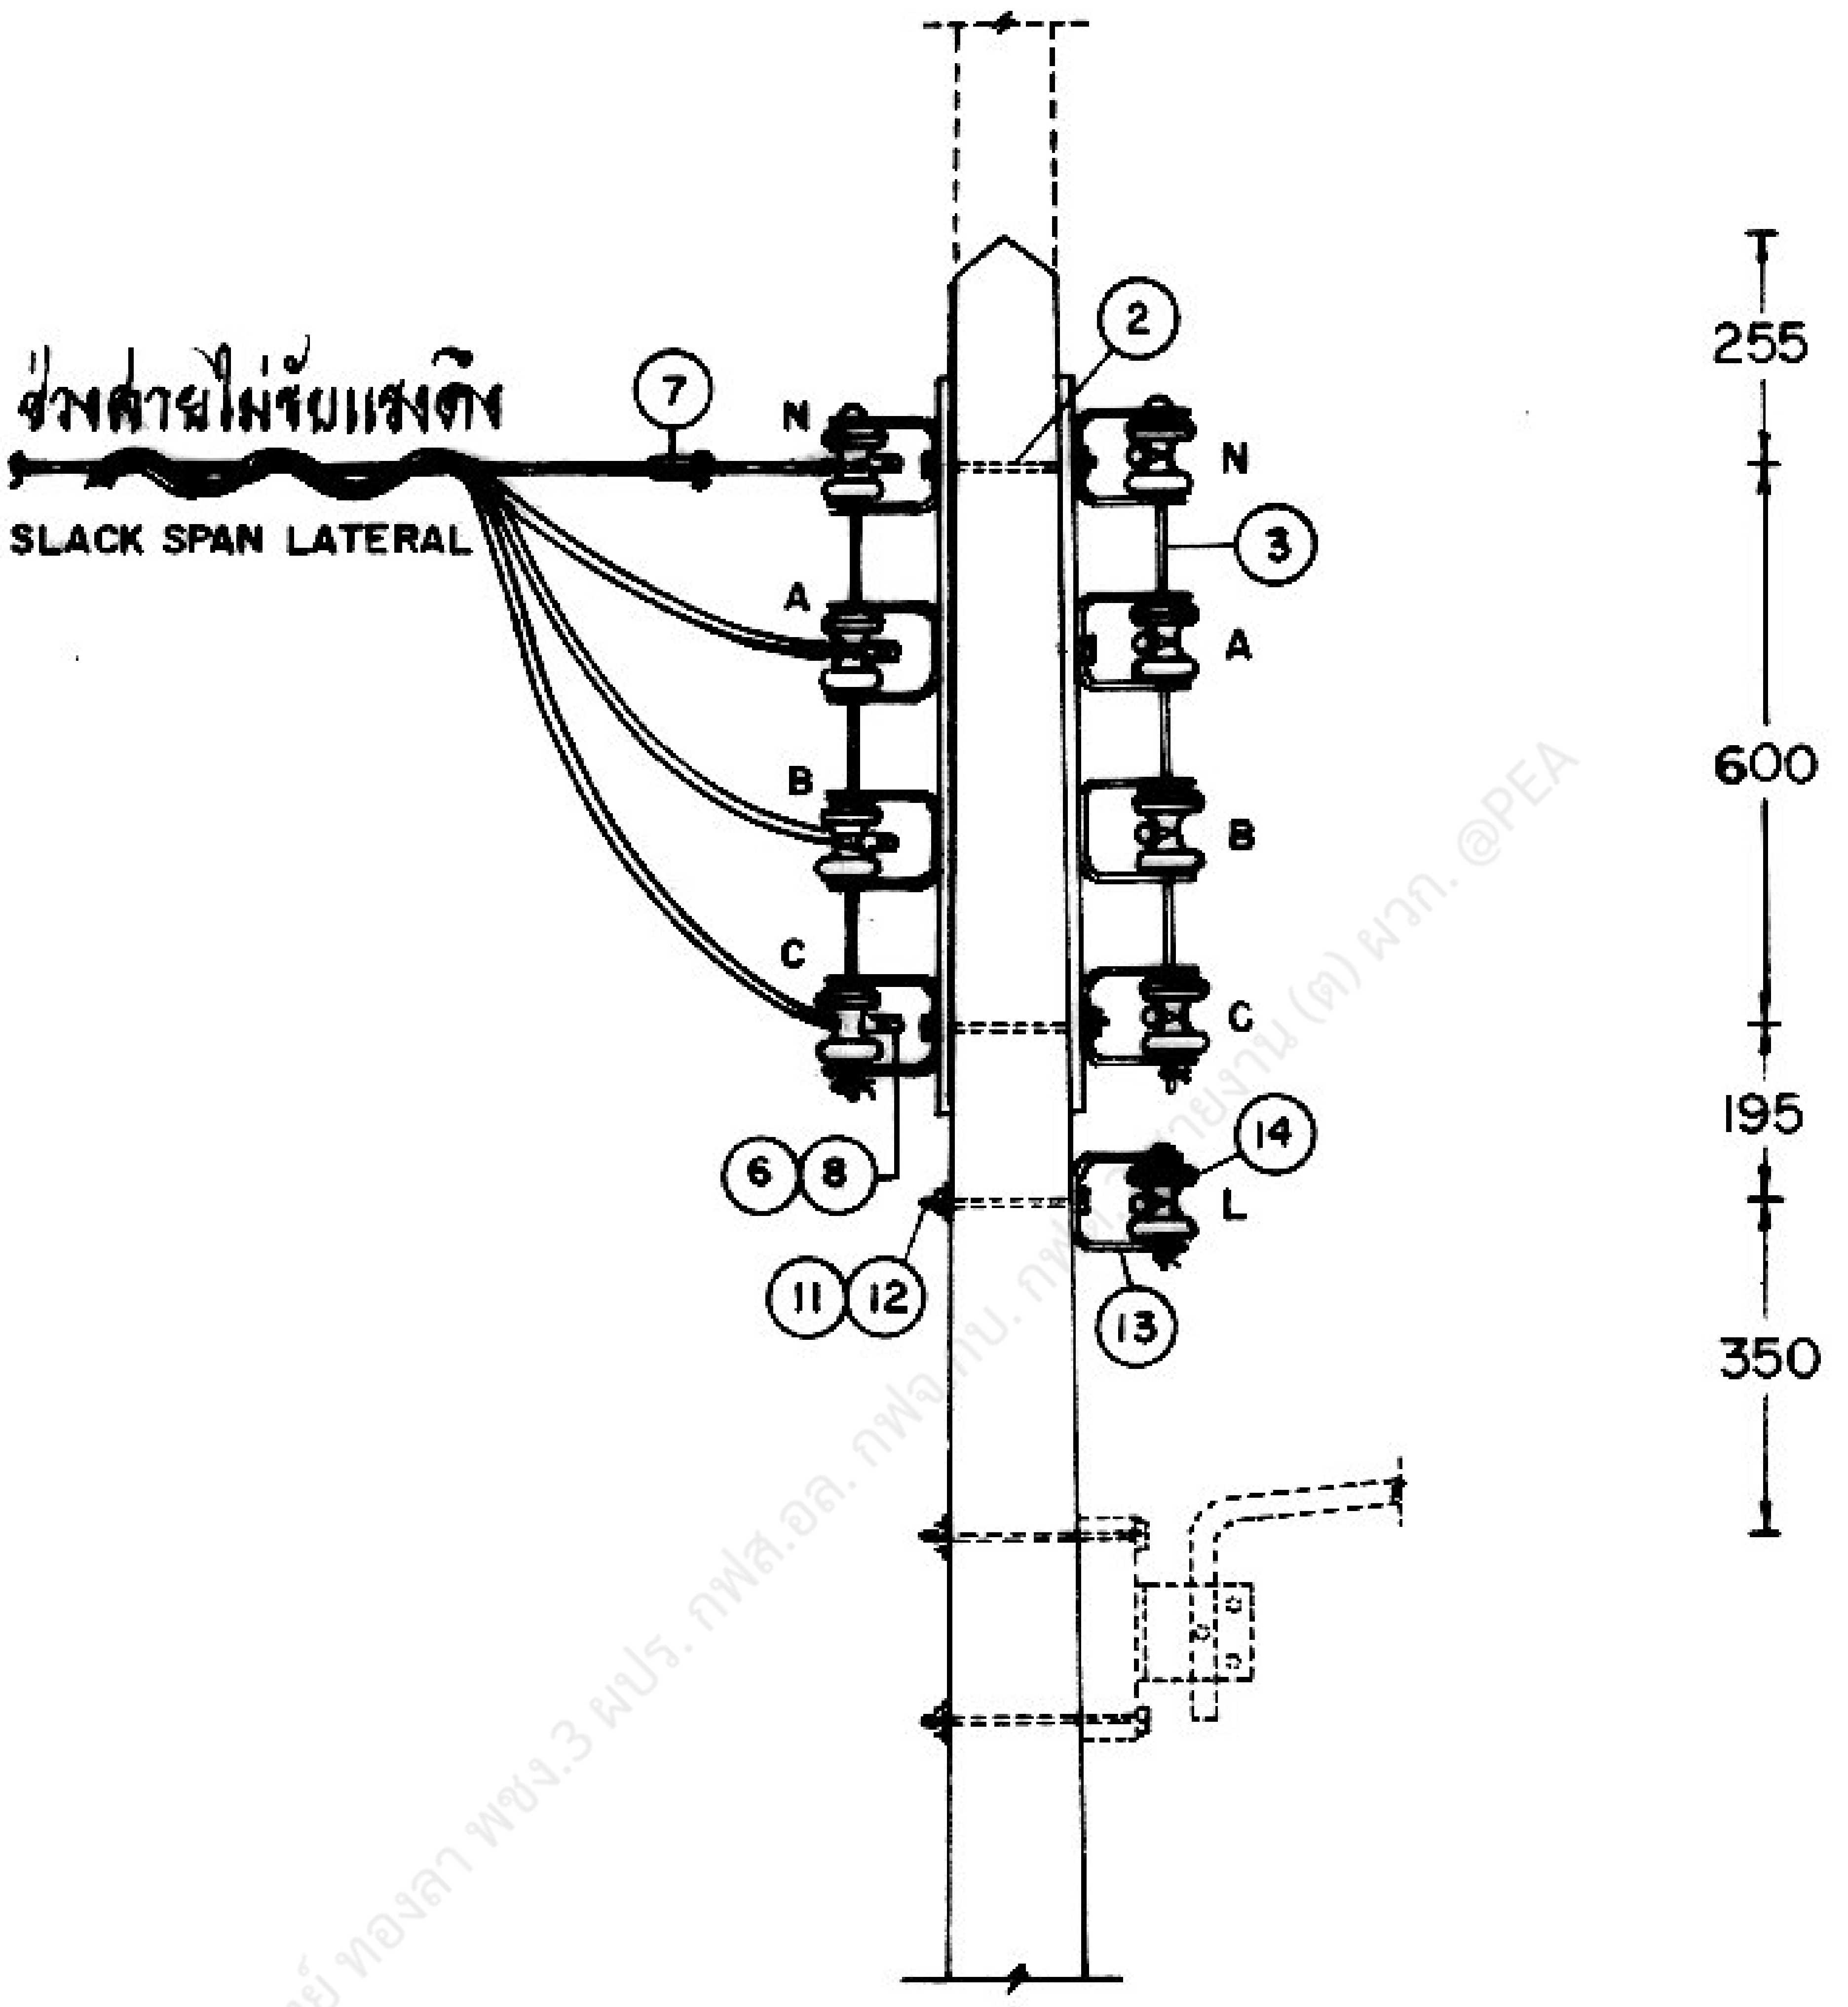

แบบที่
TYPE 4

อดิวิทย์ ทองลา พชง.3 ผปร. กฟส.อล. กฟจ.ลบ. กฟก.1 ... (ต) ผวก. @PEA

ข้อแนะนำในการขึงสายระบบจำหน่ายแรงต่ำ

1. ระยะช่วงสายไม่รับแรงดึง ไม่เกิน 20 ม.
2. ระยะหย่อนยานต่ำสุดของสาย 50,70 และ 95 ต.มม. เท่ากับ 0.70, 0.80 และ 0.90 ม. ตามลำดับ

L.T. DISTRIBUTION LINE ERECTION SUGESTION

1. MAXIMUM SLACK SPAN LATERAL 20 m.
2. MINIMUM SAG OF 50,70 AND 95 mm^2 CONDUCTOR SHALL BE 0.70, 0.80 AND 0.90m RESPECTIVELY.

กองวิศวกรรมไฟฟ้าและเครื่องกล ฝ่ายวิศวกรรม	**การไฟฟ้าส่วนภูมิภาค**	ใช้แทนแบบ ถูกแทนโดยแบบ เขียนเสร็จวันที่ 12 เม.ย. 22
ผู้เขียน ผู้ตรวจ วิศวกร กิตติพงษ์ หัวหน้าแผนก หัวหน้ากอง ผู้อำนวยการฝ่าย	ผู้ว่าการ การติดตั้งแร็คแรงต่ำกับเสาคอนกรีต 9 ม. 2 วงจร สำหรับการต่อแยกสาย 1 วงจร	แก้แบบวันที่ มิติเป็น มม. มาตราส่วน 1 : 20
รองผู้ว่าการฝ่ายเทคนิค	SECONDARY RACK INSTALLATION ON 9 m CONCRETE POLE 2-CIRCUITS FOR 1-CIRCUIT TAP LINE	แบบเลขที่ SAI-015/22024 แผ่นที่ 4 ของจำนวน 6 แผ่น

การประกอบเลขที่ ASSEMBLY NO. 0214

บัญชีวัสดุ
BILL OF MATERIAL

ลำดับที่ ITEM	รายละเอียด DESCRIPTION	จำนวน REQ'D 1	2	3	4	วัสดุเลขที่ MAT. NO.
1	สลักเกลียว M 16 X 130 มม. BOLT, MACHINE, M 16 X 130 mm	8	8	-	-	01110200
2	สลักเกลียว M 16 X 200 มม. BOLT, MACHINE, M 16 X 200 mm	4	4	2	2	01110202
2a	สลักเกลียว M 16 X 250 มม. สำหรับเสาคอนกรีต 12 ม. BOLT, MACHINE, M 16 X 250 mm FOR 12 m CONCRETE POLE	4	4	2	2	01110203
3	แร็ค 4 X 200 มม. แบบหลังยื่น RACK, SECONDARY, MEDIUM PRESSED STEEL 4 X 200 mm EXTENDED BACK	2	2	2	2	03130002
4	ลูกถ้วยแรงต่ำ มอก. 227 แบบ ข (แบบ 53-2) INSULATOR, SPOOL TYPE, L.T. TIS 227 TYPE B (CLASS 53-2)	12	12	8	8	03030000
5	เหล็กแผ่น 6 X 30 X 150 มม. แบบเลขที่ SAI-015/22030 (การประกอบเลขที่ 0105) PLATE STEEL 6 X 30 X 150 mm DWG. NO. SAI-015/22030 (ASS. NO. 0105)	8	8	-	-	—
6	พี.จี. คอนเนคเตอร์ สำหรับสายอลูมิเนียม ขนาดตามต้องการ CONNECTOR, PARALLEL GROOVE, Al SIZE AS REQUIRED	4	4	4	4	02300102-3
7	คอนเนคเตอร์เข้าปลายสายอลูมิเนียม ขนาดตามต้องการ CONNECTOR, DEADEND, Al SIZE AS REQUIRED	4	4	1	1	02310000-2
8	PVC เทป กว้าง 19 มม. (ใช้ความยาว 2 ม. ต่อ จุด) มอก. 386 PVC TAPE, 19 mm WIDE (2 m LONG PER POINT) TIS 386					02180001 or 02180002
9	การประกอบสายยึดโยง GY-01 GUY ASSEMBLY GY-01	1	-	1	-	—
9a	การประกอบสายยึดโยง GY-02 สำหรับเสาคอนกรีต 12 ม. GUY ASSEMBLY GY-02 FOR 12 m CONCRETE POLE	1	-	1	-	—
	สำหรับการติดตั้งสายดับไฟถนน FOR STREET LIGHTING INSTALLATION					
10	สลักเกลียว M 16 X 130 มม. BOLT, MACHINE, M 16 X 130 mm	2	-	-	-	01110202
11*	สลักเกลียว M 16 X 170 มม. BOLT, MACHINE, M 16 X 170 mm	1	1	1	1	01110201
11a*	สลักเกลียว M 16 X 250 มม. สำหรับเสาคอนกรีต 12 ม. BOLT, MACHINE, M 16 X 250 mm FOR 12 m CONCRETE POLE	1	1	1	1	01110203
12*	แหวนสี่เหลี่ยมแบน 52 X 52 X 4.5 มม. รู Ø 18 มม. มอก. 258 WASHER, SQUARE, FLAT, 52 X 52 X 4.5 mm HOLE Ø 18 mm TIS 258	-	-	-	1	01180100
13	ที่จับลูกถ้วย สำหรับลูกถ้วย มอก. 227 (แบบ 53-2) CLEVIS, STEEL FLAT, FOR INSULATOR TIS 227 (CLASS 53-2)	1	2	1	1	03130100
14	ลูกถ้วยแรงต่ำ มอก. 227 แบบ ข (แบบ 53-2) INSULATOR, SPOOL TYPE, L.T. TIS 227 TYPE B (CLASS 53-2)	2	2	1	1	03030000
15	เหล็กแผ่น 6 X 30 X 150 มม. แบบเลขที่ SAI-015/22030 (การประกอบเลขที่ 0105) PLATE STEEL 6 X 30 X 150 mm DWG. NO. SAI-015/22030 (ASS. NO. 0105)	2	-	-	-	—
16	พี.จี. คอนเนคเตอร์ สลักคู่ สำหรับสายอลูมิเนียม 25-95 ต.มม. CONNECTOR, PARALLEL GROOVE, DOUBLE BOLT, Al 25-95 mm^2	1	1	-	-	02300102

กองวิศวกรรมไฟฟ้าและเครื่องกล ฝ่ายวิศวกรรม	**การไฟฟ้าส่วนภูมิภาค**	ใช้แทนแบบ ถูกแทนโดยแบบ เขียนเสร็จวันที่ 12 เม.ย. 22
ผู้เขียน ผู้สำรวจ วิศวกร สดศิพงษ์ หัวหน้าแผนก หัวหน้ากอง ผู้อำนวยการฝ่าย	ผู้ว่าการ 1 ก.ย. 25.. การติดตั้งแร็คแรงต่ำกับเสาคอนกรีต 9 ม. 2 วงจร สำหรับการต่อแยกสาย 1 วงจร	แก้แบบวันที่ มิติเป็น มาตราส่วน
รองผู้ว่าการฝ่ายเทคนิค	SECONDARY RACK INSTALLATION ON 9 m CONCRETE POLE 2-CIRCUITS FOR 1-CIRCUIT TAP LINE	แบบเลขที่ SAI-015/22024 แผ่นที่ 5 ของจำนวน 6 แผ่น

1 ก.ย. 25

การประกอบเลขที่
ASSEMBLY NO. 0214

บัญชีวัสดุ
BILL OF MATERIAL

ลำดับที่ ITEM	รายละเอียด DESCRIPTION	จำนวน REQ'D 1	2	3	4	วัสดุเลขที่ MAT. NO.
17	คอนเนคเตอร์เข้าปลายสายอะลูมิเนียม 25-35 ต.มม. CONNECTOR, DEADEND, Al 25-35 mm^2	1	1	–	–	02310000
18	PVC เทป กว้าง 19 มม. (ใช้ความยาว 2 ม. ต่อ จุด) มอก. 386 PVC TAPE 19 mm WIDE (2 m LONG PER POINT) TIS 386			–	–	02180001 or 02180002

หมายเหตุ 1 การประกอบพี.จี. คอนเนคเตอร์ ดูแบบเลขที่ SAI-015/21032

~~2 การประกอบคอนเนคเตอร์เข้าปลายสาย ดูแบบเลขที่ SAI-015/22015~~

NOTES 1 P.G. CONNECTOR ASSEMBLY SEE DWG. NO. SAI-015/21032

2 DEADEND CONNECTOR ASEMBLY SEE DWG. NO. SAI-015/22015

อดิวิทย์ ทองลา พชง.3 ผปร. กฟส.อล. กฟจ.กบ. กฟต.2 สายงาน (ต) ผวก. PEA

กองวิศวกรรมไฟฟ้าและเครื่องกล ฝ่ายวิศวกรรม	**การไฟฟ้าส่วนภูมิภาค**	ใช้แทนแบบ.......... ถูกแทนโดยแบบ..........
ผู้เขียน.......... ผู้สำรวจ.......... วิศวกร.......... หัวหน้าแผนก.......... หัวหน้ากอง.......... ผู้อำนวยการฝ่าย..........	ผู้ว่าการ.......... 7 ก.ย. 22 การติดตั้งแร็คแรงต่ำบนเสาคอนกรีต 9 ม. 2 วงจร สำหรับการต่อแยกสาย 1 วงจร	เขียนเสร็จวันที่ 12 เม.ย. 22 แก้แบบวันที่.......... มิติเป็น.......... มาตราส่วน..........
รองผู้ว่าการฝ่ายเทคนิค 7 ก.ย. 22	SECONDARY RACK INSTALLATION ON 9 m CONCRETE POLE 2-CIRCUITS FOR 1-CIRCUIT TAP LINE	แบบเลขที่ SAI-015/22024 แผ่นที่ 6 ของจำนวน 6 แผ่น