การประกอบเลขที่
ASSEMBLY NO. 0303

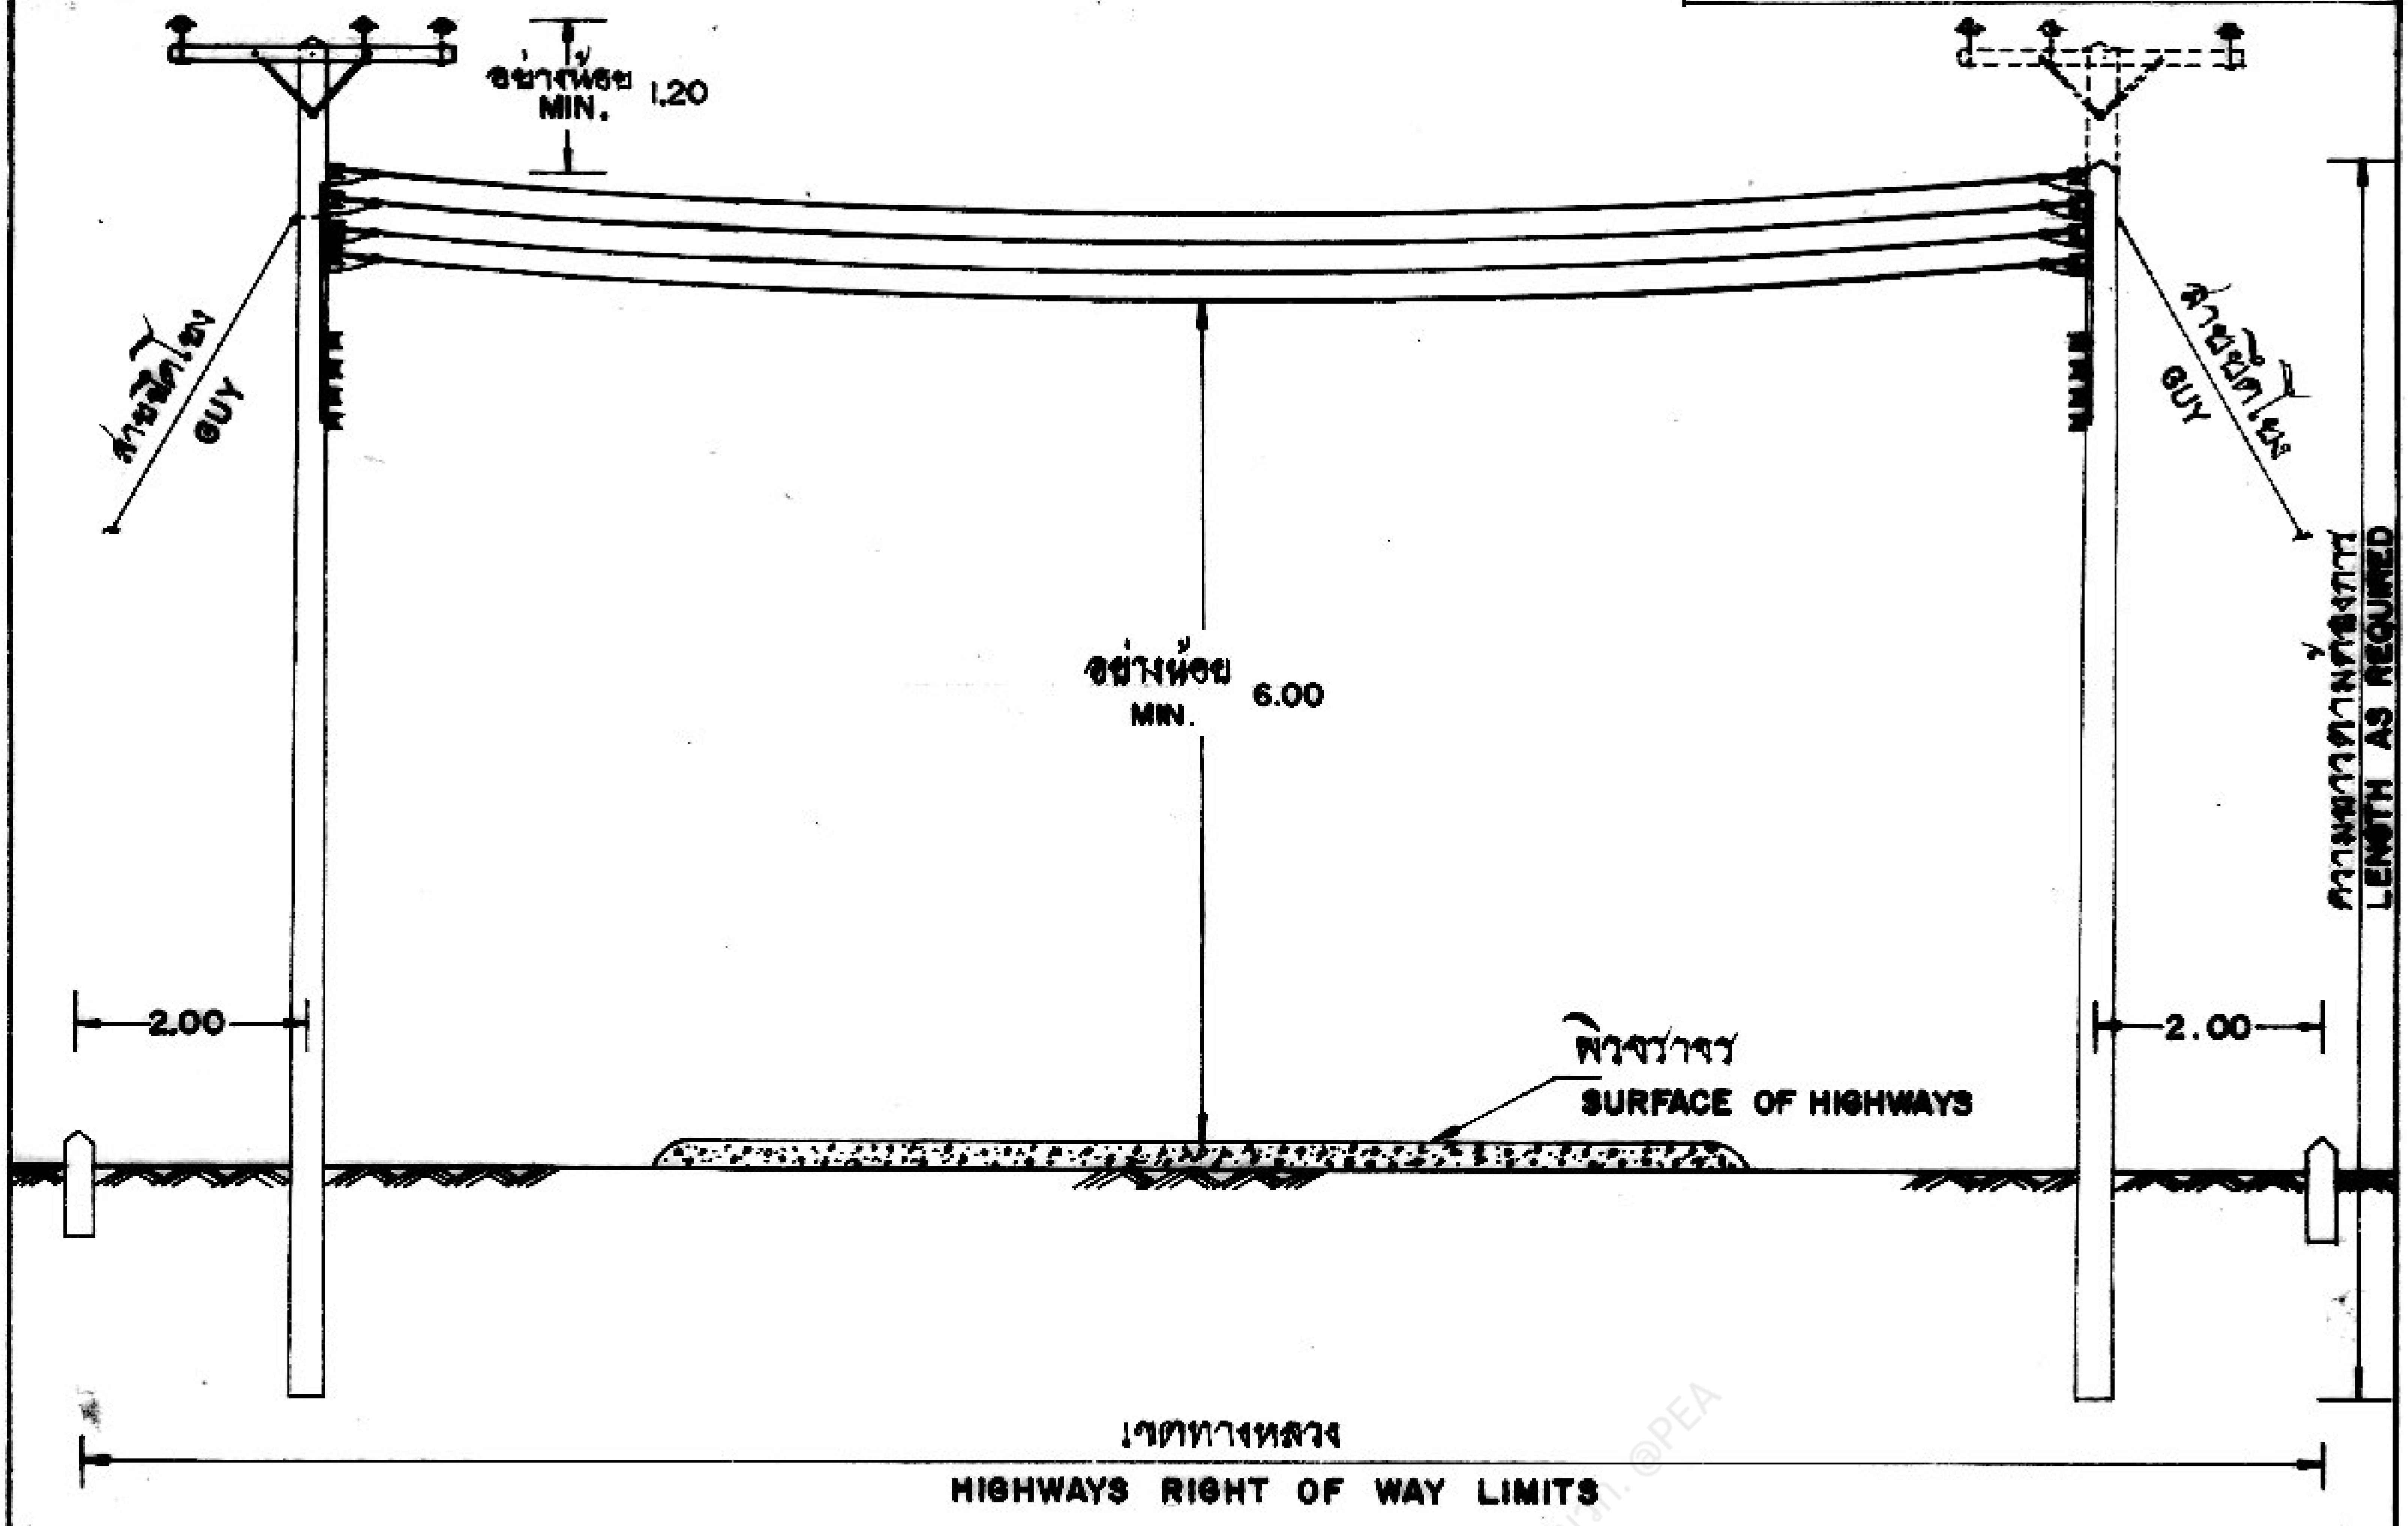

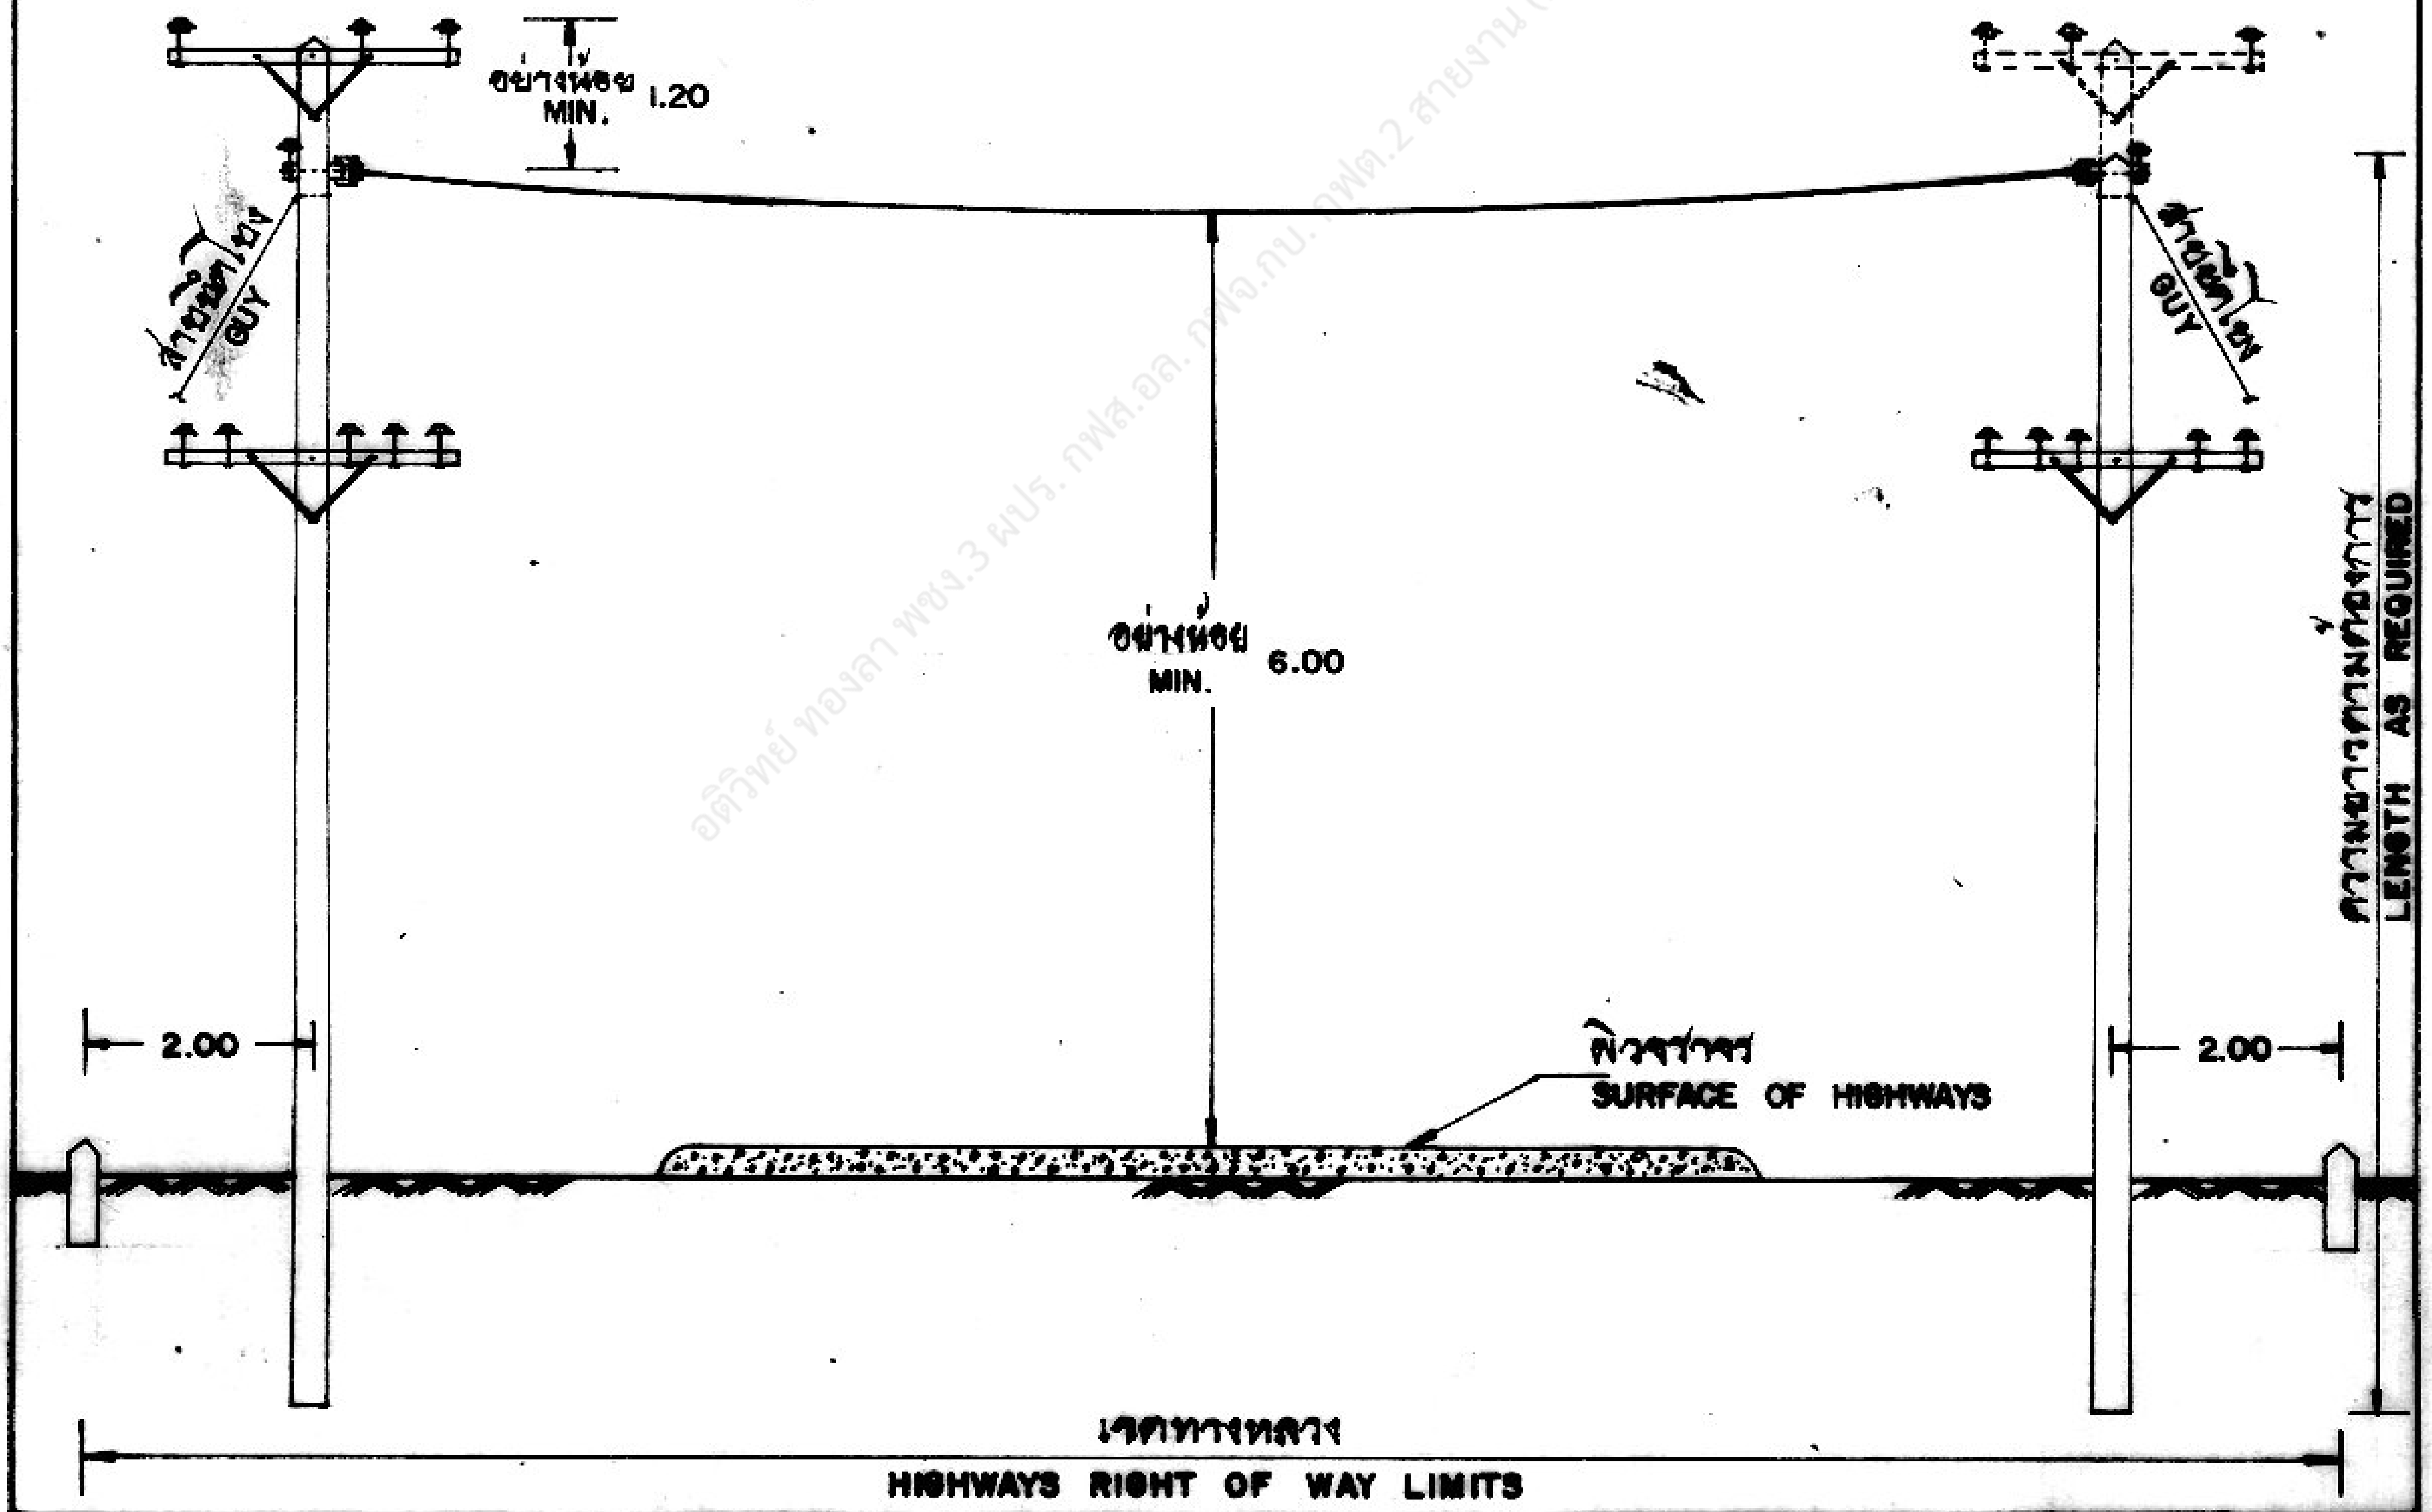

อดิวิทย์ ทองลา พชง.3 ผปร. กฟส.อล. กฟจ.กบ. กฟต.2 สายงาน (ต) ผหพ. @PEA

กองวิศวกรรม

ผู้เขียน ....
สถาปนิก ....
วิศวกร ....
หัวหน้าแผนก ....
ผู้อำนวยการกอง ....
รองผู้ว่าการฝ่ายเทคนิค
....

การไฟฟ้าส่วนภูมิภาค

ผู้ว่าการ 20.9.18

การพาดสายแรงต่ำไม่เกิน 1 kV ข้ามถนน

L.T. 1 kV OR LESS ACROSS THE HIGHWAYS

ใช้แทนแบบ ....
ถูกแทนโดยแบบ ....
เขียนเสร็จวันที่ 1 ต.ค.18
แก้แบบวันที่ ....
มิติเป็น เมตร
มาตราส่วน 1 : 125
แบบเลขที่ 302-015/18068
แผ่นที่ 1 ของจำนวน 1 แผ่น