

การประกอบเลขที่ ASSEMBLY NO. 5277

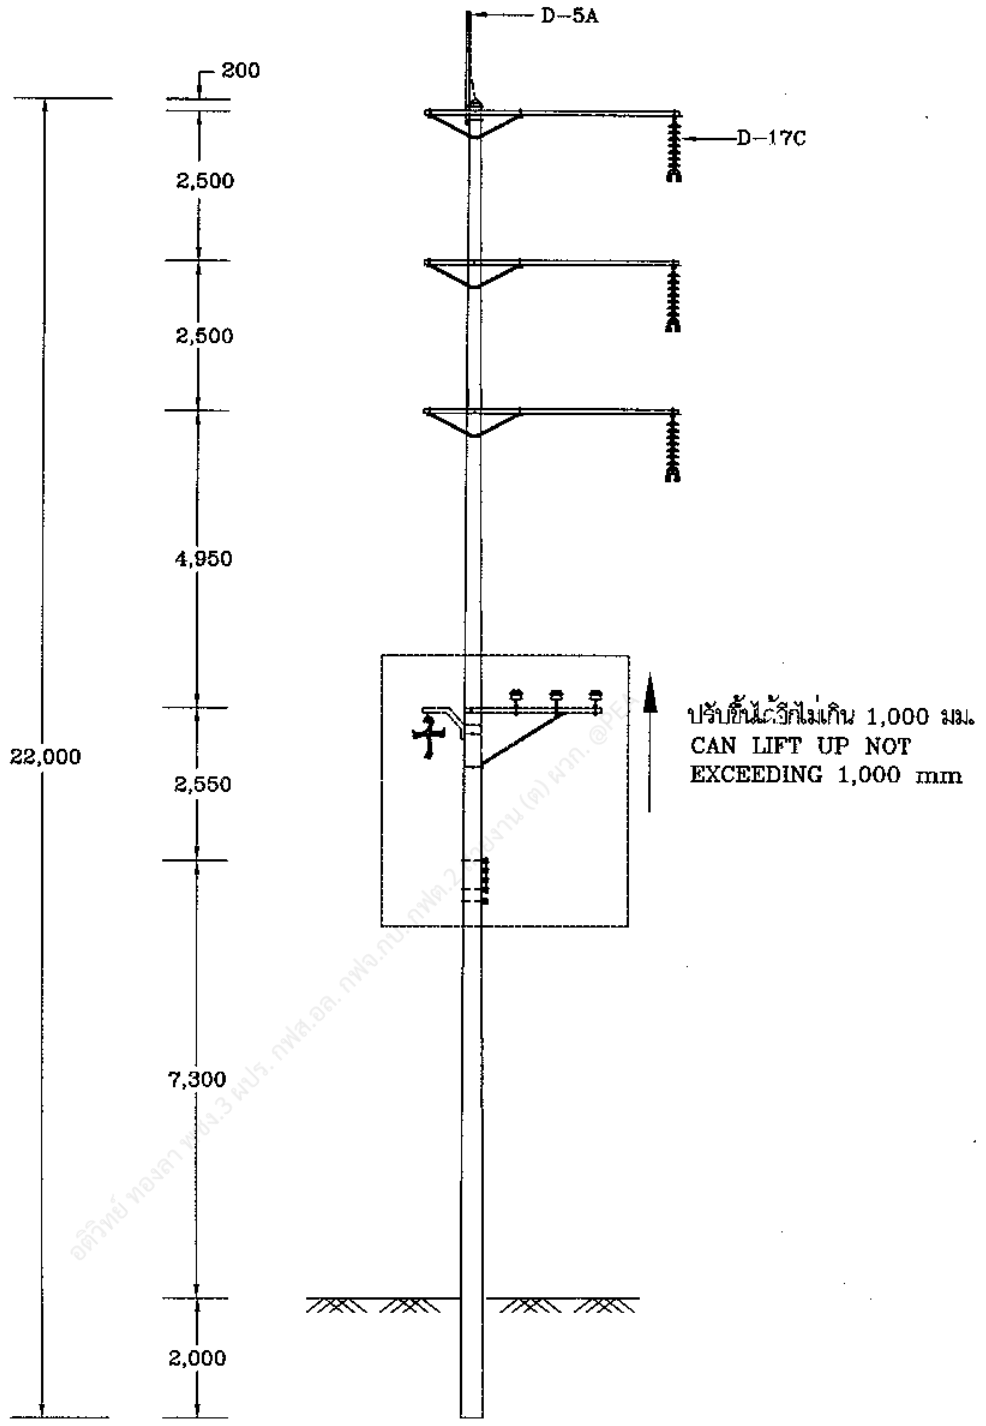

กองวิศวกรรมไฟฟ้าและเครื่องกล ฝ่ายวิศวกรรม	การไฟฟ้าส่วนภูมิภาค	ใช้แทนแบบ ..... ถูกแทนโดยแบบ .....
ผู้เขียน ...สมนึก...สาคร..... ผู้สำรวจ ..... วิศวกร ..... หัวหน้าแผนก ..... ผู้อำนวยการกอง ..... ผู้อำนวยการฝ่าย	ผู้ว่าการ ..... 16 พ.ย. 2541	เขียนเสร็จวันที่ 21 ตค. 2541 แก้แบบวันที่ ..... มิติเป็น ...มิลลิเมตร..... มาตราส่วน ..1 : 125.....
	115 kV วงจรเดี่ยว สายไฟฟ้าคู่ เสาสำหรับทางตรง แบบ SD–TG–7	
รองผู้ว่าการเทคนิคและบริการ	115 kV SINGLE CIRCUIT DOUBLE CONDUCTOR TANGENT STRUCTURE TYPE SD–TG–7	แบบเลขที่ SA1–015/41009 แผ่นที่ 1 ของจำนวน 4 แผ่น

16 พ.ย. 2541

การประกอบเลขที่ ASSEMBLY NO.	5277

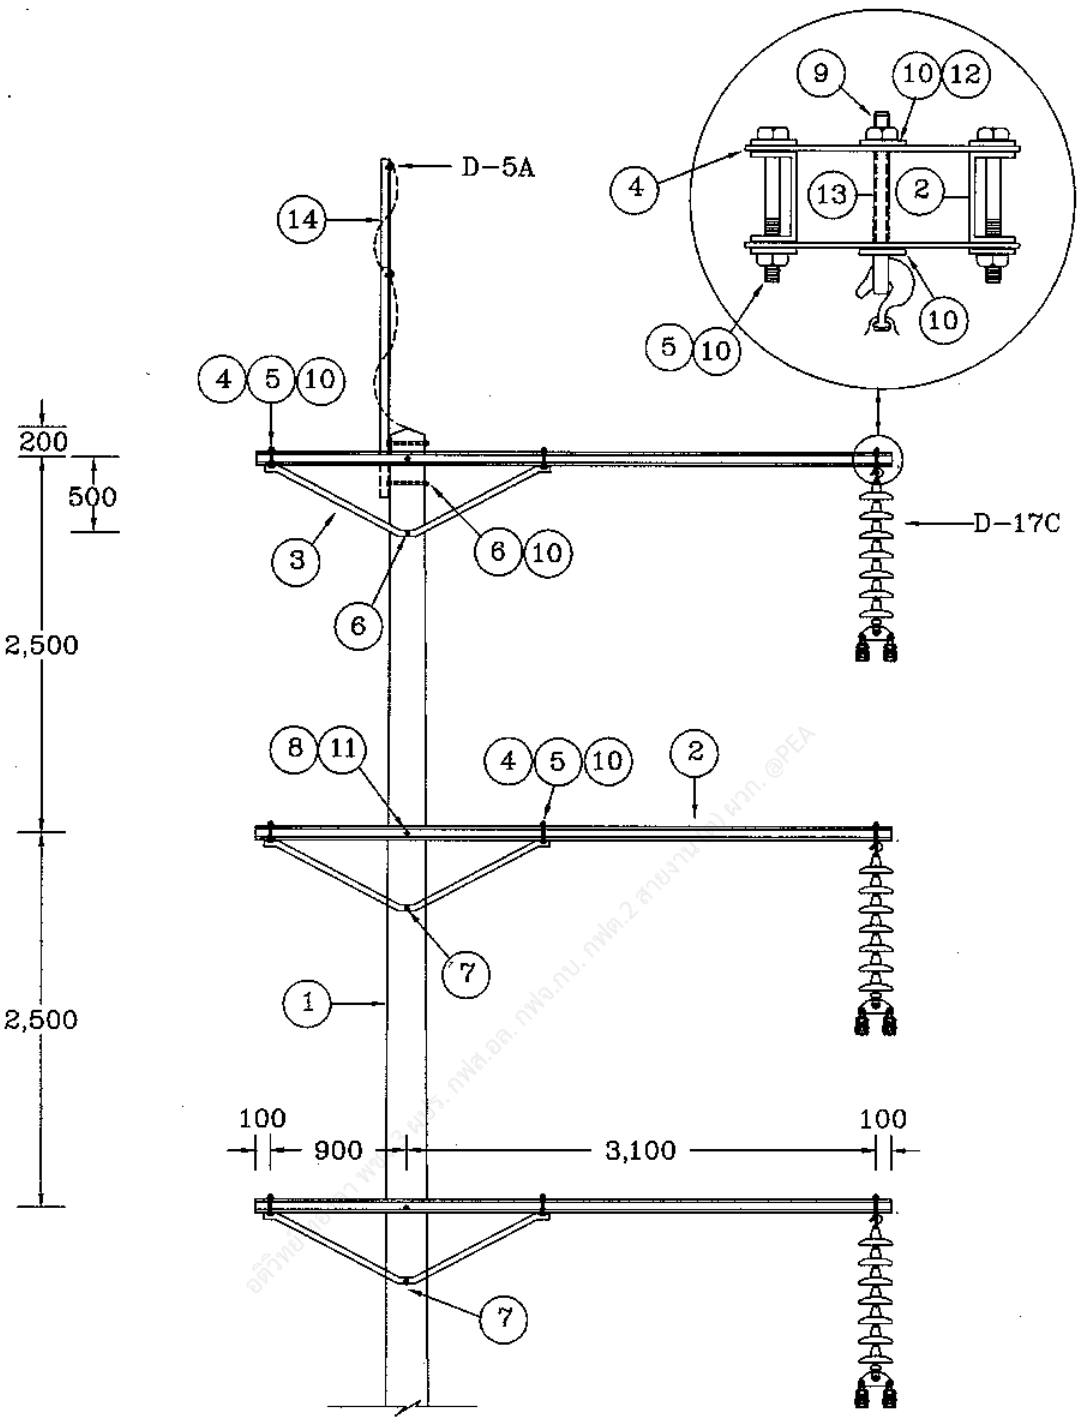

กองวิศวกรรมไฟฟ้าและเครื่องกล ฝ่ายวิศวกรรม	การไฟฟ้าส่วนภูมิภาค	ใช้แทนแบบ..... ถูกแทนโดยแบบ.....
ผู้เขียน สมนึก สาครฯ ผู้สำรวจ..... วิศวกร..... หัวหน้าแผนก..... ผู้อำนวยการกอง..... ผู้อำนวยการฝ่าย.....	ผู้ว่าการ.....	เขียนเสร็จวันที่ 21 ตค. 2541 แก้แบบวันที่ .....
	115 kV วงจรเดี่ยว สายไฟฟ้า เสาสำหรับทางตรง แบบ SD-TG-7	มิติเป็น มิลลิเมตร มาตราส่วน 1 : 50
รองผู้ว่าการเทคนิคและบริการ	115 kV SINGLE CIRCUIT DOUBLE CONDUCTOR TANGENT STRUCTURE TYPE SD-TG-7	แบบเลขที่ SA1-015/41009 แผ่นที่ 2 ของจำนวน 4 แผ่น

16 พ.ย. 2541

16 พ.ย. 2541

การประกอบเลขที่ ASSEMBLY NO. 5277

บัญชีวัสดุ
BILL OF MATERIAL

ลำดับที่ ITEM	รายละเอียด DISCRIPTION	จำนวน REQ'D	วัสดุเลขที่ MAT.NO.
1	เสาคอนกรีต 22 ม. POLE, CONCRETE, 22 m LONG	1	00010011
2	คอนสายแบบเหล็กรูปรางน้ำ ขนาด 100x50x5 มม. ยาว 4.20 ม. มอก.116 CROSSARM,STEEL,CHANNEL 100x50x5 mm, 4.20 m LONG, TIS 116	6	01030003
3	เหล็กฉากรับคอนสาย ขนาด 50x50x6 มม. ช่วงกว้าง 1,800 มม. ดรอพ 450 มม. BRACE,ANGLE STEEL, 50x50x6 mm, 1,800 mm WIDE, 450 mm, DROP	6	00120007
4	แผ่นเหล็ก ขนาด 6x100x450 มม. PLATE,STEEL 6x100x450 mm	12	01030002
5	สลักเกลียว M 16x170 มม. BOLT, MACHINE, M 16x170 mm	18	01110201
6	สลักเกลียว M 16x300 มม. BOLT, MACHINE, M 16x300 mm	3	01110204
7	สลักเกลียว M 16x350 มม. BOLT, MACHINE, M 16x350 mm	2	01110205
8	สลักเกลียว M 20x350 มม. BOLT, MACHINE, M 20x350 mm	3	01110300
9	สลักห่วงโอแวล M 16x150 มม. BOLT, OVAL EYE, M 16x150 mm	3	01150000
10	แหวนสี่เหลี่ยมแบน 52x52x4.5 มม. รู ø 18 มม. มอก. 258 WASHER, SQUARE, FLAT 52x52x4.5 mm, HOLE ø 18 mm, TIS 258	44	01180100
11	แหวนสี่เหลี่ยมแบน 62x62x6 มม. รู ø 22 มม. มอก. 258 WASHER, SQUARE, FLAT 62x62x6 mm, HOLE ø 22 mm, TIS 258	6	01180101
12	แหวนสปริง M 16 มอก. 259 WASHER, LOCK, M 16 TIS 259	3	01180301
13	ท่อเหล็กขนาดระบุ 20 ประเภทที่ 2 ยาว 100 มม. มอก.277 แต่ไม่มีเกลียวที่ปลาย PIPE,STEEL,SIZE 20,TYPE 2,100 mm. LONG TIS.277 BUT WITHOUT THREADED END	3	01050000
14	เหล็กฉาก รับสายล่อฟ้า 65x65x6 มม. ยาว 2,500 มม. STEEL ANGLE, OVERHEAD GROUND WIRE BAYONET 65x65x6 mm 2,500 mm LONG	1	01010004
D-17C	การประกอบลูกถ้วยแขวน SUSPENSION INSULATOR ASSEMBLY	3	
D-5A	การต่อสายล่อฟ้า OVERHEAD GROUND WIRE CONNECTION	1	

กองวิศวกรรมไฟฟ้าและเครื่องกล
ฝ่ายวิศวกรรม

ผู้เขียน ....สมนึก...สาคร...
ผู้สำรวจ.....
วิศวกร.....
หัวหน้าแผนก.....
ผู้อำนวยการกอง.....
ผู้อำนวยการฝ่าย.....

รองผู้ว่าการเทคนิคและบริการ
.....

16 พ.ย. 2541

การไฟฟ้าส่วนภูมิภาค

ผู้ว่าการ ..... 16 พ.ย. 2541


115 kV วงจรเดี่ยว สายไฟฟ้าคู่
เสาสำหรับทางตรง
แบบ SD-TG-7


115 kV SINGLE CIRCUIT DOUBLE CONDUCTOR
TANGENT STRUCTURE
TYPE SD-TG-7

ใช้แทนแบบ.....
ถูกแทนโดยแบบ.....
เขียนแสร็จวันที่ 21 ตค. 2541
แก้แบบวันที่ .....
มิติเป็น.....
มาตราส่วน.....

แบบเลขที่ SA1-015/41009
แผ่นที่ 3 ของจำนวน 4 แผ่น

การประกอบเลขที่ ASSEMBLY NO.	5277

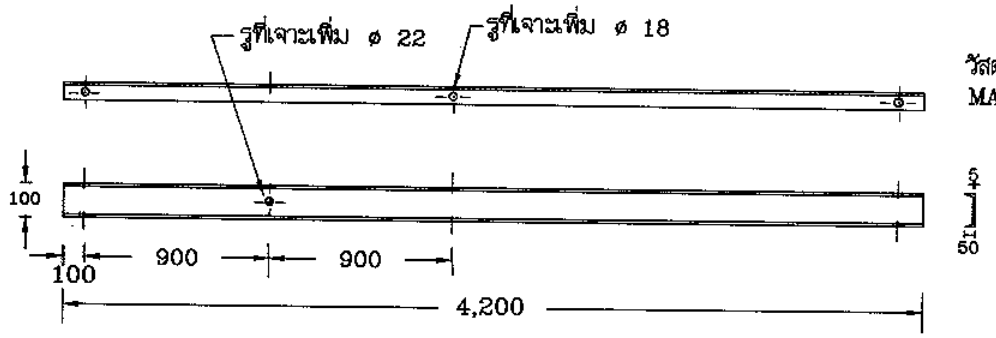

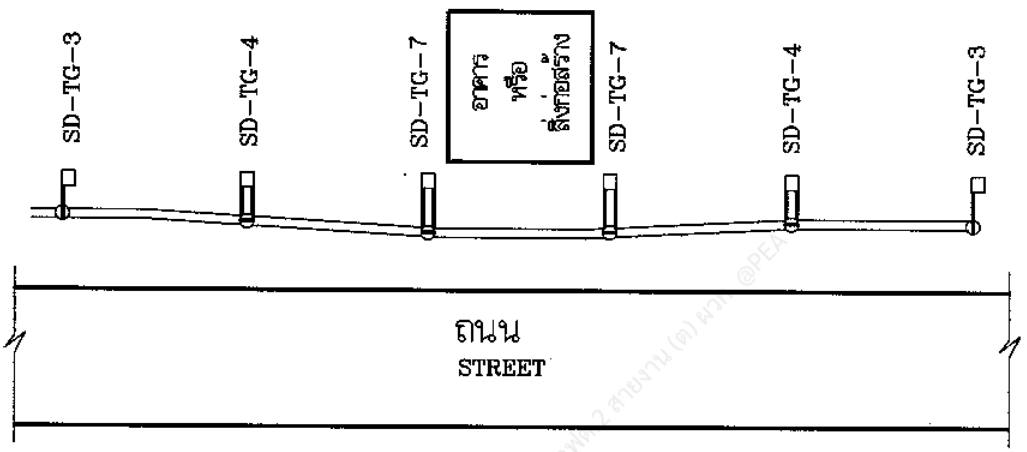

การนำไปใช้งาน
APPLICATION

หมายเหตุ
แบบนี้นำมาใช้กรณีที่ต้องการเพิ่มระยะห่างระหว่างสายไฟฟ้ากับอาคาร ป้าย และสิ่งก่อสร้างอื่น ๆ

NOTES

THIS DWG. USE FOR ADDITIONAL CLEARANCES BETWEEN CONDUCTOR AND BUILDING, OR SIGN OR OTHER STRUCTURE.

กองวิศวกรรมไฟฟ้าและเครื่องกล ฝ่ายวิศวกรรม	การไฟฟ้าส่วนภูมิภาค	ใช้แทนแบบ..... ถูกแทนโดยแบบ.....
ผู้เขียน สมนึก สาคร ผู้สำรวจ..... วิศวกร..... หัวหน้าแผนก..... ผู้อำนวยการกอง..... ผู้อำนวยการฝ่าย.....	ผู้ว่าการ ..... 16 พ.ย. 2541	เขียนเสร็จวันที่ 21 ตค. 2541 แก้แบบวันที่ ..... มิติเป็น มิลลิเมตร มาตราส่วน.....
	115 kV วงจรเดี่ยว สายไฟฟ้าคู่ เสาสำหรับทางตรง แบบ SD-TG-7	
รองผู้ว่าการเทคนิคและบริการ	115 kV SINGLE CIRCUIT DOUBLE CONDUCTOR TANGENT STRUCTURE TYPE SD-TG-7	แบบเลขที่ SA1-015/41009 แผ่นที่ 4 ของจำนวน 4 แผ่น

16 พ.ย. 2541