การประกอบเลขที่
ASSEMBLY NO. **3237**

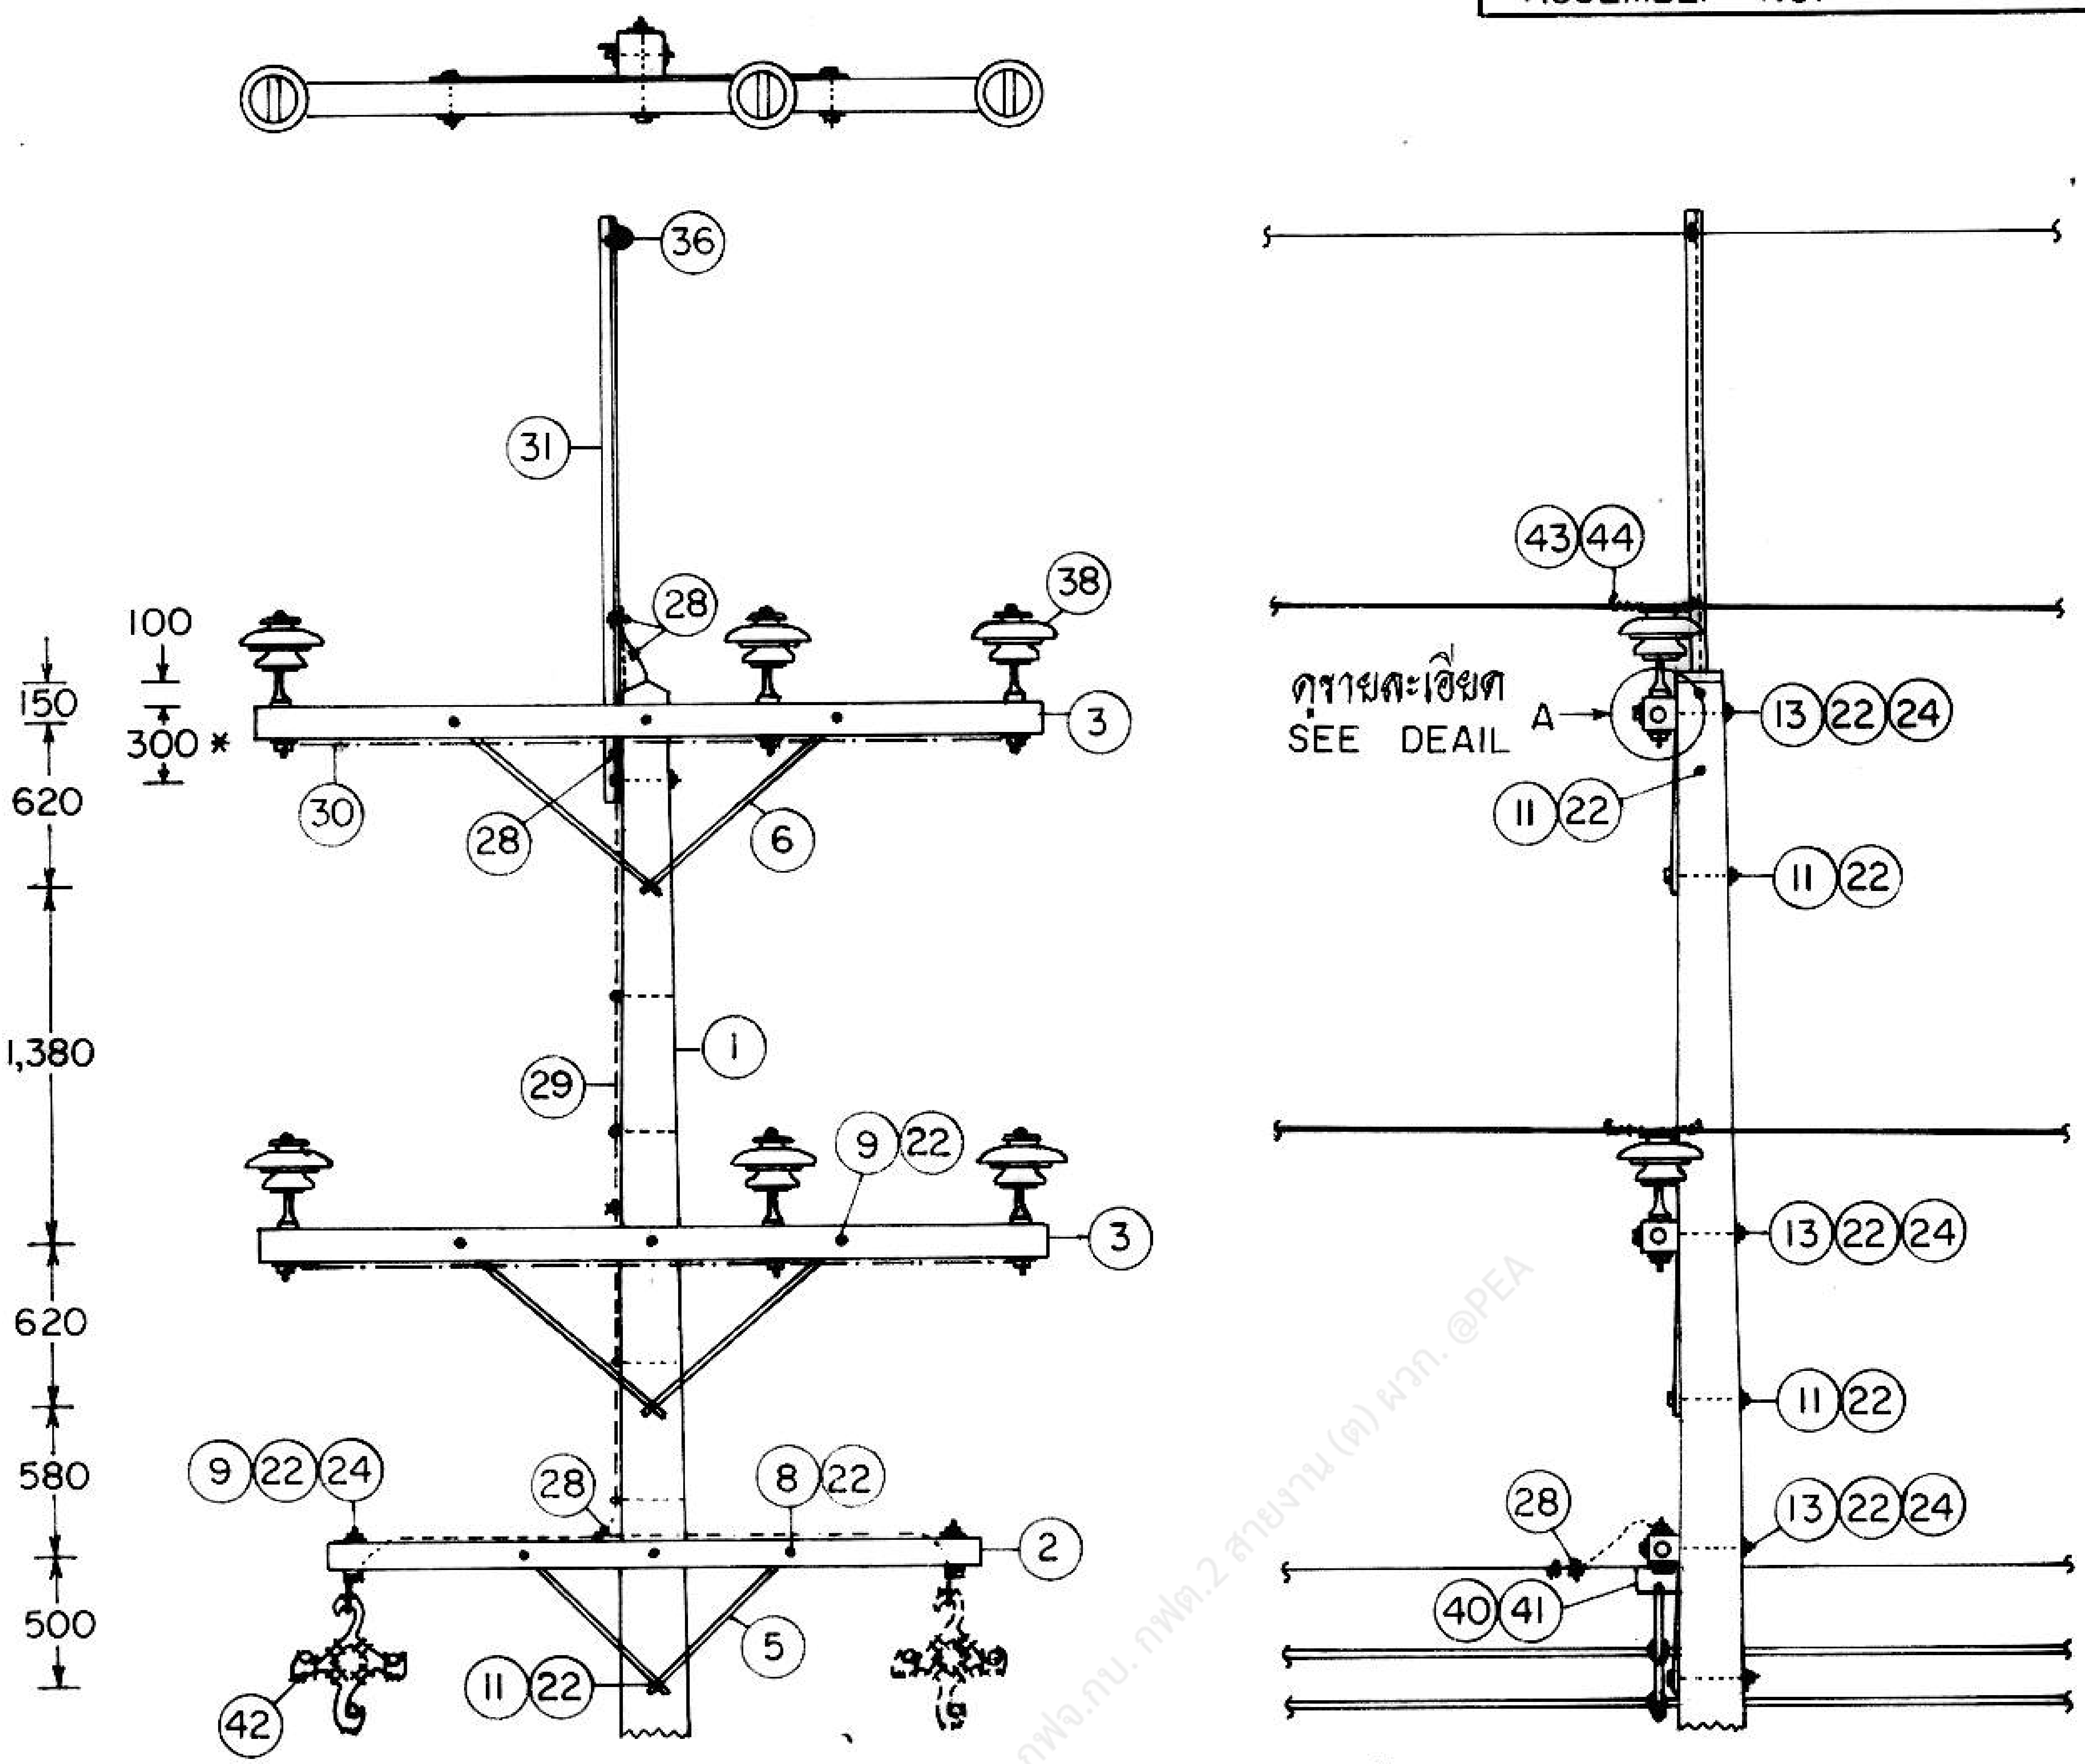

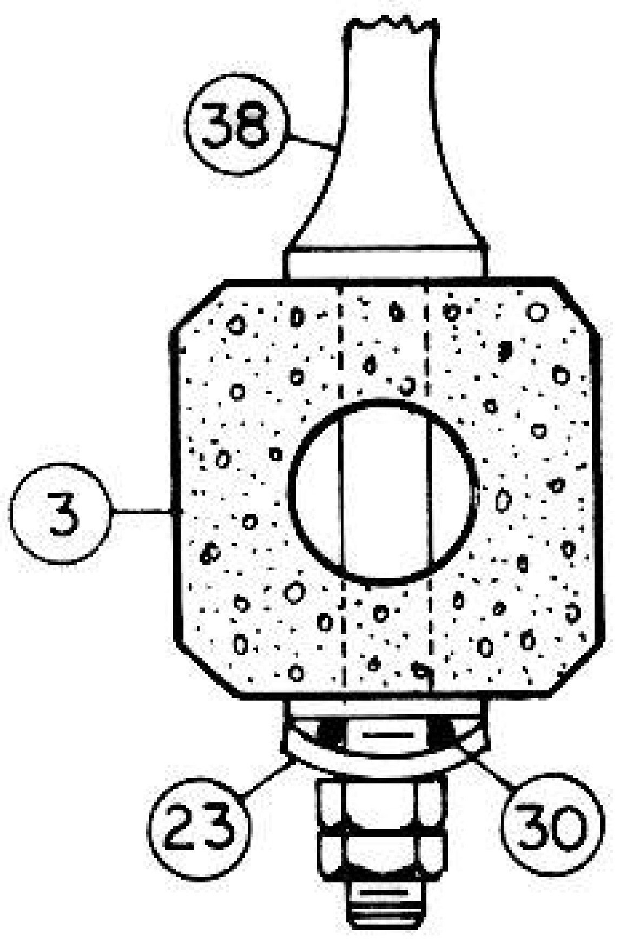

รายละเอียด A
DETAIL A

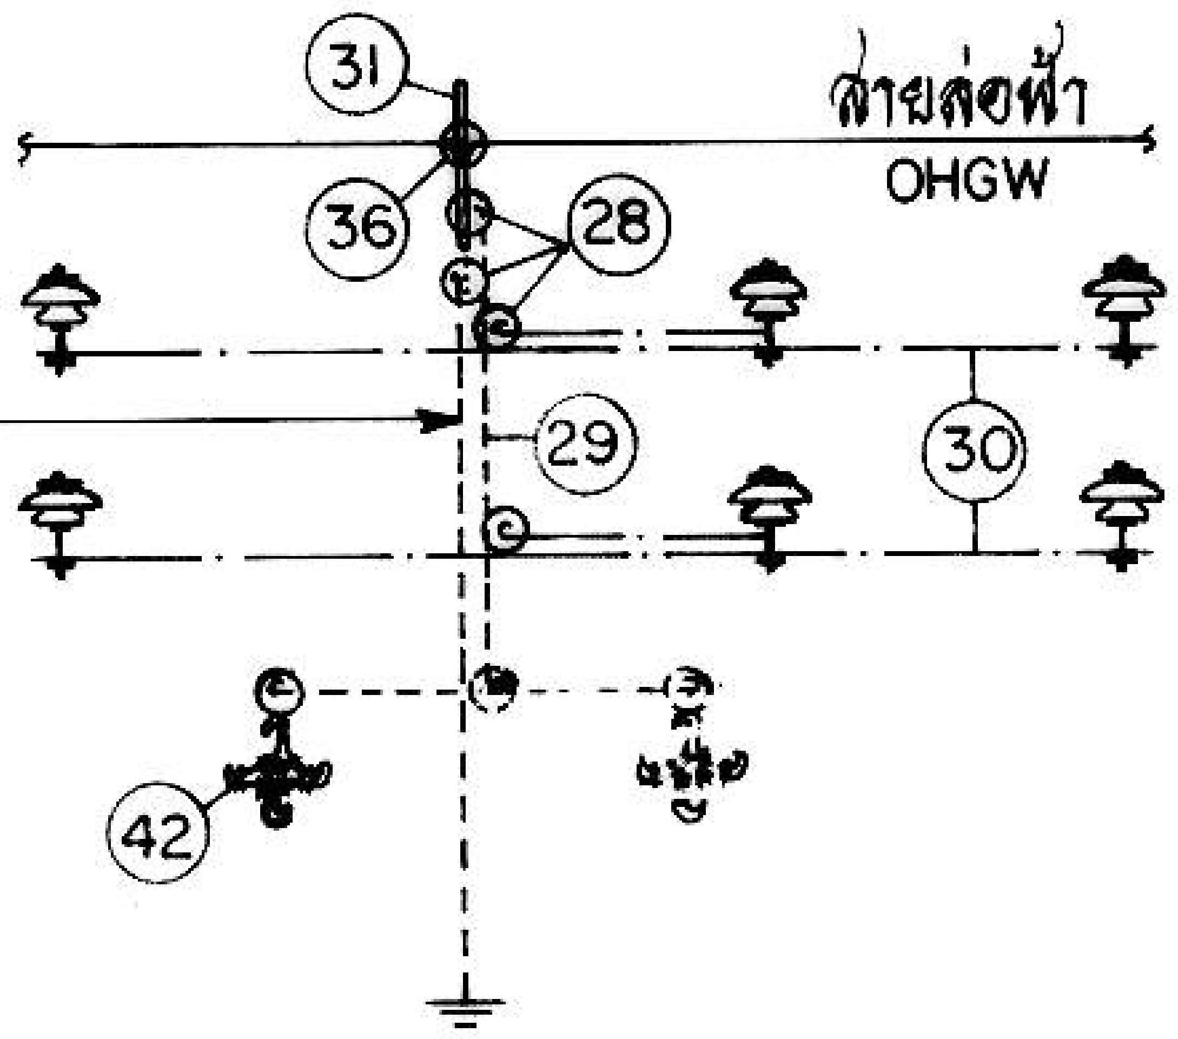

แผนผังแสดงการต่อลงดิน
EARTHING DIAGRAM

I สำหรับทางตรงและทางโค้งไม่เกิน 5°
FOR LINE ANGLE NOT EXCEEDING 5°

กองวิศวกรรมไฟฟ้าและเครื่องกล ฝ่ายวิศวกรรม	**การไฟฟ้าส่วนภูมิภาค**	ใช้แทนแบบ .... ถูกแทนโดยแบบ ....
ผู้เขียน .... ผู้สำรวจ .... วิศวกร .... หัวหน้าแผนก .... ผู้อำนวยการกอง .... ผู้อำนวยการฝ่าย	ผู้ว่าการ .... 16 ต.ค. 34	เขียนเสร็จวันที่ 2 ก.ย. 34 แก้แบบวันที่ .... ผลิตเป็น มิลลิเมตร มาตราส่วน 1 : 50
	การประกอบคอนกับเสาคอนกรีต 33 kV 3 - 4 วงจร	
รองผู้ว่าการฝ่ายเทคนิค	33 kV CROSSARM ASSEMBLY ON CONCRETE POLE 3 - 4 CIRCUIT	แบบเลขที่ SAI-015/34024 แผ่นที่ 1 ของจำนวน 11 แผ่น

11 ต.ค. 2534 (เทพ.)

อดิวิทย์ กฟส.อล. กฟจ.กบ. กฟต.2 สายงาน (ต) ผวก. @PEA

การประกอบเลขที่
ASSEMBLY NO. **3237**

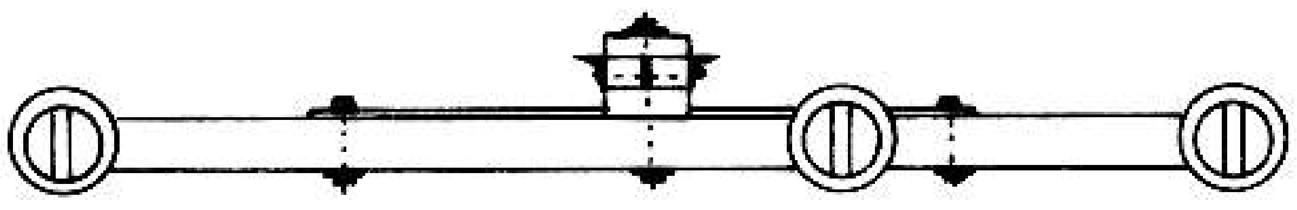

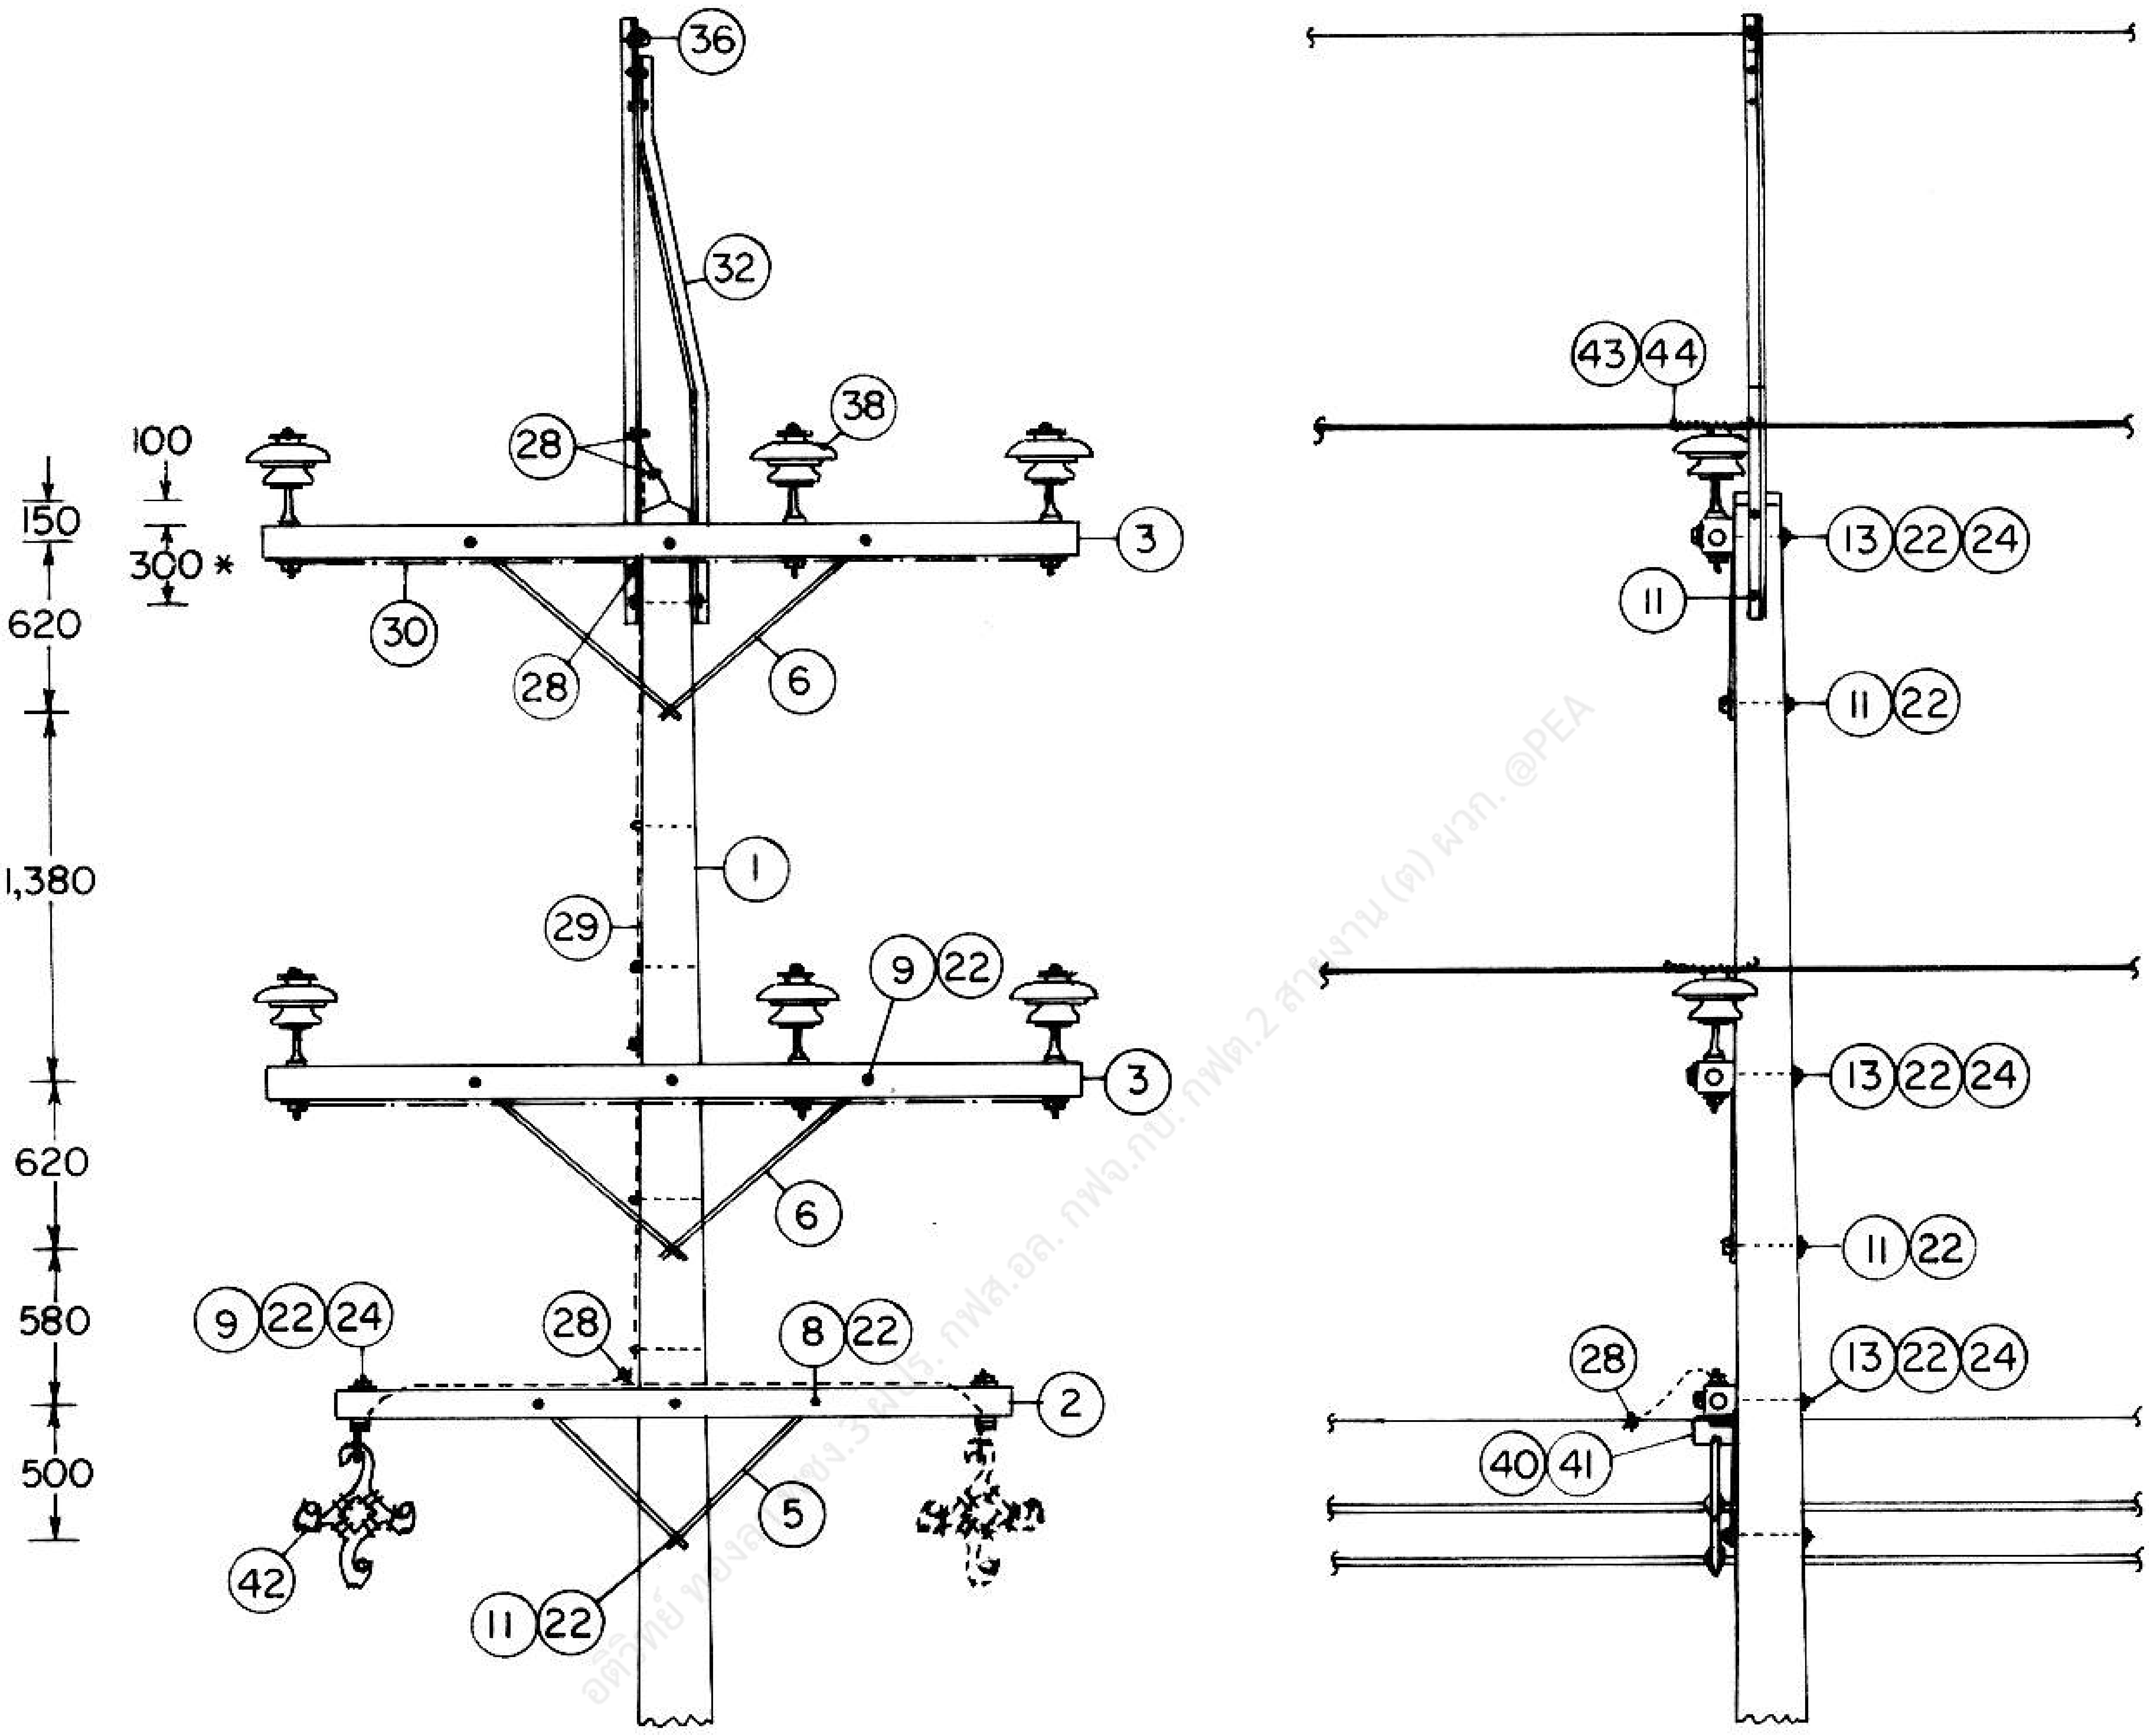

II สำหรับทางโค้งไม่เกิน 30°
FOR LINE ANGLE NOT EXCEEDING 30°

กองวิศวกรรมไฟฟ้าและเครื่องกล ฝ่ายวิศวกรรม	**การไฟฟ้าส่วนภูมิภาค**	ใช้แทนแบบ.......... ถูกแทนโดยแบบ..........
ผู้เขียน.......... ผู้สำรวจ.......... วิศวกร.......... หัวหน้าแผนก.......... ผู้อำนวยการกอง.......... ผู้อำนวยการฝ่าย..........	ผู้ว่าการ.......... 16.ต.ค.34	เขียนเสร็จวันที่ 2 ก.ย. 34 แก้แบบวันที่.......... มิติเป็น มิลลิเมตร มาตราส่วน 1 : 50
	การประกอบคอนกับเสาคอนกรีต 33 kV 3 - 4 วงจร	
รองผู้ว่าการฝ่ายเทคนิค..........	33 kV CROSSARM ASSEMBLY ON CONCRETE POLE 3 - 4 CIRCUIT	แบบเลขที่ SAI-015/34024 แผ่นที่ 2 ของจำนวน 11 แผ่น

11 ต.ค. 2534

อติวิทย์ ... ชง.3 ฝปร. กฟส.อล. กฟจ.กบ. กฟต.2 สายงาน (ต) ผวก. @PEA

การประกอบเลขที่
ASSEMBLY NO. 3237

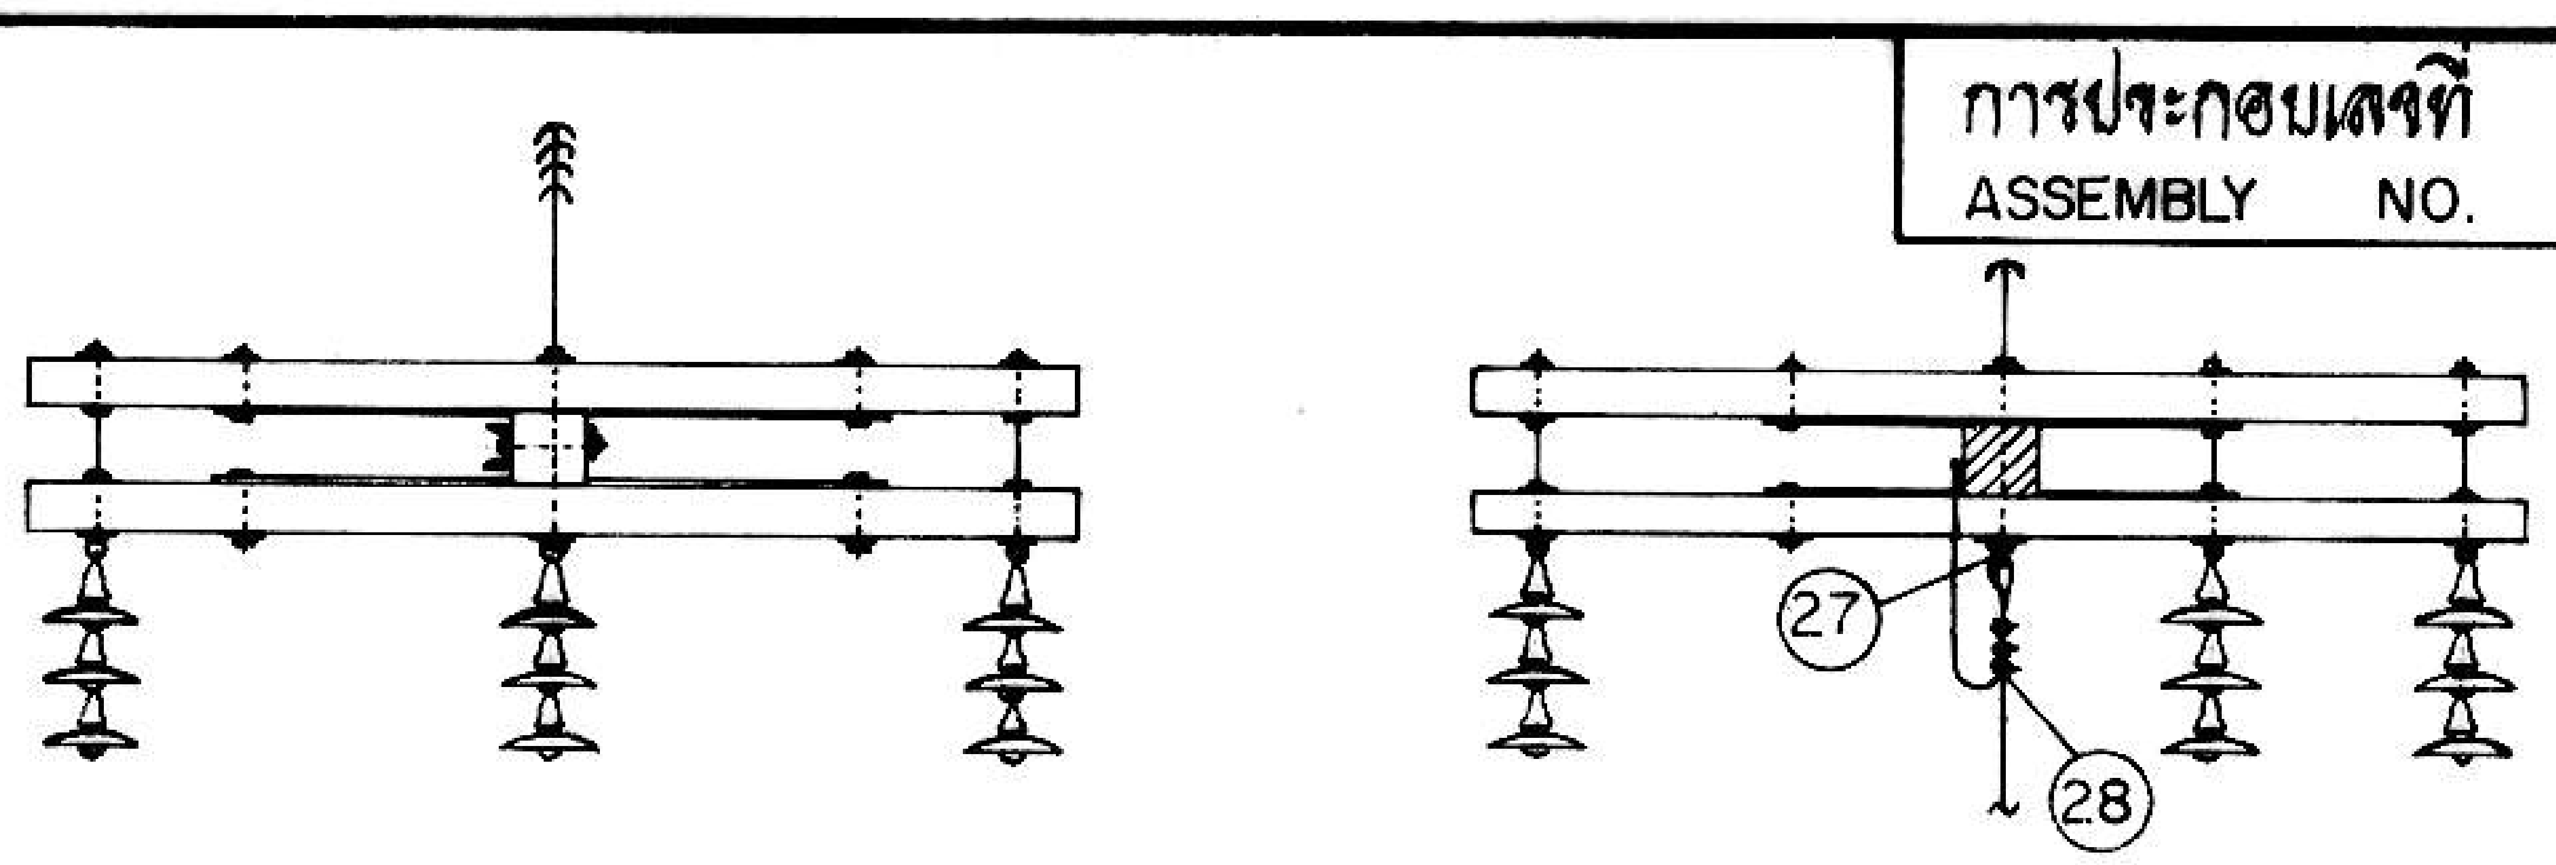

รูปตัด
SECTION A-A

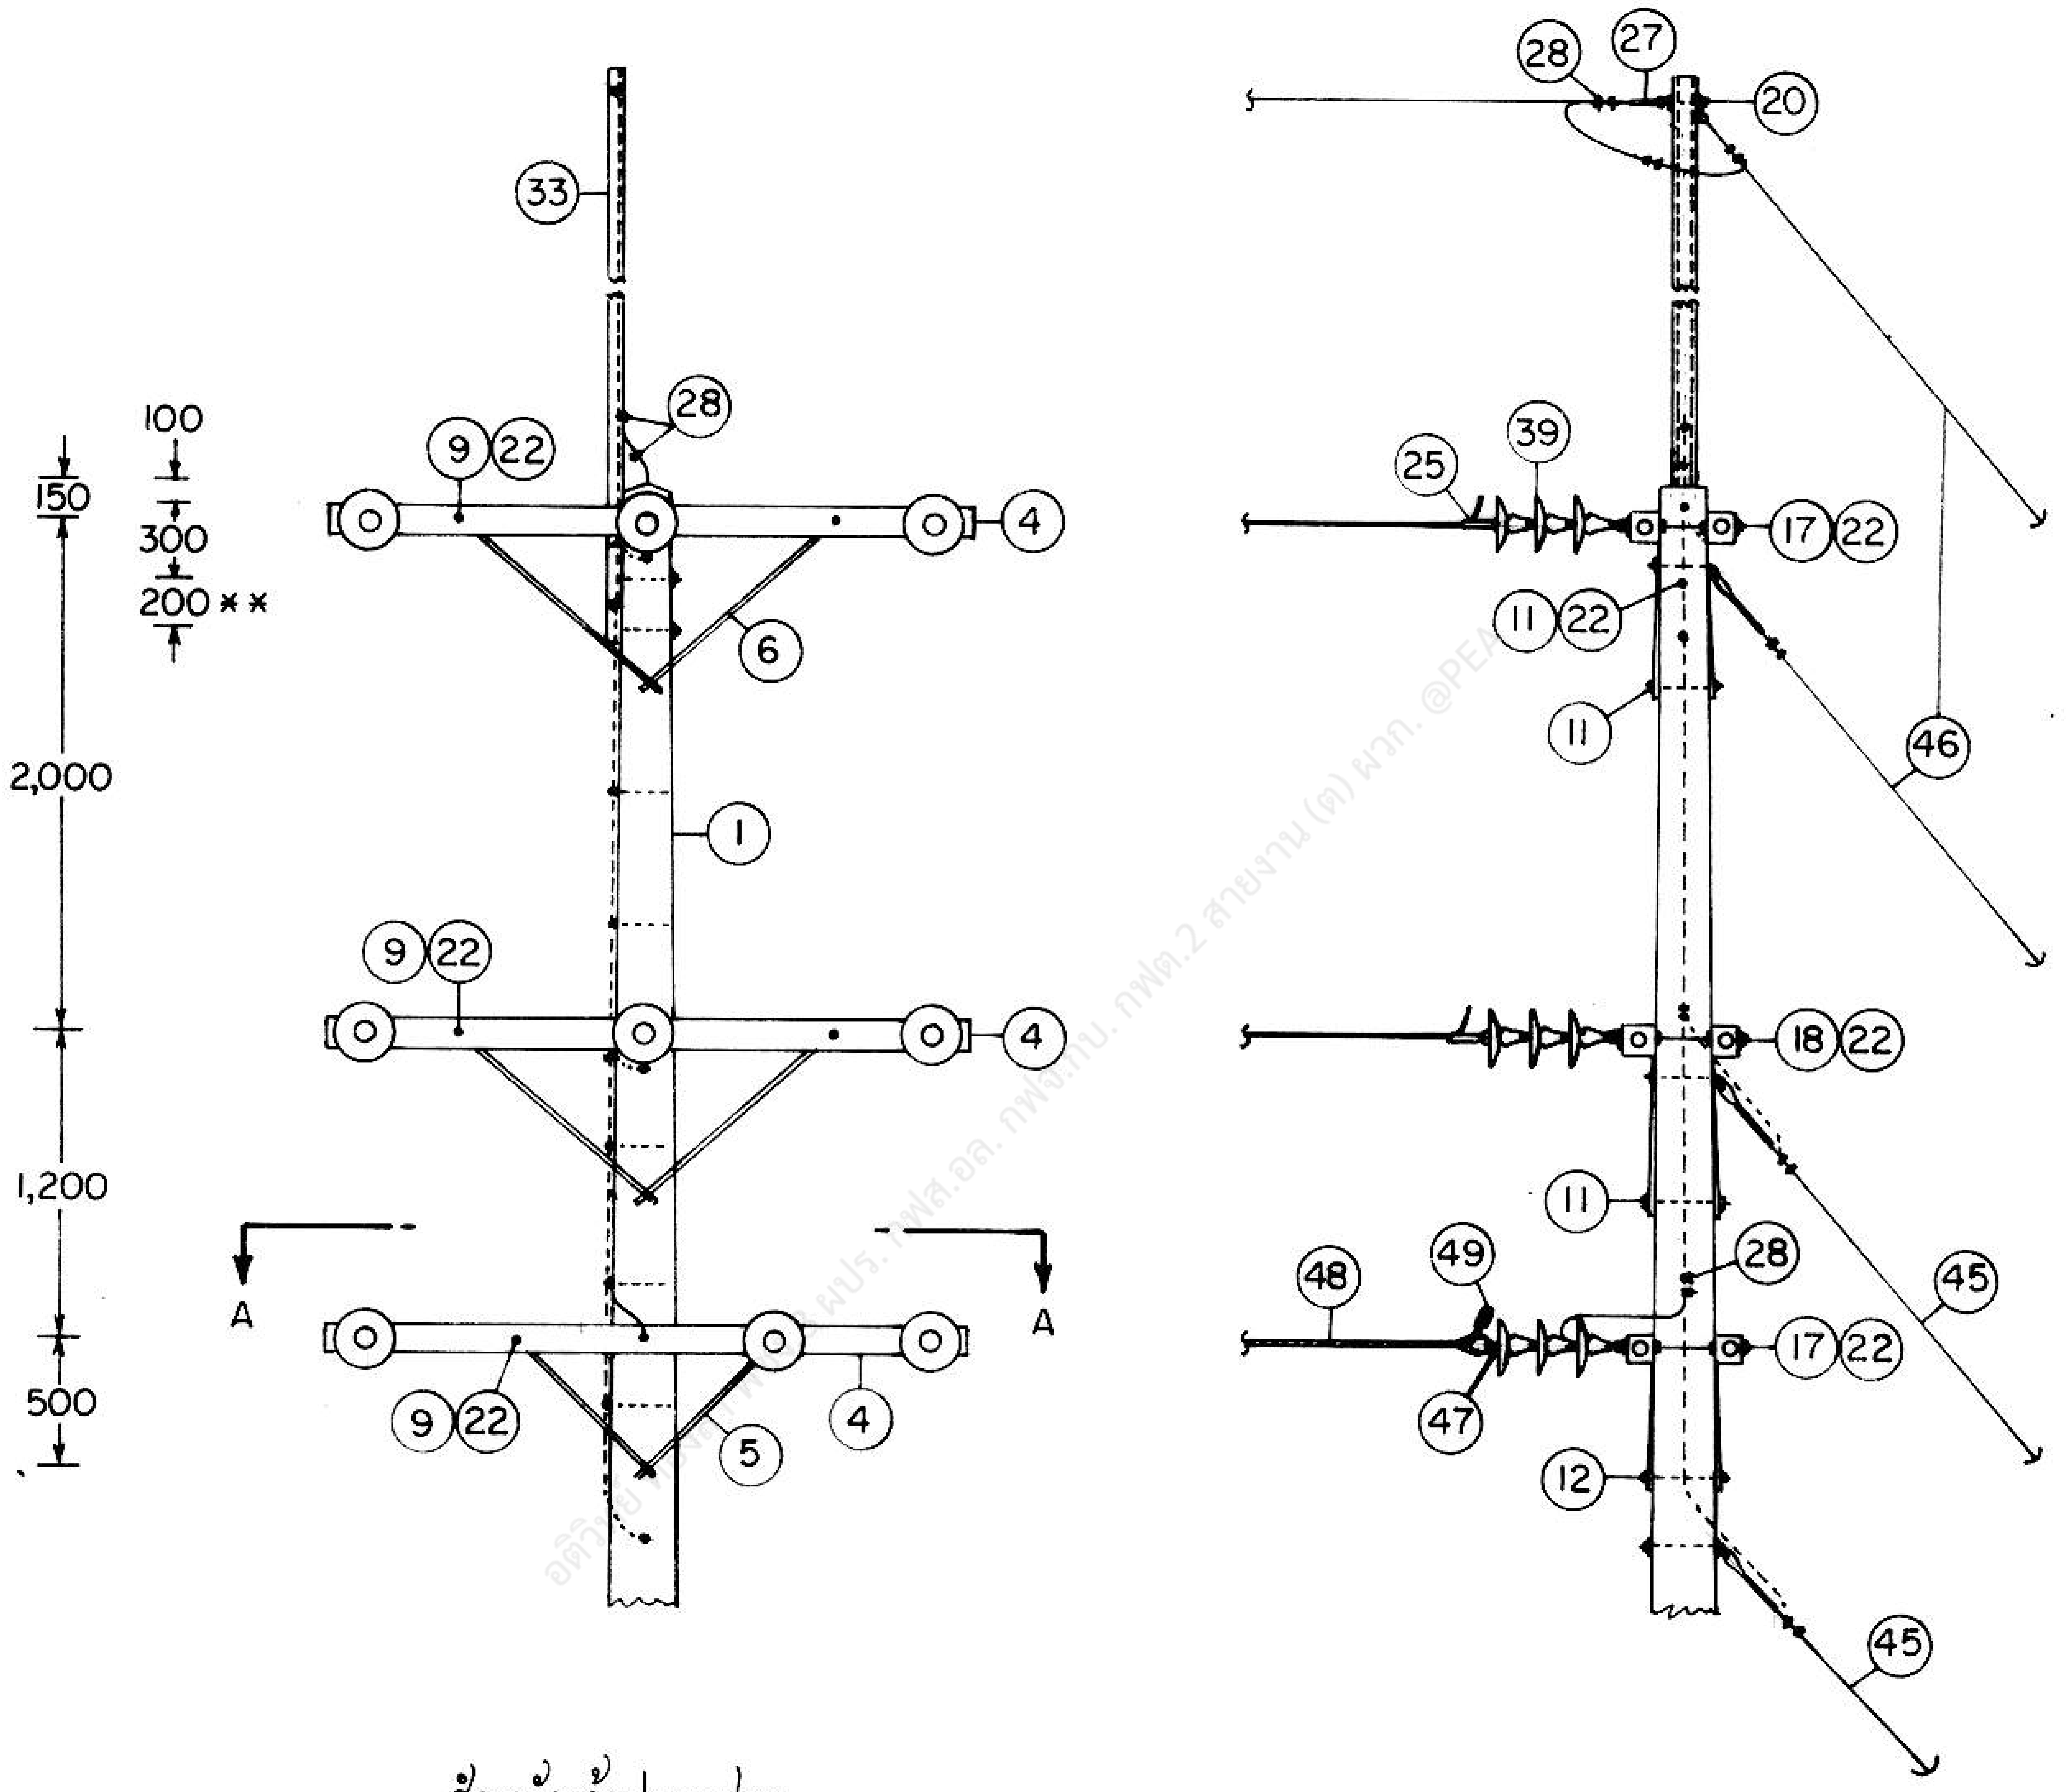

III สำหรับเข้าปลายสาย
(สายเปลือย 2 วงจร และเคเบิลอากาศ 1 วงจร)
FOR DEADENDING
(2-CIRCUIT BARE CONDUCTOR & 1-CIRCUIT AERIAL CABLE)

กองวิศวกรรมไฟฟ้าและเครื่องกล
ฝ่ายวิศวกรรม

ผู้เขียน
ผู้สำรวจ
วิศวกร
หัวหน้าแผนก
ผู้อำนวยการกอง
ผู้อำนวยการฝ่าย

รองผู้ว่าการฝ่ายเทคนิค

การไฟฟ้าส่วนภูมิภาค

ผู้ว่าการ 16 ต.ค. 34

การประกอบคอนกับเสาคอนกรีต 33 kV
3 - 4 วงจร

33 kV CROSSARM ASSEMBLY ON CONCRETE POLE
3 - 4 CIRCUIT

ใช้แทนแบบ
ถูกแทนโดยแบบ
เขียนเสร็จวันที่ 2 ก.ย. 34
แก้แบบวันที่
มิติเป็น มิลลิเมตร
มาตราส่วน 1 : 50
แบบเลขที่ SAI-015/34024
แผ่นที่ 3 ของจำนวน 11 แผ่น

11 ต.ค. 2534

การประกอบเลขที่
ASSEMBLY NO. **3237**

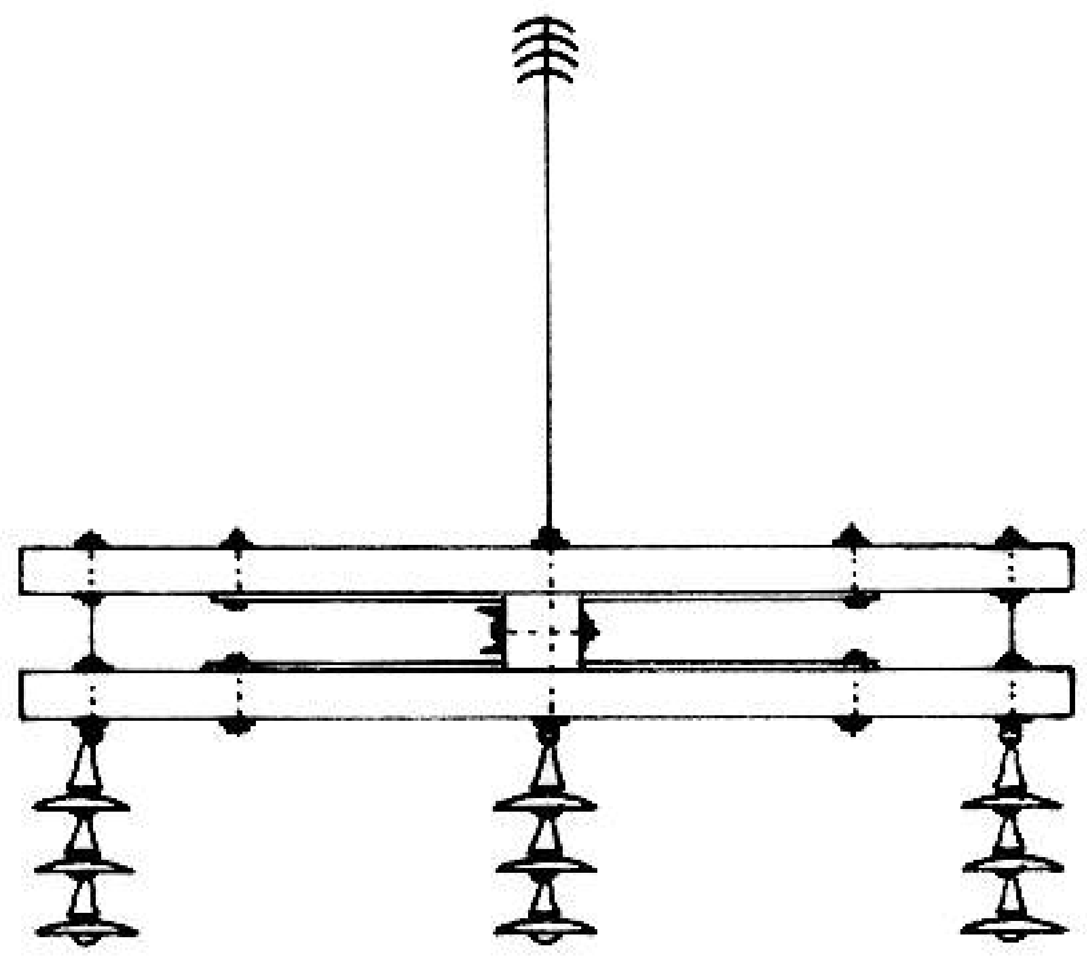

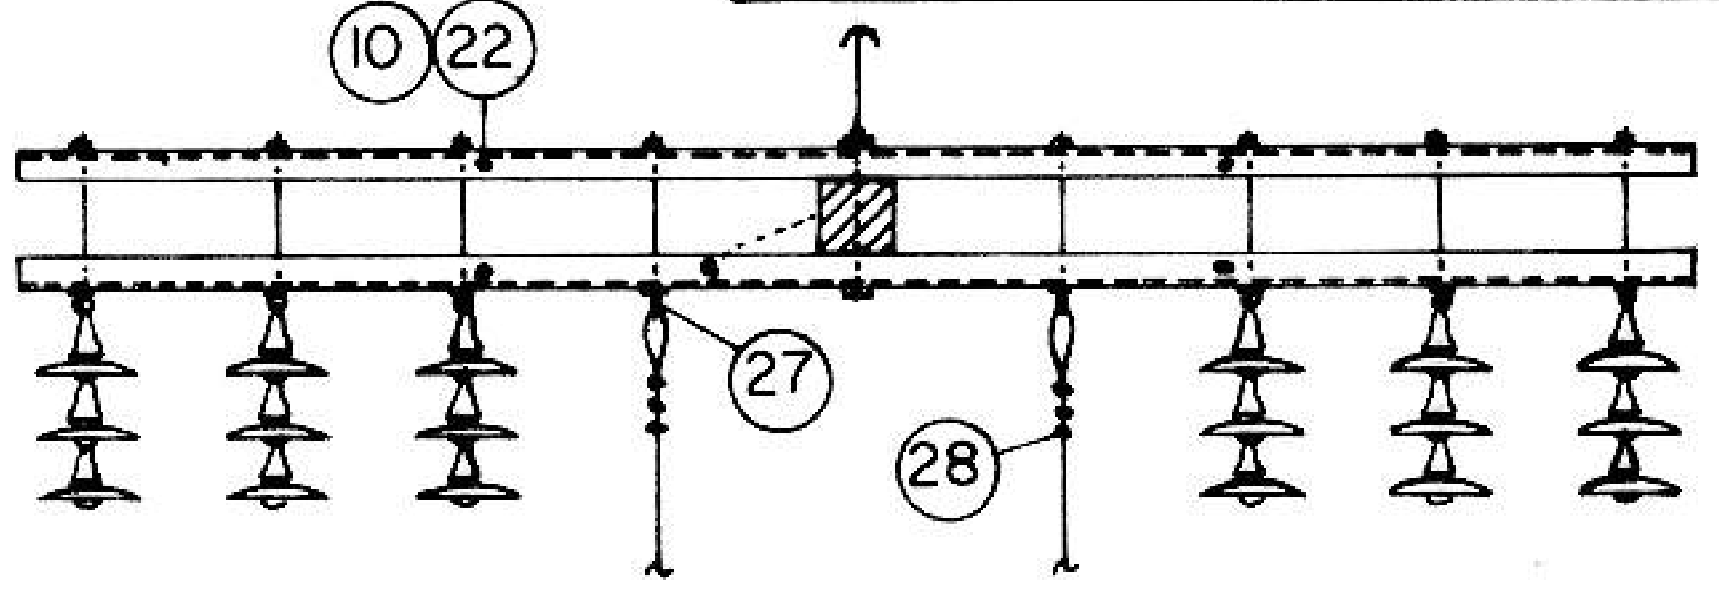

รูปตัด
SECTION A – A

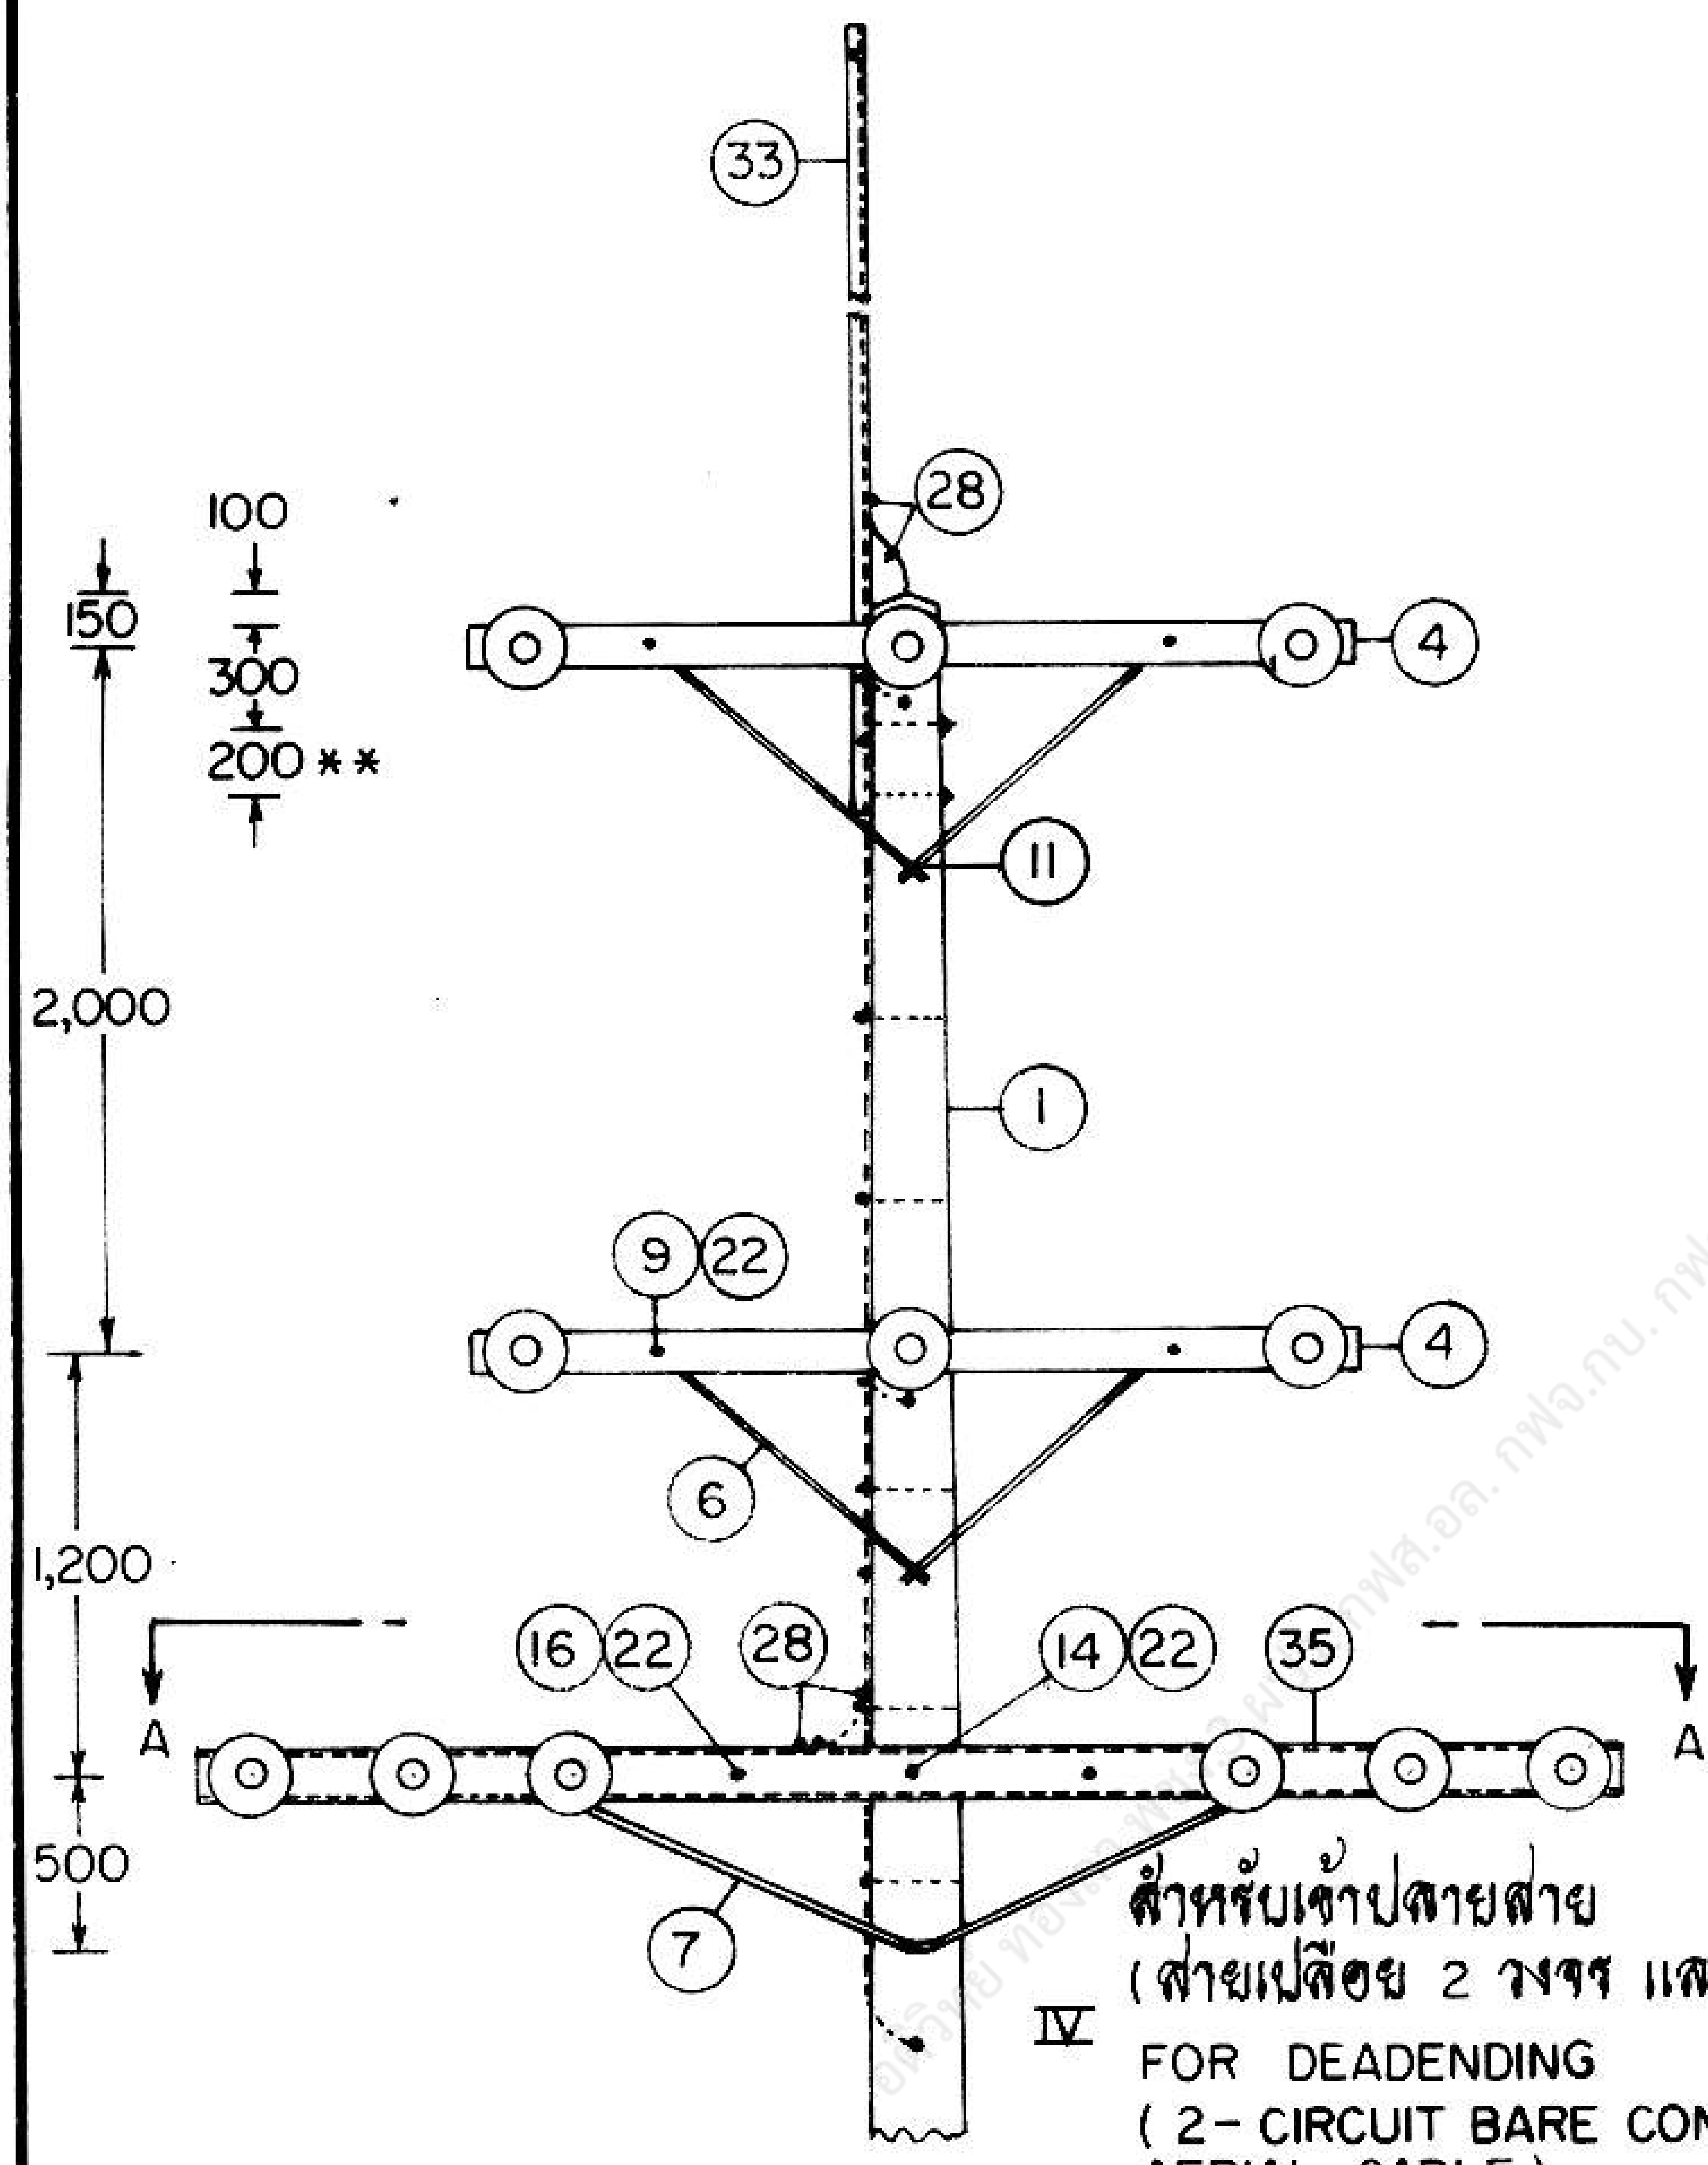

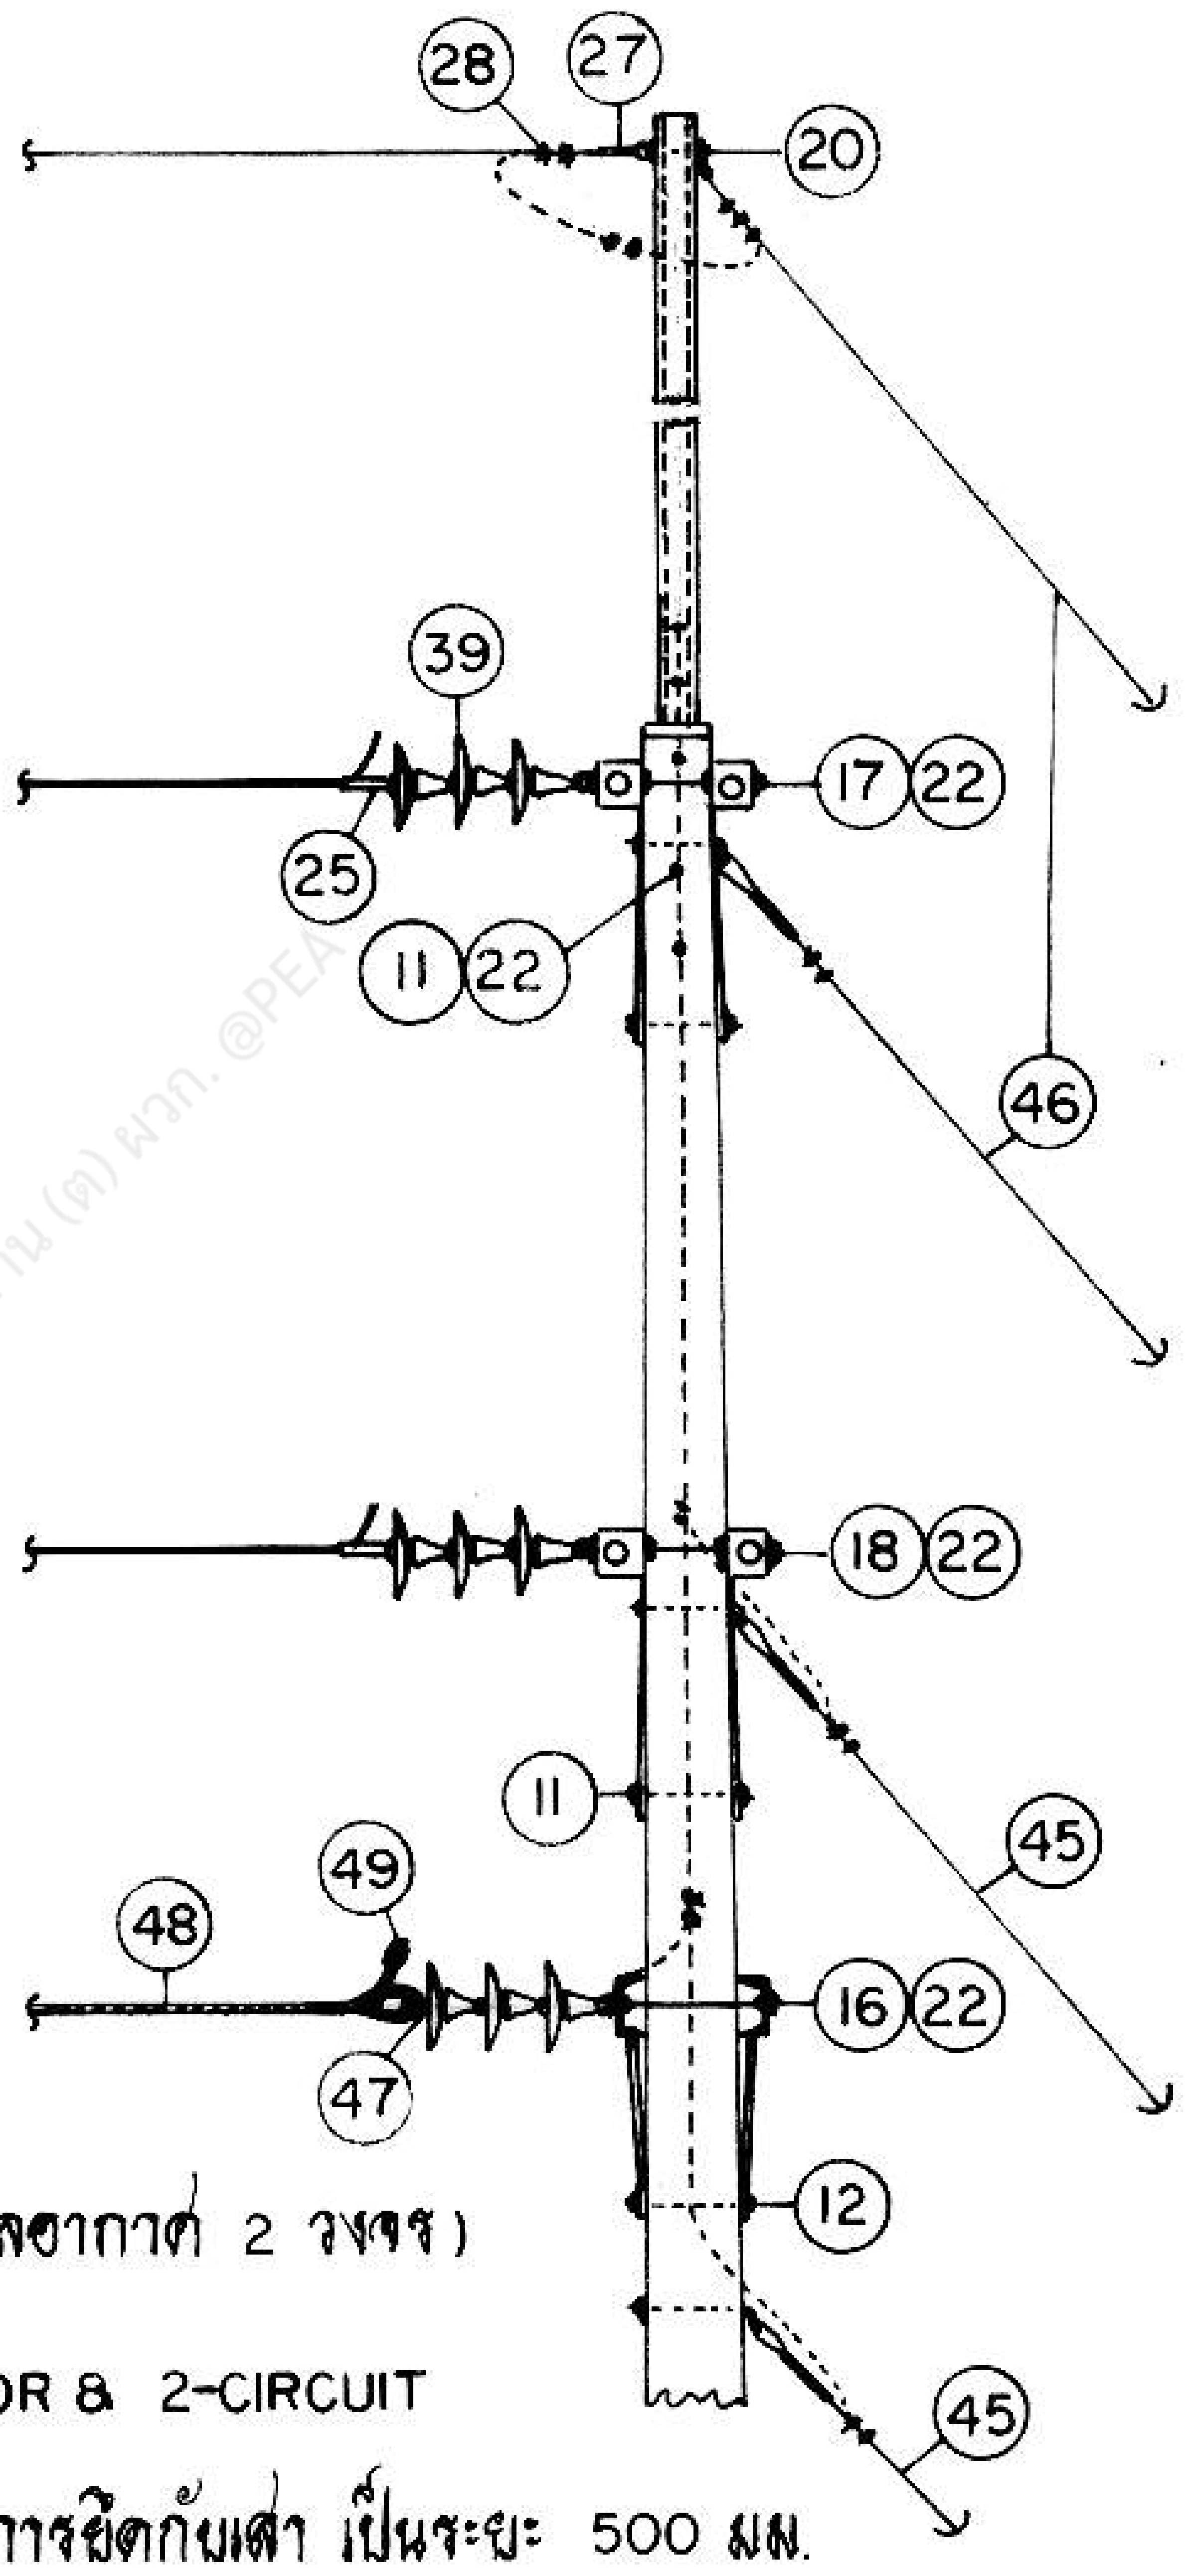

IV สำหรับเข้าปลายสาย
(สายเปลือย 2 วงจร และเคเบิลอากาศ 2 วงจร)
FOR DEADENDING
(2- CIRCUIT BARE CONDUCTOR & 2-CIRCUIT AERIAL CABLE)

* กรณีใช้เหล็กฉากรับสายล่อฟ้า วัสดุเลขที่ 0128 หรือ 0129 ให้ใช้ระยะการยึดกับเสา เป็นระยะ 500 มม.
IN CASE OF USE OVERHEAD GROUND WIRE BAYONET MATERIAL NO. 0128 OR 0129, THE DISTANCE FOR FITTING ON POLE SHALL BE 500 mm .

** กรณีใช้เหล็กรูปรางน้ำรับสายล่อฟ้า วัสดุเลขที่ 6013 ให้เพิ่มสลักเกลียว และแหวนสี่เหลี่ยมแบน รายการที่ 11 และ 22 อีกอย่างละ 1 อัน เพื่อยึดกับเสาที่ระยะ 200 มม. ถัดลงมา
IN CASE OF USE CHANNEL STEEL OVERHEAD GROUND WIRE BAYONET MATERIAL NO. 6013 ADD EACH OF ITEMS 11 AND 22 FOR FITTING AT 200 mm LOWER.

กองวิศวกรรมไฟฟ้าและเครื่องกล ฝ่ายวิศวกรรม	**การไฟฟ้าส่วนภูมิภาค**	ใช้แทนแบบ ถูกแทนโดยแบบ
ผู้เขียน ผู้สำรวจ วิศวกร หัวหน้าแผนก ผู้อำนวยการกอง ผู้อำนวยการฝ่าย	ผู้ว่าการ 16 ต.ค. 34	เขียนเสร็จวันที่ 2 ก.ย. 34 แก้แบบวันที่ มิติเป็น มิลลิเมตร มาตราส่วน 1 : 50
	การประกอบคอนกับเสาคอนกรีต 33 kV 3 – 4 วงจร	
รองผู้ว่าการฝ่ายเทคนิค (แทน)	33 kV CROSSARM ASSEMBLY ON CONCRETE POLE 3 – 4 CIRCUIT	แบบเลขที่ SAI-015/34024 แผ่นที่ 4 ของจำนวน 11 แผ่น

11 ต.ค. 2534

การประกอบเลขที่ ASSEMBLY NO. **3237**

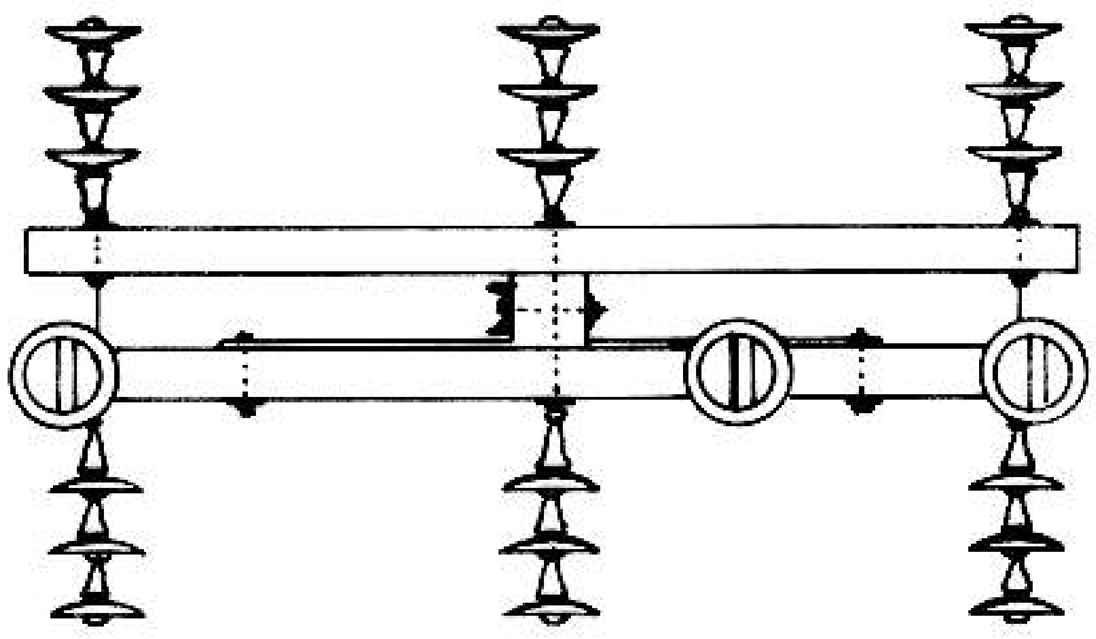

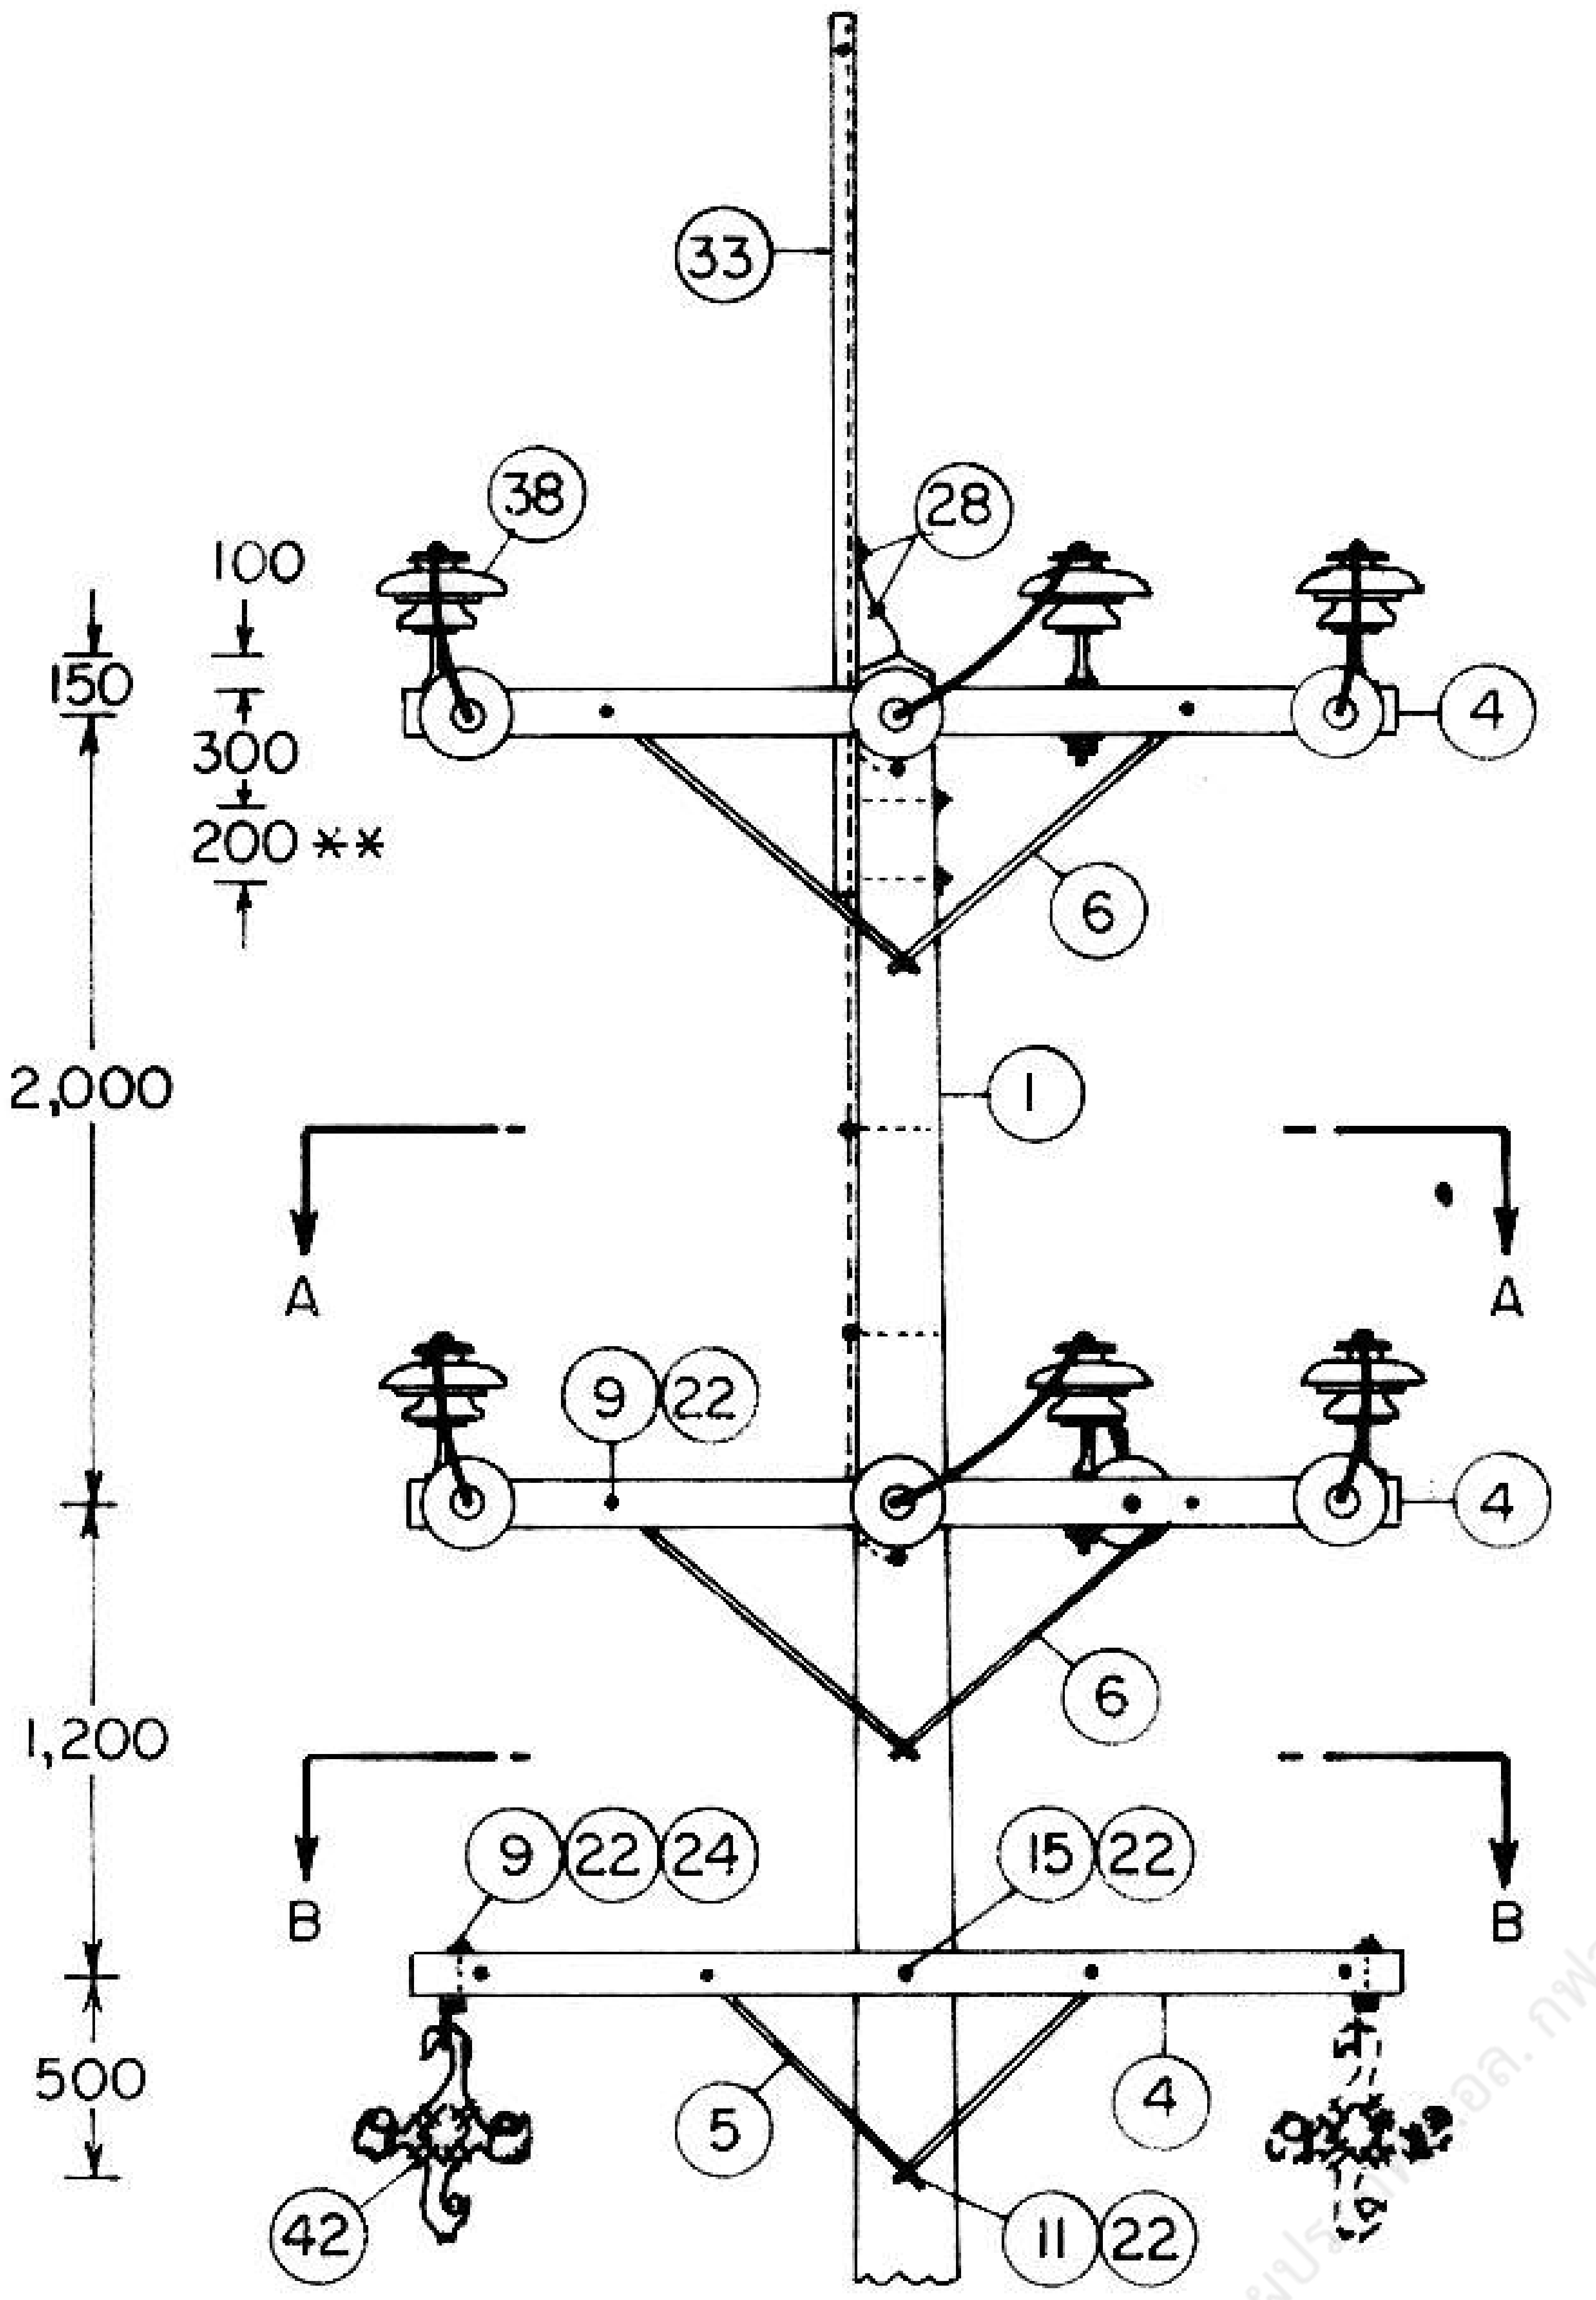

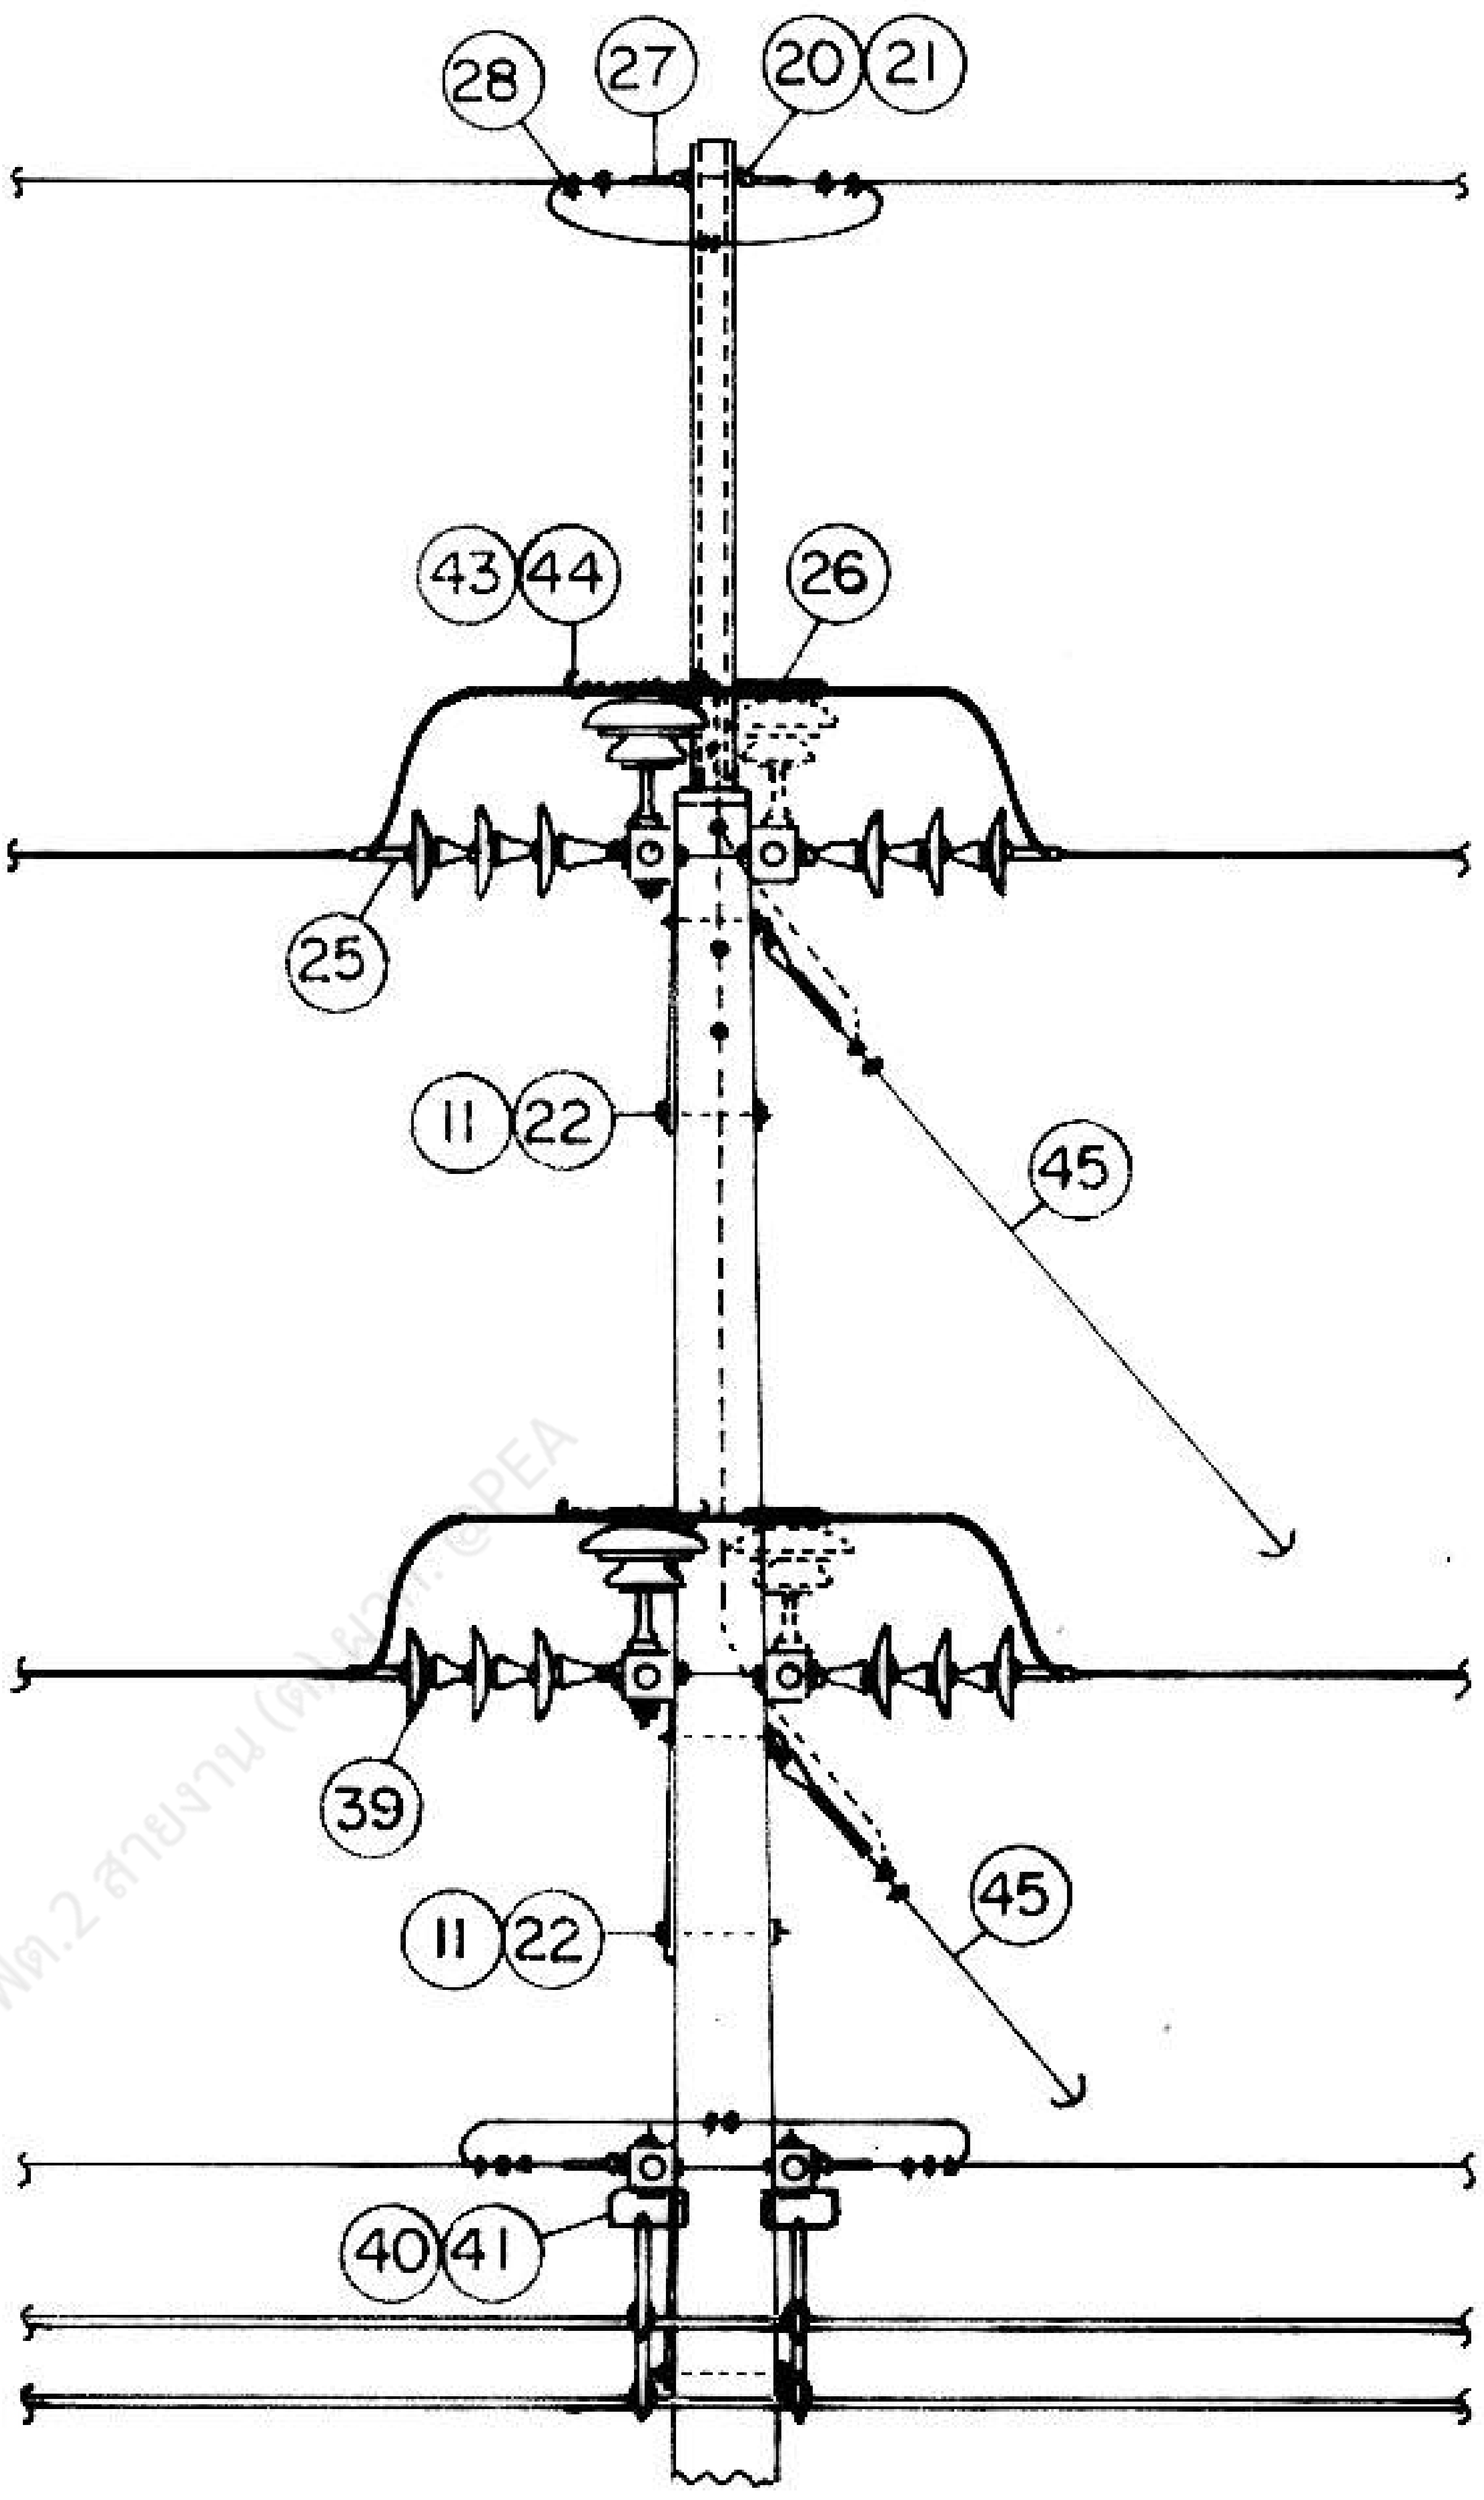

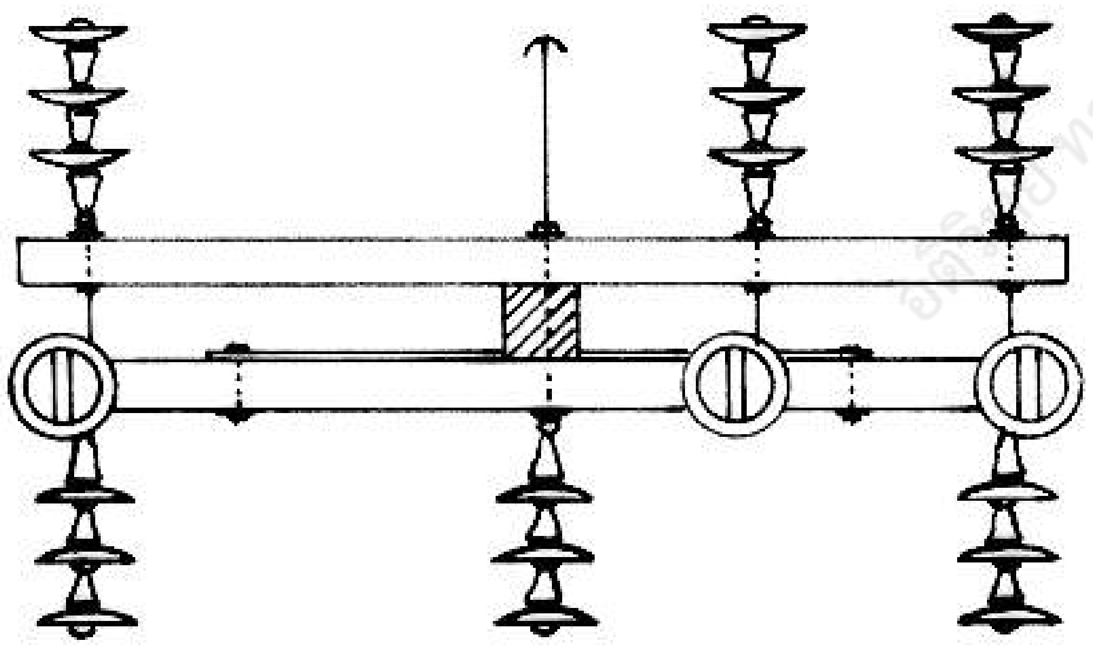

รูปตัด
SECTION **A – A**

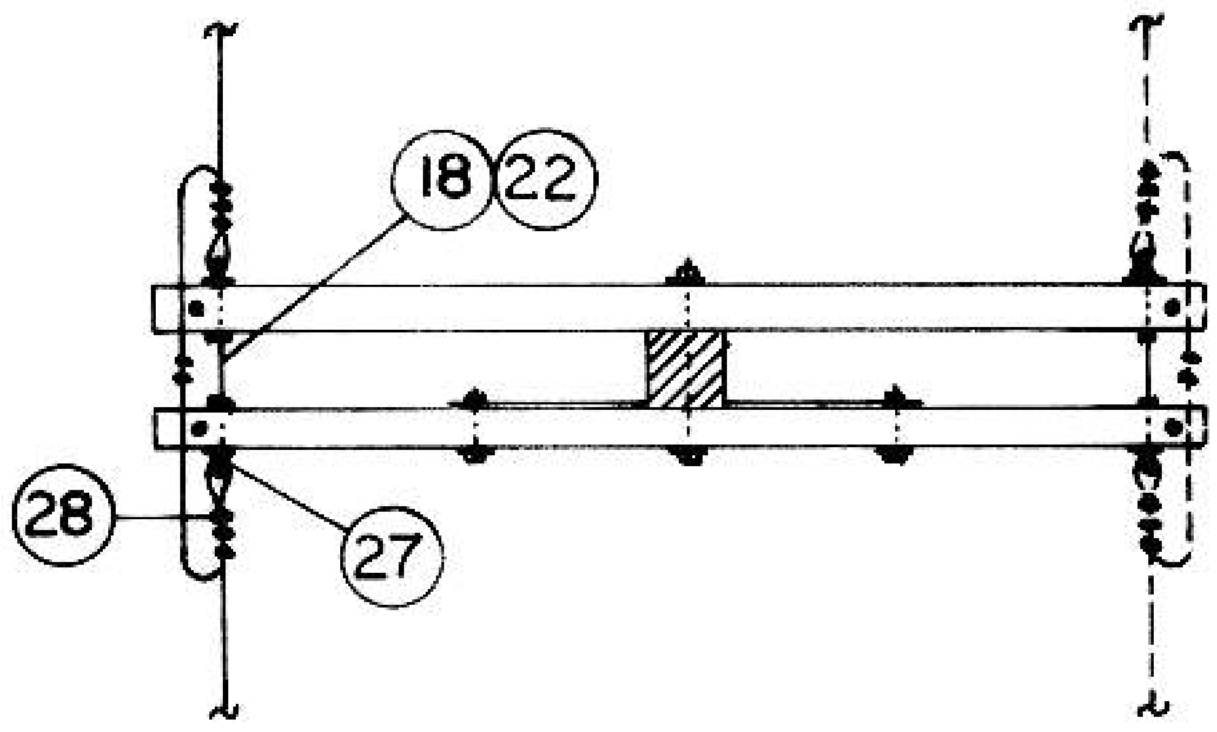

รูปตัด
SECTION **B – B**

V สำหรับเข้าปลายสายสองข้าง (ช่วงทางโค้งลดแรงดึง)
FOR DOUBLE DEADENDING (WITH REDUCED TENSION SPAN LATERAL)

[illegible] ทองลา พชง.3 ผปร. [illegible] กฟจ.กบ. กฟต.2 สายงาน (ดพ.) ผวก. @PEA

กองวิศวกรรมไฟฟ้าและเครื่องกล
ฝ่ายวิศวกรรม

ผู้เขียน
ผู้สำรวจ
วิศวกร
หัวหน้าแผนก
ผู้อำนวยการกอง
ผู้อำนวยการฝ่าย

รองผู้ว่าการฝ่ายเทคนิค

(แทน)

11 ต.ค. 2534

การไฟฟ้าส่วนภูมิภาค

ผู้ว่าการ 16.๙.34

การประกอบคอนกับเสาคอนกรีต 33 kV
3 – 4 วงจร

33 kV CROSSARM ASSEMBLY ON CONCRETE POLE
3 – 4 CIRCUIT

ใช้แทนแบบ
ถูกแทนโดยแบบ
เขียนเสร็จวันที่ 2 ก.ย. 34
แก้แบบวันที่
มิติเป็น มิลลิเมตร
มาตราส่วน 1 : 50

แบบเลขที่ SAI-015/34024
แผ่นที่ 5 ของจำนวน 11 แผ่น

การประกอบเลขที่ ASSEMBLY NO. 3237

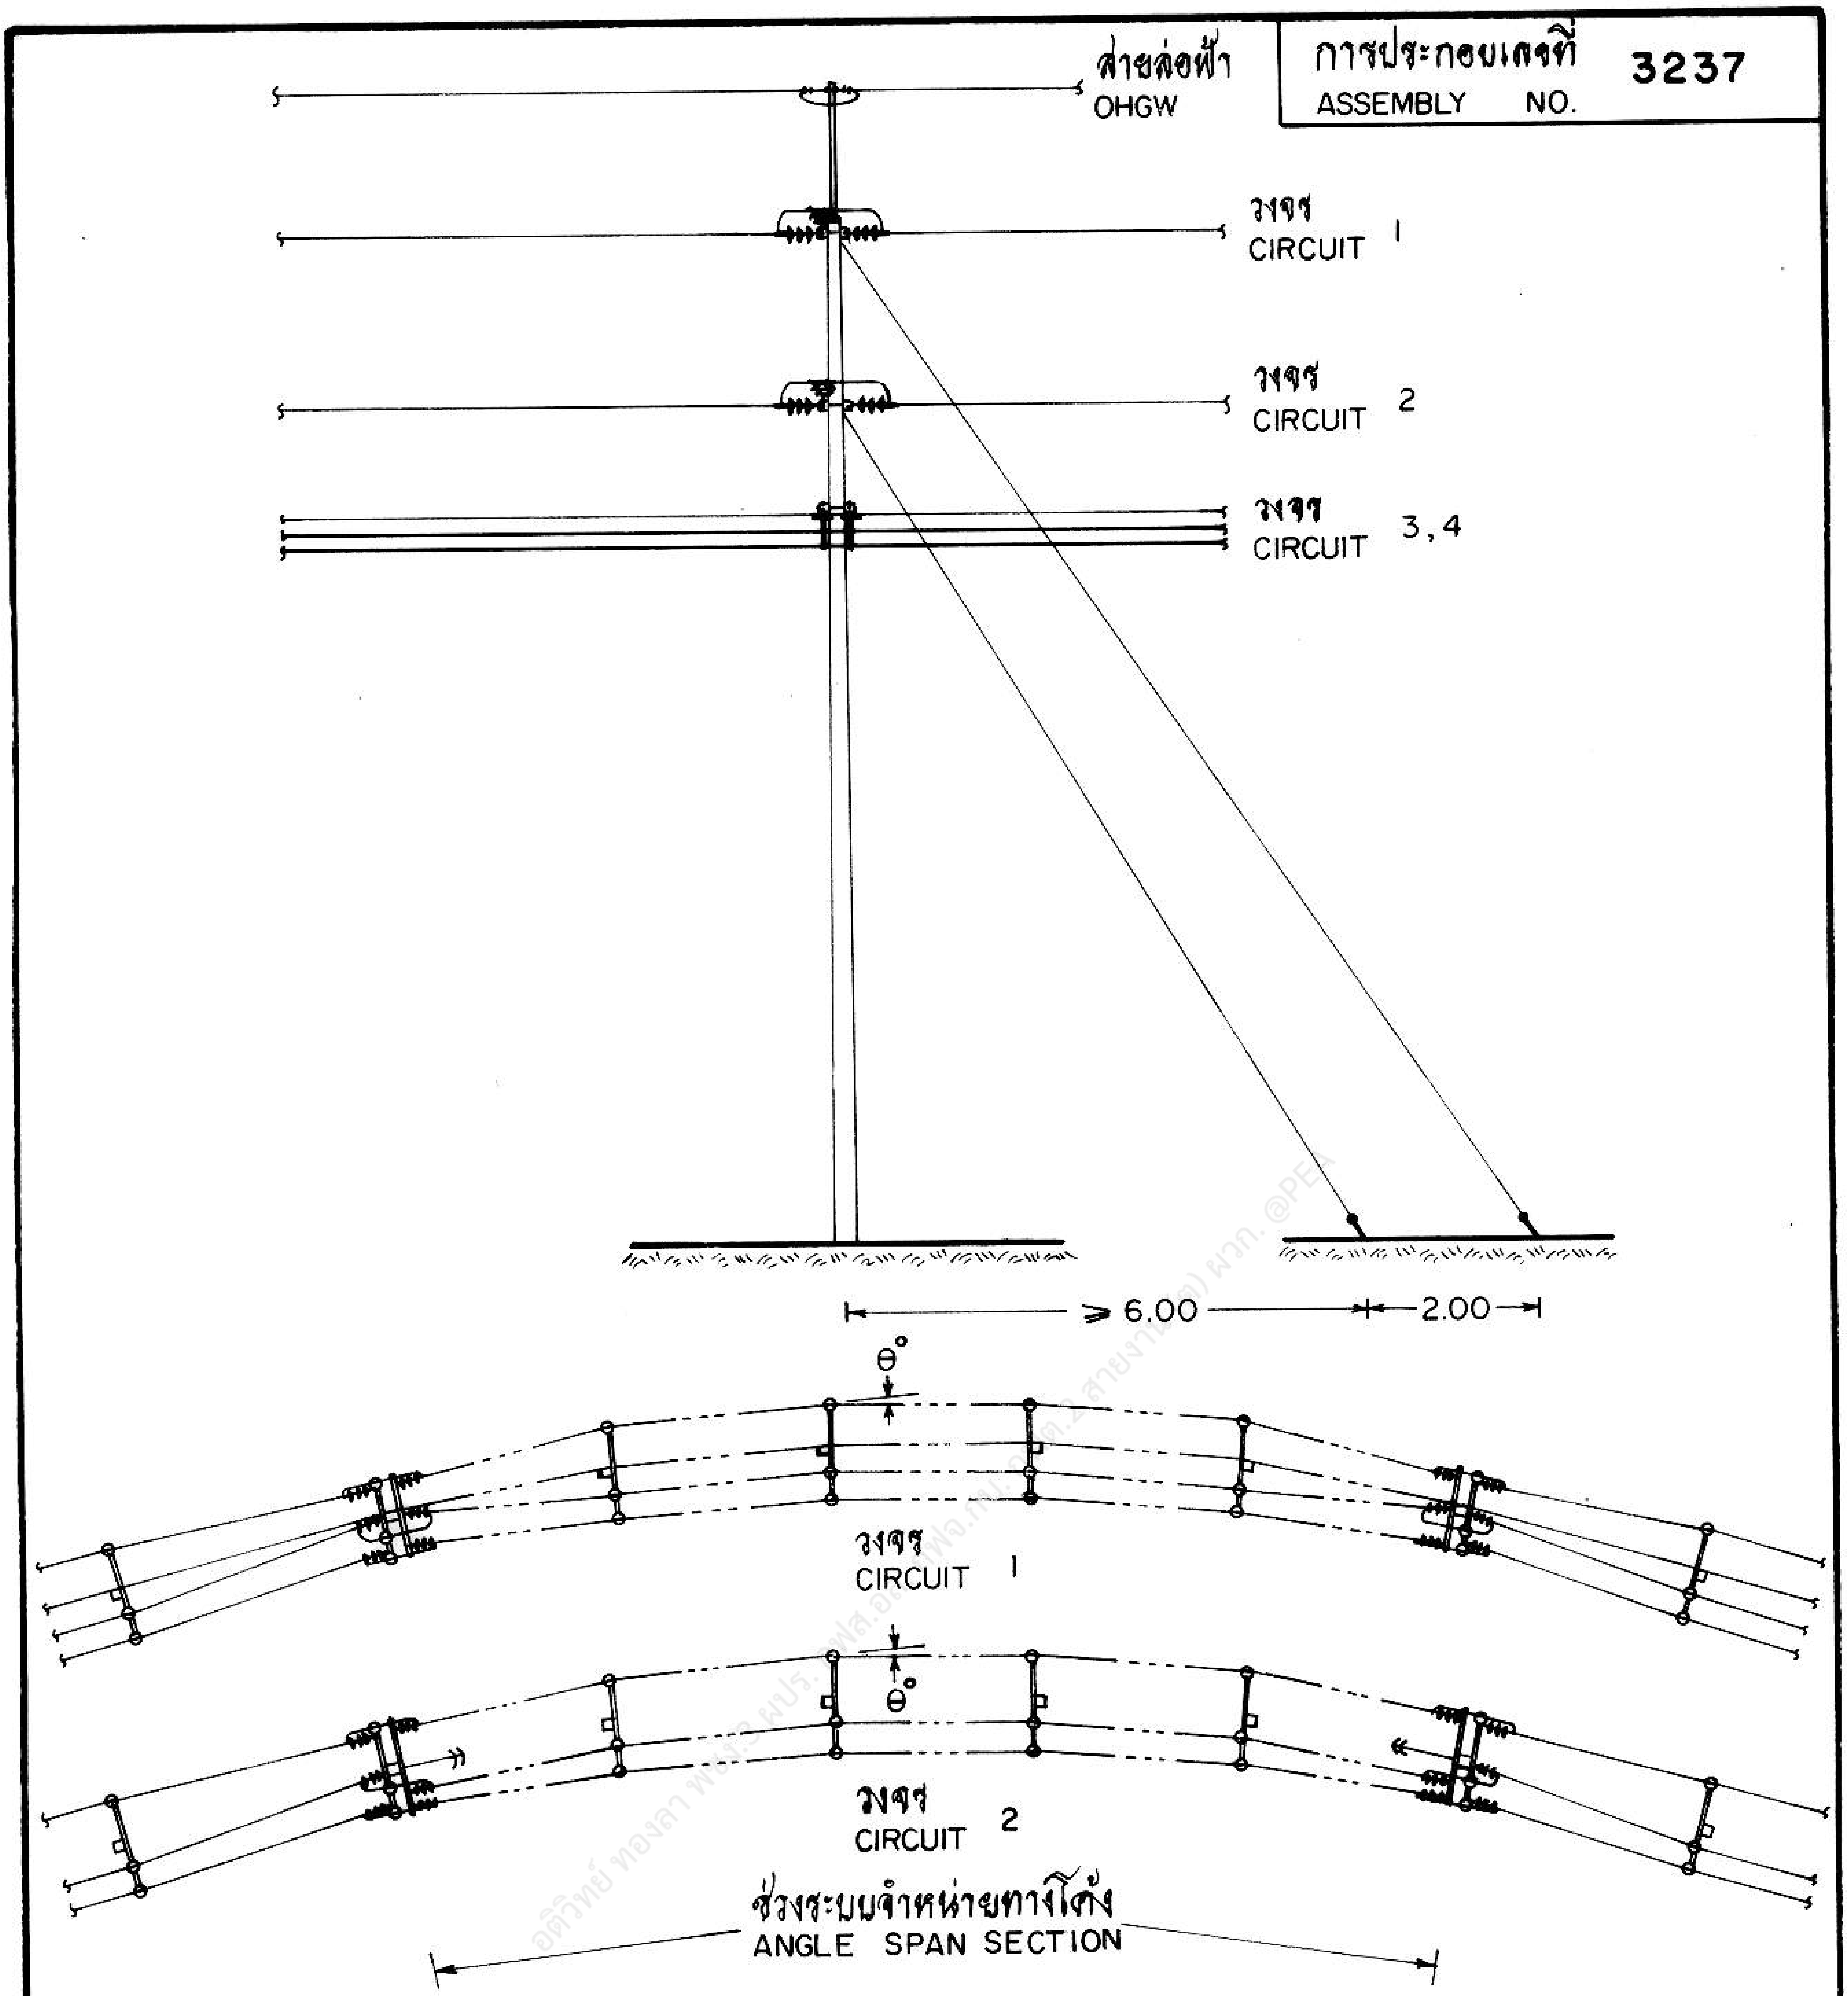

V สำหรับเข้าปลายสายสองข้าง (ช่วงทางโค้งลดแรงดึง) (ต่อ)
FOR DOUBLE DEADEND (WITH REDUCED TENSION SPAN LATERAL) (CONT.)

หมายเหตุ มุมเบี่ยงเบนของสาย (θ°) ช่วงเสาสูงสุด และระยะหย่อนยานต่ำสุดของสาย ดูแบบเลขที่ IBI-015/34071

NOTE LINE DEFLECTION ANGLE (θ°), MAX. SPAN LENGTH AND MIN. SAG OF ALL CONDUCTORS FOR STRUCTURE, SEE DETAIL IN DRAWING NO. IBI-015/34071.

กองวิศวกรรมไฟฟ้าและเครื่องกล
ฝ่ายวิศวกรรม

การไฟฟ้าส่วนภูมิภาค

ผู้เขียน
ผู้สำรวจ
วิศวกร
หัวหน้าแผนก
ผู้อำนวยการกอง
ผู้อำนวยการฝ่าย
รองผู้ว่าการฝ่ายเทคนิค

ผู้ว่าการ 16 ต.ค. 34

การประกอบคอนกับเสาคอนกรีต 33 kV
3 - 4 วงจร

33 kV CROSSARM ASSEMBLY ON CONCRETE POLE
3 - 4 CIRCUIT

ใช้แทนแบบ
ถูกแทนโดยแบบ
เขียนเสร็จวันที่ 2 ก.ย. 34
แก้แบบวันที่
มิติเป็น เมตร
มาตราส่วน 1 : 125
แบบเลขที่ SAI-015/34024
แผ่นที่ 6 ของจำนวน 11 แผ่น

11 ต.ค. 2534

การประกอบเลขที่ 3237
ASSEMBLY NO. 3237

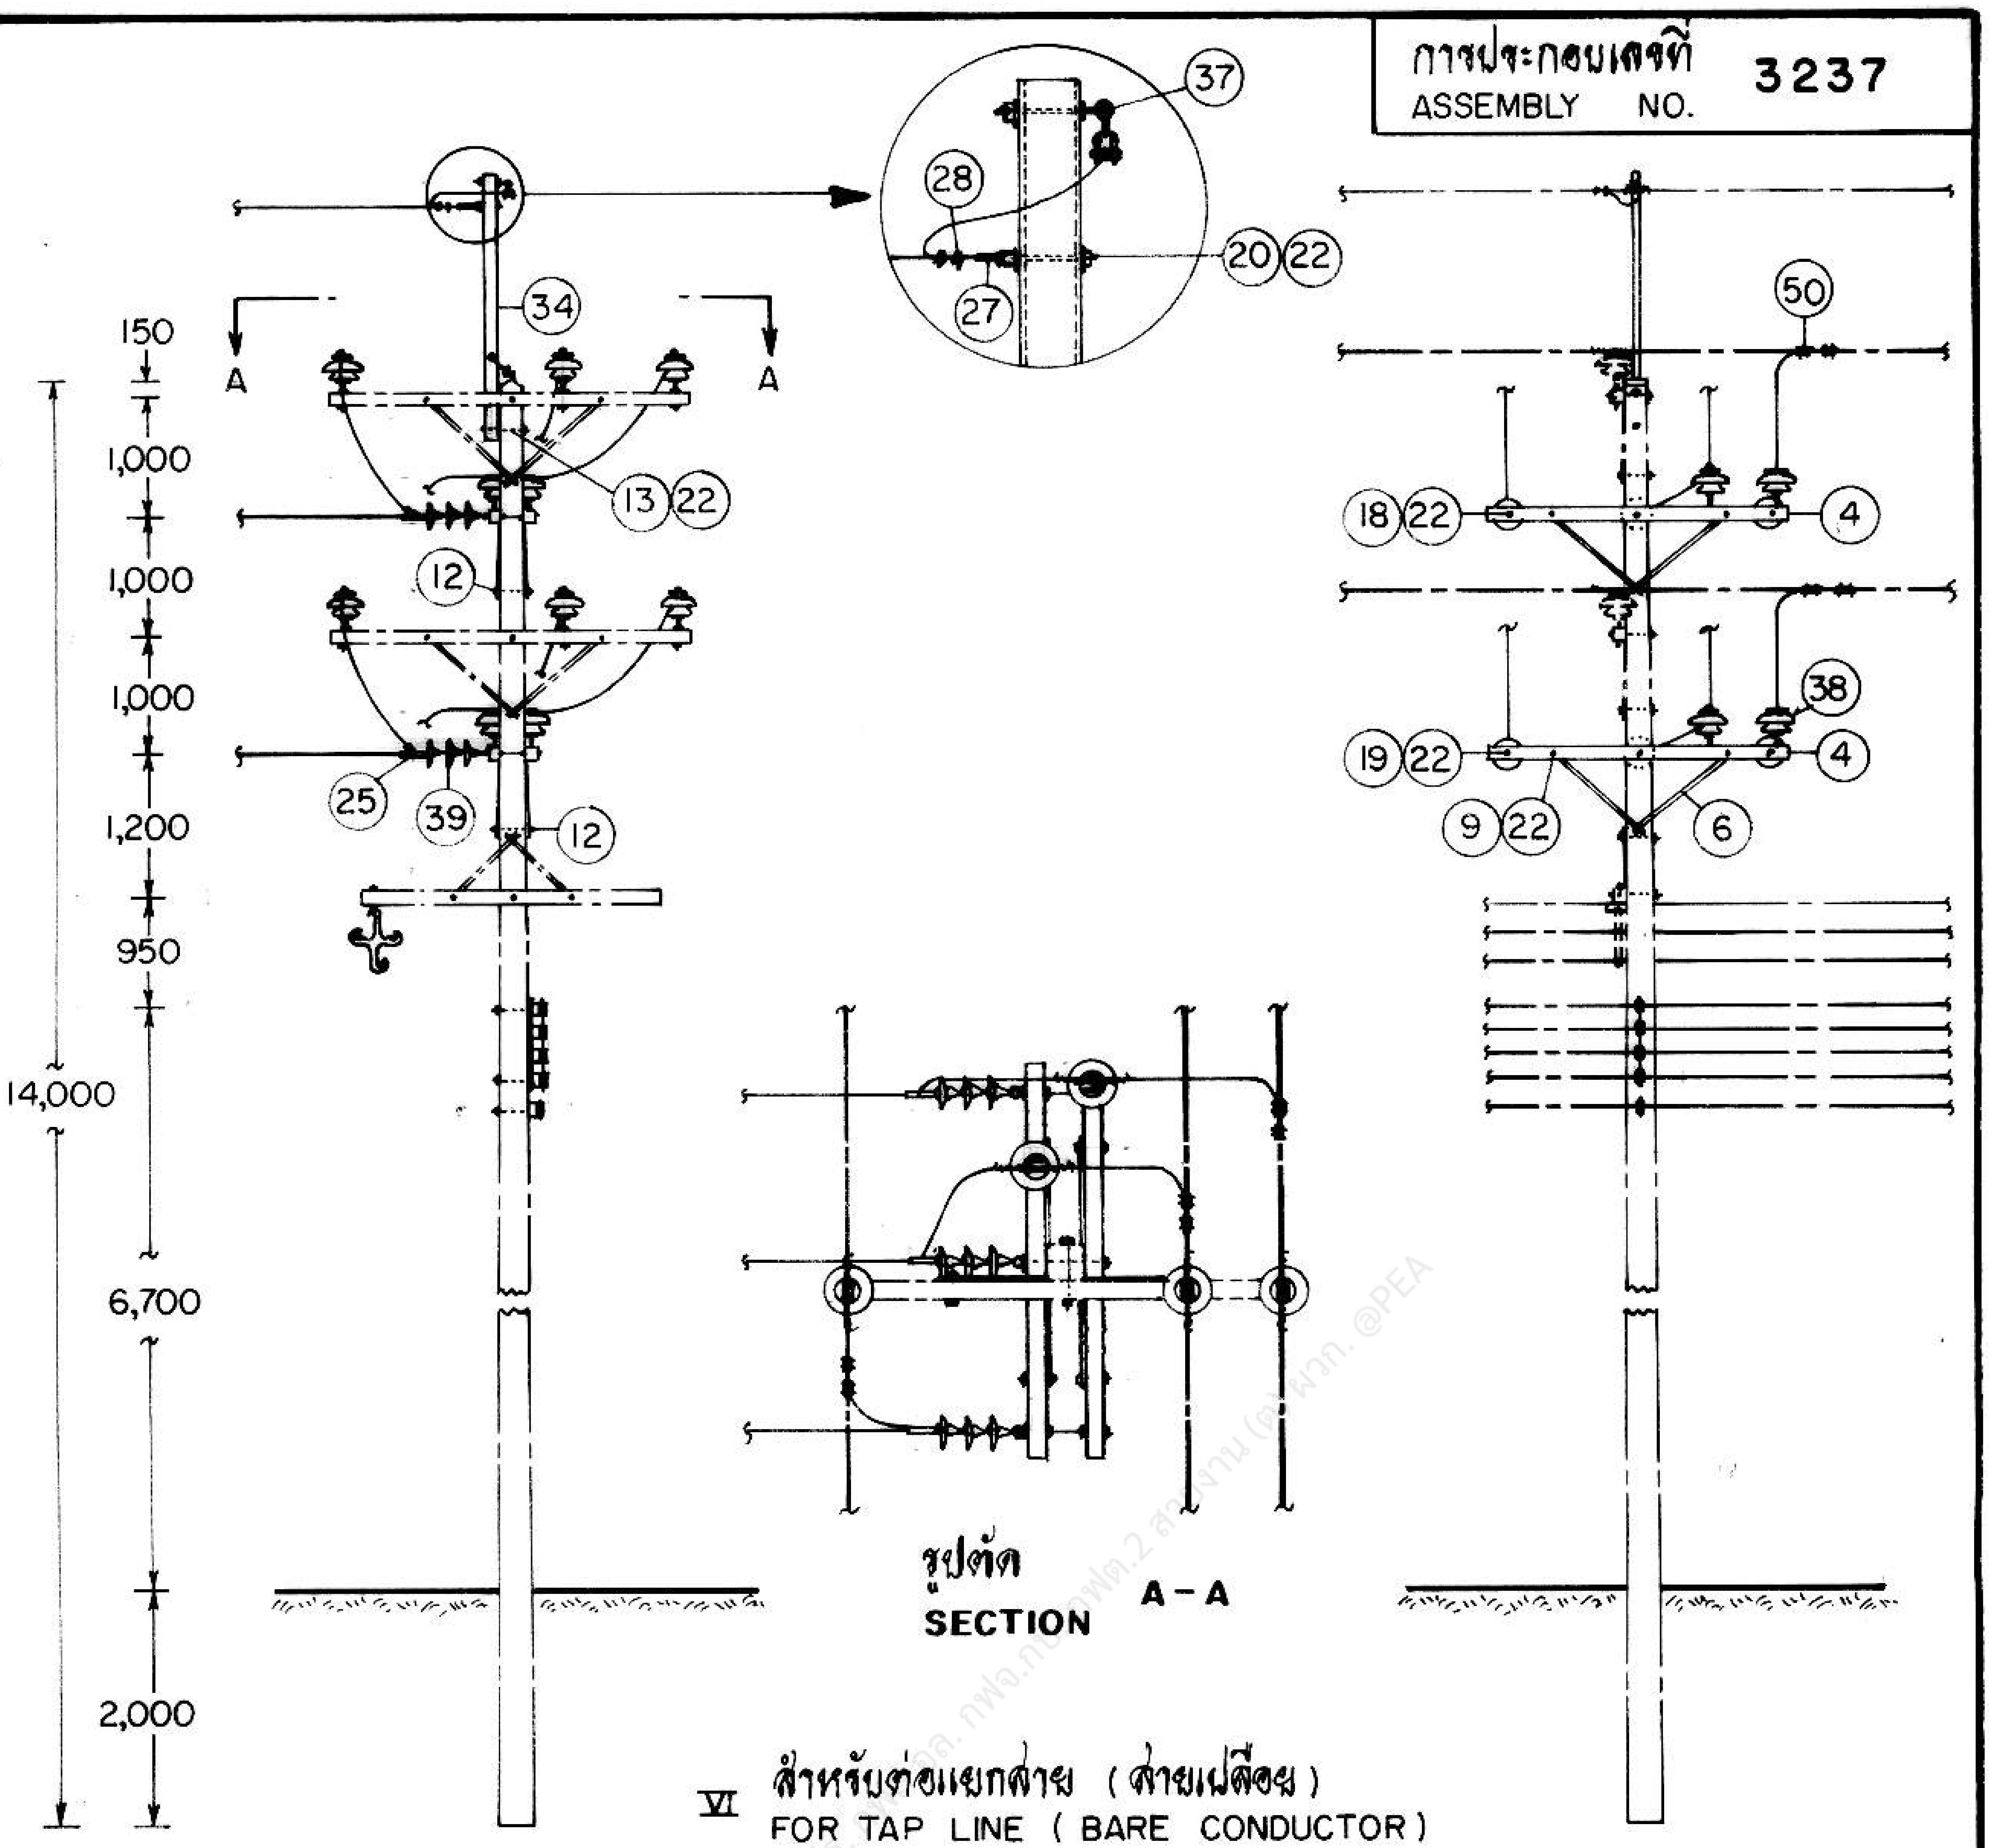

VI สำหรับต่อแยกสาย (สายเปลือย)
FOR TAP LINE (BARE CONDUCTOR)

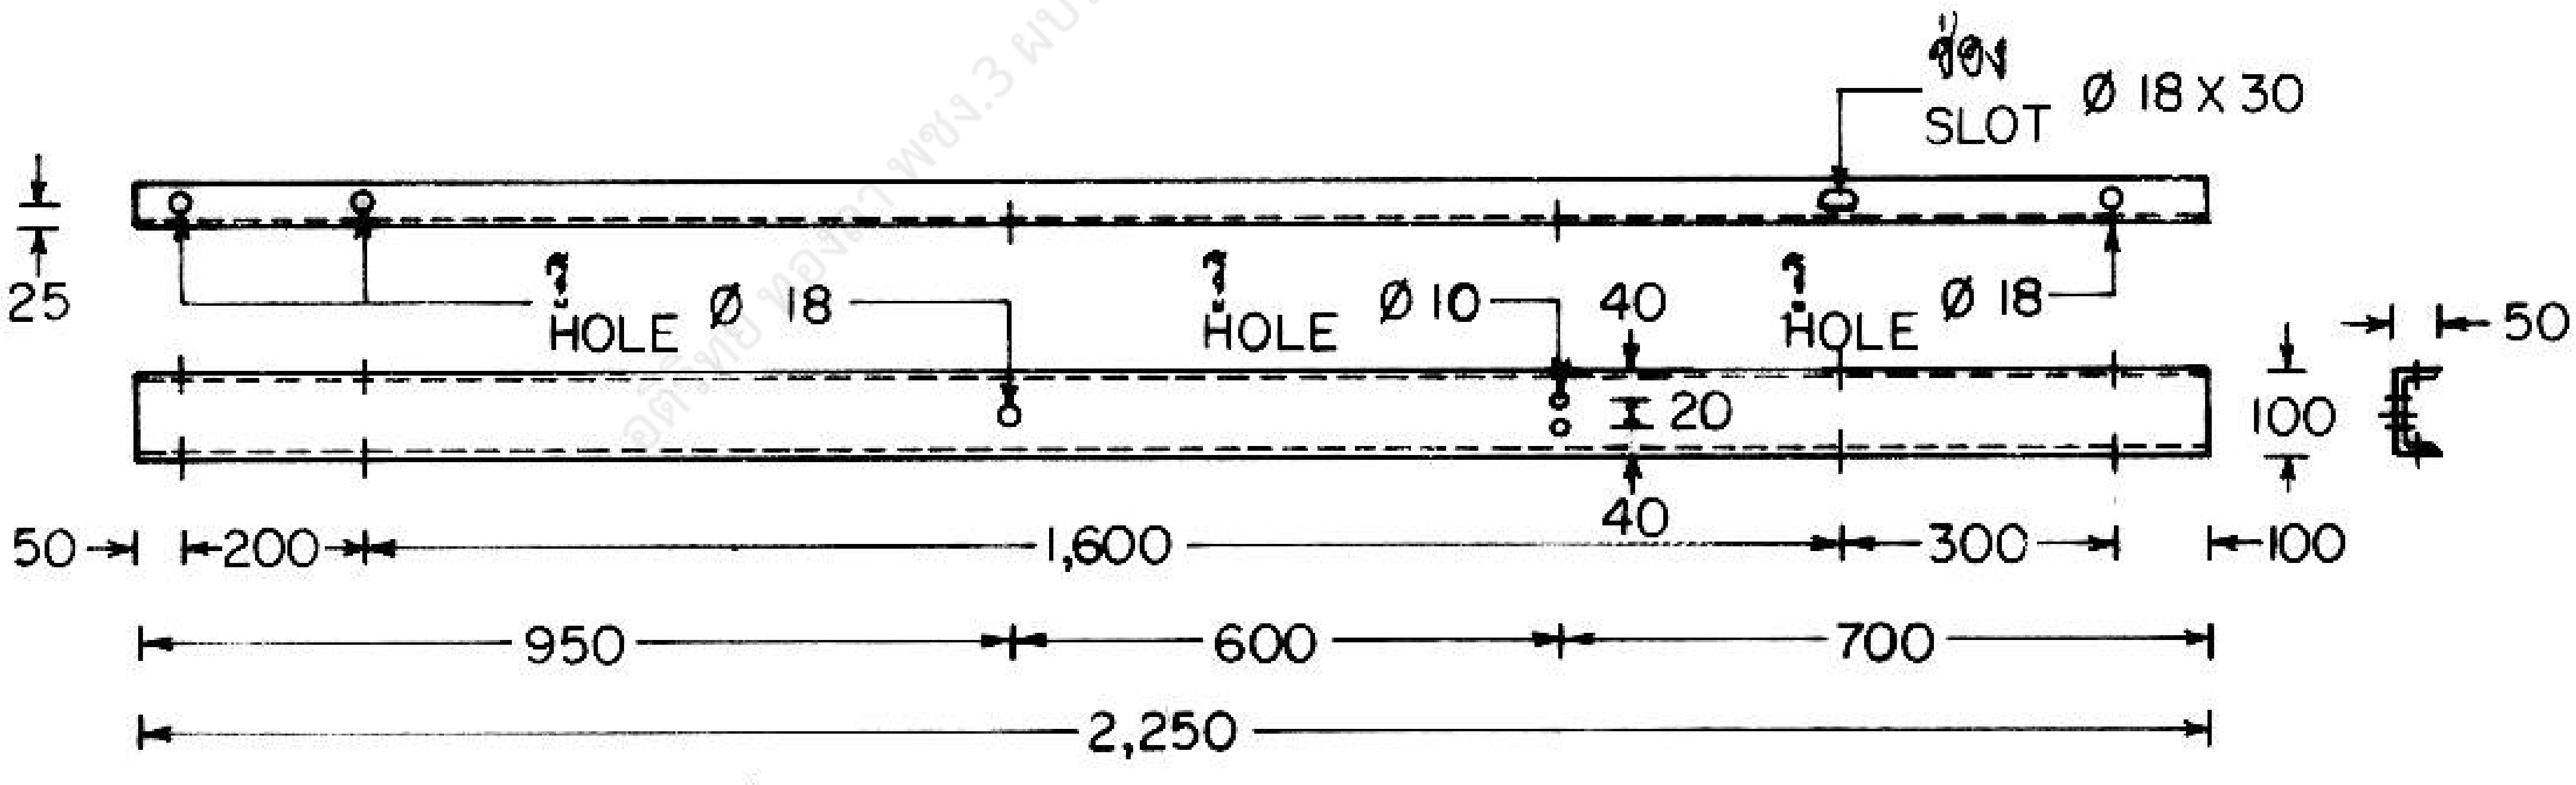

เหล็กรูปรางน้ำ ชนิดรีดร้อน ขนาด 100 X 50 X 5 มม. ยาว 2.25 ม. มอก. 116
(อาจทำจาก เหล็กรูปรางน้ำ วัสดุเลขที่ 6012 ได้)

(34) STEEL, CHANNEL, 100 X 50 X 5 mm, 2.25 m LONG, TIS 116
(MAY BE MADE FROM CHANNEL STEEL MAT. NO. 6012)

กองวิศวกรรมไฟฟ้าและเครื่องกล ฝ่ายวิศวกรรม	การไฟฟ้าส่วนภูมิภาค	ใช้แทนแบบ ถูกแทนโดยแบบ
ผู้เขียน ผู้สำรวจ วิศวกร หัวหน้าแผนก ผู้อำนวยการกอง ผู้อำนวยการฝ่าย	ผู้ว่าการ 16 ต.ค. 34 การประกอบคอนกับเสาคอนกรีต 33 kV 3 - 4 วงจร	เขียนเสร็จวันที่ 2 ก.ย. 34 แก้แบบวันที่ มิติเป็น มิลลิเมตร มาตราส่วน 1 : 100, 1 : 20
รองผู้ว่าการฝ่ายเทคนิค	33 kV CROSSARM ASSEMBLY ON CONCRETE POLE 3 - 4 CIRCUIT	แบบเลขที่ SAI-015/34024 แผ่นที่ 7 ของจำนวน 11 แผ่น

11 ต.ค. 2534

การประกอบเลขที่
ASSEMBLY NO. **3237**

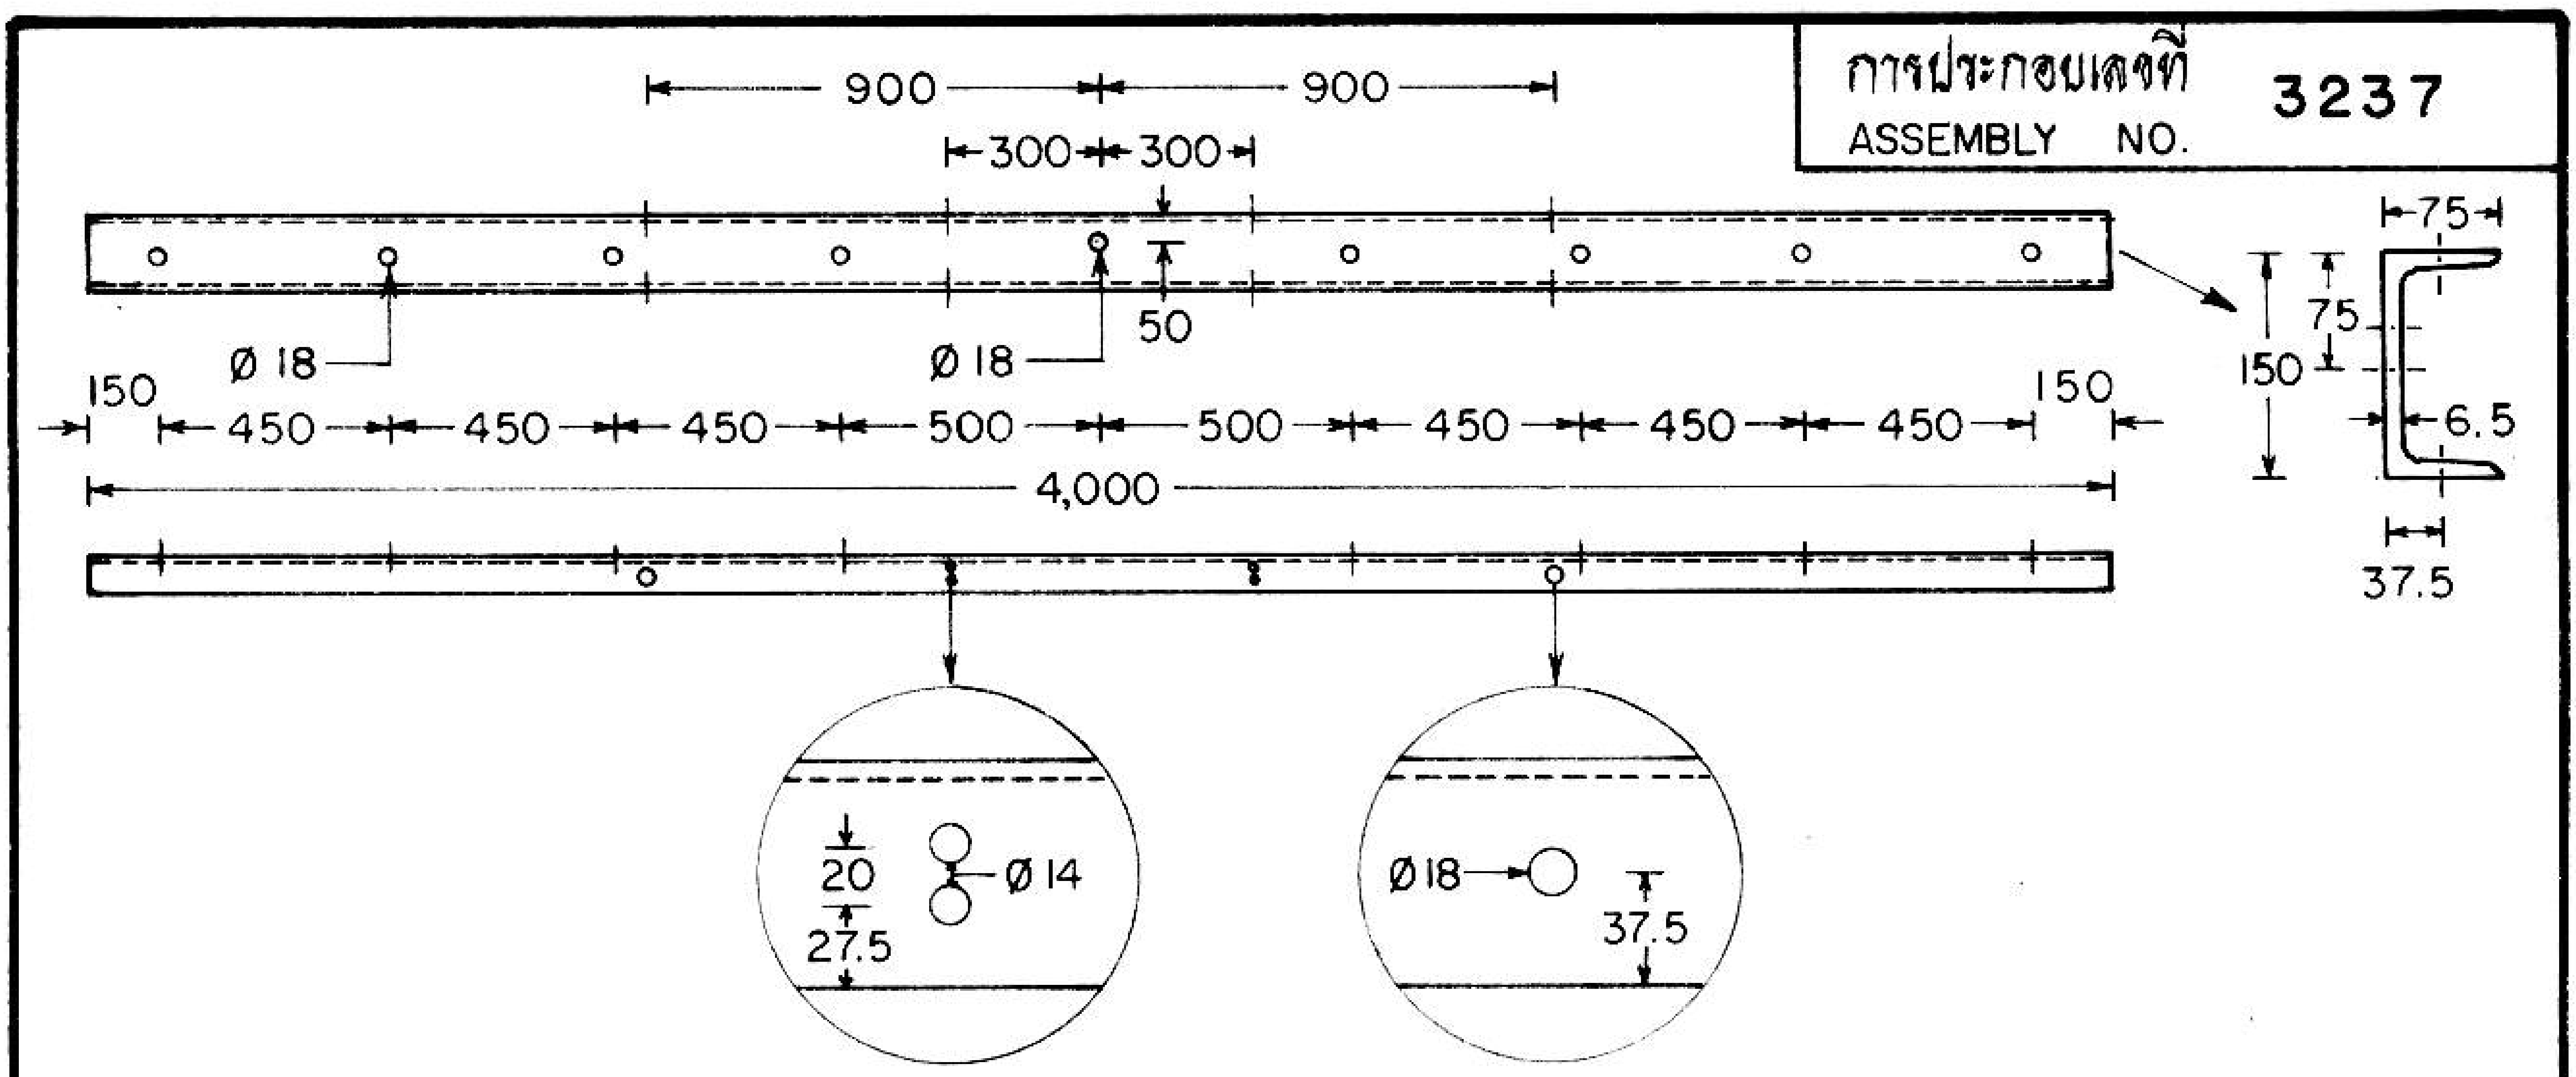

㉟ เหล็กรูปรางน้ำ ชนิดรีดร้อน ขนาด 150 X 75 X 6.5 มม. ยาว 4.00 ม. มอก. 116
STEEL, CHANNEL, 150 X 75 X 6.5 mm, 4.00 m LONG, TIS 116

บัญชีวัสดุ
BILL OF MATERIAL

ลำดับที่ ITEM	รายละเอียด DESCRIPTION	จำนวน REQ'D						วัสดุเลขที่ MAT. NO.
		I	II	III	IV	V	VI	
1	เสาคอนกรีต ขนาด 14 ม. POLE, CONCRETE, 14 m LONG	1	1	1	1	1	–	00010006 (0036)
2	คอน คอร. สปัน ขนาด 100 X 100 X 2,500 มม. CROSSARM, SPUN, PRESTRESSED CONCRETE, 100X100 X 2,500 mm	1	1	–	–	–	–	00110001 (0103)
3	คอน คอร. สปัน ขนาด 120 X 120 X 3,000 มม. CROSSARM, SPUN, PRESTRESSED CONCRETE, 120 X 120 X 3,000 mm	2	2	–	–	–	–	00110002 (0104)
4	คอน คอร. สปัน (สำหรับเข้าปลายสาย) ขนาด 120X120 X 2,500 มม. CROSSARM, SPUN, PRESTRESSED (FOR DEADENDING), 120 X 120 X 2,500 mm	–	–	6	4	6	4	00110004 (0196)
5	เหล็กประกับคอน ขนาด 30 X 6 X 760 มม. BRACE, FLAT, FOR CROSSARM, 30X6X 760 mm	2	2	4	–	2	–	01200001 (0120)
6	เหล็กประกับคอน ขนาด 40 X 6 X 1,000 มม. BRACE, FLAT, FOR CROSSARM, 40 X 6 X 1,000 mm	4	4	8	8	4	8	01200002 (0121)
7	เหล็กฉากรับคอนสาย ขนาด 50 X 50 X 6 มม. ช่วงกว้าง 1,800 มม. ดรอพ 450 มม. BRACE, ANGLE STEEL, 50 X 50 X 6 mm, 1,800 mm WIDE, 450 mm DROP	–	–	–	2	–	–	01200007 (0119)
8	สลักเกลียว M 16 X 130 มม. BOLT, MACHINE, M 16 X 130 mm	2	2	–	–	–	–	01110200 (0220)
9	สลักเกลียว M 16 X 170 มม. BOLT, MACHINE, M 16 X 170 mm	5 (6)	5 (6)	10	8	10	8	01110201 (0221)
10	สลักเกลียว M 16 X 200 มม. BOLT, MACHINE, M 16 X 200 mm	–	–	–	4	–	–	01110202 (0222)
11	สลักเกลียว M 16 X 250 มม. BOLT, MACHINE, M 16 X 250 mm	5	5	4	4	5	–	01110203 (0223)

กองวิศวกรรมไฟฟ้าและเครื่องกล
ฝ่ายวิศวกรรม

การไฟฟ้าส่วนภูมิภาค

ผู้เขียน
ผู้สำรวจ
วิศวกร
หัวหน้าแผนก
ผู้อำนวยการกอง
ผู้อำนวยการฝ่าย

รองผู้ว่าการฝ่ายเทคนิค

ผู้ว่าการ 16 ต.ค. 34

การประกอบคอนกับเสาคอนกรีต 33 kV
3 - 4 วงจร

33 kV CROSSARM ASSEMBLY ON CONCRETE POLE
3 - 4 CIRCUIT

ใช้แทนแบบ
ถูกแทนโดยแบบ
เขียนเสร็จวันที่ 2 ก.ย. 34
แก้แบบวันที่
มิติเป็น มิลลิเมตร
มาตราส่วน 1 : 30
แบบเลขที่ SAI-015/34024
แผ่นที่ 8 ของจำนวน 11 แผ่น

11 ต.ค. 2536

การประกอบเลขที่
ASSEMBLY NO. **3237**

บัญชีวัสดุ
BILL OF MATERIAL

ลำดับที่ ITEM	รายละเอียด DESCRIPTION	จำนวน REQ'D						วัสดุเลขที่ MAT. NO.
		I	II	III	IV	V	VI	
12	สลักเกลียว M 16 X 300 มม. BOLT, MACHINE, M 16 X 300 mm	–	–	–	–	–	2	01110204 (0224)
13	สลักเกลียว M 16 X 350 มม. BOLT, MACHINE, M 16 X 350 mm	3	3	–	–	–	2	01110205 (0225)
14	สลักเกลียว M 16 X 400 มม. BOLT, MACHINE, M 16 X 400 mm	–	–	–	1	–	–	01110206 (0226)
15	สลักเกลียว M 16 X 500 มม. BOLT, MACHINE, M 16 X 500 mm	–	–	–	–	1	–	01110208 (0228)
16	สลักเกลียวห่วงกลม M 16 X 400 มม. BOLT, DOUBLE ARMING, ROUND EYE, M 16 X 400 mm	–	–	–	8	–	–	01130000 (0246)
17	สลักเกลียวห่วงกลม M 16 X 450 มม. BOLT, DOUBLE ARMING, ROUND EYE, M 16 X 450 mm	–	–	3	3	–	–	01130001 (0247)
18	สลักเกลียวห่วงกลม M 16 X 500 มม. BOLT, DOUBLE ARMING, ROUND EYE, M 16 X 500 mm	–	–	7	3	9	3	01130002 (0248)
19	สลักเกลียวห่วงกลม M 16 X 600 มม. BOLT, DOUBLE ARMING, ROUND EYE, M 16 X 600 mm	–	–	–	–	–	3	01130003 (0249)
20	สลักห่วงกลม M 16 X 200 มม. BOLT, ROUND EYE, M 16 X 200 mm	–	–	–	–	–	3	01140001 (0253)
21	นัทรูปห่วง M 16 DIN 582 NUT, EYE, M 16, DIN 582	–	–	–	–	5	–	01180001 (0345)
22	แหวนสี่เหลี่ยมแบน 52 X 52 X 4.5 มม. รู Ø 18 มม. มอก. 258 WASHER, SQUARE, FLAT, 52 X 52 X 4.5 mm, HOLE Ø 18 mm, TIS 258	20 (23)	18 (21)	44	68	49 (53)	30	01180100 (0355)
23	แหวนสี่เหลี่ยมโค้ง 60 X 60 X 5 มม. รู Ø 22 มม. WASHER, SQUARE, CURVED, 60 X 60 X 5 mm, HOLE Ø 22 mm	6	6	–	–	–	–	01180201 (0361)
24	แหวนรองแบบสปริง ขนาดระบุ 16 มม. มอก. 259 WASHER, LOCK, SPRING, SIZE 16 mm, TIS 259	4 (5)	4 (5)	–	–	–	–	01180301 (0365)
25	สเตรนแคล้มป์ สำหรับสายอะลูมิเนียม ขนาดตามต้องการ CLAMP, STRAIN, FOR Al CONDUCTOR; SIZE AS REQUIRED	–	–	6	6	12	6	03110000 03110101
26	หลอดต่อสายชนิดบีบไม่รับแรงดึง สายอะลูมิเนียมขนาดตามต้องการ CONNECTOR, SPLICE, COMPRESSION TYPE, TENSIONLESS, Al ; SIZE AS REQUIRED	–	–	–	–	6	–	02410001-5 02410007
27	กายทิมเบิล สำหรับสายยึดโยง 50-95 ต.มม. THIMBLE, GUY, FOR STEEL WIRE 50-95 mm^2	–	–	2	3	4 (6)	1	01210304 (0150)
28	ยูแคล้มป์ สลัก 1 ตัว M 8 CLAMP, SINGLE U-BOLT, M 8	5 (7)	5 (7)	9	13	16 (24)	6	01230000 (0165)
29	ลวดเหล็กตีเกลียว 25 ต.มม. มอก. 404 WIRE, STEEL STRANDED, 25 mm^2, TIS 404	5 ม. m (7)	5 ม. m (7)	–	–	–	–	01100002 (0181)
30	ลวดเหล็กกลม เส้นผ่านศูนย์กลาง 4 มม. มอก. 71 (นน.ประมาณ 0.1 กก./ม.) WIRE, STEEL, SOLID, DIA 4 mm, TIS 71 (WEIGHT 0.1 kg/m)	8 ม. m	8 ม. m	–	–	–	–	01100000 (0191)

กองวิศวกรรมไฟฟ้าและเครื่องกล
ฝ่ายวิศวกรรม

ผู้เขียน
ผู้สำรวจ
วิศวกร
หัวหน้าแผนก
ผู้อำนวยการกอง
ผู้อำนวยการฝ่าย

รองผู้ว่าการฝ่ายเทคนิค

การไฟฟ้าส่วนภูมิภาค

ผู้ว่าการ 16 ต.ค. 34

การประกอบคอนกับเสาคอนกรีต 33 kV
3 - 4 วงจร

33 kV CROSSARM ASSEMBLY ON CONCRETE POLE
3 - 4 CIRCUIT

ใช้แทนแบบ
ถูกแทนโดยแบบ
เขียนเสร็จวันที่ 2 ก.ย. 34
แก้แบบวันที่
มิติเป็น
มาตราส่วน

แบบเลขที่ SAI-015/34024
แผ่นที่ 9 ของจำนวน 11 แผ่น

(แทน)