การประกอบเลขที่
ASSEMBLY NO. 3301

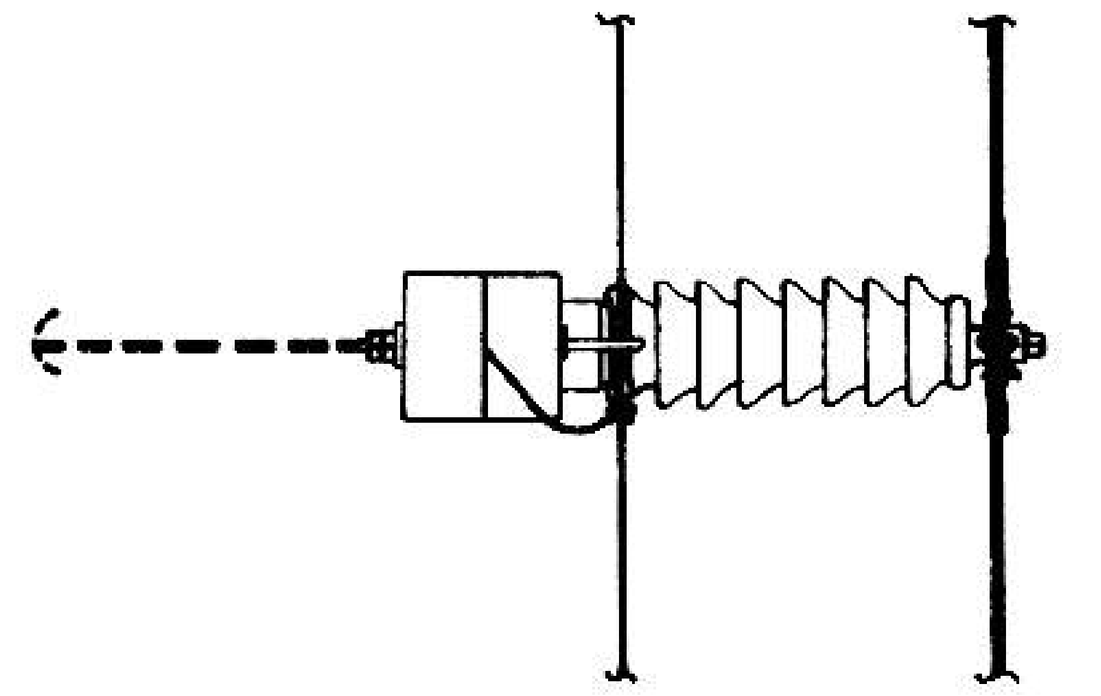

ดูข้อแนะนำในการก่อสร้างระบบจำหน่าย 1 เฟส 19 kV
แบบเลขที่ S02-015/20016

SEE CONSTRUCTION SUGGESTION OF 1-PHASE 19 kV SYSTEM
DWG. NO. S02-015/20016

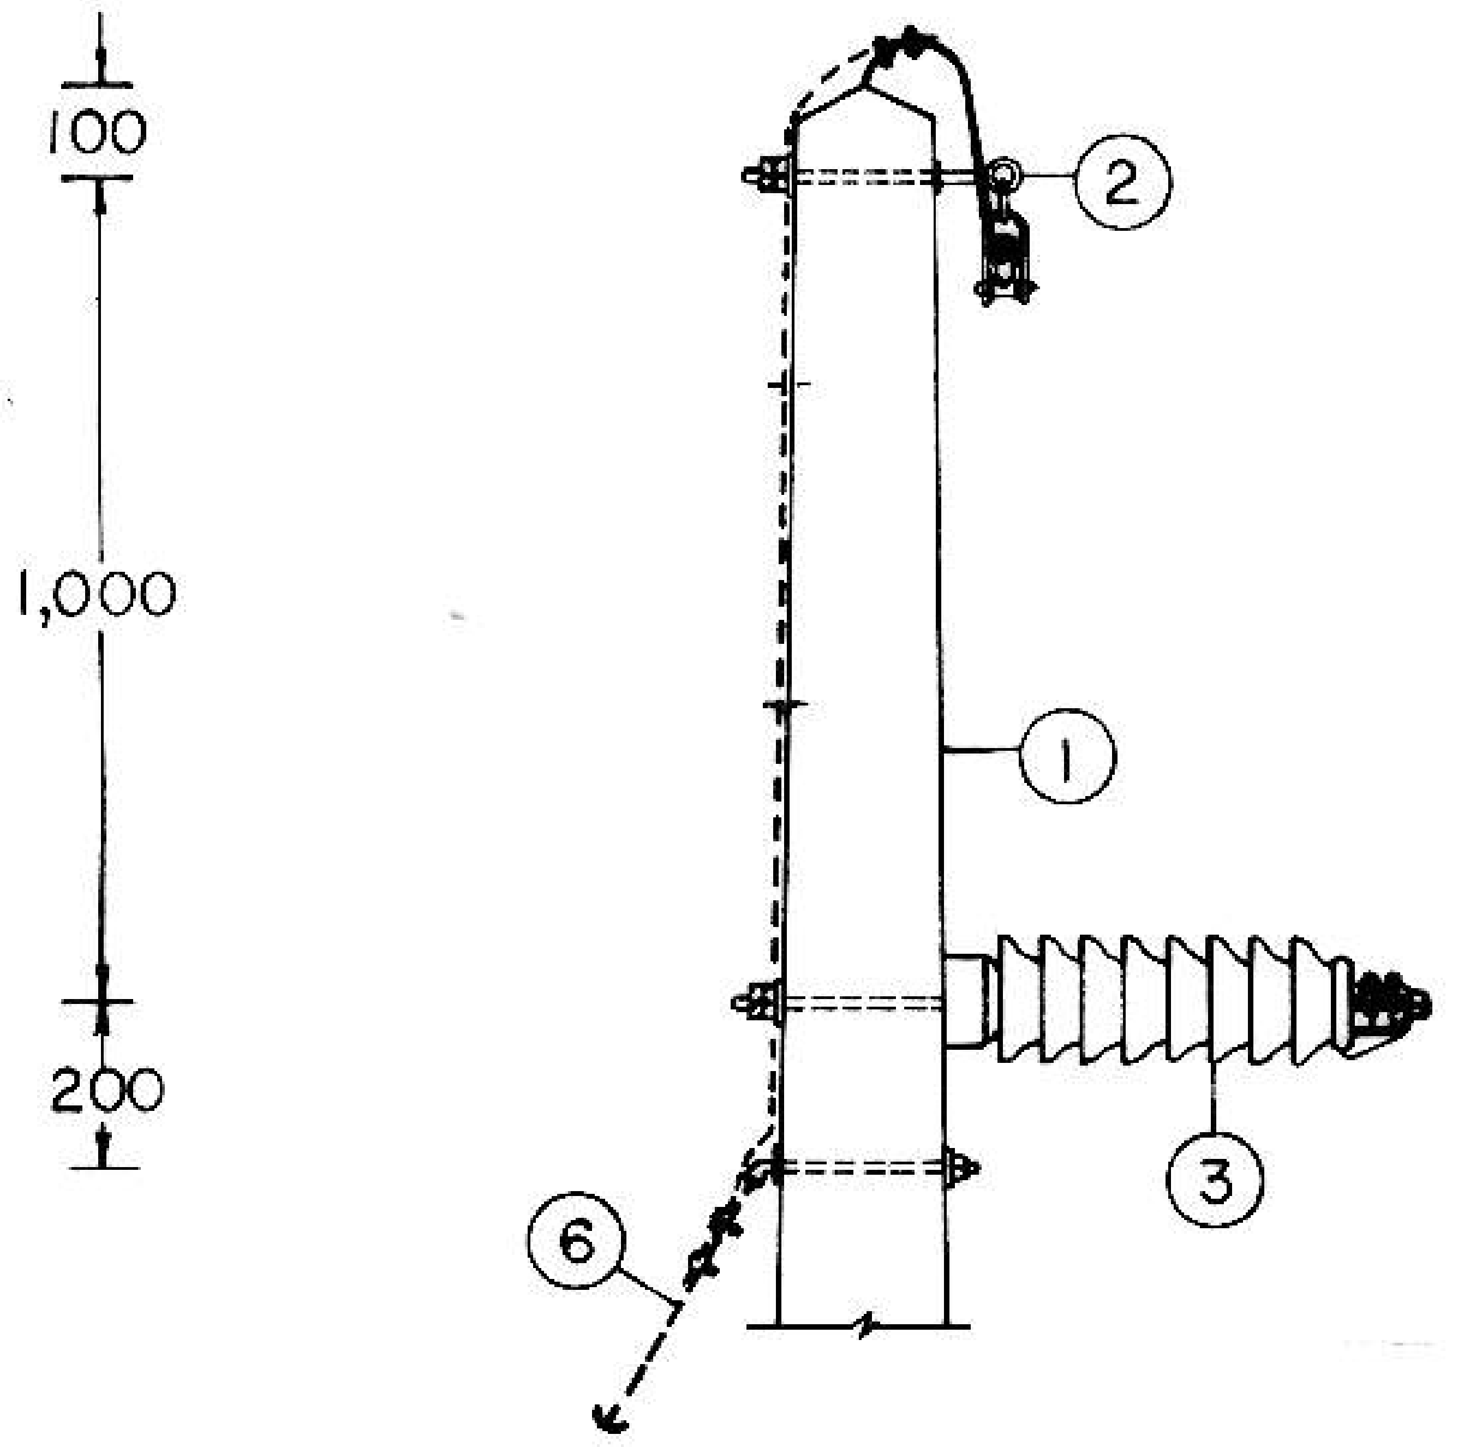

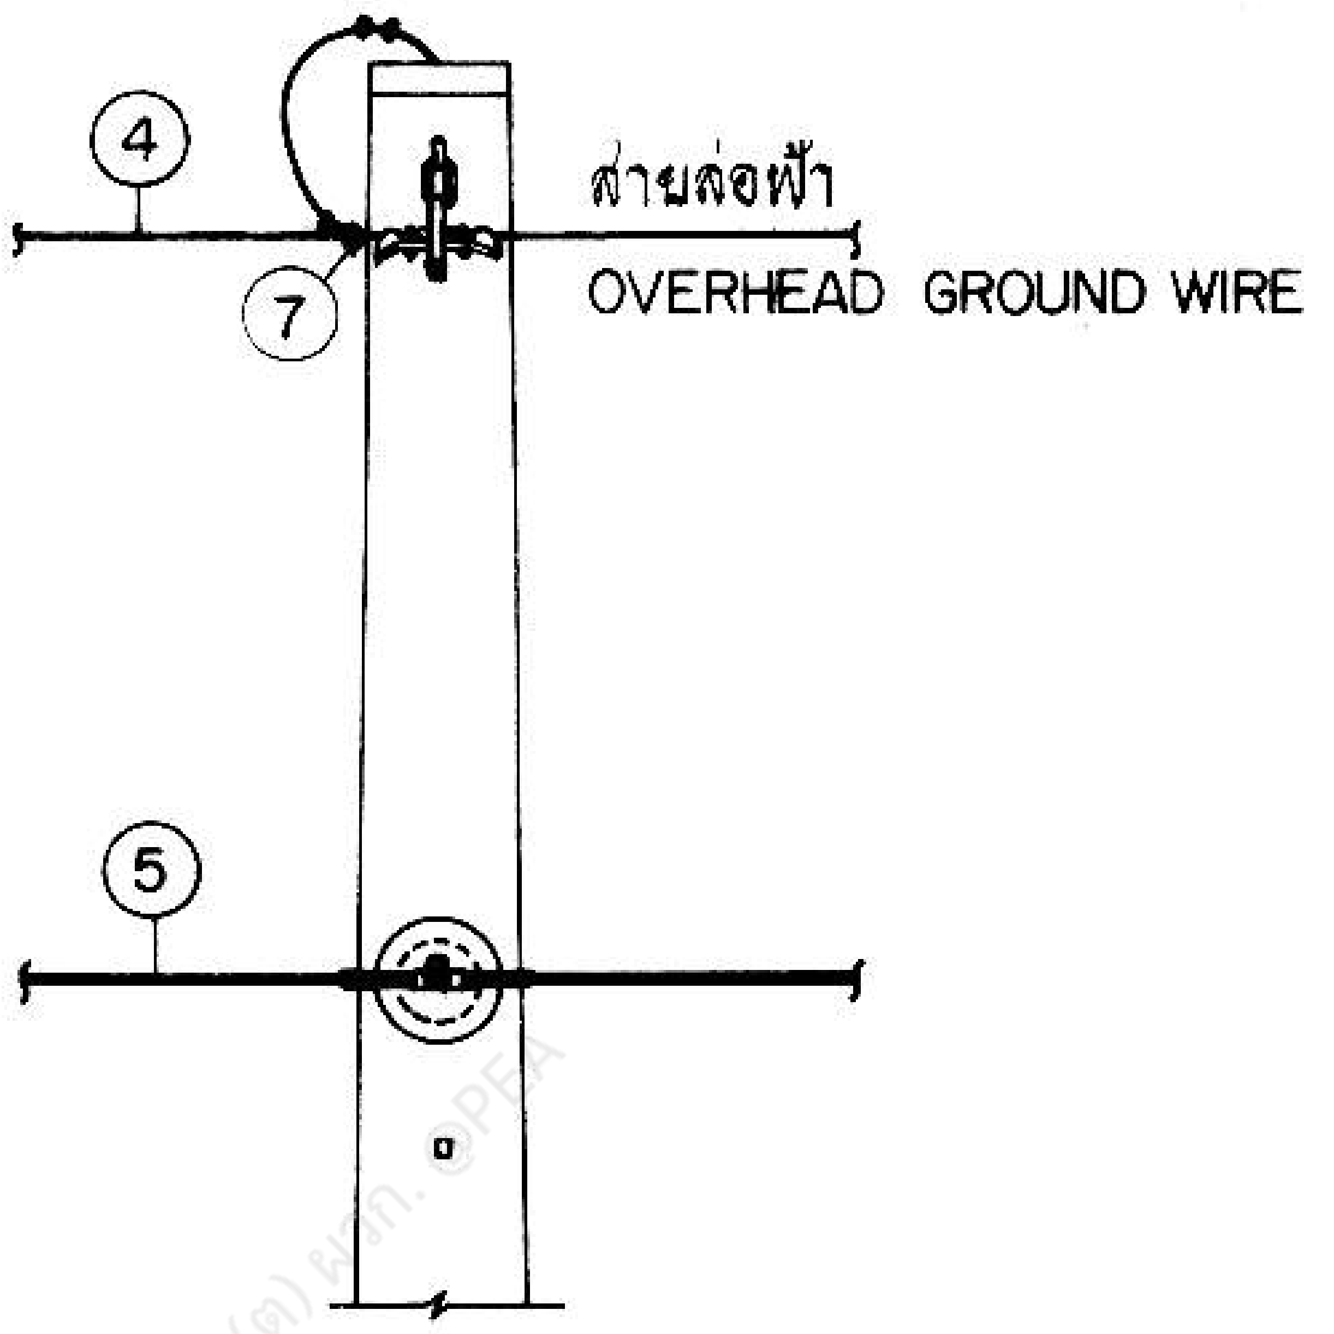

บัญชีวัสดุ
BILL OF MATERIAL

ลำดับที่ ITEM	รายละเอียด DESCRIPTION	จำนวน REQ'D		วัสดุเลขที่ MAT. NO.
		0°-5°	5°-30°	
1	เสาคอนกรีต ขนาด 12 ม. (สำหรับระบบ 33 kV) CONCRETE POLE 12 m LONG (FOR 33 kV SYSTEM)	1	1	00010004 (0034)
2	กราวด์วายร์แคล้มป์ สำหรับเสาคอนกรีต GROUND WIRE SUPPORT AND CLAMP, FOR CONCRETE POLE	1	1	01230201 (0298)
3	ลูกถ้วยโพสท์ไทพ์ 33 kV แบบฐานเรียบใช้กับเสาคอนกรีต INSULATOR, POST TYPE, 33 kV, WITH PLAIN BASE	1	1	03010000 (0410)
4	ลวดเหล็กตีเกลียว 25 ต.มม. มอก. 404 WIRE, STEEL STRANDED 25 mm^2 TIS 404			01100002 (0181)
5	สายอะลูมิเนียมแกนเหล็ก หรืออะลูมิเนียมอัลลอย 35-50 ต.มม. CONDUCTOR, ACSR. OR ALUMINIUM - ALLOY 35-50 mm^2			02020001-2 02030001-2
6	สายยึดโยงระบบ 33 kV พร้อมสมอบกครบชุด GY-32 ANCHOR GUY FOR 33 kV SYSTEM GY-32	—	1	——
7	ยูแคล้มป์ สลัก 1 ตัว M 8 (ไวร์โร้ป คลิ้ฟ) CLAMP, SINGLE U-BOLT, M 8 (WIRE ROPE CLIP)	4	2	01230000 (0165)

กองวิศวกรรม
ผู้เขียน
ผู้สำรวจ
วิศวกร
หัวหน้าแผนก
หัวหน้ากอง
รองผู้ว่าการฝ่ายเทคนิค

การไฟฟ้าส่วนภูมิภาค

ผู้ว่าการ

การประกอบลูกถ้วยโพสท์ไทพ์กับเสาคอนกรีต
ระบบ 1 เฟส 19 kV
สำหรับมุม 0°-30°

POST TYPE INSULATOR ASSEMBLY ON CONCRETE POLE
1-PHASE 19 kV SYSTEM
ANGLE STRUCTURE 0°-30°

ใช้แทนแบบ
ถูกแทนโดยแบบ
เขียนเสร็จวันที่ 21 ม.ค. 20
แก้แบบวันที่
มิติเป็น มม.
มาตราส่วน 1 : 25
แบบเลขที่ S02-015/20012
แผ่นที่ 1 ของจำนวน 1 แผ่น