การประกอบเลขที่
ASSEMBLY NO. **3235**

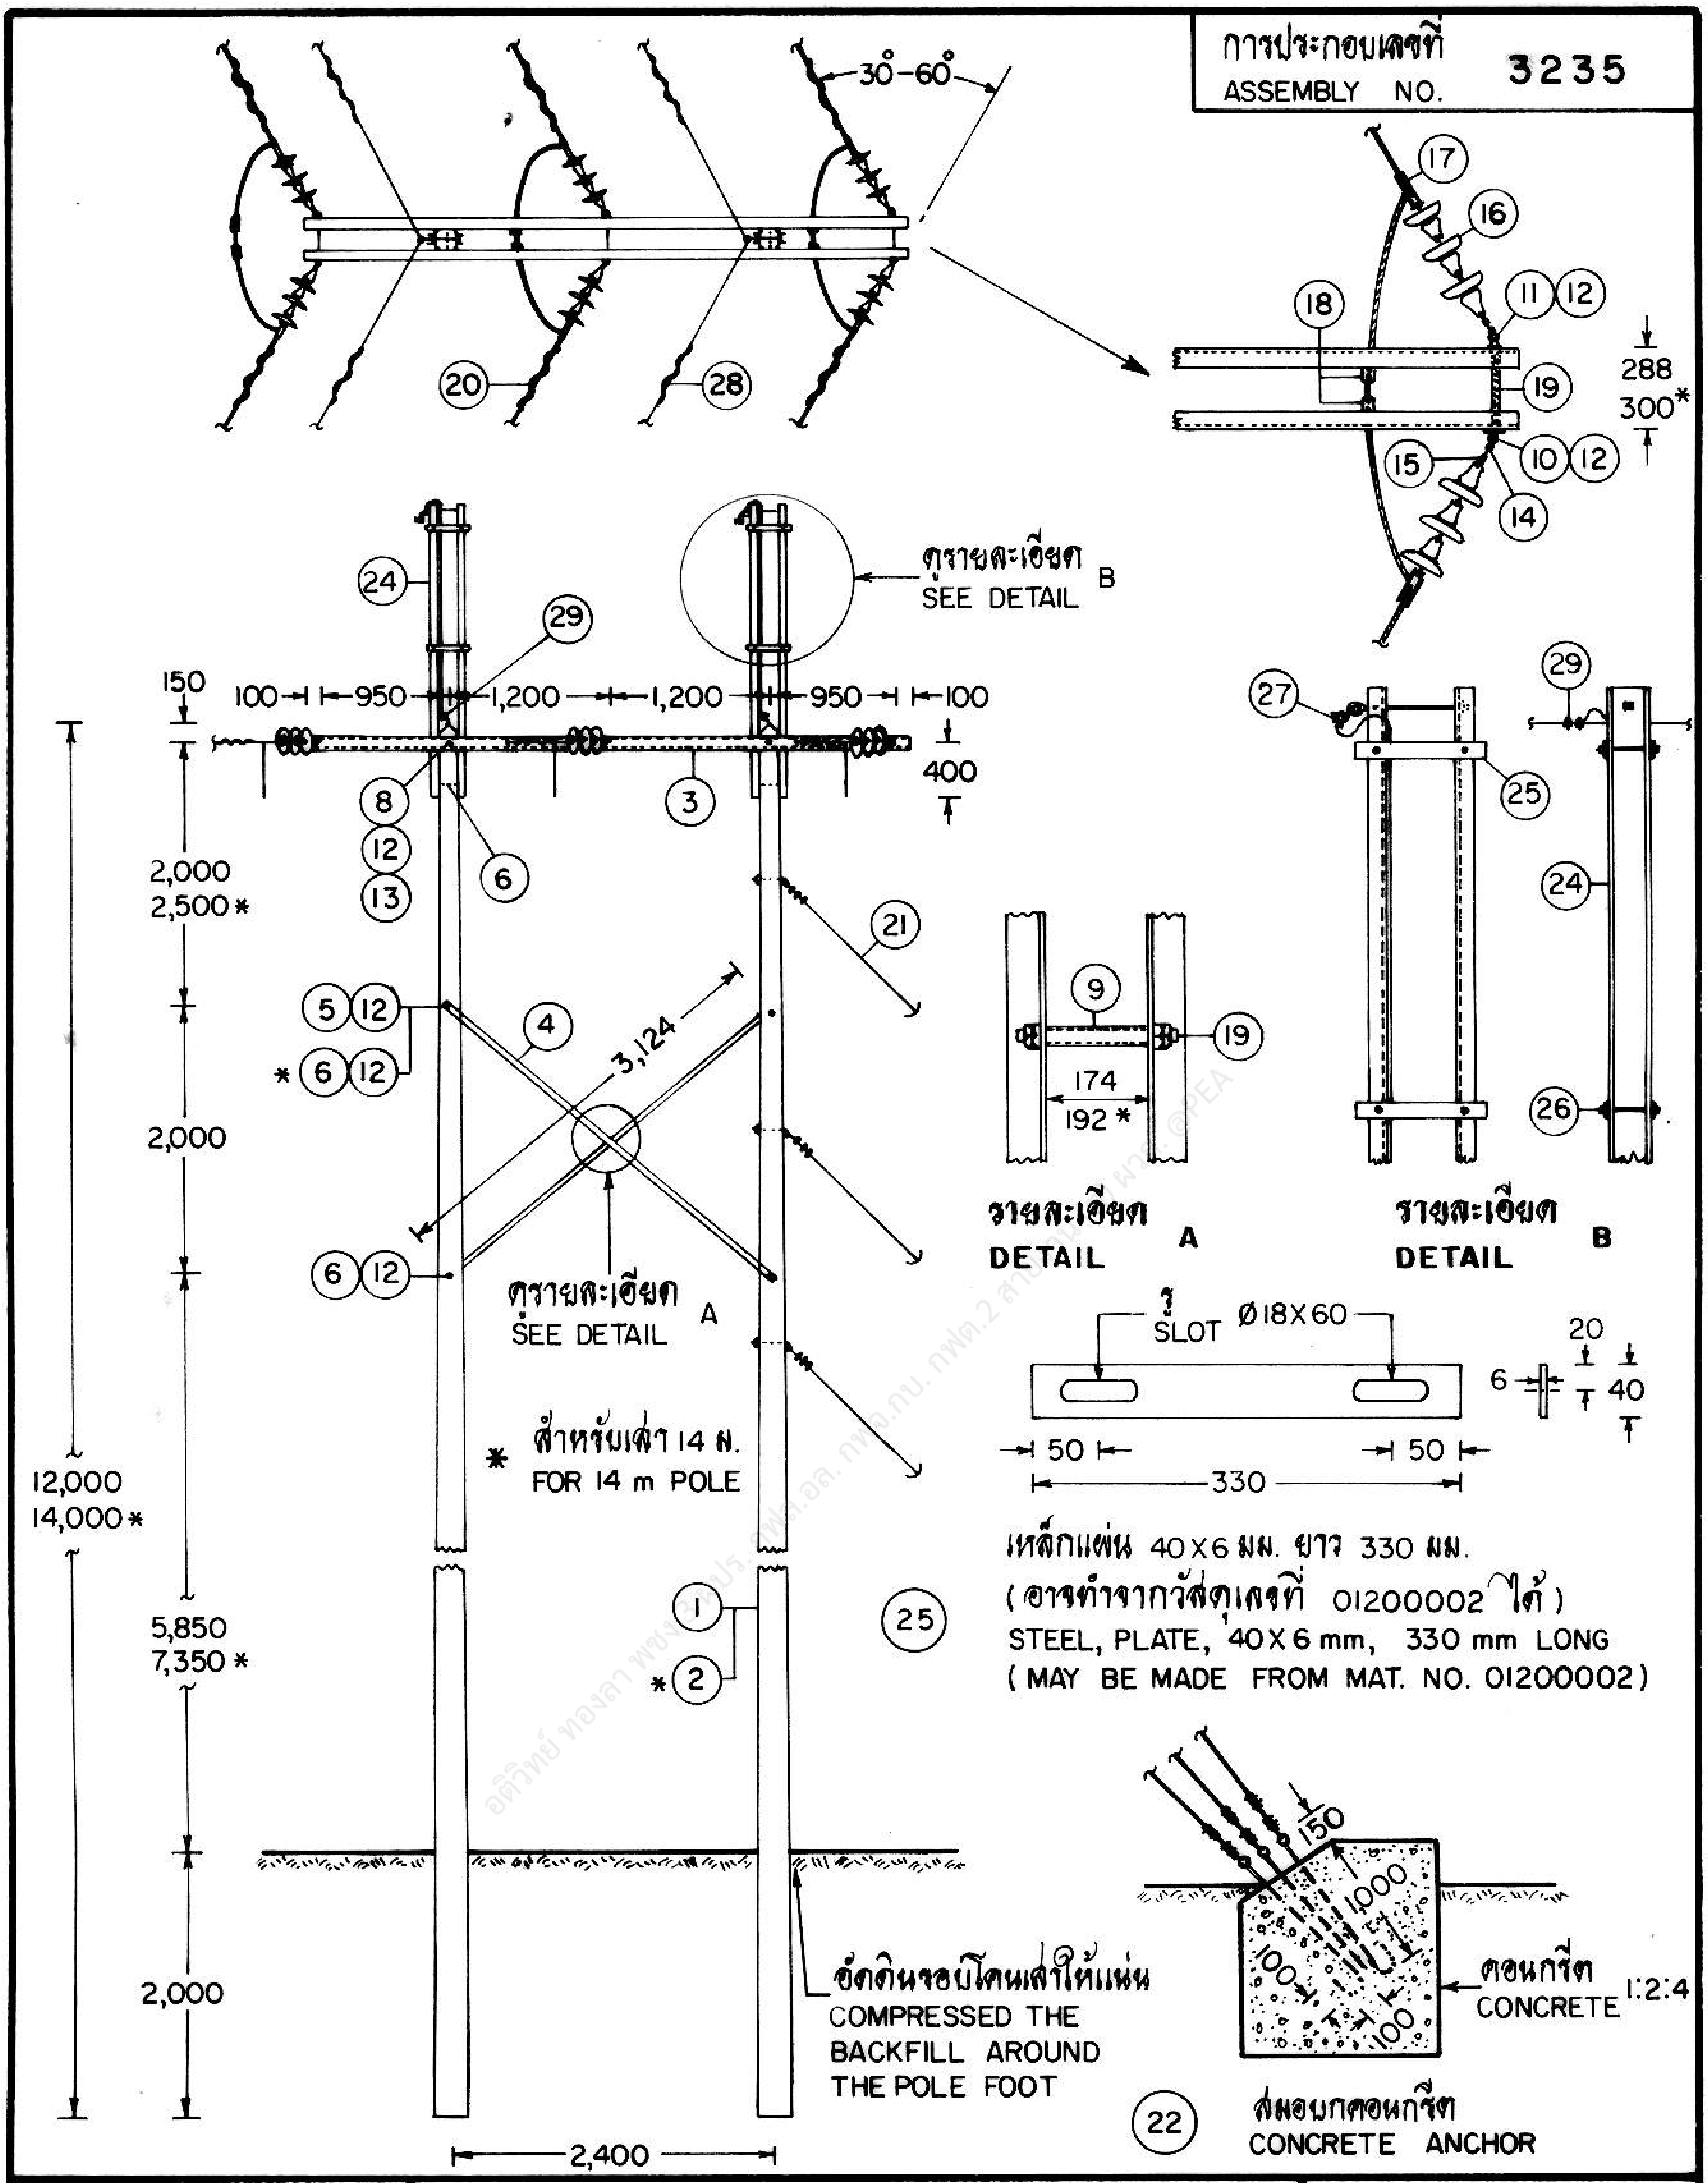

กองวิศวกรรมไฟฟ้าและเครื่องกล ฝ่ายวิศวกรรม	**การไฟฟ้าส่วนภูมิภาค**	ใช้แทนแบบ ถูกแทนโดยแบบ เขียนเสร็จวันที่ 21 ส.ค. 34 แก้แบบวันที่ มิติเป็น มิลลิเมตร มาตราส่วน 1 : 75
ผู้เขียน ผู้สำรวจ วิศวกร หัวหน้าแผนก ผู้อำนวยการกอง ผู้อำนวยการฝ่าย	ผู้ว่าการ 30 ก.ย. 34 โครงสร้างเสาคู่ สำหรับแนวสายไฟฟ้า ระบบ 33 kV ช่วงเสา 120 - 200 ม. มุม > 30°- 60°	
รองผู้ว่าการฝ่ายเทคนิค	33 kV, H - FRAME SUSPENSION STRUCTURE SPAN 120 - 200 m LINE ANGLE > 30°- 60°	แบบเลขที่ SAI-015/34021 แผ่นที่ 1 ของจำนวน 4 แผ่น

26 ก.ย. 2534 (แทน.)

การประกอบเลขที่
ASSEMBLY NO. **3235**

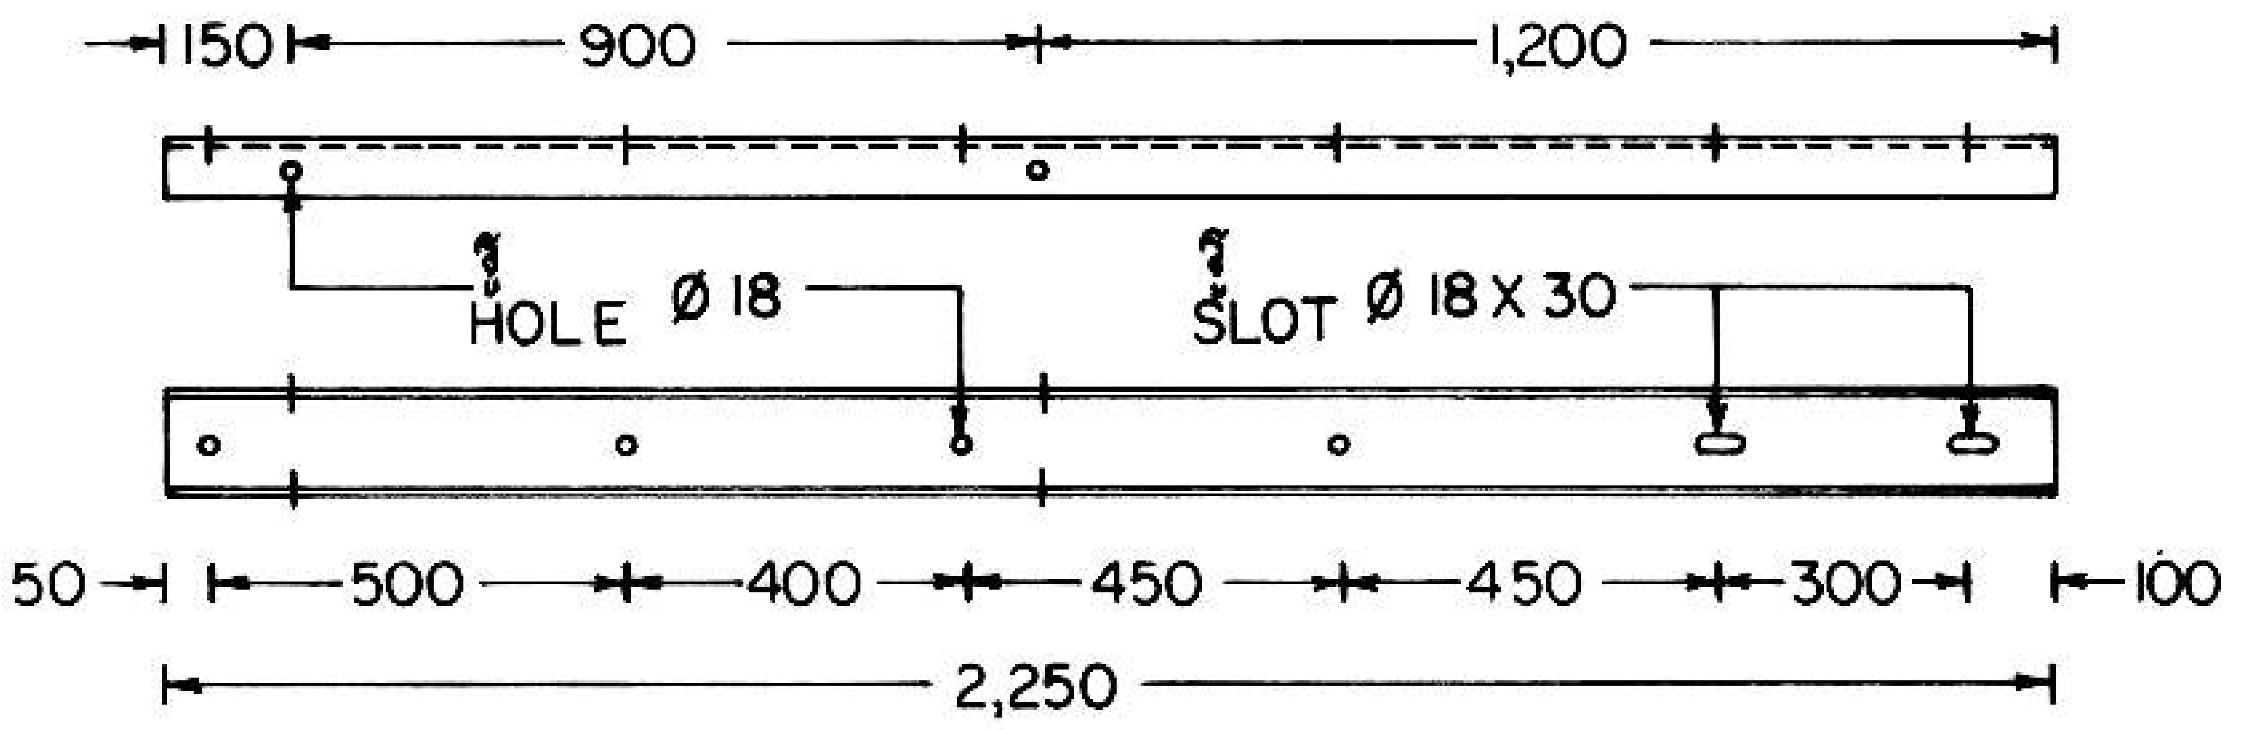

㉔ เหล็กรูปรางน้ำ ขนาด 125 X 65 X 6 มม. ยาว 2.25 ม. มอก. 116
STEEL, CHANNEL, 125 X 65 X 6 mm, 2.25 m LONG, TIS 116

บัญชีวัสดุ
BILL OF MATERIAL

ลำดับที่ ITEM	รายละเอียด DESCRIPTION	จำนวน REQ'D I	II	วัสดุเลขที่ MAT. NO.
1	เสาคอนกรีต 12 ม. POLE, CONCRETE, 12 m LONG	2	–	00010003 (0033)
2	เสาคอนกรีต 14 ม. POLE, CONCRETE, 14 m LONG	–	2	00010005 (0035)
3	เหล็กรูปรางน้ำ ขนาด 150 X 75 X 6.5 มม. ยาว 4.50 ม. (มอก. 116) STEEL CHANNEL, 150 X 75 X 6.5 mm, 4.50 m LONG (TIS 116)	2	2	01000302 (0114)
4	เหล็กฉาก ขนาด 75 X 75 X 6 มม. ยาว 3.50 ม. (มอก. 116) STEEL ANGLE, 75 X 75 X 6 mm, 3.50 m LONG (TIS 116)	2	2	01010100 (0123)
5	สลักเกลียว M 16 X 200 มม. BOLT, MACHINE, M 16 X 200 mm	2	–	01110202 (0220)
6	สลักเกลียว M 16 X 250 มม. BOLT, MACHINE, M 16 X 250 mm	6	8	01110203 (0223)
7	สลักเกลียว M 16 X 300 มม. BOLT, MACHINE, M 16 X 300 mm	–	–	01110204 (0224)
8	สลักเกลียว M 16 X 350 มม. BOLT, MACHINE, M 16 X 350 mm	2	2	01110205 (0225)
9	สลักเกลียวตลอด M 16 X 400 มม. BOLT, DOUBLE ARMING, M 16 X 400 mm	1	1	01120000 (0243)
10	สลักเกลียวห่วงกลม M 16 X 400 มม. BOLT, DOUBLE ARMING, ROUND EYE, M 16 X 400 mm	3	3	01130000 (0246)
11	นัทรูปห่วง M 16 NUT, EYE, M 16	3	3	01180001 (0345)
12	แหวนสี่เหลี่ยมแบน 52 X 52 X 4.5 มม. รู Ø 18 มม. มอก. 258 WASHER, SQUARE, FLAT, 52 X 52 X 4.5 mm, HOLE Ø 18 mm, TIS 258	14	14	01180100 (0355)
13	แหวนสปริง M 16 มอก. 259 WASHER, LOCK, M 16, TIS 259	2	2	01180301 (0365)
14	ข้อต่อแบบบอล - เคลวิส ANSI แบบ B BALL-CLEVIS, ANSI, TYPE B	6	6	03140005 (0486)

กองวิศวกรรมไฟฟ้าและเครื่องกล
ฝ่ายวิศวกรรม

ผู้เขียน
ผู้สำรวจ
วิศวกร
หัวหน้าแผนก
ผู้อำนวยการกอง
ผู้อำนวยการฝ่าย

รองผู้ว่าการฝ่ายเทคนิค

26 ก.ย. 2534 (แทน)

การไฟฟ้าส่วนภูมิภาค

ผู้ว่าการ 30 ก.ย. 34

โครงสร้างเสาคู่ สำหรับแขวนสายไฟฟ้า ระบบ 33 kV
ช่วงเสา 120 - 200 ม.
มุม > 30°- 60°

33 kV, H-FRAME SUSPENSION STRUCTURE
SPAN 120 - 200 m
LINE ANGLE > 30°- 60°

ใช้แทนแบบ
ถูกแทนโดยแบบ
เขียนเสร็จวันที่ 21 ส.ค. 34
แก้แบบวันที่
มิติเป็น มิลลิเมตร
มาตราส่วน

แบบเลขที่ SAI-015/34021
แผ่นที่ 2 ของจำนวน 4 แผ่น

การประกอบเลขที่
ASSEMBLY NO. 3235

บัญชีวัสดุ
BILL OF MATERIAL

ลำดับที่ ITEM	รายละเอียด DESCRIPTION	จำนวน REQ'D I	II	วัสดุเลขที่ MAT. NO.
15	ข้อต่อแบบซ็อกเก็ต-อาย ANSI แบบ B SOCKET-EYE, ANSI, TYPE B	6	6	
16	ลูกถ้วยแขวน มอก. 354 แบบ ง (แบบ 52-4) INSULATOR, SUSPENSION TYPE, TIS 354, TYPE D (CLASS 52-4)	18	18	03020000 (0414)
17	สเตรนแคล้มป์ สำหรับสายอะลูมิเนียมแกนเหล็ก CLAMP, STRAIN, FOR ACSR	6	6	03110002 03110005
18	พี.จี. คอนเนคเตอร์ 3 สลัก CONNECTOR, PARALLEL GROOVE, TRIPLE BOLT	6	6	02300103 02300104
19	ท่อเหล็ก ชื่อขนาด 20 มม. หนา 2.65 มม. ความยาวตามต้องการ PIPE, IRON, DIA. 20 mm I.D., 2.65 mm THICKNESS; LENGTH AS REQUIRED	4	4	—
20	ไวเบรชั่นแดมเปอร์ แบบสไปแรล สำหรับสายอะลูมิเนียมแกนเหล็ก และสายอะลูมิเนียมเจือ VIBRATION DAMPER, SPIRAL, FOR ACSR, AND Al-ALLOY CONDUCTOR			02200101 02200103
21	การยึดโยง GY-32 (ลวดเหล็กตีเกลียว 95 ต.มม. ไม่รวมสมอบก) GUY, GY-32 (STEEL STRANDED WIRE 95 mm², ANCHOR NOT INCLUDED)	3	3	—
22	สมอบกคอนกรีต 1,750 X 1,750 X 1,750 มม. (คอนกรีต 1:2:4) ANCHOR, CONCRETE, 1,750 X 1,750 X 1,750 mm (CONCRETE 1:2:4)	1	1	—
23	คอนกรีต 1:3:5 CONCRETE 1:3:5	4 ม.³ m³	4 ม.³ m³	—
24	เหล็กรูปรางน้ำ ขนาด 125 X 65 X 6 มม. ยาว 2.25 ม. มอก. 116 เจาะรูตามแบบแผ่นที่ 2 STEEL, CHANNEL, 125 X 65 X 6 mm, 2.25 m LONG, TIS 116; PUNCH HOLE AS DWG. ON SHEET NO. 2	4	4	—
25	เหล็กแผ่น ขนาด 40X6 มม. ยาว 330 มม. เจาะรูตามแบบแผ่นที่ 1 STEEL, PLATE, 40X6 mm, 330 mm LONG; PUNCH HOLE AS DWG. ON SHEET NO. 1	8	8	—
26	สลักเกลียว M 16 X 170 มม. BOLT, MACHINE, M 16 X 170 mm	8	8	01110201 (0221)
27	กราวด์วายร์แคล้มป์ สำหรับเสาคอนกรีต GROUND WIRE SUPPORT AND CLAMP, FOR CONCRETE POLE	2	2	(0298)
28	ไวเบรชั่นแดมเปอร์ แบบสไปแรล สำหรับลวดเหล็กตีเกลียว 25 ต.มม. VIBRATION DAMPER, SPIRAL, FOR 25 mm² STEEL STRANDED WIRE	4	4	(0904)
29	ยูแคล้มป์ สลัก 1 ตัว M 8 CLAMP, SINGLE U-BOLT, M 8	8	8	01230000 (0165)

กองวิศวกรรมไฟฟ้าและเครื่องกล
ฝ่ายวิศวกรรม

ผู้เขียน
ผู้สำรวจ
วิศวกร
หัวหน้าแผนก
ผู้อำนวยการกอง
ผู้อำนวยการฝ่าย

รองผู้ว่าการฝ่ายเทคนิค

การไฟฟ้าส่วนภูมิภาค

ผู้ว่าการ 30 ก.ย. 34

โครงสร้างเสาคู่ สำหรับแขวนสายไฟฟ้า ระบบ 33 kV
ช่วงเสา 120 - 200 ม.
มุม > 30°-60°

33 kV, H-FRAME SUSPENSION STRUCTURE
SPAN 120 - 200 m
LINE ANGLE > 30°-60°

ใช้แทนแบบ
ถูกแทนโดยแบบ
เขียนเสร็จวันที่ 21 ส.ค. 34
แก้แบบวันที่
มิติเป็น
มาตราส่วน

แบบเลขที่ SAI-015/34021
แผ่นที่ 3 ของจำนวน 4 แผ่น

26 ก.ย. 2534

การประกอบเลขที่
ASSEMBLY NO. 3235

ข้อกำหนด
REGULATIONS

ชนิดและขนาดของสายไฟฟ้า ต.มม. TYPE AND SIZE OF CONDUCTOR mm^2	ระยะระหว่างเสาสูงสุด ม. MAXIMUM SPAN LENGTH m	ระยะหย่อนยานต่ำสุดของสายไฟฟ้าทุกเส้น ม. MINIMUM SAG OF ALL CONDUCTORS m
ACSR 95/15	200	3.00
ACSR 120/20		4.00
ACSR 185/30		6.00
AA 95		3.00
AA 120		3.00
AA 185		4.00

หมายเหตุ

1. จำนวนในบัญชีวัสดุ :
   สดมภ์ I สำหรับเสาคอนกรีต 12 ม.
   สดมภ์ II สำหรับเสาคอนกรีต 14 ม.
2. ACSR หมายถึงสายอะลูมิเนียมแกนเหล็ก

   AA หมายถึงสายอะลูมิเนียมเจือ
3. เสาต้นที่ปักอยู่ในบริเวณที่เป็นดินอ่อน (ดินเหนียว, ดินเลน) หรือดินแข็งปานกลาง (ดินปนทราย) ให้เทคอนกรีตหุ้มโคนเสา ลึก 2.00 ม. จากระดับผิวดิน ขนาดหน้าตัด 1.00 X 1.00 ม.

NOTES

1. REQ'D IN BILL OF MATERIAL :
   COLUMN I, FOR 12 m CONCRETE POLE.
   COLUMN II, FOR 14 m CONCRETE POLE.
2. ACSR IS ALUMINIUM CONDUCTOR STEEL REINFORCED.

   AA IS ALL ALUMINIUM ALLOY CONDUCTOR.
3. THE POLE FOOT SHALL BE COVERED WITH CONCRETE 2.00 m DEPTH, CROSS-SECTION 1.00 X 1.00 m, IF IT IS SET IN POOR SOIL (MARCHY SOIL, OR CLAY) OR NORMAL SOIL (SANDY CLAY).

กองวิศวกรรมไฟฟ้าและเครื่องกล
ฝ่ายวิศวกรรม

ผู้เขียน
ผู้สำรวจ
วิศวกร
หัวหน้าแผนก
ผู้อำนวยการกอง
ผู้อำนวยการฝ่าย

รองผู้ว่าการฝ่ายเทคนิค

(แทน)

26 ก.ย. 2534

การไฟฟ้าส่วนภูมิภาค

ผู้ว่าการ 30 ก.ย. 34

โครงสร้างเสาคู่ สำหรับแขวนสายไฟฟ้า ระบบ 33 kV
ช่วงเสา 120 - 200 ม.
มุม >30°-60°

33 kV, H-FRAME SUSPENSION STRUCTURE
SPAN 120 - 200 m
LINE ANGLE >30°-60°

ใช้แทนแบบ
ถูกแทนโดยแบบ
เขียนเสร็จวันที่ 21 ส.ค. 34
แก้แบบวันที่
มิติเป็น
มาตราส่วน

แบบเลขที่ SAL-015/34021
แผ่นที่ 4 ของจำนวน 4 แผ่น