การประกอบเลขที่ 5221
ASSEMBLY NO.

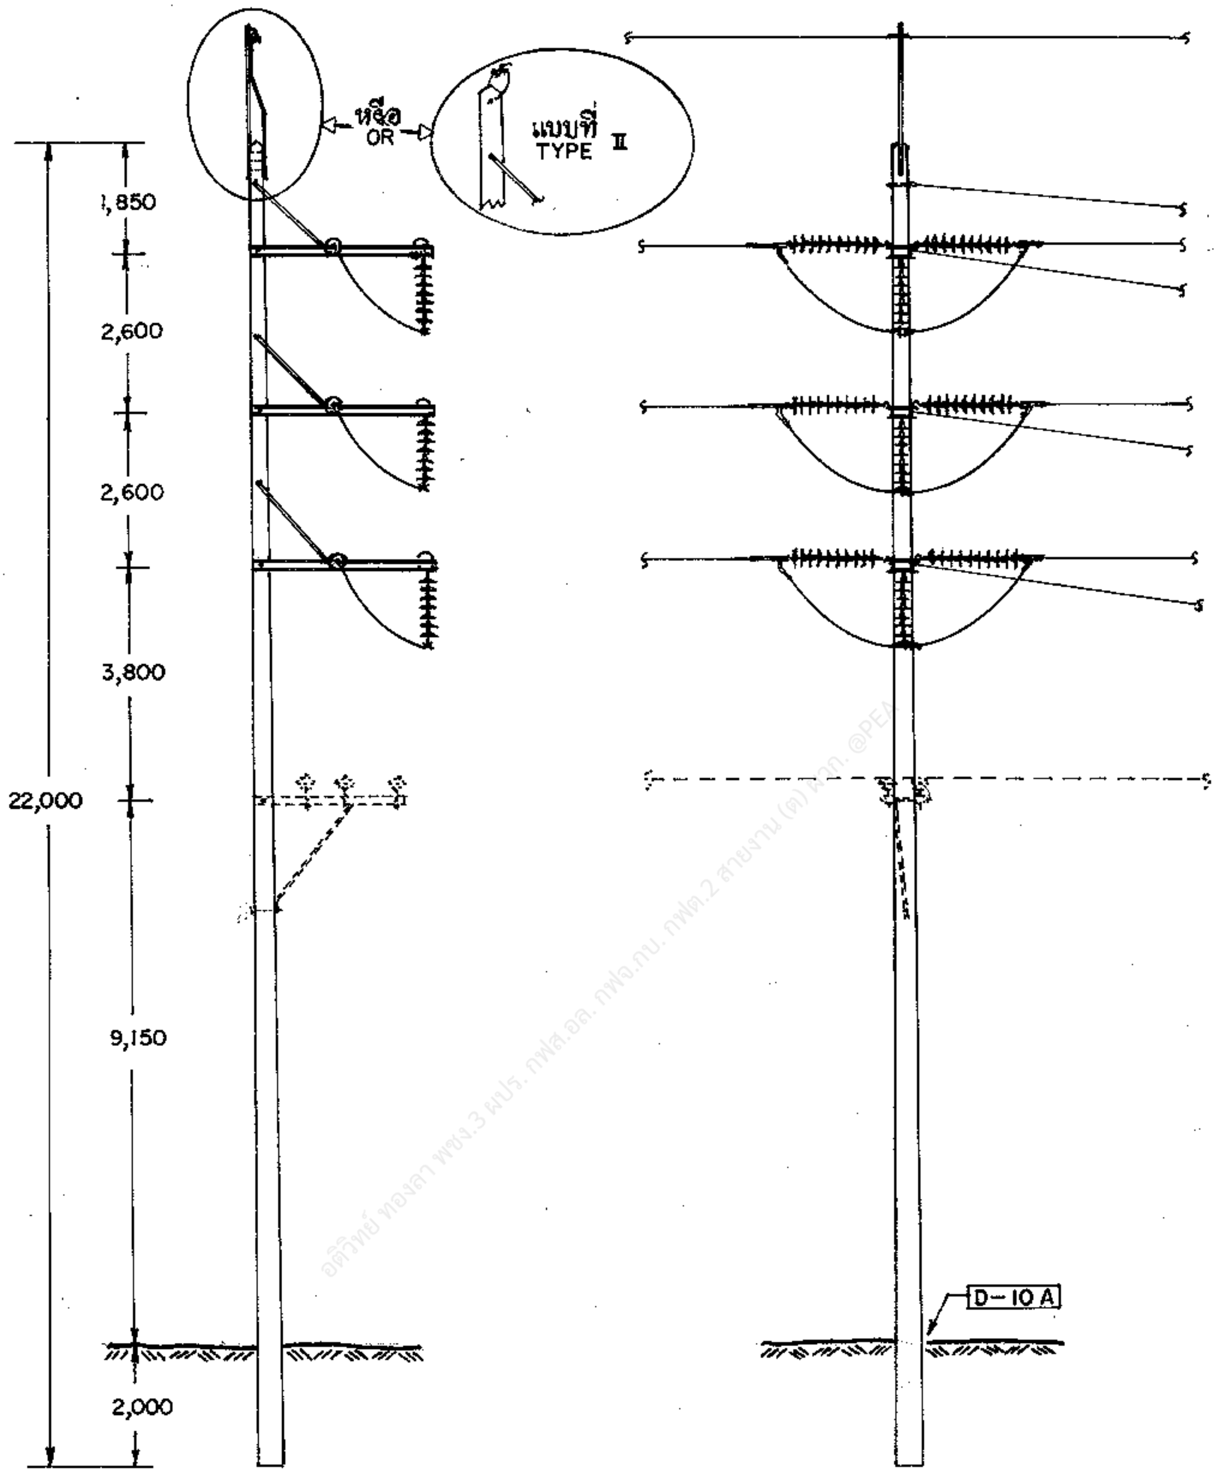

อดิวิทย์ ทองลา พชง.3 ผปร. กฟส.อล. กฟจ.กบ. กฟต.2 สายงาน (ต) ผวก. @PEA

กองวิศวกรรมไฟฟ้าและเครื่องกล ฝ่ายวิศวกรรม	การไฟฟ้าส่วนภูมิภาค	ใช้แทนแบบ .... ถูกแทนโดยแบบ ....
ผู้เขียน ผู้ตรวจ วิศวกร หัวหน้าแผนก ผู้อำนวยการกอง ผู้อำนวยการฝ่าย	ผู้ว่าการ .... 2539 115 kV วงจรเดี่ยว สายไฟฟ้าเดี่ยว โครงสร้างเสาเข้าปลายสายสองข้าง ก่อนเสาวางทางโค้ง แบบ SS-AS-4	เขียนเสร็จวันที่ 5 ก.ย. 39 แก้แบบวันที่ .... วัดเป็น มิลลิเมตร มาตราส่วน 1 : 125
รองผู้ว่าการ	115 kV SINGLE-CIRCUIT SINGLE-CONDUCTOR DOUBLE DEADEND STRUCTURE, ADJACENT POLE TO ANGLE TYPE SS-AS-4	แบบเลขที่ SAI-015/39013 แผ่นที่ 1 ของจำนวน 5 แผ่น

การประกอบเลขที่ / ASSEMBLY NO. 5221

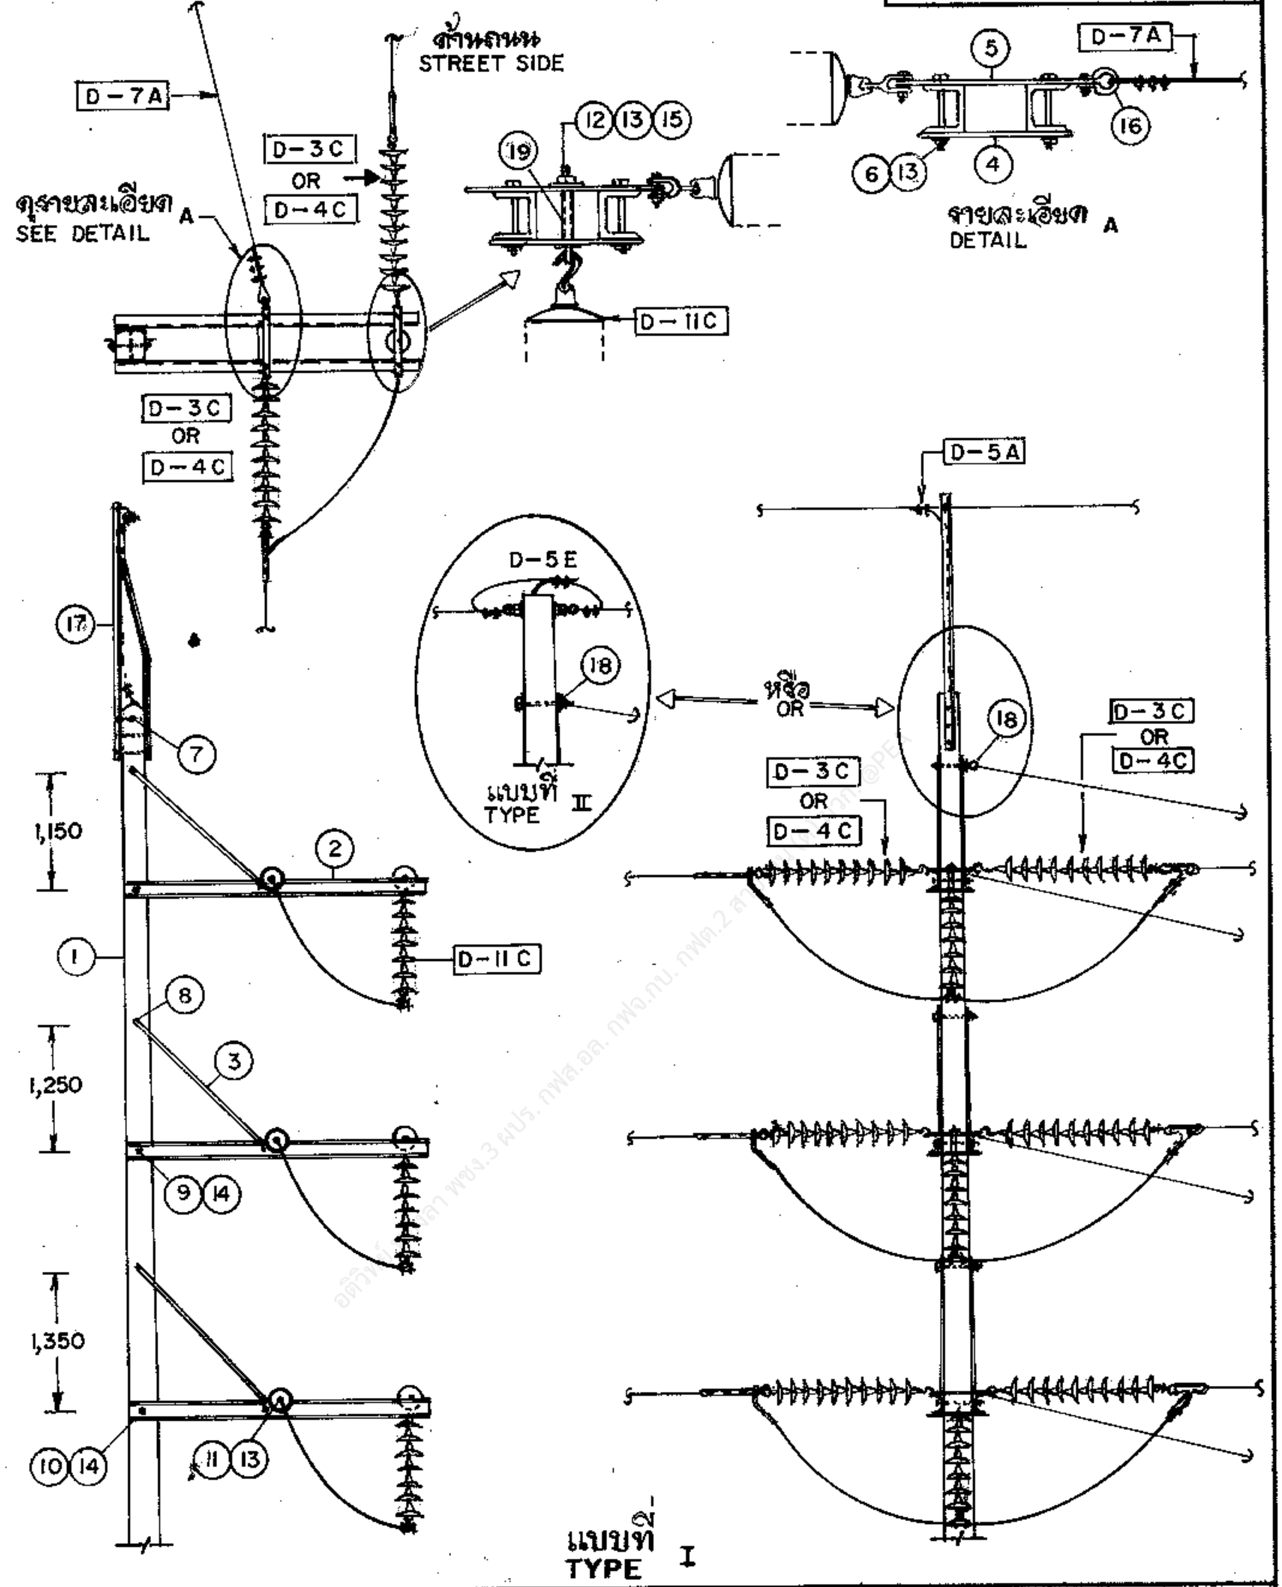

แบบที่ I
TYPE

กองวิศวกรรมไฟฟ้าและเครื่องกล ฝ่ายวิศวกรรม	การไฟฟ้าส่วนภูมิภาค	ใช้แทนแบบ .... ถูกแทนโดยแบบ ....
ผู้เขียน .... ผู้สำรวจ .... วิศวกร .... หัวหน้าแผนก .... ผู้อำนวยการกอง .... ผู้อำนวยการฝ่าย	ผู้ว่าการ .... 115 kV วงจรเดี่ยว สายไฟฟ้าเดี่ยว โครงสร้างเสาเข้าปลายสายสองข้าง ก่อนเสาช่วงทางโค้ง SS-AS-4	เขียนเสร็จวันที่ 5 ก.ย. 39 แก้แบบวันที่ .... วัดเป็น มิลลิเมตร มาตราส่วน 1 : 75
รองผู้ว่าการ	115 kV SINGLE CIRCUIT SINGLE CONDUCTOR DOUBLE DEADEND STRUCTURE, ADJACENT POLE TO ANGLE TYPE SS-AS-4	แบบเลขที่ SAI-015/39013 แผ่นที่ 2 ของจำนวน 5 แผ่น

การประกอบเลขที่ ASSEMBLY NO. **5221**

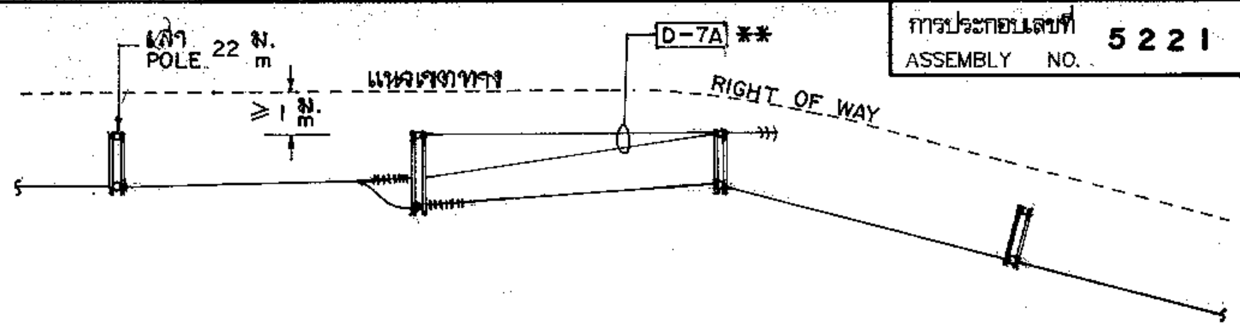

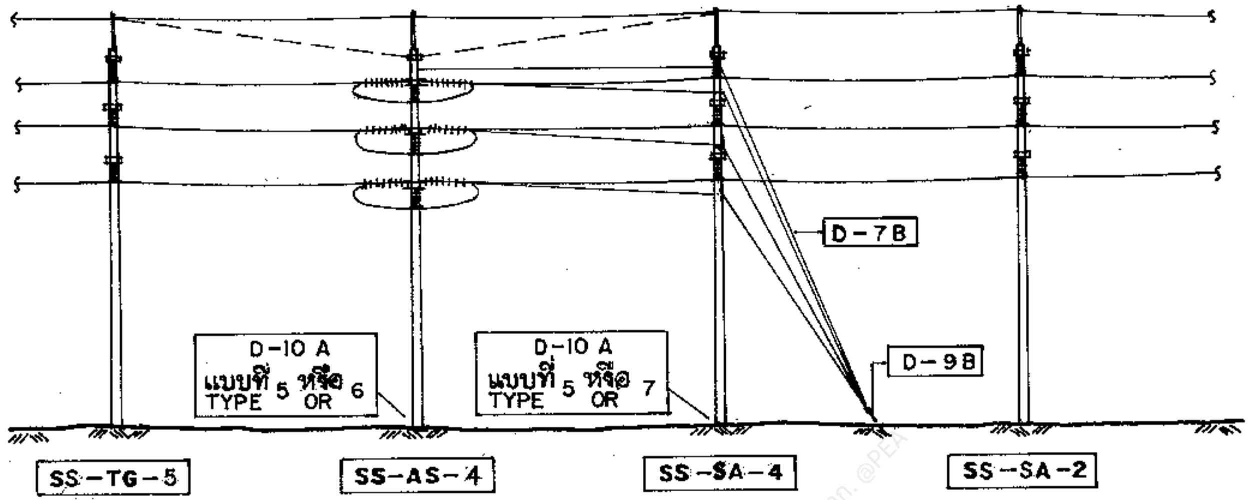
D-7B
D-9B
D-10 A แบบที่ 5 หรือ 6 TYPE OR
D-10 A แบบที่ 5 หรือ 7 TYPE OR
SS-TG-5
SS-AS-4
SS-SA-4
SS-SA-2

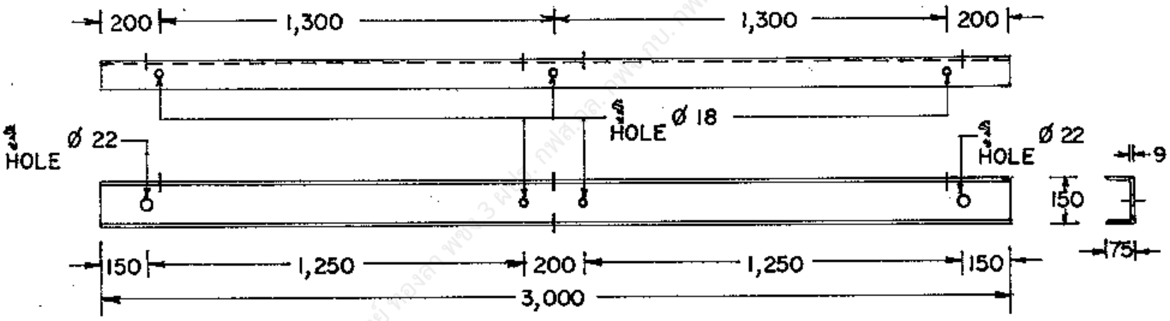

วัสดุลำดับที่ MATERIAL ITEM ②

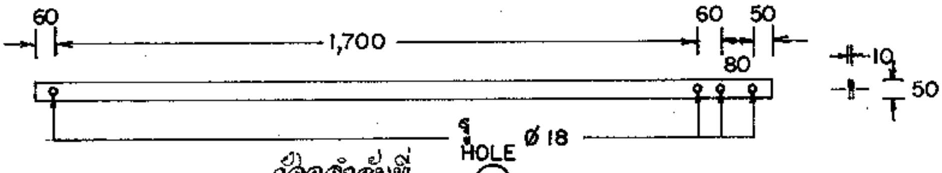

วัสดุลำดับที่ MATERIAL ITEM ③

กองวิศวกรรมไฟฟ้าและเครื่องกล ฝ่ายวิศวกรรม	การไฟฟ้าส่วนภูมิภาค	ใช้แทนแบบ .... ถูกแทนโดยแบบ ....
ผู้เขียน .... ผู้ตรวจ .... วิศวกร .... หัวหน้าแผนก .... ผู้อำนวยการกอง .... ผู้อำนวยการฝ่าย	ผู้ว่าการ .... 115 kV วงจรเดี่ยว สายไฟฟ้าเดี่ยว โครงสร้างเสาเข้าปลายสายสองข้าง ก่อนเสาช่วงทางโค้ง แบบ SS-AS-4	เขียนเสร็จวันที่ 5 ก.ย. 39 แก้แบบวันที่ .... มิติเป็น มิลลิเมตร มาตราส่วน 1:20, 1:25
รองผู้ว่าการ	115 kV SINGLE-CIRCUIT SINGLE-CONDUCTOR DOUBLE DEADEND STRUCTURE, ADJACENT POLE TO ANGLE TYPE SS-AS-4	แบบเลขที่ SAI-015/39013 แผ่นที่ 3 ของจำนวน 5 แผ่น

การประกอบเลขที่
ASSEMBLY NO. **5221**

บัญชีวัสดุ
BILL OF MATERIAL

ลำดับที่ ITEM	รายละเอียด DESCRIPTION	จำนวน REQ'D I	จำนวน REQ'D II	วัสดุเลขที่ MAT. NO.
1	เสาคอนกรีต 22 เมตร POLE, CONCRETE, 22 m LONG	1	1	0041 00010011
2	คอนสายแบบเหล็กรูปรางน้ำ ขนาด 150x75x9 มม. ยาว 3.00 มม. มอก. 116 CROSSARM,STEEL CHANNEL, 150x75x9 mm.,3.00 m. LONG TIS 116	6	6	-
3	เหล็กประกับคอนสาย ขนาด 50x10x1,950 มม. มอก. 55 BRACE, FLAT, FOR CROSSARM, 50x10x1,950 mm TIS 55	6	6	0109 01200003
4	แผ่นเหล็ก ขนาด 6x100x450มม. PLATE, STEEL 6x100x450 mm	6	6	0143 01030002
5	แผ่นเหล็กยึดสองปลาย ขนาด 12x100x760 มม. PLATE,STEEL,DOUBLE ARMING,12x100x760 mm.	6	6	6006 01030102
6	สลักเกลียว เอ็ม 16x250มม. BOLT, MACHINE M.16x250 mm	12	12	0223 01110203
7	สลักเกลียว เอ็ม 16x300มม. BOLT, MACHINE M.16x300 mm	4	1	0224 01110204
8	สลักเกลียว เอ็ม 16x350มม. BOLT, MACHINE M.16x350 mm	2	2	0225 01110205
9	สลักเกลียว เอ็ม 20x350มม. BOLT, MACHINE M.20x350 mm	2	2	0232 01110300
10	สลักเกลียว เอ็ม 20x400 มม. BOLT, MACHINE M.20x400 mm	1	1	0233 01110301
11	สลักเกลียวตลอด เอ็ม 16x400มม. BOLT, DOUBLE ARMING, M.16x400 mm	3	3	0243 01120000
12	สลักห่วงโอเวล เอ็ม 16x200มม. BOLT, OVAL EYE M.16x200 mm	3	3	0258 01150001
13	แหวนรองแบบเรียบ ประเภทจัตุรัสขนาดใหญ่ 52x52x4.5 มม เส้นผ่านศูนย์กลางรู 18 มม มอก. 258 WASHER, PLAIN, SQUARE, LARGE 52x52x4.5 mm HOLE DIA. 18 mm TIS 258	42	42	0355 01180100
14	แหวนรองแบบเรียบ ประเภทจัตุรัสขนาดใหญ่ 62x62x6 มม เส้นผ่านศูนย์กลางรู 22 มม มอก. 258 WASHER, PLAIN, SQUARE, LARGE 62x62x6 mm HOLE DIA. 22 mm TIS 258	6	6	0356 01180101
15	แหวนรองแบบสปริง ขนาดระบุ 16 มม. ประเภทใช้งานทั่วไป มอก. 259 WASHER, LOCK, SPRING, SIZE 16 mm, GENERAL PURPOSE, TIS 259	3	3	0365 01180301
16	ทิมเบิลเคลวิส สำหรับปรีฟอร์มเข้าปลายสาย CIVIS, THIMBLE, FOR PREFORMED DEAD-END	3	3	0482 03140011
17	เหล็กฉาก รับสายล่อฟ้าทางโค้ง 65x65x6 มม. ยาว 2,500 มม. STEEL ANGLE, OVERHEAD GROUND WIRE CORNER BAYONET 65x65x6 mm 2,500 mm LONG	1	-	0136 01010005
18	อายนัท M 16 DIN 582 พร้อมกายทิมเบิล NUT,EYE,M 16 DIN 582, WITH THIMBLE GUY	1	1	0347 01180003
19	ท่อเหล็ก ขนาดระบุ 20 ประเภทที่ 2 ยาว 150 มม. มอก.277 แต่ไม่มีเกลียวที่ปลาย PIPE, STEEL, SIZE 20, TYPE 2, 150 mm LONG TIS.277 BUT WITHOUT THREADED END	3	3	0905 01050000

กองวิศวกรรมไฟฟ้าและเครื่องกล
ฝ่ายวิศวกรรม

การไฟฟ้าส่วนภูมิภาค

ผู้เขียน วิสุทธิ์ ชื่อเพราะ
ผู้สำรวจ ....
วิศวกร ....
หัวหน้าแผนก ....
ผู้อำนวยการกอง ....
ผู้อำนวยการฝ่าย ....

รองผู้ว่าการ
28 ต.ค. 2539

ผู้ว่าการ ....
28 ต.ค. 2539

115 kV วงจรเดียว สายไฟฟ้าเดี่ยว
โครงสร้างเสาเข้าปลายสายสองข้าง ก่อนเสาช่วงทางโค้ง
แบบ SS-AS-4

115 kV SINGLE-CIRCUIT SINGLE-CONDUCTOR
DOUBLE DEADEND STRUCTURE, ADJACENT POLE TO ANGLE
TYPE SS-AS-4

ใช้แทนแบบ ....
ถูกแทนโดยแบบ ....
เขียนเสร็จวันที่ 5 ก.ย. 2539
แก้แบบวันที่ ....
มิติเป็น ....
มาตราส่วน ....

แบบเลขที่ SA1-015/39013
แผ่นที่ 4 ของจำนวน 5 แผ่น

การประกอบเลขที่ ASSEMBLY NO.	5221

บัญชีวัสดุ
BILL OF MATERIAL

ลำดับที่ ITEM	รายละเอียด DESCRIPTION	จำนวน REQ'D I	จำนวน REQ'D II	การประกอบเลขที่ ASM.NO.
D-3C	การประกอบลูกถ้วยแขวน SUSPENSION INSULATOR ASSEMBLY	3	3	5603
D-4C	การประกอบลูกถ้วยแขวน SUSPENSION INSULATOR ASSEMBLY	3	3	5604
D-11C	การประกอบลูกถ้วยแขวน SUSPENSION INSULATOR ASSEMBLY	3	3	5605
D-5A	การต่อสายล่อฟ้า	1	–	5626
D-5E	OVERHEAD GROUND WIRE CONNECTION	–	1	
D-7A**	การประกอบสายยึดโยงลวดเหล็กตีเกลียว 95 ต.มม. STEEL STRANDED WIRE 95 sq.mm.,GUY ASSEMBLY	4	4	5638
D-10A*	ฐานรากเสา ตามแบบเลขที่ IB1-015/240024 (การประกอบเลขที่ 5667) POLE FOUNDATION ACCD. TO DWG. NO. IB1-015/240024 (ASSEMBLY NO.5667)	1	1	5661

* อาจเปลี่ยนแปลงเป็นแบบอื่น โดยขึ้นอยู่กับสภาพของดิน

IT MAY BE CHANGED TO THE OTHER TYPE WHICH DEPEND ON SOIL CONDITION

** ตัดรายการสลักห่วงแบบธรรมดา (วัสดุเลขที่ 0163) และแหวนสี่เหลี่ยมแบน (วัสดุเลขที่ 0355)

OMITTED, STRAND EYE BOLT (MAT NO.0163) AND SQUARE FLAT WASHER (MAT. NO.0355)

อดิวิทย์ ทองลา พชง.3 ผปร. กฟส.อล. กฟจ.[illegible] กฟต.[illegible] สายงาน[illegible] ผวก. @PEA

กองวิศวกรรมไฟฟ้าและเครื่องกล ฝ่ายวิศวกรรม	การไฟฟ้าส่วนภูมิภาค	ใช้แทนแบบ .... ถูกแทนโดยแบบ ....
ผู้เขียน ...วิสุทธิ์ ซื่อเพราะ... ผู้สำรวจ .... วิศวกร .... หัวหน้าแผนก .... ผู้อำนวยการกอง .... ผู้อำนวยการฝ่าย	ผู้ว่าการ .... 115 kV วงจรเดี่ยว สายไฟฟ้าเดี่ยว โครงสร้างเสาเข้าปลายสายสองข้าง ก่อนเสาช่วงทางโค้ง แบบ SS-AS-4	เขียนเสร็จวันที่ .5 ก.ย. 2539 แก้แบบวันที่ .... มิติเป็น .... มาตราส่วน ....
รองผู้ว่าการ	115 kV SINGLE-CIRCUIT SINGLE-CONDUCTOR DOUBLE DEADEND STRUCTURE, ADJACENT POLE TO ANGLE TYPE SS-AS-4	แบบเลขที่ SA1-015/39013 แผ่นที่.5.ของจำนวน.5.แผ่น