การประกอบเลขที่
ASSEMBLY NO. 0707

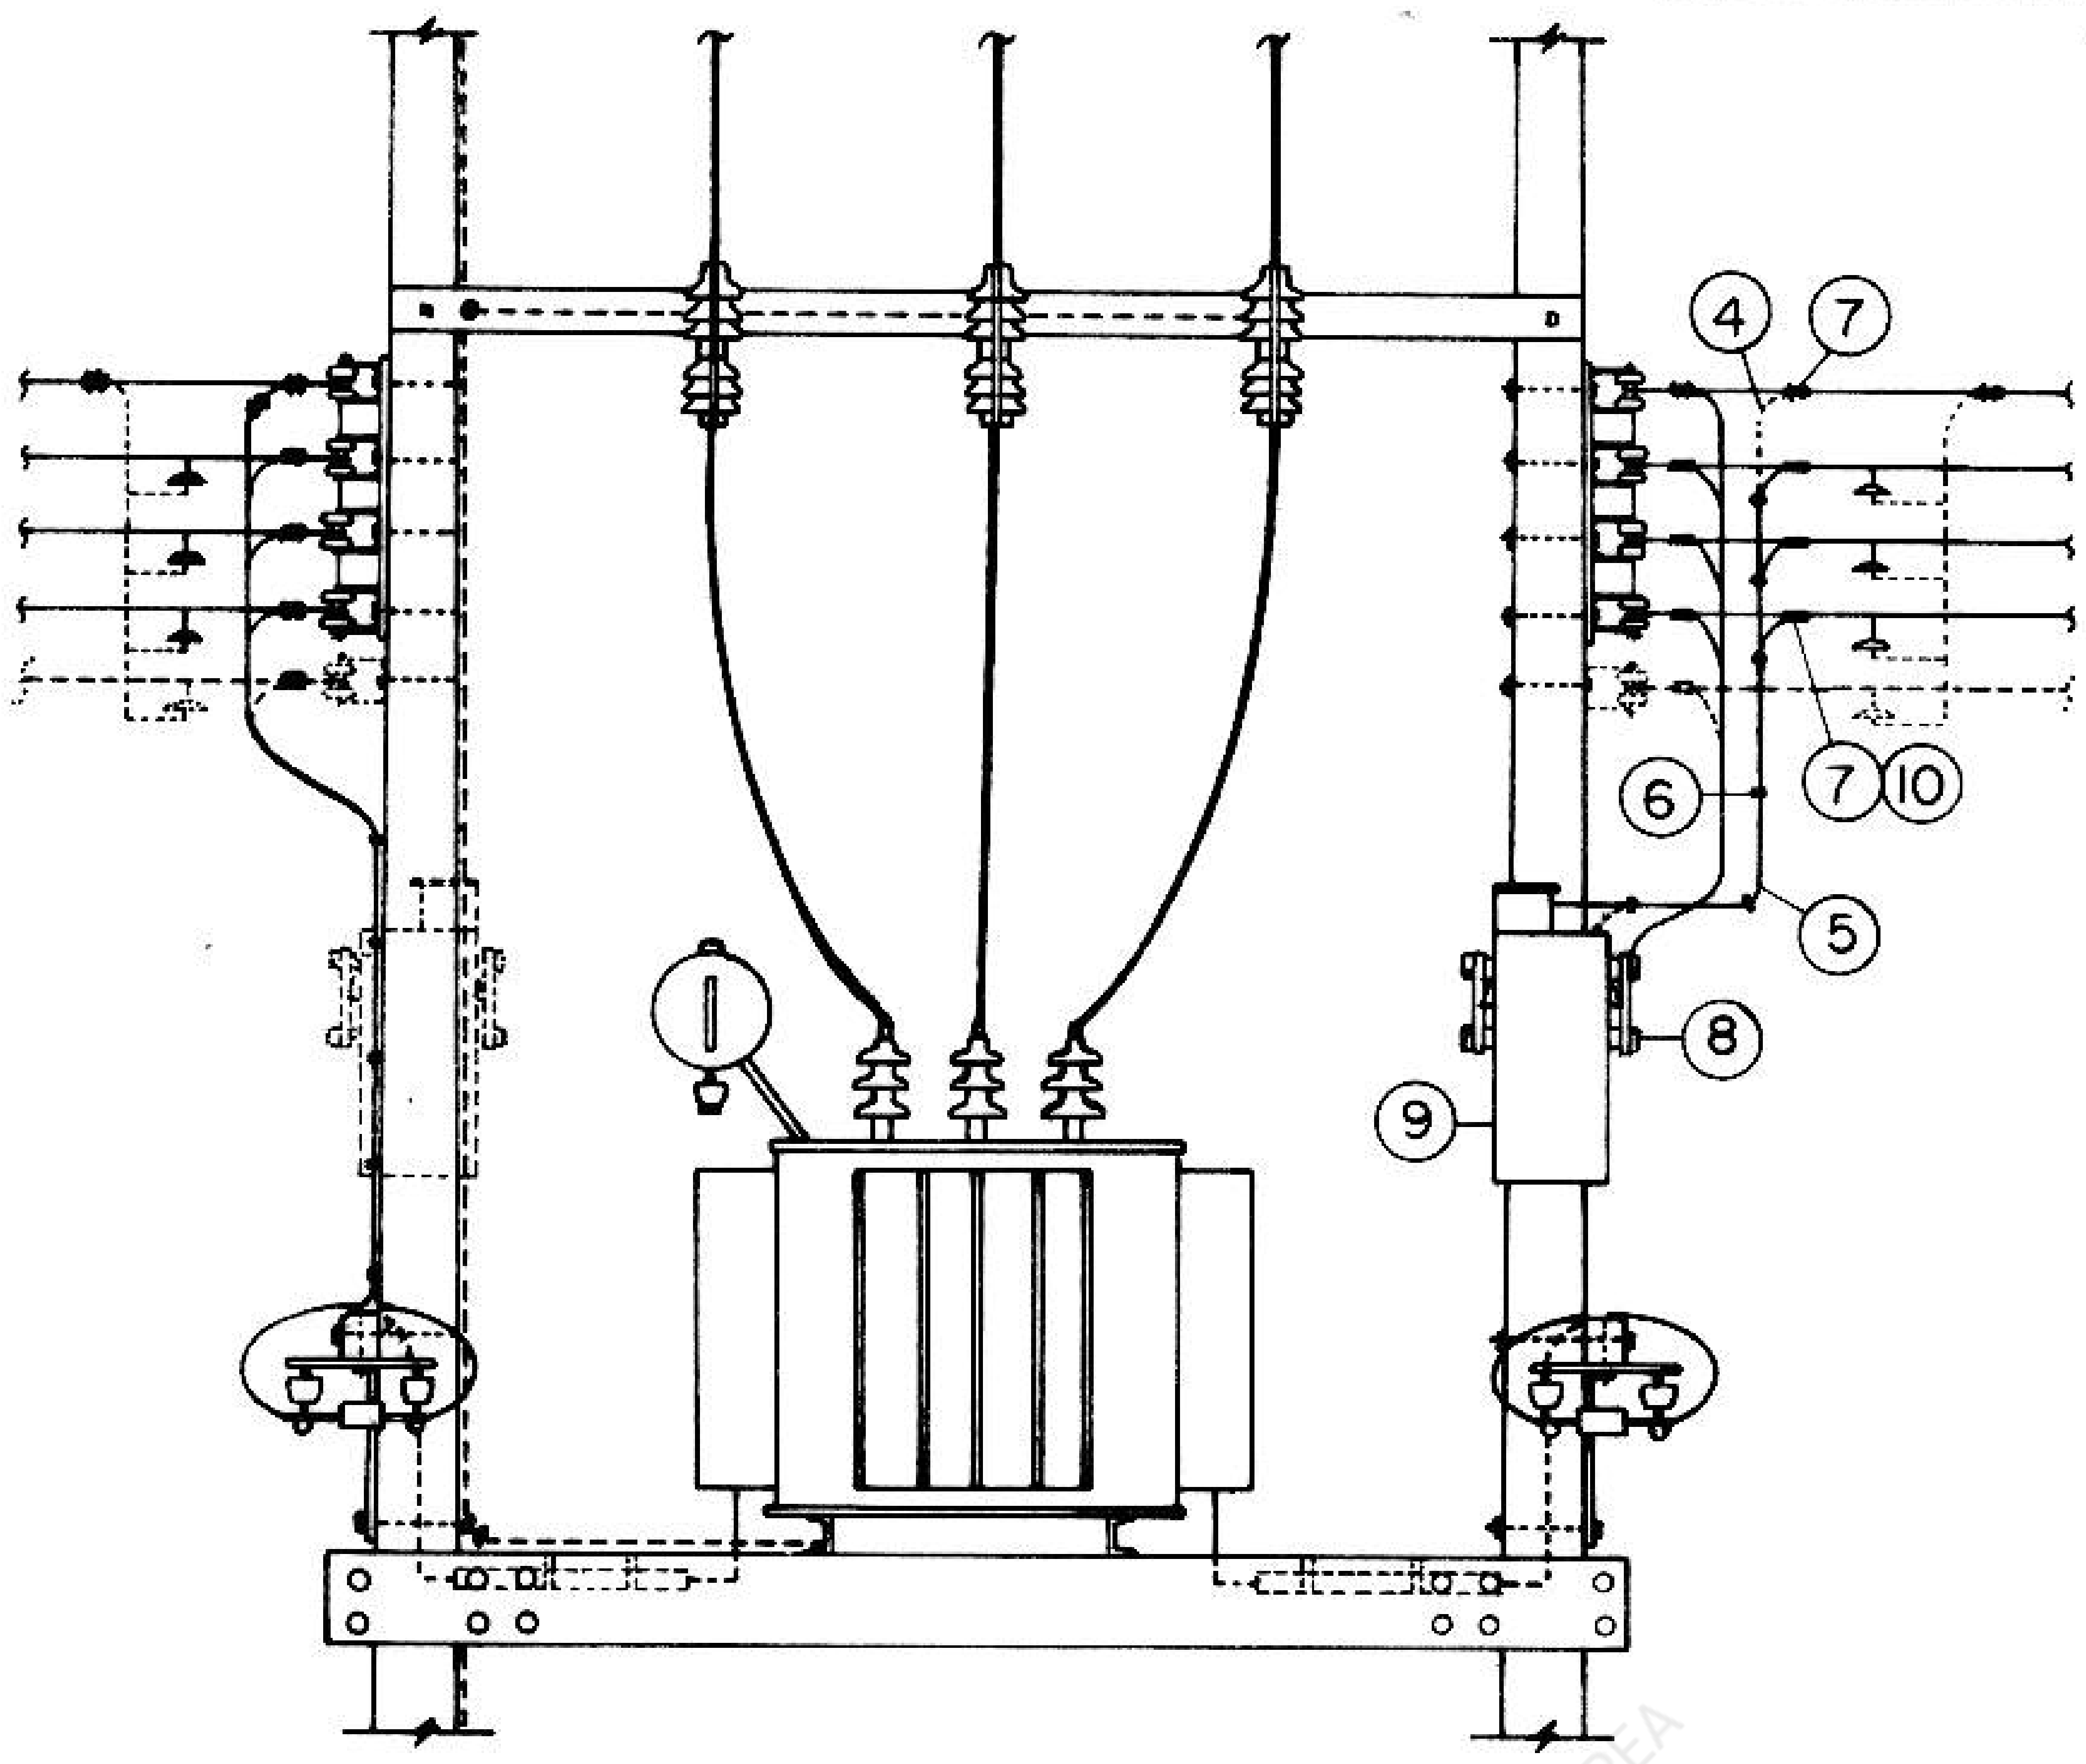

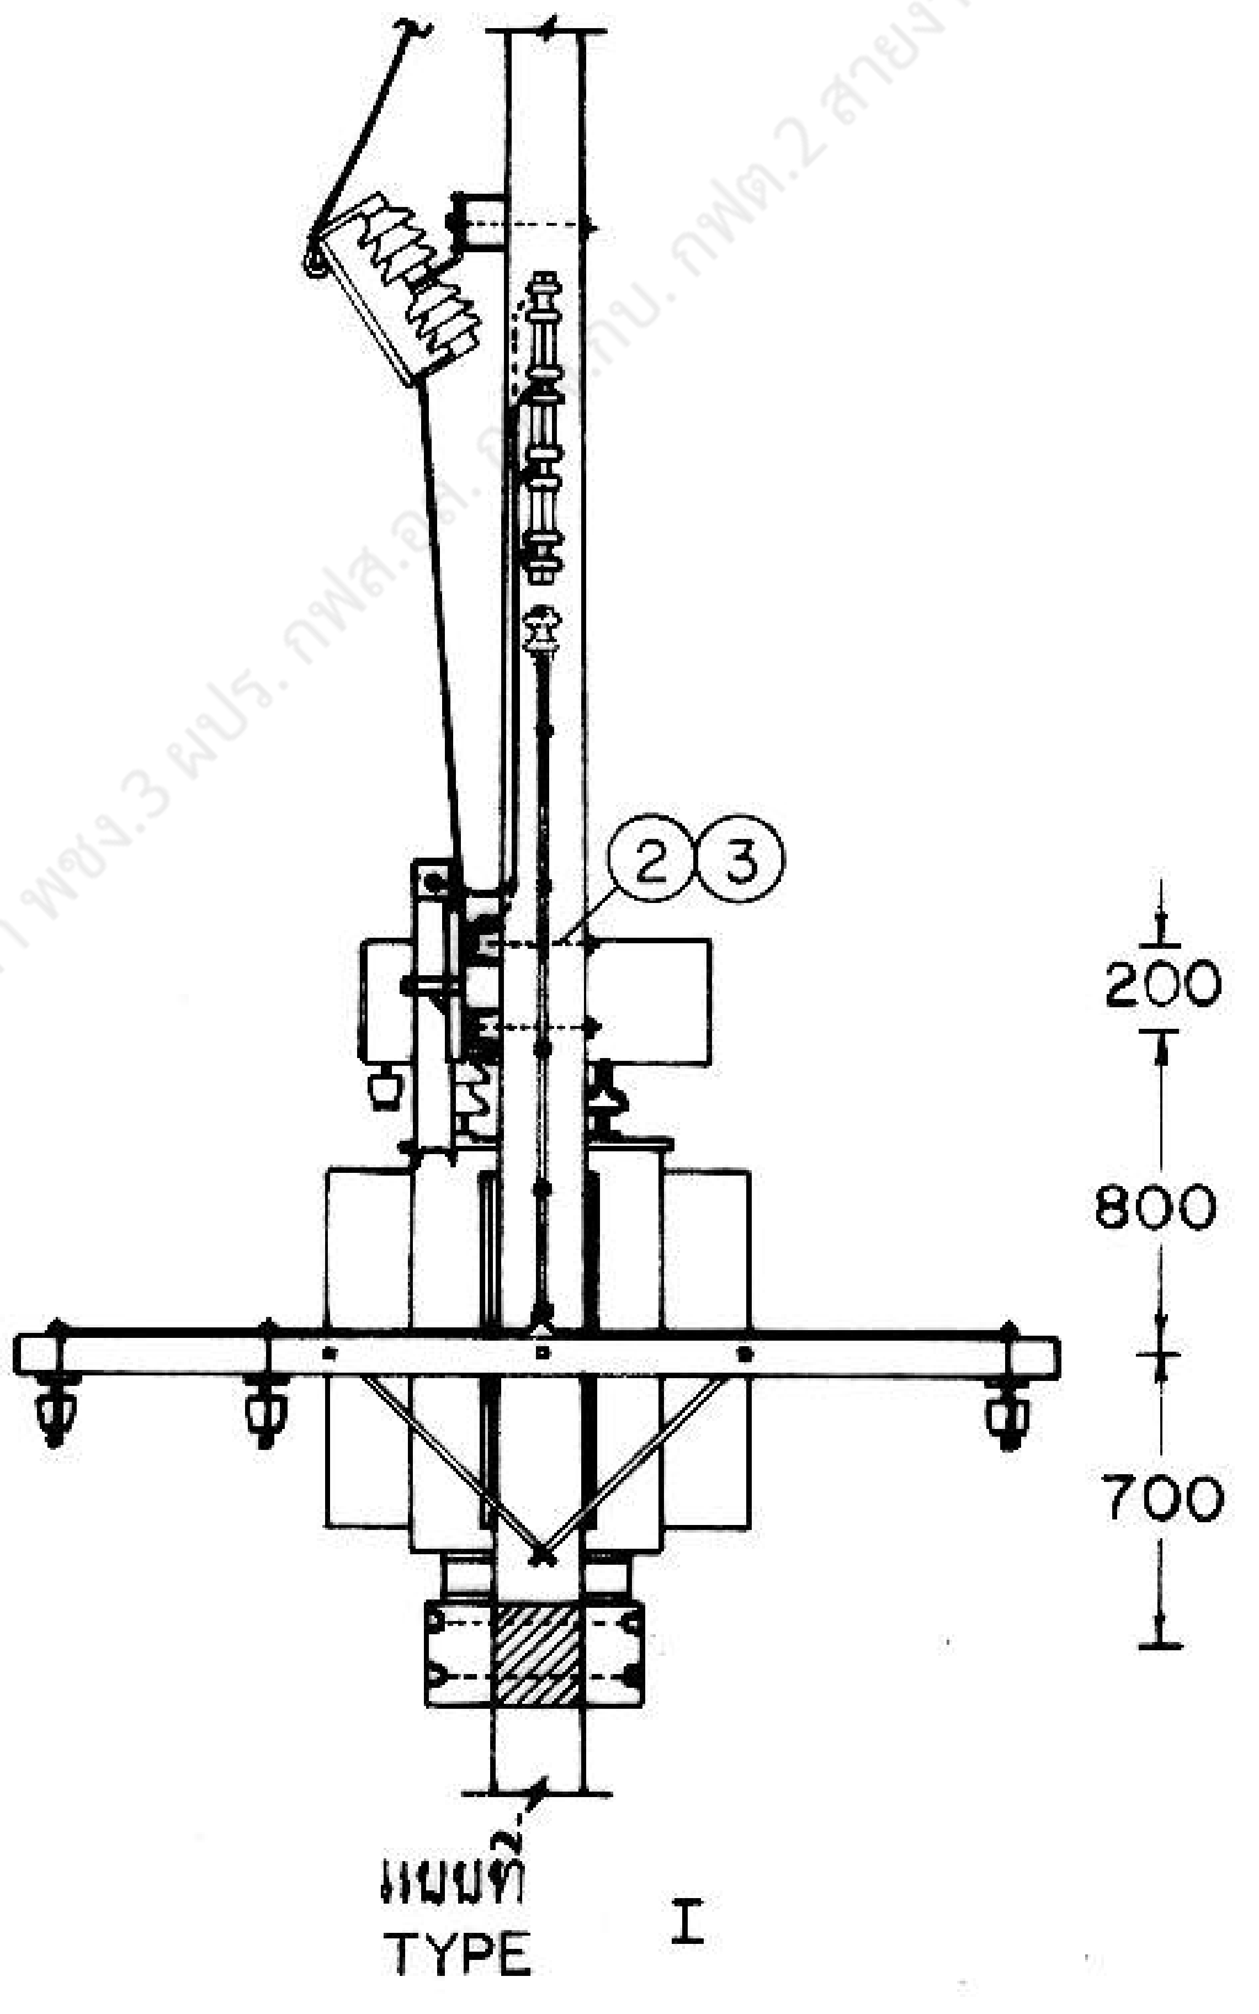

แบบที่
TYPE I

อดิวิทย์ ทองลา พชง.3 ผปร. กฟส.อ[illegible] กฟต.2 สายงาน (ต) ผวก. @PEA

กองวิศวกรรมไฟฟ้าและเครื่องกล
ฝ่ายวิศวกรรม

ผู้เขียน
ผู้สำรวจ
วิศวกร
หัวหน้าแผนก
หัวหน้ากอง
ผู้อำนวยการฝ่าย
รองผู้ว่าการฝ่ายเทคนิค

การไฟฟ้าส่วนภูมิภาค

ผู้ว่าการ

การติดตั้งคะแปซิเตอร์ 3 เฟส 400 โวลต์ ที่เสาต้นนั่งร้านหม้อแปลง

3-Ø 400 V CAPACITOR INSTALLATION AT TRANSFORMER STATION

ใช้แทนแบบ
ถูกแทนโดยแบบ
เขียนเสร็จวันที่ 30 พ.ย. 21
แก้แบบวันที่
มิติเป็น มม.
มาตราส่วน 1 : 50

แบบเลขที่ SA1-015/21077
แผ่นที่ 1 ของจำนวน 3 แผ่น

การประกอบเลขที่
ASSEMBLY NO. 0707

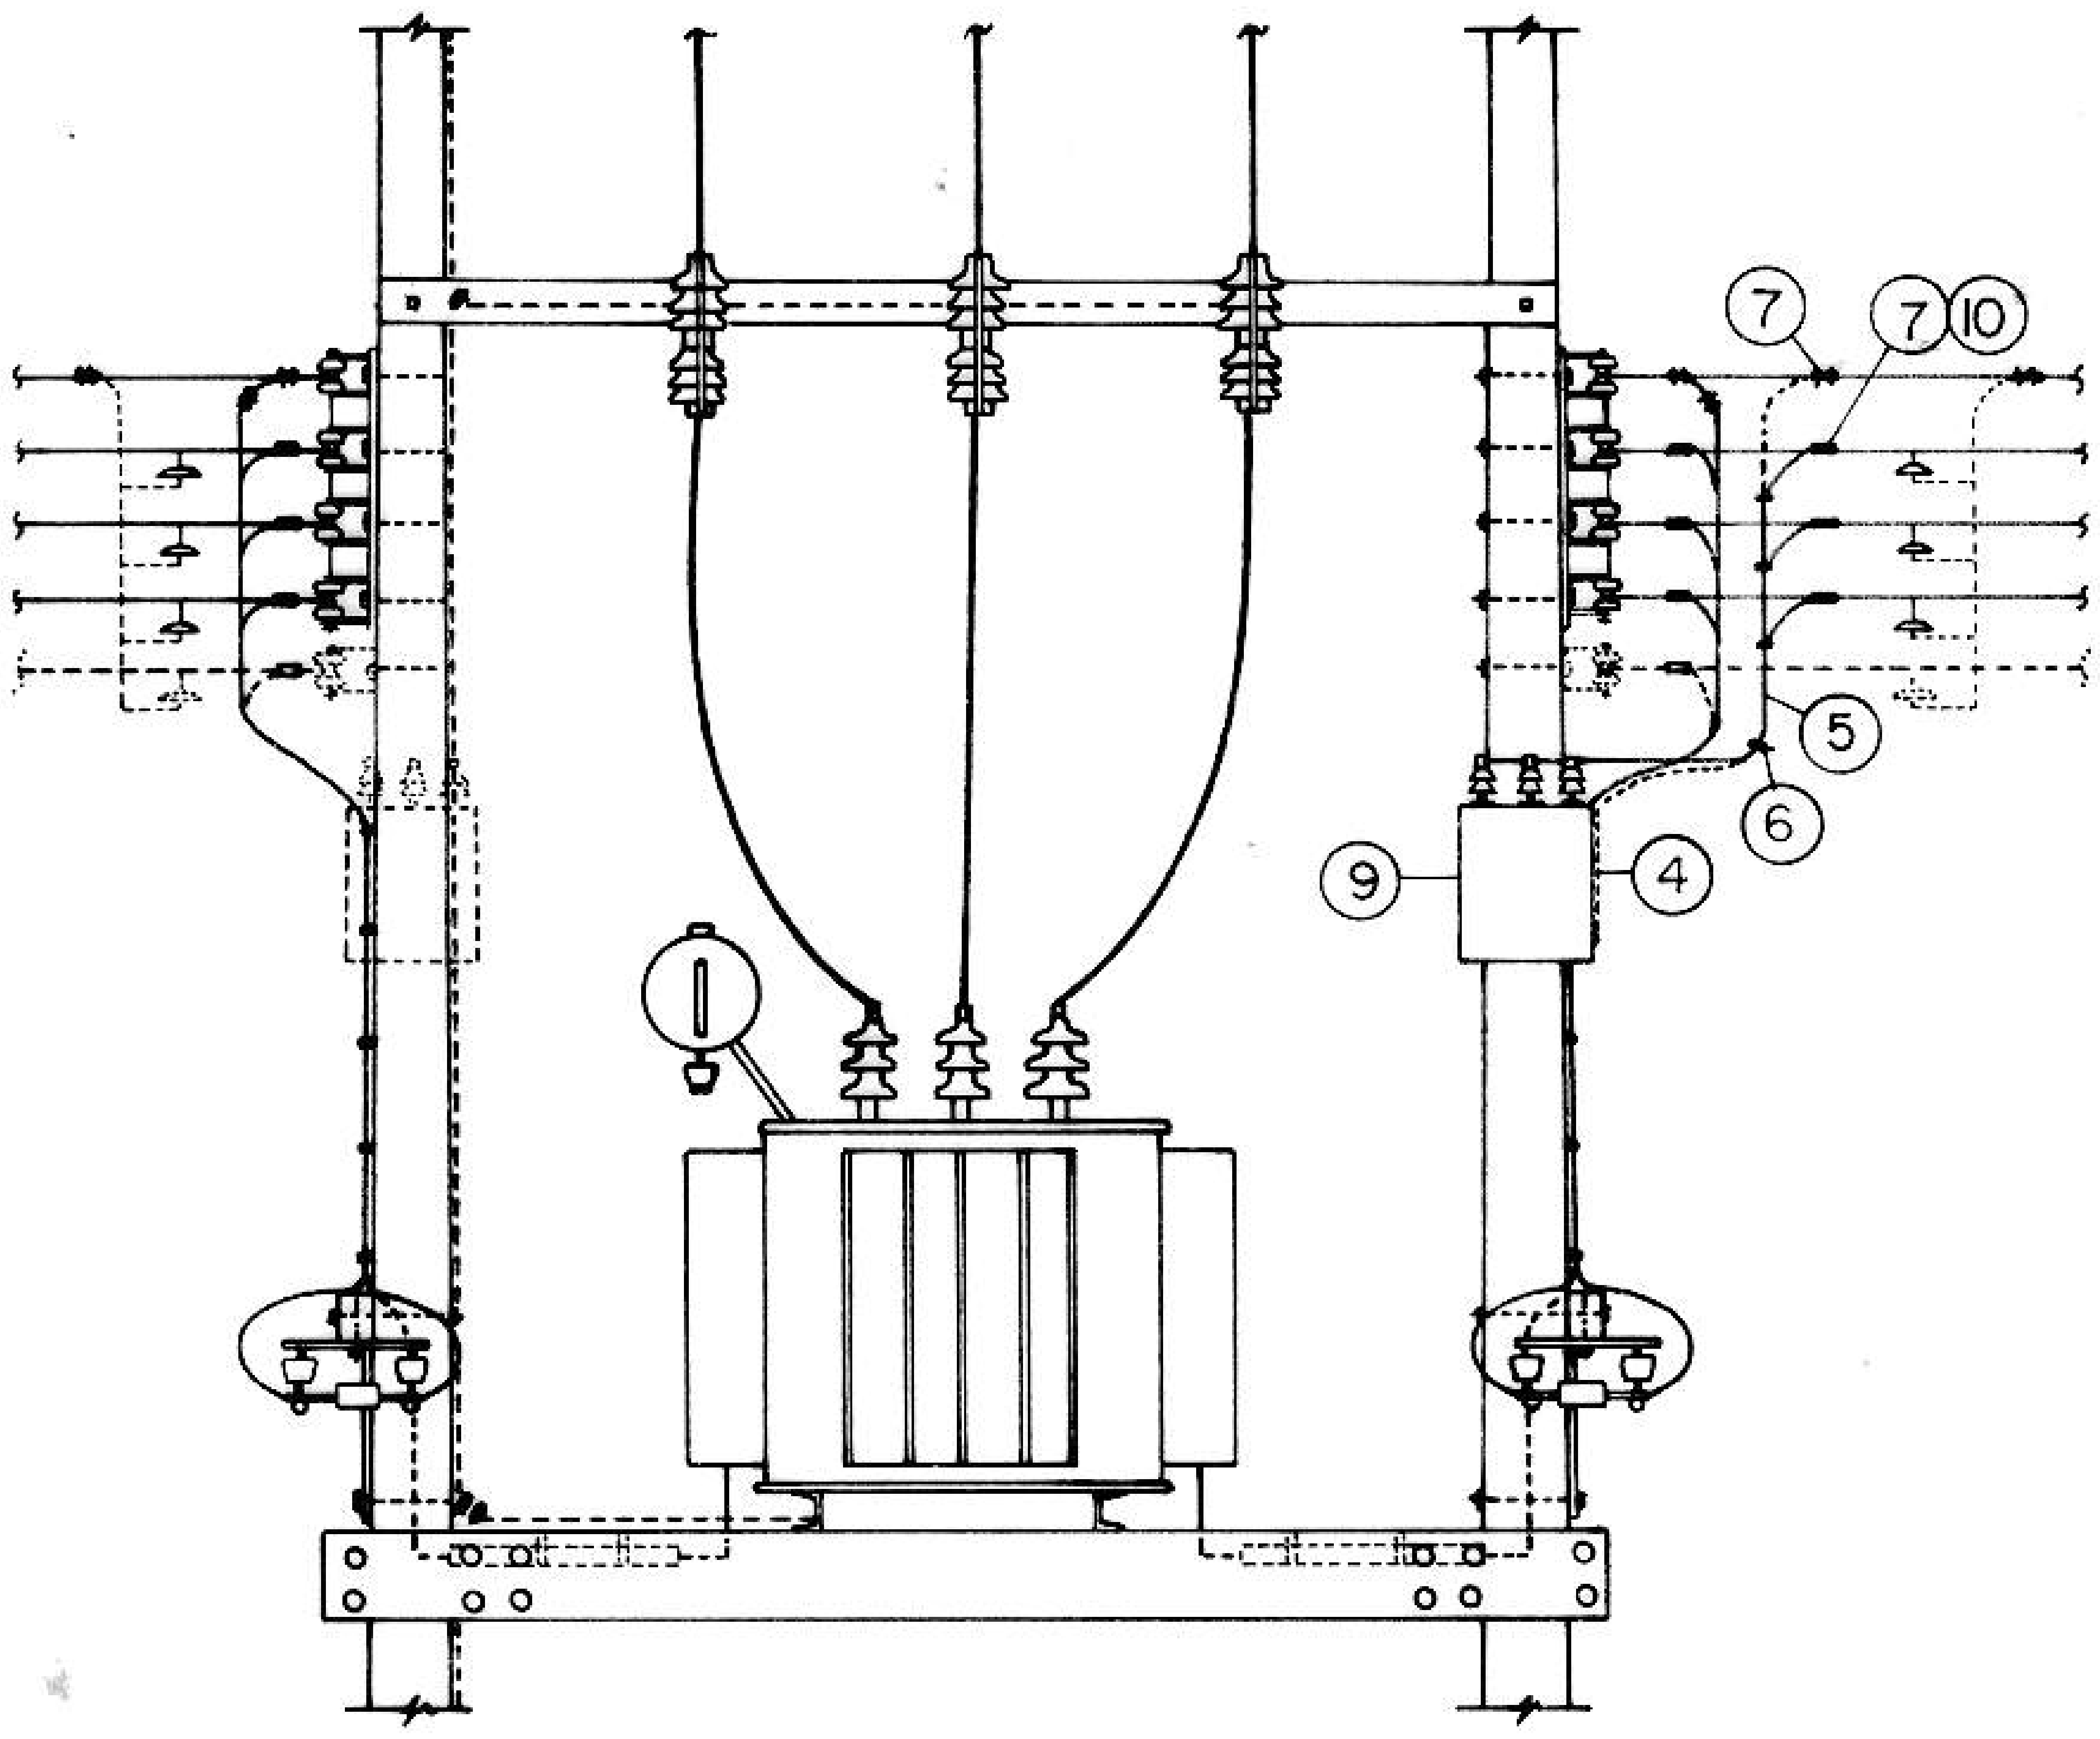

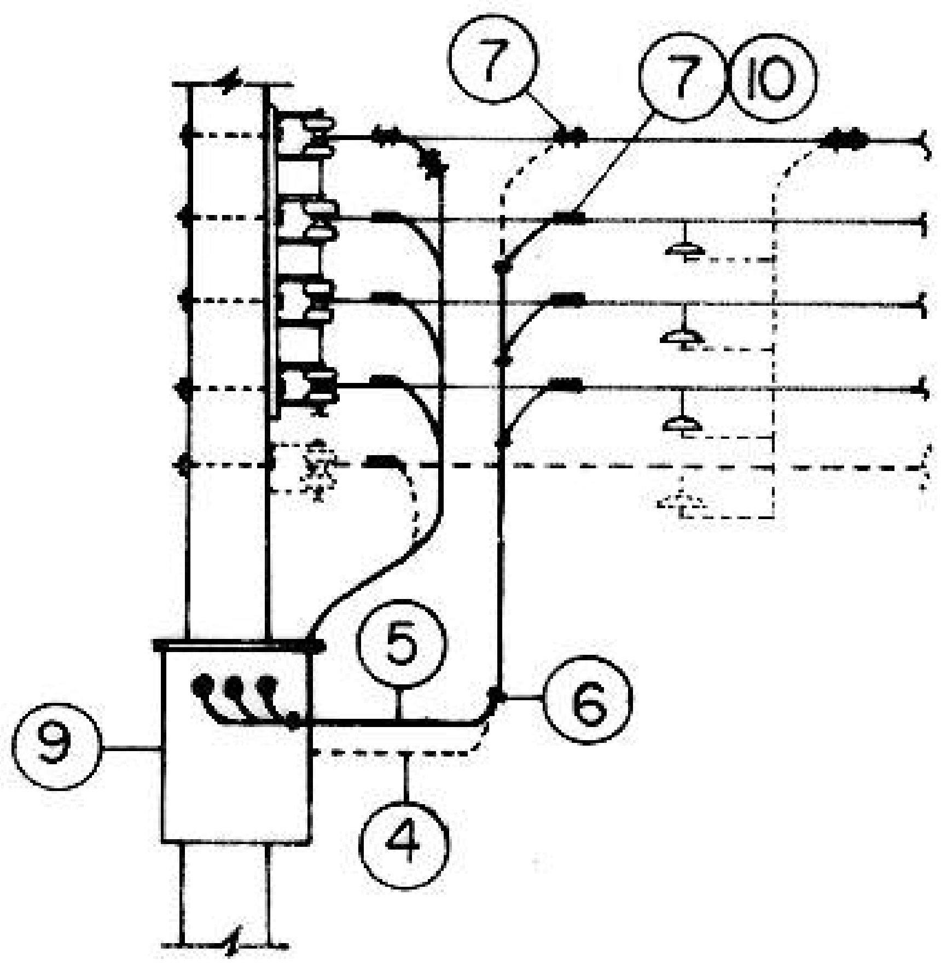

แบบเผื่อเลือก
ALTERNATIVE

กฟส.อล. กฟจ.กบ. กฟต.2 สายงาน (ต) ผวก. @PEA

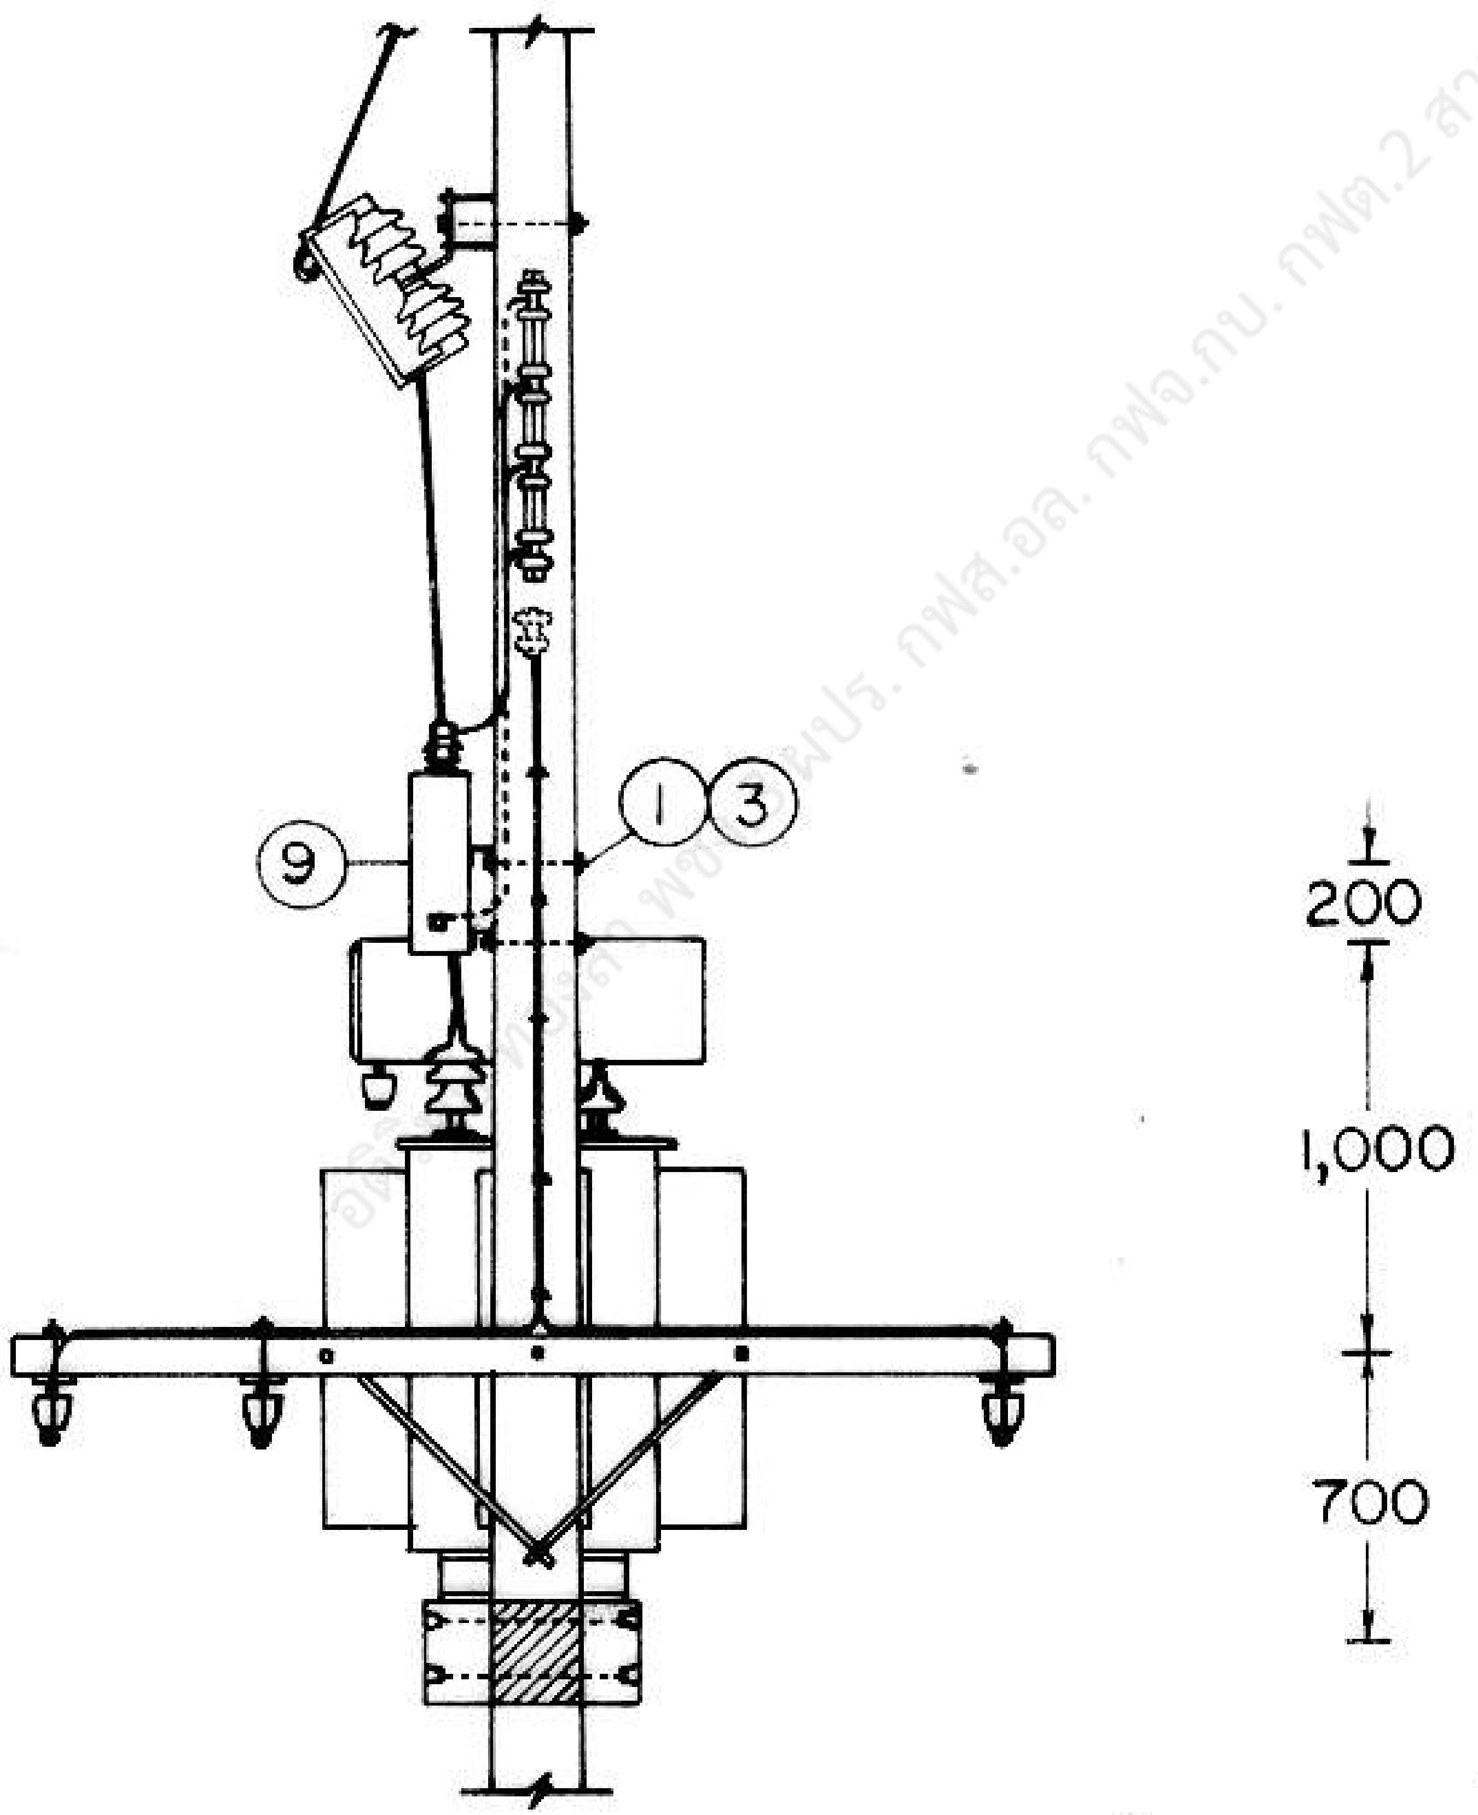

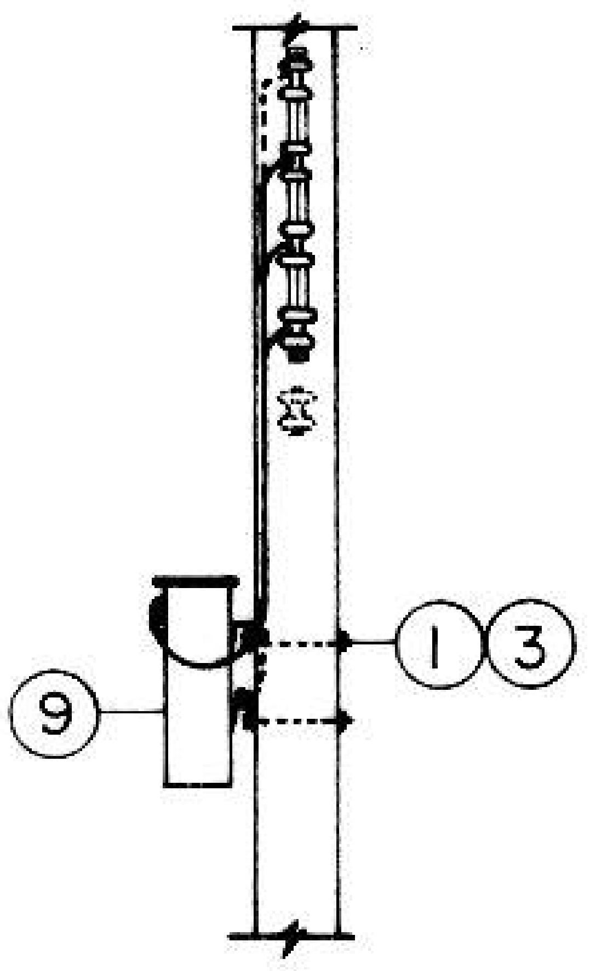

แบบเผื่อเลือก
ALTERNATIVE

แบบที่ II
TYPE II

กองวิศวกรรมไฟฟ้าและเครื่องกล
ฝ่ายวิศวกรรม

การไฟฟ้าส่วนภูมิภาค

ผู้ว่าการ ๒๐ ธ.ค. ๒๑

ผู้เขียน
ผู้สำรวจ
วิศวกร สิทธิพงษ์
หัวหน้าแผนก
หัวหน้ากอง
ผู้อำนวยการฝ่าย

รองผู้ว่าการฝ่ายเทคนิค

การติดตั้งคะแปซิเตอร์ 3 เฟส 400 โวลต์ ที่เสาต้นนั่งร้านหม้อแปลง

3-Ø 400 V CAPACITOR INSTALLATION AT TRANSFORMER STATION

ใช้แทนแบบ
ถูกแทนโดยแบบ
เขียนเสร็จวันที่ 30 พ.ย. 21
แก้แบบวันที่
พิมพ์เป็น ผม.
มาตราส่วน 1 : 50

แบบเลขที่ SA1-015/21077
แผ่นที่ 2 ของจำนวน 3 แผ่น

การประกอบเลขที่
ASSEMBLY NO. 0707

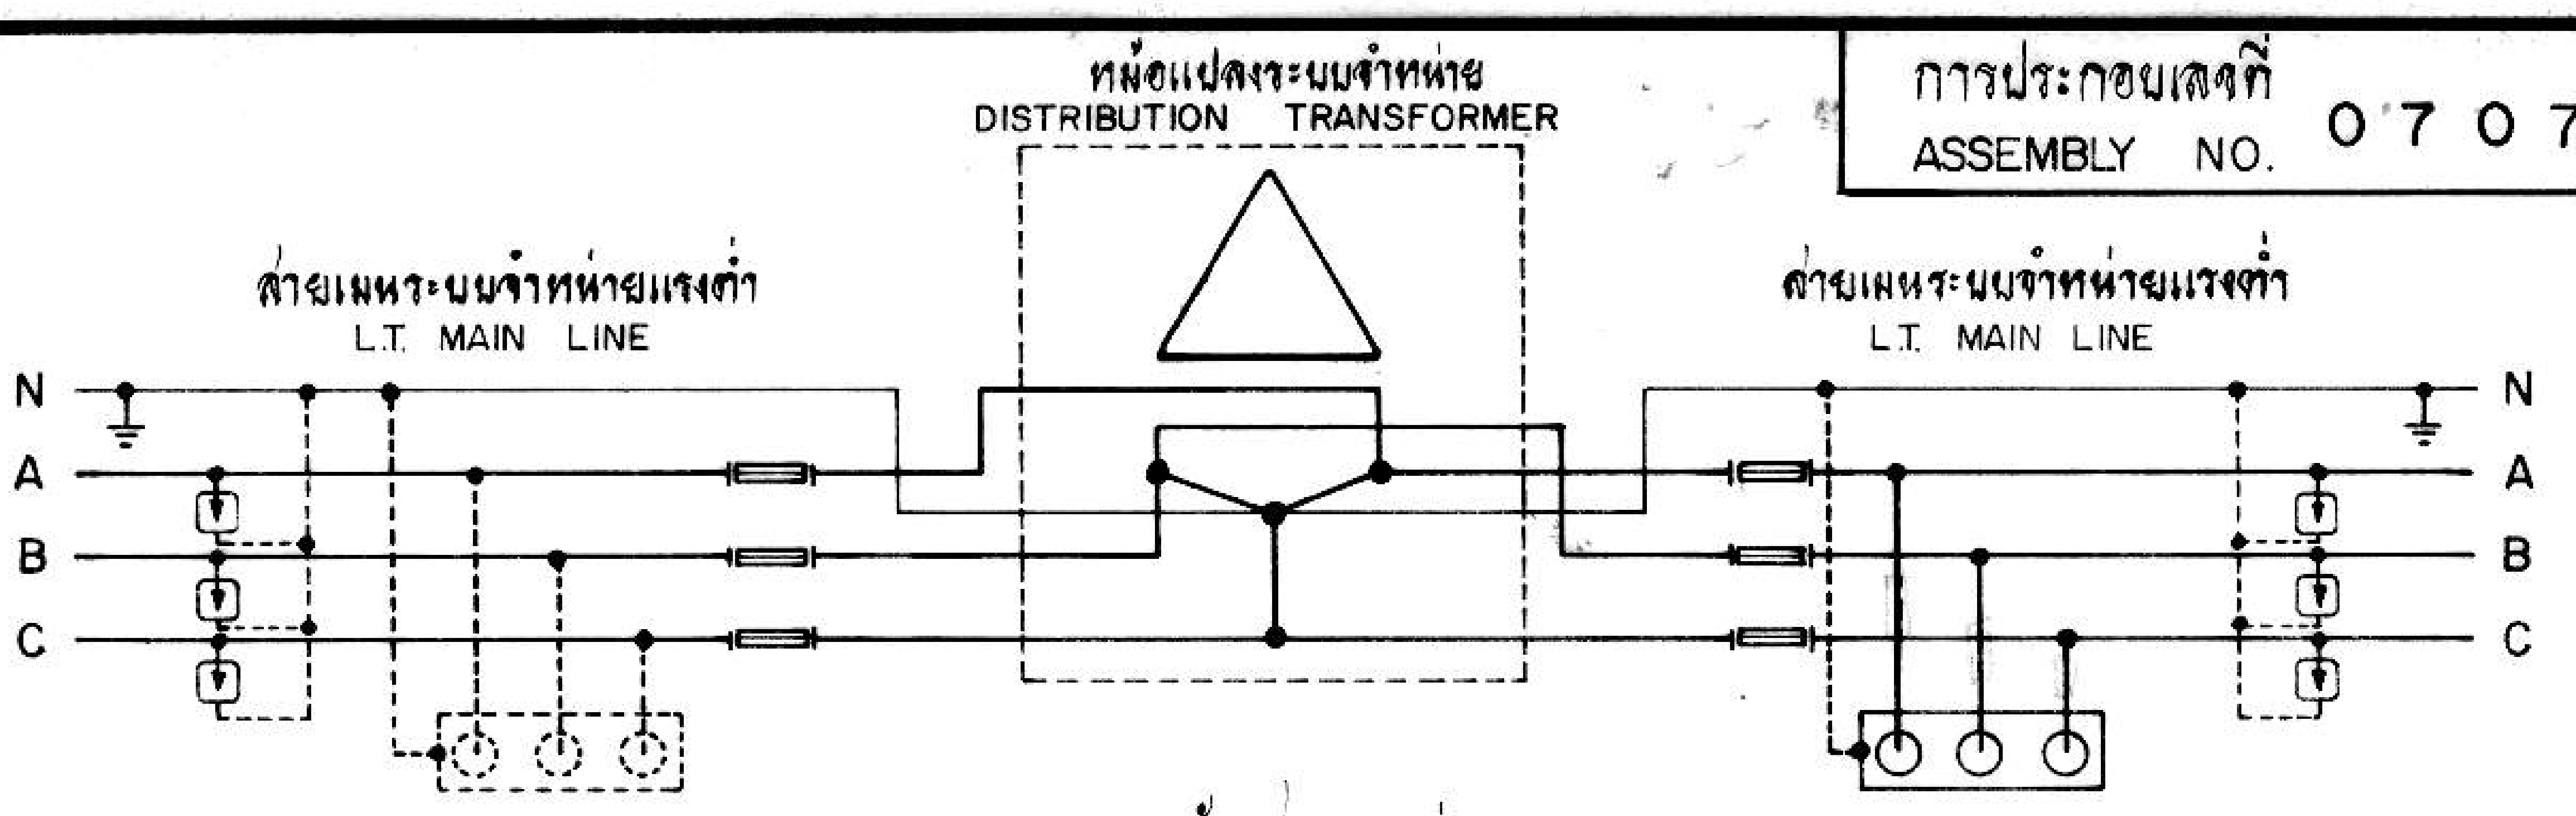

แผนผังแสดงการต่อ
CONNECTION DIAGRAM

บัญชีวัสดุ
BILL OF MATERIAL

ลำดับที่ ITEM	รายละเอียด DESCRIPTION	จำนวน REQ'D		วัสดุเลขที่ MAT. NO.
		I	II	
1	สลักเกลียว M 16 X 250 มม. BOLT, MACHINE, M 16 X 250 mm	–	2	01110203
2	สลักเกลียว M 16 X 300 มม. BOLT, MACHINE, M 16 X 300 mm	2	–	01110204
3	แหวนสี่เหลี่ยมแบน 52 X 52 X 4.5 มม. รู Ø 18 มม. มอก. 258 WASHER, SQUARE, FLAT, 52 X 52 X 4.5 mm, HOLE Ø 18 mm, TIS 258	4	6	01180100
4	ลวดเหล็กตีเกลียว 50/7 ต.มม. มอก. 404 WIRE, STEEL STRANDED, 50/7 mm², TIS 404	2 ม./m	2.5 ม./m	01100004
5	สายอะลูมิเนียมหุ้มฉนวน PVC 25-70 ต.มม. มอก. 293 CABLE, Al STRANDED, PVC-INSULATED, 25-70 mm², TIS 293	5 ม./m	5 ม./m	02070000-3
6	ลวดอะลูมิเนียมแบน ขนาด 1 X 10 มม. ความยาวตามต้องการ TAPE, ARMOUR, Al, 1 X 10 mm, LENGTH AS REQUIRED			02200000
7	คอนเนคเตอร์ ชนิดบีบ แบบ H สำหรับสายอะลูมิเนียมขนาดตามต้องการ CONNECTOR, COMPRESSION, H-TYPE, FOR Al CONDUCTOR, SIZE AS REQUIRED	4	4	02320003 02320002
8	ที่แขวนคะแปซิเตอร์แรงต่ำ แบบเลขที่ SA1-015/21003 L.T. CAPACITOR HANGER DWG. NO. SA1-015/21003	1	–	—
9	คะแปซิเตอร์ 3 เฟส ใช้นอกอาคาร 400 โวลต์ 5-75 กิโลวาร์ CAPACITOR, POWER, THREE-PHASE, OUTDOOR 400 V, 5-75 kvar	1	1	05040200-5
10	PVC เทป กว้าง 19 มม. (ใช้ความยาว 2 ม. ต่อ จุด) มอก. 386 PVC TAPE, 19 mm WIDE (2 m LONG PER POINT) TIS 386	6 ม./m	6 ม./m	02180001 or 02180002

หมายเหตุ
1. บัญชีวัสดุใช้สำหรับการติดตั้งคะแปซิเตอร์ 3 เฟส 400 โวลต์ เท่านั้น
2. แบบที่ I ใช้สำหรับคะแปซิเตอร์รุ่นเก่า ต้องใช้ที่แขวนคะแปซิเตอร์เพื่อประกอบยึดกับเสา
แบบที่ II ใช้สำหรับคะแปซิเตอร์ที่จัดซื้อรุ่นใหม่ ซึ่งมีห่วงแขวนยึดกับเสาแล้ว

NOTES
1. BILL OF MATERIAL USED FOR 3-Ø 400 V CAPACITOR INSTALLATION ONLY.
2. TYPE I FOR PREVIOUS PURCHASING, THE CAPACITOR MUST BE USED WITH MOUNTING HANGER.
TYPE II FOR NEW PURCHASING, THE CAPACITOR SHALL BE COMPLETED WITH MOUNTING LUGS.

กองวิศวกรรมไฟฟ้าและเครื่องกล
ฝ่ายวิศวกรรม

ผู้เขียน
ผู้สำรวจ
วิศวกร
หัวหน้าแผนก
หัวหน้ากอง
ผู้อำนวยการฝ่าย
รองผู้ว่าการฝ่ายเทคนิค

การไฟฟ้าส่วนภูมิภาค

ผู้ว่าการ

การติดตั้งคะแปซิเตอร์ 3 เฟส 400 โวลต์
ที่เสาต้นนั่งร้านหม้อแปลง

3-Ø 400 V CAPACITOR INSTALLATION
AT TRANSFORMER STATION

ใช้แทนแบบ
ถูกแทนโดยแบบ
เขียนเสร็จวันที่ 30 พ.ย. 21
แก้แบบวันที่ 1 ก.พ. 31
มิติเป็น
มาตราส่วน
แบบเลขที่ SA1-015/21077
แผ่นที่ 3 ของจำนวน 3 แผ่น