การประกอบเลขที่ 2509
ASSEMBLY NO. 3512

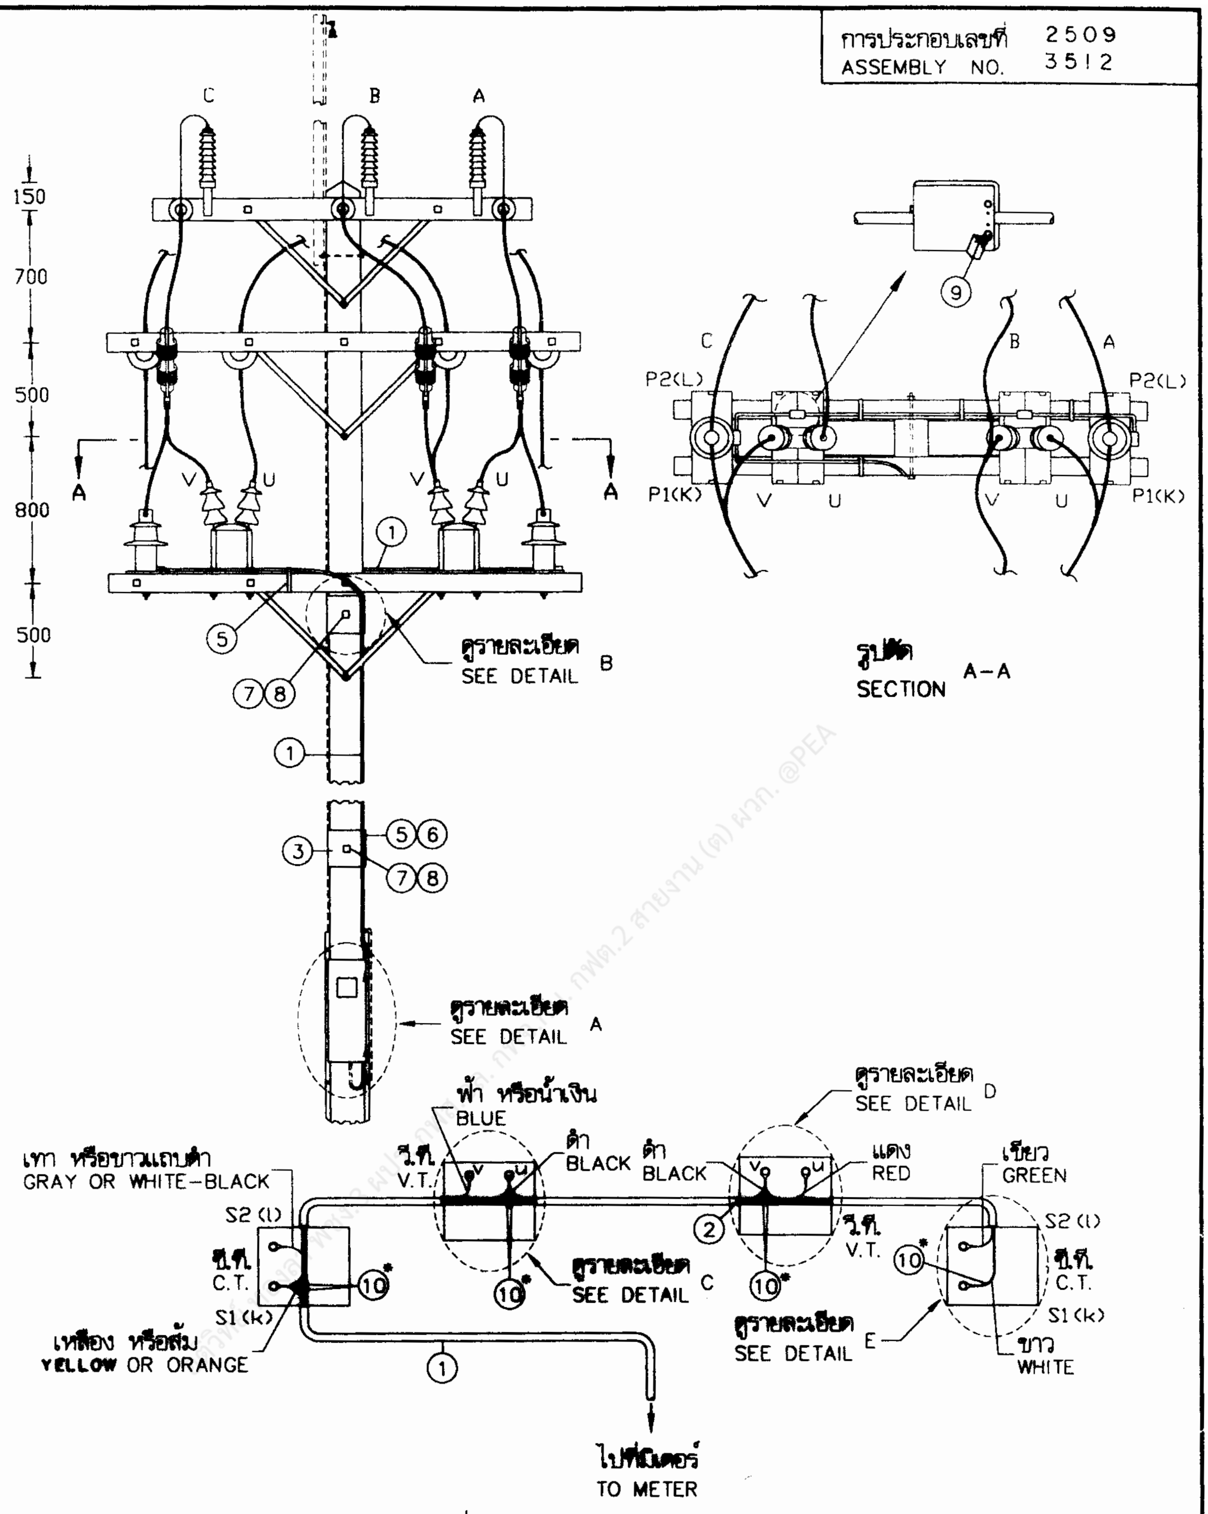

แผนผังการต่อสายควบคุมกับ วี.ที. และ ซี.ที.
CONNECTION DIAGRAM OF CONTROL CABLE WITH V.T. AND C.T.

I สำหรับเสาต้นคอนทางตรง
FOR CROSS ARM ASSEMBLY

COPY

กองมาตรฐานระบบไฟฟ้า
ฝ่ายมาตรฐานและความปลอดภัย

การไฟฟ้าส่วนภูมิภาค

ใช้แทนแบบ ....
ถูกแทนโดยแบบ ....

ผู้เขียน พนูศักดิ์ ศิริสมบูรณ์
ผู้สำรวจ ....
วิศวกร
หัวหน้าแผนก
ผู้อำนวยการกอง
ผู้อำนวยการฝ่าย

ผู้ว่าการ .... ~~4 ก.ย. 2550~~

เขียนเสร็จวันที่ 18 มิ.ย. 2550
แก้แบบวันที่ ....
มิติเป็น มิลลิเมตร
มาตราส่วน 1 : 40

การเดินสายควบคุมในท่อร้อยสาย
สำหรับการติดตั้งมิเตอร์ประกอบ วี.ที. และ ซี.ที. แรงสูง

WIRING OF CONTROL CABLE IN CONDUIT
FOR METER INSTALLATION WITH H.V., V.T. AND C.T.

รองผู้ว่าการวางแผนและพัฒนาระบบไฟฟ้า

แบบเลขที่ SA2-015/50009
แผ่นที่ 1 ของจำนวน 5 แผ่น

การประกอบเลขที่ 2509
ASSEMBLY NO. 3512

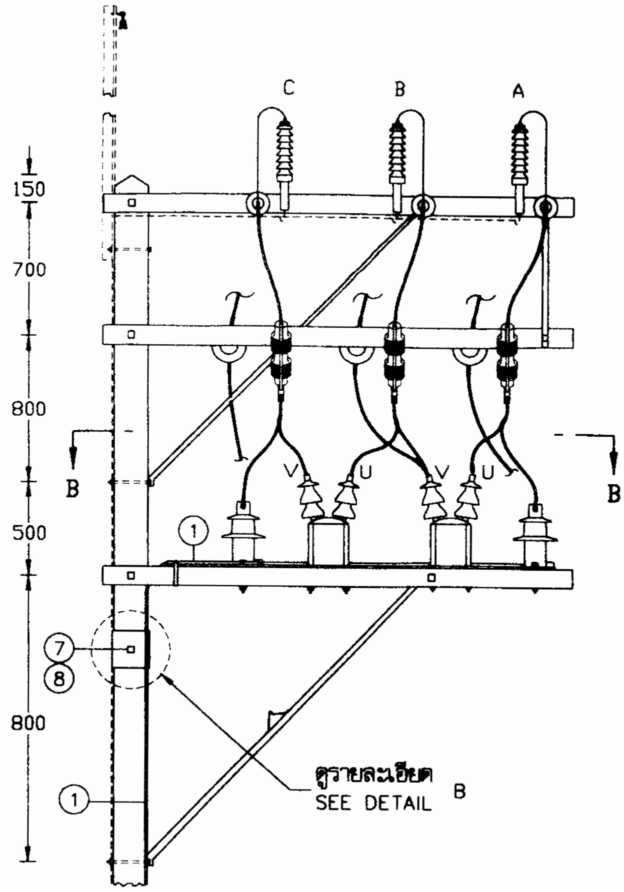

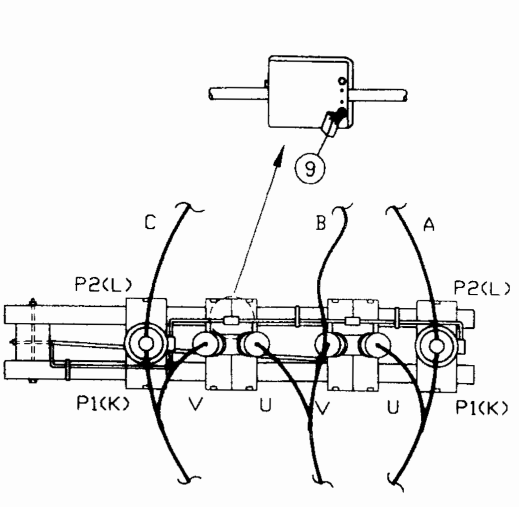

รูปตัด
SECTION B-B

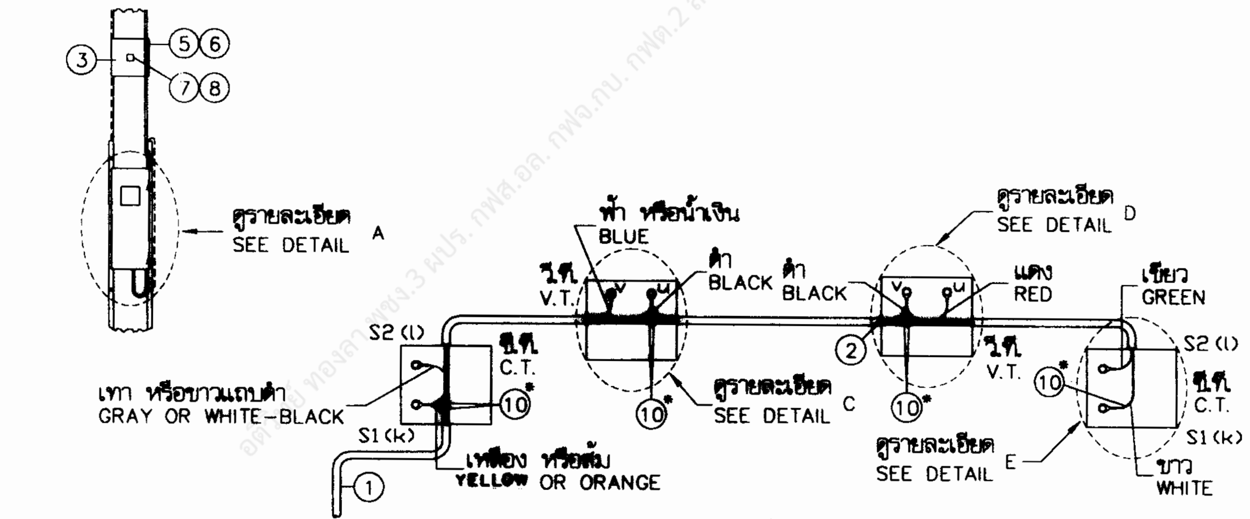

แผนผังการต่อสายควบคุมกับ วี.ที. และ ซี.ที.
CONNECTION DIAGRAM OF CONTROL CABLE WITH V.T. AND C.T.

II **สำหรับเสาต้นตอนข้ามแขน**
FOR ALLEY ARM ASSEMBLY

COPY

อดิศักดิ์ ทองลาภ พชง.3 ผปร. กฟส.อล. กฟจ.กบ. กฟต.2 สายงาน (ต) ผวก. @PEA

กองมาตรฐานระบบไฟฟ้า ฝ่ายมาตรฐานและความปลอดภัย	การไฟฟ้าส่วนภูมิภาค	ใช้แทนแบบ ...... ถูกแทนโดยแบบ ......
ผู้เขียน พนุศักดิ์ ศิริสมบูรณ์ ผู้สำรวจ ...... วิศวกร หัวหน้าแผนก ผู้อำนวยการกอง ผู้อำนวยการฝ่าย	ผู้ว่าการ ...... (ท) 1 4 ก.ค. 2550 การเดินสายควบคุมในท่อร้อยสาย สำหรับการติดตั้งมิเตอร์ประกอบ วี.ที. และ ซี.ที. แรงสูง	เขียนเสร็จวันที่ 18 มิ.ย. 2550 แก้แบบวันที่ ...... มิติเป็น มิลลิเมตร มาตราส่วน 1 : 40
รองผู้ว่าการวางแผนและพัฒนาระบบไฟฟ้า ...... (ท)	WIRING OF CONTROL CABLE IN CONDUIT FOR METER INSTALLATION WITH H.V., V.T. AND C.T.	แบบเลขที่ SA2-015/50009 แผ่นที่ 2 ของจำนวน 5 แผ่น

2550

การประกอบเลขที่	2509
ASSEMBLY NO.	3512

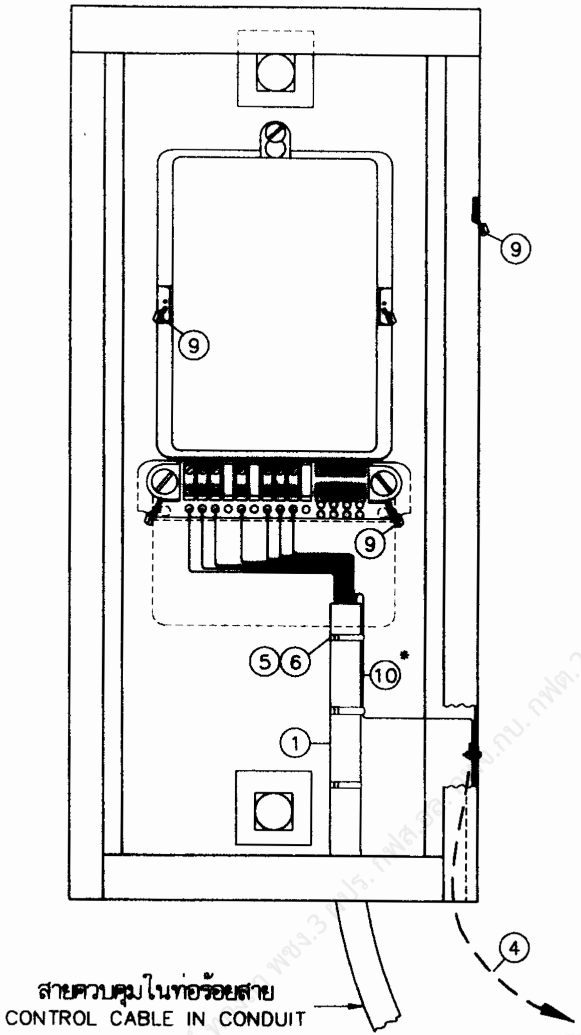

⑨
⑨
⑨
⑤⑥
⑩*
①
④
สายควบคุมในท่อร้อยสาย
CONTROL CABLE IN CONDUIT
ไปต่อลงดินระบบจำหน่ายแรงต่ำ
TO GROUNDING SYSTEM OF L.V. SYSTEM

รายละเอียด A
DETAIL

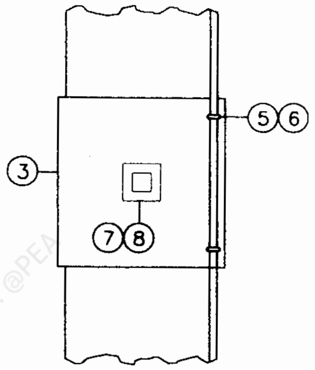

รายละเอียด B
DETAIL

พชง.3 ... กฟต.2 สายงาน (ต) ผวก. @PEA

COPY

กองมาตรฐานระบบไฟฟ้า
ฝ่ายมาตรฐานและความปลอดภัย

การไฟฟ้าส่วนภูมิภาค

ผู้เขียน พงษ์ศักดิ์ ศิริสมบูรณ์
ผู้สำรวจ
วิศวกร
หัวหน้าแผนก
ผู้อำนวยการกอง
ผู้อำนวยการฝ่าย

ผู้ว่าการ (ท)

การเดินสายควบคุมในท่อร้อยสาย
สำหรับการติดตั้งมิเตอร์ประกอบ วี.ที. และ ซี.ที. แรงสูง

รองผู้ว่าการวางแผนและพัฒนาระบบไฟฟ้า
(ท)
2550

WIRING OF CONTROL CABLE IN CONDUIT
FOR METER INSTALLATION WITH H.V., V.T. AND C.T.

ใช้แทนแบบ
ถูกแทนโดยแบบ
เขียนเสร็จวันที่ 18 มิ.ย. 2550
แก้แบบวันที่
มิติเป็น
มาตราส่วน

แบบเลขที่ SA2-015/50009
แผ่นที่ 3 ของจำนวน 5 แผ่น

การประกอบเลขที่ 2509
ASSEMBLY NO. 3512

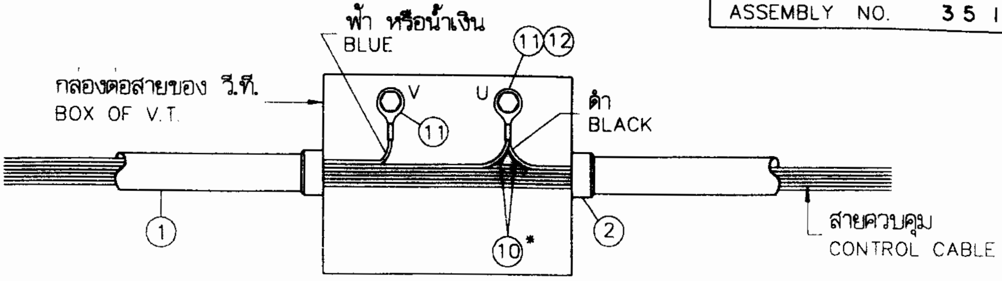

รายละเอียด
DETAIL C

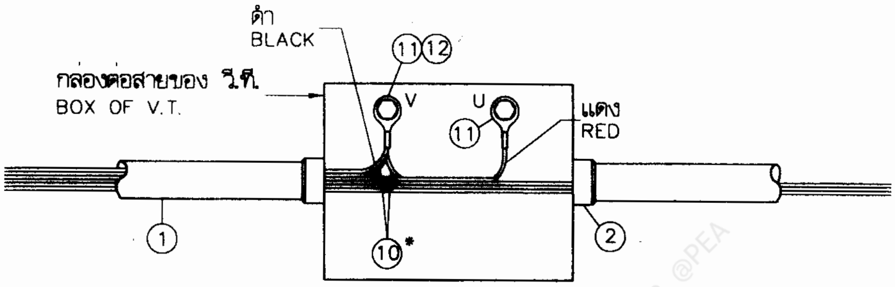

รายละเอียด
DETAIL D

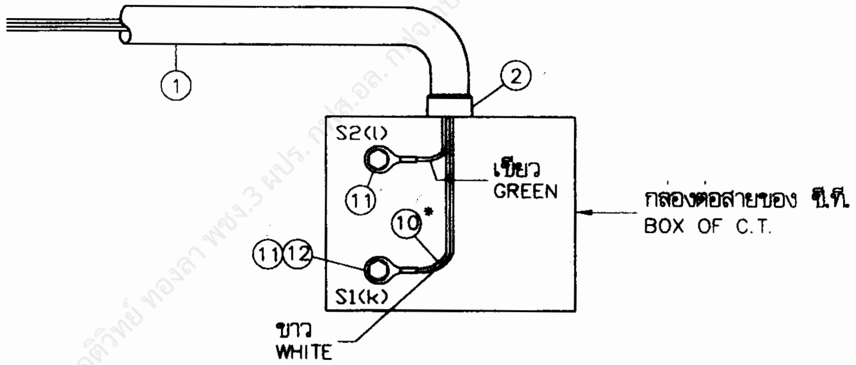

รายละเอียด
DETAIL E

อดิวิทย์ ทองลา พชง.3 ผปร. กปส.อล. กฟจ.ภบ. กฟต.2 สายงาน (ต) ผวก. @PEA

COPY

กองมาตรฐานระบบไฟฟ้า
ฝ่ายมาตรฐานและความปลอดภัย

การไฟฟ้าส่วนภูมิภาค

ใช้แทนแบบ ....
ถูกแทนโดยแบบ ....

ผู้เขียน พงษ์ศักดิ์ ศิริสมบูรณ์
ผู้สำรวจ ....
วิศวกร
หัวหน้าแผนก
ผู้อำนวยการกอง
ผู้อำนวยการฝ่าย

ผู้ว่าการ (ท)
18 ก.ย. 2550

เขียนเสร็จวันที่ 18 มิ.ย. 2550
แก้แบบวันที่ ....

การเดินสายควบคุมในท่อร้อยสาย
สำหรับการติดตั้งมิเตอร์ประกอบ วี.ที. และ ซี.ที. แรงสูง

มิติเป็น ....
มาตราส่วน ....

รองผู้ว่าการวางแผนและพัฒนาระบบไฟฟ้า
(ท)

WIRING OF CONTROL CABLE IN CONDUIT
FOR METER INSTALLATION WITH H.V., V.T. AND C.T.

แบบเลขที่ SA2-015/50009
แผ่นที่ 4 ของจำนวน 5 แผ่น

การประกอบเลขที่ 2509
ASSEMBLY NO. 3512

บัญชีวัสดุ
BILL OF MATERIAL

ลำดับที่ ITEM	รายละเอียด DESCRIPTION	จำนวน REQ'D	วัสดุเลขที่ MATM NO.
1	ท่อโลหะอ่อนกันของเหลว ขนาด ø 1 นิ้ว CONDUIT, LIQUIDTIGHT FLEXIBLE METAL, ø 1 INCH	15 ม. m	1080050050
2	คอนเน็คเตอร์จับท่อโลหะอ่อนกันของเหลวแบบตรง ขนาด ø 1 นิ้ว CONNECTOR, FOR LIQUIDTIGHT FLEXIBLE METAL CONDUIT, ø 1 INCH	7	1080050700
3	แป้นมิเตอร์ ขนาด 2x20x20 ซม. METER PLATE, 2x20x20 cm	2	1060100000
4	ลวดเหล็กตีเกลียว 50/7 ต.มม. WIRE, STEEL STRANDED, 50/7 mm^2	4 ม. m	1010100004
5	เข็มขัดรัดสาย (ทำจากลวดอะลูมิเนียมแบน ขนาด 1x10 มม.) ความยาวตามต้องการ CABLE STRAP (MADE OF ARMOUR TAPE 1x10 mm), LENGTH AS REQUIRED	–	1020200000
6	ตะปูหัวกลมแบน ยาว 15–50 มม. ø 1.00 มม. มอก. 113 NAIL, ROUND MILD WIRE 15–50 mm LONG, ø 1.00 mm TIS 113	7	–
7	สลักเกลียว M 16x300 มม. BOLT, MACHINE, M 16x300 mm	2	1010110204
8	แหวนสี่เหลี่ยมแบน ขนาด 52x52x4.5 มม. รู ø 18 มม. มอก. 258 WASHER, SQUARE, FLAT 52x52x4.5 mm HOLE ø 18 mm TIS 258	4	1010180100
9	ผนึกตรามิเตอร์ SECURITY SEAL	10	1060100015
10	สายทองแดงหุ้มฉนวนใช้ภายนอก ขนาด 4 ต.มม. (คอนโทรลเคเบิล) CONDUCTOR, INSULATED, WEATHER-PROOF, cu 4 mm^2 (CONTROL CABLE)	12 ม. m	1020080403 1020080457
11	หางปลาสำหรับสาย ขนาด 2.5 ต.มม. CABLE LUG, COMPRESSION TYPE, FOR Cu CABLE 2.5 mm^2	9	1020420503
12	หางปลาสำหรับสาย ขนาด 4 ต.มม. CABLE LUG, COMPRESSION TYPE, FOR Cu CABLE 4 mm^2	7	1020420504

หมายเหตุ

* ขั้วต่อสายทางด้านทุติยภูมิของ วี.ที. และ ซี.ที. ต้องต่อลงดิน โดยใช้วัสดุลำดับที่ 10 และเชื่อมต่อกับระบบการต่อลงดินที่ตู้มิเตอร์

NOTE

* SECONDARY SIDE OF TERMINAL FOR V.T. AND C.T. SHALL BE GROUNDED BY MAT. NO. 10 AND CONNECT WITH GROUNDING SYSTEM AT CABINET .

COPY

กองมาตรฐานระบบไฟฟ้า
ฝ่ายมาตรฐานและความปลอดภัย

ผู้เขียน พุงศักดิ์ ศิริสมบูรณ์
ผู้สำรวจ
วิศวกร
หัวหน้าแผนก
ผู้อำนวยการกอง
ผู้อำนวยการฝ่าย

รองผู้ว่าการวางแผนและพัฒนาระบบไฟฟ้า
(ท)

การไฟฟ้าส่วนภูมิภาค

ผู้ว่าการ (ท)
1 4 ก.ย. 2550

การเดินสายควบคุมในท่อร้อยสาย
สำหรับการติดตั้งมิเตอร์ประกอบ วี.ที. และ ซี.ที. แรงสูง

WIRING OF CONTROL CABLE IN CONDUIT
FOR METER INSTALLATION WITH H.V., V.T. AND C.T.

ใช้แทนแบบ ....
ถูกแทนโดยแบบ ....
เขียนเสร็จวันที่ 18 มิ.ย. 2550
แก้แบบวันที่ ....
มิติเป็น ....
มาตราส่วน ....
แบบเลขที่ SA2-015/50009
แผ่นที่ 5 ของจำนวน 5 แผ่น

1 4