

| การประกอบเลขที่ ASSEMBLY NO. | 5687 D |
|---|---|

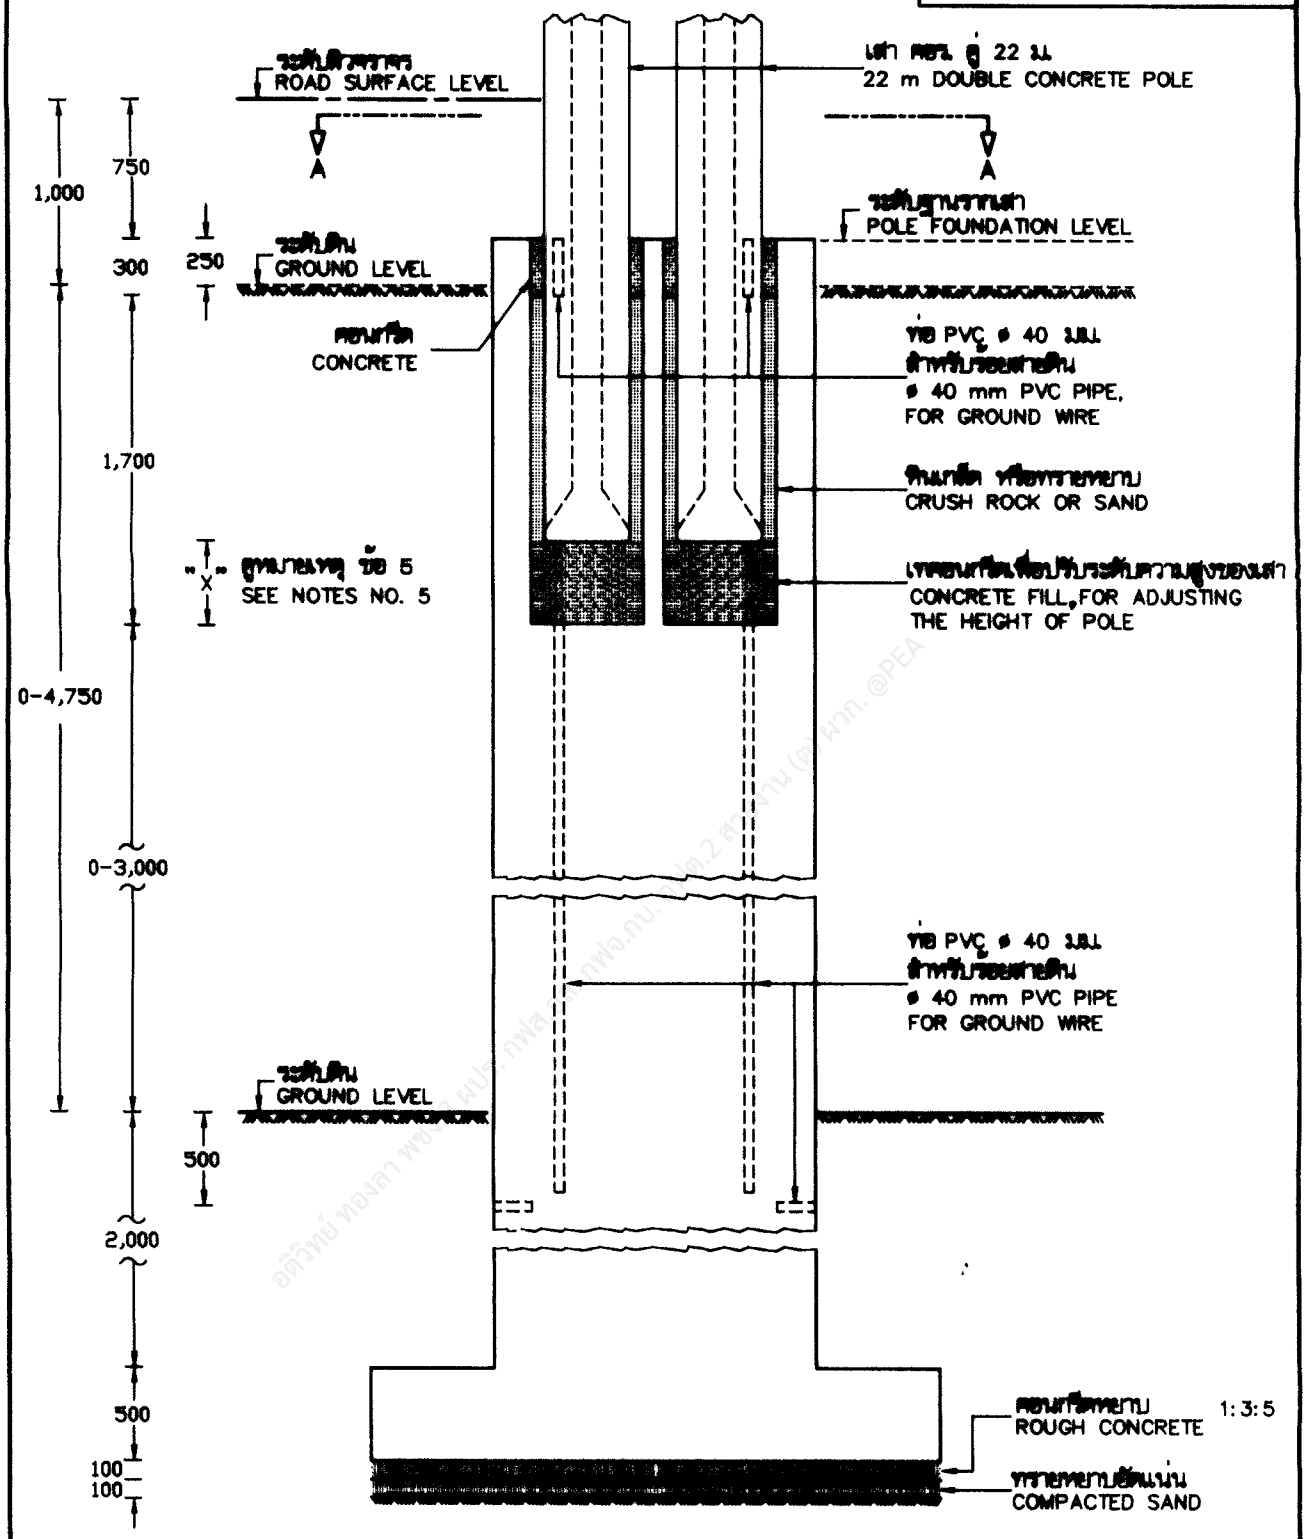


| | | |
|---|---|---|
| กองมาตรฐานระบบไฟฟ้า<br>ฝ่ายมาตรฐานและความปลอดภัย | การไฟฟ้าส่วนภูมิภาค | ใช้แทนแบบ SA1-015/45013<br>ดูแทนโดยแบบ .....<br>เขียนเสร็จวันที่ 10 มิ.ย. 2547<br>แก้แบบวันที่ .....<br>หน่วยเป็น มิลลิเมตร<br>มาตราส่วน 1:40 |
| ผู้เขียน<br>ผู้ตรวจ<br>ผู้สอบ<br>หัวหน้าแผนก<br>ผู้อำนวยการกอง<br>ผู้อำนวยการฝ่าย | ผู้ว่าการ<br>รายละเอียดที่ 10 ลว 3 ก.ย. 2547<br>ฐานราเสา ( แบบที่ 10 ) | |
| รองผู้ว่าการวิศวกรรมและบริหารระบบไฟฟ้า | DETAIL 10 B<br>POLE FOUNDATION ( TYPE 10 ) | แบบแสดงที่ SA1-015/47021<br>แผ่นที่ .1. ของจำนวน .2. แผ่น |

2 ก.ย. 47

| การประกอบแบบที่ ASSEMBLY NO. | 5687 D |
|---|---|

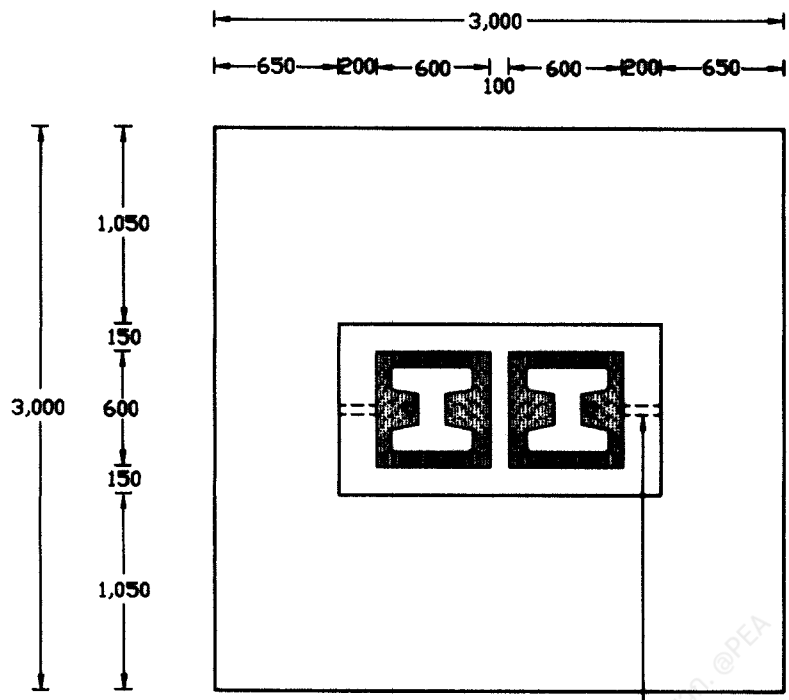


รูปตัด A–A
SECTION

**หมายเหตุ**

1 ฐานรากนี้ใช้ในการที่ดินสามารถรับน้ำหนักปลอดภัยได้ตั้งแต่ 12 ตัน / ตารางเมตรขึ้นไป

2 ใช้ในการเดินทางตรงหรือทางโค้ง ที่มีและไม่มีสายยึดโยง (กรณีพื้นที่ก่อสร้างฐานรากสามระดับต่ำกว่าระดับผิวจราจร 1.00–5.75 ม.)

3 รายละเอียดเพิ่มเติมใน แบบเลขที่ IB2–011/44013

4 ข้อกำหนดการติดตั้งฐานรากเสาในเขตทางหลวง ตามแบบเลขที่ SA1–015/43012 (การประกอบเลขที่ 5687)

5 ระยะ "X"= 450 มม. สำหรับการก่อสร้างฐานรากเสาในพื้นที่ทางหลวงที่ไม่มีทางเท้า ส่วนพื้นที่อื่นๆ ระยะ "X"= 0 มม.

**NOTES**

1 THIS FOUNDATION IS USED IN CASE ALLOWABLE SOIL BEARING CAPACITY OF 12 TON/$m^2$ OR MORE .

2 USE FOR STRAIGHT OR ANGLE LINE WITH AND WITHOUT GUY (IN CASE OF GROUND SURFACE LEVEL IS BETWEEN 1.00–5.75 m LOWER THAN ROAD SURFACE LEVEL) .

3 SEE ADDITIONAL DETAIL, DWG. NO. IB2–011/44013 .

4 SEE RECOMMENDATION, FOR POLE FOUNDATION INSTALLATION IN HIGHWAY AREA, DWG. NO. SA1–015/43012 (ASSEMBLY NO. 5687) .

5 THE "X" IS 450 mm HEIGHT FOR FOUNDATION CONSTRUCTION IN HIGHWAY AREA WHICH HAVE NO PAVEMENT, OTHER AREA THE "X" IS ZERO .

| | | |
|---|---|---|
| ตรวจมาตรฐานระบบไฟฟ้า ฝ่ายมาตรฐานและความปลอดภัย | การไฟฟ้าส่วนภูมิภาค | ใช้แทนแบบ SA1–015/45013 |
| ผู้เรียบ ..... | ผู้ว่าการ ..... | ฐานแทนโดยแบบ ..... |
| ผู้ตรวจ ..... | | เขียนเสร็จวันที่ 10 มิ.ย. 2547 |
| วิศวกร ..... | รายละเอียดที่ 10 23 ก.ย. 2547 | แก้แบบวันที่ ..... |
| หัวหน้าแผนก ..... | ฐานรากเสา ( แบบที่ 10 ) | หน่วยเป็น มิลลิเมตร |
| ผู้ช่วยอาวุโส ..... | | มาตราส่วน 1:40 |
| ผู้ช่วยอาวุโส ..... | | |
| รองผู้ว่าการวางแผนและพัฒนาระบบไฟฟ้า ..... | DETAIL 10 B<br>POLE FOUNDATION ( TYPE 10 ) | แบบเลขที่ SA1–015/47021 |
| 23 ก.ย. 2547 | | แผ่นที่ 2 ของจำนวน 2 แผ่น |