การประกอบเลขที่
ASSEMBLY NO. 3240

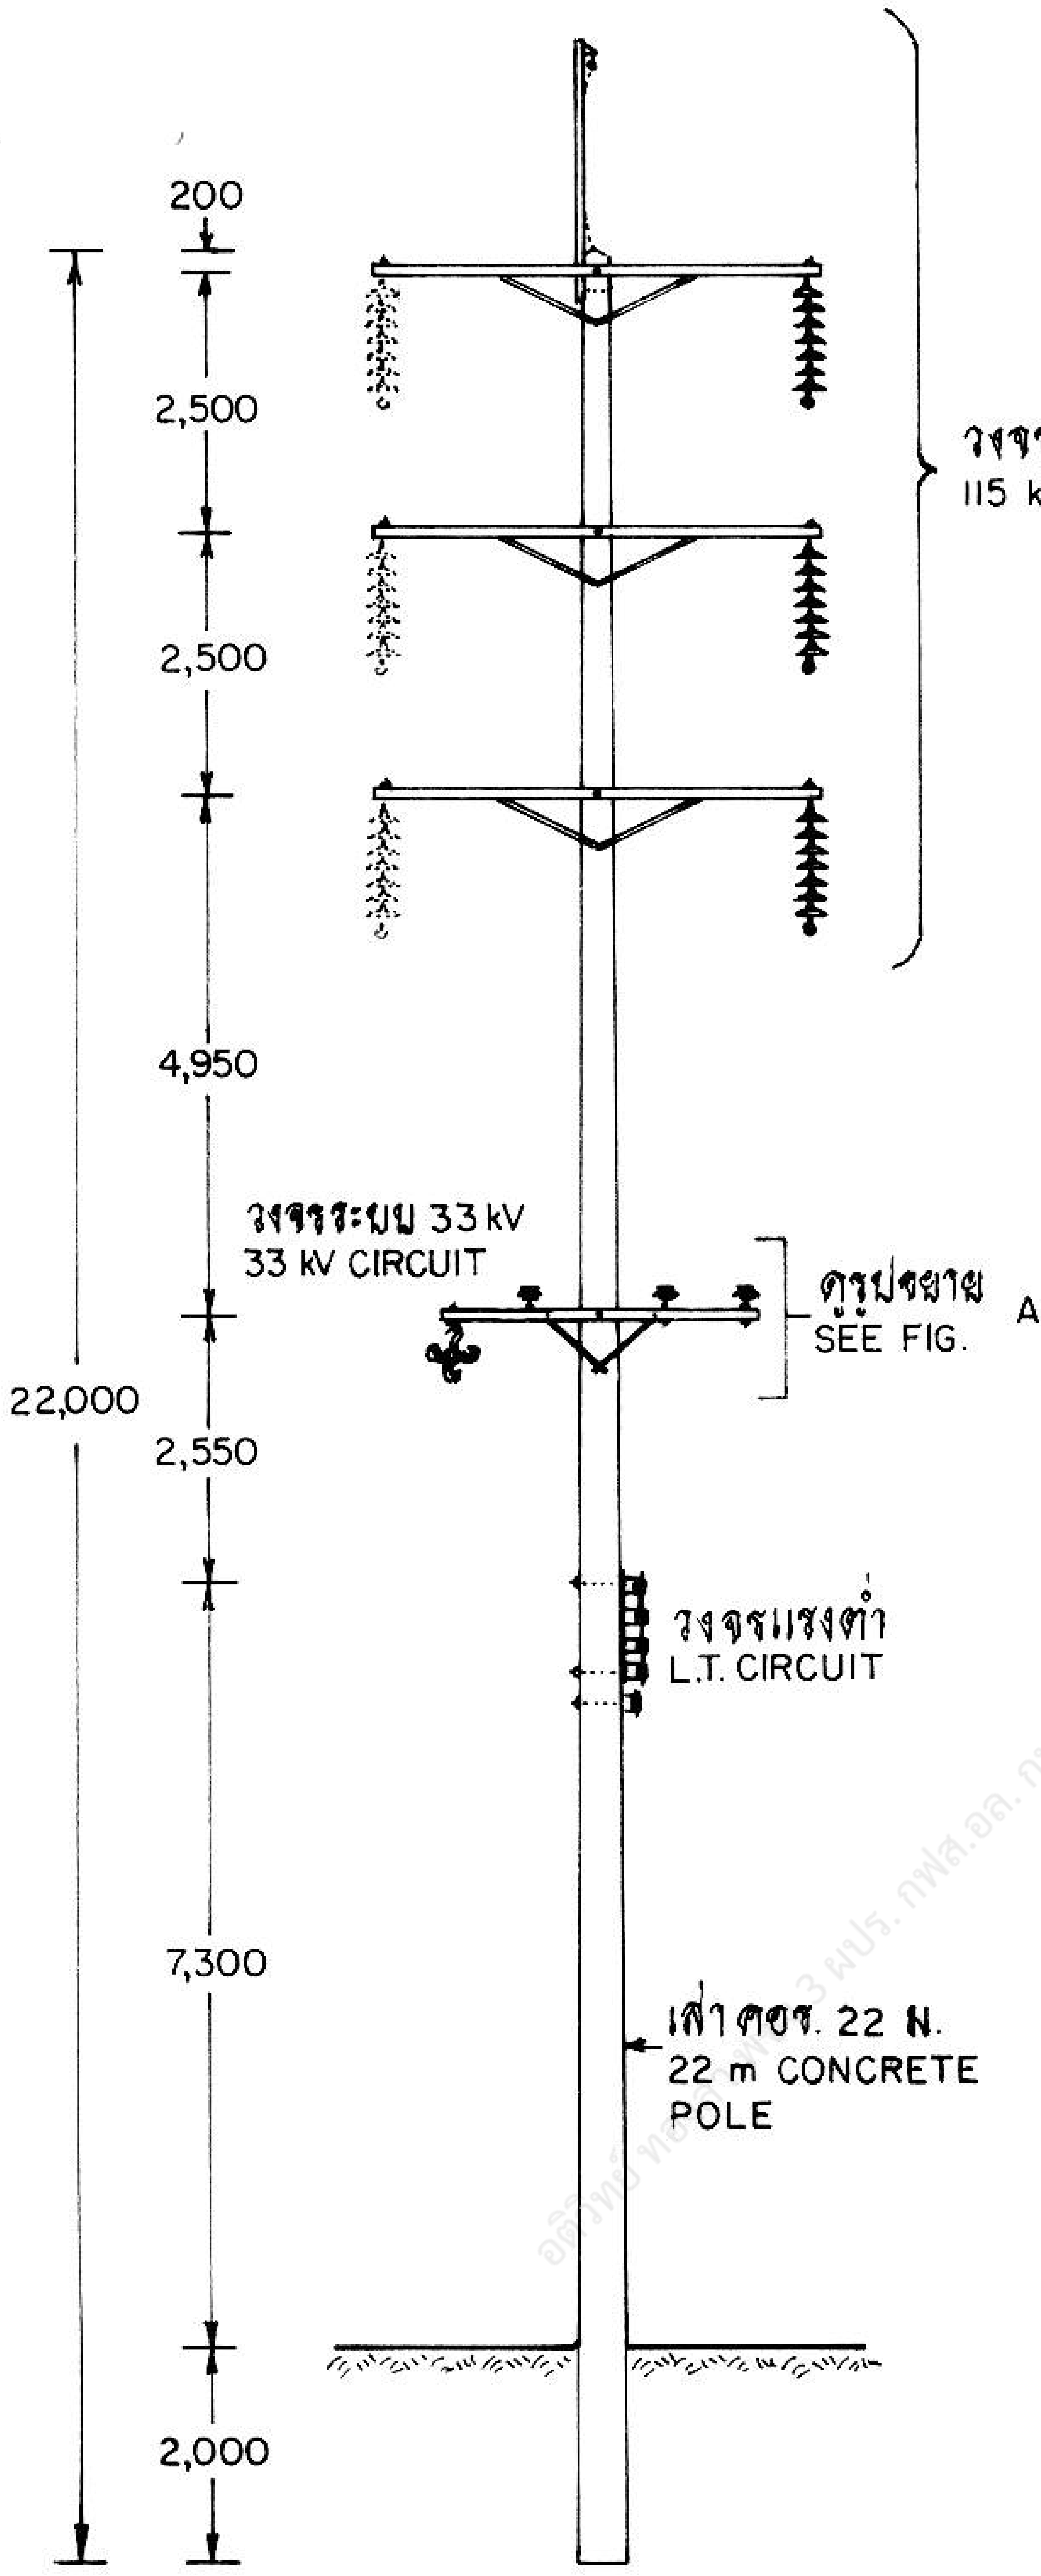
200
2,500
2,500
4,950
2,550
7,300
2,000
22,000
วงจรระบบ 115 kV
115 kV CIRCUIT
วงจรระบบ 33 kV
33 kV CIRCUIT
ดูรูปขยาย A
SEE FIG. A
วงจรแรงต่ำ
L.T. CIRCUIT
เสา คอร. 22 ม.
22 m CONCRETE POLE

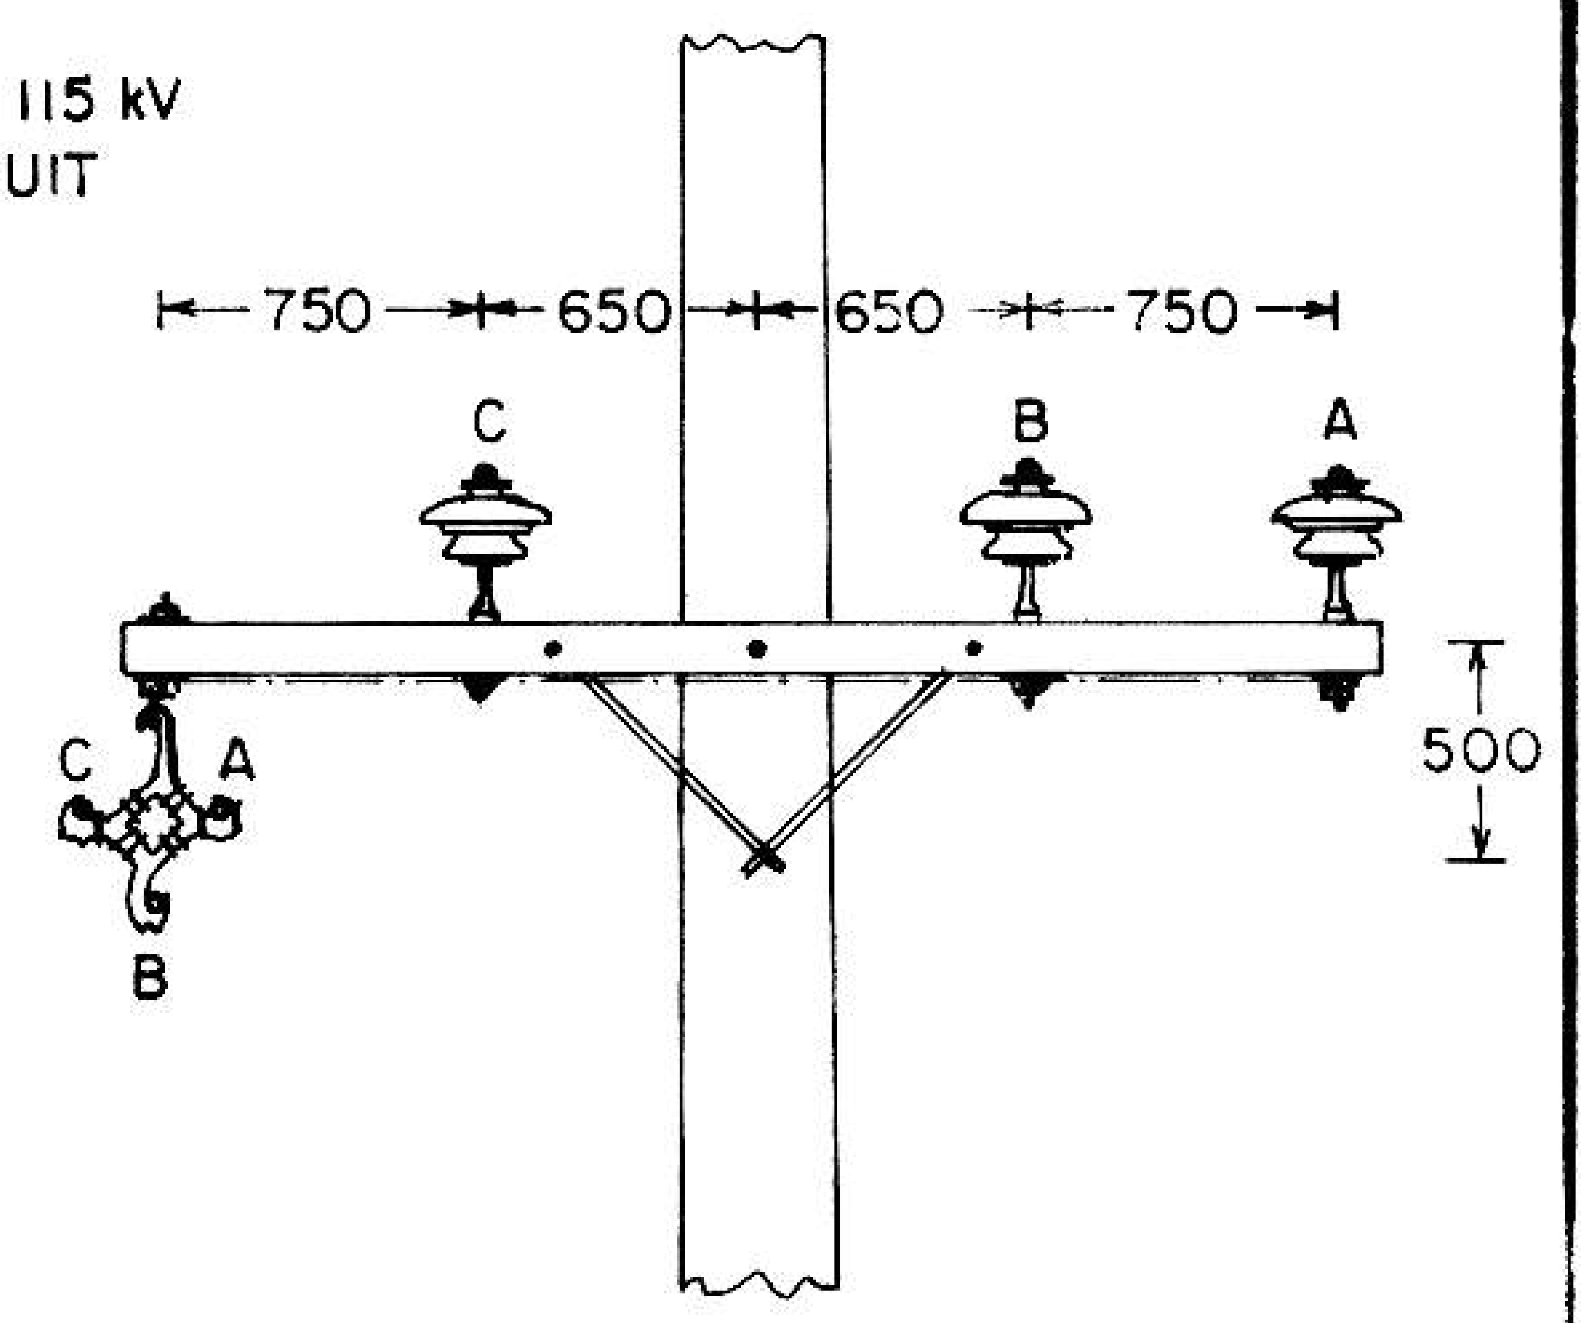
750
650
650
750
C
B
A
500
C
A
B

รูปขยาย A
FIG A

ข้อกำหนดการใช้งาน ระยะห่างระหว่างช่วงเสา และระยะหย่อนยานของสายที่มุมเบี่ยงเบนต่างๆ ดูรายละเอียดจากแบบระยะห่างระหว่างช่วงเสาของโครงสร้างสายส่ง 115 kV ตามแบบเลขที่ IBI-015/36038 (การประกอบเลขที่ 5151A)

THE RECOMMENDATION OF SPAN LENGTH AND SAG OF CONDUCTOR AT ANY LINE DEFLECTION ANGLE, SEE DETAIL IN DRAWING NO. IBI-015/36038 (ASSEMBLY NO. 5151A) SPAN LENGTHS FOR 115 kV CONSTRUCTION STRUCTURE.

3 ผปร. กฟส.อล. กฟจ. กฟต.2 สายงาน (ต) ผวก. @PEA

กองวิศวกรรมไฟฟ้าและเครื่องกล
ฝ่ายวิศวกรรม

ผู้เขียน
ผู้สำรวจ
วิศวกร
หัวหน้าแผนก
ผู้อำนวยการกอง
ผู้อำนวยการฝ่าย

รองผู้ว่าการฝ่ายเทคนิค

การไฟฟ้าส่วนภูมิภาค

ผู้ว่าการ 2536

การติดตั้งสายระบบจำหน่าย 33 kV
บนโครงสร้างสายส่ง ระบบ 115 kV

33 kV DISTRIBUTION LINE INSTALLATION
ON 115 kV SUBTRANSMISSION POLE

ใช้แทนแบบ
ถูกแทนโดยแบบ
เขียนเสร็จวันที่ 27 ต.ค. 36
แก้แบบวันที่
หน่วยเป็น มิลลิเมตร
มาตราส่วน 1 : 50, 1 : 125

แบบเลขที่ SA4-015/36016
แผ่นที่ 1 จากจำนวน 5 แผ่น

การประกอบเลขที่
ASSEMBLY NO. 3240

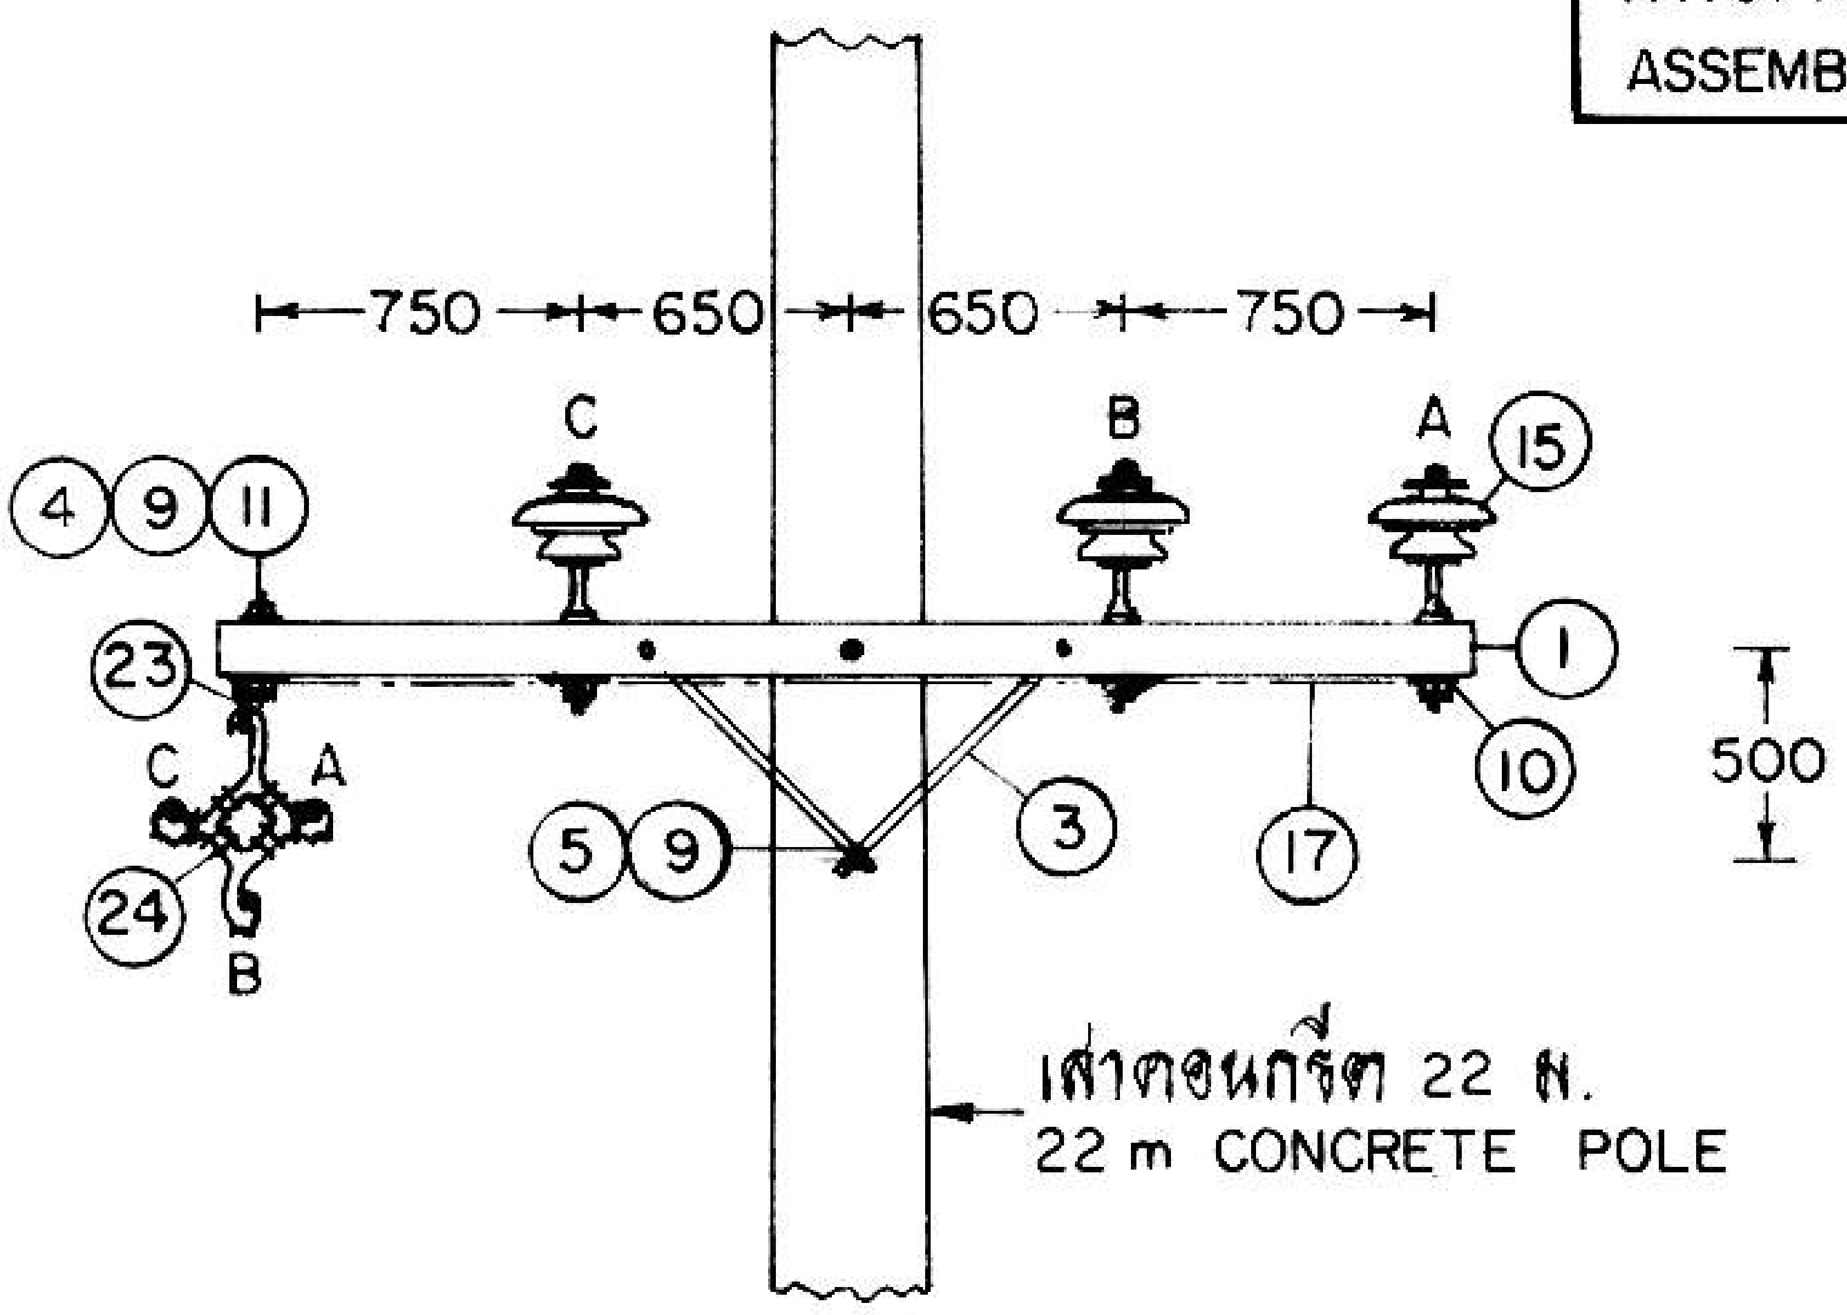
750
650
650
750
C
B
A
15
4 9 11
23
1
10
500
C A
24
B
5 9
3
17
เสาคอนกรีต 22 ม.
22 m CONCRETE POLE

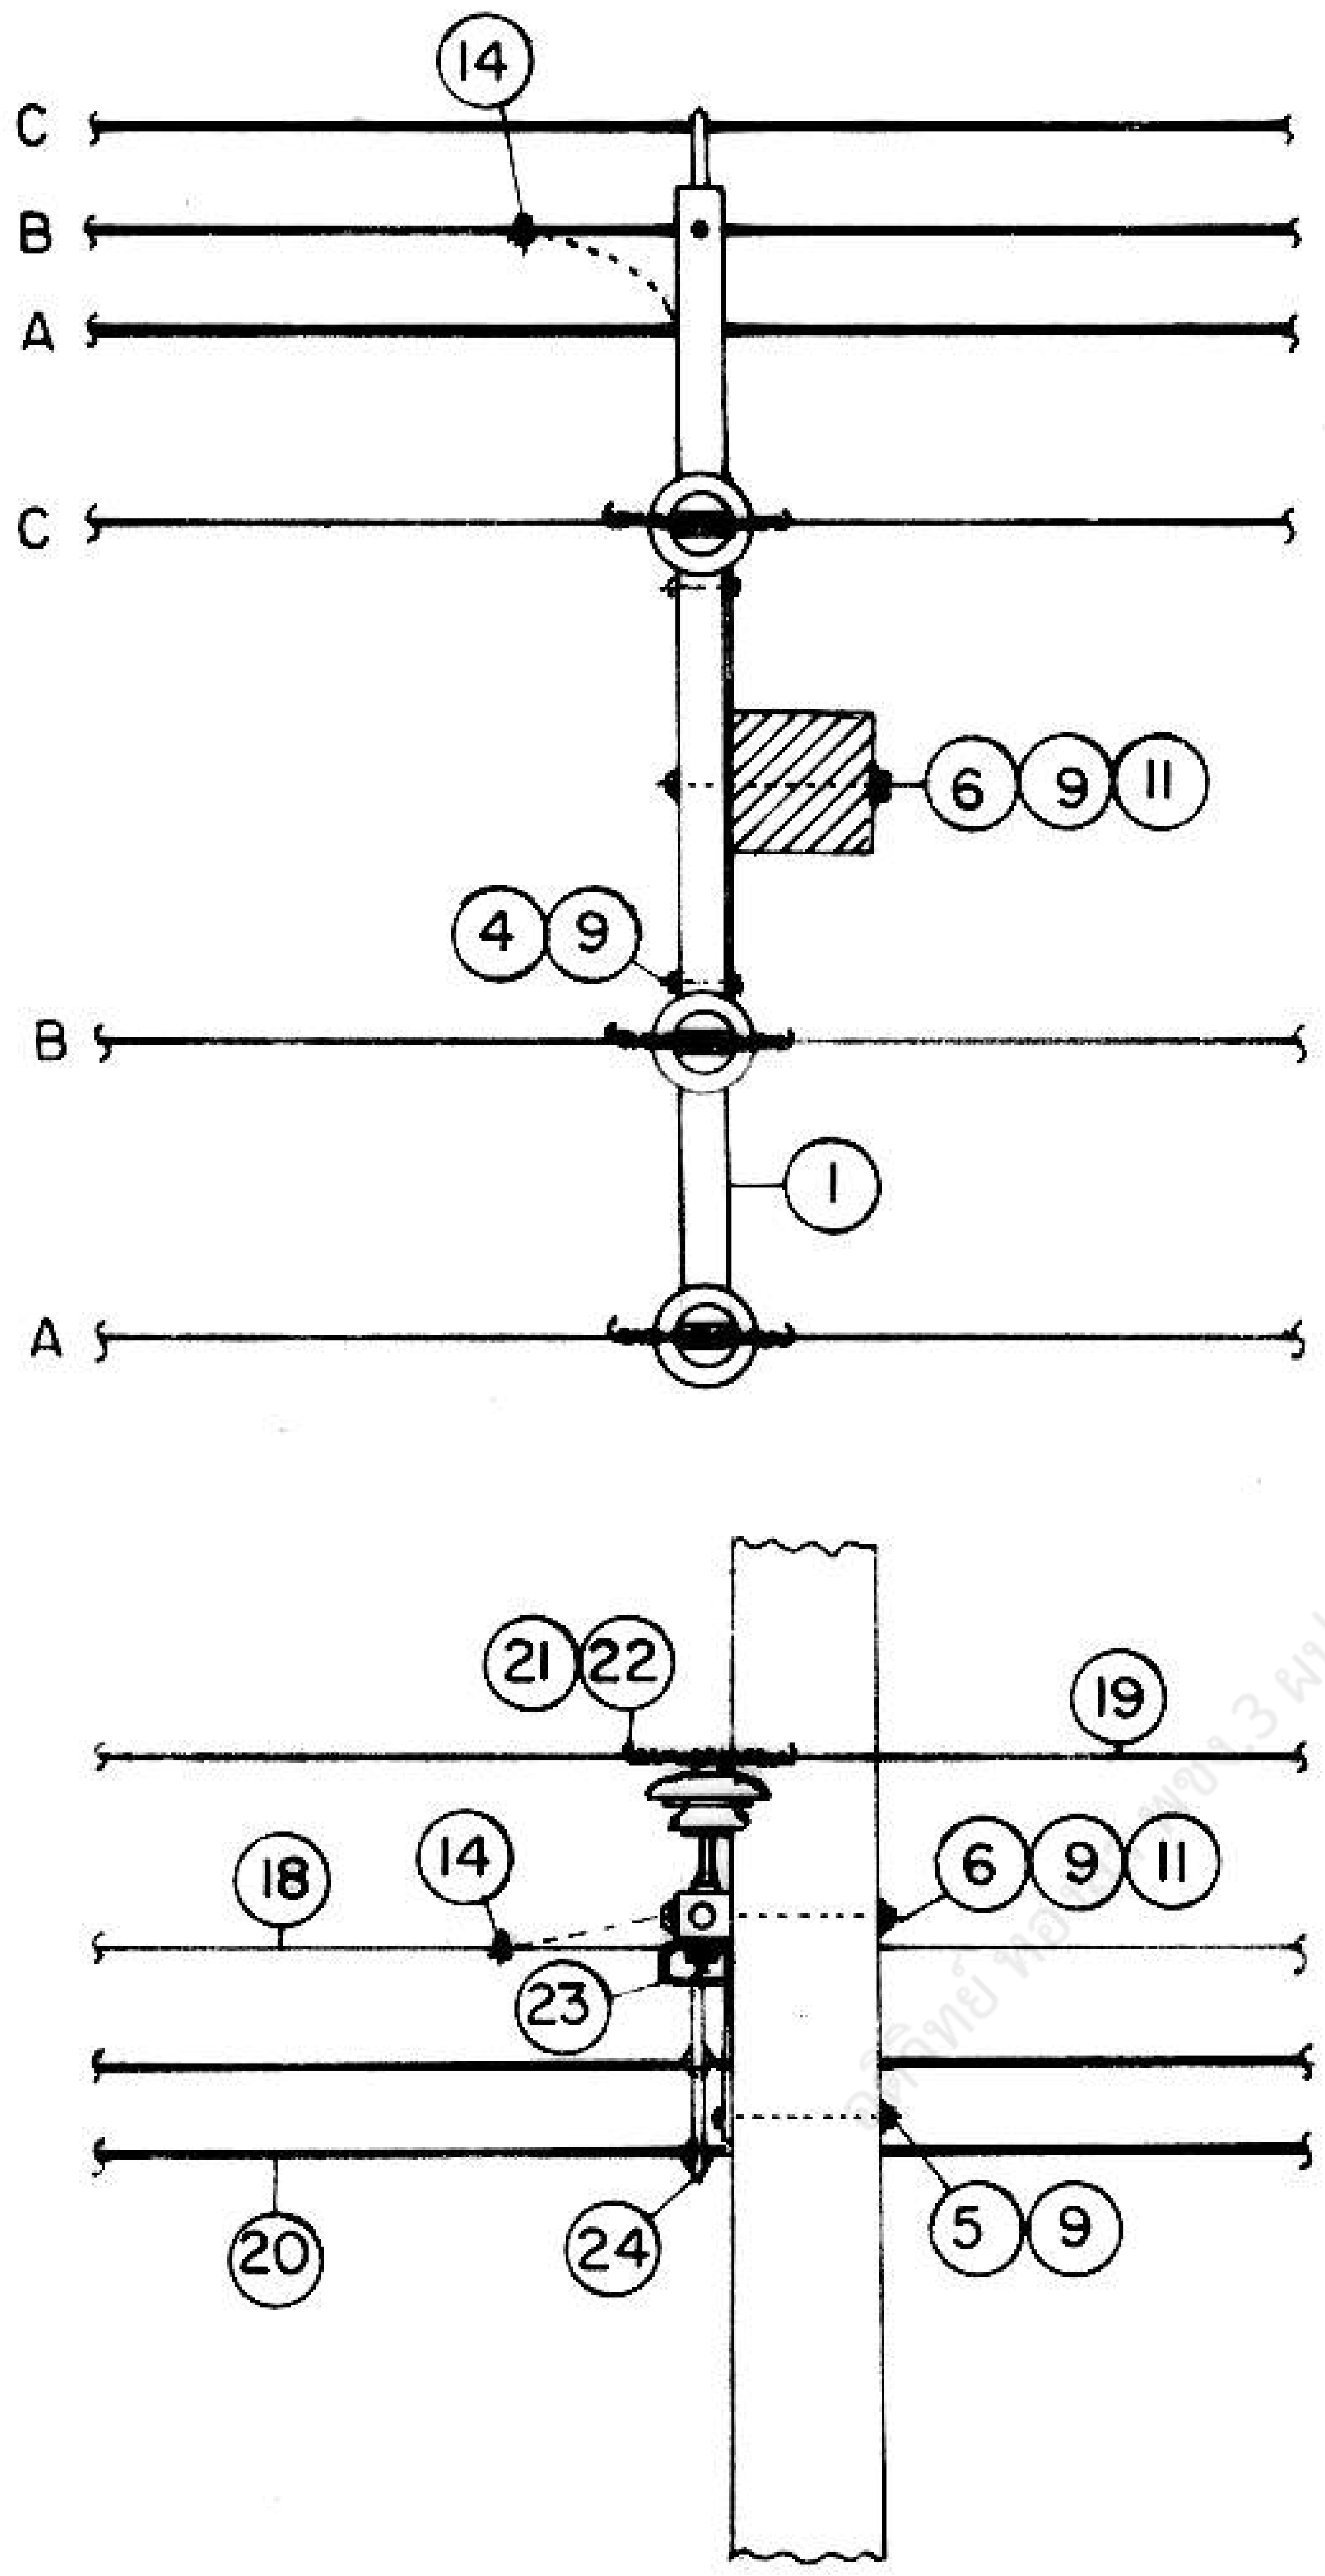
14
C
B
A
C
6 9 11
4 9
B
1
A
21 22
19
18
14
6 9 11
23
5 9
20
24

I สำหรับทางตรง
FOR LINE ANGLE 0°- 5°

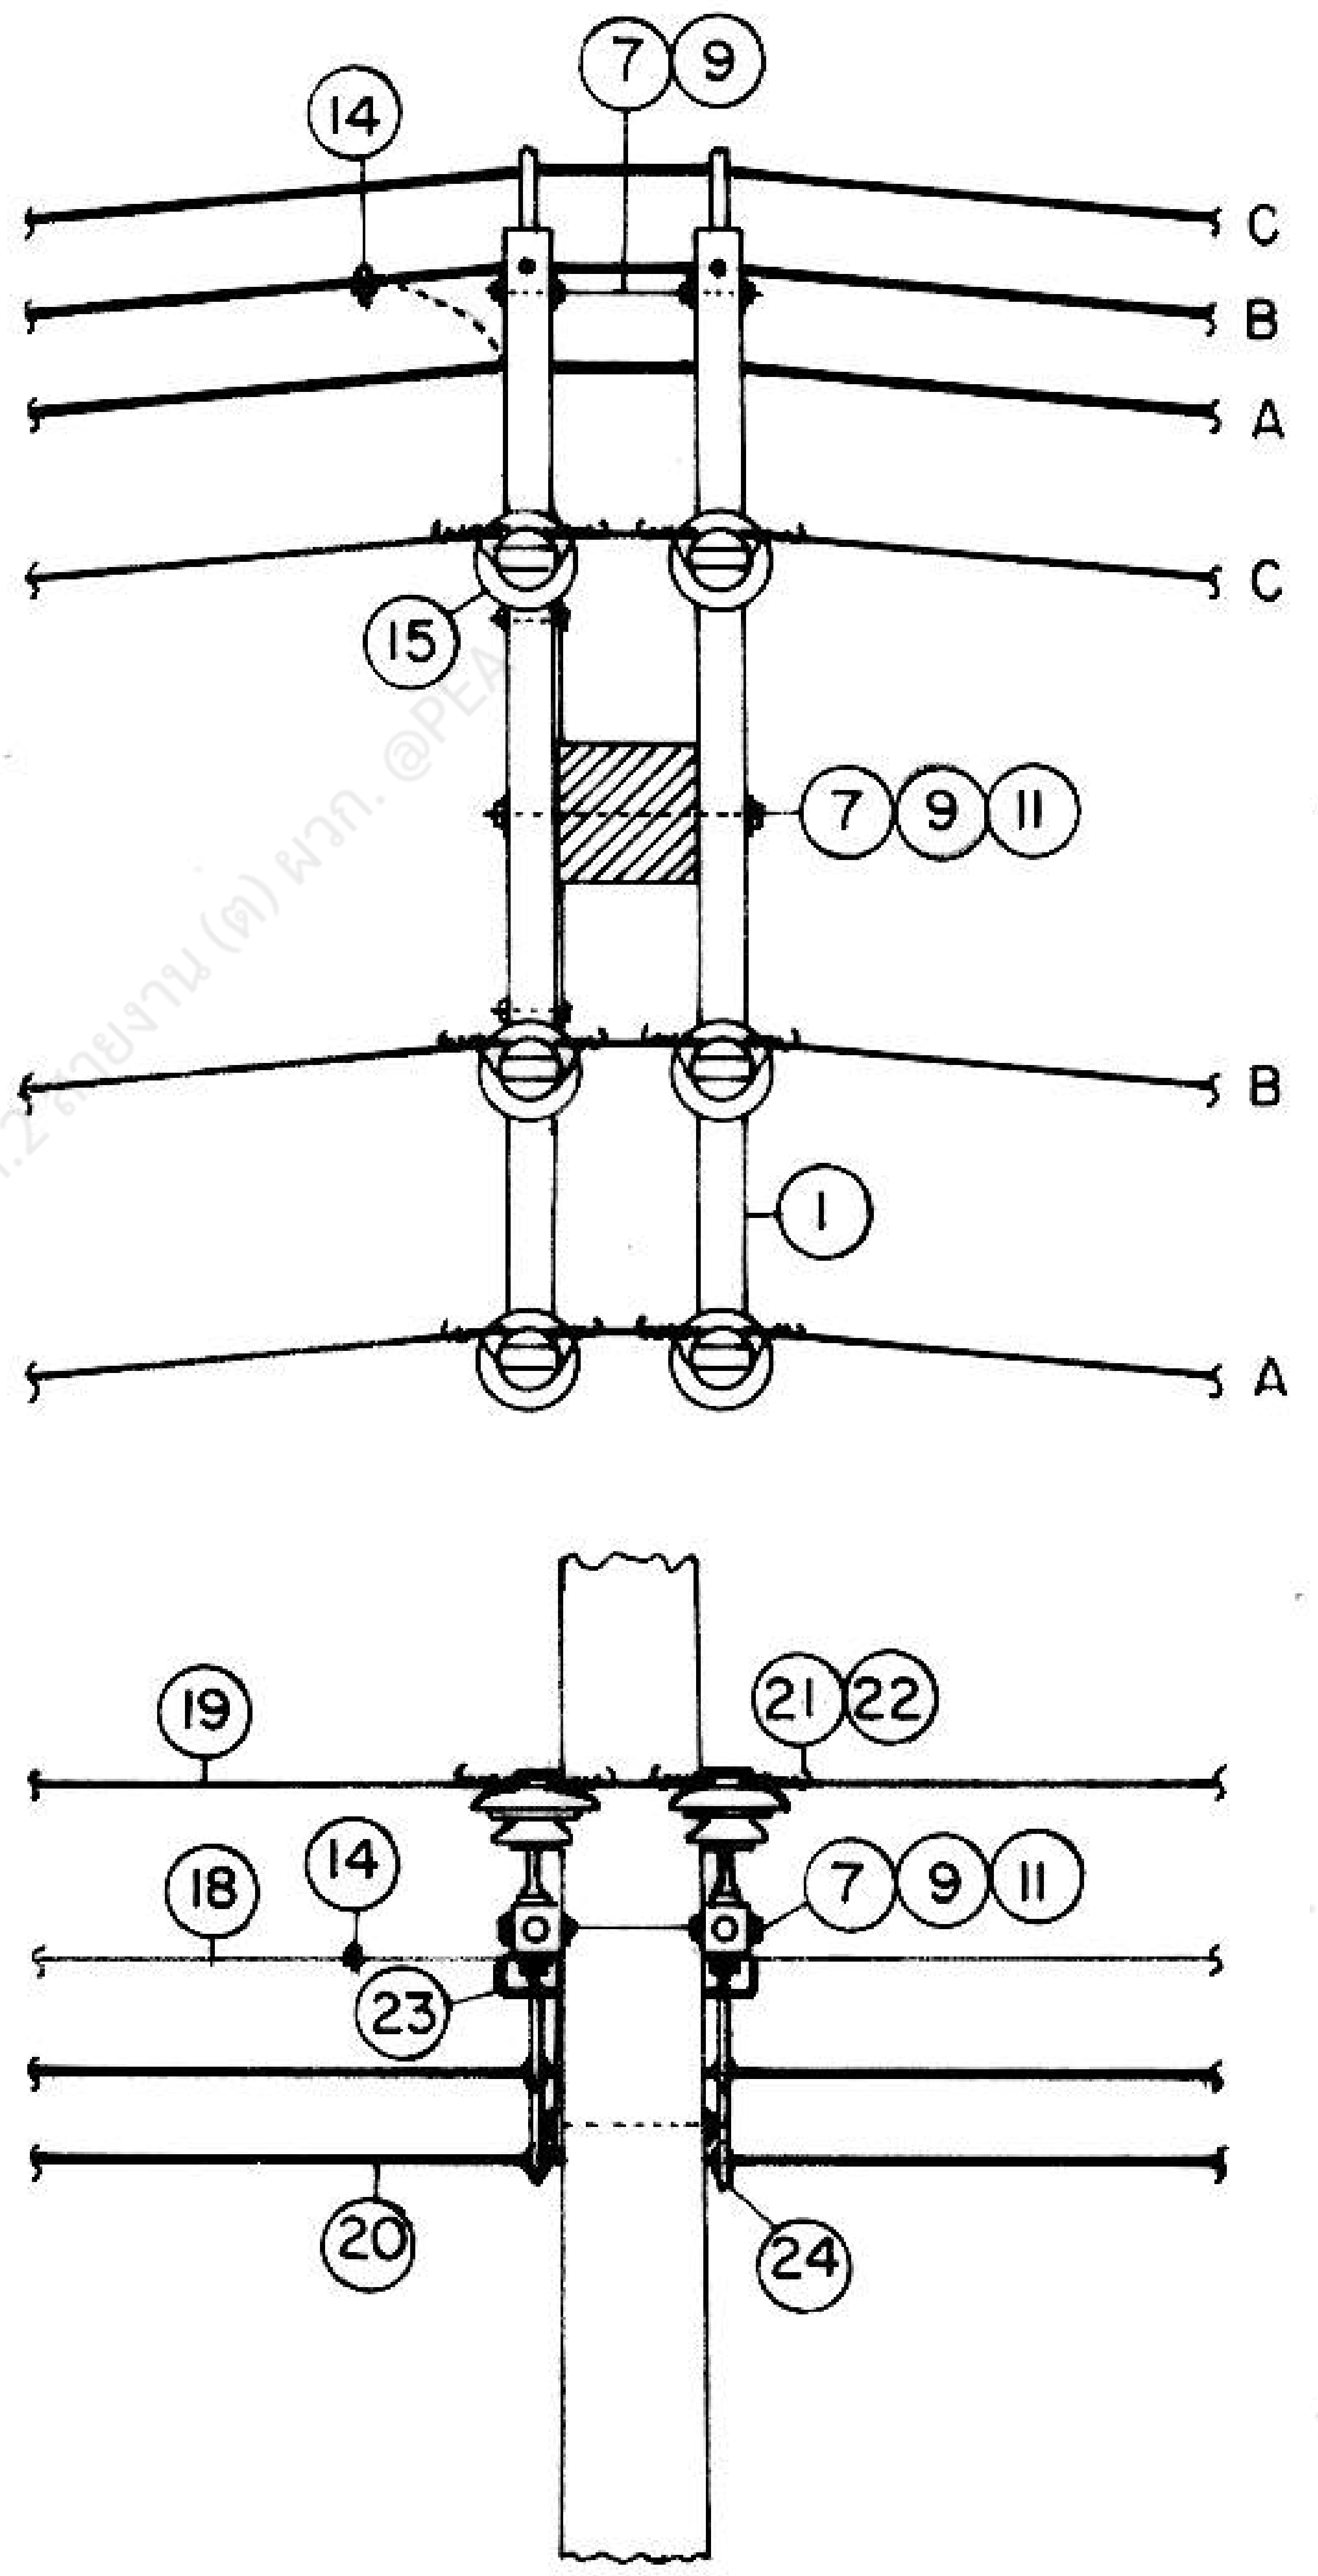
14
7 9
C
B
A
C
15
7 9 11
B
1
A
19
21 22
18
14
7 9 11
23
20
24

II สำหรับทางโค้ง
FOR LINE ANGLE 5°- 30°

กองวิศวกรรมไฟฟ้าและเครื่องกล
ฝ่ายวิศวกรรม

ผู้เขียน
ผู้สำรวจ
วิศวกร
หัวหน้าแผนก
ผู้อำนวยการกอง
ผู้อำนวยการฝ่าย

รองผู้ว่าการฝ่ายเทคนิค

การไฟฟ้าส่วนภูมิภาค

ผู้ว่าการ 27 ธ.ค. 2536

การติดตั้งสายระบบจำหน่าย 33 kV
บนโครงสร้างสายส่ง ระบบ 115 kV

33 kV DISTRIBUTION LINE INSTALLATION
ON 115 kV SUBTRANSMISSION POLE

ใช้แทนแบบ
ถูกแทนโดยแบบ
เขียนเสร็จวันที่ 27 ต.ค. 36
แก้แบบวันที่
มิติเป็น มิลลิเมตร
มาตราส่วน 1 : 50

แบบเลขที่ SA4-015/36016
แผ่นที่ 2 ของจำนวน 5 แผ่น

การประกอบเลขที่
ASSEMBLY NO. 3240

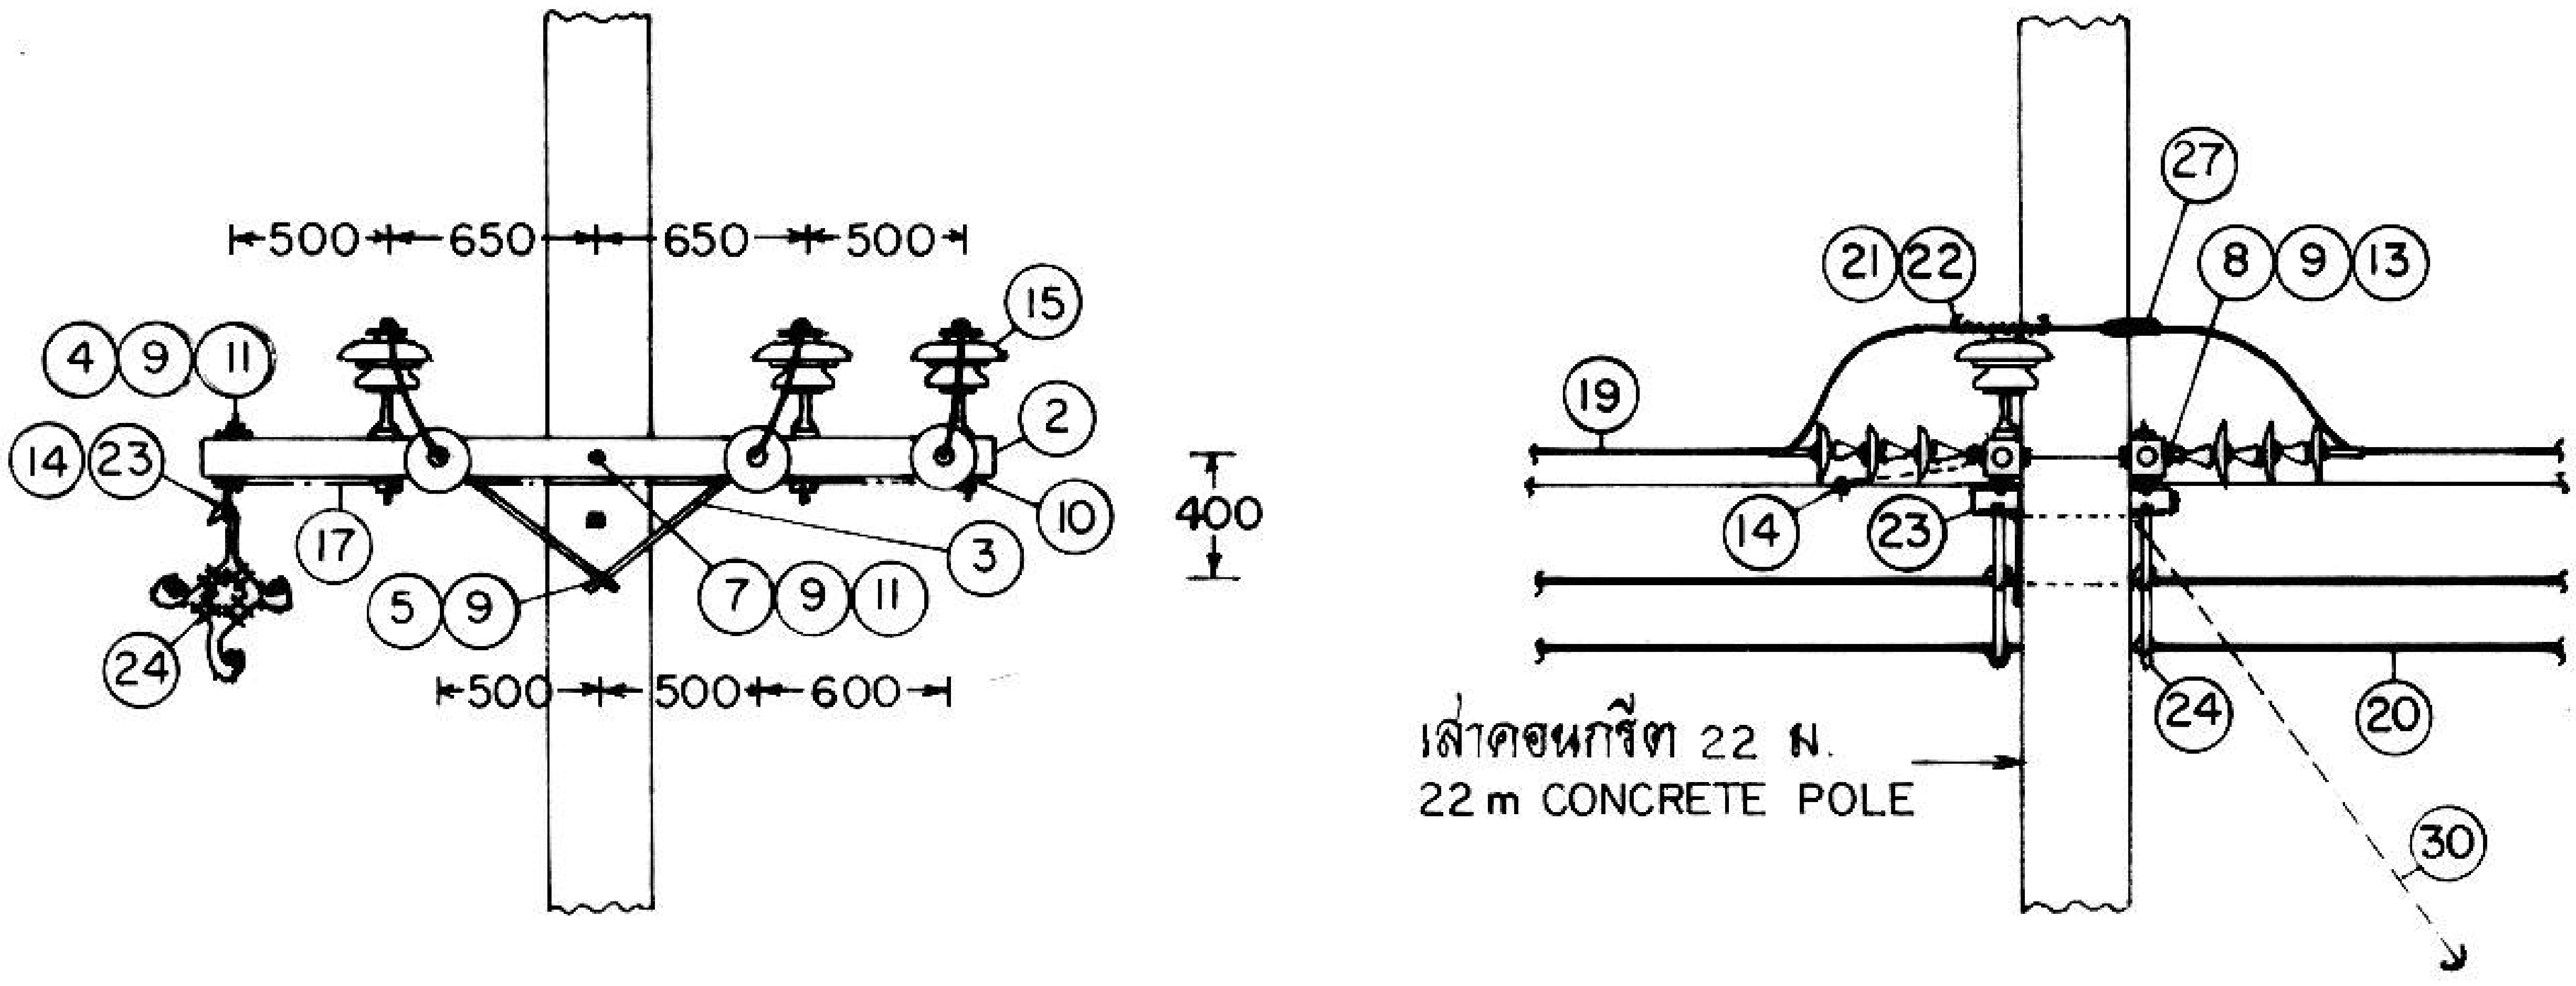
500
650
650
500
400
500
500
600
4 9 11
14 23
17
24
5 9
7 9 11
3
10
2
15
19
21 22
27
8 9 13
14
23
24
20
30
เสาคอนกรีต 22 ม.
22 m CONCRETE POLE

III สำหรับเข้าปลายสายสองข้าง ของวงจรสายเปลือย
FOR DOUBLE DEADEND OF BARE CONDUCTOR

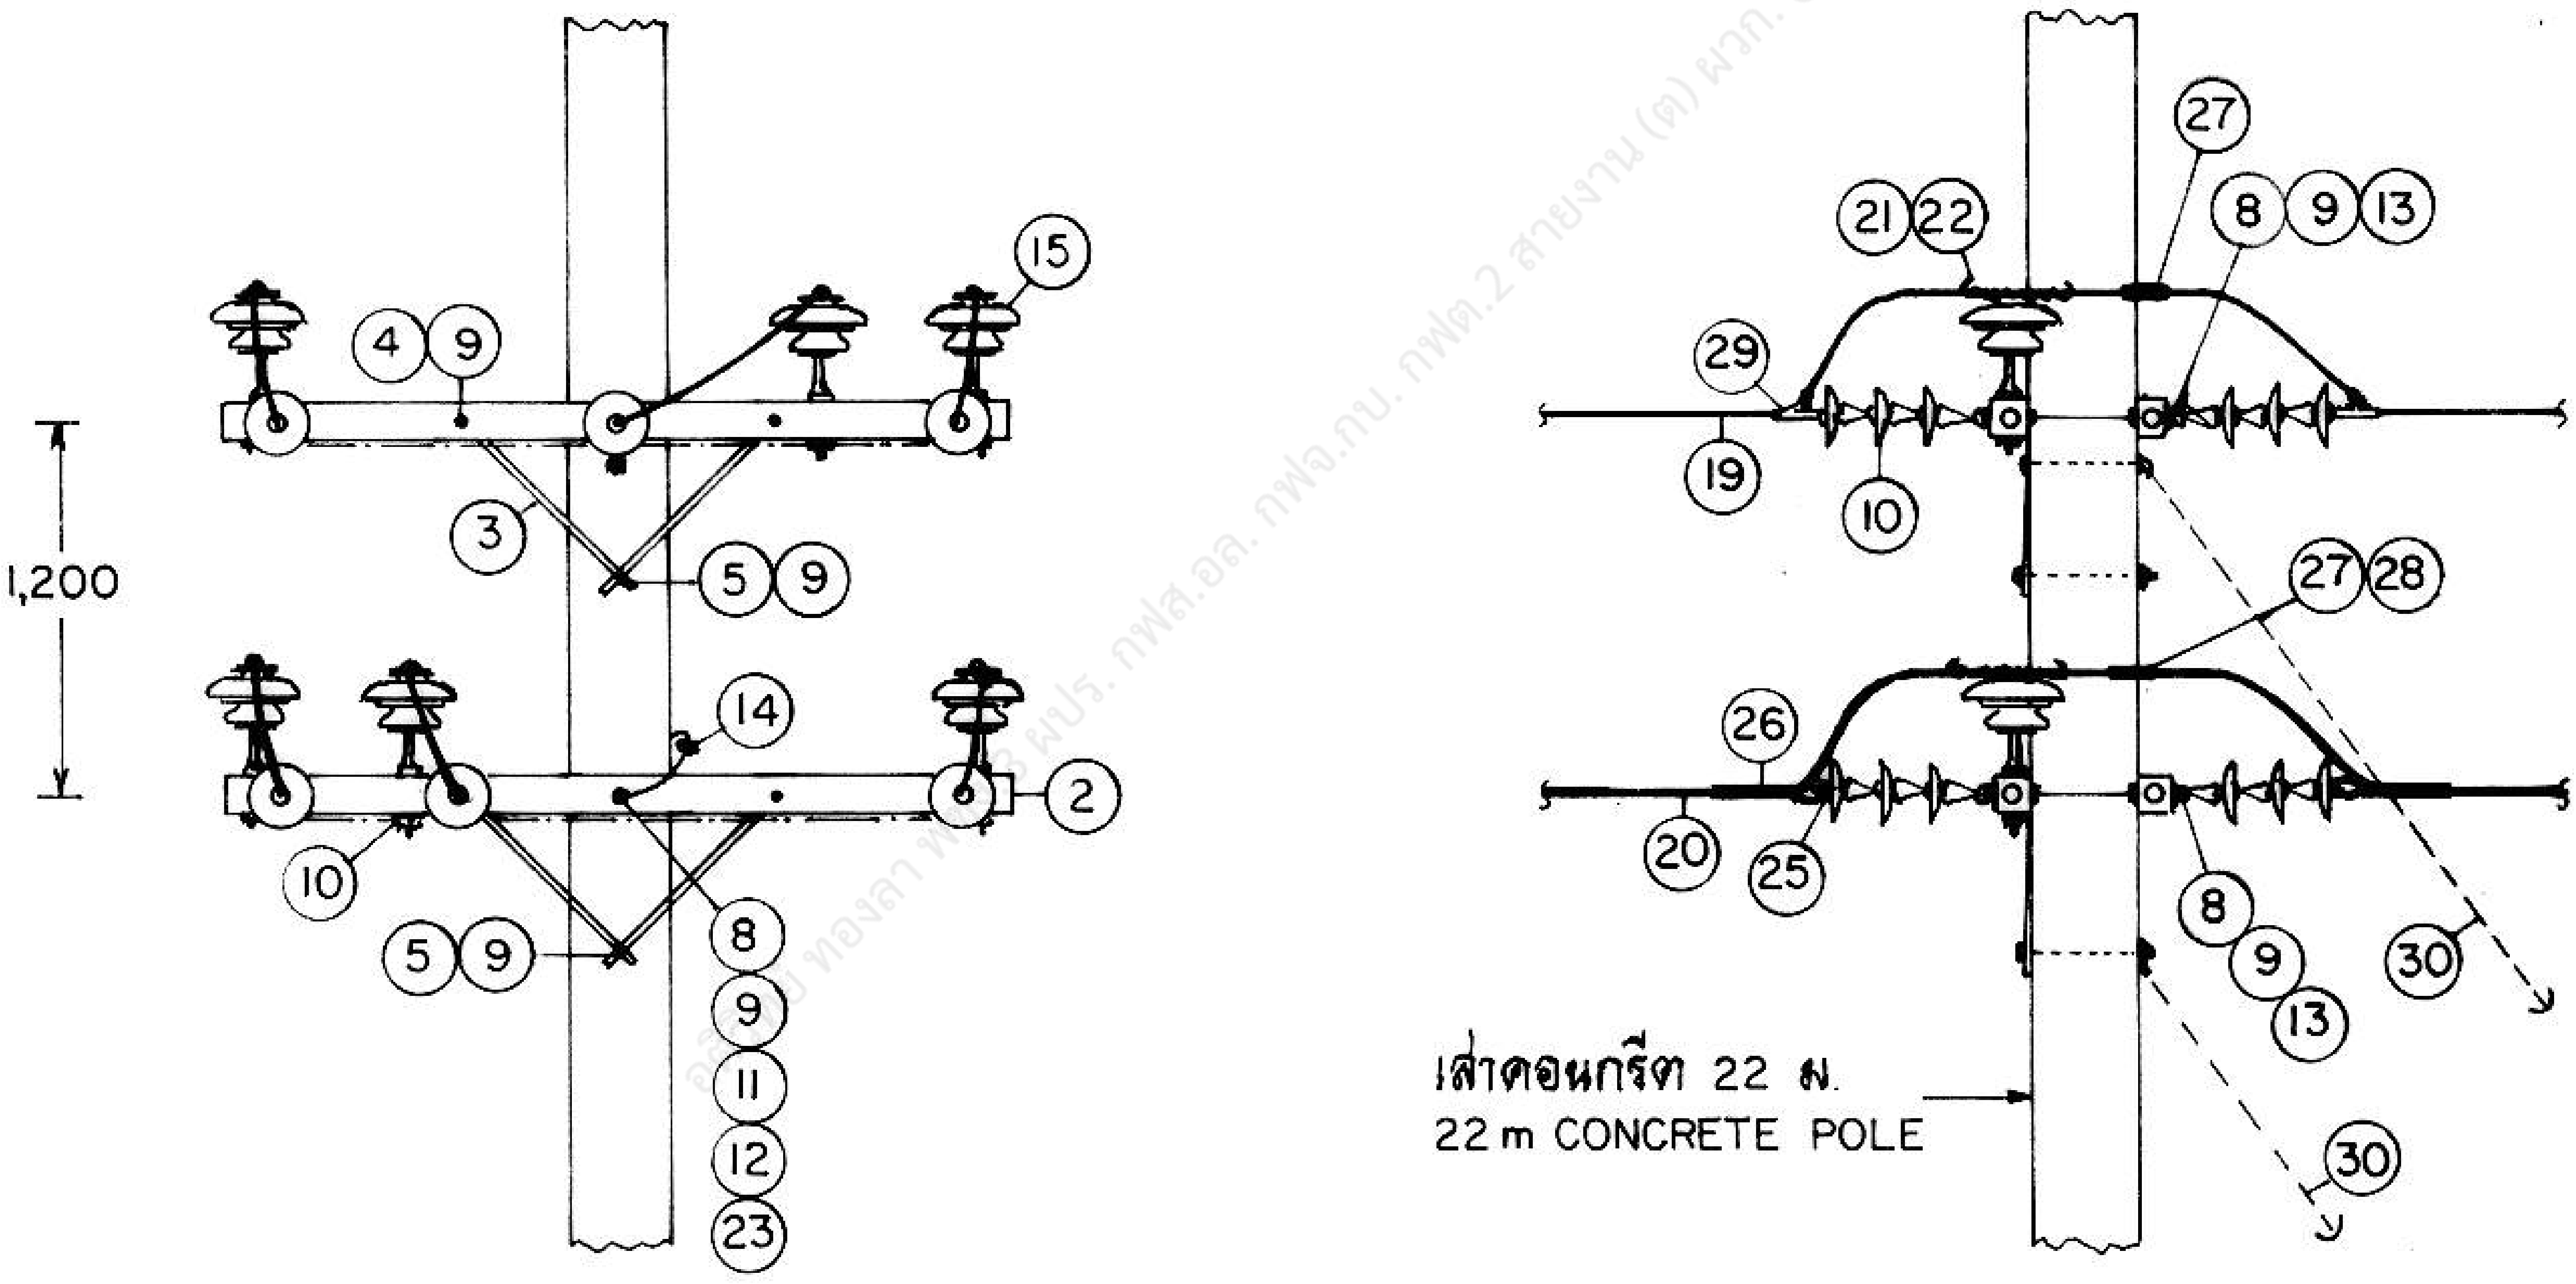
1,200
4 9
15
3
5 9
14
2
10
5 9
8
9
11
12
23
21 22
27
8 9 13
29
19
10
27 28
26
20
25
8
9
13
30
30
เสาคอนกรีต 22 ม.
22 m CONCRETE POLE

IV สำหรับเข้าปลายสายสองข้าง ทั้ง 2 วงจร
FOR 2 CIRCUITS DOUBLE DEADEND

กฟส.อล. กฟจ.กบ. กฟต.2 สายงาน (ต) ผวก. @PEA

กองวิศวกรรมไฟฟ้าและเครื่องกล
ฝ่ายวิศวกรรม

ผู้เขียน
ผู้สำรวจ
วิศวกร
หัวหน้าแผนก
ผู้อำนวยการกอง
ผู้อำนวยการฝ่าย

รองผู้ว่าการฝ่ายเทคนิค

การไฟฟ้าส่วนภูมิภาค

ผู้ว่าการ 27 ธ.ค. 2536 ผวก.

การติดตั้งสายระบบจำหน่าย 33 kV
บนโครงสร้างสายส่ง ระบบ 115 kV

33 kV DISTRIBUTION LINE INSTALLATION
ON 115 kV SUBTRANSMISSION POLE

ใช้แทนแบบ
ถูกแทนโดยแบบ
เขียนเสร็จวันที่ 27 ต.ค. 36
แก้แบบวันที่
มิติเป็น มิลลิเมตร
มาตราส่วน 1 : 50

แบบเลขที่ SA4-015/36016
แผ่นที่ 3 ของจำนวน 5 แผ่น

การประกอบเลขที่
ASSEMBLY NO. 3240

บัญชีวัสดุ
BILL OF MATERIAL

ลำดับที่ ITEM	รายละเอียด DESCRIPTION	จำนวน REQ'D I	II	III	IV	วัสดุเลขที่ MAT. NO.
1	คอน คอร. สปัน ขนาด 120 X 120 X 3,000 มม. CROSSARM, SPUN, PRESTRESSED CONCRETE 120 X 120 X 3,000 mm	1	2	–	–	00110002 (0104)
2	คอน คอร. สปัน ขนาด 120 X 120 X 2,500 มม. CROSSARM, SPUN, PRESTRESSED CONCRETE 120 X 120 X 2,500 mm	–	–	2	4	00110004 (0196)
3	เหล็กประกับคอน ขนาด 30 X 6 X 760 มม. BRACE, FLAT, FOR CROSSARM, 30 X 6 X 760 mm	2	2	2	4	01200001 (0120)
4	สลักเกลียว M 16 X 170 มม. BOLT, MACHINE M 16 X 170 mm	3	4	2	3	01110201 (0221)
5	สลักเกลียว M 16 X 400 มม. BOLT, MACHINE M 16 X 400 mm	1	1	1	2	01110206 (0226)
6	สลักเกลียว M 16 X 500 มม. BOLT, MACHINE M 16 X 500 mm	1	–	–	–	01110208 (0228)
7	สลักเกลียวตลอด M 16 X 650 มม. BOLT, DOUBLE ARMING, M 16 X 650 mm	–	3	1	–	
8	สลักเกลียวห่วงกลม M 16 X 650 มม. BOLT, DOUBLE ARMING, ROUND EYE, M 16 X 650 mm	–	–	3	7	
9	แหวนสี่เหลี่ยมแบน 52 X 52 X 4.5 มม. รู Ø 18 มม. มอก. 258 WASHER, SQUARE, FLAT 52 X 52 X 4.5 mm, HOLE Ø 18 mm TIS 258	6	20	19	29	01180100 (0355)
10	แหวนสี่เหลี่ยมโค้ง 60 X 60 X 5 มม. รู Ø 22 มม. WASHER, SQUARE, CURVED 60 X 60 X 5 mm, HOLE Ø 22 mm	3	6	3	6	01180201 (0361)
11	แหวนสปริง M 16 มอก. 259 WASHER, LOCK, M 16 TIS 259	2	3	2	2	01180301 (0365)
12	กายทิมเบิ้ล สำหรับสายยึดโยง 50 – 95 ต.มม. THIMBLE, GUY, FOR STEEL WIRE 50 – 95 mm^2	–	–	–	2	01210304 (0150)
13	นัทรูปห่วง M 16 DIN 582 NUT EYE M 16 DIN 582	–	–	3	7	01180001 (0345)
14	ยูแคล้มป์ สลัก 1 ตัว M 8 (ไวร์ โร้ป คลิ๊ฟ) CLAMP, SINGLE U-BOLT M 8 (WIRE ROPE CLIP)	1	1	1	8	01230000 (0165)
15	ลูกถ้วยก้านตรง 33 kV มอก. 279 แบบ ค (แบบ 56-3) INSULATOR, PIN TYPE, 33 kV TIS 279 TYPE C (CLASS 56-3) COMP. WITH PIN	3	6	3	6	03000002 03100001
16	ลูกถ้วยแขวน มอก. 354 แบบ ง (แบบ 52-4) INSULATOR, SUSPENSION TYPE, TIS 354 TYPE D (CLASS 52-4)	–	–	18	36	03020002 (0415)

กองวิศวกรรมไฟฟ้าและเครื่องกล
ฝ่ายวิศวกรรม

ผู้เขียน
ผู้สำรวจ
วิศวกร
หัวหน้าแผนก
ผู้อำนวยการกอง
ผู้อำนวยการฝ่าย

รองผู้ว่าการฝ่ายเทคนิค

การไฟฟ้าส่วนภูมิภาค

ผู้ว่าการ 2536 ผวก.

การติดตั้งสายระบบจำหน่าย 33 kV
บนโครงสร้างสายส่ง ระบบ 115 kV

33 kV DISTRIBUTION LINE INSTALLATION
ON 115 kV SUBTRANSMISSION POLE

ใช้แทนแบบ
ถูกแทนโดยแบบ
เขียนเสร็จวันที่ 27 ต.ค. 36
แก้แบบวันที่
ผิดเป็น
มาตราส่วน

แบบเลขที่ SA4-015/36016
แผ่นที่ 4 ของจำนวน 5 แผ่น

2536

การประกอบเลขที่
ASSEMBLY NO. 3240

บัญชีวัสดุ
BILL OF MATERIAL

ลำดับที่ ITEM	รายละเอียด DESCRIPTION	จำนวน REQ'D I	 II	 III	 IV	วัสดุเลขที่ MAT. NO.
17	ลวดเหล็กกลม เส้นผ่านศูนย์กลาง 4 มม. เส้นเดียว (มอก. 71) น้ำหนักประมาณ 0.1 กก./ม. WIRE, STEEL SOLID, DIAMETER 4 mm (TIS 71) WEIGHT APPROX 0.1 kg/m	3.5 ม. m	6.5 ม. m	3 ม. m	6 ม. m	01100000 (0191)
18	ลวดเหล็กตีเกลียว 50/7 ต.มม. มอก. 404 ความยาวตามต้องการ WIRE, STEEL STRANDED 50/7 mm², TIS 404 LENGTH AS REQUIRED	ม. m	ม. m	ม. m	ม. m	01100004 (0183)
19	สายอะลูมิเนียมเปลือย ขนาด 95-185 ต.มม. มอก. 85 ความยาวตามต้องการ Al CONDUCTOR 95-185 mm², TIS 85 LENGTH AS REQUIRED	ม. m	ม. m	ม. m	ม. m	02010004 - 02010007
20	เคเบิลอากาศอะลูมิเนียม 33 kV ขนาดตามต้องการ CABLE, AERIAL Al 33 kV, SIZE AS REQUIRED	ม. m	ม. m	ม. m	ม. m	02050102 - 02050104
21	ลวดอะลูมิเนียมแบน 1 X 10 มม. ความยาวตามต้องการ TAPE, ARMOUR, Al 1 X 10 mm, LENGTH AS REQUIRED	ม. m	ม. m	ม. m	ม. m	02200000 (0700)
22	ลวดอะลูมิเนียมกลม 4 มม. ความยาวตามต้องการ TIE WIRE, Al 4 mm, LENGTH AS REQUIRED	ม. m	ม. m	ม. m	ม. m	02200002 (0704)
23	แคล้มป์แขวนเคเบิล และที่จับเคเบิลสเปเซอร์ หรือ กายแคล้มป์ สลัก 3 ตัว และห่วงแขวนเคเบิลสเปเซอร์ CLAMP, CABLE SUSPENSION AND CLEVIS, FLAT STEEL, FOR CABLE SPACER OR CLAMP, GUY, TRIPLE BOLT AND LINK CABLE SPACER	1	2	2	–	02440100 - 02440101 or 02440102 - 02440103
24	เคเบิลสเปเซอร์ 33 kV พร้อมห่วงรัดสาย ขนาดตามต้องการ CABLE SPACER, 33 kV COMP. WITH SNAPTIE SIZE AS REQUIRED	1	2	2	–	——
25	ทิมเบิลเคลวิส สำหรับปรีฟอร์มเข้าปลายสาย CLEVIS, THIMBLE, FOR PREFORMED DEADEND	–	–	–	6	03140011 (0482)
26	ปรีฟอร์มเข้าปลายสาย สำหรับเคเบิลอากาศอะลูมิเนียม ขนาดตามต้องการ PREFORMED DEADEND, FOR AERIAL CABLE Al SIZE AS REQUIRED	–	–	–	6	02260002 - 02260004
27	หลอดต่อสายชนิดบีบไม่รับแรงดึง สายอะลูมิเนียม ขนาด 95-185 ต.มม. ขนาดตามต้องการ CONNECTOR, SPLICE, COMPRESSION TYPE TENSIONLESS Al 95-185 mm² SIZE AS REQUIRED	–	–	3	6	02400004 - 02400008
28	เทปพันเคเบิลอากาศแรงสูง ELECTRICAL SPLICING TAPE, FOR AERIAL CABLE	–	–	–		02180003 (5903)
29	สเตรนแคล้มป์ สำหรับสายอะลูมิเนียม และอะลูมิเนียมแกนเหล็ก ขนาดตามต้องการ CLAMP, STRAIN, FOR Al AND ACSR SIZE AS REQUIRED	–	–	6	6	03110001 - 03110101
30	การประกอบสายยึดโยง GY-31 หรือ GY-32 ตามต้องการ GUY ASSEMBLY GY-31 OR GY-32 AS REQUIRED	–	–	1	2	——

กองวิศวกรรมไฟฟ้าและเครื่องกล
ฝ่ายวิศวกรรม

ผู้เขียน
ผู้สำรวจ
วิศวกร
หัวหน้าแผนก
ผู้อำนวยการกอง
ผู้อำนวยการฝ่าย

รองผู้ว่าการฝ่ายเทคนิค

การไฟฟ้าส่วนภูมิภาค

ผู้ว่าการ 27 S.A. 2536 ผวก.

การติดตั้งสายระบบจำหน่าย 33 kV
บนโครงสร้างสายส่ง ระบบ 115 kV

33 kV DISTRIBUTION LINE INSTALLATION
ON 115 kV SUBTRANSMISSION POLE

ใช้แทนแบบ
ถูกแทนโดยแบบ
เขียนเสร็จวันที่ 27 ต.ค. 36
แก้แบบวันที่
ผิดเป็น
มาตราส่วน

แบบเลขที่ SA4-015/36016
แผ่นที่ 5 ของจำนวน 5 แผ่น

27 S.A. 2536