การประกอบเลขที่ 3225
ASSEMBLY NO. 3225

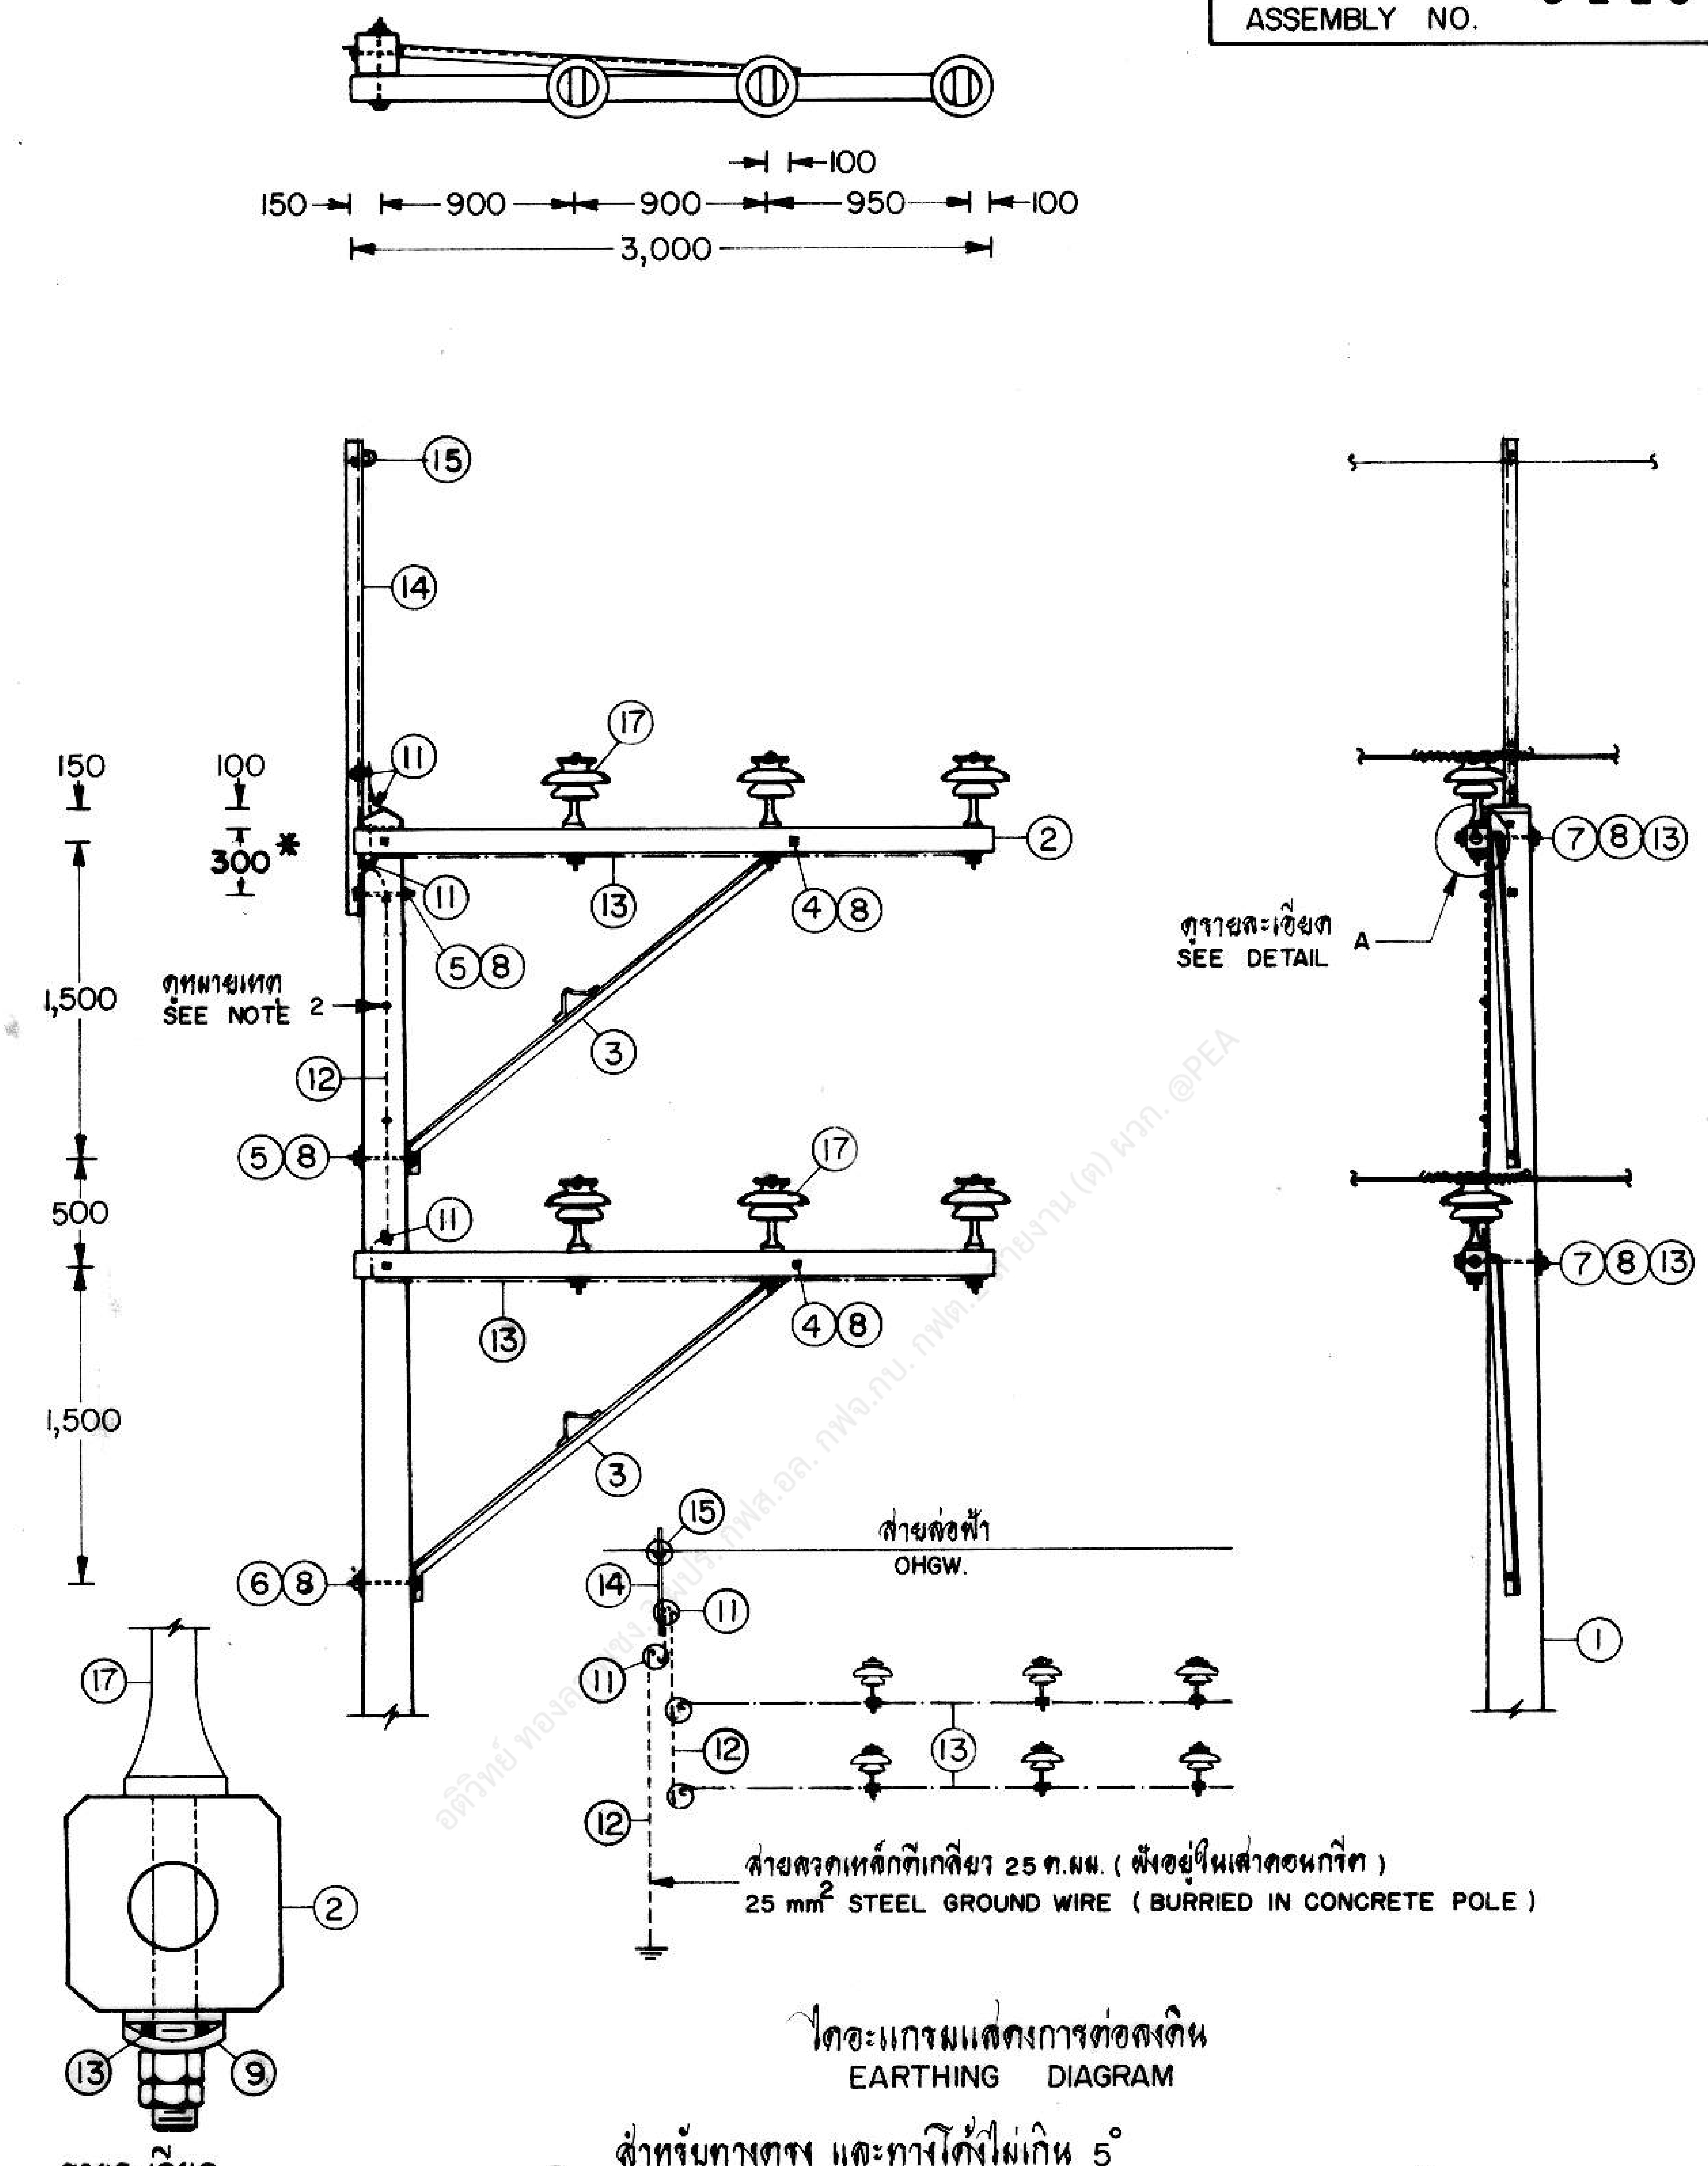

150
900
900
950
100
100
3,000
150
100
300*
1,500
500
1,500
ดูหมายเหตุ
SEE NOTE 2
15
14
11
11
58
12
58
11
68
17
2
13
48
3
17
13
48
3
ดูรายละเอียด
SEE DETAIL A
7 8 13
7 8 13
1
17
2
13
9
สายล่อฟ้า
OHGW.
15
14
11
11
12
13
12
สายลวดเหล็กตีเกลียว 25 ต.มม. (ฝังอยู่ในเสาคอนกรีต)
25 mm² STEEL GROUND WIRE (BURRIED IN CONCRETE POLE)

ไดอะแกรมแสดงการต่อลงดิน
EARTHING DIAGRAM

รายละเอียด A
DETAIL A

I สำหรับทางตรง และทางโค้งไม่เกิน 5°
FOR TANGENT AND LINE ANGLE NOT EXCEEDING 5°

กองวิศวกรรมไฟฟ้าและเครื่องกล
ฝ่ายวิศวกรรม

ผู้เขียน
ผู้สำรวจ
วิศวกร
หัวหน้าแผนก
ผู้อำนวยการกอง
ผู้อำนวยการฝ่าย

รองผู้ว่าการฝ่ายเทคนิค

- 1 ก.พ. 2526

การไฟฟ้าส่วนภูมิภาค

ผู้ว่าการ 9 ก.พ. 26

การประกอบคอน คอร.สปัน แบบท้าวแขน กับเสาคอนกรีต
ระบบ 33 kV 2 วงจร

SPUN PRESTRESSED CONCRETE ALLEY ARM ASSEMBLY
33 kV SYSTEM 2 CIRCUITS

ใช้แทนแบบ
ถูกแทนโดยแบบ
เขียนเสร็จวันที่ 12 ต.ค. 25
แก้แบบวันที่ 5 มี.ค. 34
มิติเป็น มม.
มาตราส่วน 1 : 50

แบบเลขที่ SAI-015/26003
แผ่นที่ 1 ของจำนวน 4 แผ่น

การประกอบเลขที่ 3225
ASSEMBLY NO. 3225

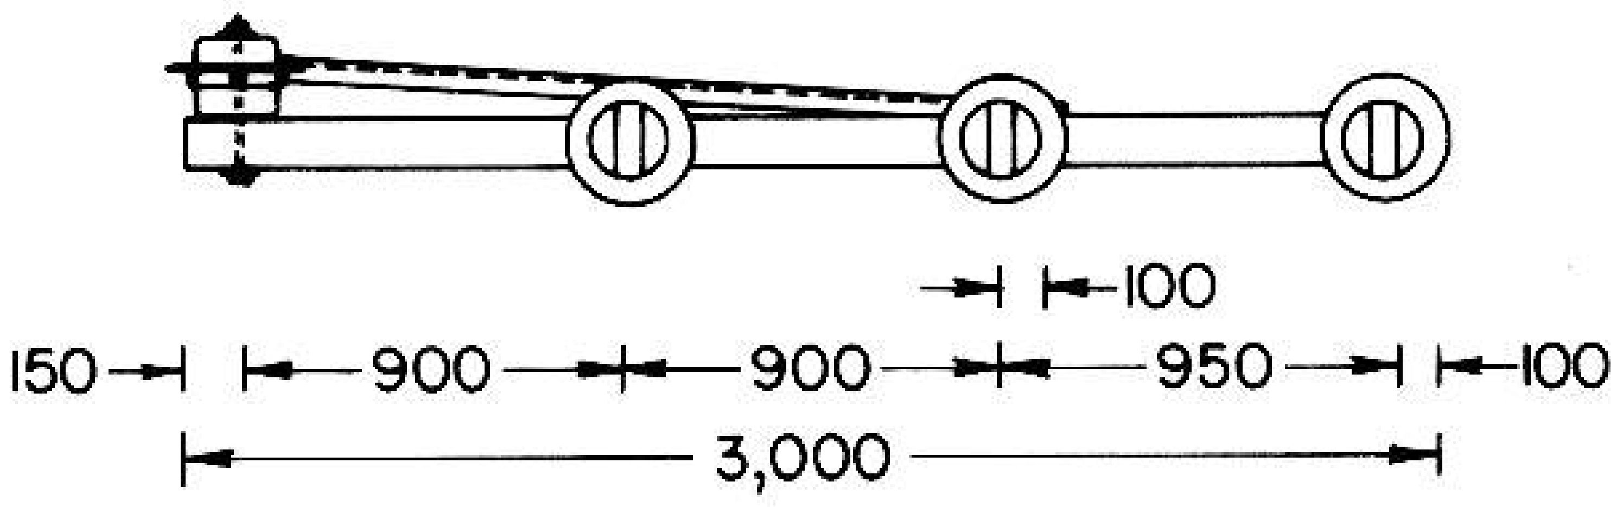

100
150
900
900
950
100
3,000

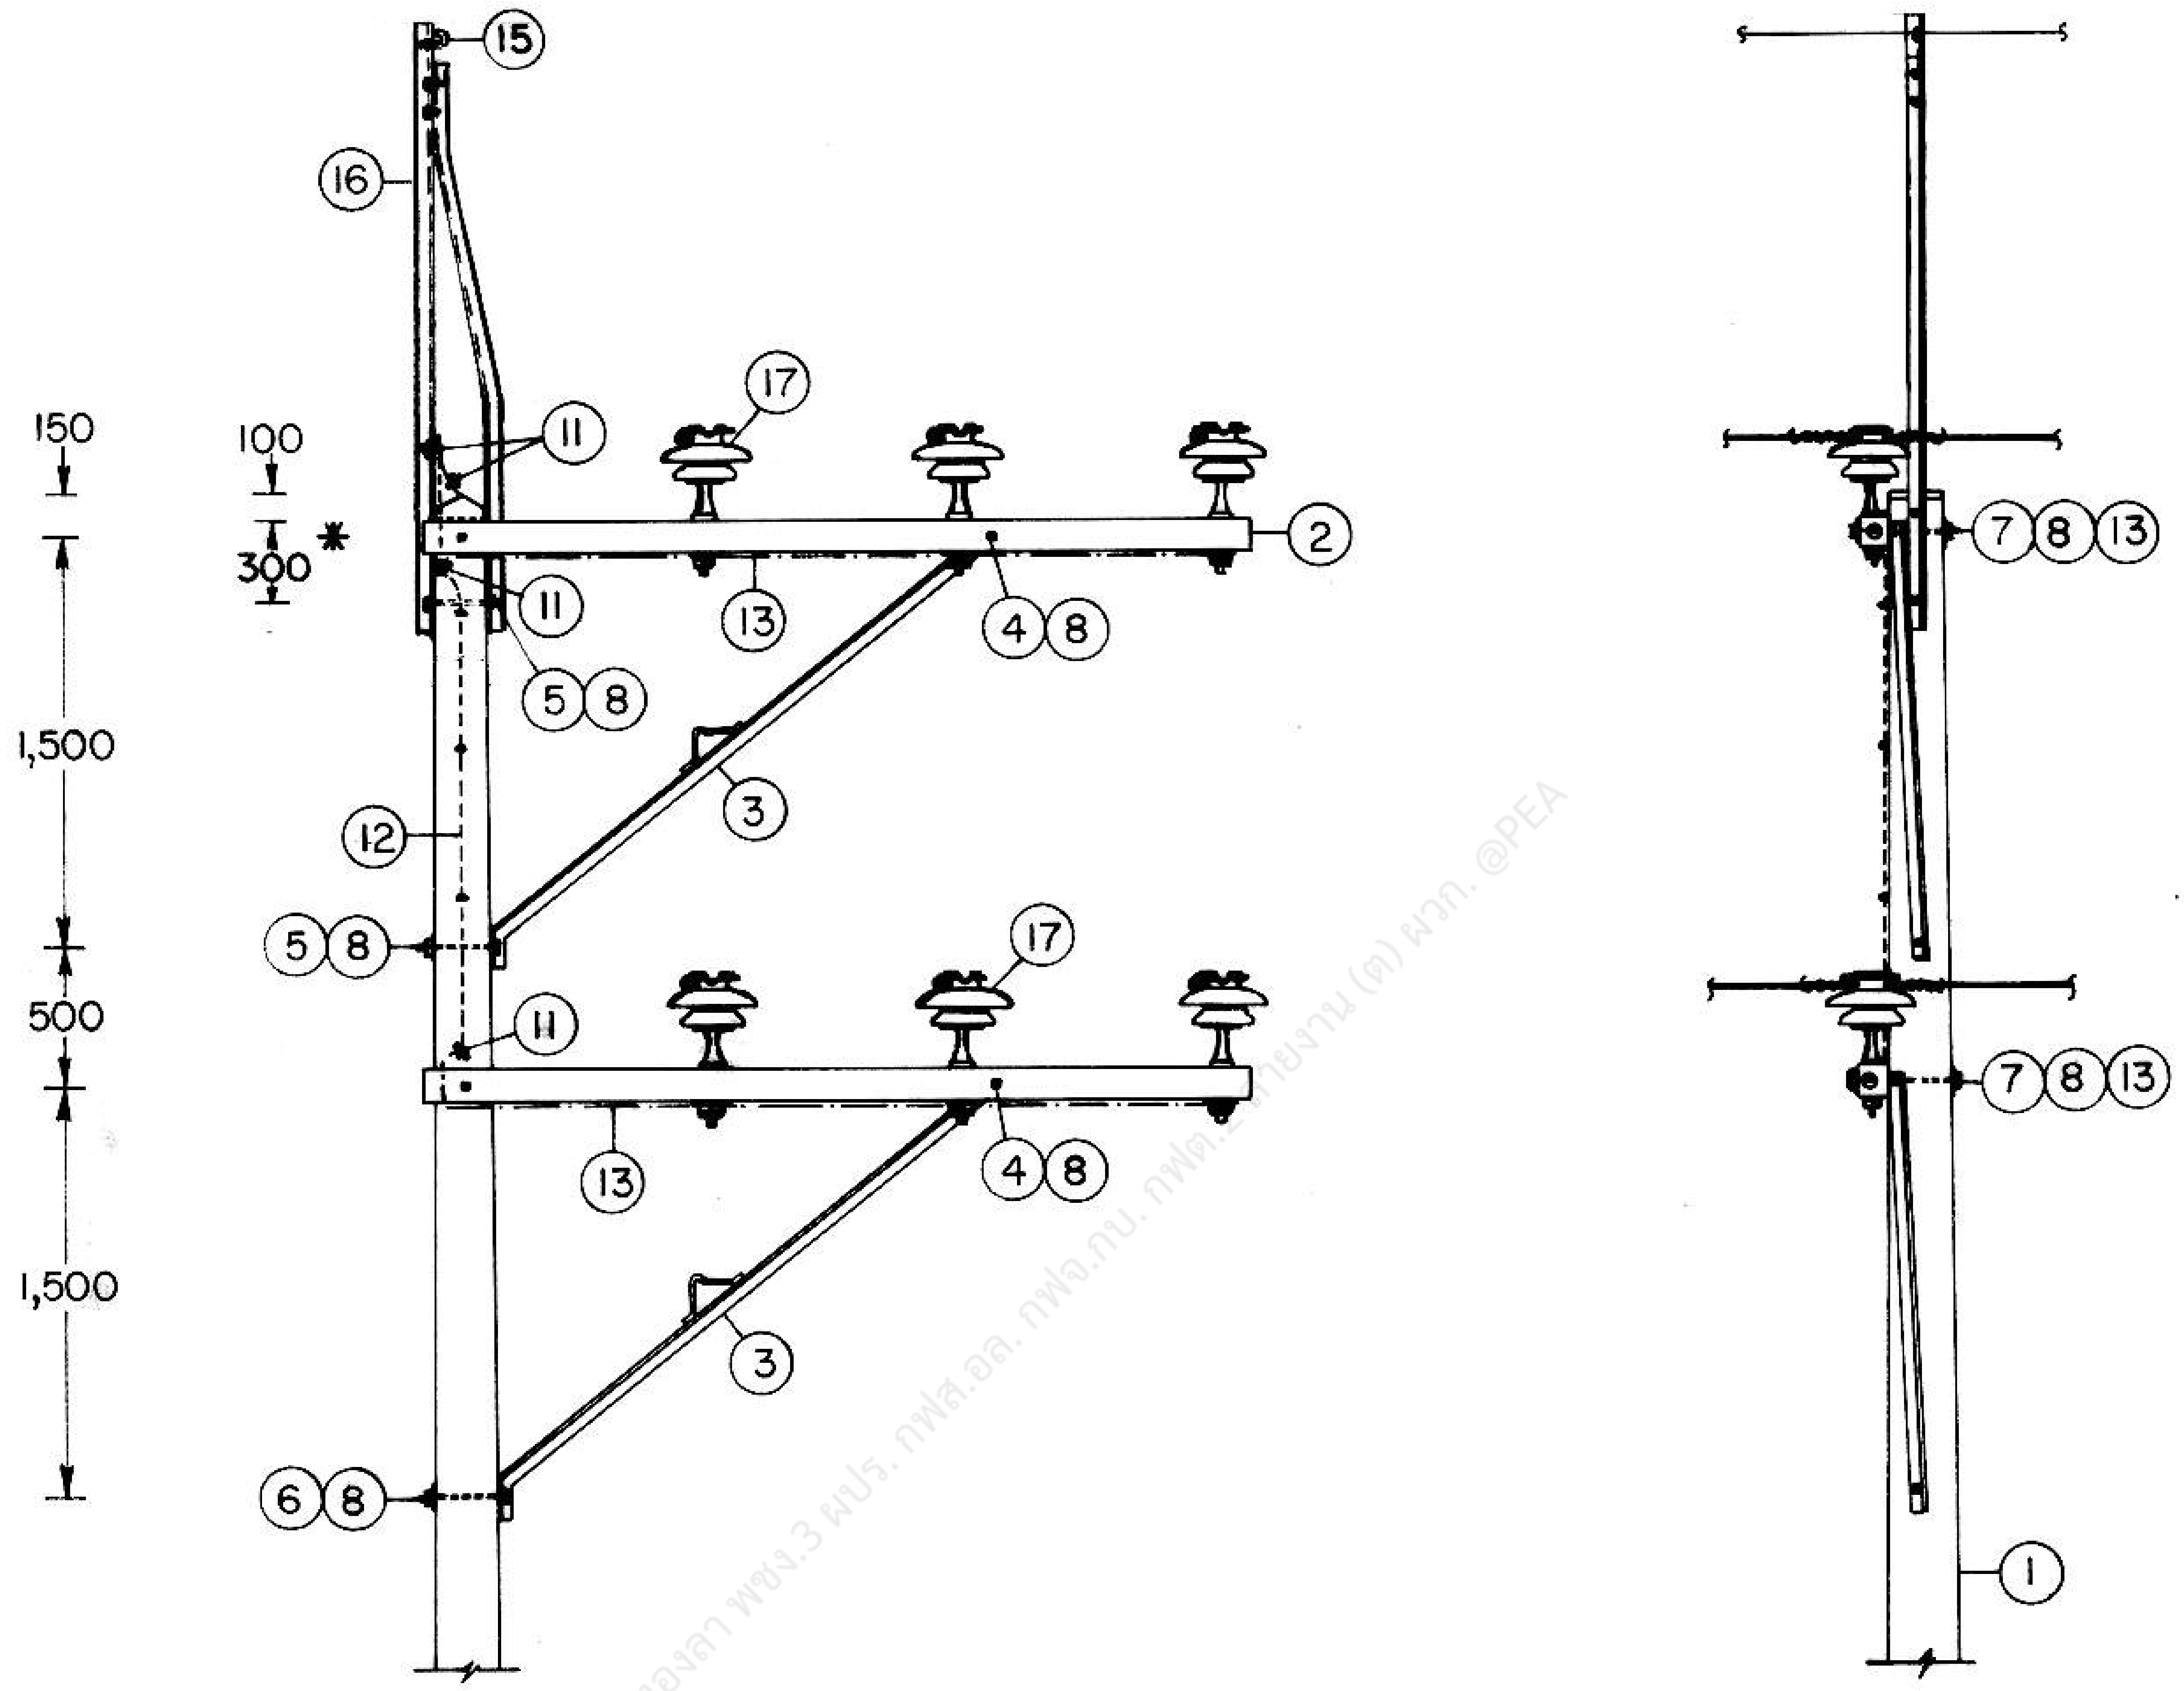

⑮
⑯
⑰
⑪
②
⑬
④⑧
⑤⑧
③
⑫
⑪
⑤⑧
⑪
⑰
⑬
④⑧
③
⑥⑧
⑦⑧⑬
⑦⑧⑬
①
150
100
300 *
1,500
500
1,500

II สำหรับทางโค้งไม่เกิน 30°
FOR LINE ANGLE NOT EXCEEDING 30°

อติวิทย์ ทองลา พชง.3 ผปร. กฟส.อล. กฟจ.กบ. กฟต.2 ฝ่ายงาน (ต) ผวก. @PEA

กองวิศวกรรมไฟฟ้าและเครื่องกล ฝ่ายวิศวกรรม	การไฟฟ้าส่วนภูมิภาค	ใช้แทนแบบ ถูกแทนโดยแบบ เขียนเสร็จวันที่ 12 ต.ค. 25
ผู้เขียน ผู้สำรวจ วิศวกร หัวหน้าแผนก ชัยรัตน์ ผู้อำนวยการกอง ผู้อำนวยการฝ่าย	ผู้ว่าการ ๙ ก.พ. 26	แก้แบบวันที่ 5 มี.ค. 34 มิติเป็น มม. มาตราส่วน 1 : 50
	การประกอบคอน คอร.สปัน แบบท้าวแขน กับเสาคอนกรีต ระบบ 33 kV 2 วงจร	
รองผู้ว่าการฝ่ายเทคนิค	SPUN PRESTRESSED CONCRETE ALLEY ARM ASSEMBLY 33 kV SYSTEM 2 CIRCUITS	แบบเลขที่ SAI-015/26003 แผ่นที่ 2 ของจำนวน 4 แผ่น

การประกอบเลขที่ ASSEMBLY NO. 3225

บัญชีวัสดุ
BILL OF MATERIAL

ลำดับที่ ITEM	รายละเอียด DESCRIPTION	จำนวน REQ'D		วัสดุเลขที่ MAT. NO.
		I	II	
1	เสาคอนกรีต 14 ม. POLE, CONCRETE 14 m LONG	1	1	00010006 (0036)
2	คอน คอร.สปัน ขนาด 120 X 120 X 3,000 มม. CROSSARM, SPUN, PRESTRESSED CONCRETE 120 X 120 X 3,000 mm	4	4	00110002 (0104)
3	เหล็กประกับไม้คอนแบบท้าวแขน 50 X 50 X 5 มม. ยาว 2,350 มม. BRACE, ALLEY ARM 50 X 50 X 5 mm, 2,350 mm LONG	2	2	01200005 (0125)
4	สลักเกลียว M 16 X 170 มม. BOLT, MACHINE, M 16 X 170 mm	2	2	01110201 (0221)
5	สลักเกลียว M 16 X 250 มม. BOLT, MACHINE, M 16 X 250 mm	3	3	01110203 (0223)
6	สลักเกลียว M 16 X 300 มม. BOLT, MACHINE, M 16 X 300 mm	1	1	01110204 (0224)
7	สลักเกลียว M 16 X 350 มม. BOLT, MACHINE, M 16 X 350 mm	2	2	01110205 (0225)
8	แหวนสี่เหลี่ยมแบน 52 X 52 X 4.5 มม. รู Ø 18 มม. มอก. 258 WASHER, SQUARE, FLAT 52 X 52 X 4.5 mm HOLE Ø 18 mm TIS. 258	10	8	01180100 (0355)
9	แหวนสี่เหลี่ยมโค้ง 60 X 60 X 5 มม. รู Ø 22 มม. WASHER, SQUARE, CURVED 60 X 60 X 5 mm HOLE Ø 22 mm	6	6	01180200 (0361)
10	แหวนสปริง ขนาด 16 มม. มอก. 259 WASHER, LOCK, SPRING, 16 mm, TIS 259	2	2	01180301 (0365)
11	ยูแคล้มป์ สลัก 1 ตัว M 8 CLAMP, SINGLE U-BOLT, M 8	4	4	01230000 (0165)
12	ลวดเหล็กตีเกลียว 25 ต.มม. มอก. 404 STEEL STRANDED WIRE 25 mm^2 TIS 404	2.5 ม. m	2.5 ม. m	01100002 (0181)
13	ลวดเหล็กกลม เส้นผ่าศูนย์กลาง 4 มม. เส้นเดียว มอก. 71 นน.ประมาณ 0.1 กก./ม. WIRE, STEEL, SOLID, DIAMETER 4 mm TIS 71 WEIGHT APPROX. 0.1 kg/m	6 ม. m	6 ม. m	01100000 (0191)
14	เหล็กฉากรับสายล่อฟ้า 65 X 65 X 6 มม. ยาว 2,250 มม. OVERHEAD GROUND WIRE BAYONET 65 X 65 X 6 mm, 2,250 mm LONG	1	–	01010003 (6010)
15	กราวด์วายร์แคล้มป์ แบบ J 1152 GROUND WIRE CLAMP, J 1152	1	1	01230205 (0296)
16	เหล็กฉากรับสายล่อฟ้าทางโค้ง พร้อมสลักเกลียว M 12 X 35 มม. และแหวนสปริง วัสดุเลขที่ 0212 และ 0346 จำนวน 2 ชุด OVERHEAD GROUND WIRE CORNER BAYONET COMP. WITH 2 SETS OF 12 X 35 mm BOLT AND SPRING WASHER MAT. NO. 0212 AND 0346	–	1	01010002 (6011)
17	ลูกถ้วยก้านตรง 33 kV แบบ ค (แบบ 56-3) มอก. 279 พร้อมก้าน INSULATOR, PIN TYPE, 33 kV TYPE C (CLASS 56-3) TIS 279 COMP. WITH PIN	6	6	03000002 03100001

กองวิศวกรรมไฟฟ้า และเครื่องกล ฝ่ายวิศวกรรม	**การไฟฟ้าส่วนภูมิภาค**	ใช้แทนแบบ ถูกแทนโดยแบบ
ผู้เขียน ผู้สำรวจ วิศวกร หัวหน้าแผนก ผู้อำนวยการกอง ผู้อำนวยการฝ่าย	ผู้ว่าการ 9 ก.พ. 26	เขียนเสร็จวันที่ 12 ต.ค. 25 แก้แบบวันที่ 5 มี.ค. 34
	การประกอบคอน คอร.สปัน แบบท้าวแขน กับเสาคอนกรีต ระบบ 33 kV 2 วงจร	มิติเป็น มาตราส่วน
รองผู้ว่าการฝ่ายเทคนิค	SPUN PRESTRESSED CONCRETE ALLEY ARM ASSEMBLY 33 kV SYSTEM 2 CIRCUITS	แบบเลขที่ SAI-015/26003 แผ่นที่ 3 ของจำนวน 4 แผ่น

ก.พ. 2526

กฟต.2 สายงาน (ต) ผวก. ©PEA

การประกอบเลขที่ 3225
ASSEMBLY NO.

หมายเหตุ

1. การดัดโค้งสายดินลวดเหล็กเส้นเดียว ø 4 มม. ต่อระหว่างก้านลูกถ้วย ประกอบที่คอน คอร. สปัน ; ดูรายละเอียดแบบเลขที่ SAI-015/21022 (การประกอบเลขที่ 3804)
2. การยึดสายลวดเหล็กกับเสาคอนกรีต ; ดูรายละเอียดแบบเลขที่ S02-015/19166 และ SAI-015/31012 (การประกอบเลขที่ 9703 และ 9703 A)
3. โครงสร้างเสา และข้อกำหนดการใช้งาน ; ดูรายละเอียดแบบเลขที่ IBI-015/34091 (การประกอบเลขที่ 8276)
4. หลักเกณฑ์การใช้ลูกถ้วยแรงสูงในบริเวณใกล้ฝั่งทะเล ; ดูรายละเอียดแบบเลขที่ SAI-015/24019 (การประกอบเลขที่ 9502)
5. * กรณีใช้เหล็กฉากรับสายล่อฟ้า วัสดุเลขที่ 0128 หรือ 0129 ให้ใช้ระยะการยึดกับเสาเป็นระยะ 500 มม.

NOTES

1. THE ARRANGEMENT OF ø 4 mm GALVANIZED STEEL WIRE BOND BETWEEN INSULATOR PINS; SEE DETAIL DWG. NO. SAI-015/21022 (ASSEMBLY NO. 3804).
2. GROUND FITTING ON CONCRETE POLE; SEE DETAIL DWG. NO. S02-015/19166 AND SAI-015/31012 (ASSEMBLY NO. 9703 AND 9703A).
3. POLE STRUCTURE AND RECOMMENDATION; SEE DETAIL DWG. NO. IBI-015/34091 (ASSEMBLY NO. 8276)
4. RECOMMENDATION FOR H.V. INSULATOR INSTALLATION NEAR THE SEA COAST ; SEE DETAIL IN DWG. NO. SAI-015/24019 (ASSEMBLY NO. 9502).
5. * IN CASE OF USE OVERHEAD GROUND WIRE BAYONET MATERIAL NO. 0128 OR 0129, THE DISTANCE FOR FITTING ON POLE SHALL BE 500 mm .

กองวิศวกรรมไฟฟ้าและเครื่องกล
ฝ่ายวิศวกรรม

ผู้เขียน
ผู้สำรวจ
วิศวกร
หัวหน้าแผนก
ผู้อำนวยการกอง
ผู้อำนวยการฝ่าย

รองผู้ว่าการฝ่ายเทคนิค

การไฟฟ้าส่วนภูมิภาค

ผู้ว่าการ 9 ก.พ. 26

การประกอบคอน คอร.สปัน แบบท้าวแขน กับเสาคอนกรีต
ระบบ 33 kV 2 วงจร

SPUN PRESTRESSED CONCRETE ALLEY ARM ASSEMBLY
33 kV SYSTEM 2 CIRCUITS

ใช้แทนแบบ
ถูกแทนโดยแบบ
เขียนเสร็จวันที่ 12 ต.ค. 25
แก้แบบวันที่ 5 มี.ค. 34
17 ต.ค. 34
มิติเป็น
มาตราส่วน

แบบเลขที่ SAI-015/26003
แผ่นที่ 4 จากจำนวน 4 แผ่น

1 ก.พ. 2526