การประกอบเลขที่
ASSEMBLY NO. **5220**

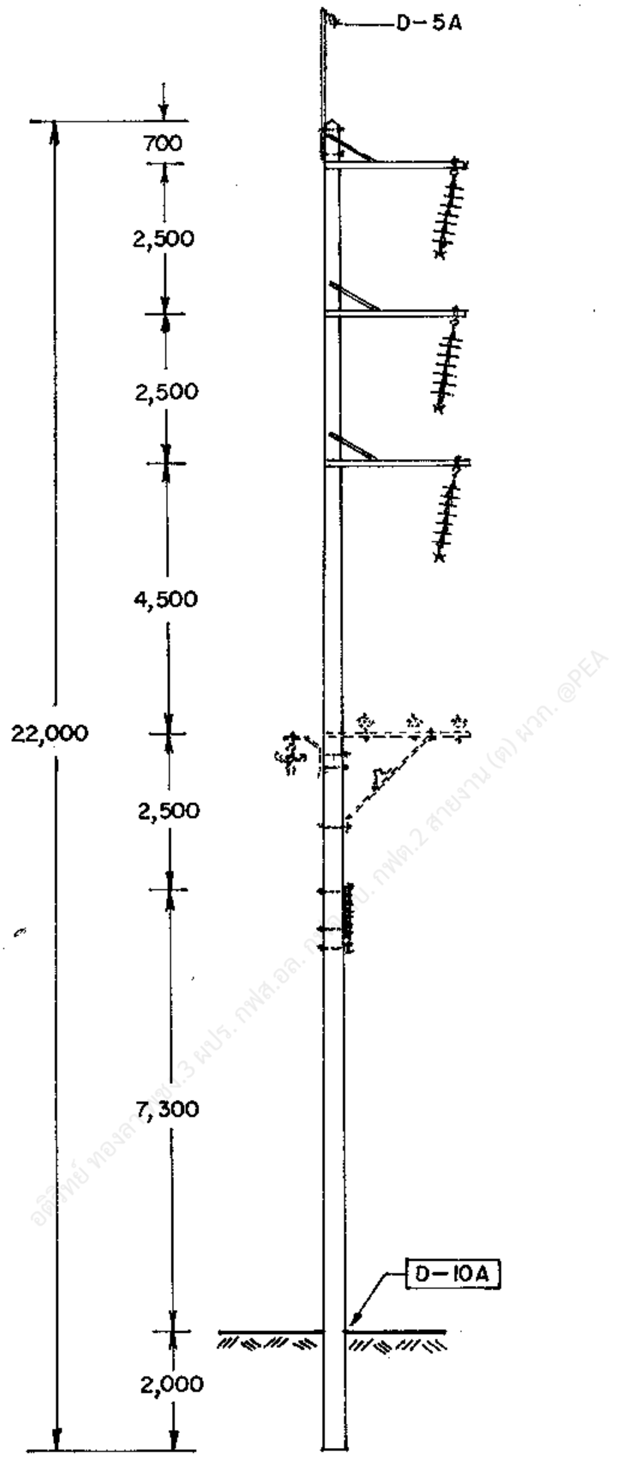

กองวิศวกรรมไฟฟ้าและเครื่องกล
ฝ่ายวิศวกรรม

ผู้เขียน
ผู้ตรวจ
วิศวกร
หัวหน้าแผนก
ผู้อำนวยการกอง
ผู้อำนวยการฝ่าย

รองผู้ว่าการ

การไฟฟ้าส่วนภูมิภาค

ผู้ว่าการ
2 8 ต.ค. 2539

115 kV วงจรเดี่ยว สายไฟฟ้าเดี่ยว
เสาต้นทางตรง ก่อนเสาต้นเข้าปลายสาย
แบบ SS-TG-5

115 kV SINGLE-CIRCUIT SINGLE-CONDUCTOR
TANGENT STRUCTURE, ADJACENT TO DEADEND POLE
TYPE SS-TG-5

ใช้แทนแบบ
ถูกแทนโดยแบบ
เขียนเสร็จวันที่ 5 ก.ย. 39
แก้แบบวันที่
หน่วยเป็น มิลลิเมตร
มาตราส่วน 1 : 125
แบบเลขที่ SAI-015/39014
แผ่นที่ 1 ของจำนวน 3 แผ่น

2 8 ต.ค. 2539

การประกอบเลขที่
ASSEMBLY NO. **5220**

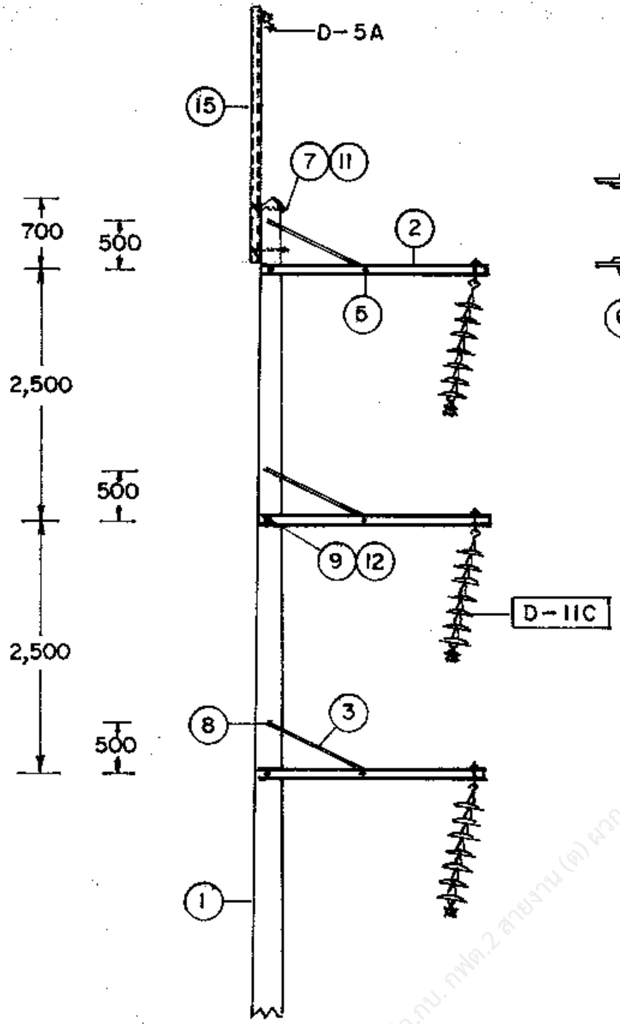

SS – TG – 5

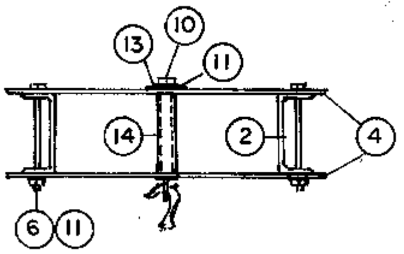

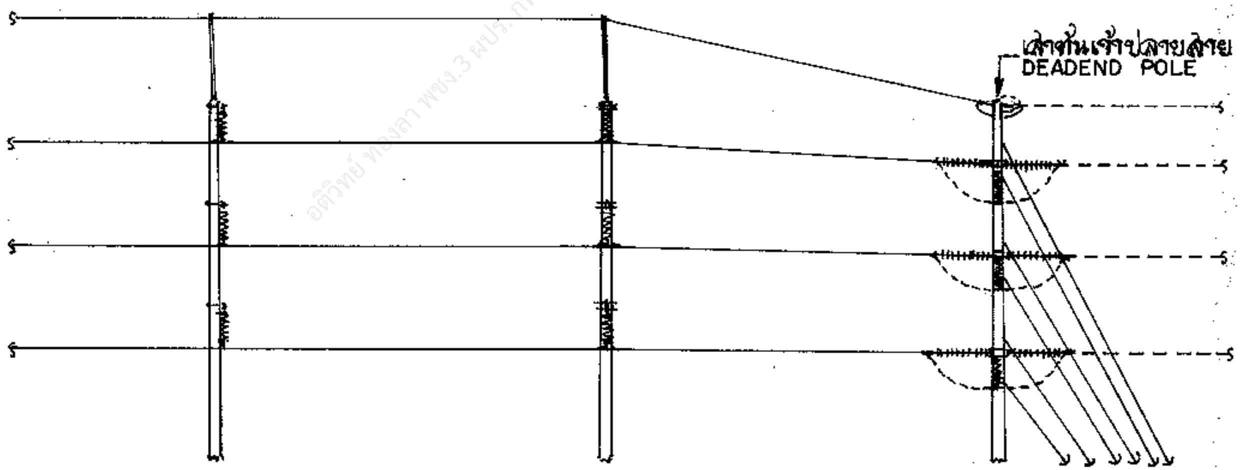

SS-TG-2

SS-TG-5

กองวิศวกรรมไฟฟ้าและเครื่องกล ฝ่ายวิศวกรรม	# การไฟฟ้าส่วนภูมิภาค	ใช้แทนแบบ .... ถูกแทนโดยแบบ ....
ผู้เขียน .... ผู้ตรวจ .... วิศวกร .... หัวหน้าแผนก .... ผู้อำนวยการกอง .... ผู้อำนวยการฝ่าย	**ผู้ว่าการ** .... 115 kV วงจรเดี่ยว สายไฟฟ้าเดี่ยว เสาต้นทางตรง ก่อนเสาต้นเจ้าปลายสาย แบบ SS – TG – 5	เขียนเสร็จวันที่ 5 ก.ย. 39 แก้แบบวันที่ .... วัดเป็น มิลลิเมตร มาตราส่วน 1 : 75
รองผู้ว่าการ	115 kV SINGLE – CIRCUIT SINGLE – CONDUCTOR TANGENT STRUCTURE, ADJACENT TO DEADEND POLE TYPE SS – TG – 5	แบบเลขที่ SAI-015/39014 แผ่นที่ 2 ของจำนวน 3 แผ่น

การประกอบเลขที่ **5220**
ASSEMBLY NO.

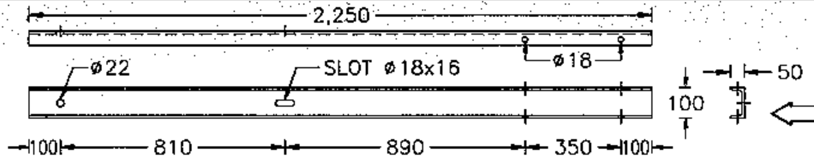

วัสดุลำดับที่ ②
MATERIAL ITEM

บัญชีวัสดุ
BILL OF MATERIAL

ลำดับที่ ITEM	รายละเอียด DESCRIPTION	จำนวน REQ'D	วัสดุเลขที่ MAT. NO.
1	เสาคอนกรีต 22 เมตร POLE, CONCRETE, 22 m LONG	1	0041 00010011
2	คอนเหล็กแบบท้าวแขนขนาด [100x50x5 มม. ยาว 2.25 ม. มอก. 116 STEEL ALLEY ARM, [100x50x5 mm., 2.25 m.LONG, TIS 116	6	6012 01000100
3	เหล็กประกับคอน ขนาด 40x6 มม. ยาว 1,000 มม. BRACE, FLAT, FOR CROSSARM 40x6x1,000 mm	6	0121 01200002
4	แผ่นเหล็ก ขนาด 6x100x450 มม. PLATE, STEEL 6x100x450 mm	6	0143 01030002
5	สลักเกลียวหัวหกเหลี่ยม เอ็ม 16x75 มม. พร้อมแหวนกลม 2 อัน BOLT, MACHINE, HEXAGON, M.16x75 mm, COMPLETE WITH 2 ROUND WASHERS	6	0236 01110400
6	สลักเกลียว เอ็ม 16x170 มม. BOLT, MACHINE M.16x170 mm	3	0221 01110201
7	สลักเกลียว เอ็ม 16x300 มม. BOLT, MACHINE M.16x300 mm	2	0224 01110204
8	สลักเกลียว เอ็ม 16x350 มม. BOLT, MACHINE M.16x350 mm	3	0225 01110205
9	สลักเกลียว เอ็ม 20x350 มม. BOLT, MACHINE M.20x350 mm	3	0232 01110300
10	สลักห่วงโอเวล เอ็ม 16x150 มม. BOLT, OVAL EYE M.16x150 mm	3	0257 01150000
11	แหวนรองแบบเรียบ ประเภทจัตุรัสขนาดใหญ่ 52x52x4.5 มม เส้นผ่านศูนย์กลางรู 18 มม มอก. 258 WASHER, PLAIN, SQUARE, LARGE 52x52x4.5 mm HOLE DIA. 18 mm TIS 258	20	0355 01180100
12	แหวนรองแบบเรียบ ประเภทจัตุรัสขนาดใหญ่ 62x62x6 มม เส้นผ่านศูนย์กลางรู 22 มม มอก. 258 WASHER, PLAIN, SQUARE, LARGE 62x62x6 mm HOLE DIA. 22 mm TIS 258	6	0356 01180101
13	แหวนรองแบบสปริง ขนาดระบุ 16 มม. ประเภทใช้งานทั่วไป มอก. 259 WASHER, LOCK, SPRING, SIZE 16 mm, GENERAL PURPOSE, TIS 259	3	0365 01180301
14	ท่อเหล็กขนาดระบุ 20 ประเภทที่ 2 ยาว 100 มม. มอก.277 แต่ไม่มีเกลียวที่ปลาย PIPE,STEEL,SIZE 20,TYPE 2,100 mm. LONG TIS.277 BUT WITHOUT THREADED END	3	0905 01050000
15	เหล็กฉาก รับสายล่อฟ้าทางโค้ง 65x65x6 มม. ยาว 2,500 มม. STEEL ANGLE, OVERHEAD GROUND WIRE CORNER BAYONET 65x65x6 mm 2,500 mm LONG	1	0135 01010004

	รายละเอียด DESCRIPTION		การประกอบเลขที่ ASSEMBLY NO.
D-11C	การประกอบลูกถ้วยแขวน SUSPENSION INSULATOR ASSEMBLY	3	5605
D-5A	การต่อสายล่อฟ้า OVERHEAD GROUND WIRE CONNECTOR	1	5626
D-10A	ฐานรากเสา POLE FOUNDATION	1	5661

กองวิศวกรรมไฟฟ้าและเครื่องกล
ฝ่ายวิศวกรรม

การไฟฟ้าส่วนภูมิภาค

ใช้แทนแบบ ....
ถูกแทนโดยแบบ ....

ผู้เขียน วิสุทธิ์ ชื่อเพราะ
ผู้สำรวจ ....
วิศวกร
หัวหน้าแผนก
ผู้อำนวยการกอง
ผู้อำนวยการฝ่าย

ผู้ว่าการ ....

เขียนเสร็จวันที่ 5 ก.ย. 39
แก้แบบวันที่ ....
มิติเป็น ....
มาตราส่วน ....

115 kV วงจรเดี่ยว สายไฟฟ้าเดี่ยว
เสาต้นทางตรงก่อนเสาต้นเข้าปลายสาย
แบบ SS-TG-5

รองผู้ว่าการ

115 kV SINGLE-CIRCUIT SINGLE CONDUCTOR
TANGENT STRUCTURE,ADJACENT TO DEADEND POLE
TYPE SS-TG-5

แบบเลขที่ SA1-015/39014

แผ่นที่ 3 ของจำนวน 3 แผ่น