การประกอบเลขที่
ASSEMBLY NO. 5253

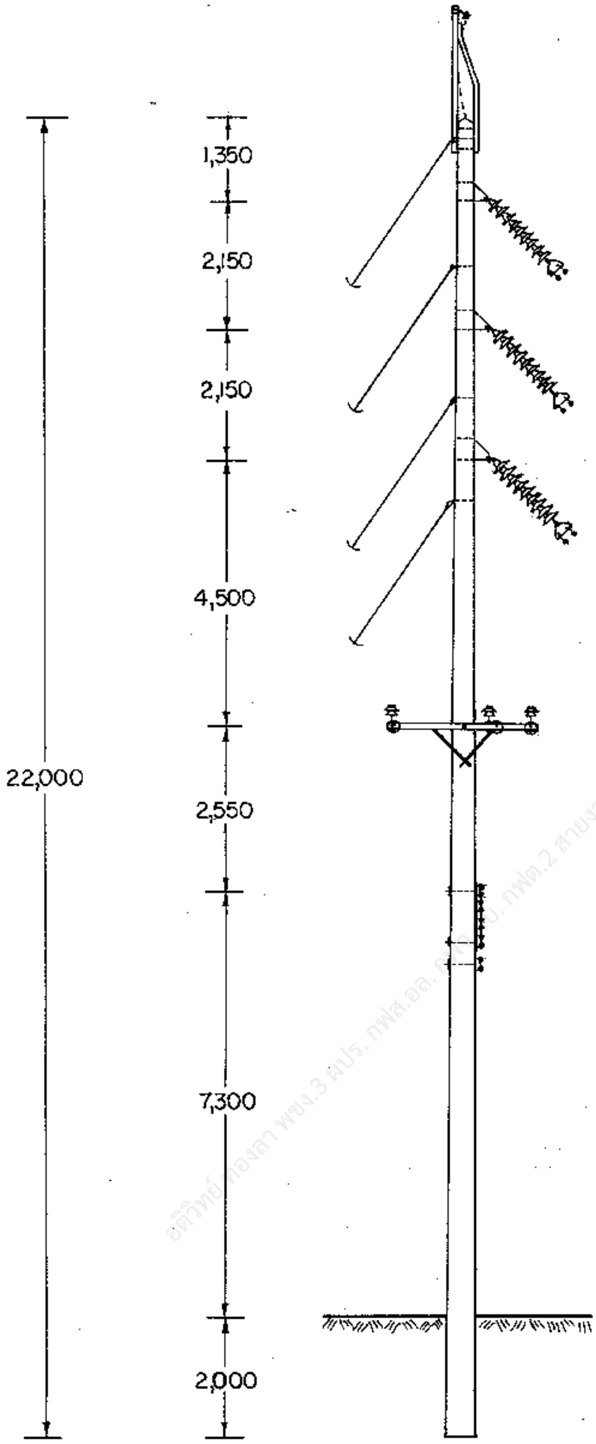

อติวิทย์ ทองลา พชง.3 ผปร. กฟส.อล. [illegible] กฟต.2 สายงาน (ต) ผวก. @PEA

กองวิศวกรรมไฟฟ้าและเครื่องกล ฝ่ายวิศวกรรม	การไฟฟ้าส่วนภูมิภาค	ใช้แทนแบบ ถูกแทนโดยแบบ
ผู้เขียน ผู้สำรวจ วิศวกร หัวหน้าแผนก หัวหน้ากอง ผู้อำนวยการฝ่าย	ผู้ว่าการ 24 มี.ค. 23	เขียนเสร็จวันที่ 2 ม.ค. 23 แก้แบบวันที่ มิติเป็น มม. มาตราส่วน 1 : 125
	115 kV วงจรเดี่ยว สายไฟฟ้าคู่ เสาสำหรับทางโค้ง แบบ SD-MA-1	
รองผู้ว่าการฝ่ายเทคนิค 23	115 kV SINGLE CIRCUIT DOUBLE CONDUCTOR MEDIUM ANGLE STRUCTURE TYPE SD-MA-1	แบบเลขที่ SAI-015/23007 แผ่นที่ 1 ของจำนวน 3 แผ่น

19 มี.ค. 2523

การประกอบเลขที่ ASSEMBLY NO. 5253

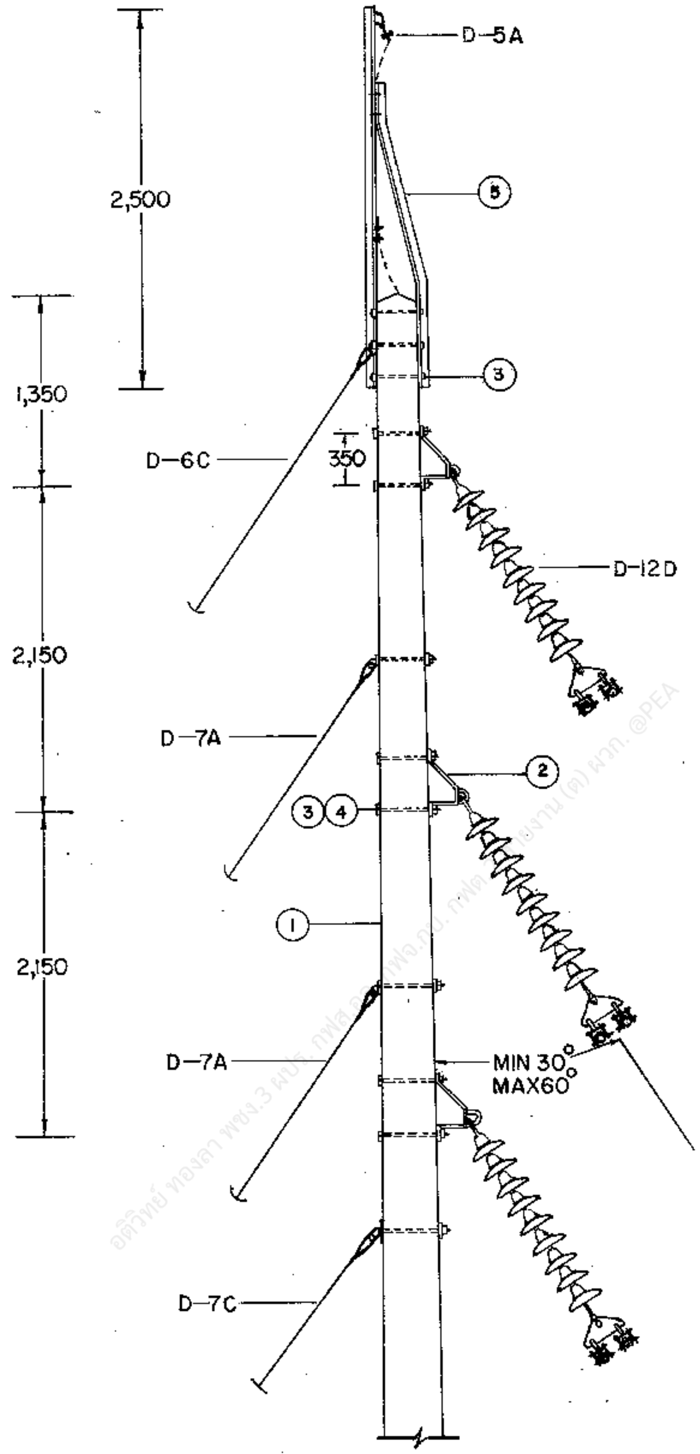

กองวิศวกรรมไฟฟ้าและเครื่องกล
ฝ่ายวิศวกรรม

ผู้เขียน
ผู้ตรวจ
วิศวกร
หัวหน้าแผนก
หัวหน้ากอง
ผู้อำนวยการฝ่าย
รองผู้ว่าการฝ่ายเทคนิค

19 มี.ค. 2523

การไฟฟ้าส่วนภูมิภาค

ผู้ว่าการ 24 มี.ค. 23

115 kV วงจรเดี่ยว สายไฟฟ้าคู่
เสาสำหรับทางโค้ง
แบบ SD-MA-1

115 kV SINGLE CIRCUIT DOUBLE CONDUCTOR
MEDIUM ANGLE STRUCTURE
TYPE SD-MA-1

ใช้แทนแบบ
ถูกแทนโดยแบบ
เขียนเสร็จวันที่ 2 ม.ค.23
แก้แบบวันที่ 15 ก.ย.40
มิติเป็น มม.
มาตราส่วน 1 : 50

แบบเลขที่ SAI-015/23007
แผ่นที่ 2 ของจำนวน 3 แผ่น

การประกอบเลขที่
ASSEMBLY NO. 5253

บัญชีวัสดุ
BILL OF MATERIAL

ลำดับที่ ITEM	รายละเอียด DESCRIPTION	จำนวน REQ'D	วัสดุเลขที่ MAT. NO.
1	เสาคอนกรีต 22 ม. POLE, CONCRETE 22 m. LONG	1	00010011 (0041)
2	ที่แขวนลูกถ้วยทางโค้ง BRACKET, CORNER SUSPENSION	3	03140012 (0489)
3	สลักเกลียว M 16 X 350 มม. BOLT, MACHINE, M 16 X 350 mm	8	01110205 (0225)
4	แหวนสี่เหลี่ยมแบน 52X52X4.5 มม. รู Ø 18 มม. มอก. 258 WASHER, SQUARE, FLAT 52X52X4.5 mm, HOLE Ø 18 mm, TIS 258	6	01180100 (0355)
5	เหล็กฉากรับสายล่อฟ้าทางโค้ง OVERHEAD GROUND WIRE CORNER BAYONET	1	01010005 (0136)

รายละเอียด
DETAIL

D-12D	การประกอบลูกถ้วยแขวน SUSPENSION INSULATOR ASSEMBLY	3	
D-5A	การต่อสายล่อฟ้า OVERHEAD GROUND WIRE CONNECTION	1	
D-6C	การประกอบสายยึดโยงลวดเหล็กตีเกลียว 50 ต.มม. STEEL STRANDED WIRE 50 mm² GUY ASSEMBLY	1	
D-7A	การประกอบสายยึดโยงลวดเหล็กตีเกลียว 95 ต.มม. STEEL STRANDED WIRE 95 mm² GUY ASSEMBLY	2	
D-7C	การประกอบสายยึดโยงลวดเหล็กตีเกลียว 95 ต.มม. STEEL STRANDED WIRE 95 mm² GUY ASSEMBLY	1	
D-9C	สมอบกคอนกรีต CONCRETE ANCHOR	1	
D-10A	ฐานรากเสา POLE FOUNDATION	1	

อดิวิทย์ ทองลา พชง.3 ผบร. กฟส.อล. [illegible] กบ. กฟต.2 สายงาน (ต) ผวก. @PEA

กองวิศวกรรมไฟฟ้าและเครื่องกล ฝ่ายวิศวกรรม	การไฟฟ้าส่วนภูมิภาค	ใช้แทนแบบ.......... ถูกแทนโดยแบบ..........
ผู้เขียน.......... ผู้ตรวจ.......... วิศวกร.......... หัวหน้าแผนก.......... หัวหน้ากอง.......... ผู้อำนวยการฝ่าย..........	ผู้ว่าการ.......... 24 มิ.ย. 23 115 kV วงจรเดี่ยว สายไฟฟ้าคู่ เสาสำหรับทางโค้ง แบบ SD-MA-1	เขียนเสร็จวันที่ 2 ม.ค. 23 แก้แบบวันที่ 15 ก.ย. 40 มิติเป็น.......... มาตราส่วน..........
รองผู้ว่าการฝ่ายเทคนิค	115 kV SINGLE CIRCUIT DOUBLE CONDUCTOR MEDIUM ANGLE STRUCTURE TYPE SD-MA-1	แบบเลขที่ SAI-015/23007 แผ่นที่ 3 ของจำนวน 3 แผ่น

19 มี.ค. 2523