การประกอบเลขที่ ASSEMBLY NO. 3411

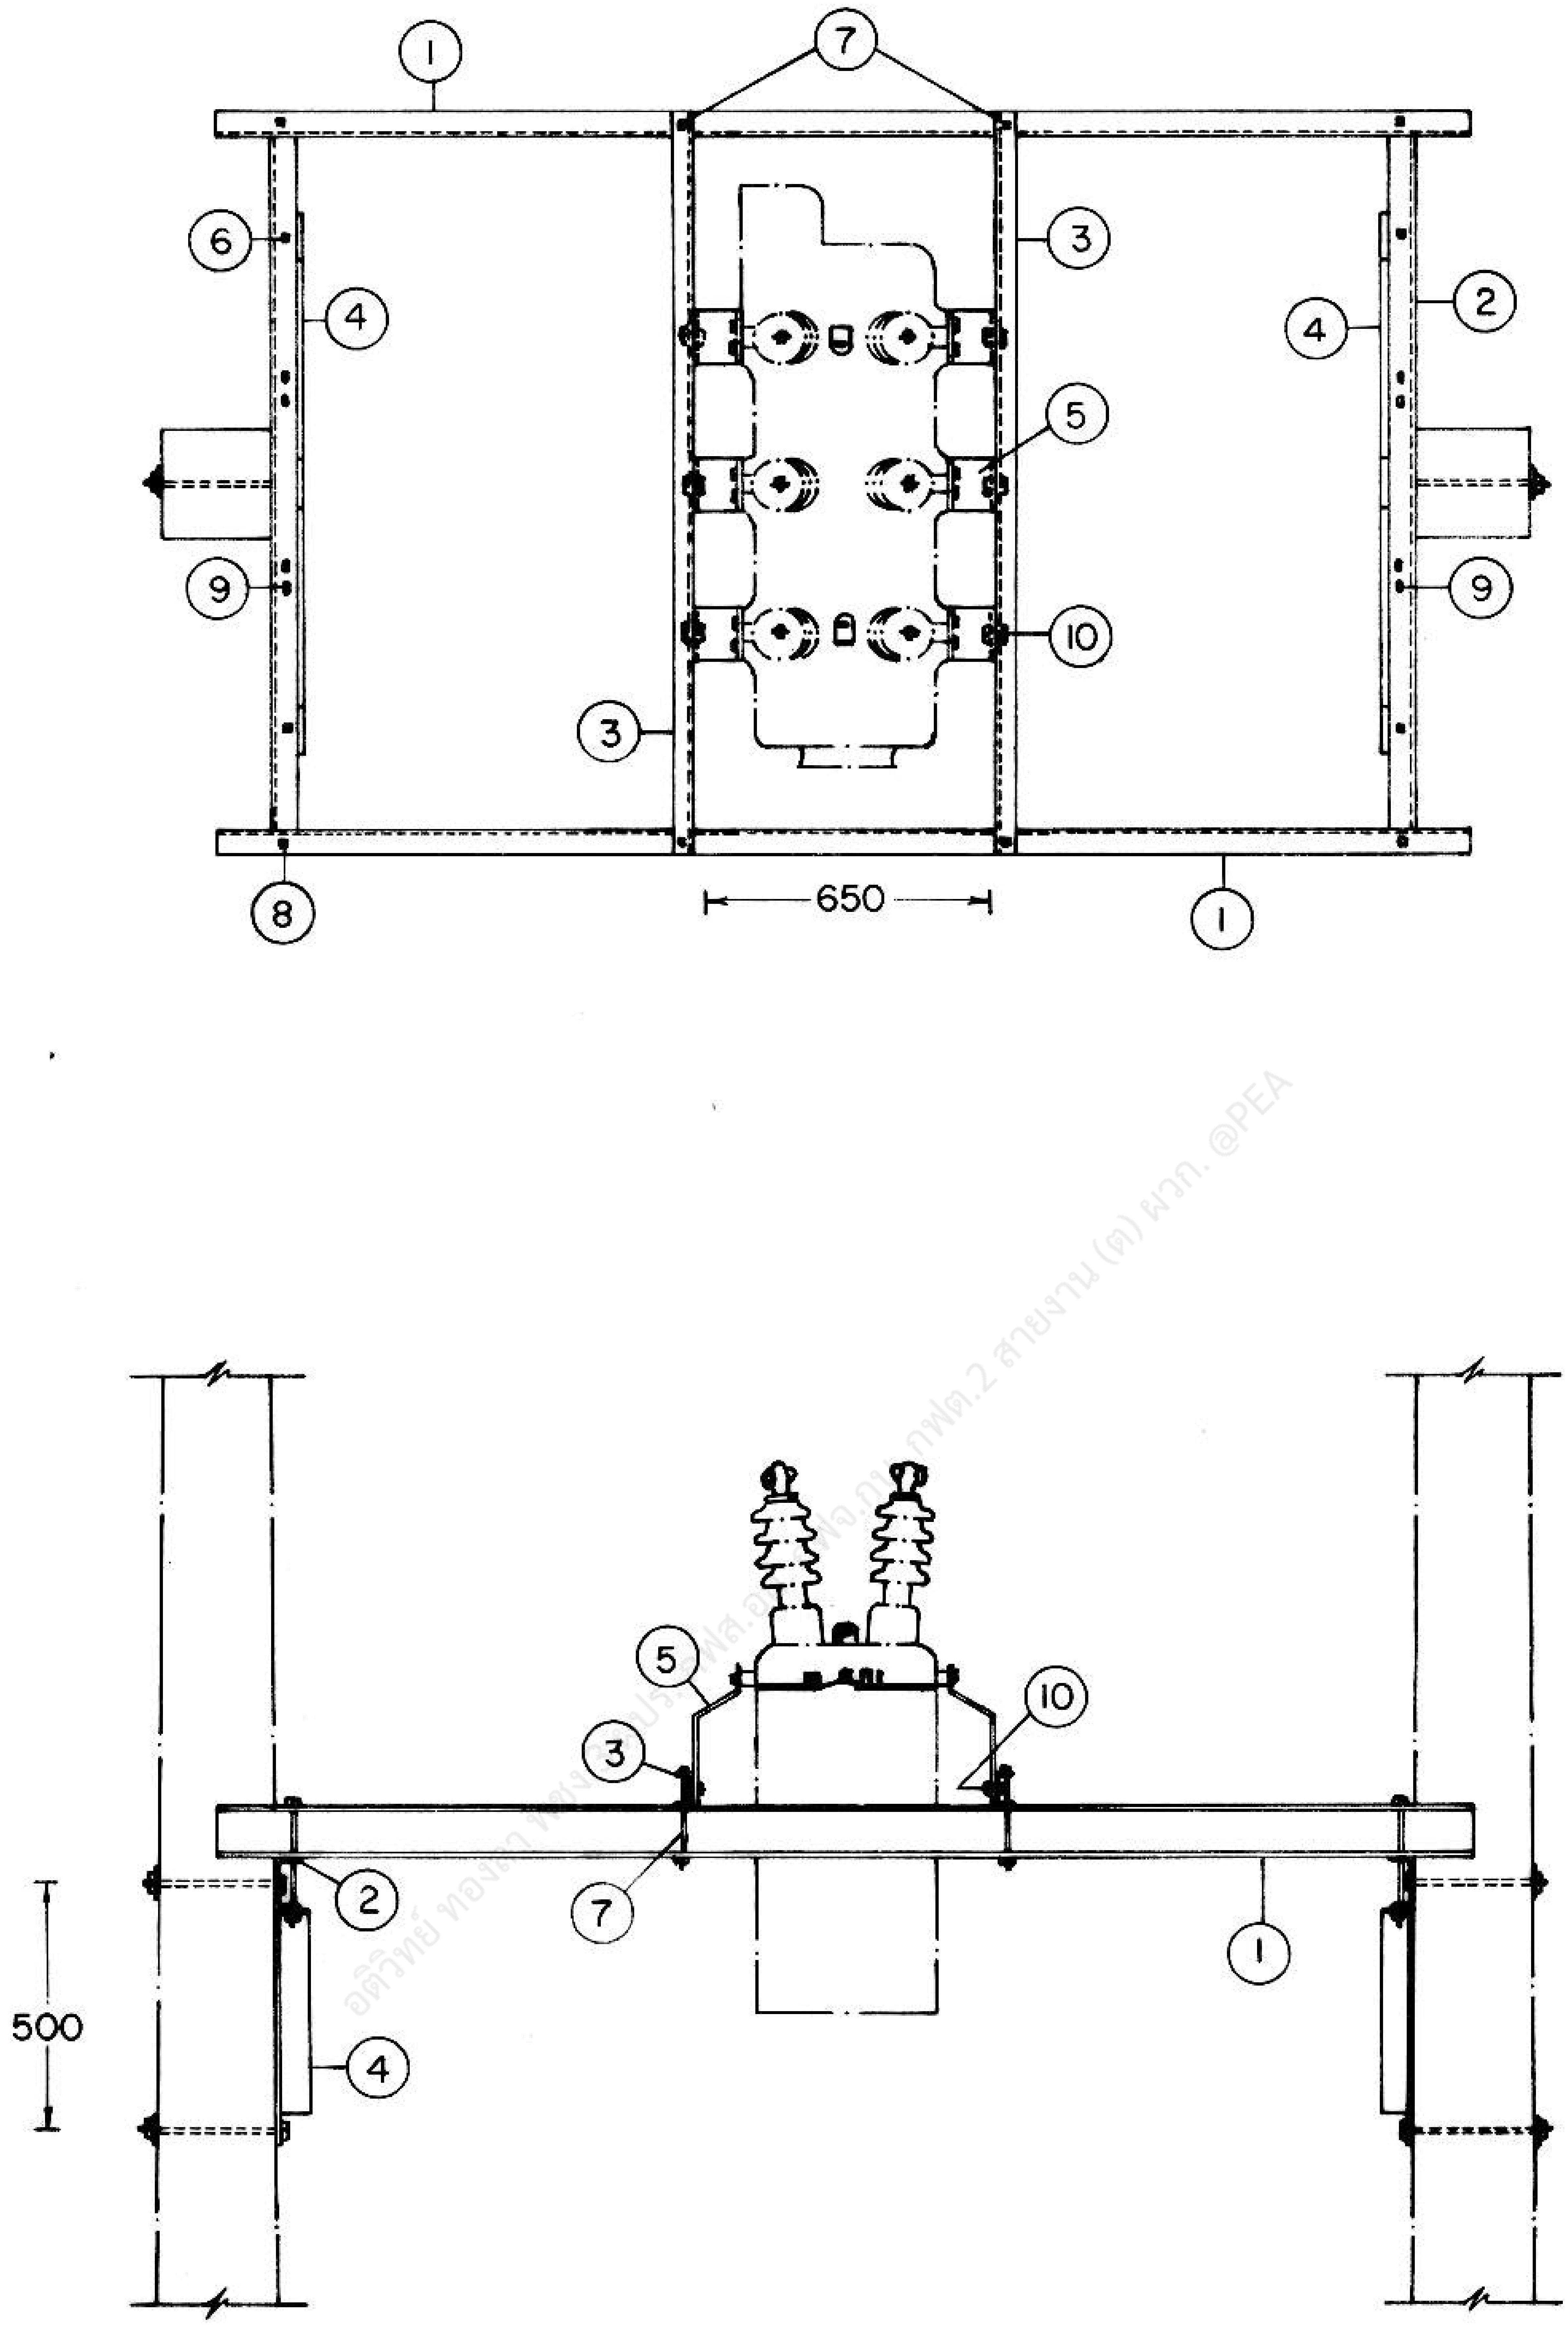

กองวิศวกรรมไฟฟ้าและเครื่องกล
ฝ่ายวิศวกรรม

ผู้เขียน
ผู้สำรวจ
วิศวกร กล้าหาญ
หัวหน้าแผนก ธีรวัฒ
หัวหน้ากอง
ผู้อำนวยการฝ่าย

รองผู้ว่าการฝ่ายเทคนิค
21 พ.ย. 2522

การไฟฟ้าส่วนภูมิภาค

ผู้ว่าการ 23 พ.ย. 22.

ที่แขวนรีโคลสเซอร์กับเสาคู่
(แบบที่ 2)

DOUBLE POLE MOUNTING FRAME FOR RECLOSER
(TYPE 2)

ใช้แทนแบบ
ถูกแทนโดยแบบ
เขียนเสร็จวันที่ 5 พ.ย. 22
แก้แบบวันที่ 4 มี.ค. 24
มิติเป็น มม.
มาตราส่วน 1 : 25
แบบเลขที่ SAI-015/22052
แผ่นที่ 1 ของจำนวน 4 แผ่น

การประกอบเลขที่ ASSEMBLY NO.	3411

① เหล็กรูปรางน้ำ ขนาด 100X50X5 มม. ยาว 2,500 มม.
STEEL CHANNEL 100 X 50 X 5 mm, 2,500 mm LONG

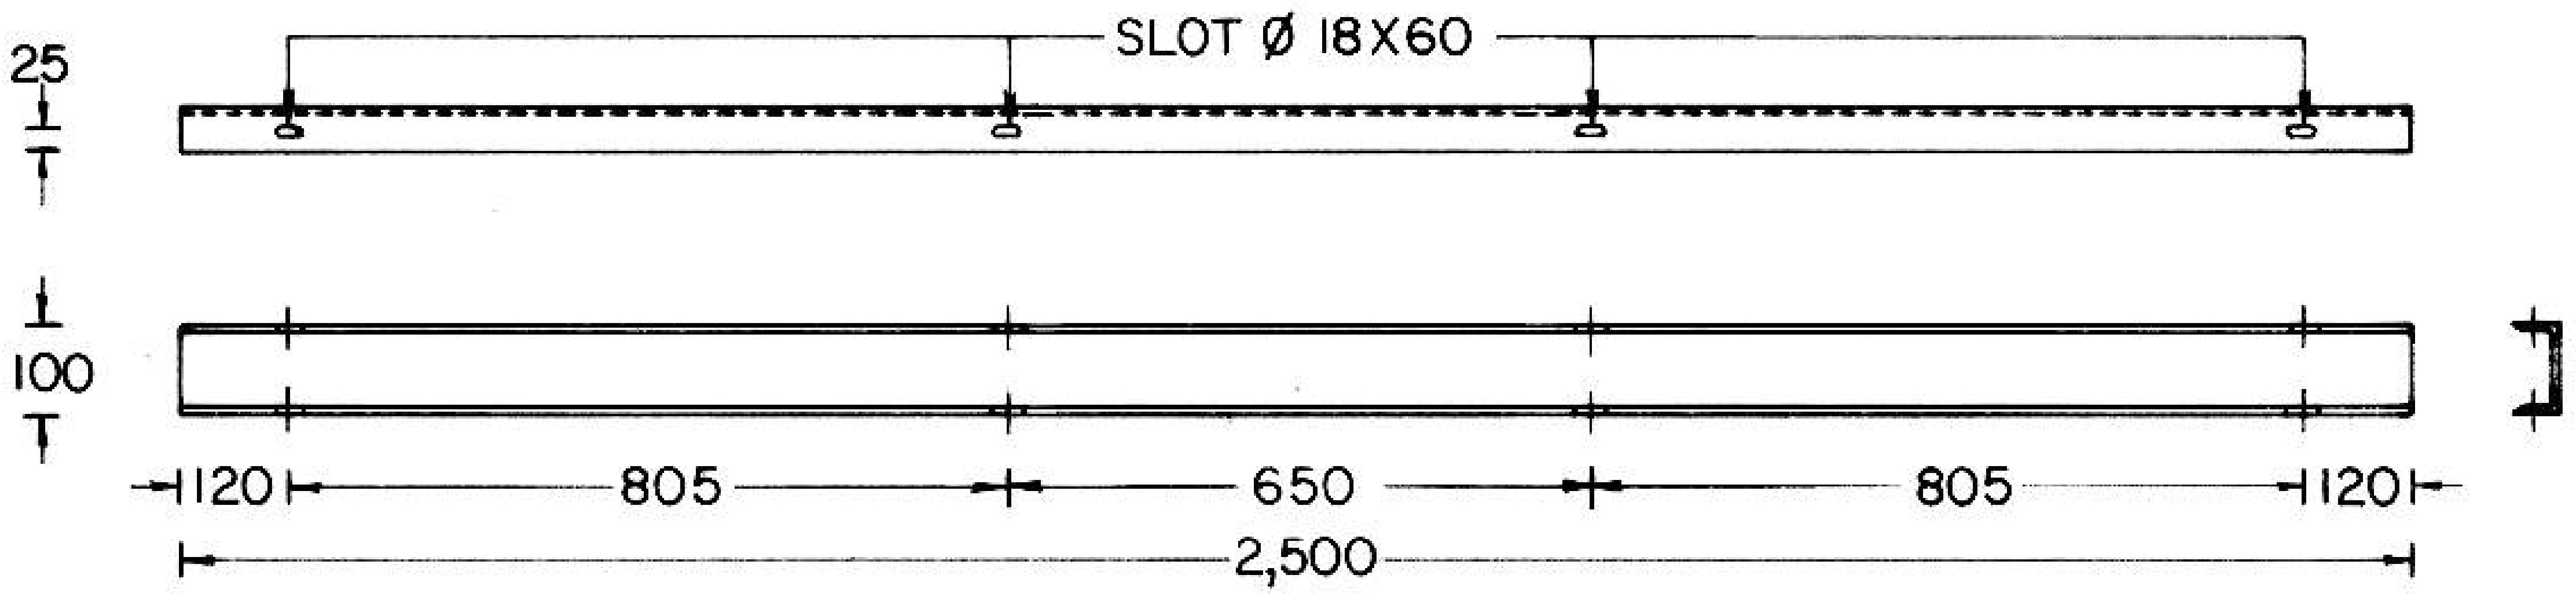

SLOT Ø 18X60
25
100
120
805
650
805
120
2,500

② เหล็กรูปรางน้ำ ขนาด 100X50X5 มม. ยาว 1,500 มม.
STEEL CHANNEL 100X50X5 mm, 1,500 mm LONG

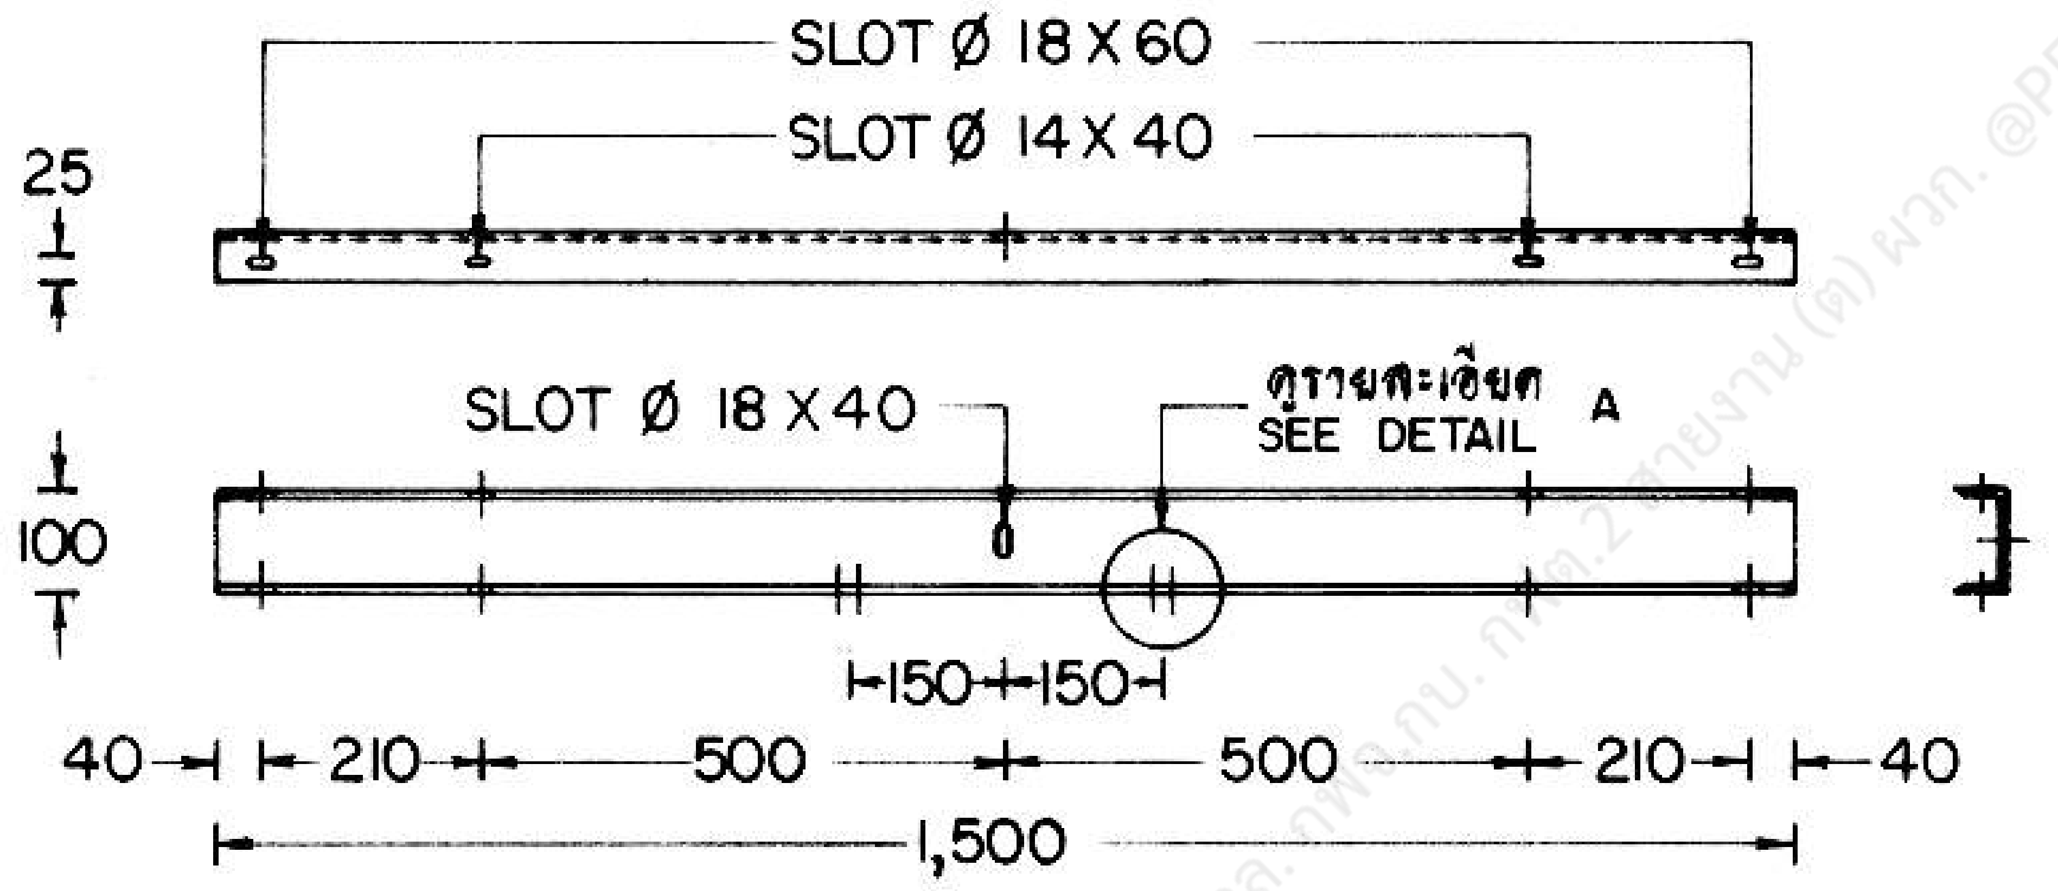

SLOT Ø 18X60
SLOT Ø 14X40
25
SLOT Ø 18X40
ดูรายละเอียด A
SEE DETAIL
100
150
150
40
210
500
500
210
40
1,500

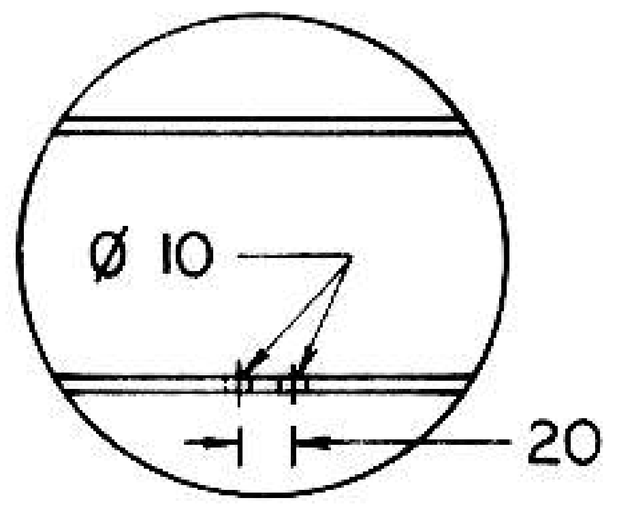

รายละเอียด A
DETAIL

③ เหล็กรูปรางน้ำ ขนาด 75X40X5 มม. ยาว 1,500 มม.
STEEL CHANNEL 75 X 40X5 mm, 1,500 mm LONG

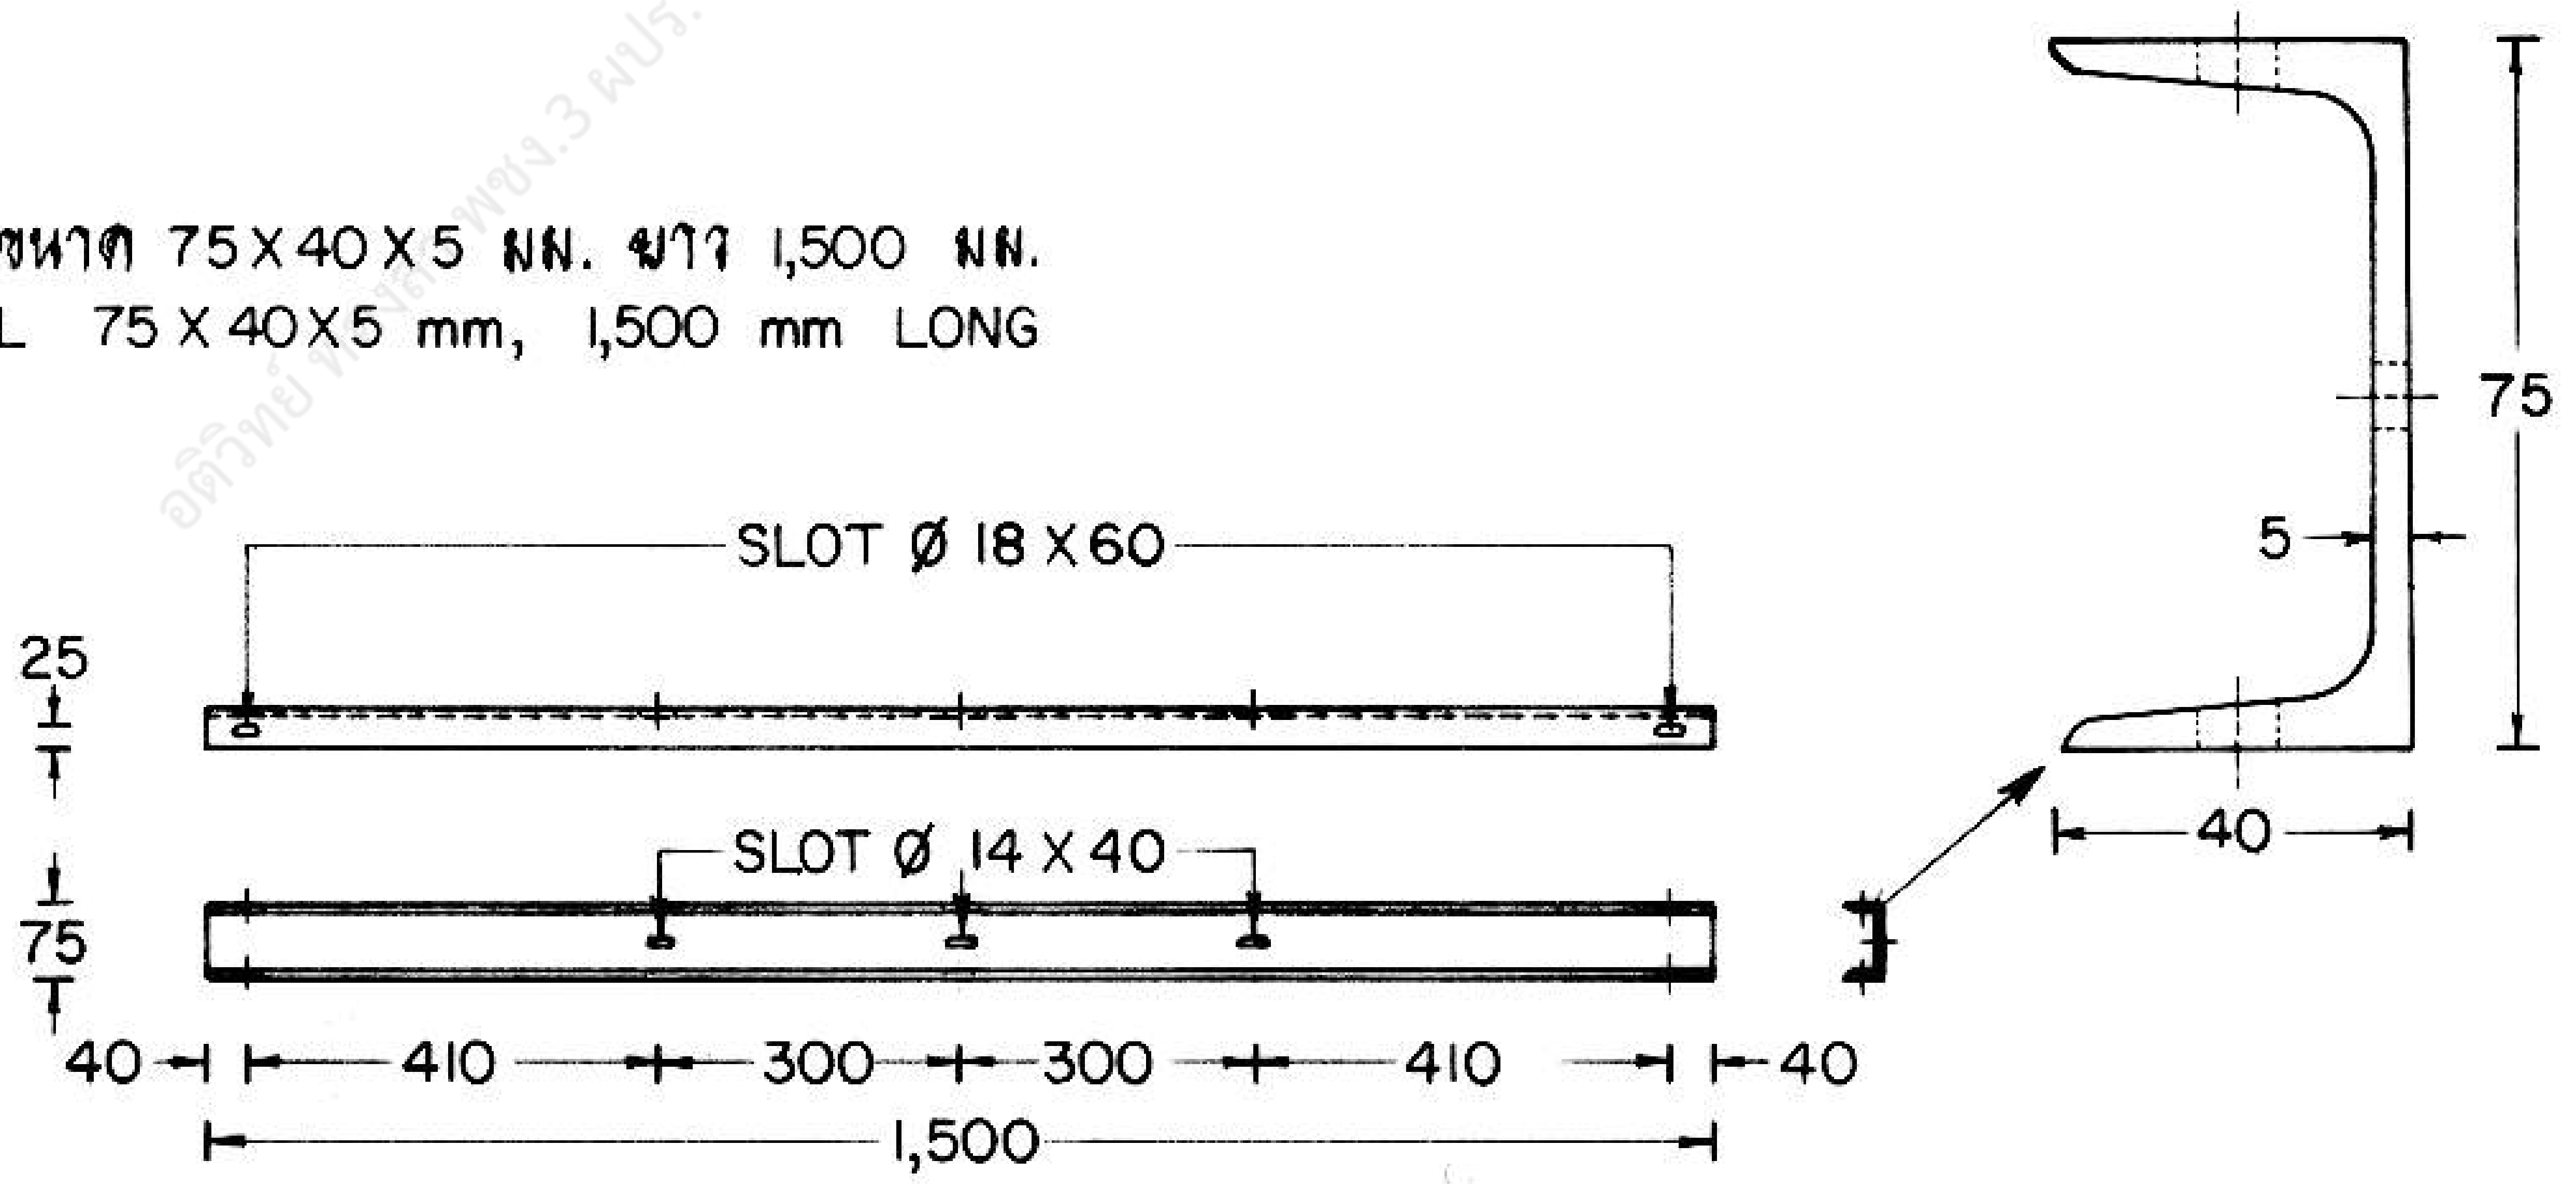

SLOT Ø 18X60
25
SLOT Ø 14X40
75
40
410
300
300
410
40
1,500
75
5
40

อติวิทย์ พชง.3 ผปร. กฟส.อล. กฟฉ.กบ. กฟก.2 รายงาน (ต) ผวก. @PEA

กองวิศวกรรมไฟฟ้าและเครื่องกล
ฝ่ายวิศวกรรม

ผู้เขียน
ผู้สำรวจ
วิศวกร กล้าหาญ
หัวหน้าแผนก
หัวหน้ากอง
ผู้อำนวยการฝ่าย

รองผู้ว่าการฝ่ายเทคนิค

21 พ.ย. 2522

การไฟฟ้าส่วนภูมิภาค

ผู้ว่าการ 23 พ.ย. 22

ที่แขวนรีโคลสเซอร์กับเสาคู่
(แบบที่ 2)

DOUBLE POLE MOUNTING FRAME FOR RECLOSER
(TYPE 2)

ใช้แทนแบบ
ถูกแทนโดยแบบ
เขียนเสร็จวันที่ 5 พ.ย. 22
แก้แบบวันที่ 4 มิ.ค. 24
มิติเป็น มม.
มาตราส่วน 1 : 20

แบบเลขที่ SAI-015/22052
แผ่นที่ 2 ของจำนวน 4 แผ่น

การประกอบเลขที่ ASSEMBLY NO.	3411

④ เหล็กฉากรับโครงเหล็ก ขนาด 65X65X6 มม. ช่วงกว้าง 1,000 มม. ดรอพ 480 มม.
ANGLE STEEL FOR SUPPORTING 65 X 65 X 6 mm, 1,000 mm WIDE, 480 mm DROP

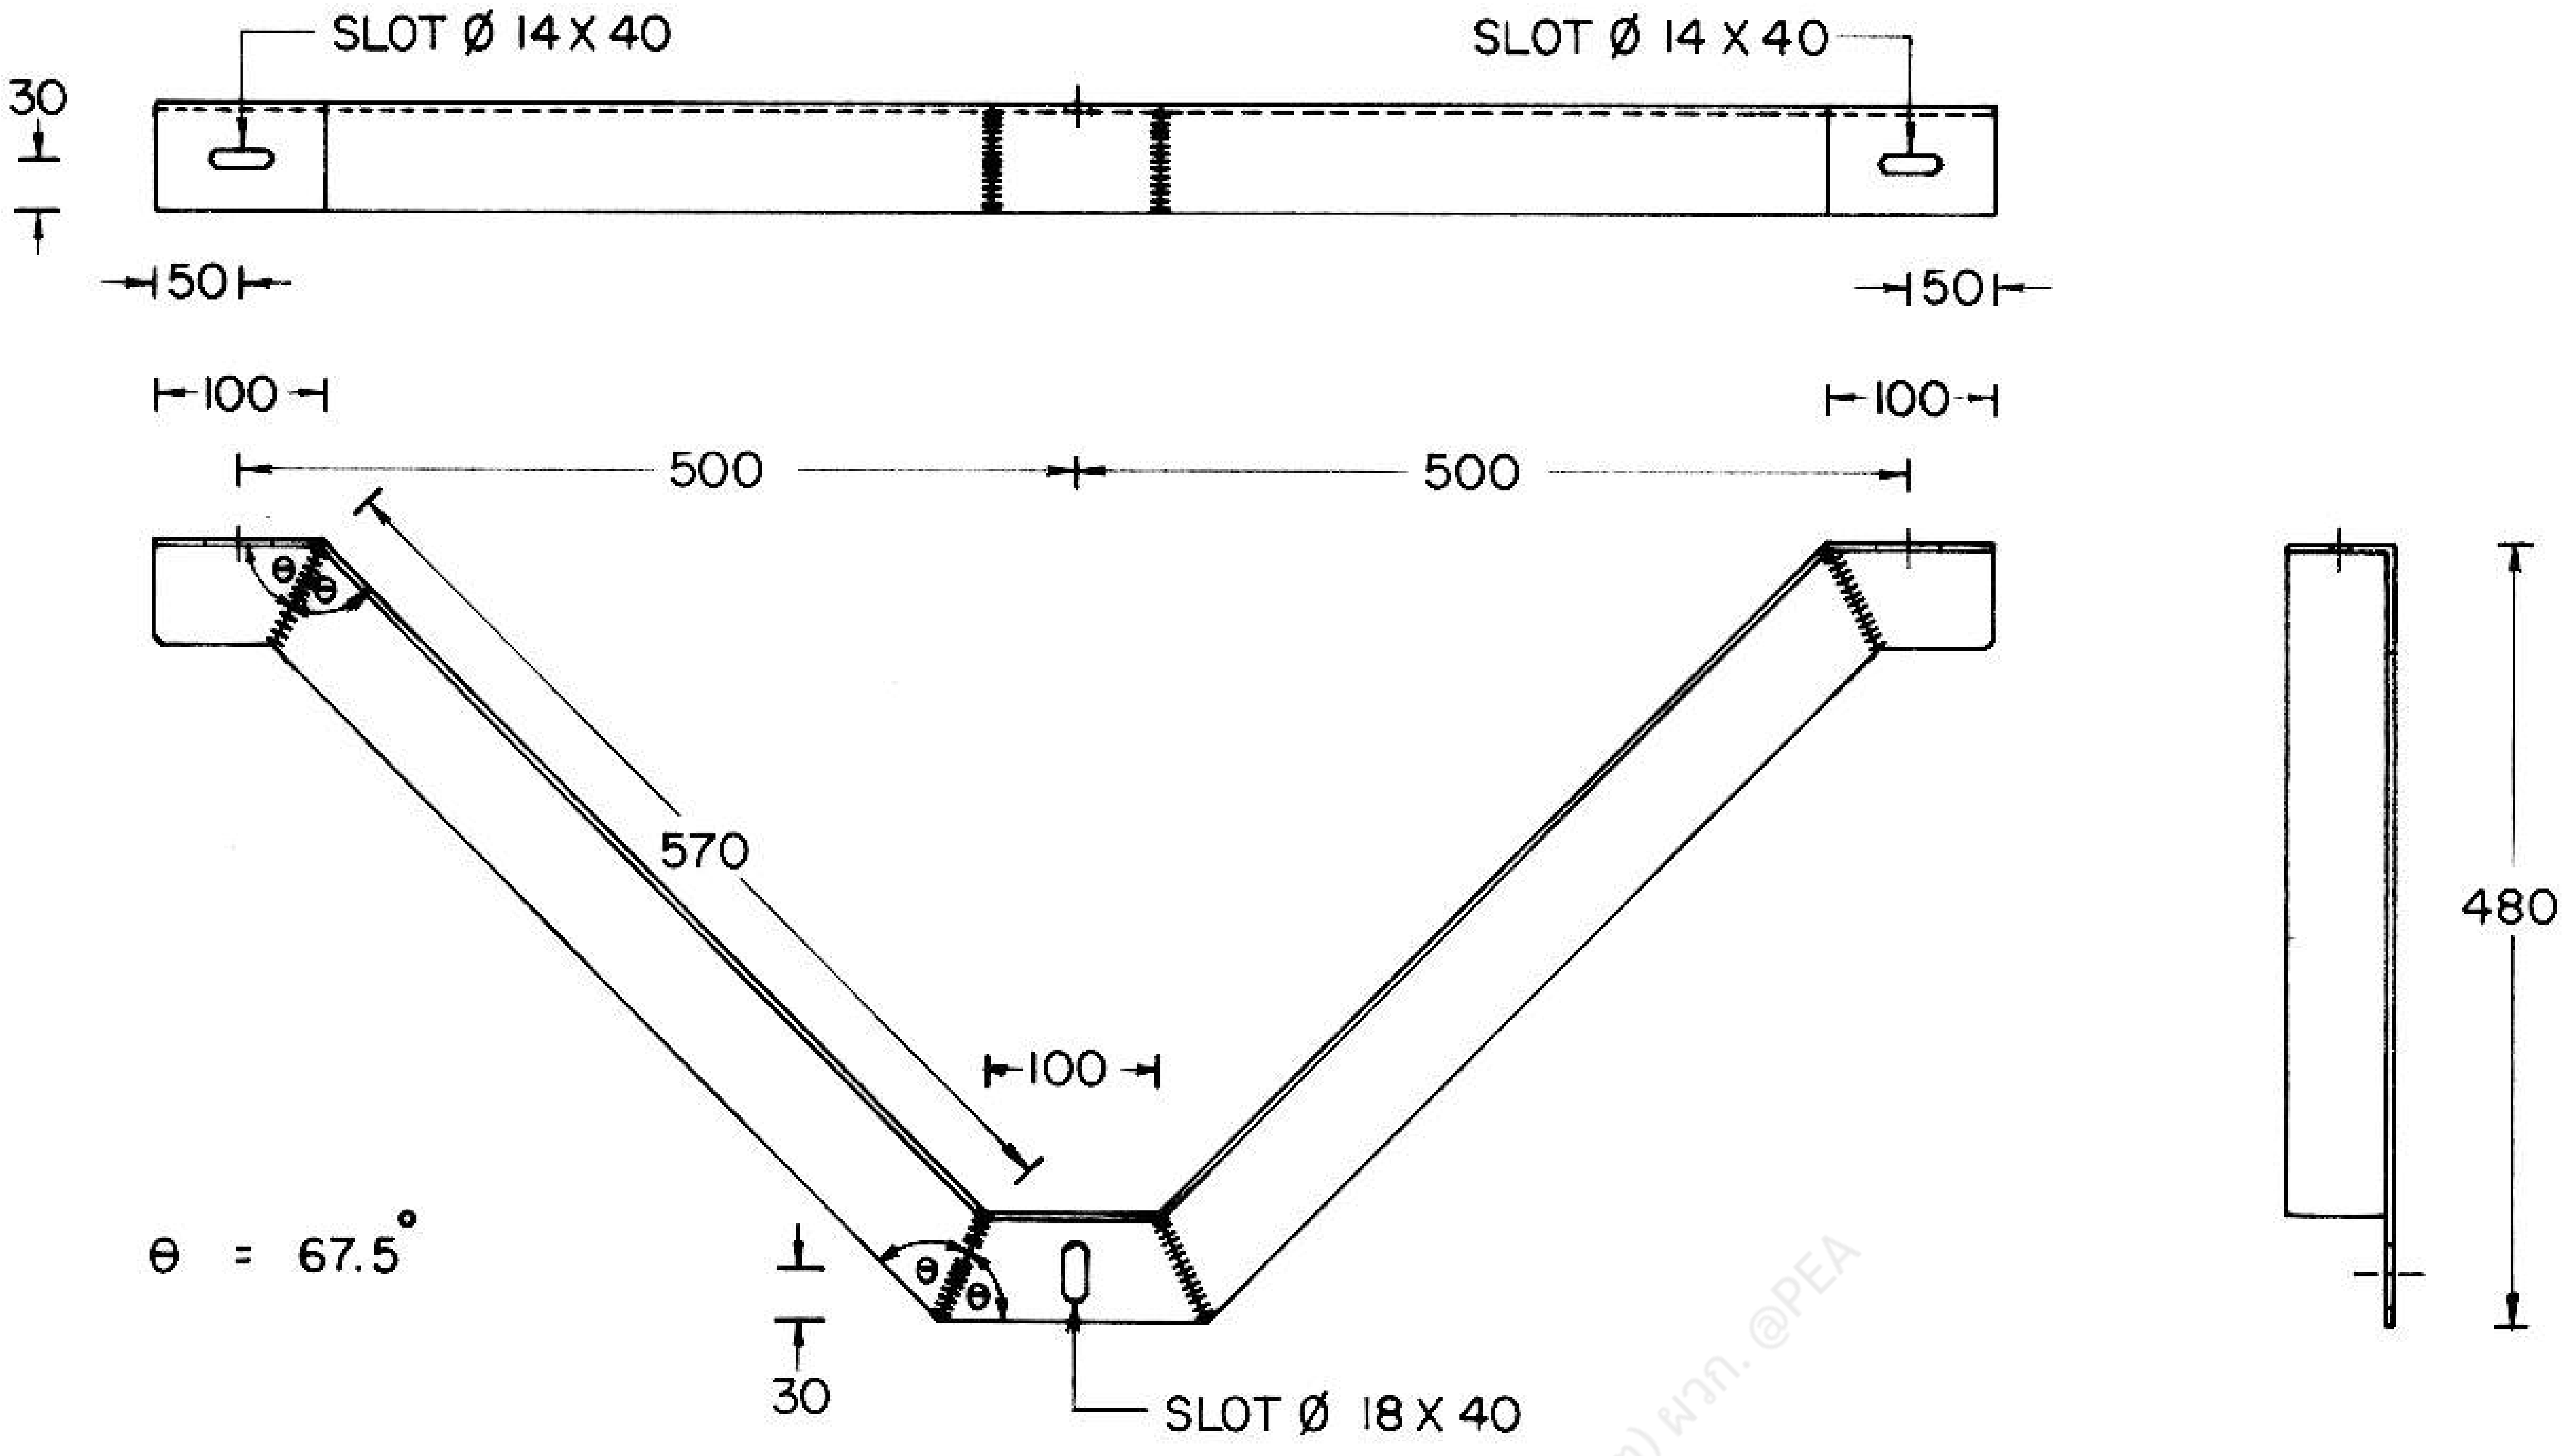
SLOT Ø 14 X 40
SLOT Ø 14 X 40
30
50
50
100
100
500
500
570
100
480
θ = 67.5°
θ
30
SLOT Ø 18 X 40

⑤ เหล็กแผ่นแบน ขนาดกว้าง 65 มม. หนา 6 มม. โค้งดัดดังรูป
STEEL PLATE, 65 mm WIDE, 6 mm THICKNESS, CURVED AS FIG.

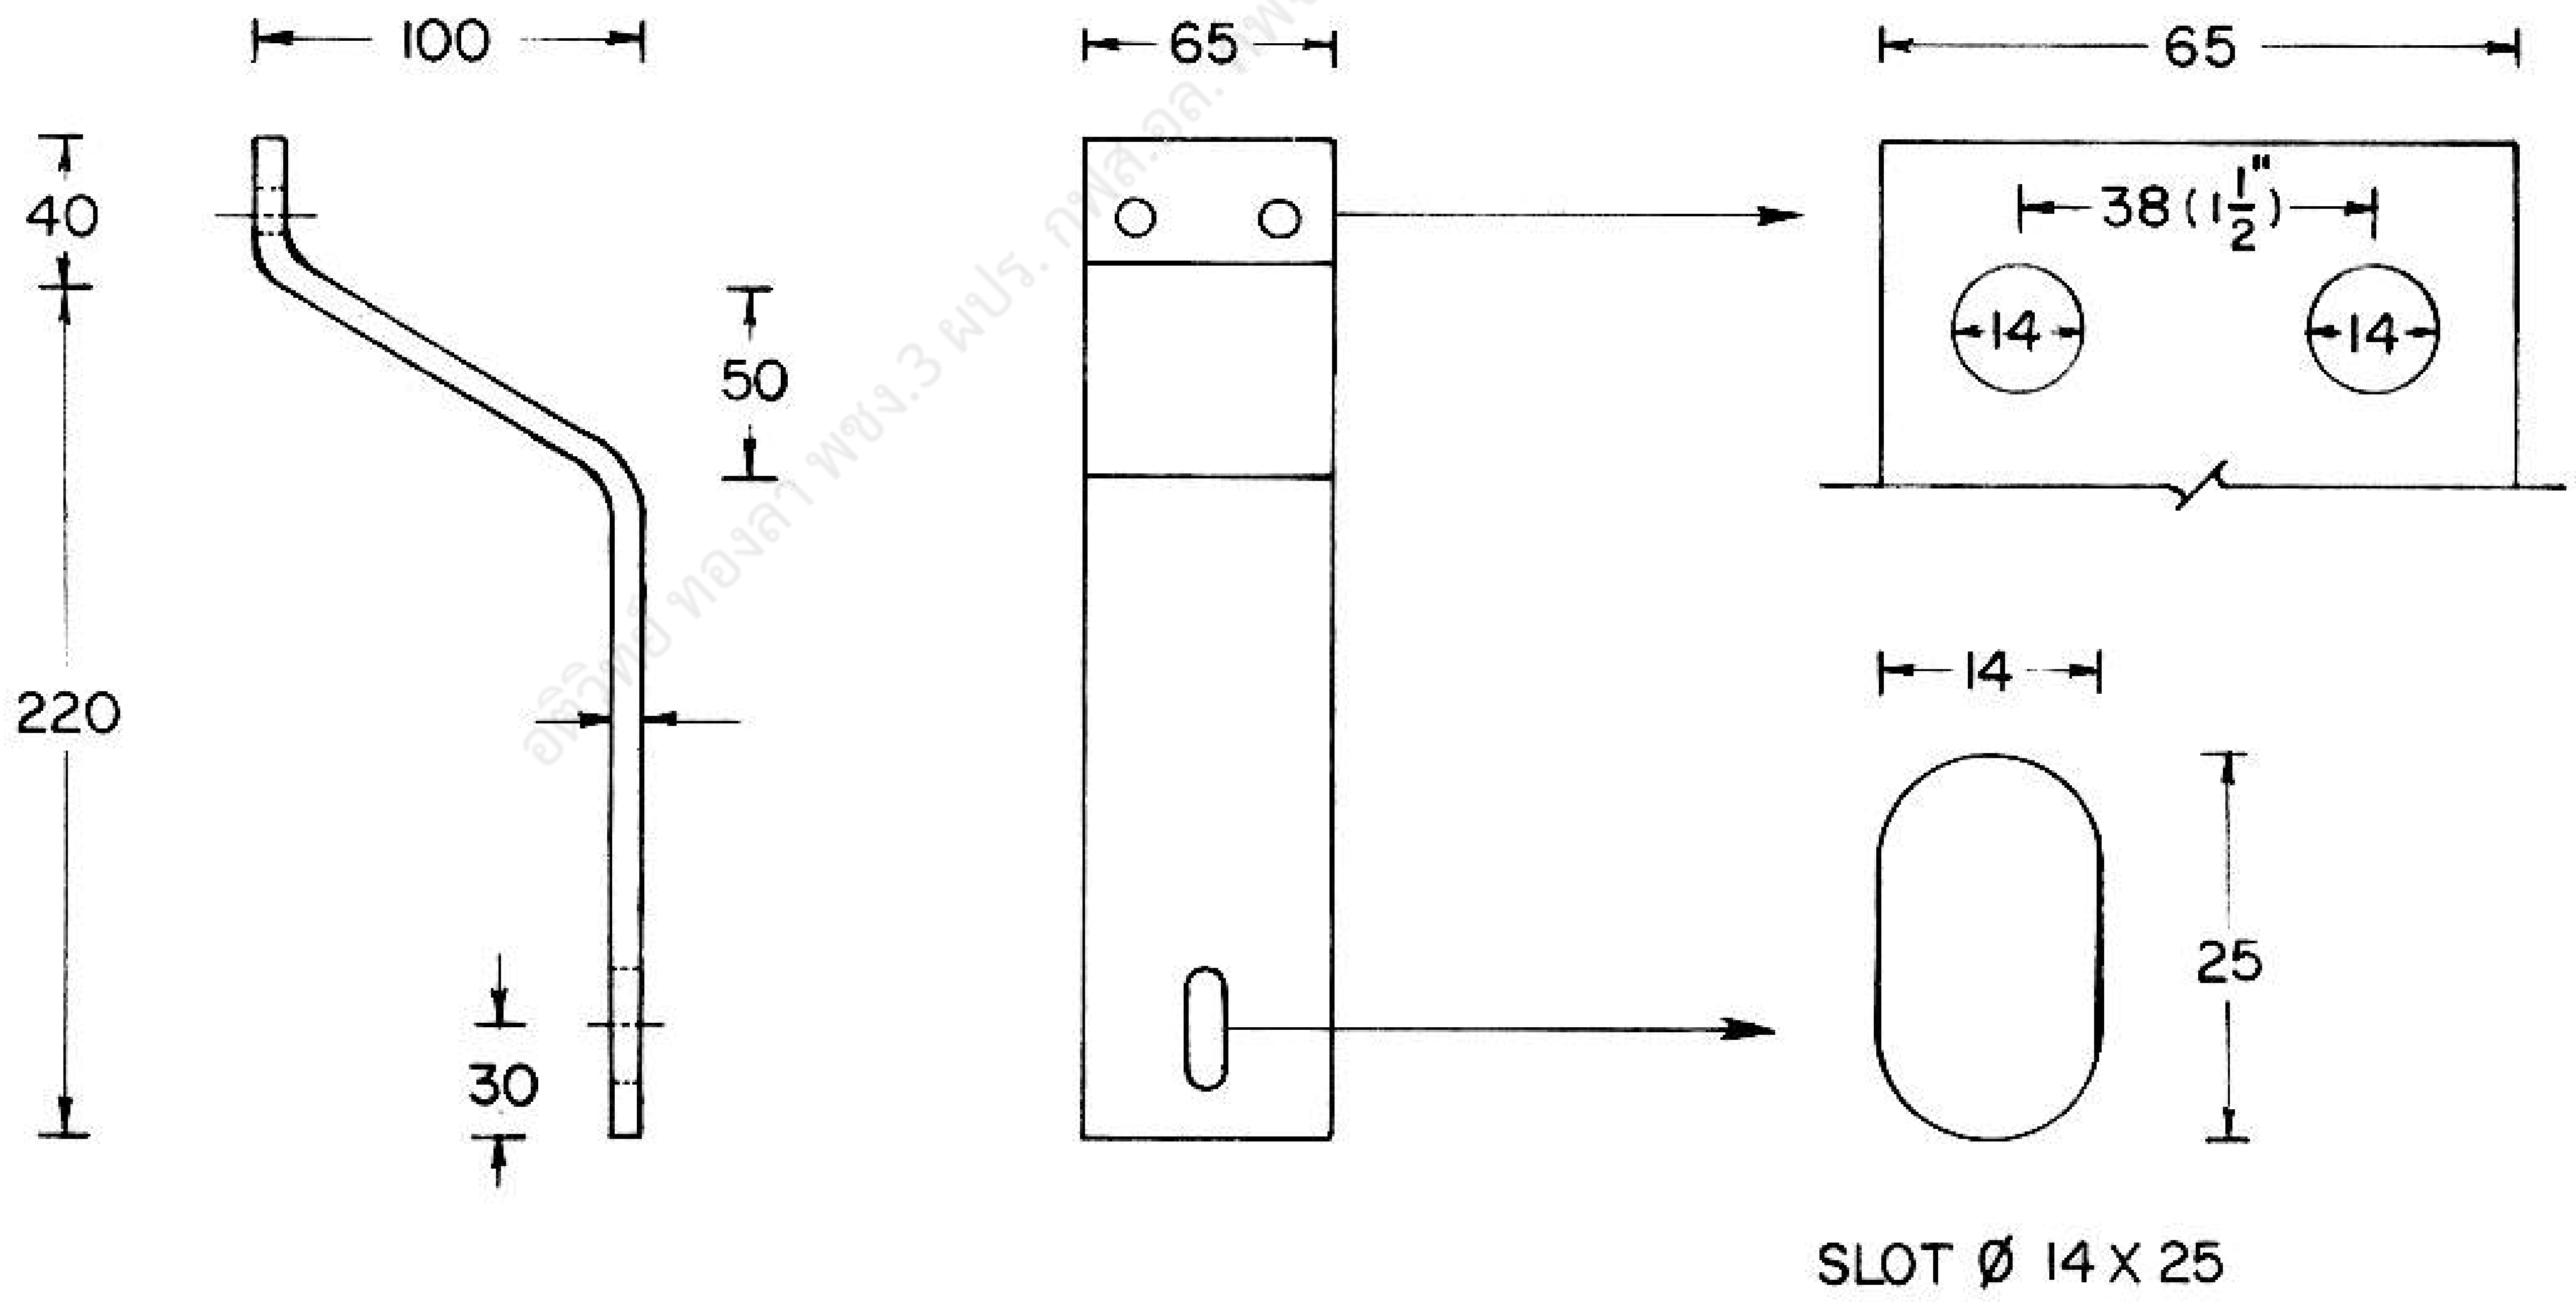
100
40
220
50
30
65
65
38 (1½")
14
14
20
14
25

SLOT Ø 14 X 25

กองวิศวกรรมไฟฟ้าและเครื่องกล ฝ่ายวิศวกรรม	การไฟฟ้าส่วนภูมิภาค	ใช้แทนแบบ ถูกแทนโดยแบบ
ผู้เขียน ผู้สำรวจ วิศวกร กล้าหาญ หัวหน้าแผนก หัวหน้ากอง ผู้อำนวยการฝ่าย	ผู้ว่าการ 23 พ.ย. 22.	เขียนเสร็จวันที่ 5 พ.ย. 22 แก้แบบวันที่ 4 มี.ค. 24
	ที่แขวนรีโคลสเซอร์กับเสาคู่ (แบบที่ 2)	มิติเป็น มม. มาตราส่วน 1 : 5, 1 : 10
รองผู้ว่าการฝ่ายเทคนิค	DOUBLE POLE MOUNTING FRAME FOR RECLOSER (TYPE 2)	แบบเลขที่ SAI-015/22052 แผ่นที่ 3 ของจำนวน 4 แผ่น

2 1 พ.ย. 2522

สายงาน (ต) ผวก. @PEA

การประกอบเลขที่
ASSEMBLY NO. 3411

บัญชีวัสดุ
BILL OF MATERIAL

ลำดับที่ ITEM	รายละเอียด DESCRIPTION	จำนวน REQ'D	วัสดุเลขที่ MAT. NO.
1	เหล็กรูปรางน้ำ 100 X 50 X 5 มม. ยาว 2,500 มม. STEEL, CHANNEL 100 X 50 X 5 mm, 2,500 mm LONG	2	——
2	เหล็กรูปรางน้ำ 100 X 50 X 5 มม. ยาว 1,500 มม. STEEL, CHANNEL 100 X 50 X 5 mm, 1,500 mm LONG	2	——
3	เหล็กรูปรางน้ำ 75 X 40 X 5 มม. ยาว 1,500 มม. STEEL, CHANNEL 75 X 40 X 5 mm, 1,500 mm LONG	2	——
4	เหล็กฉากรับโครงเหล็ก ขนาด 65 X 65 X 6 มม. ช่วงกว้าง 1,000 มม. ดรอพ 480 มม. STEEL, ANGLE FOR SUPPORTING 65 X 65 X 6 mm, 1,000 mm WIDE, 480 mm DROP	2	——
5	เหล็กแผ่นแบน ขนาดกว้าง 65 มม. หนา 6 มม. ความยาวโค้งดัดดังรูป STEEL PLATE, 65 mm WIDE, 6 mm THICKNESS, CURVED AS FIGURE	6	——
6	สลักเกลียว M 12 X 130 มม. พร้อมแหวนกลม 4 ตัว และแหวนสปริง 1 ตัว BOLT, MACHINE, M 12 X 130 mm COMP. WITH 4 ROUND WASHERS AND 1 SPRING WASHER	4	——
7	สลักเกลียว M 16 X 200 มม. พร้อมแหวนสี่เหลี่ยมแบน 2 ตัว และแหวนสปริง 1 ตัว BOLT, MACHINE, M 16 X 200 mm COMP. WITH 2 SQUARE WASHERS AND 1 SPRING WASHER	4	01110202
8	สลักเกลียว M 16 X 250 มม. พร้อมแหวนสี่เหลี่ยมแบน 2 ตัว และแหวนสปริง 1 ตัว BOLT, MACHINE, M 16 X 250 mm COMP. WITH 2 SQUARE WASHERS AND 1 SPRING WASHER	4	01110203
9	ยูแคล้มป์ สลัก 1 ตัว M 8 CLAMP, SINGLE U-BOLT, M 8	2	01230000
10	สลักเกลียว M 12 X 40 มม. พร้อมแหวนกลม 2 ตัว และแหวนสปริง 1 ตัว BOLT, MACHINE, M 12 X 40 mm COMP. WITH 2 ROUND WASHERS AND 1 SPRING WASHER	6	——

หมายเหตุ

1. โครงเหล็กทุกชิ้นให้อาบสังกะสี หรือทาด้วยสีกันสนิม แล้วทาทับด้วยสีเทา
2. ที่แขวน สำหรับรีโคลสเซอร์ ผลิตภัณฑ์ McGRAW-EDISON แบบ RV
3. แบบนี้ใช้สำหรับติดตั้งรีโคลสเซอร์ระบบ 33 kV หรือใช้สำหรับการติดตั้งรีโคลสเซอร์ ระบบ 22 kV กรณีที่มีสายระบบจำหน่ายแรงต่ำ
4. เหล็กรูปรางน้ำ และเหล็กฉาก เป็นชนิดผลิตร้อน ตาม มอก. 116

NOTES

1. ALL STEEL STRUCTURES SHALL BE GALVANIZED OR PAINTED WITH A PRIMER COAT AND GRAY WEATHER-RESISTANCE COATS.
2. HANGER FOR McGRAW-EDISON RECLOSER TYPE RV.
3. THIS HANGER IS USED FOR 33 kV RECLOSER INSTALLATION OR 22 kV RECLOSER INSTALLATION IN CASE OF HAVING L.T. DISTRIBUTION LINE.
4. CHANNEL STEEL AND ANGLE STEEL ACCORDING TO TIS 116

กองวิศวกรรมไฟฟ้าและเครื่องกล
ฝ่ายวิศวกรรม

ผู้เขียน
ผู้สำรวจ
วิศวกร
หัวหน้าแผนก
หัวหน้ากอง
ผู้อำนวยการฝ่าย

รองผู้ว่าการฝ่ายเทคนิค
21 พ.ย. 2522

การไฟฟ้าส่วนภูมิภาค

ผู้ว่าการ 23 พ.ย. 22.

ที่แขวนรีโคลสเซอร์กับเสาคู่
(แบบที่ 2)

DOUBLE POLE MOUNTING FRAME FOR RECLOSER
(TYPE 2)

ใช้แทนแบบ
ถูกแทนโดยแบบ
เขียนเสร็จวันที่ 5 พ.ย. 22
แก้แบบวันที่ 4 มี.ค. 24
มิติเป็น
มาตราส่วน

แบบเลขที่ SAI-015/22052
แผ่นที่ 4 ของจำนวน 4 แผ่น