

การประกอบเลขที่ 3310
ASSEMBLY NO.

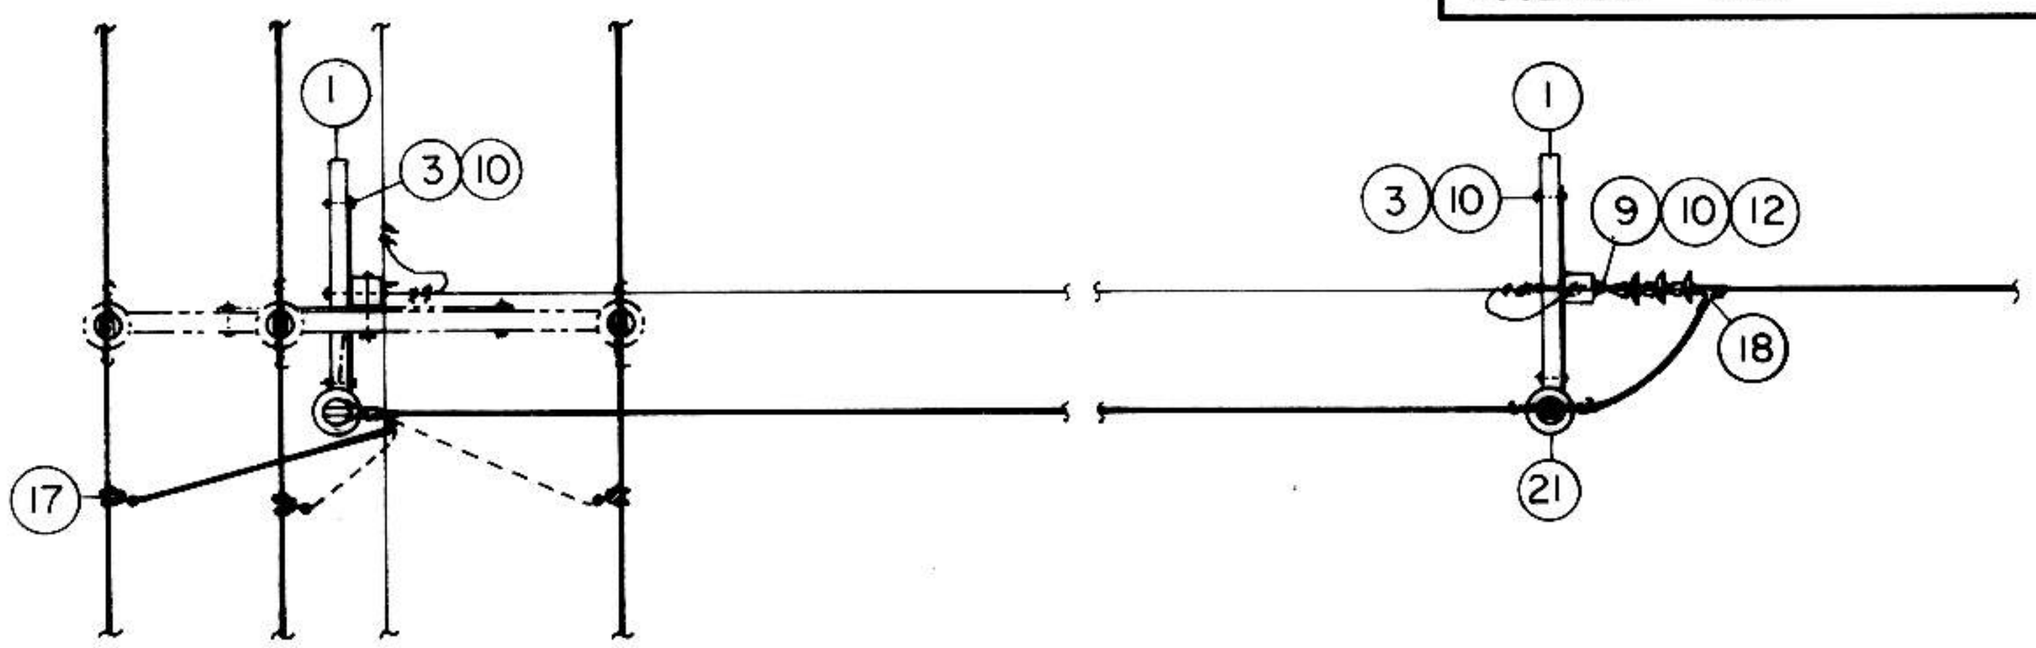

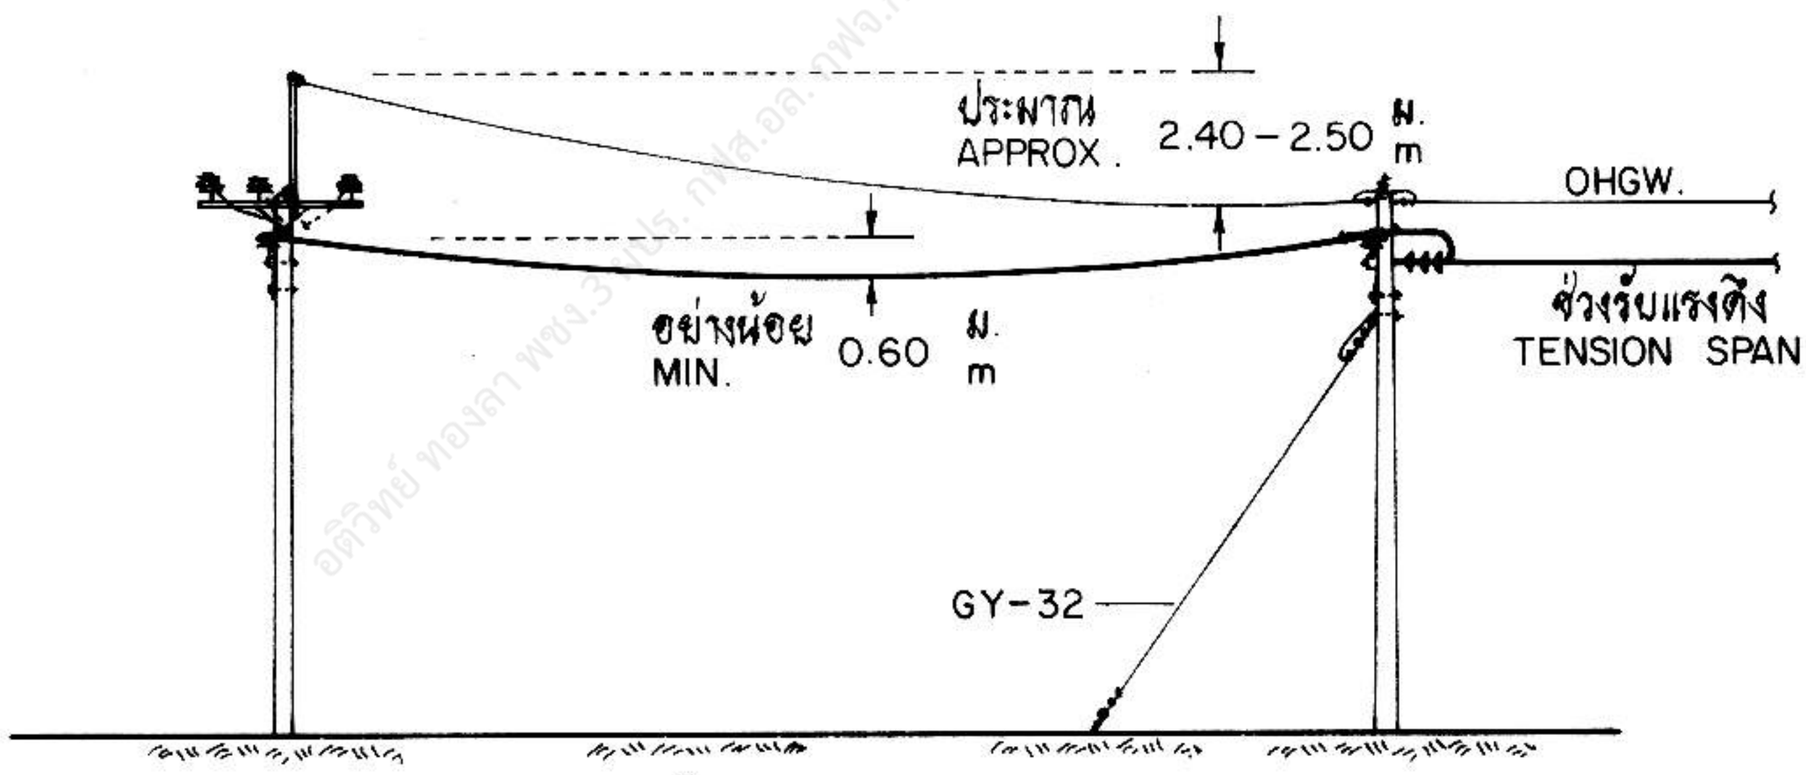


สำหรับใช้ก่อสร้างในบริเวณที่มีโหลดน้อย และไม่มีการปรับปรุงเป็นระบบ 3 เฟส 33 กิโลโวลต์ ในอนาคตอันใกล้
FOR CONSTRUCTION IN LIGHT LOAD SITE WHERE SHALL NOT BE REVAMPED TO 3-PHASE, 33 kV SYSTEM IN THE NEAR FUTURE.


กองวิศวกรรมไฟฟ้าและเครื่องกล ฝ่ายวิศวกรรม	**การไฟฟ้าส่วนภูมิภาค**	ใช้แทนแบบ .....
ผู้เขียน	ผู้ว่าการ	ถูกแทนโดยแบบ .....
ผู้สำรวจ	2 ธ.ค. 2531	เขียนเสร็จวันที่ 17 พ.ค. 31
วิศวกร	การติดตั้งบัคอาร์ม ระบบ 1 เฟส 19 kV (กรณีใช้คอนครอนกรีต) สำหรับการพาดสายช่วงสั้นไม่รับแรงดึง	แก้แบบวันที่ .....
หัวหน้าแผนก		มิติเป็น มม.
ผู้อำนวยการกอง		มาตราส่วน 1 : 75, 1 : 250
ผู้อำนวยการฝ่าย		
รองผู้ว่าการฝ่ายเทคนิค	1-PHASE, 19 kV BUCKARM INSTALLATION (CONCRETE CROSSARM) SLACK SPAN LATERAL	แบบเลขที่ SAI-015/31046 แผ่นที่ 1 ของจำนวน 4 แผ่น

27 พ.ค. 2531

การประกอบเลขที่ ASSEMBLY NO. 3310

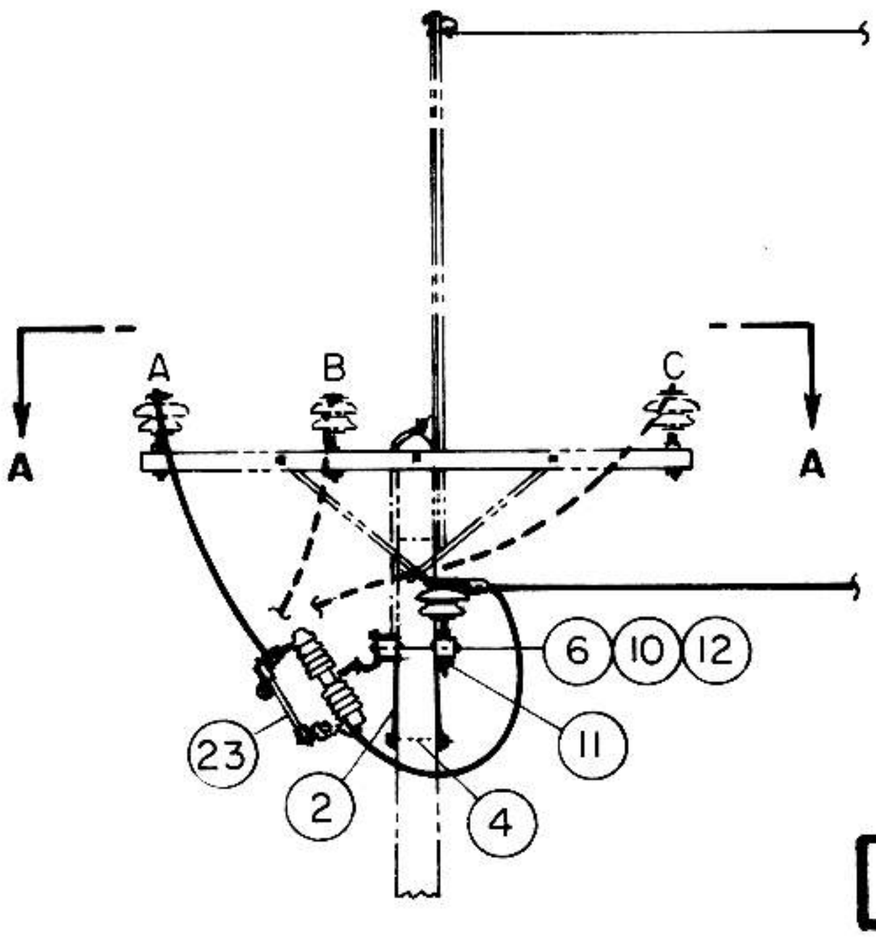


BCS – 2

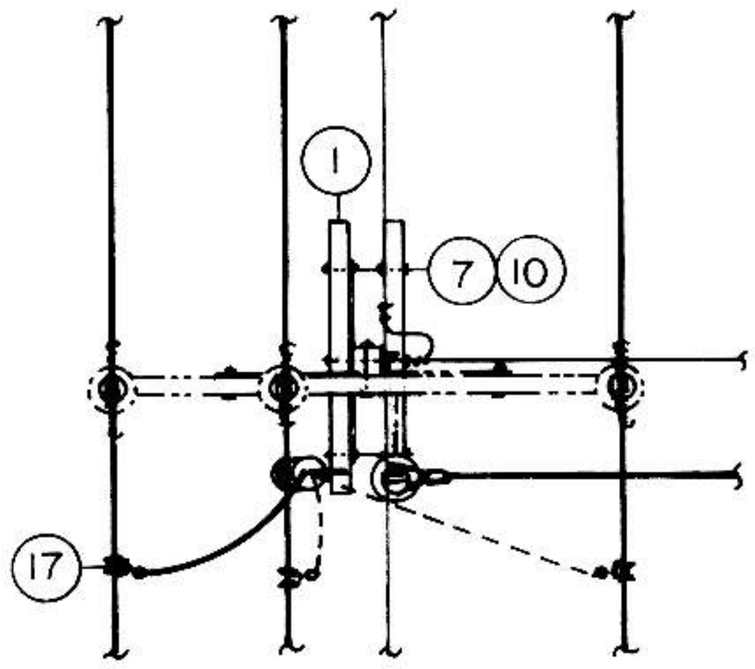

รูปตัด A – A
SECTION

วิธีผูกลูกถ้วย (การเข้าปลายสายช่วงไม่รับแรงดึงบนลูกถ้วยก้านตรง)
TYING METHOD (SLACK SPAN DEADENDING ON PIN INSULATOR)

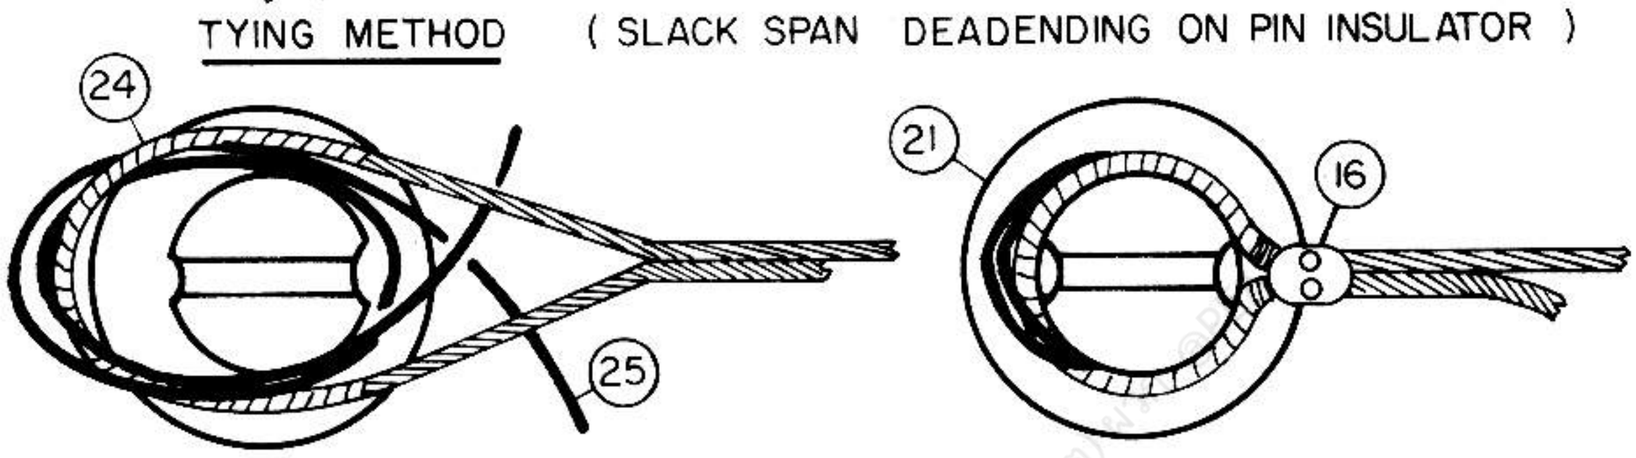

ให้พันลวดอะลูมิเนียมแบนรอบสายไฟหนึ่งชั้น แล้วใช้ลวดอะลูมิเนียมกลมพันรอบลูกถ้วย และสายไฟ พร้อมกันใช้คอนเนคเตอร์เข้าปลายสาย 1 ชุด จับสายไฟให้ใกล้ลูกถ้วยมากที่สุด

CONDUCTOR SHOULD BE WRAPPED WITH ALUMINIUM ARMOUR TAPE ONE LAYER AND TIED WITH THE TIE WIRE. THE CONDUCTOR SHOULD BE CLAMPED WITH DEADEND CONNECTOR CLOSE TO INSULATOR.

ข้อกำหนดการใช้งาน

1. ระยะห่างระหว่างช่วงเสาประธานไม่เกิน 50 ม.
2. ระยะห่างระหว่างช่วงเสาไม่รับแรงดึงไม่เกิน 20 ม.
3. สายไฟฟ้าขนาดสูงสุด
   สายอะลูมิเนียม หรืออะลูมิเนียมอัลลอย ขนาด 50 ต.มม.
   สายอะลูมิเนียมแกนเหล็ก ขนาด 50/8 ต.มม.

RECOMMENDATION

1. MAXIMUM MAIN SPAN 50 m
2. MAXIMUM SLACK SPAN LATERAL 20 m
3. CONDUCTOR, MAXIMUM SIZE
   Al OR Al-ALLOY 50 mm^2
   ACSR 50/8 mm^2

กองวิศวกรรมไฟฟ้าและเครื่องกล ฝ่ายวิศวกรรม	**การไฟฟ้าส่วนภูมิภาค**	ใช้แทนแบบ ..... ถูกแทนโดยแบบ ..... เขียนเสร็จวันที่ 17 พ.ค. 31 แก้แบบวันที่ ..... มิติเป็น ..... มาตราส่วน .....
ผู้เขียน ..... ผู้สำรวจ ..... วิศวกร ..... หัวหน้าแผนก ..... ผู้อำนวยการกอง ..... ผู้อำนวยการฝ่าย	ผู้ว่าการ ..... 2 มิ.ย. 2531 การติดตั้งบัคอาร์ม ระบบ 1 เฟส 19 kV (กรณีใช้คอนคอนกรีต) สำหรับการพาดสายช่วงสั้นไม่รับแรงดึง	
รองผู้ว่าการฝ่ายเทคนิค	1-PHASE, 19 kV BUCKARM INSTALLATION (CONCRETE CROSSARM) SLACK SPAN LATERAL	แบบเลขที่ SA1-015/31046 แผ่นที่ 2 ของจำนวน 4 แผ่น

27 W.A. 2531

การประกอบเลขที่ ASSEMBLY NO. 3310

บัญชีวัสดุ
BILL OF MATERIAL

ลำดับที่ ITEM	รายละเอียด DESCRIPTION	จำนวน REQ'D BCS-1	BCS-2	DES	วัสดุเลขที่ MAT. NO
1	คอน คอร. ขนาด 100 X 100 X 1,500 มม. CROSSARM, PRESTRESSED CONCRETE 100 X 100 X 1,500 mm	1	2	1	00110000
2	เหล็กประกับคอน 30 X 6 X 760 มม. BRACE, FLAT, FOR CROSSARM, 30 X 6 X 760 mm	2	2	2	01200001
3	สลักเกลียว M 16 X 130 มม. BOLT, MACHINE M 16 X 130 mm	2	–	2	01110200
4	สลักเกลียว M 16 X 250 มม. BOLT, MACHINE M 16 X 250 mm	1	1	1	01110203
5	สลักเกลียว M 16 X 350 มม. BOLT, MACHINE M 16 X 350 mm	1	–	–	01110205
6	สลักเกลียว M 16 X 450 มม. BOLT, MACHINE M 16 X 450 mm	–	1	–	01110207
7	สลักเกลียวตลอด M 16 X 450 มม. BOLT, DOUBLE ARMING, M 16 X 450 mm	–	2	–	01120001
8	สลักห่วงกลม M 16 X 200 มม. BOLT, ROUND EYE, M 16 X 200 mm	–	–	1	01140001
9	สลักห่วงกลม M 16 X 300 มม. BOLT, ROUND EYE, M 16 X 300 mm	–	–	1	01140003
10	แหวนสี่เหลี่ยมแบน 52 X 52 X 4.5 มม. รู Ø 18 มม. มอก. 258 WASHER, SQUARE, FLAT, 52 X 52 X 4.5 mm, HOLE Ø 18 mm, TIS 258	5	11	7	01180100
11	แหวนสี่เหลี่ยมโค้ง 60 X 60 X 5 มม. รู Ø 22 มม. WASHER, SQUARE, CURVED, 60 X 60 X 5 mm, HOLE Ø 22 mm	1	1	–	01180201
12	แหวนสปริง M 16 มอก. 259 WASHER, LOCK, M 16, TIS 259	1	1	1	01180301
13	นัทรูปห่วง M 16 DIN 582 NUT, EYE M 16 DIN 582	–	–	1	01180001
14	กายทิมเบิ้ล สำหรับสายยึดโยง 50-95 ต.มม. THIMBLE, GUY, FOR STEEL WIRE 50-95 mm^2	–	–	2	01210304
15	ลวดเหล็กกลมเส้นผ่านศูนย์กลาง 4 มม. เส้นเดี่ยว มอก. 71 หน. ประมาณ 0.1 กก./ม. WIRE, STEEL, SOLID, DIAMETER 4 mm TIS 71 WEIGHT APPROX.. 0.1 kg / m	2.0 ม./m	2.5 ม./m	–	01100000
16	คอนเนคเตอร์เข้าปลายสายอะลูมิเนียม ขนาดตามต้องการ CONNECTOR, DEADEND, AI SIZE AS REQUIRED	1	1	–	02310000 02310001
17	เบล (สเตอร์รัพ) แคล้มป์ และฮอทไลน์แคล้มป์ ขนาดตามต้องการ CLAMP, BAIL (STIRRUP); AND HOT LINE CLAMP ; SIZE AS REQUIRED	1	1	–	02330000-1 02330100-1
18	สเตรนแคล้มป์สำหรับสายอะลูมิเนียม 35-95 ต.มม. อะลูมิเนียมแกนเหล็ก 35-50 ต.มม. CLAMP, STRAIN FOR AI 35-95 mm^2, ACSR 35-50 mm^2	–	–	1	03110000 03110001
19	กราวด์รายแคล้มป์ แบบ J 1152 GROUND WIRE SUPPORT AND CLAMP, J 1152	1	1	–	01230205
20	ยูแคล้มป์ สลัก 1 ตัว M 8 (ไวร์ โรป คลิ๊ฟ) CLAMP, SINGLE U-BOLT, M 8 (WIRE ROPE CLIP)	6	6	6	01230000

กองวิศวกรรมไฟฟ้าและเครื่องกล
ฝ่ายวิศวกรรม

ผู้เขียน
ผู้สำรวจ
วิศวกร
หัวหน้าแผนก
ผู้อำนวยการกอง
ผู้อำนวยการฝ่าย

รองผู้ว่าการฝ่ายเทคนิค

การไฟฟ้าส่วนภูมิภาค

ผู้ว่าการ

2 ส.ค. 2531

การติดตั้งบัคอาร์ม ระบบ 1 เฟส 19 kV
(กรณีใช้ดอนคอนกรีต)
สำหรับการพาดสายช่วงสั้นไม่รับแรงดึง

1-PHASE, 19 kV BUCKARM INSTALLATION
(CONCRETE CROSSARM)
SLACK SPAN LATERAL

ใช้แทนแบบ
ถูกแทนโดยแบบ
เขียนเสร็จวันที่ 17 พ.ค. 31
แก้แบบวันที่
มิติเป็น
มาตราส่วน

แบบเลขที่ SAI-015/31046
แผ่นที่ 3 ของจำนวน 4 แผ่น

27 พ.ค. 2531

การประกอบเลขที่ ASSEMBLY NO. 3310

บัญชีวัสดุ
BILL OF MATERIAL

ลำดับที่ ITEM	รายละเอียด DESCRIPTION	จำนวน REQ'D BCS-1	BCS-2	DES	วัสดุเลขที่ MAT. NO
21	ลูกถ้วยก้านตรง 33 kV มอก. 279 แบบ ค (แบบ 56-3) พร้อมก้าน INSULATOR, PIN TYPE, 33 kV, TIS 279 TYPE C (CLASS 56-3), COMP. WITH PIN	1	1	1	03000002 03100001
22	ลูกถ้วยแขวน มอก. 354 แบบ ง (แบบ 52-4) INSULATOR, SUSPENSION TYPE, TIS 354 TYPE D (CLASS 52-4)	–	–	3	03020002
23	ดรอพเอาต์ ฟิวส์ดัดเอาต์ หนึ่งอินซูเลเตอร์ 33 kV 100 แอมป์ CUTOUT, FUSE, DROPOUT, SINGLE INSULATOR, 33 kV, 100 A	–	1	–	02200000
24	ลวดอะลูมิเนียมแบน 1X10 มม. ความยาวตามต้องการ ARMOUR TAPE, Al 1X10 mm, LENGTH AS REQUIRED				02200002
25	ลวดอะลูมิเนียมกลม Ø 4 มม. ความยาวตามต้องการ TIE WIRE, Al Ø 4 mm, LENGTH AS REQUIRED				
26	การประกอบสายยึดโยง GY-32 GUY ASSEMBLY GY-32	–	–	1	

	แบบอ้างอิง REFERENCE DRAWING	แบบเลขที่ DWG. NO.	การประกอบเลขที่ ASSEMBLY NO.
1	ข้อแนะนำในการก่อสร้างระบบจำหน่าย 1 เฟส 19 kV CONSTRUCTION SUGGESTION OF 1-PHASE 19 kV SYSTEM	S02-015/20016	3305
2	รายละเอียดการประกอบสายยึดโยง ชุด GY-32 DETAIL OF GUY ASSEMBLY GY-32	SA1-015/20040	8453
3	การประกอบสายลงดินด้วยวิธียึดลวดเหล็ก GROUND LEAD ASSEMBLY STEEL WIRE FITTING	S02-015/19166	9703

กองวิศวกรรมไฟฟ้าและเครื่องกล
ฝ่ายวิศวกรรม

ผู้เขียน
ผู้สำรวจ
วิศวกร
หัวหน้าแผนก
ผู้อำนวยการกอง
ผู้อำนวยการฝ่าย

รองผู้ว่าการฝ่ายเทคนิค

27 พ.ค. 2531

การไฟฟ้าส่วนภูมิภาค

ผู้ว่าการ

2 มิ.ย. 2531

การติดตั้งบัคอาร์ม ระบบ 1 เฟส 19 kV
(กรณีใช้คอนคอนกรีต)
สำหรับการพาดสายช่วงสั้นไม่รับแรงดึง

1-PHASE, 19 kV BUCKARM INSTALLATION
(CONCRETE CROSSARM)
SLACK SPAN LATERAL

ใช้แทนแบบ
ถูกแทนโดยแบบ
เขียนเสร็จวันที่ 17 พ.ค. 31
แก้แบบวันที่
มิติเป็น
มาตราส่วน

แบบเลขที่ SA1-015/31046

แผ่นที่ 4 ของจำนวน 4 แผ่น