การประกอบเลขที่
ASSEMBLY NO. **3720**

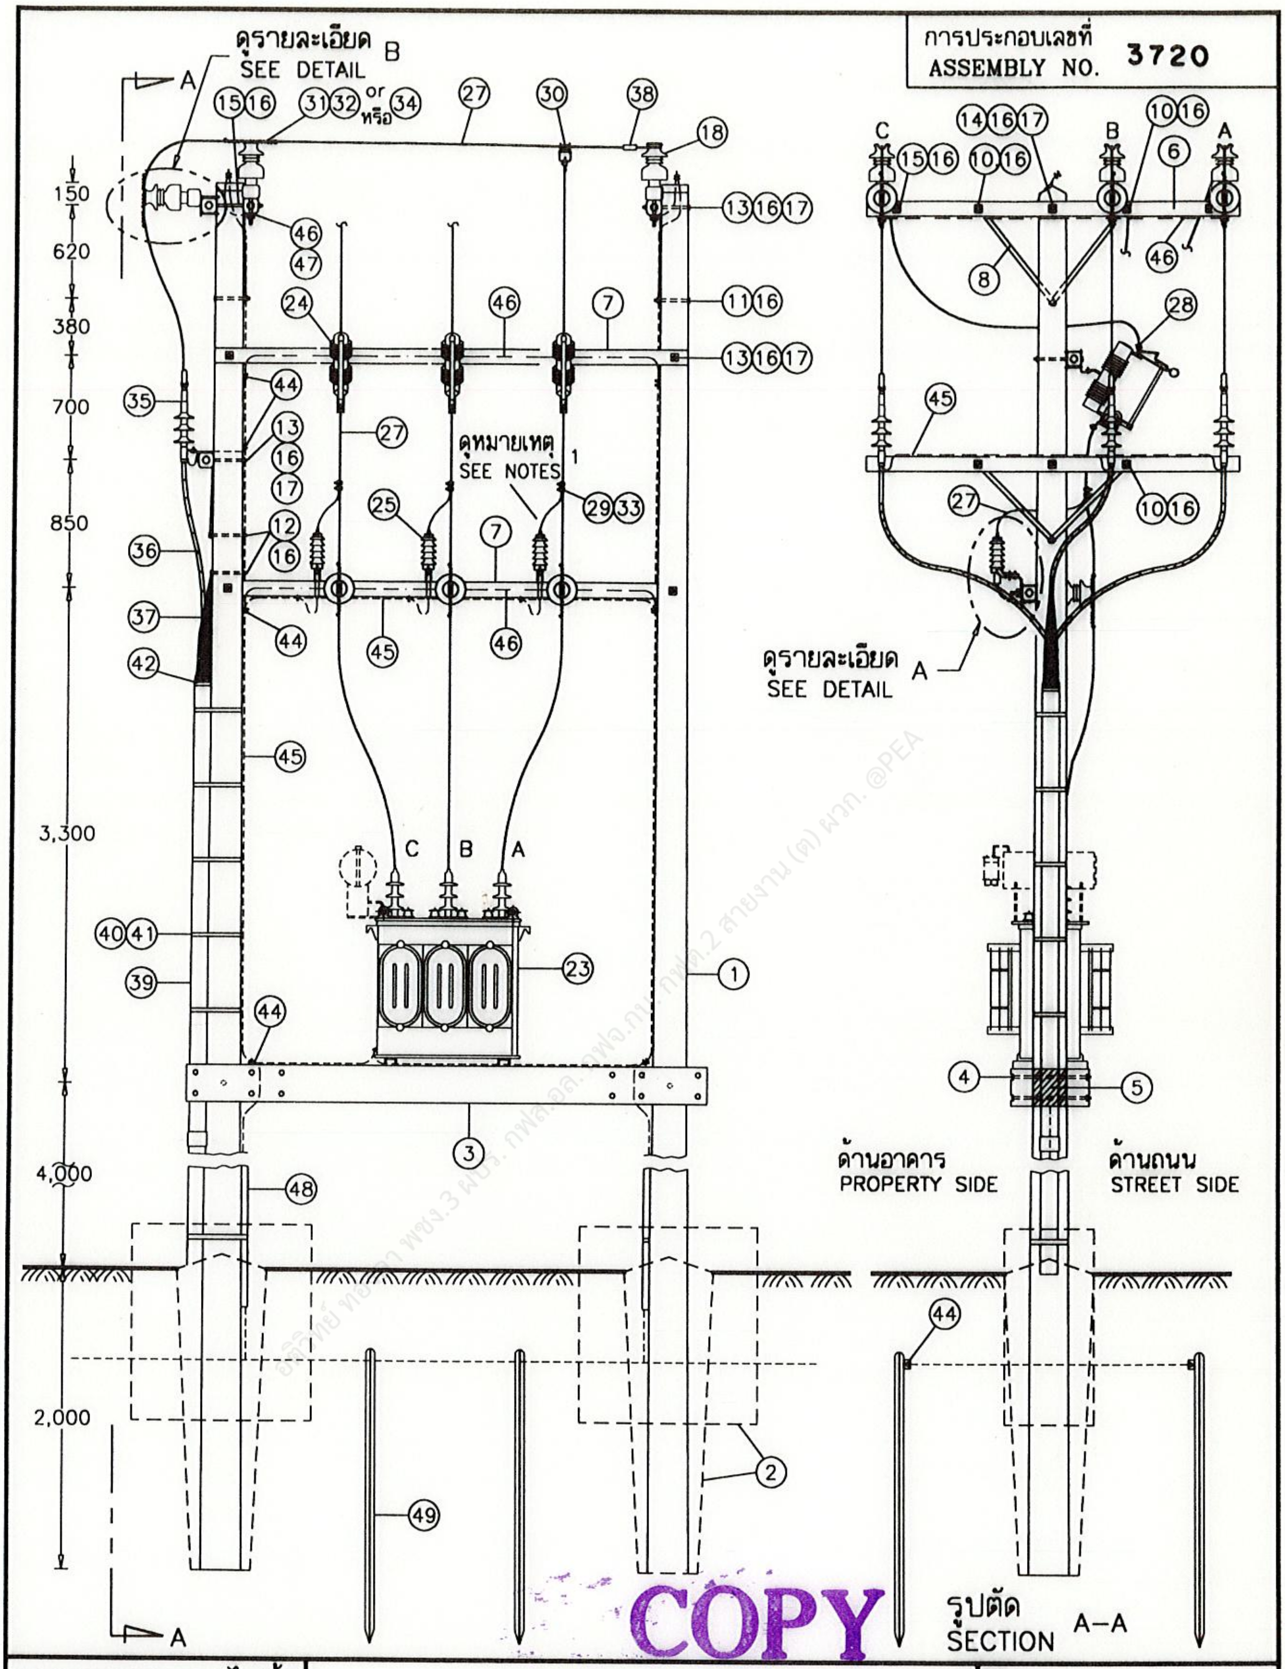

พชง.3 ผบร. กฟส.อล. กฟจ.กบ. กฟต.2 สายงาน (ต) ผวก. @PEA

COPY

กองมาตรฐานระบบไฟฟ้า ฝ่ายมาตรฐานและความปลอดภัย	การไฟฟ้าส่วนภูมิภาค	ใช้แทนแบบ .... ถูกแทนโดยแบบ ....
ผู้เขียน Supphakit Boonreung ผู้สำรวจ .... วิศวกร .... หัวหน้าแผนก .... ผู้อำนวยการกอง .... ผู้อำนวยการฝ่าย	ผู้ว่าการ .... 17 ธ.ค. 2544 การติดตั้งหม้อแปลง 3 เฟส ระบบ 33 kV ขนาด 50-500 kVA บนนั่งร้าน กรณีสายประธานเป็นเคเบิลใต้ดินแรงสูง I คอนแบบธรรมดา	เขียนเสร็จวันที่ 28 พ.ค. 2544 แก้แบบวันที่ .... มิติเป็น มิลลิเมตร มาตราส่วน 1 : 50
รองผู้ว่าการวางแผนและพัฒนาระบบไฟฟ้า	3-PHASE TRANSFORMER INSTALLATION 33 kV, 50-500 kVA, ON PLATFORM H.V. UNDERGROUND CABLE AS PRIMARY MAIN LINE I CROSS ARM	แบบเลขที่ SA4-015/44005 แผ่นที่ 1 ของจำนวน 8 แผ่น

การประกอบเลขที่
ASSEMBLY NO. **3720**

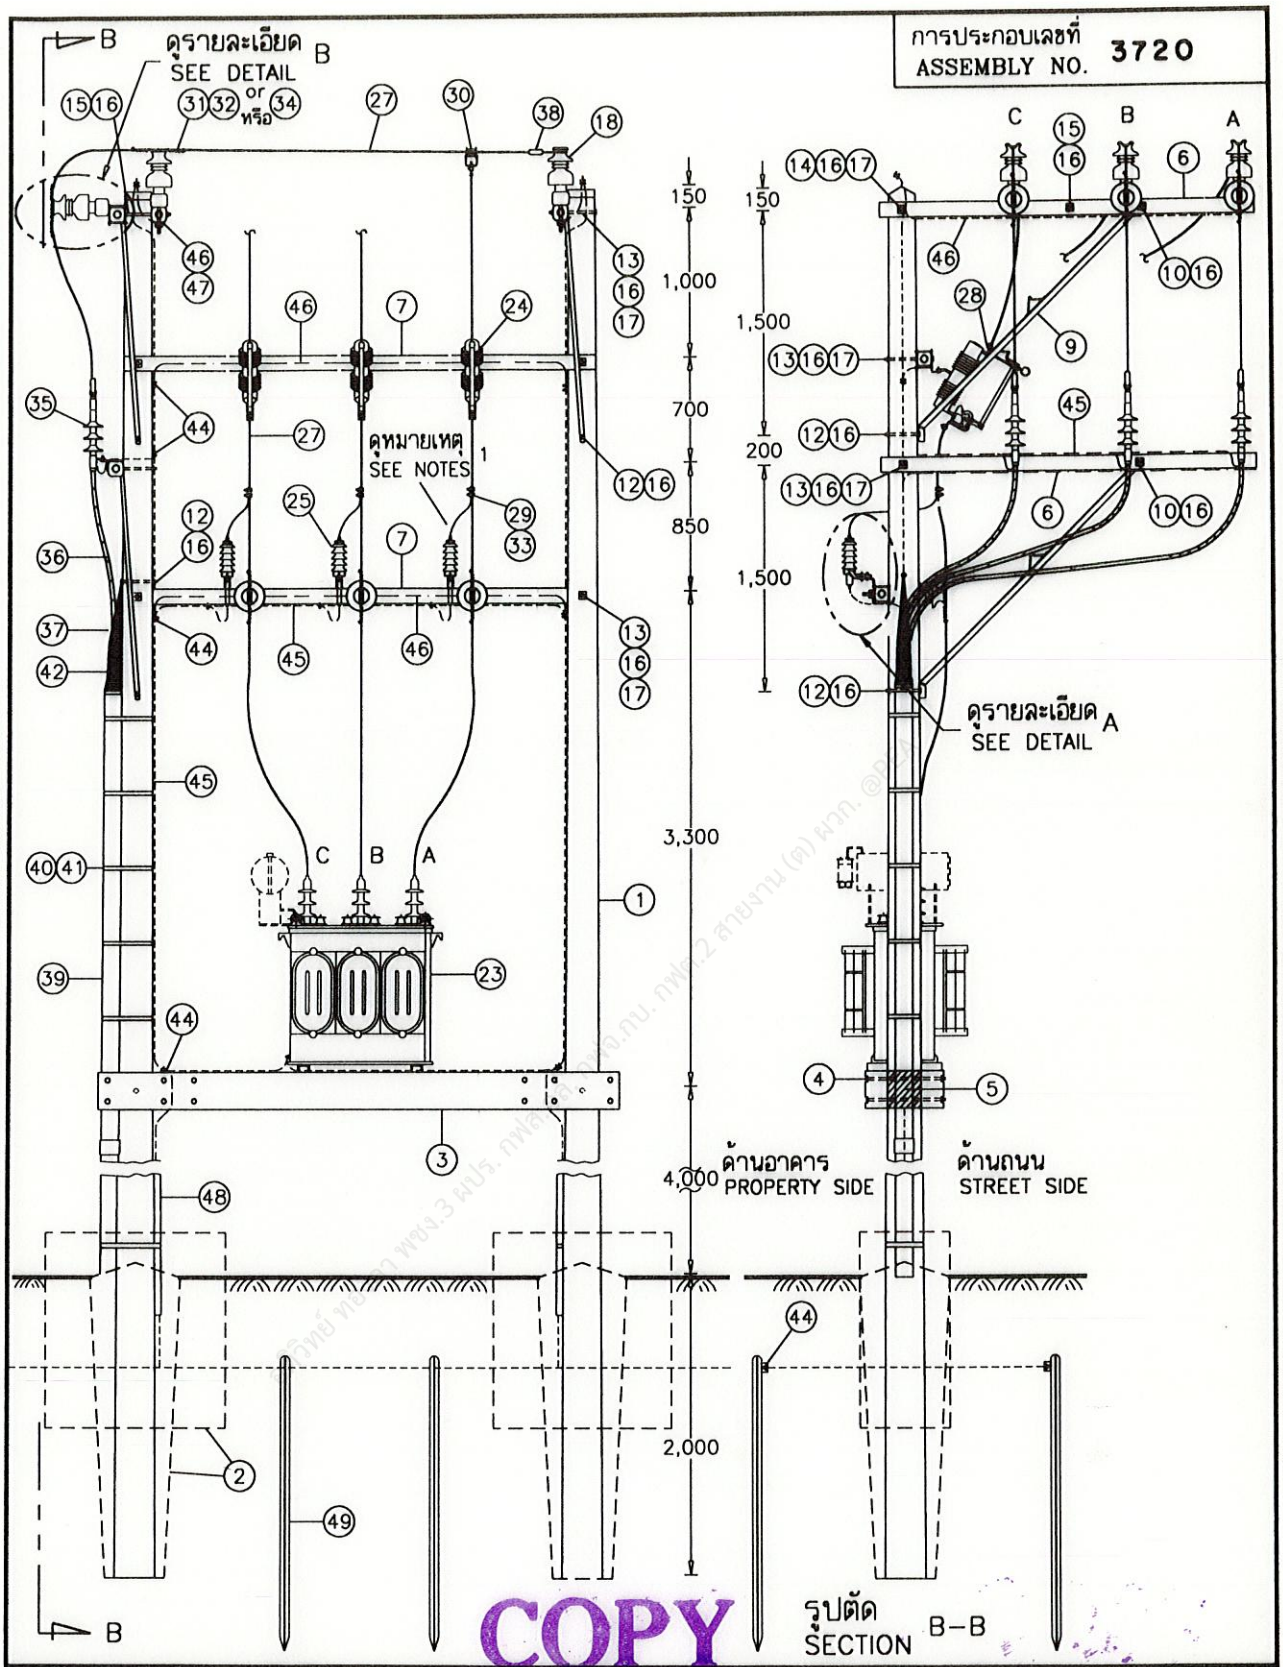

COPY

สุวิทย์ ทองทา พชง.3 ผปร. กฟส.ลล. กฟจ.กบ. กฟฉ.2 สายงาน (ด) ผวภ. @PEA

กองมาตรฐานระบบไฟฟ้า
ฝ่ายมาตรฐานและความปลอดภัย

การไฟฟ้าส่วนภูมิภาค

ใช้แทนแบบ..............
ถูกแทนโดยแบบ ....

ผู้เขียน Supphakit Boonreung
ผู้สำรวจ..................
วิศวกร......................
หัวหน้าแผนก..................
ผู้อำนวยการกอง..............
ผู้อำนวยการฝ่าย..............

ผู้ว่าการ.................................. 1 9 มิ.ย. 2544

เขียนเสร็จวันที่ 28 พ.ค. 2544
แก้แบบวันที่ ....

การติดตั้งหม้อแปลง 3 เฟส ระบบ 33 kV ขนาด 50–500 kVA
บนนั่งร้าน กรณีสายประธานเป็นเคเบิลใต้ดินแรงสูง
II คอนแบบทาวแขน

มิติเป็น มิลลิเมตร
มาตราส่วน 1 : 50

รองผู้ว่าการวางแผน
และพัฒนาระบบไฟฟ้า
....

3-PHASE TRANSFORMER INSTALLATION
33 kV, 50–500 kVA, ON PLATFORM
H.V. UNDERGROUND CABLE AS PRIMARY MAIN LINE
II ALLEY ARM

แบบเลขที่ SA4–015/44005
แผ่นที่ 2 ของจำนวน 8 แผ่น

การประกอบเลขที่
ASSEMBLY NO. **3720**

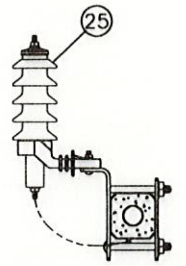

รายละเอียด
DETAIL A

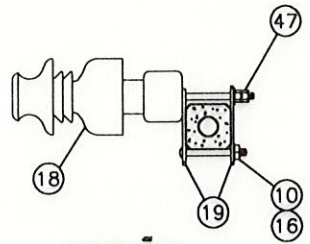

รายละเอียด
DETAIL B

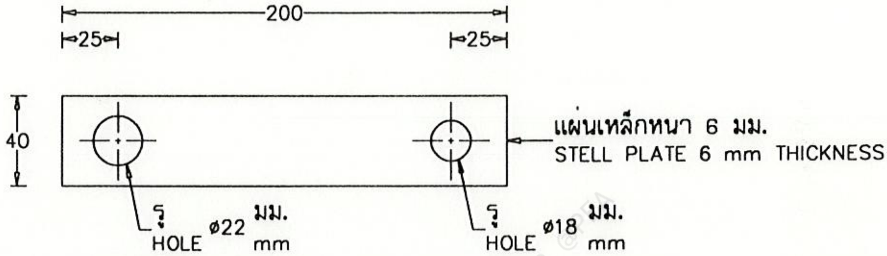

(ดัดแปลงโดยใช้เหล็กประกับ วัสดุเลขที่ 01200002 ได้)
(MAY BE MADE OF BRACE MAT NO.01200002)

⑲ แผ่นเหล็ก 40x6 มม. ยาว 200 มม.
STEEL PLATE, 40x6 mm, 200 mm LONG

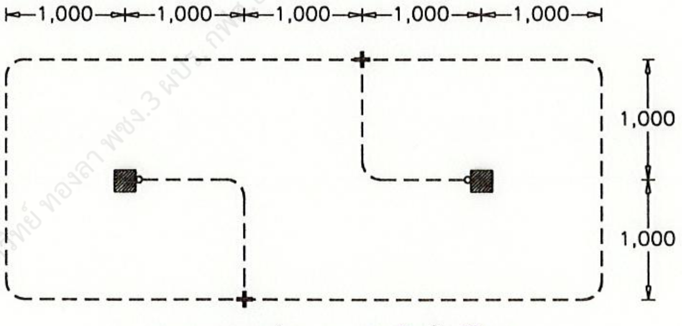

สำหรับกับดักเสิร์จและเปลือกหม้อแปลง
FOR H.V. SURGE ARRESTER AND TRANSFORMER CASE

รายละเอียดการต่อลงดิน
DETAIL OF EARTHING

COPY

กองมาตรฐานระบบไฟฟ้า
ฝ่ายมาตรฐานและความปลอดภัย

การไฟฟ้าส่วนภูมิภาค

ผู้เขียน
ผู้สำรวจ..................
วิศวกร..................
หัวหน้าแผนก..................
ผู้อำนวยการกอง..................
ผู้อำนวยการฝ่าย..................

ผู้ว่าการ.................. 13 มิ.ย. 2544

การติดตั้งหม้อแปลง 3 เฟส ระบบ 33 kV ขนาด 50–500 kVA
บนนั่งร้าน
กรณีสายประธานเป็นเคเบิลใต้ดินแรงสูง

3–PHASE TRANSFORMER INSTALLATION
33 kV, 50–500 kVA, ON PLATFORM
H.V. UNDERGROUND CABLE AS PRIMARY MAIN LINE

รองผู้ว่าการวางแผน
และพัฒนาระบบไฟฟ้า
....

ใช้แทนแบบ ....
ถูกแทนโดยแบบ ....
เขียนเสร็จวันที่ 28 พ.ค. 2544
แก้แบบวันที่ ....
มิติเป็น..................
มาตราส่วน..................
แบบเลขที่ SA4–015/44005
แผ่นที่ 3 ของจำนวน 8 แผ่น

การประกอบเลขที่
ASSEMBLY NO. **3720**

บัญชีวัสดุ
BILL OF MATERIAL

ลำดับที่ ITEM	รายละเอียด DESCRIPTION	จำนวน REQ'D I	II	วัสดุเลขที่ MAT. NO.
A	**เสาและฐานราก / POLE & FOUNDATION**			
1	เสาคอนกรีต 12 ม. หรือ 12.20 ม. POLE, CONCRETE 12 m OR 12.20 m LONG	2	2	00010004 or 00010012
2	คอนกรีต 1 : 2 : 4 พร้อมเหล็กเส้น เส้นผ่านศูนย์กลาง 15 มม. ยาว 500 มม. 2 ท่อน และยาว 1,100 มม. 2 ท่อน สำหรับสภาพดินอ่อนหรือแข็งปานกลาง (ดินท้องนาทั่วไปและดินเหนียวปนทราย) CONCRETE 1 : 2 : 4 COMP. WITH STEEL BAR ø15 mm, 500 mm LONG 2 EACH AND 1,100 mm LONG 2 EACH ; FOR POOR AND NORMAL SOIL CONDITION (MARCHY SOIL, CLAY & SANDY CLAY)	2 ม.^{3} m^3	2 ม.^{3} m^3	–
	คอนกรีต 1 : 3 : 5 สำหรับสภาพดินแข็ง (ดินทรายและดินลูกรัง) CONCRETE 1 : 3 : 5 ; FOR GOOD SOIL CONDITION (SANDY SOIL & LATERITIC SOIL)	0.75 ม.^{3} m^3	0.75 ม.^{3} m^3	–
B	**การประกอบคาน คอร. นั่งร้านหม้อแปลง / CONCRETE PLATFORM ASSEMBLY**			
3	คาน คอร. ขนาด 150x250x3,450 มม. หรือขนาด 150x250x3,550 มม. สำหรับนั่งร้านหม้อแปลง PRESTRESSED CONCRETE BEAM 150x250x3,450 mm OR 150x250x3,550 mm FOR TRANSFORMER PLATFORM	2	2	00210001 OR 00210003
4	สลักเกลียวหัวหกเหลี่ยม M 16x550 มม. สำหรับเสาคอนกรีต 12.00 ม. BOLT, MACHINE, HEXAGON M 16x550 mm FOR 12.00 m CONCRETE POLE	12	12	01110401
	สลักเกลียวหัวหกเหลี่ยม M 16x600 มม. สำหรับเสาคอนกรีต 12.20 ม. BOLT, MACHINE, HEXAGON M 16x600 mm FOR 12.20 m CONCRETE POLE			01110402
5	ปูนทราย 1 : 3 (ปูนซีเมนต์ผสมทรายหยาบ) MORTAR 1 : 3	50 กก. kg	50 กก. kg	–
C	**การประกอบคอนและคาน คอร. สปัน / CONCRETE CROSSARM AND BEAM ASSEMBLY**			
6	คอน คอร. สปัน ขนาด 120x120x3,000 มม. CROSSARM, SPUN PRESTRESSED CONCRETE, 120x120x3,000 mm	4	4	00110002
7	คาน คอร. สปัน ขนาด 100x100x3,200 มม. BEAM, SPUN PRESTRESSED CONCRETE, 100x100x3,200 mm	2	2	00210000
8	เหล็กประกับคอน 40x6x1,000 มม. BRACE, FLAT FOR CROSSARM 40x6x1,000 mm	6	–	01200002
9	เหล็กประกับคอน แบบท้าวแขน 50x50x6 มม. ยาว 2,350 มม. BRACE, ALLEY ARM, 50x50x6 mm, 2,350 mm LONG	–	3	01200005
10	สลักเกลียว M 16x170 มม. BOLT, MACHINE M 16x170 mm	9	6	01110201
11	สลักเกลียว M 16x200 มม. สำหรับเสาคอนกรีต 12.00 ม. BOLT, MACHINE M 16x200 mm FOR 12.00 m CONCRETE POLE	2	–	01110202
	สลักเกลียว M 16x250 มม. สำหรับเสาคอนกรีต 12.20 ม. BOLT, MACHINE M 16x250 mm FOR 12.20 m CONCRETE POLE			01110203

COPY

กองมาตรฐานระบบไฟฟ้า ฝ่ายมาตรฐานและความปลอดภัย	# การไฟฟ้าส่วนภูมิภาค	ใช้แทนแบบ .... ถูกแทนโดยแบบ ....
ผู้เขียน .... ผู้สำรวจ .... วิศวกร .... หัวหน้าแผนก .... ผู้อำนวยการกอง .... ผู้อำนวยการฝ่าย	ผู้ว่าการ .... 1 3 [illegible] 254	เขียนเสร็จวันที่ 28 พ.ค. 2544 แก้แบบวันที่ ....
	การติดตั้งหม้อแปลง 3 เฟส ระบบ 33 kV ขนาด 50–500 kVA บนนั่งร้าน กรณีสายประธานเป็นเคเบิลใต้ดินแรงสูง	มิติเป็น มิลลิเมตร มาตราส่วน ....
รองผู้ว่าการวางแผนและพัฒนาระบบไฟฟ้า	3-PHASE TRANSFORMER INSTALLATION 33 kV, 50–500 kVA, ON PLATFORM H.V. UNDERGROUND CABLE AS PRIMARY MAIN LINE	แบบเลขที่ SA4-015/44005 แผ่นที่ 4 ของจำนวน 8 แผ่น

การประกอบเลขที่
ASSEMBLY NO. **3720**

บัญชีวัสดุ
BILL OF MATERIAL

ลำดับที่ ITEM	รายละเอียด DESCRIPTION	จำนวน REQ'D I	จำนวน REQ'D II	วัสดุเลขที่ MAT. NO.
C	การประกอบคอนและคาน คอร. สปัน (ต่อ) / CONCRETE CROSSARM AND BEAM ASSEMBLY (CONT.)			
12	สลักเกลียว M 16x250 มม. สำหรับเสาคอนกรีต 12.00 ม. BOLT, MACHINE M 16x250 mm FOR 12.00 m CONCRETE POLE	2	4	01110203
	สลักเกลียว M 16x300 มม. สำหรับเสาคอนกรีต 12.20 ม. BOLT, MACHINE M 16x300 mm FOR 12.20 m CONCRETE POLE			01110204
13	สลักเกลียว M 16x350 มม. สำหรับเสาคอนกรีต 12.00 ม. BOLT, MACHINE M 16x350 mm FOR 12.00 m CONCRETE POLE	6	6	01110205
	สลักเกลียว M 16x400 มม. สำหรับเสาคอนกรีต 12.20 ม. BOLT, MACHINE M 16x400 mm FOR 12.20 m CONCRETE POLE			01110206
14	สลักเกลียว M 16x450 มม. สำหรับเสาคอนกรีต 12.00 ม. BOLT, MACHINE M 16x450 mm FOR 12.00 m CONCRETE POLE	1	1	01110207
	สลักเกลียว M 16x500 มม. สำหรับเสาคอนกรีต 12.20 ม. BOLT, MACHINE M 16x500 mm FOR 12.20 m CONCRETE POLE			01110208
15	สลักเกลียวตลอด M 16x500 มม. BOLT, DOUBLE ARMING, M 16x500 mm	2	2	01120002
16	แหวนสี่เหลี่ยมแบน 52x52x4.5 มม. รู ø18 มม. มอก. 258 WASHER, SQUARE, FLAT 52x52x4.5 mm HOLE ø18 mm TIS 258	35	33	01180100
17	แหวนรองแบบสปริง ขนาดระบุ 16 มม. ประเภทใช้งานทั่วไป มอก. 259 WASHER, LOCK, SPRING M 16 GENERAL PURPOSE TIS 259	7	7	01180301
18	ลูกถ้วยแท่ง หรือลูกถ้วยแท่งก้านตรง 33 kV ชนิดตามต้องการ INSULATOR, LINE POST TYPE OR PIN POST TYPE, 33 kV, TYPE AS REQUIRED	12	12	03010003-4 03010102-3
19	แผ่นเหล็ก 40x6 มม. ยาว 200 มม. STEEL PLATE, 40x6 mm, 200 mm LONG	6	6	–
20				
21				
22				

COPY

กองมาตรฐานระบบไฟฟ้า
ฝ่ายมาตรฐานและความปลอดภัย

ผู้เขียน Supphalit Boonruang
ผู้สำรวจ..................
วิศวกร.....................
หัวหน้าแผนก...............
ผู้อำนวยการกอง.............
ผู้อำนวยการฝ่าย............

รองผู้ว่าการวางแผน
และพัฒนาระบบไฟฟ้า
....

การไฟฟ้าส่วนภูมิภาค

ผู้ว่าการ.................... 13 มิ.ย. 2544

การติดตั้งหม้อแปลง 3 เฟส ระบบ 33 kV ขนาด 50-500 kVA
บนนั่งร้าน
กรณีสายประธานเป็นเคเบิลใต้ดินแรงสูง

3-PHASE TRANSFORMER INSTALLATION
33 kV, 50-500 kVA, ON PLATFORM
H.V. UNDERGROUND CABLE AS PRIMARY MAIN LINE

ใช้แทนแบบ ....
ถูกแทนโดยแบบ ....
เขียนเสร็จวันที่ 28 พ.ค. 2544
แก้แบบวันที่ ....
มิติเป็น..................
มาตราส่วน................

แบบเลขที่ SA4-015/44005
แผ่นที่ 5 ของจำนวน 8 แผ่น

การประกอบเลขที่
ASSEMBLY NO. **3720**

บัญชีวัสดุ
BILL OF MATERIAL

ลำดับที่ ITEM	รายละเอียด DESCRIPTION	จำนวน REQ'D I	จำนวน REQ'D II	วัสดุเลขที่ MAT. NO.
D	หม้อแปลงและอุปกรณ์ป้องกัน / TRANSFORMER & PROTECTIVE EQUIPMENTS			
23	หม้อแปลง 3 เฟส 33 kV ขนาด 50-500 kVA TRANSFORMER, 3-PHASE, 33 kV, 50-500 kVA	1	1	05010102 _ 05010109
24	ดรอพเอาต์ฟิวส์คัตเอาต์ หนึ่งอินซูเลเตอร์ 33 kV 100 A CUT-OUT, FUSE, OPEN TYPE, SINGLE INSULATOR, DROPOUT 33 kV, 100 A	3	3	04010100
25	กับดักเสิร์จ 30 kV 5 kA SURGE ARRESTER, 30 kV, 5 kA	3	3	04000100
26				
E	สายและอุปกรณ์ประกอบสายด้านแรงสูง / H.V. CONDUCTORS & ACCESORIES			
27	สายอะลูมิเนียมหุ้มฉนวนแบบไม่เต็มพิกัด แกนเดียว 33 kV ขนาดตามต้องการ CONDUCTOR, Al, PARTIAL INSULATED SINGLE-CORE, 33 kV SIZE AS REQUIRED	ม. 35 m	ม. 35 m	02060101-2
28	สลักต่อปลายสายเข้าอุปกรณ์ไฟฟ้าสำหรับสายอะลูมิเนียม PIN TERMINAL, FOR Al CONDUCTOR	6	6	02420400
29	พี.จี. คอนเนคเตอร์ สลักคู่ สำหรับสายอะลูมิเนียม 25-95 ต.มม. CONDUCTOR, PARALLEL GROOVE, DOUBLE BOLT, Al 25-95 mm^2	3	3	02300102
30	สเตอร์รัพแคล้มป์ หรือเบลแคล้มป์ และฮอทไลน์แคล้มป์ ขนาดตามต้องการ CLAMP, STIRRUP OR BAIL AND CLAMP, HOT LINE, SIZE AS REQUIRED	3	3	02330000-1 02330100-1
31	ลวดอะลูมิเนียมแบน 1x10 มม. ความยาวตามต้องการ ARMOUR TAPE, Al 1x10 mm LENGTH AS REQUIRED	–	–	02200000
32	ลวดอะลูมิเนียมกลม ขนาด ø4 มม. ความยาวตามต้องการ TIE WIRE, Al ø4 mm LENGTH AS REQUIRED	–	–	02200002
33	เทปพันเคเบิลอากาศแรงสูง ขนาด 3/4"x 30' และเทปไฟฟ้า PVC ใช้ภายนอก ม้วนขนาด 19 มม.x20 ม. ELECTRICAL SPLICING TAPE, FOR H.V. AERIAL CABLE, SIZE 3/4"x30' AND TAPE, ELECTRICAL, PVC PLASTIC, OUTDOOR TYPE, ROLL SIZE 19 mmx20m	ม. m	ม. m	02180003 02180002
34	ฉนวนของสายอะลูมิเนียมหุ้มฉนวนแบบไม่เต็มพิกัด ความยาวตามต้องการ PIC INSULATION, LENGTH AS REQUIRED	ม. m	ม. m	–

COPY

กองมาตรฐานระบบไฟฟ้า ฝ่ายมาตรฐานและความปลอดภัย	การไฟฟ้าส่วนภูมิภาค	ใช้แทนแบบ .... ถูกแทนโดยแบบ ....
ผู้เขียน Supphakit Boonsang ผู้สำรวจ .... วิศวกร .... หัวหน้าแผนก .... ผู้อำนวยการกอง .... ผู้อำนวยการฝ่าย	ผู้ว่าการ .... 13 มิ.ย. 254 การติดตั้งหม้อแปลง 3 เฟส ระบบ 33 kV ขนาด 50-500 kVA บนนั่งร้าน กรณีสายประธานเป็นเคเบิลใต้ดินแรงสูง	เขียนเสร็จวันที่ 28 พ.ค. 2544 แก้แบบวันที่ .... มิติเป็น .... มาตราส่วน ....
รองผู้ว่าการวางแผน และพัฒนาระบบไฟฟ้า	3-PHASE TRANSFORMER INSTALLATION 33 kV, 50-500 kVA, ON PLATFORM H.V. UNDERGROUND CABLE AS PRIMARY MAIN LINE	แบบเลขที่ SA4-015/44005 แผ่นที่ 6 ของจำนวน 8 แผ่น

การประกอบเลขที่ ASSEMBLY NO.	3720

บัญชีวัสดุ
BILL OF MATERIAL

ลำดับที่ ITEM	รายละเอียด DESCRIPTION	จำนวน REQ'D I	 II	วัสดุเลขที่ MAT. NO.
E	สายและอุปกรณ์ประกอบสายด้านแรงสูง (ต่อ) / H.V. CONDUCTORS & ACCESSORIES (CONT.)			
35	ชุดต่อปลายสายเคเบิล สำหรับภายนอกอาคาร 33 kV ขนาดตามต้องการ TERMINATION KITS, OUTDOOR TYPE, FOR 33 kV CABLE, SIZE AS REQUIRED	3	3	02150101-3
36	เคเบิลใต้ดิน ทองแดง 33 kV ขนาดและความยาวตามต้องการ CABLE, UNDERGROUND, Cu, 33 kV ; SIZE AS REQUIRED	ม. m	ม. m	
37	ห่วงรองรับสายเคเบิล CABLE GRIP	1	1	–
38	คอนเนคเตอร์เข้าปลายสายอะลูมิเนียมขนาดตามต้องการ CONNECTOR, DEAD END, Al ; SIZE AS REQUIRED	3	3	02310000-2
39	ท่อเหล็กร้อยสายเคเบิล ขนาด ø 100-125 มม. ยาว 4 เมตร พร้อมข้อต่อ CABLE STEEL CONDUIT ø 100-125 mm, 4 m LONG ; COMPLETE WITH COUPLING	2	2	–
40	เทปรัด 30x1.5 มม. รู ø 10 มม. PERFORATED TAPE 30x1.5 mm, HOLE ø 10 mm	ม. 18 m	ม. 18 m	–
41	สลักเกลียว M 8x25 มม. BOLT, MACHINE M 8x25 mm	12	12	01110000
42	คอมเปาด์ สำหรับอุดปิด จำนวนตามต้องการ SEALING COMPOUND, QUANTITY AS REQUIRED			–
43				
F	อุปกรณ์ต่อลงดิน / GROUNDING EQUIPMENTS			
44	ยูแคล้มป์ สลัก 1 ตัว M 8 CLAMP, SINGLE U-BOLT, M 8	38	38	01230000
45	ลวดเหล็กตีเกลียว 50/7 ต.มม. มอก. 404 STEEL STRANDED WIRE 50/7 mm^2, TIS 404	ม. 50 m	ม. 50 m	01110004
46	ลวดเหล็กกลม เส้นผ่านศูนย์กลาง 4 มม. เส้นเดี่ยว (มอก.71) WIRE, STEEL, SOLID, DIAMETER 4 mm (TIS 71)	ม. 14 m	ม. 14 m	01100000
47	แหวนสี่เหลี่ยมโค้ง 60x60x5 มม. รู ø22 มม. WASHER, SQUARE, CURVED 60x60x5 mm HOLE ø 22 mm	9	9	01180201
48	ท่อ PVC แข็ง ขนาด ø20 มม. พร้อมอุปกรณ์ยึด CONDUIT, PVC RIGID, ø20 mm, COMPLETE WITH FIXING ACCESSORIES	2	2	08040001-2
49	หลักดิน 60x60x5 มม. ยาว 2,000 มม. ROD, GROUND 60x60x5 mm, 2,000 mm LONG	2	2	01220002
50				

COPY

กองมาตรฐานระบบไฟฟ้า ฝ่ายมาตรฐานและความปลอดภัย	การไฟฟ้าส่วนภูมิภาค	ใช้แทนแบบ .... ถูกแทนโดยแบบ ....
ผู้เขียน .... ผู้สำรวจ .... วิศวกร .... หัวหน้าแผนก .... ผู้อำนวยการกอง .... ผู้อำนวยการฝ่าย	ผู้ว่าการ .... 13 มิ.ย. 2544 การติดตั้งหม้อแปลง 3 เฟส ระบบ 33 kV ขนาด 50-500 kVA บนนั่งร้าน กรณีสายประธานเป็นเคเบิลใต้ดินแรงสูง	เขียนเสร็จวันที่ 28 พ.ค. 2544 แก้แบบวันที่ .... มิติเป็น .... มาตราส่วน ....
รองผู้ว่าการวางแผน และพัฒนาระบบไฟฟ้า	3-PHASE TRANSFORMER INSTALLATION 33 kV, 50-500 kVA, ON PLATFORM H.V. UNDERGROUND CABLE AS PRIMARY MAIN LINE	แบบเลขที่ SA4-015/44005 แผ่นที่ 7 ของจำนวน 8 แผ่น

การประกอบเลขที่ ASSEMBLY NO.	**3720**

	แบบอ้างอิง REFERENCE DRAWING	แบบเลขที่ DWG. NO.	การประกอบเลขที่ ASSEMBLY NO.
1	การทำฐานรากเสาคู่ประกอบนั่งร้านหม้อแปลง POLE FOUNDATION AT TRANSFORMER STATION	IB1-015/240032	8503
2	การติดตั้งคาน คอร. นั่งร้านหม้อแปลง PRESTRESSED CONCRETE PLATFORM INSTALLATION	IB2-015/39015	3706
3	การประกอบคอน คอร. สปัน กับเสาคอนกรีต ระบบ 33 kV SPUN PRESTRESSED CONCRETE CROSSARM ASSEMBLY 33 kV SYSTEM	SA1-015/21021 SA1-015/21022	3803 3804
4	การติดตั้งอุปกรณ์ป้องกันและการต่อลงดิน สำหรับการติดตั้งหม้อแปลง 3 เฟส ระบบ 33 kV ขนาด ต่ำกว่า 160 kVA บนนั่งร้าน PROTECTION DEVICE INSTALLATION AND EARTHING FOR 3-PHASE TRANSFORMER, 33 kV, LASS THAN 160 kVA, ON PLATFORM	SA4-015/43005	3702
5	การต่อลงดินระบบแรงสูง และแรงต่ำ H.V. AND L.V. EARTHING SYSTEM	S02-015/20039	9701

หมายเหตุ

1. กรณีที่หม้อแปลงมีขนาดต่ำกว่า 160 kVA ให้ดูแบบเลขที่ SA4-015/43005 (การประกอบเลขที่ 3702) สำหรับการติดตั้งกับดักเสิร์จแรงสูง
2. ขนาดของหม้อแปลง ที่ติดตั้งบนนั่งร้าน ดูแบบเลขที่ IB2-015/39015 (การประกอบเลขที่ 3706)
3. หม้อแปลงขนาด 500 kVA ต้องมีคุณสมบัติดังนี้ :-
   - แรงดันอิมพีแดนซ์ ค่าระบุที่ 75°C ⩾ 6.5%
   - น้ำหนักไม่เกิน 3,000 กก.
   - ขนาดความยาว ความสูงไม่เกิน 2x2 ม.
4. การติดตั้งอุปกรณ์ด้านแรงต่ำผู้ใช้ไฟเป็นผู้จัดทำ
5. บัญชีวัสดุ :-
   สดมภ์ I : สำหรับการติดตั้งคอนแบบธรรมดา
   สดมภ์ II : สำหรับการติดตั้งคอนแบบท้าวแขน

NOTES

1. H.V. SURGE ARRESTER INSTALLATION, IN CASE OF TRANSFORMER SIZE LESS THAN 160 kVA SEE DWG. NO. SA4-015/43005 (ASSEMBLY NO. 3702)
2. RECOMMENDED SIZE OF TRANSFORMER, INSTALLED ON PLATFORM, SEE DWG. NO. IB2-015/39015 (ASSEMBLY NO. 3706).
3. 500 kVA TRANSFORMER SHALL BE SPECIFICATION AS :-
   - IMPEDANCE VOLTAGE NOMINAL VALUE AT 75°C ⩾ 6.5%
   - NET WEIGHT NOT MORE THAN 3,000 kg
   - SIZE (LENGTH x HIGHT) NOT MORE THAN 2x2 m
4. INSTALLATION IN LOW VOLTAGE SIDE SHALL BE PROVIDED BY CUSTOMER
5. BILL OF MATERIAL :-
   COLUMN I : FOR CROSS ARM INSTALLATION
   COLUMN II : FOR ALLEY ARM INSTALLATION

COPY

กฟจ.กบ. กฟต.2 สายงาน (ต) ผวก. ©PEA

กองมาตรฐานระบบไฟฟ้า ฝ่ายมาตรฐานและความปลอดภัย	การไฟฟ้าส่วนภูมิภาค	ใช้แทนแบบ .... ถูกแทนโดยแบบ ....
ผู้เขียน Sypkdit Boonrung ผู้สำรวจ .... วิศวกร .... หัวหน้าแผนก .... ผู้อำนวยการกอง .... ผู้อำนวยการฝ่าย	ผู้ว่าการ .... การติดตั้งหม้อแปลง 3 เฟส ระบบ 33 kV ขนาด 50-500 kVA บนนั่งร้าน กรณีสายประธานเป็นเคเบิลใต้ดินแรงสูง	เขียนเสร็จวันที่ 28 พ.ค. 2544 แก้แบบวันที่ .... มิติเป็น .... มาตราส่วน ....
รองผู้ว่าการวางแผน และพัฒนาระบบไฟฟ้า	3-PHASE TRANSFORMER INSTALLATION 33 kV, 50-500 kVA, ON PLATFORM H.V. UNDERGROUND CABLE AS PRIMARY MAIN LINE	แบบเลขที่ SA4-015/44005 แผ่นที่ 8 ของจำนวน 8 แผ่น