การประกอบเลขที่ 5230
ASSEMBLY NO.

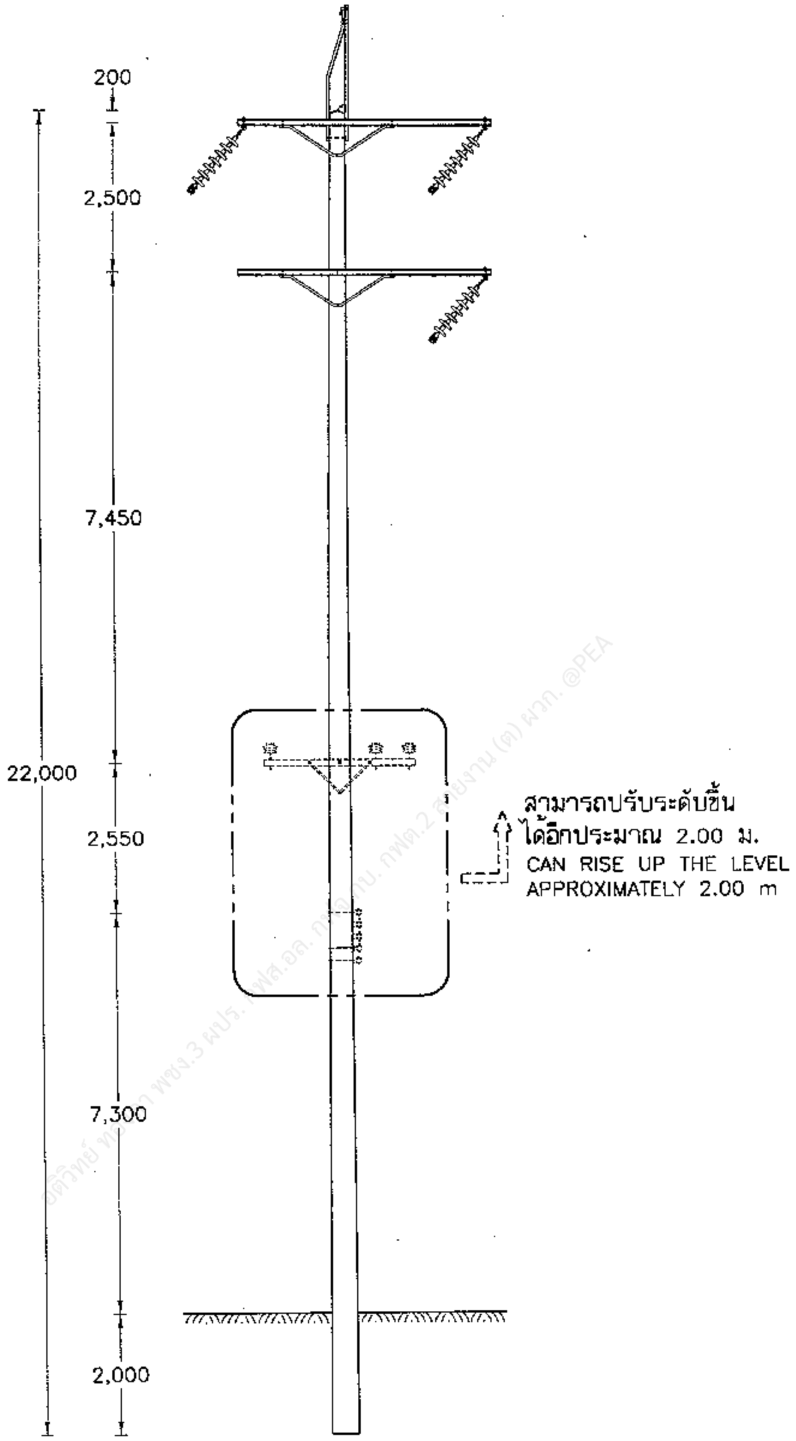

สามารถปรับระดับขึ้นได้อีกประมาณ 2.00 ม.
CAN RISE UP THE LEVEL APPROXIMATELY 2.00 m

อดิวิทย์ ท[illegible] พชง.3 ผปร. กฟส.อล. [illegible] กฟฉ.2 สายงาน (ต) ผวก. @PEA

กองวิศวกรรมไฟฟ้าและเครื่องกล
ฝ่ายวิศวกรรม

การไฟฟ้าส่วนภูมิภาค

ผู้เขียน
ผู้สำรวจ
วิศวกร
หัวหน้าแผนก (แทน)
ผู้อำนวยการกอง
ผู้อำนวยการฝ่าย

รองผู้ว่าการเทคนิคและบริการ

ผู้ว่าการ - 3 ส.ค. 2542

115 kV วงจรเดียว สายไฟฟ้าเดี่ยว
เสาสำหรับทางโค้ง
แบบ SS–SA–6

115 kV SINGLE CIRCUIT, SINGLE CONDUCTOR
ANGLE STRUCTURE
TYPE SS–SA–6

ใช้แทนแบบ
ถูกแทนโดยแบบ
เขียนเสร็จวันที่ 22 ก.พ. 2542
แก้แบบวันที่
มิติเป็น มิลลิเมตร
มาตราส่วน 1 : 125
แบบเลขที่ SA1–015/42003
แผ่นที่ 1 ของจำนวน 3 แผ่น

- 3 ส.ค. 2542

การประกอบเลขที่ ASSEMBLY NO. **5230**

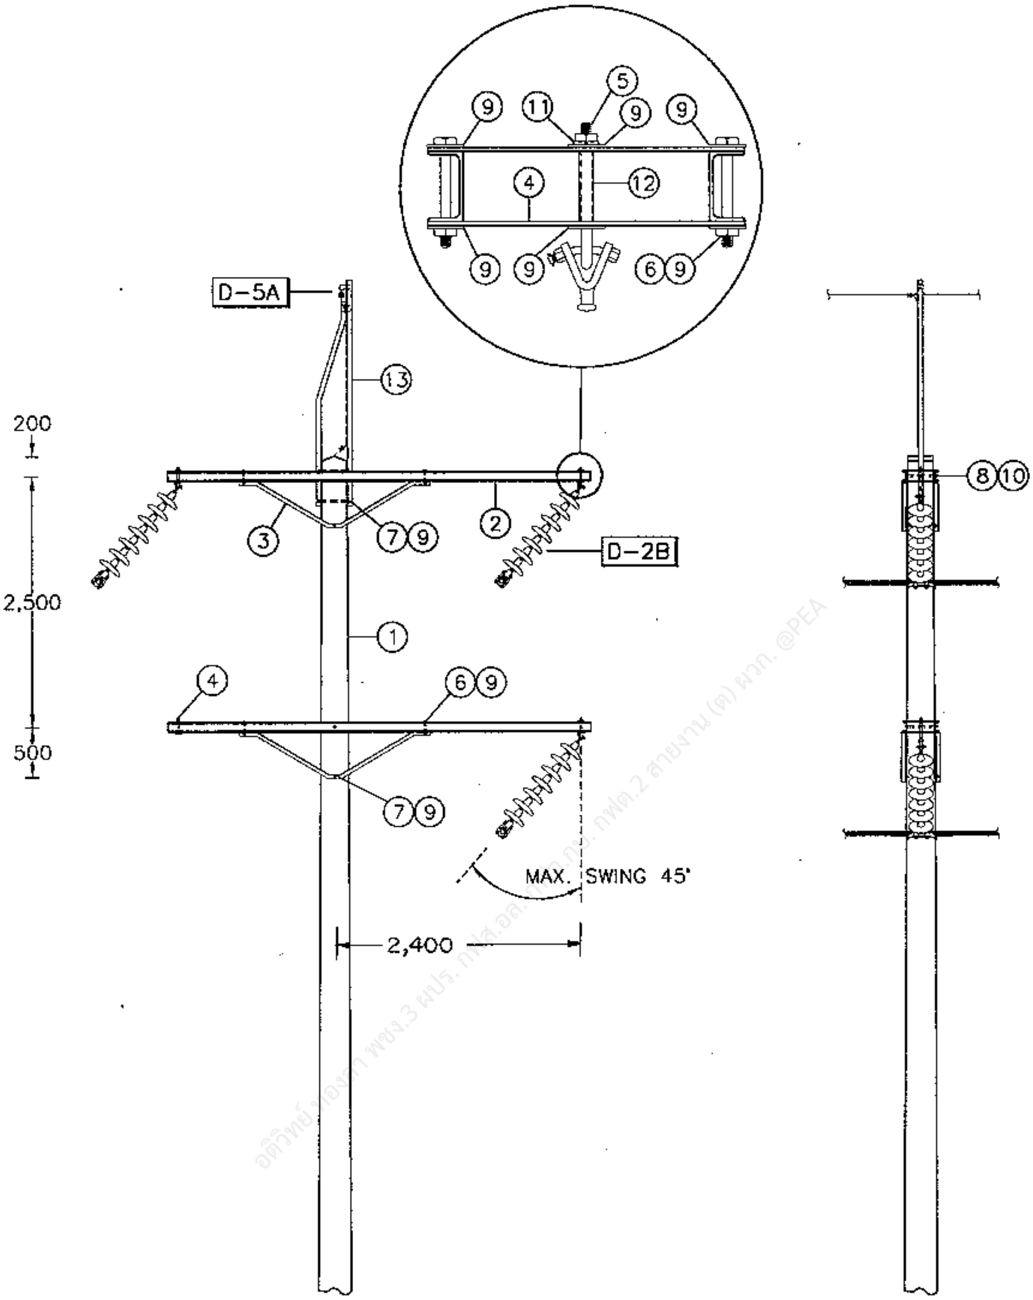

อดิวิทย์ ทองงาม พชง.3 ผปร. กฟส.อล. [illegible] กฟต.2 สายงาน (ต) ผวก. @PEA

กองวิศวกรรมไฟฟ้าและเครื่องกล ฝ่ายวิศวกรรม	**การไฟฟ้าส่วนภูมิภาค**	ใช้แทนแบบ .... ถูกแทนโดยแบบ ....
ผู้เขียน Supphakit Boonmung ผู้สำรวจ.................. วิศวกร.................. หัวหน้าแผนก.......(mmi) ผู้อำนวยการกอง.......... ผู้อำนวยการฝ่าย..........	ผู้ว่าการ.......................... - 3 มี.ค. 2542 115 kV วงจรเดียว สายไฟฟ้าเดี่ยว เสาสำหรับทางโค้ง แบบ SS-SA-6	เขียนเสร็จวันที่ 22 ก.พ. 2542 แก้แบบวันที่ .... มิติเป็น มิลลิเมตร มาตราส่วน 1 : 75
รองผู้ว่าการเทคนิคและบริการ	115 kV SINGLE CIRCUIT, SINGLE CONDUCTOR ANGLE STRUCTURE TYPE SS-SA-6	แบบเลขที่ SA1-015/42003 แผ่นที่ 2 ของจำนวน 3 แผ่น

- 3 มี.ค. 2542

การประกอบเลขที่ ASSEMBLY NO.	5 2 3 0

บัญชีวัสดุ
BILL OF MATERIAL

ลำดับที่ ITEM	รายละเอียด DESCRIPTION	จำนวน REQ'D	วัสดุเลขที่ MAT. NO.
1	เสาคอนกรีต 22 ม. POLE, CONCRETE 22 m LONG	1	00010011
2	คอนสายแบบเหล็กรูปรางน้ำ 100x50x5 มม. ยาว 4.20 ม. มอก. 116 CROSSARM, STEEL, CHANNEL 100x50x5 mm, 4.20 m LONG, TIS 116	4	01000103
3	เหล็กฉากรับคอนสายขนาด 50x50x6 มม. ช่วงกว้าง 1,800 มม. ดรอพ 450 มม. BRACE, ANGLE STEEL, 50X50X6 mm, 1,800 mm WIDE 450 mm DROP	4	00120007
4	แผ่นเหล็กขนาด 6x100x450 มม. PLATE, STEEL 6x100x450 mm	8	01030002
5	สลักห่วงโอแวล M 16x150 มม. BOLT, OVAL EYE M 16x150 mm	3	01150000
6	สลักเกลียว M 16x130 มม. BOLT, MACHINE M 16x130 mm	16	01110200
7	สลักเกลียว M 16x350 มม. BOLT, MACHINE M 16x350 mm	5	01110301
8	สลักเกลียว M 20x400 มม. BOLT, MACHINE M 20x400 mm	2	01110301
9	แหวนสี่เหลี่ยมแบน 52x52x4.5 มม. รู ø18 มม. มอก. 258 WASHER, SQUARE FLAT 52x52x4.5 mm HOLE ø18 mm TIS 258	33	01180100
10	แหวนสี่เหลี่ยมแบน 62x62x6 มม. รู ø22 มม. มอก. 258 WASHER, SQUARE FLAT 62x62x6 mm HOLE ø22 mm TIS 258	2	01180101
11	แหวนสปริง M 16 มอก. 259 WASHER, LOCK M 16 TIS 259	3	01180301
12	ท่อเหล็กขนาด 20 มม. หนา 2.65 มม. ยาว 100 มม. มอก. 277 ประเภท 2 PIPE, IRON DIA. 20 mm ID, 2.65 mm THICKNESS, 100 mm LONG, TIS 277 TYPE 2	3	01050000
13	เหล็กฉากรับสายล่อฟ้าทางโค้ง OVERHEAD GROUND WIRE CORNER BAYONET	1	01010005

รายละเอียด
DETAIL

D-2B	การประกอบลูกถ้วยแขวน SUSPENSION INSULATOR ASSEMBLY	3	
D-5A	การต่อสายล่อฟ้า OVERHEAD GROUND WIRE CONNECTION	1	
D-10A*	ฐานรากเสา POLE FOUNDATION	1	

* สามารถเปลี่ยนได้ตามความเหมาะสม
CAN BE CHANGEDTO BE SUITABLE

กองวิศวกรรมไฟฟ้าและเครื่องกล ฝ่ายวิศวกรรม	การไฟฟ้าส่วนภูมิภาค	ใช้แทนแบบ .... ถูกแทนโดยแบบ ....
ผู้เขียน.................. ผู้สำรวจ.................. วิศวกร.................. หัวหน้าแผนก.................. ผู้อำนวยการกอง.................. ผู้อำนวยการฝ่าย..................	ผู้ว่าการ.............................. - 3 มี.ค. 2542 115 kV วงจรเดียว สายไฟฟ้าเดี่ยว เสาสำหรับทางโค้ง แบบ SS-SA-6	เขียนเสร็จวันที่ 22 ก.พ. 2542 แก้แบบวันที่ .... มิติเป็น.................. มาตราส่วน..................
รองผู้ว่าการเทคนิคและบริการ	115 kV SINGLE CIRCUIT, SINGLE CONDUCTOR ANGLE STRUCTURE TYPE SS-SA-6	แบบเลขที่ SA1-015/42003 แผ่นที่ 3 ของจำนวน 3 แผ่น

- 3 มี.ค. 2542