การประกอบเลขที่
ASSEMBLY NO. 5687 J

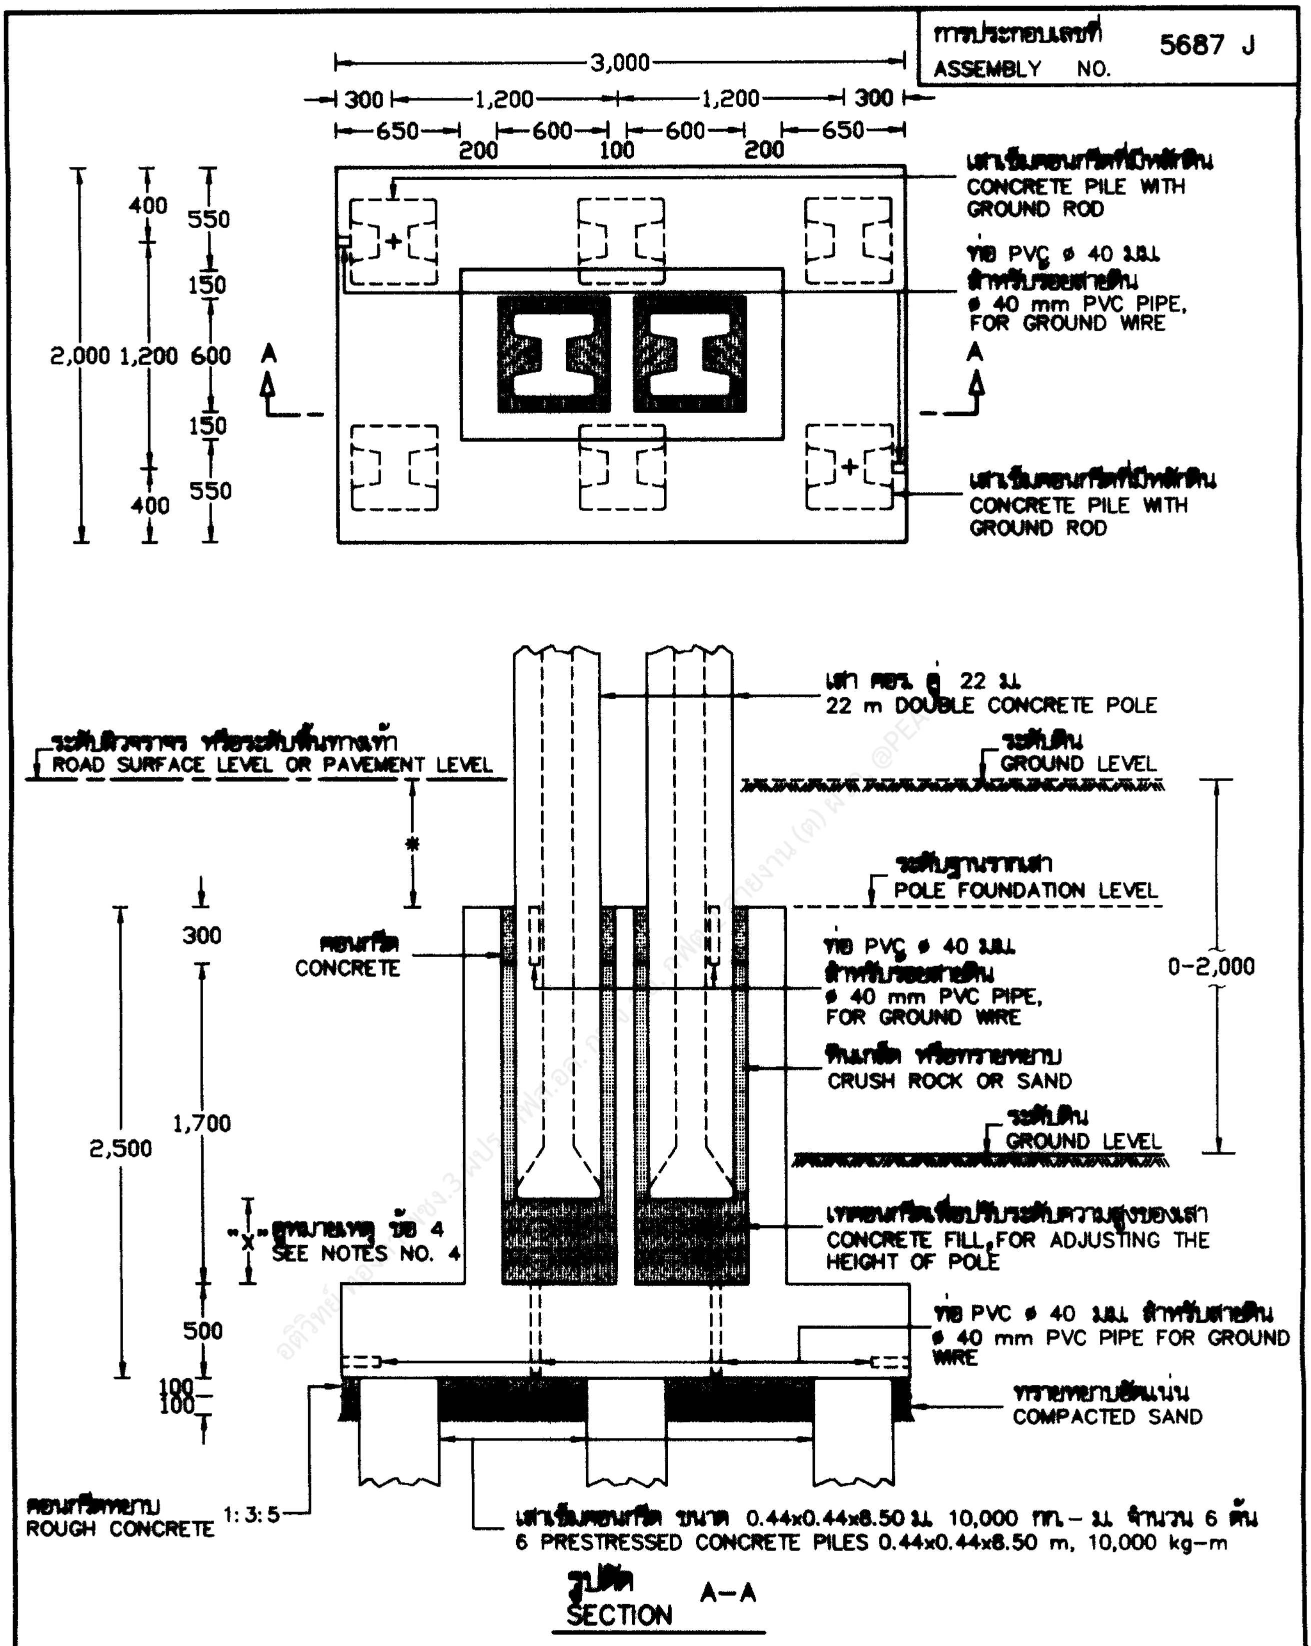
3,000
300
1,200
1,200
300
650
600
600
650
200
100
200
2,000
1,200
400
550
150
600
150
550
400
A
A
เสาเข็มคอนกรีตที่มีหลักดิน
CONCRETE PILE WITH GROUND ROD
ท่อ PVC ø 40 มม.
สำหรับร้อยสายดิน
ø 40 mm PVC PIPE, FOR GROUND WIRE
เสาเข็มคอนกรีตที่มีหลักดิน
CONCRETE PILE WITH GROUND ROD
เสา คอร. คู่ 22 ม.
22 m DOUBLE CONCRETE POLE
ระดับผิวจราจร หรือระดับพื้นทางเท้า
ROAD SURFACE LEVEL OR PAVEMENT LEVEL
ระดับดิน
GROUND LEVEL
*
ระดับฐานรากเสา
POLE FOUNDATION LEVEL
300
คอนกรีต
CONCRETE
ท่อ PVC ø 40 มม.
สำหรับร้อยสายดิน
ø 40 mm PVC PIPE, FOR GROUND WIRE
0–2,000
หินเกล็ด หรือทรายหยาบ
CRUSH ROCK OR SAND
2,500
1,700
ระดับดิน
GROUND LEVEL
"X"
ดูหมายเหตุ ข้อ 4
SEE NOTES NO. 4
เทคอนกรีตเพื่อปรับระดับความสูงของเสา
CONCRETE FILL FOR ADJUSTING THE HEIGHT OF POLE
500
ท่อ PVC ø 40 มม. สำหรับสายดิน
ø 40 mm PVC PIPE FOR GROUND WIRE
100
100
ทรายหยาบอัดแน่น
COMPACTED SAND
คอนกรีตหยาบ
ROUGH CONCRETE 1:3:5
เสาเข็มคอนกรีต ขนาด 0.44x0.44x8.50 ม. 10,000 กก.-ม. จำนวน 6 ต้น
6 PRESTRESSED CONCRETE PILES 0.44x0.44x8.50 m, 10,000 kg-m

รูปตัด A–A
SECTION A–A

กองมาตรฐานระบบไฟฟ้า
ฝ่ายมาตรฐานและความปลอดภัย

ผู้เขียน ..สมชาย..........
ผู้ตรวจ ....
วิศวกร ....
หัวหน้าแผนก ....
ผู้อำนวยการกอง ....
ผู้อำนวยการฝ่าย ....

รองผู้ว่าการวางแผนและพัฒนาระบบไฟฟ้า

12 3 ก.ย. 2547

การไฟฟ้าส่วนภูมิภาค

ผู้ว่าการ ....

รายละเอียดที่ 10B 3 ก.ย. 2547
ฐานรากเสา (แบบที่ 11)

DETAIL 10B
POLE FOUNDATION (TYPE 11)

ใช้แทนแบบ SA1–015/45019
ถูกแทนโดยแบบ ....
เขียนเสร็จวันที่ .10. มค. 2547
แก้แบบวันที่ ....
หน่วยเป็น .มิลลิเมตร..........
มาตราส่วน ....1:40..........
แบบเลขที่. SA1–015/47027.
แผ่นที่ .1. ของจำนวน .2. แผ่น

การประกอบเลขที่ ASSEMBLY NO.	5687 J

หมายเหตุ

1 ใช้ในกรณีทางตรงหรือทางโค้ง ที่มีและไม่มีสายยึดโยง (กรณีพื้นที่ก่อสร้างฐานรากเสามีระดับต่ำกว่าระดับผิวจราจร หรือระดับพื้นทางเท้า 0.00-2.00 ม.)

2 ดูรายละเอียดเพิ่มเติมใน แบบเลขที่ IB2-011/44018

3* ดูข้อกำหนดการติดตั้งฐานรากเสาในเขตทางหลวง ตามแบบเลขที่ SA1-015/43012 (การประกอบเลขที่ 5687)

4 ระยะ "X"= 450 มม. สำหรับการก่อสร้างฐานรากเสา ในพื้นที่ทางหลวงที่ไม่มีทางเท้า ส่วนพื้นที่อื่นๆ ระยะ "X"= 0 มม.

NOTES

1 USE FOR STRAIGHT OR ANGLE LINE WITH AND WITHOUT GUY (IN CASE OF GROUND SURFACE LEVEL IS BETWEEN 0.00–2.00 m LOWER THAN ROAD SURFACE LEVEL OR PAVEMENT LEVEL) .

2 SEE ADDITIONAL DETAIL, DWG. NO. IB2-011/44018 .

3* SEE RECOMMENDATION, FOR POLE FOUNDATION INSTALLATION IN HIGHWAY AREA, DWG. NO SA1-015/43012 (ASSEMBLY NO. 5687) .

4 THE "X" IS 450 mm HEIGHT FOR FOUNDATION CONSTRUCTION IN HIGHWAY AREA WHICH HAVE NO PAVEMENT, OTHER AREA THE "X" IS ZERO .

อดิศักดิ์ ทองลา พชง.3 ผปร. กฟส.อล. กฟจ.กน. กฟฉ.2 สายงาน (ต) ผวก. @PEA

กองมาตรฐานระบบไฟฟ้า ฝ่ายมาตรฐานและความปลอดภัย	การไฟฟ้าส่วนภูมิภาค	ใช้แทนแบบ SA1-015/45019 ถูกแทนโดยแบบ ....
ผู้เขียน ..สมชาย.......... ผู้ตรวจ .... วิศวกร .... หัวหน้าแผนก .... ผู้อำนวยการกอง .... ผู้อำนวยการฝ่าย	ผู้ว่าการ .... รายละเอียดที่ 10B 3 ก.ย. 2547 ฐานรากเสา (แบบที่ 11)	เขียนเสร็จวันที่ .10. พ.ค. 2547. แก้แบบวันที่ .... มิติเป็น .... มาตราส่วน..............
รองผู้ว่าการวางแผนและพัฒนาระบบไฟฟ้า	DETAIL 10B POLE FOUNDATION (TYPE 11)	แบบเลขที่ .SA1-015/47027. แผ่นที่ .2. ของจำนวน .2. แผ่น

12 ก.ย. 2547