การประกอบเลขที่ ASSEMBLY NO. 3807

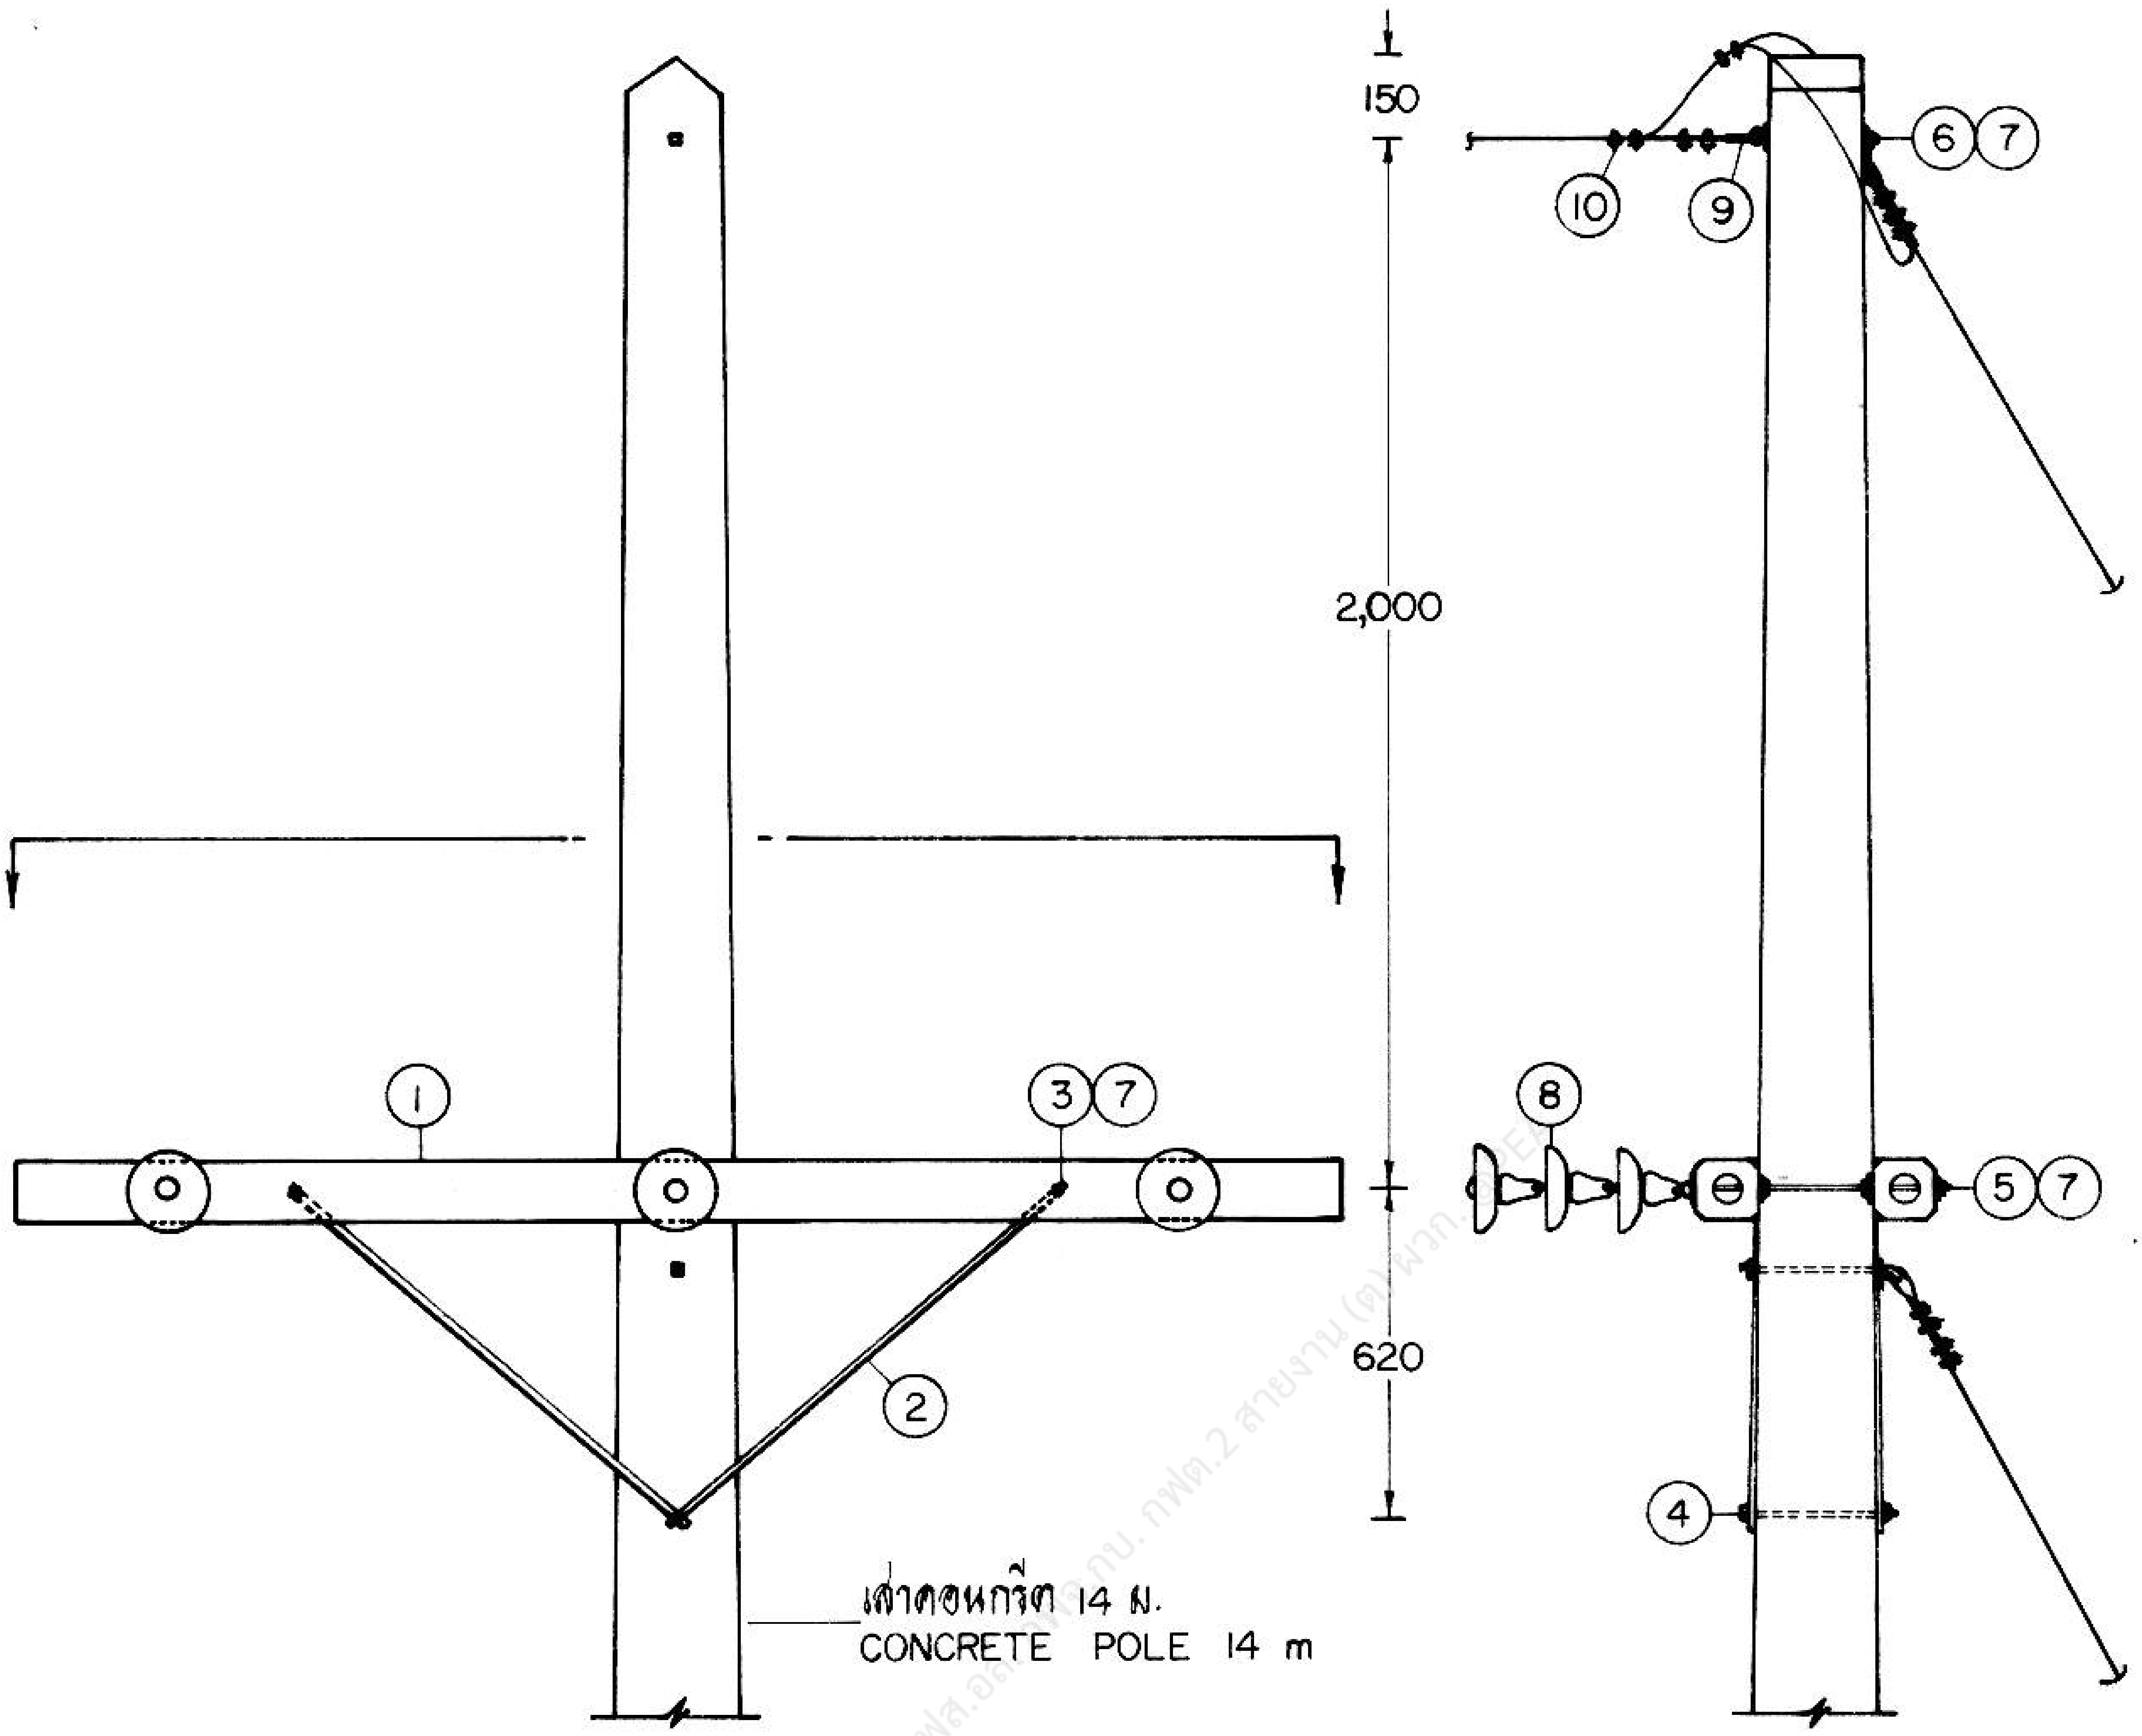

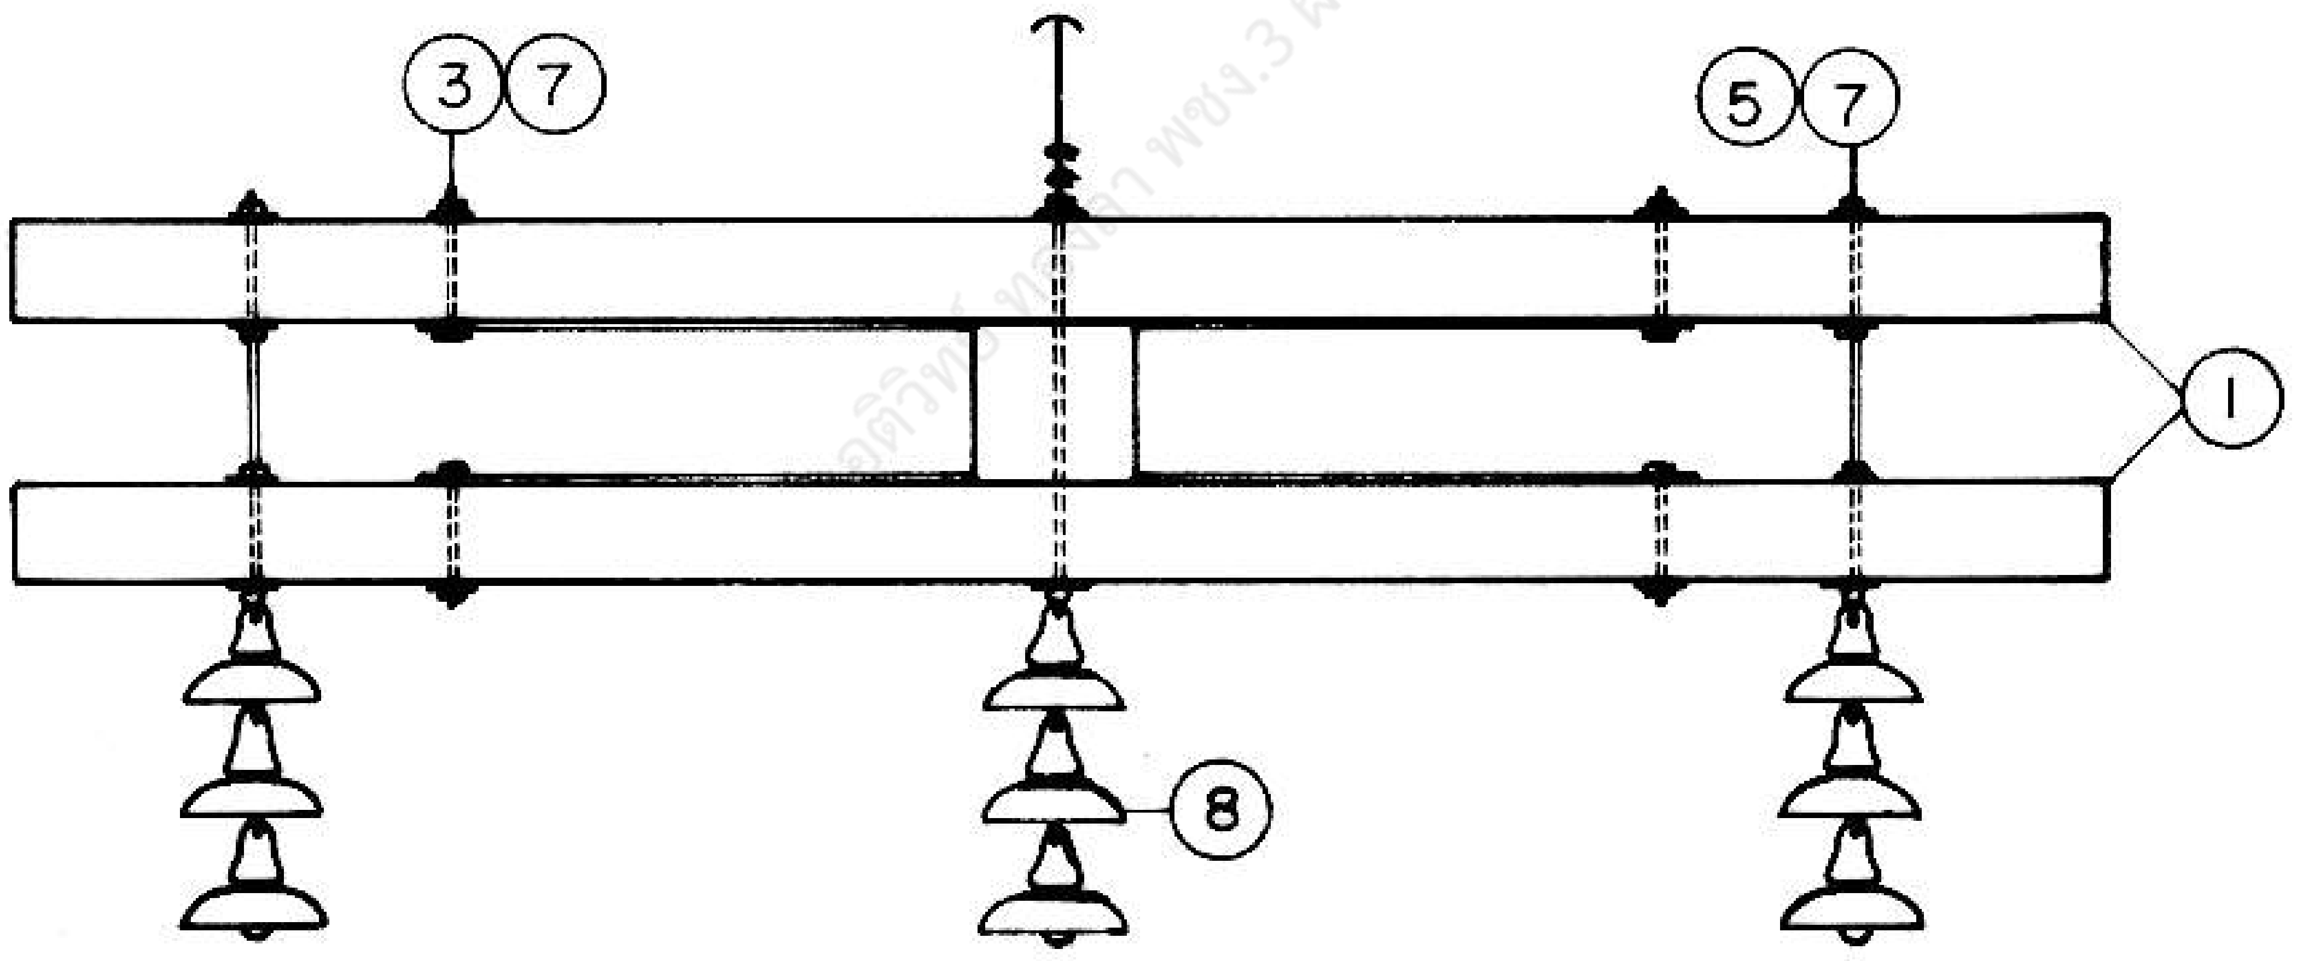

กองวิศวกรรมไฟฟ้าและเครื่องกล
ฝ่ายวิศวกรรม

ผู้เขียน
ผู้สำรวจ
วิศวกร
หัวหน้าแผนก
หัวหน้ากอง
ผู้อำนวยการฝ่าย

รองผู้ว่าการฝ่ายเทคนิค

การไฟฟ้าส่วนภูมิภาค

ผู้ว่าการ 4 มิ.ย. 24

การประกอบคอน คอร. สปัน กับเสาคอนกรีต
ระบบ 33 kV
สำหรับเข้าปลายสาย

SPUN PRESTRESSED CONCRETE CROSSARM ASSEMBLY
33 kV SYSTEM
DEADEND STRUCTURE

ใช้แทนแบบ
ถูกแทนโดยแบบ
เขียนเสร็จวันที่ 28 พ.ค. 24
แก้แบบวันที่
มิติเป็น มม.
มาตราส่วน 1 : 25

แบบเลขที่ SAI-015/24017
แผ่นที่ 1 ของจำนวน 2 แผ่น

3 ส.ค. 2524

การประกอบเลขที่ ASSEMBLY NO. 3807

บัญชีวัสดุ
BILL OF MATERIAL

ลำดับที่ ITEM	รายละเอียด DESCRIPTION	จำนวน REQ'D	วัสดุเลขที่ MAT. NO.
1	คอน คอร. สปัน (สำหรับเข้าปลายสาย) 120 X 120 X 2,500 มม. CROSSARM, SPUN PRESTRESSED (FOR DEADENDING) 120 X 120 X 2,500 mm	2	00110004
2	เหล็กประกับไม้คอน 40 X 6 X 1,000 มม. BRACE, FLAT, FOR CROSSARM 40 X 6 X 1,000 mm	4	01200002
3	สลักเกลียว M 16 X 170 มม. BOLT, MACHINE, M 16 X 170 mm	4	01110201
4	สลักเกลียว M 16 X 250 มม. BOLT, MACHINE, M 16 X 250 mm	1	01110203
5	สลักเกลียวห่วงกลม M 16 X 500 มม. BOLT, DOUBLE ARMING, ROUND EYE, M 16 X 500 mm	3	01130002
6	สลักห่วงกลม M 16 X 300 มม. BOLT, ROUND EYE, M 16 X 300 mm	1	01140003
7	แหวนสี่เหลี่ยมแบน 52X52X 4.5 มม. รู Ø 18 มม. มอก. 258 WASHER, SQUARE, FLAT 52X52X4.5 mm HOLE Ø 18 mm TIS 258	15	01180100
8	ลูกถ้วยแขวน มอก. 354 แบบ ง (แบบ 52-4) INSULATOR, SUSPENSION TYPE, TIS 354 TYPE D (CLASS 52-4)	9	03020002
9	กายทิมเบิล สำหรับสายยึดโยง 50-95 ต.มม. THIMBLE, GUY, FOR STEEL WIRE 50 - 95 mm^2	1	01210304
10	ยูแคล้มป์ สลัก 1 ตัว M 8 (ไวร์ โร้ป คลิ้พ) CLAMP, SINGLE U-BOLT, M 8 (WIRE ROPE CLIP)	4	01230000

อดิศักดิ์ ทองลา พชง.3 ผปร. ผส.อล. กฟจ.กน. กฟต.2 สายงาน (ต) ผวก. @PEA

หมายเหตุ

1. รายละเอียดและข้อกำหนดการใช้งานของ คอน คอร. สปัน (สำหรับเข้าปลายสาย) ดูแบบเลขที่ SAI-015/24011
2. ชุดยึดโยงเข้าปลายสาย เลือกขนาดสายยึดโยงจากโนโมกราฟฟิคไดอะแกรม ในแบบเลขที่ SAI-015/22036

NOTES

1. DETAIL AND APPLICATION OF SPUN PRESTRESSED CONCRETE CROSSARM (FOR DEAD-ENDING) SEE DWG. NO. SAI-015/24011
2. FOR DEADEND GUYING, SELECT SIZE OF GUY WIRE FROM NOMOGRAPHIC DIAGRAM IN DWG. NO. SAI-015/22036

กองวิศวกรรมไฟฟ้าและเครื่องกล
ฝ่ายวิศวกรรม

ผู้เขียน
ผู้สำรวจ
วิศวกร
หัวหน้าแผนก
หัวหน้ากอง
ผู้อำนวยการฝ่าย
รองผู้ว่าการฝ่ายเทคนิค

การไฟฟ้าส่วนภูมิภาค

ผู้ว่าการ 4 มิ.ย. 24

การประกอบคอน คอร. สปัน กับเสาคอนกรีต
ระบบ 33 kV
สำหรับเข้าปลายสาย

SPUN PRESTRESSED CONCRETE CROSSARM ASSEMBLY
33 kV SYSTEM
DEADEND STRUCTURE

ใช้แทนแบบ
ถูกแทนโดยแบบ
เขียนเสร็จวันที่ 28 พ.ค. 24
แก้แบบวันที่
มิติเป็น
มาตราส่วน

แบบเลขที่ SAI-015/24017
แผ่นที่ 2 ของจำนวน 2 แผ่น