การประกอบเลขที่
ASSEMBLY NO. 3219

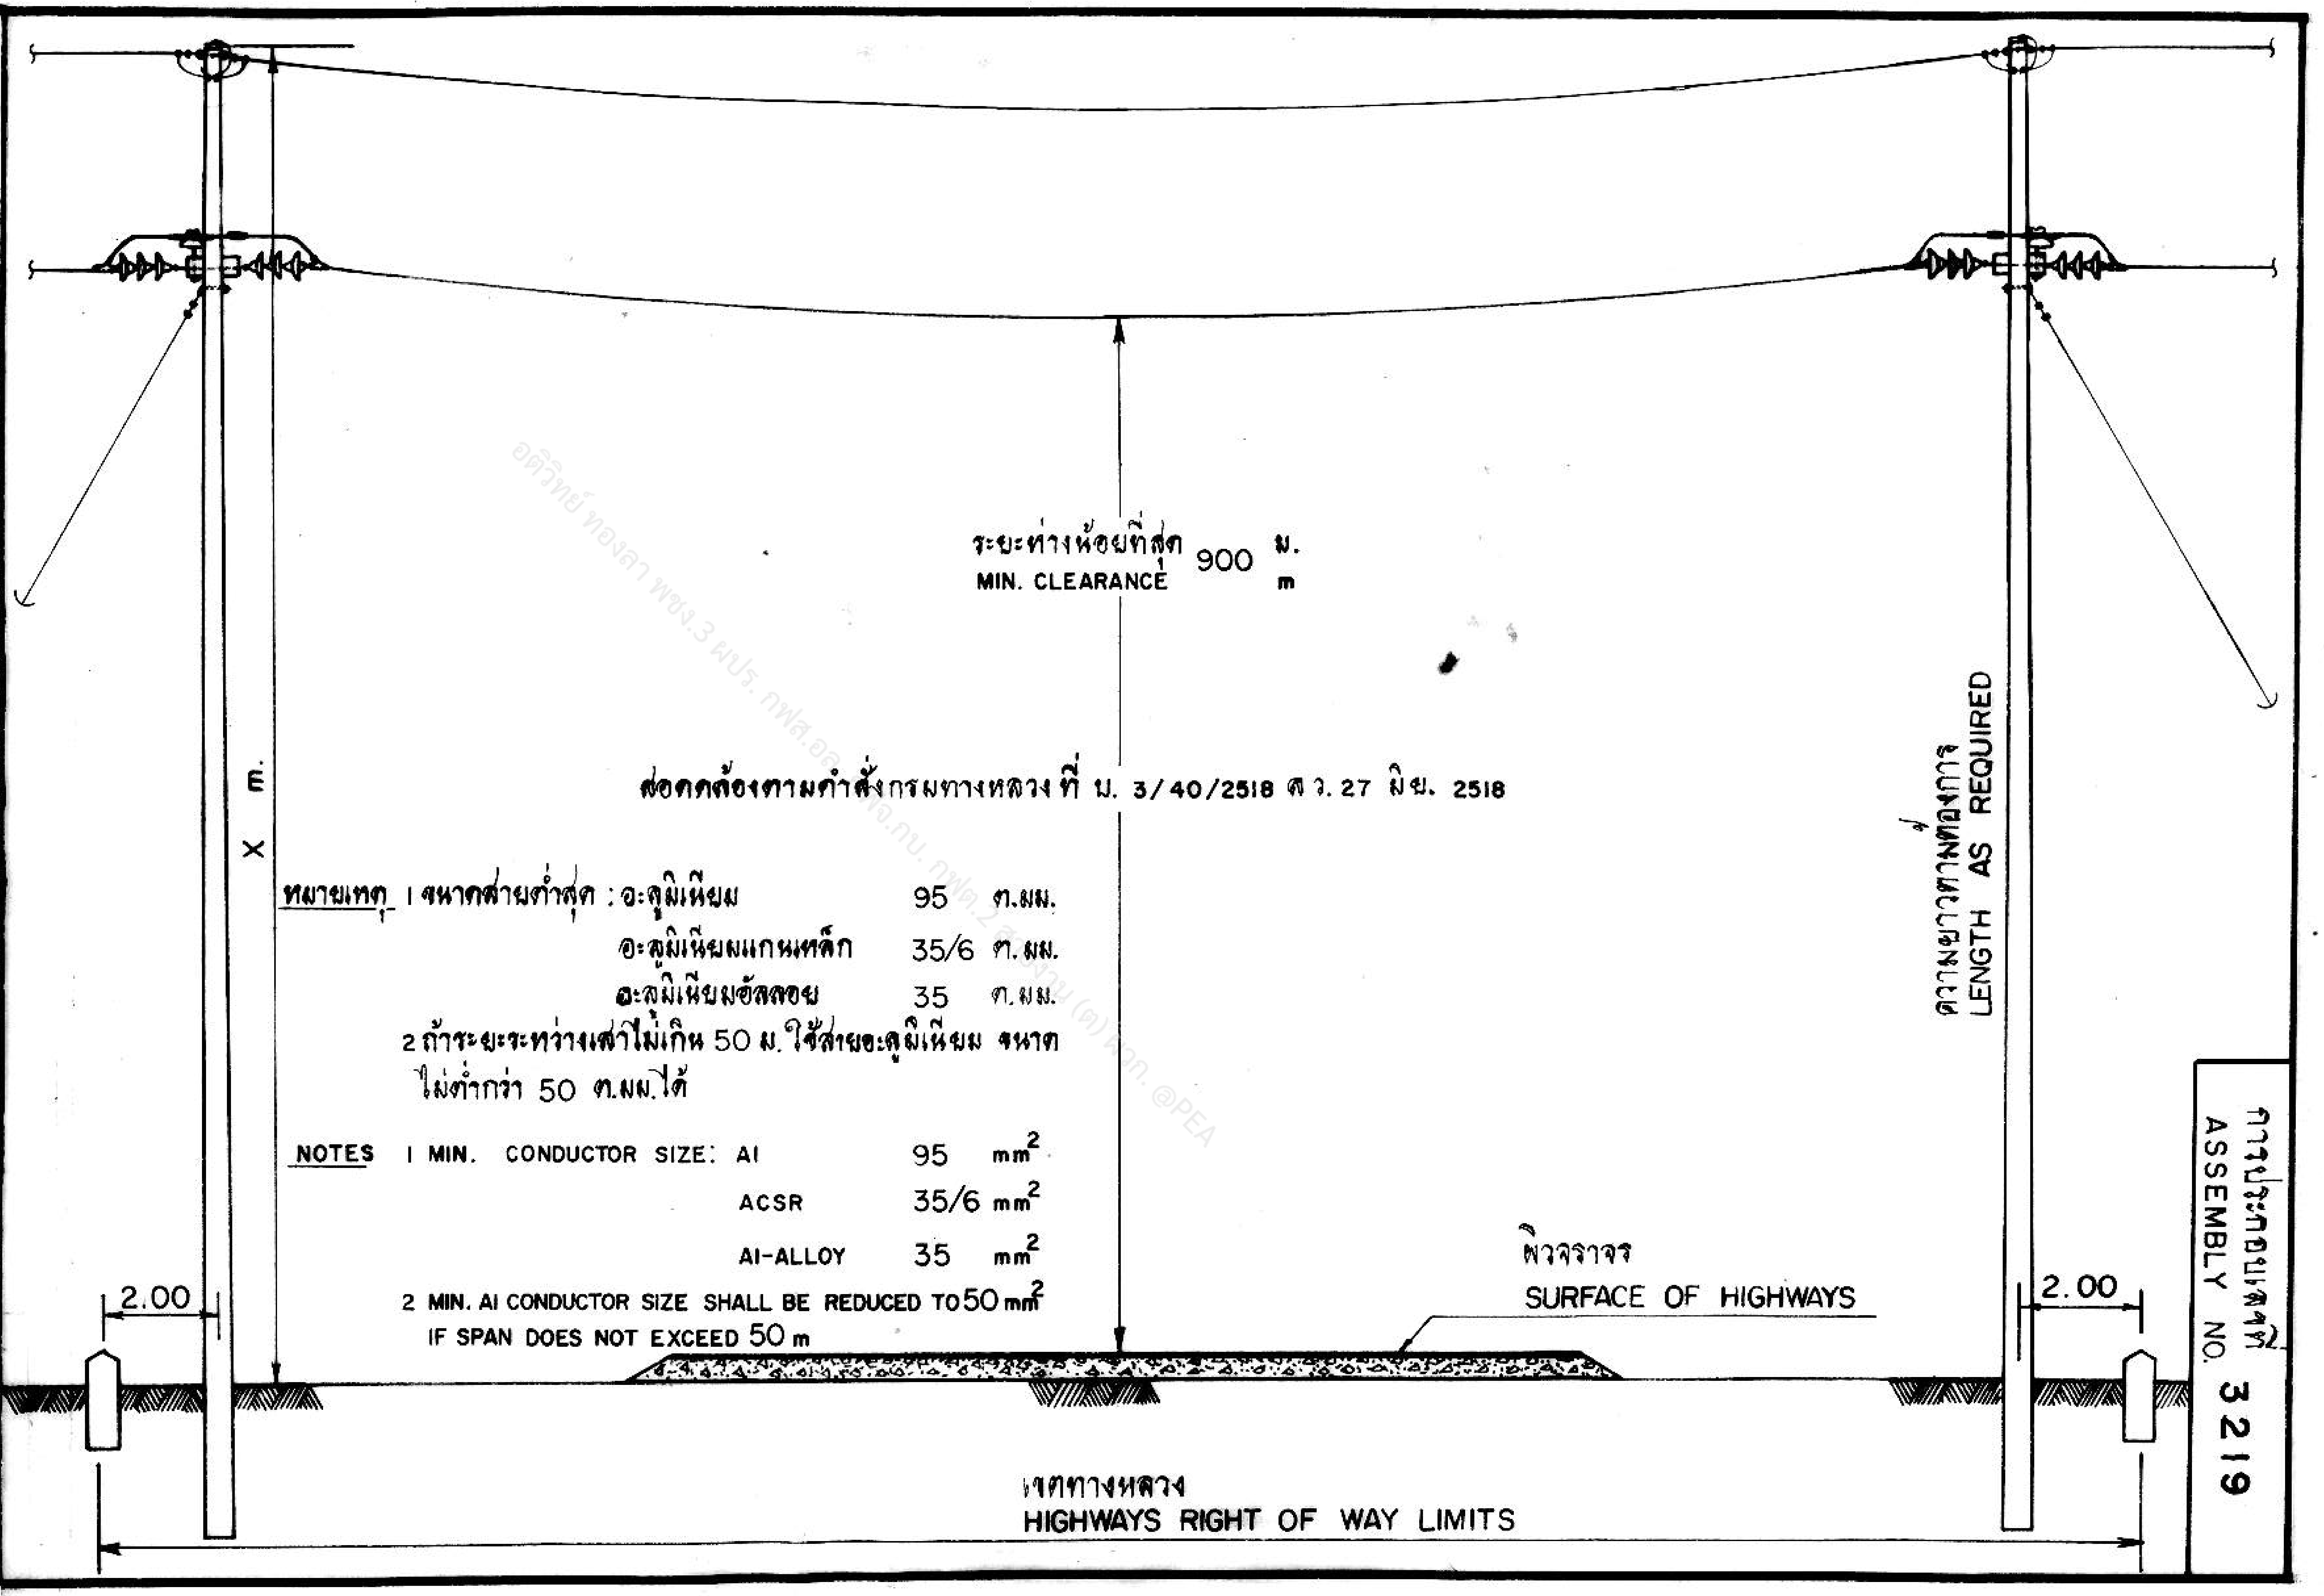

สอดคล้องตามคำสั่งกรมทางหลวงที่ ม. 3/40/2518 ลว. 27 มิย. 2518

หมายเหตุ 1 ขนาดสายต่ำสุด : อะลูมิเนียม 95 ต.มม.
อะลูมิเนียมแกนเหล็ก 35/6 ต.มม.
อะลูมิเนียมอัลลอย 35 ต.มม.
2 ถ้าระยะระหว่างเสาไม่เกิน 50 ม. ใช้สายอะลูมิเนียม ขนาดไม่ต่ำกว่า 50 ต.มม. ได้

NOTES 1 MIN. CONDUCTOR SIZE: Al 95 mm^2
ACSR 35/6 mm^2
Al-ALLOY 35 mm^2
2 MIN. Al CONDUCTOR SIZE SHALL BE REDUCED TO 50 mm^2 IF SPAN DOES NOT EXCEED 50 m

กองวิศวกรรมและวางแผน
ผู้เขียน
ผู้สำรวจ
วิศวกร
หัวหน้าแผนก
ผู้อำนวยการกอง
รองผู้ว่าการฝ่ายเทคนิค

การไฟฟ้าส่วนภูมิภาค

ผู้ว่าการ

การพาดสายแรงสูง 33 kV ข้ามถนน

HT. 33 KV LINE ACROSS THE HIGHWAYS

ใช้แทนแบบ
ถูกแทนโดยแบบ
เขียนเสร็จวันที่ 16 เม.ย. 14
แก้แบบวันที่
มิติเป็น เมตร
มาตราส่วน
แบบเลขที่ I50-015/140212
แผ่นที่ 1 ของจำนวน 1 แผ่น