การประกอบเลขที่
ASSEMBLY NO. 3405

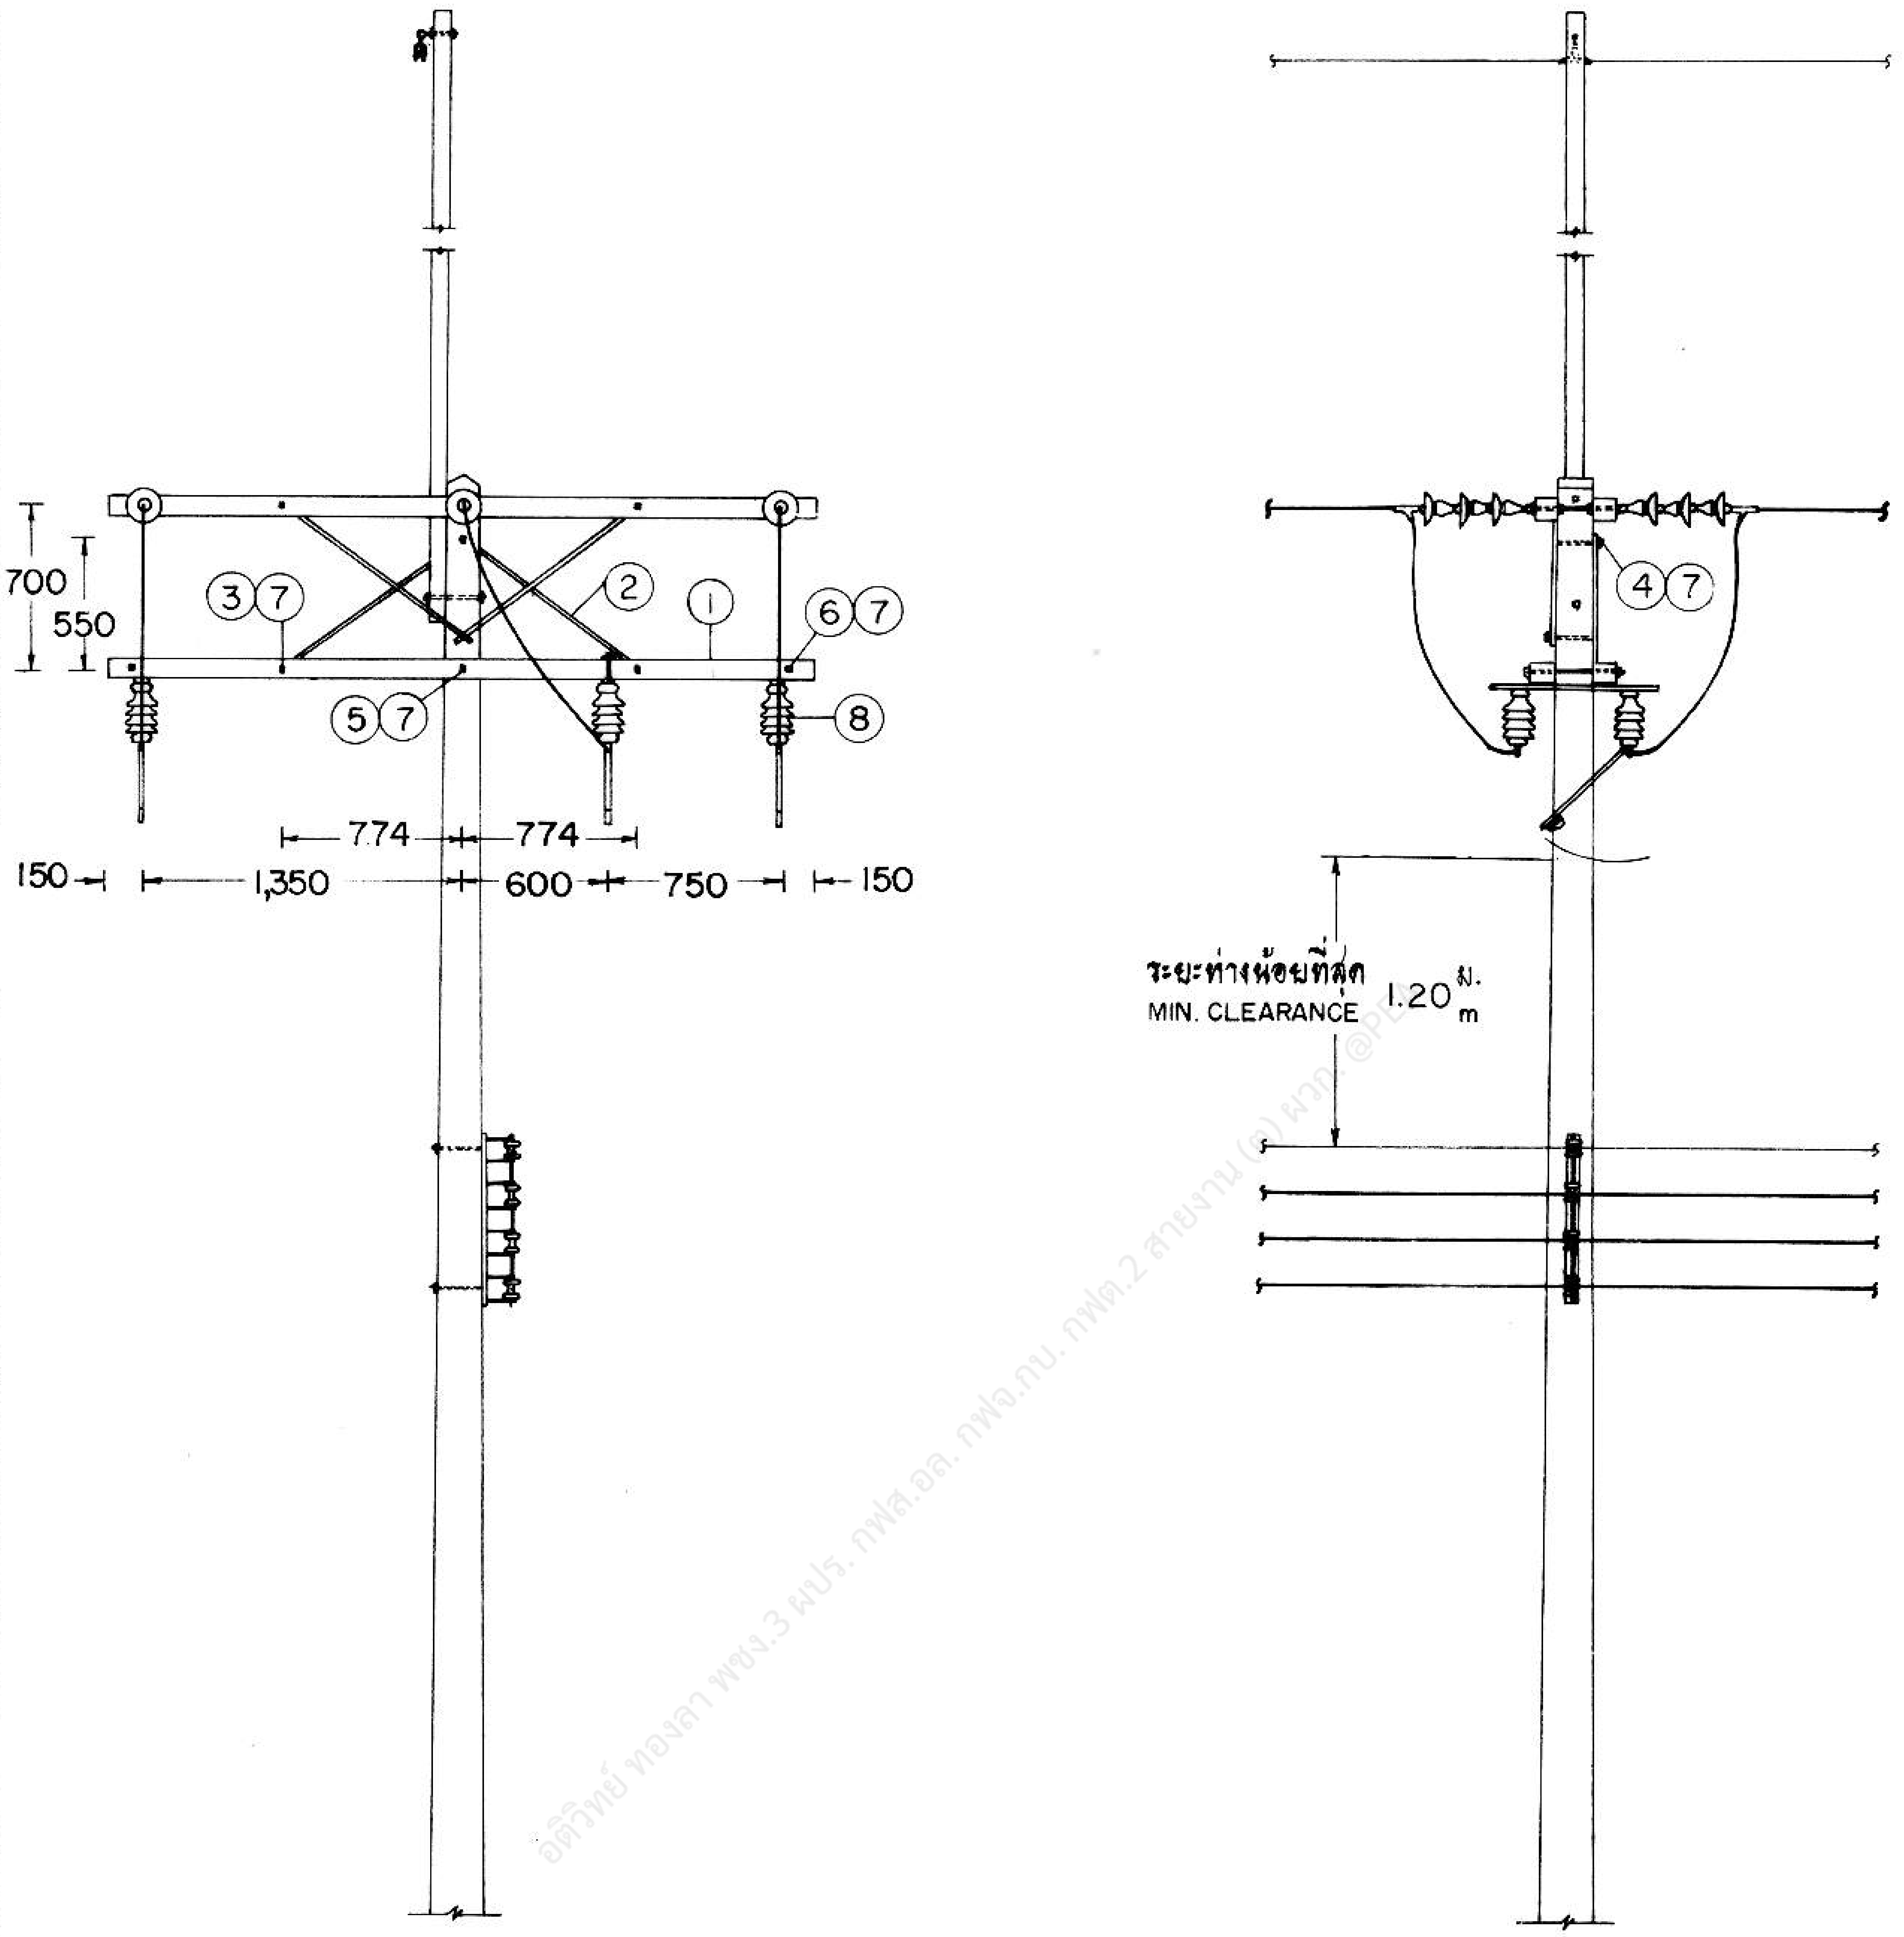

อิติวิทย์ ทองลา พชง.3 ผปร. กฟส.อล. กฟจ.กบ. กฟต.2 สายงาน (ต) ผวภ. @PEA

กองวิศวกรรม

ผู้เขียน
ผู้สำรวจ
วิศวกร
หัวหน้าแผนก
หัวหน้ากอง

รองผู้ว่าการฝ่ายเทคนิค

การไฟฟ้าส่วนภูมิภาค

ผู้ว่าการ

~~2 6 พ.ค. 2520~~

การติดตั้งสวิตซ์ธรรมดาหนึ่งขา แบบเข้าปลายสายสองข้าง
ระบบ 33 kV

SINGLE POLE ISOLATING SWITCH INSTALLATION
DOUBLE DEADEND TYPE
33 kV SYSTEM

ใช้แทนแบบ
ถูกแทนโดยแบบ
เขียนเสร็จวันที่ 25เม.ย.20
แก้แบบวันที่
ผิดเป็น
มาตราส่วน 1:50
แบบเลขที่ S 02-015/20061
แผ่นที่ 1 ของจำนวน 2 แผ่น

การประกอบเลขที่ 3405
ASSEMBLY NO. 3405

บัญชีวัสดุ
BILL OF MATERIAL

ลำดับที่ ITEM	รายละเอียด DESCRIPTION	จำนวน REQ'D	วัสดุเลขที่ MAT. NO.
1	ไม้คอนสายแรงสูง 100 X 120 X 3,000 มม. CROSSARM, WOOD, H.T. 100 X 120 X 3,000 mm	2	00100003
2	เหล็กประกับไม้คอน 40 X 6 X 1,000 มม. BRACE, FLAT, FOR CROSSARM 40 X 6 X 1,000 mm	2	01200002
3	สลักเกลียว M 16 X 130 มม. BOLT, MACHINE, M 16 X 130 mm	2	01110200
4	สลักเกลียว M 16 X 200 มม. BOLT, MACHINE, M 16 X 200 mm	1	01110202
5	สลักเกลียว M 16 X 400 มม. BOLT, MACHINE, M 16 X 400 mm	1	01110206
6	สลักเกลียวตลอด M 16 X 400 มม. BOLT, DOUBLE ARMING M 16 X 400 mm	2	01120000
7	แหวนสี่เหลี่ยมแบน 52 X 52 X 4.5 มม. รู Ø 18 มม. มอก. 258 WASHER, SQUARE, FLAT 52 X 52 X 4.5 mm HOLE Ø 18 mm TIS 258	13	01180100
8	สวิตช์ธรรมดา หนึ่งขา 33 kV ชนิดติดในสายจำหน่าย SWITCH, ISOLATING, SINGLE POLE 33 kV DISTRIBUTION CLASS	3	04050100 - 04059801

อดิวิทย์ ทองลา พชง.3 ผปร. กฟส.อล. กฟจ.กบ. กฟต.2 สายงาน (ต) ผวก. @PEA

กองวิศวกรรม
ผู้เขียน
ผู้สำรวจ
วิศวกร
หัวหน้าแผนก
หัวหน้ากอง
รองผู้ว่าการฝ่ายเทคนิค

การไฟฟ้าส่วนภูมิภาค

ผู้ว่าการ

2 6 พ.ค. 2520

การติดตั้งสวิตช์ธรรมดาหนึ่งขา แบบเข้าปลายสายสองข้าง
ระบบ 33 kV

SINGLE POLE ISOLATING SWITCH INSTALLATION
DOUBLE DEADEND TYPE
33 kV SYSTEM

ใช้แทนแบบ
ถูกแทนโดยแบบ
เขียนเสร็จวันที่ 25 เม.ย. 20
แก้แบบวันที่
มิติเป็น
มาตราส่วน
แบบเลขที่ S02-015/20061
แผ่นที่ 2 ของจำนวน 2 แผ่น