การประกอบเลขที่ ASSEMBLY NO.	0518

* ให้โค้งดัดสายขึ้น เพื่อป้องกันน้ำฝนไหลย้อนเข้าที่จุดต่อปลายสาย

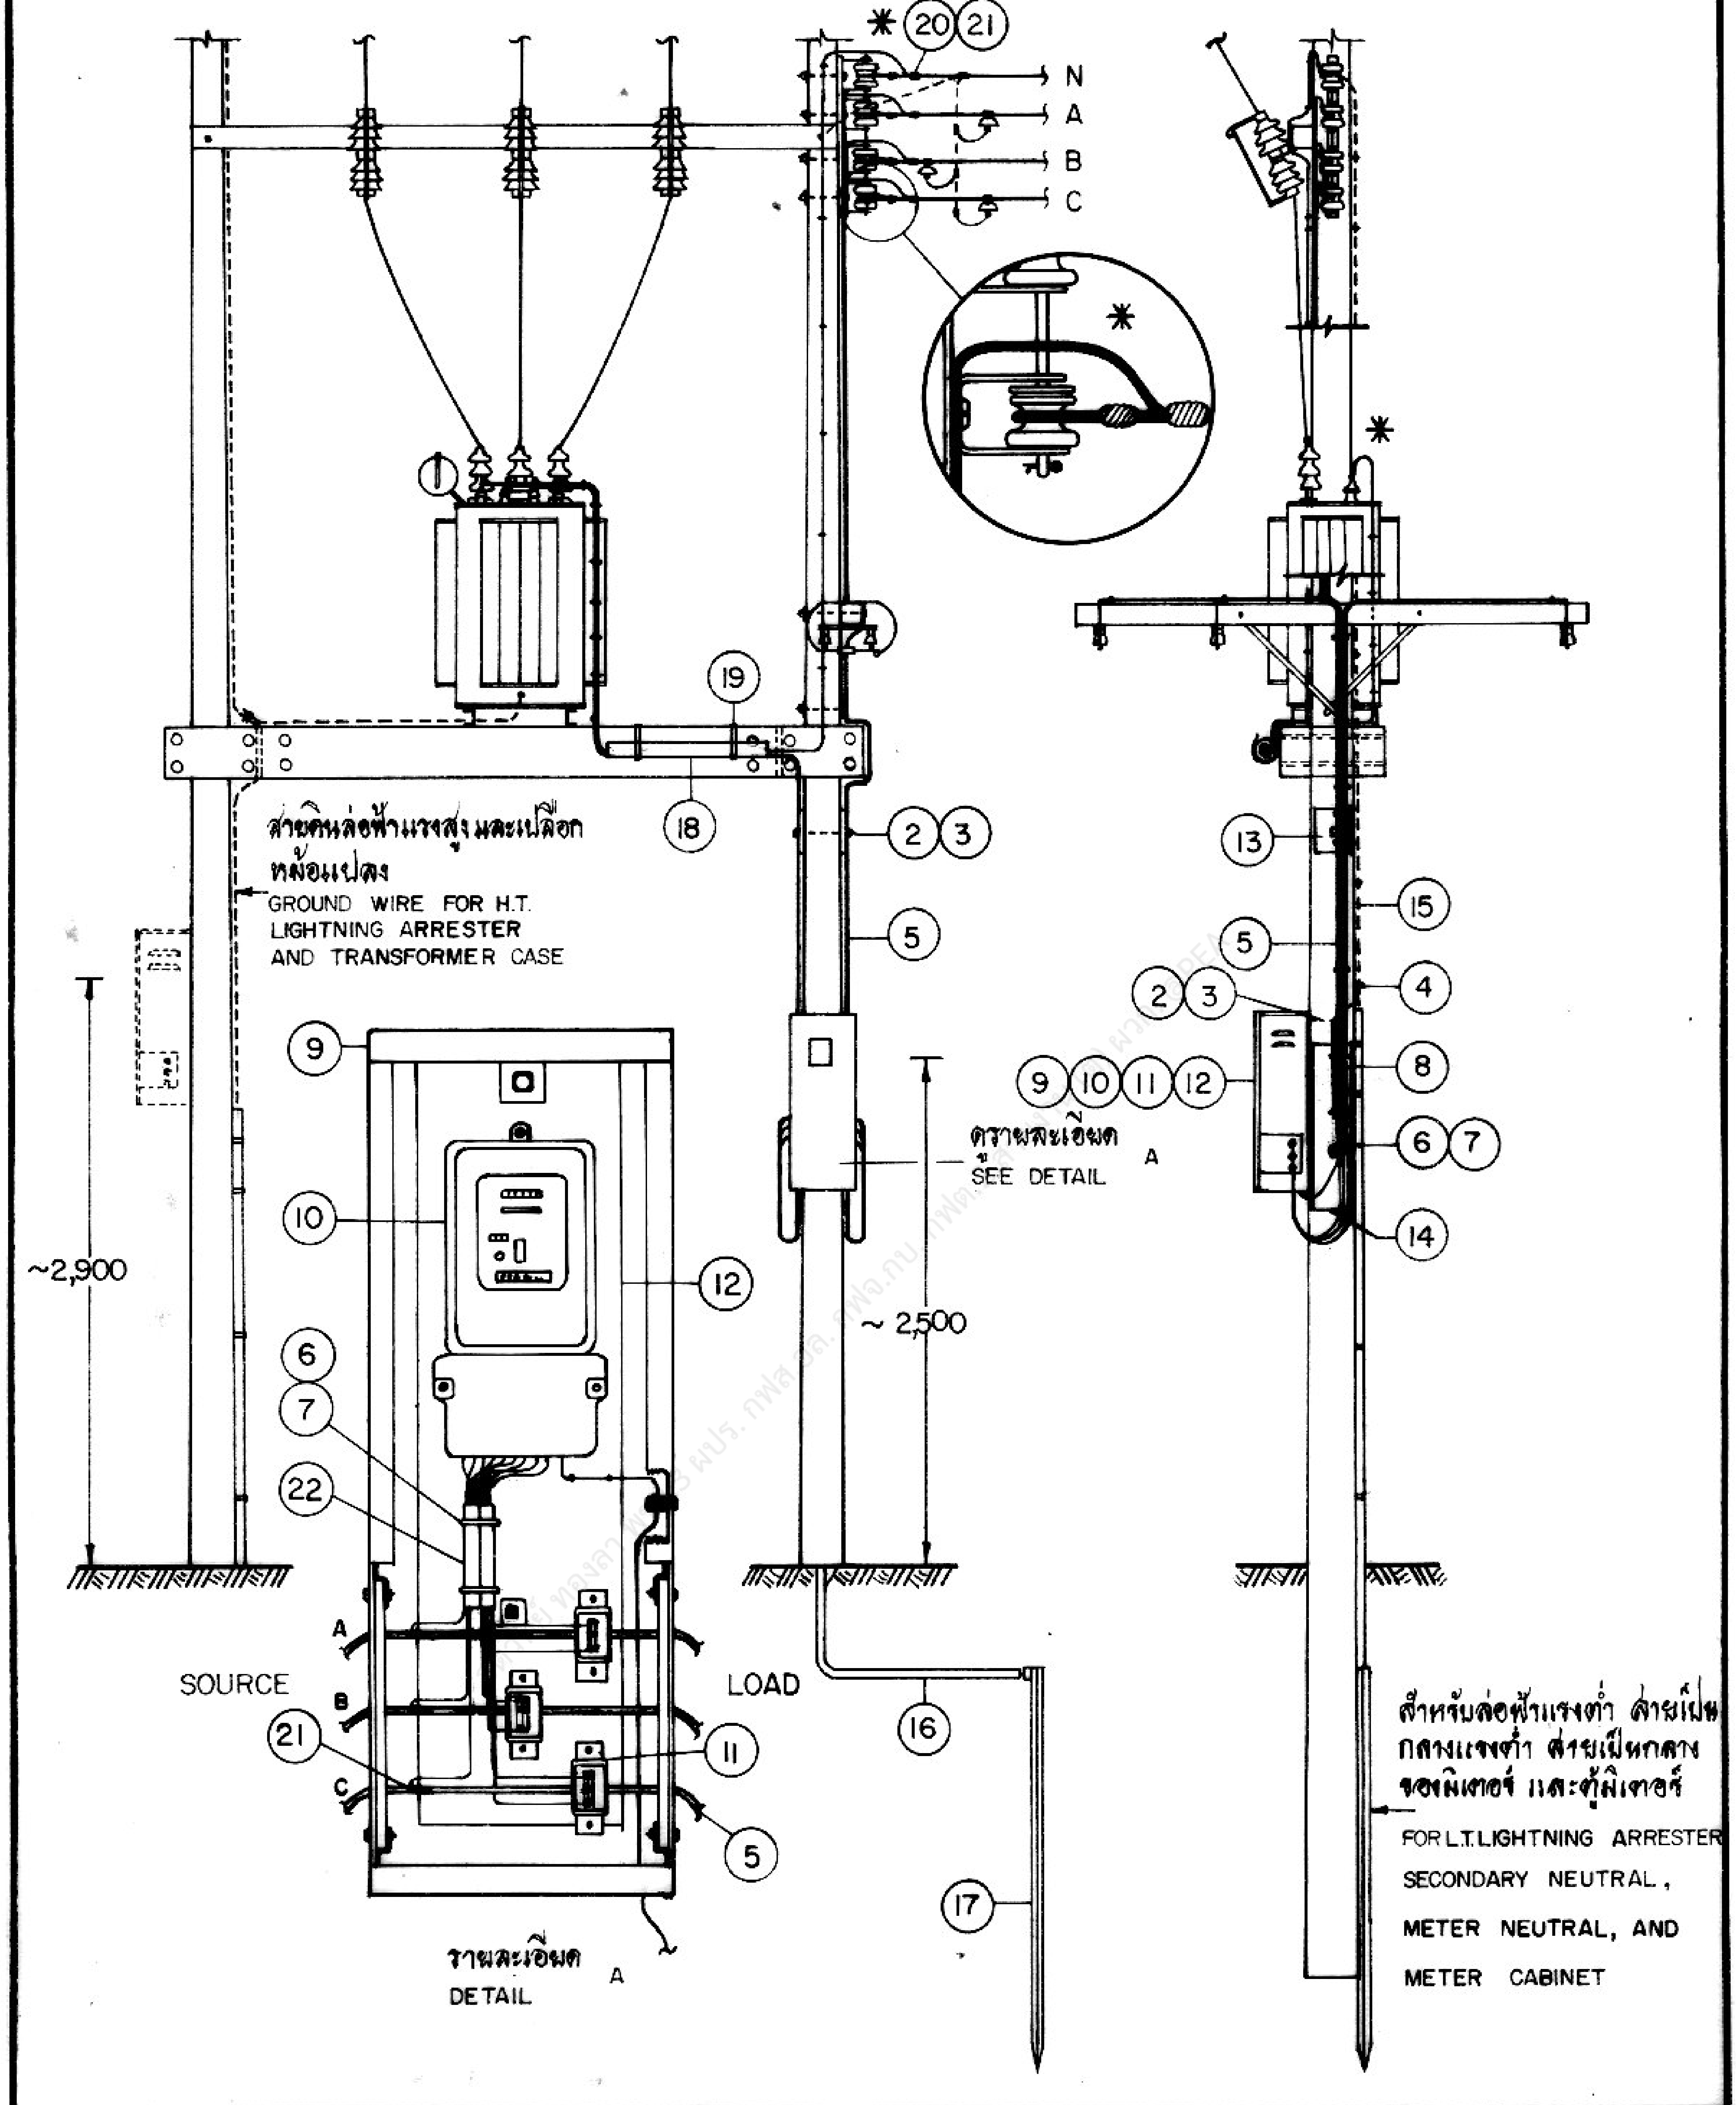

*
⑳ ㉑
N
A
B
C
*
*
①
⑲
⑱
② ③
⑤
สายดินล่อฟ้าแรงสูง และเปลือกหม้อแปลง
GROUND WIRE FOR H.T. LIGHTNING ARRESTER AND TRANSFORMER CASE
~2,900
⑨
⑩
⑫
⑥
⑦
㉒
A
B
C
SOURCE
LOAD
㉑
⑪
⑤
รายละเอียด A
DETAIL
รายละเอียด A
SEE DETAIL
~ 2,500
⑯
⑰
⑬
⑮
⑤
④
② ③
⑧
⑨ ⑩ ⑪ ⑫
⑥ ⑦
⑭
สำหรับล่อฟ้าแรงต่ำ สายเป็นกลางแรงต่ำ สายเป็นกลางของมิเตอร์ และตู้มิเตอร์
FOR L.T. LIGHTNING ARRESTER SECONDARY NEUTRAL, METER NEUTRAL, AND METER CABINET

กองวิศวกรรมไฟฟ้าและเครื่องกล ฝ่ายวิศวกรรม	การไฟฟ้าส่วนภูมิภาค	ใช้แทนแบบ ถูกแทนโดยแบบ เขียนเสร็จวันที่ 7/7/21 แก้แบบวันที่ 9/7/24, 14/5/25, 8/7/31 มิติเป็น มม. มาตราส่วน 1:50, 1:10
ผู้เขียน SAKORN.... ผู้สำรวจ วิศวกร หัวหน้าแผนก หัวหน้ากอง ผู้อำนวยการฝ่าย	ผู้ว่าการ การติดตั้งมิเตอร์แรงต่ำ 3 เฟส 4 สาย พร้อมซี.ที. แรงต่ำ ก ที่เสาต้นนั่งร้านหม้อแปลง	
รองผู้ว่าการฝ่ายเทคนิค	INSTALLATION OF 3-Ø, 4-W L.T. METER WITH L.T. CURRENT TRANSFORMERS A AT TRANSFORMER STATION	แบบเลขที่ SAI-015/21039 แผ่นที่ 1 ของจำนวน 5 แผ่น

* ให้โค้งปลายสายขึ้น เพื่อป้องกันน้ำฝนไหลย้อนเข้าที่จุดต่อปลายสาย

การประกอบเลขที่
ASSEMBLY NO. 0518

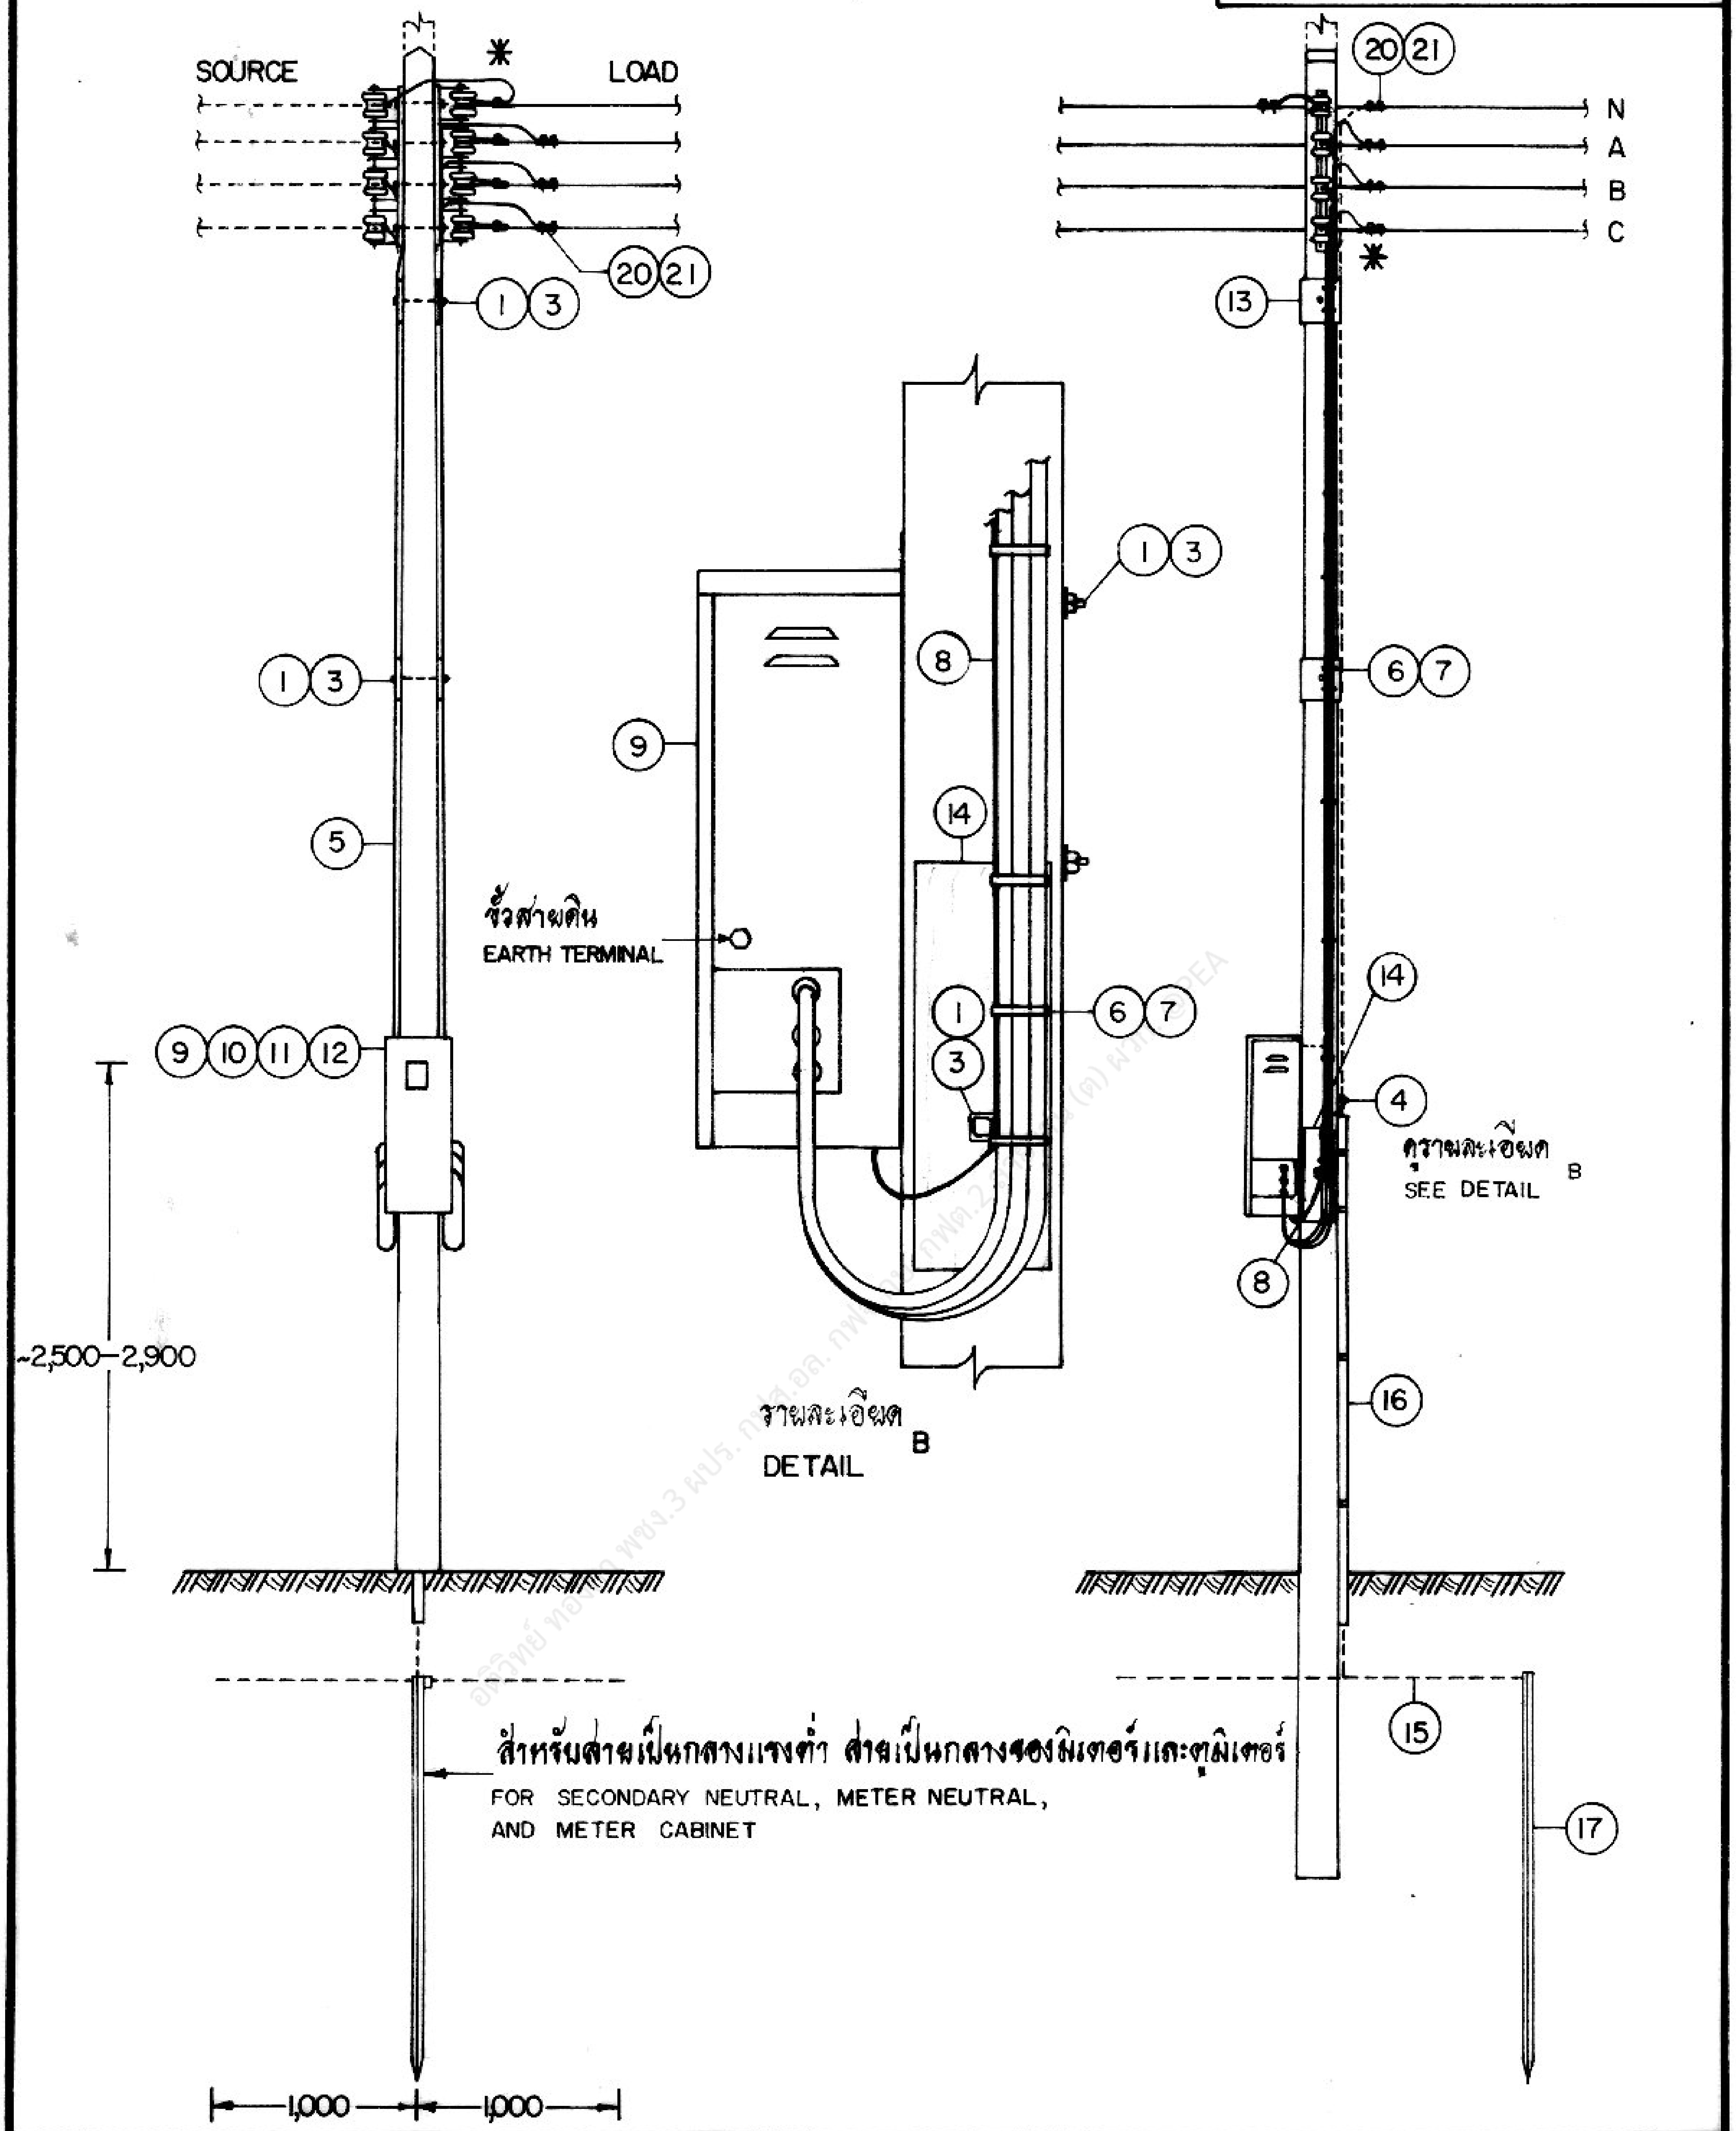

กองวิศวกรรมไฟฟ้าและเครื่องกล ฝ่ายวิศวกรรม	**การไฟฟ้าส่วนภูมิภาค**	ใช้แทนแบบ ถูกแทนโดยแบบ
ผู้เขียน SAKORN... ผู้สำรวจ วิศวกร หัวหน้าแผนก หัวหน้ากอง ผู้อำนวยการฝ่าย	ผู้ว่าการ	เขียนเสร็จวันที่ 7/7/21 แก้แบบวันที่ 9/7/24, 14/5/25, 8/7/31 มิติเป็น มม.
	การติดตั้งมิเตอร์แรงต่ำ 3 เฟส 4 สาย พร้อมซี.ที. แรงต่ำ ข ที่เสาระบบจำหน่ายแรงต่ำ	มาตราส่วน 1:50, 1:15
รองผู้ว่าการฝ่ายเทคนิค	INSTALLATION OF 3-Ø, 4-W L.T. METER WITH L.T. CURRENT TRANSFORMERS B AT L.T. DISTRIBUTION POLE	แบบเลขที่ SAI-015/21039 แผ่นที่ 2 ของจำนวน 5 แผ่น

การประกอบเลขที่
ASSEMBLY NO. 0518

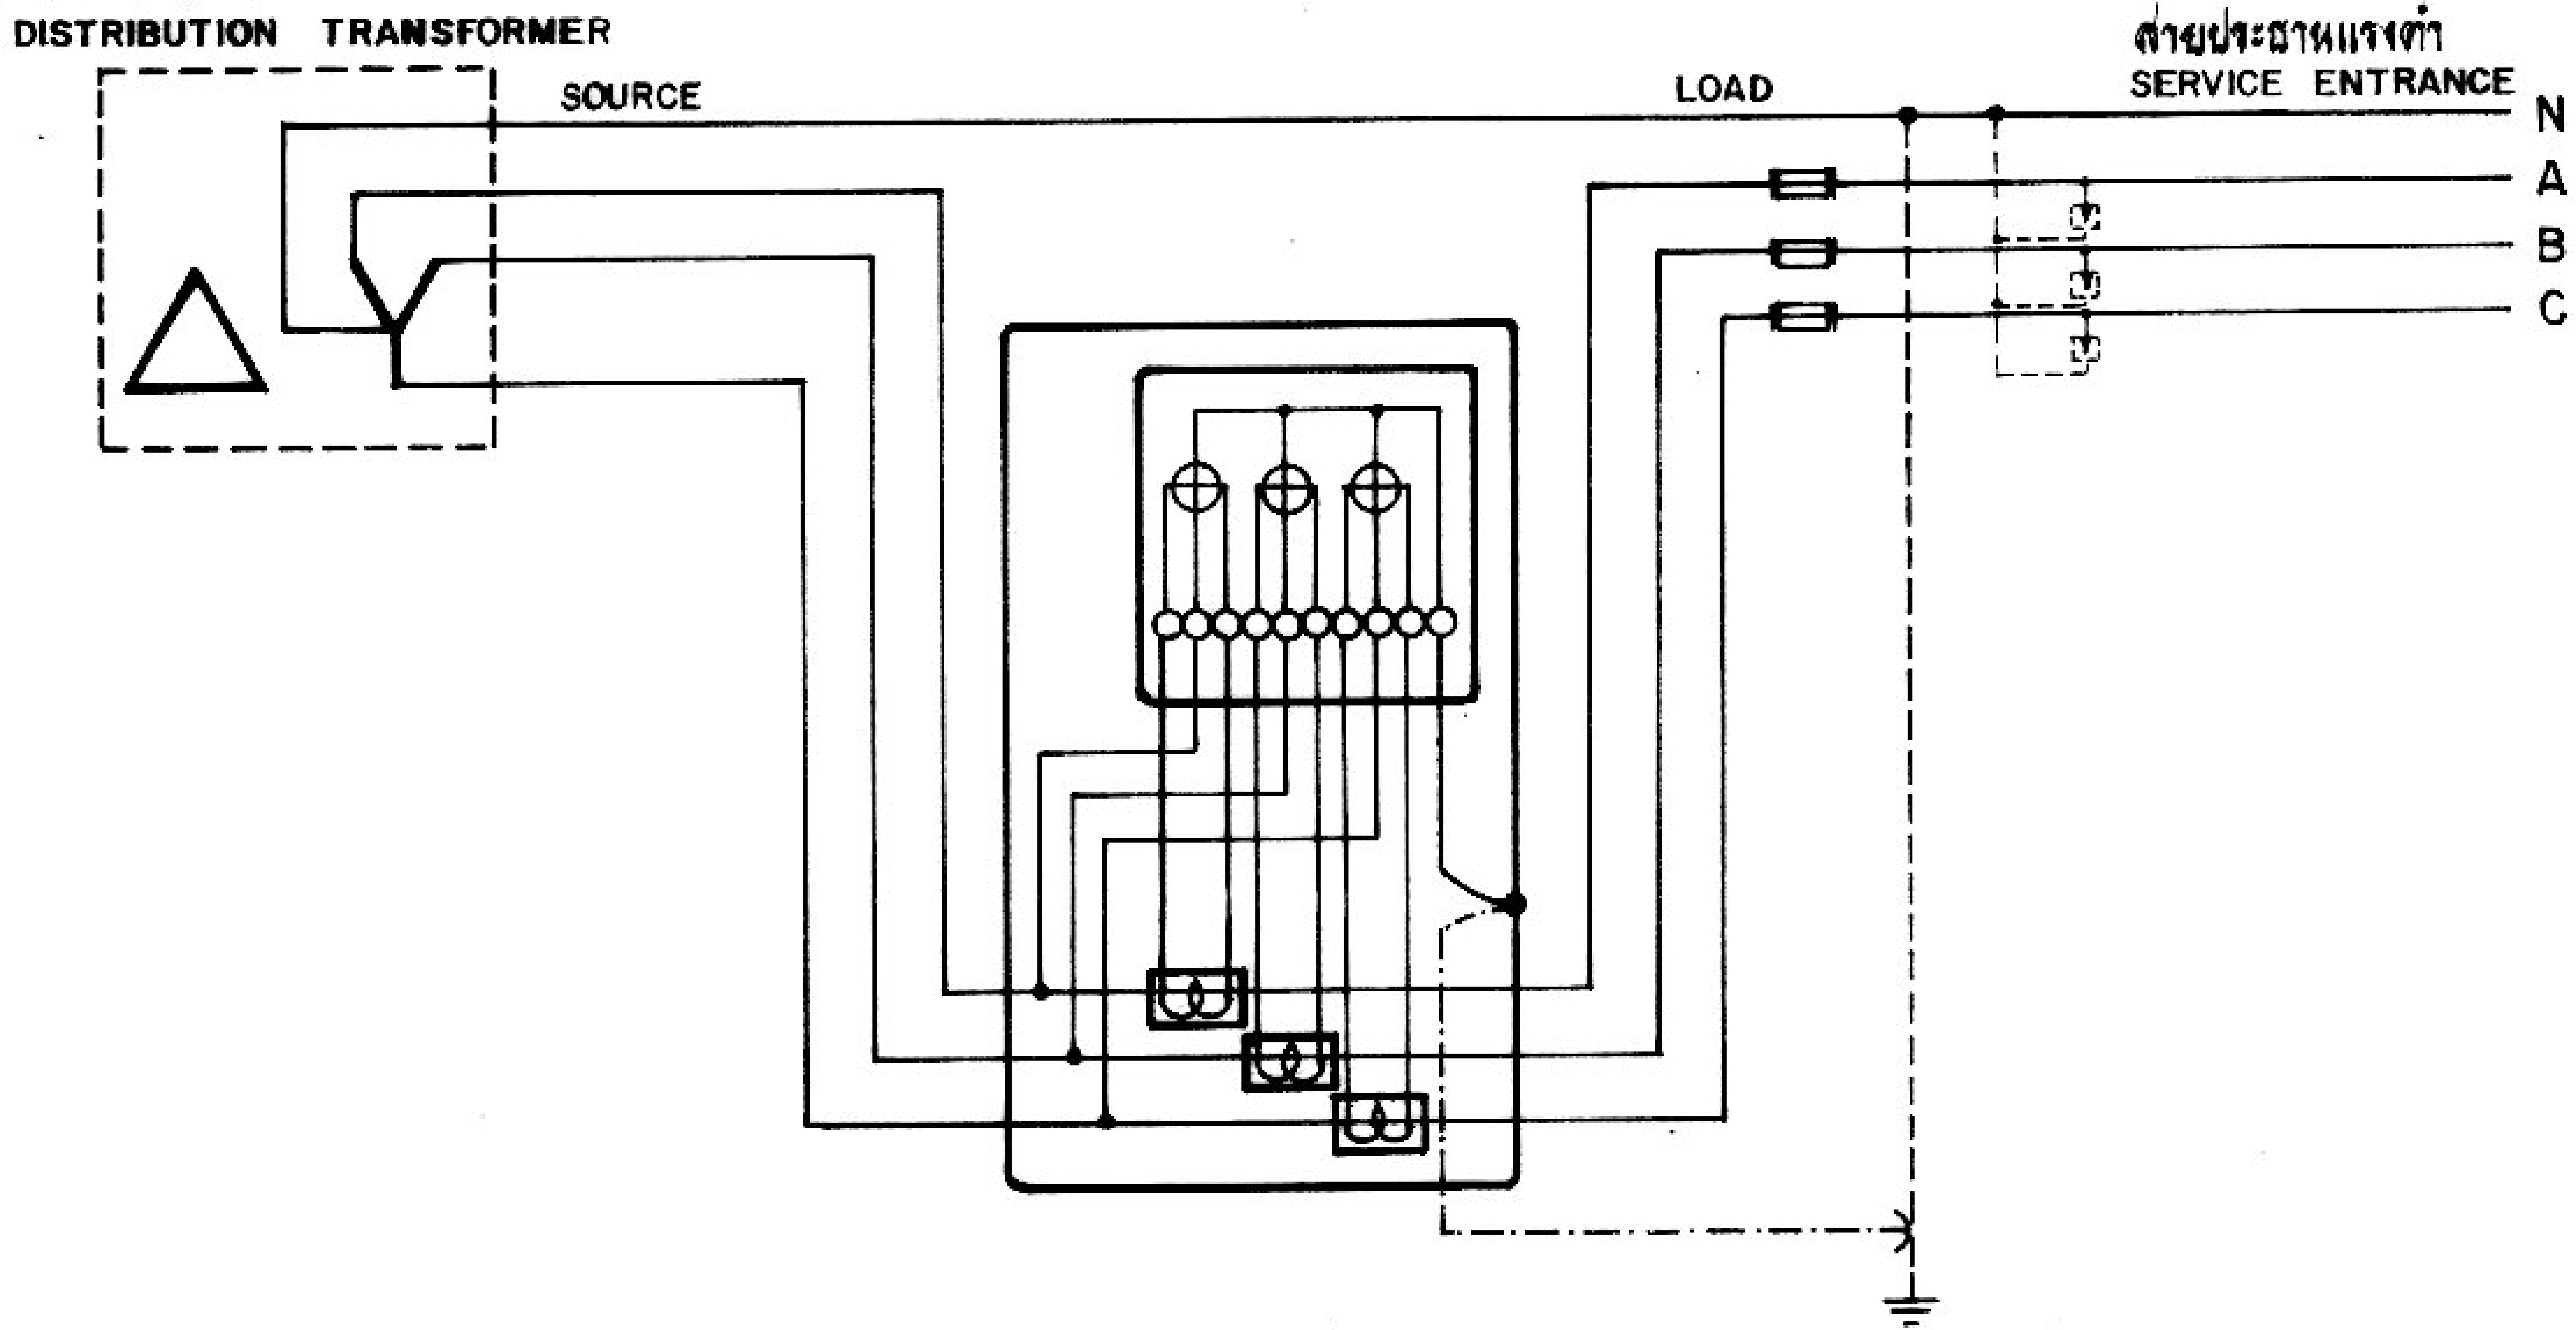

ไดอะแกรมแสดงการต่อดีมานด์มิเตอร์ 3 เฟส 4 สาย พร้อมซี.ที. แรงต่ำ
ที่เสาต้นนั่งร้านหม้อแปลง
CONNECTION DIAGRAM FOR 3-PHASE 4-WIRE DEMAND METER WITH L.T. - C.T.
AT TRANSFORMER STATION

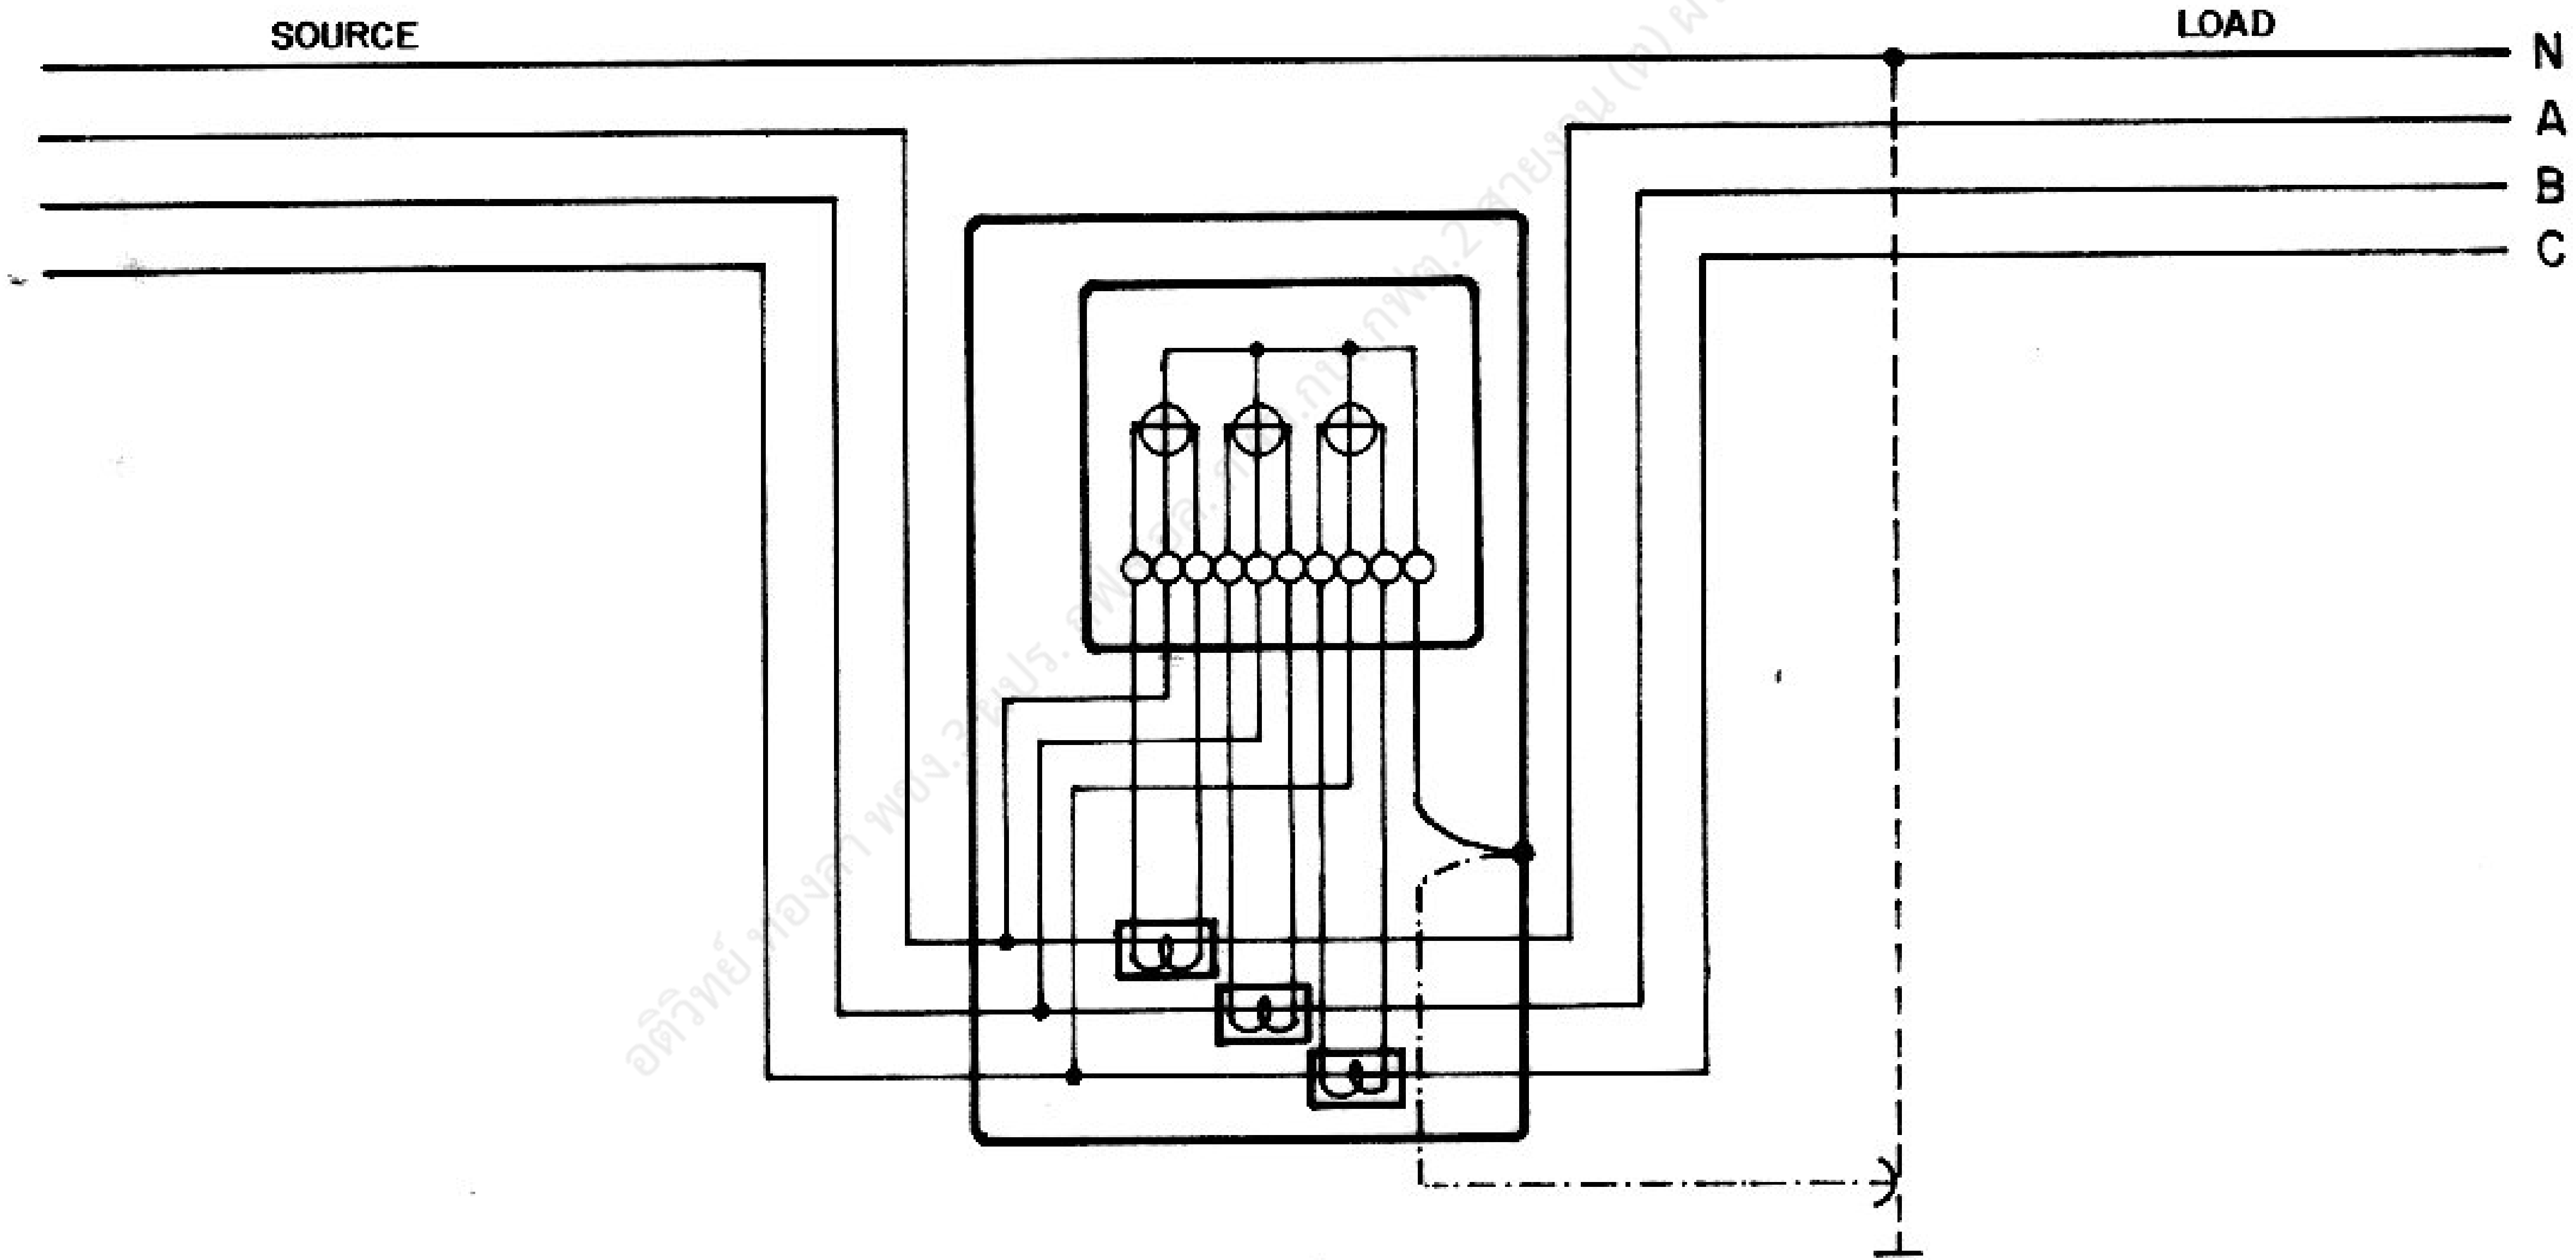

ไดอะแกรมแสดงการต่อดีมานด์มิเตอร์ 3 เฟส 4 สาย พร้อมซี.ที. แรงต่ำ
ที่เสาระบบจำหน่ายแรงต่ำ
CONNECTION DIAGRAM FOR 3-PHASE 4-WIRE DEMAND METER WITH L.T. - C.T.
AT L.T. DISTRIBUTION POLE

หมายเหตุ รายละเอียดการประกอบและต่อสายเข้ามิเตอร์ ดูแบบเลขที่ SAI-015/24012 (การประกอบเลขที่ 0527)

NOTE DETAIL OF ASSEMBLY AND WIRING, SEE DWG. NO. SAI-015/24012 (ASSEMBLY NO. 0527)

กองวิศวกรรมไฟฟ้าและเครื่องกล ฝ่ายวิศวกรรม	**การไฟฟ้าส่วนภูมิภาค**	ใช้แทนแบบ ถูกแทนโดยแบบ
ผู้เขียน ผู้สำรวจ วิศวกร หัวหน้าแผนก หัวหน้ากอง ผู้อำนวยการฝ่าย	ผู้ว่าการ	เขียนเสร็จวันที่ 7/7/21 แก้แบบวันที่ 9/7/24 8/7/31
	การติดตั้งมิเตอร์แรงต่ำ 3 เฟส 4 สาย พร้อม ซี.ที. แรงต่ำ	มิติเป็น มาตราส่วน
รองผู้ว่าการฝ่ายเทคนิค	INSTALLATION OF 3-0, 4-W. L.T. METER WITH L.T. CURRENT TRANSFORMERS	แบบเลขที่ SAI-015/21039 แผ่นที่ 3 ของจำนวน 5 แผ่น

การประกอบเลขที่
ASSEMBLY NO. 0518

บัญชีวัสดุ
BILL OF MATERIAL

ลำดับที่ ITEM	รายละเอียด DESCRIPTION	จำนวน REQ'D		วัสดุเลขที่ MAT. NO.
		ก /A	ข /B	
1	สลักเกลียว M 16 X 250 มม. BOLT, MACHINE, M 16 X 250 mm	–	5*	01110203
2	สลักเกลียว M 16 X 300 มม. BOLT, MACHINE, M 16 X 300 mm	4	–	01110204
3	แหวนสี่เหลี่ยมแบน 52 X 52 X 4.5 มม. รู Ø 18 มม. มอก. 258 WASHER, SQUARE, FLAT 52 X 52 X 4.5 mm, HOLE Ø 18 mm, TIS 258	7	9	01180100
4	ยูแคล้มป์ สลักเดี่ยว M 8 (ไวร์ โร้ป คลิ๊พ) CLAMP, SINGLE U-BOLT, M 8 (WIRE ROPE CLIP)	1	1	01230000
5	สายอะลูมิเนียม หรือสายทองแดงหุ้มฉนวนใช้ภายนอก 0.6/1 kV ขนาดตามต้องการ CONDUCTOR, INSULATED, WEATHER-PROOF, Al OR Cu 0.6/1 kV SIZE AS REQUIRED	ม. 55 m	ม. 35 m	02070002-8 02089908-14
6	ตะปูเหล็กหัวกลมแบน ยาว 20 มม. (มอก. 113) NAIL, ROUND MILD STEEL WIRE, 20 mm LONG (TIS 113)	24	32	
7	เข็มขัดรัดสายไฟฟ้า (ลวดอะลูมิเนียมแบน 1 X 10 มม.) STRAP, CABLE (ARMOUR TAPE 1 X 10 mm)	กก. 0.35 kg	กก. 0.25 kg	02200000
8	สายทองแดงหุ้มฉนวนใช้ภายนอก ขนาด 4 ต.มม. หรือ 2 X 2.5 ต.มม. (คอนโทรลเคเบิล) CONDUCTOR, INSULATED, WEATHER-PROOF Cu 4 mm² OR 2X2.5 mm² (CONTROL CABLE)	ม m	ม m	
9	ตู้สำหรับมิเตอร์พร้อม ซี.ที. แรงต่ำ CABINET, STEEL, FOR WATTHOUR METER WITH L.T. – CURRENT TRANSFORMER	1	1	06100018
10	ดีมานด์มิเตอร์, ชนิดสะสม 3 เฟส, 4 สาย 380/220 โวลต์ 5 แอมป์ (ใช้กับ ซี.ที.) DEMAND METER, COMULATIVE, THREE-PHASE, FOUR-WIRE, 380/220 V 5A (C.T. TYPE)	1	1	06000301
11	ซี.ที. แรงต่ำ 500 โวลต์ เรโชตามต้องการ แบบ 0.5 5 VA TRANSFORMER, CURRENT, L.T. 500V RATIO AS REQUIRED CLASS 0.5 5 VA	3	3	06030000-5
12	แป้นไม้รองรับมิเตอร์ไสแล้ว ขนาด 80X20X2 ซ.ม. METER PLATE (HARD WOOD) SURFACE FINISHED, SIZE 80X20X2 cm	1	1	
13	แป้นไม้ยึดสายไฟฟ้าไสแล้ว ขนาด 20X20X2 ซม. CABLE PLATE (HARD WOOD) SURFACE FINISHED, SIZE 20X20X2 cm	2	4	
14	แป้นไม้ยึดสายไฟฟ้าไสแล้ว ขนาด 60X20X2 ซม. CABLE PLATE (HARD WOOD) SURFACE FINISHED, SIZE 60X20X2 cm	2	2	
15	ลวดเหล็กตีเกลียว 50/7 ต.มม. มอก. 404 WIRE, STEEL, STRANDED 50/7 mm², TIS 404	ม. 10 m	ม. 19 m	01100004
16	ท่อ PVC แข็ง ขนาด Ø 20 X 2,500 - 4,000 มม. พร้อมอุปกรณ์ยึด CONDUIT, PVC RIGID, Ø 20 X 2,500 - 4,000 mm ; COMP. WITH FIXING ACCESS.	1	1	08040002 or 08040001
17	หลักดิน 60 X 60 X 5 มม. ยาว 2,000 มม. GROUND ROD, 60 X 60 X 5 mm 2,000 mm LONG	1	1	01220002
18	ท่อ PVC แข็งขนาด 65 X 800 มม. (มอก. 216) CONDUIT, PVC RIGID 65X800 mm (TIS. 216)	1	–	
19	เหล็กแขวนท่อ PVC (เหล็กแบน 30X4 มม. มอก. 55) STEEL BRACKET (FLAT IRON 30X4 mm TIS 55)	2	–	05100002

กองวิศวกรรมไฟฟ้าและเครื่องกล
ฝ่ายวิศวกรรม

ผู้เขียน
ผู้ตรวจ
วิศวกร
หัวหน้าแผนก
หัวหน้ากอง
ผู้อำนวยการฝ่าย

รองผู้ว่าการฝ่ายเทคนิค

การไฟฟ้าส่วนภูมิภาค

ผู้ว่าการ

การติดตั้งมิเตอร์แรงต่ำ 3 เฟส 4 สาย
พร้อม ซี.ที. แรงต่ำ

INSTALLATION OF 3-Ø, 4-W. L.T. METER
WITH L.T. CURRENT TRANSFORMERS

ใช้แทนแบบ
ถูกแทนโดยแบบ
เขียนเสร็จวันที่ 7/7/21
แก้แบบวันที่ 9/7/24
มิติเป็น
มาตราส่วน

แบบเลขที่ SAI-015/21039
แผ่นที่ 4 ของจำนวน 5 แผ่น

การประกอบเลขที่ ASSEMBLY NO.	0518

บัญชีวัสดุ
BILL OF MATERIAL

ลำดับที่ ITEM	รายละเอียด DESCRIPTION	จำนวน REQ'D ก /A	 ข /B	วัสดุเลขที่ MAT. NO.
20	พีจี. คอนเนคเตอร์ สำหรับสายอะลูมิเนียม หรือทองแดง ขนาดตามต้องการ CONNECTOR, PARALLEL-GROOVE,* Al OR Cu SIZE AS REQUIRED	1	8	02300101 or 02300102
21	PVC เทป กว้าง 19 มม. (ใช้ความยาว 2 ม. ต่อ 1 จุด) มอก. 386 PVC TAPE 19 mm WIDE (2 m LONG PER POINE) TIS 386			02810001 or 02810002
22	คอนโทรลเคเบิล ขนาด 7 X 2.5 ต.มม. CONTROL CABLE, SIZE 7 X 2.5 mm^2	2 ม. m	2 ม. m	02080402

หมายเหตุ

1. การต่อสายลงดินดูแบบเลขที่ S02-015/20039
2. * กรณีติดตั้งที่เสาคอนกรีต 12 ม. ให้เพิ่มความยาวสลักเกลียวเป็น 300 มม.
3. ตำแหน่งติดตั้งตู้มิเตอร์เปลี่ยนแปลงได้ตามความเหมาะสม
4. การติดตั้งมิเตอร์แรงต่ำ 3 เฟส 4 สาย ประกอบซีทีแรงต่ำในตู้มิเตอร์ ดูรายละเอียดในแบบเลขที่ SAI-015/24012 (การประกอบเลขที่ 0527)

NOTES

1. EARTHING CONNECTION SEE DWG. NO. S02-015/20039.
2. * FOR INSTALL ON 12 m CONCRETE POLE, INCREASE THE LENGTH OF MACHINE BOLT TO 300 mm .
3. SUITABLE HEIGHT FOR METER CABINET INSTALLATION.
4. THE ASSEMBLY OF 3-Ø, 4-W L.T. METER WITH L.T. CURRENT TRANSFORMER, SEE DETAIL IN DWG. NO. SAI-015/24012. (ASSEMBLY NO. 0527)

อติวิทย์ ทองลา พช. 3 ผบร. กฟส. กฟจ.กบ. กฟต. สายงาน (ต) ผวก. @PEA

กองวิศวกรรมไฟฟ้าและเครื่องกล ฝ่ายวิศวกรรม	การไฟฟ้าส่วนภูมิภาค	ใช้แทนแบบ ถูกแทนโดยแบบ
ผู้เขียน SAKORN ผู้สำรวจ วิศวกร หัวหน้าแผนก หัวหน้ากอง ผู้อำนวยการฝ่าย	ผู้ว่าการ 21 ก.ค. 24	เขียนเสร็จวันที่ 7/7/21 แก้แบบวันที่ 9/7/24 มิติเป็น มาตราส่วน
	การติดตั้งมิเตอร์แรงต่ำ 3 เฟส 4 สาย พร้อม ซี.ที. แรงต่ำ	
รองผู้ว่าการฝ่ายเทคนิค	INSTALLATION OF 3-Ø,4-W. L.T. METER WITH L.T. CURRENT TRANSFORMERS	แบบเลขที่ SAI-015/21039 แผ่นที่ 5 ของจำนวน 5 แผ่น

17 ก.ค. 2524