การประกอบเลขที่
ASSEMBLY NO. 5257

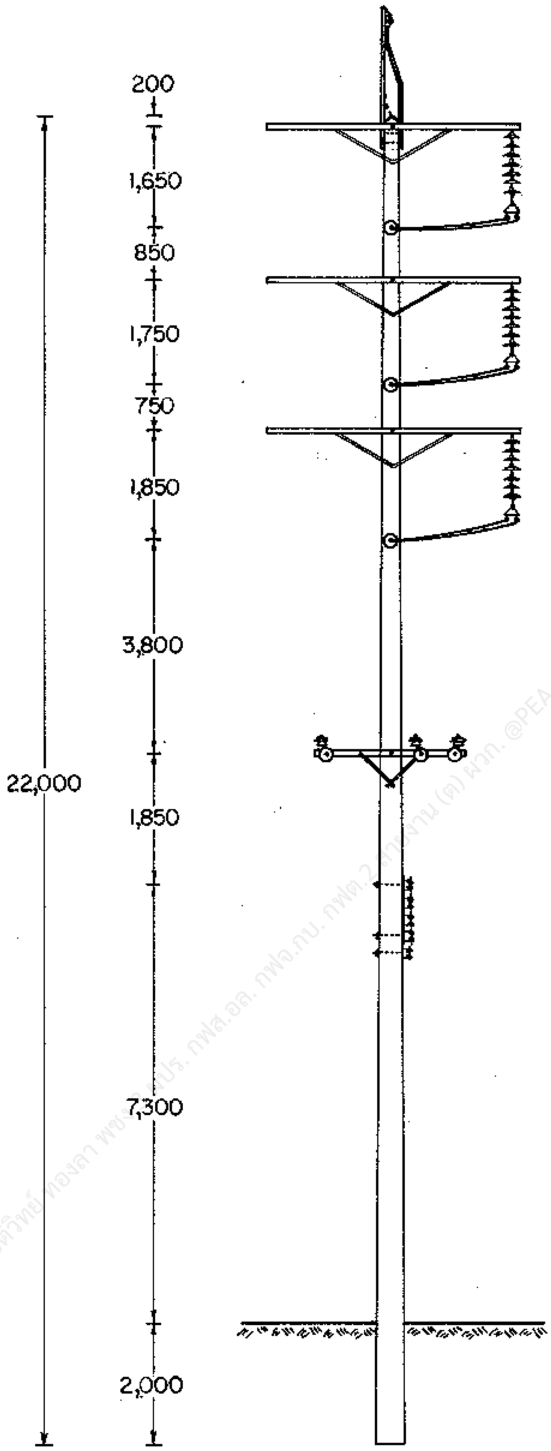

อดิวิทย์ ทองลา พชต.ปปร. กฟส.อล. กฟจ.กบ. กฟต.2 ผังงาน (ต) ผวก. @PEA

กองวิศวกรรมไฟฟ้าและเครื่องกล
ฝ่ายวิศวกรรม

ผู้เขียน
ผู้สำรวจ
วิศวกร
หัวหน้าแผนก ธีรวุฒิ
หัวหน้ากอง
ผู้อำนวยการฝ่าย
รองผู้ว่าการฝ่ายเทคนิค
23

การไฟฟ้าส่วนภูมิภาค

ผู้ว่าการ ๒๔ มี.ค.๒๓

115 kV วงจรเดี่ยว สายไฟฟ้าคู่
เสาสำหรับเข้าปลายสายสองข้าง
แบบ SD-DD-1

115 kV SINGLE CIRCUIT DOUBLE CONDUCTOR
DOUBLE DEAD END STRUCTURE
TYPE SD-DD-1

ใช้แทนแบบ
ถูกแทนโดยแบบ
เขียนเสร็จวันที่ 2 ม.ค.23
แก้แบบวันที่
มิติเป็น มม.
มาตราส่วน 1 : 125
แบบเลขที่ SAI-015/23011
แผ่นที่ 1 ของจำนวน 3 แผ่น

1 ส.ค. 2523

การประกอบเลขที่ ASSEMBLY NO. **5257**

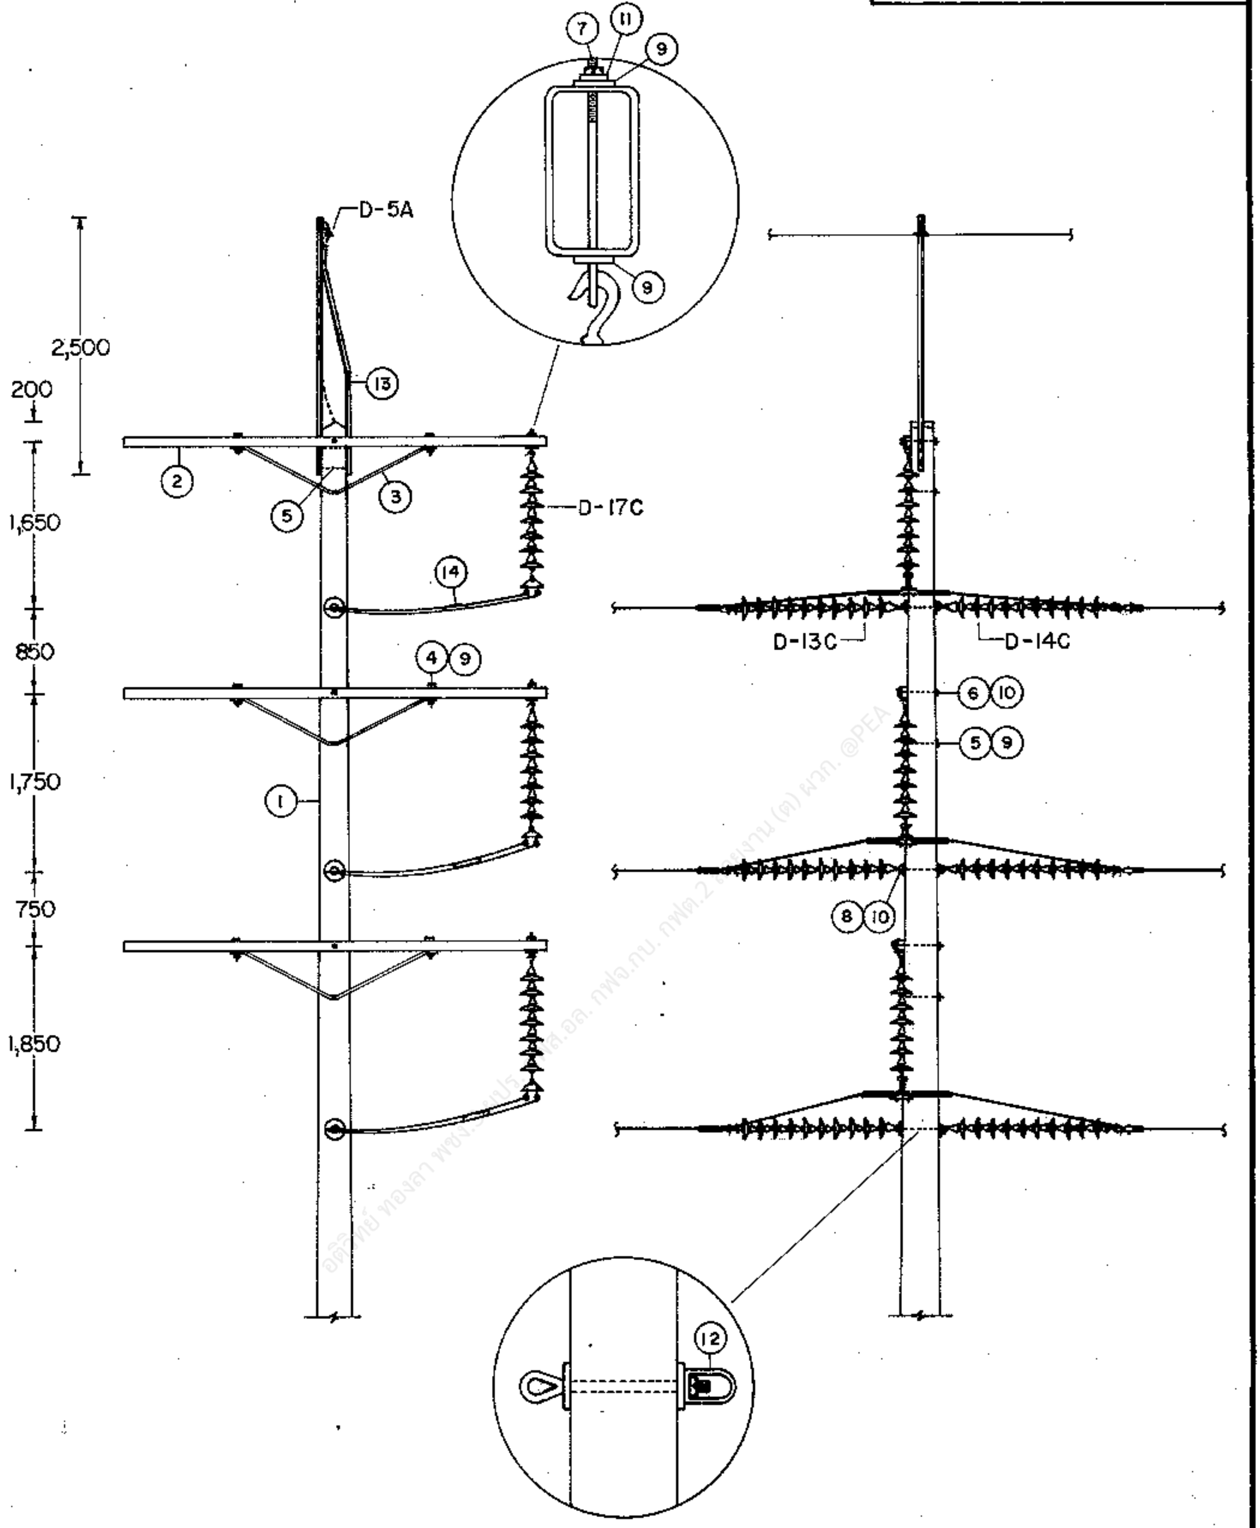
7
11
9
9
D-5A
2,500
200
13
2
5
3
D-17C
1,650
14
850
4 9
1,750
1
750
1,850
D-13C
D-14C
6 10
5 9
8 10
12

อดิสิทย์ ทองลา พชง.3 ผปร. [illegible] ผส.อล. กฟจ.กบ. กฟต.2 [illegible] (ต) ผวภ. @PEA

กองวิศวกรรมไฟฟ้าและเครื่องกล ฝ่ายวิศวกรรม	**การไฟฟ้าส่วนภูมิภาค**	ใช้แทนแบบ.......... ถูกแทนโดยแบบ.......... เขียนเสร็จวันที่ 2 มค.23 แก้แบบวันที่.......... มิติเป็น มม. มาตราส่วน 1 : 75
ผู้เขียน .... ผู้สำรวจ.......... วิศวกร .... หัวหน้าแผนก .... หัวหน้ากอง.......... ผู้อำนวยการฝ่าย.......... 23	ผู้ว่าการ.......... ๒๔ มี.ค. ๒๓.	
	115 kV วงจรเดียว สายไฟฟ้าคู่ เสาสำหรับเข้าปลายสายสองข้าง แบบ SD-DD-1	
รองผู้ว่าการฝ่ายเทคนิค	115 kV SINGLE CIRCUIT DOUBLE CONDUCTOR DOUBLE DEAD END STRUCTURE TYPE SD-DD-1	แบบเลขที่ SAI-015/23011 แผ่นที่ 2 ของจำนวน 3 แผ่น

1 มิ.ย. 2523

การประกอบเลขที่
ASSEMBLY NO. 5257

บัญชีวัสดุ
BILL OF MATERIAL

ลำดับที่ ITEM	รายละเอียด DESCRIPTION	จำนวน REQ'D	วัสดุเลขที่ MAT. NO.
1	เสาคอนกรีต 22 ม. POLE, CONCRETE 22 m LONG	1	00010011 (0041)
2	คอนสายแบบเหล็ก ขนาด 100X50X3.2 มม. ยาว 4.20 ม. CROSSARM, STEEL, 100X50X3.2 mm 4.20 m LONG	3	00120001 (0116)
3	เหล็กฉากรับคอนสาย ขนาด 50X50X6 มม. ช่วงกว้าง 1,800 มม. ดรอพ 450 มม. BRACE, ANGLE STEEL 50 X 50 X 6 mm, 1,800 mm WIDE 450 mm DROP	3	01200007 (0119)
4	สลักเกลียว M 16 X 130 มม. BOLT, MACHINE, M 16 X 130 mm	6	01110200 (0220) *
5	สลักเกลียว M 16 X 350 มม. BOLT, MACHINE, M 16 X 350 mm	6	01110205 (0225)
6	สลักเกลียว M 20 X 400 มม. BOLT, MACHINE, M 20 X 400 mm	3	01110301 (0233)
7	สลักห่วงโอแวล M 16 X 150 มม. BOLT, OVAL EYE, M 16 X 150 mm	3	01150000 (0257)
8	สลักห่วงโอแวล M 20 X 350 มม. BOLT, OVAL EYE, M 20 X 350 mm	3	01150100 (0260)
9	แหวนสี่เหลี่ยมแบน 52X52X4.5 มม. รู Ø 18 มม. มอก. 258 WASHER, SQUARE, FLAT 52X52 X4.5 mm HOLE Ø 18 mm TIS. 258	15	01180100 (0355)
10	แหวนสี่เหลี่ยมแบน 62X62X6 มม. รู Ø 22 มม. มอก. 258 WASHER, SQUARE, FLAT, 62X62X6 mm HOLE Ø 22 mm TIS 258	12	01180101 (0356)
11	แหวนสปริง M 16 มอก. 259 WASHER, LOCK, M 16, TIS 259	3	01180301 (0365)
12	อายเล็ท สำหรับสลักเกลียว M 20 EYELET FOR BOLT, M 20	3	01180002 (0346)
13	เหล็กฉากรับสายล่อฟ้าทางโค้ง OVERHEAD GROUND WIRE CORNER BAYONET	1	01010005 (0136)
14	ปรีฟอร์มแยกสาย SPACER, HELICAL ROD, PREFORMED	6	02240000 (0918)
	รายละเอียด DETAIL		
D-13C	การประกอบลูกถ้วยแขวน SUSPENSION INSULATOR ASSEMBLY	3	
D-14C	การประกอบลูกถ้วยแขวน SUSPENSION INSULATOR ASSEMBLY	3	
D-17C	การประกอบลูกถ้วยแขวน SUSPENSION INSULATOR ASSEMBLY	3	
D-5A	การต่อสายล่อฟ้า OVERHEAD GROUND WIRE CONNECTION	1	
D-10A	ฐานรากเสา POLE FOUNDATION	1	

กองวิศวกรรมไฟฟ้าและเครื่องกล
ฝ่ายวิศวกรรม
ผู้เขียน
ผู้สำรวจ
วิศวกร
หัวหน้าแผนก ธีรศักดิ์
หัวหน้ากอง
ผู้อำนวยการฝ่าย 28 [illegible] 23
รองผู้ว่าการฝ่ายเทคนิค

การไฟฟ้าส่วนภูมิภาค

ผู้ว่าการ 24 [illegible].23

115 kV วงจรเดี่ยว สายไฟฟ้าคู่
เสาสำหรับเข้าปลายสายสองข้าง
แบบ SD-DD-1

115 kV SINGLE CIRCUIT DOUBLE CONDUCTOR
DOUBLE DEAD END STRUCTURE
TYPE SD-DD-1

ใช้แทนแบบ
ถูกแทนโดยแบบ
เขียนเสร็จวันที่ 2 ม.ค.23
แก้แบบวันที่
มิติเป็น
มาตราส่วน
แบบเลขที่ SAI-015/23011
แผ่นที่ 3 ของจำนวน 3 แผ่น

1 [illegible]