

การประกอบเลขที่
ASSEMBLY NO. 5360

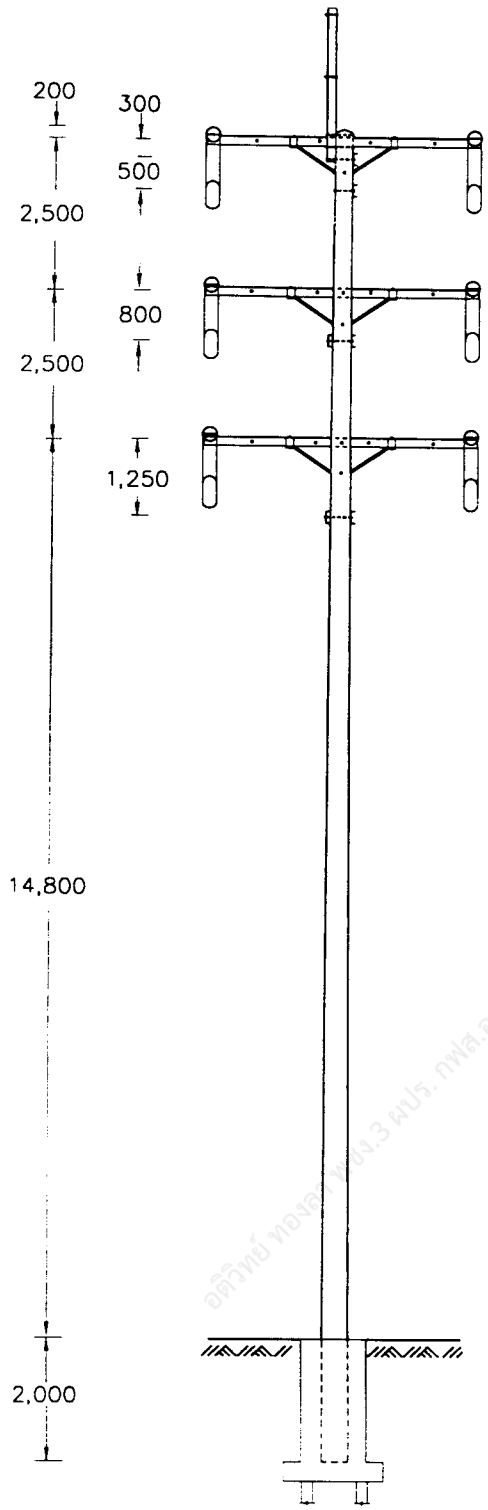


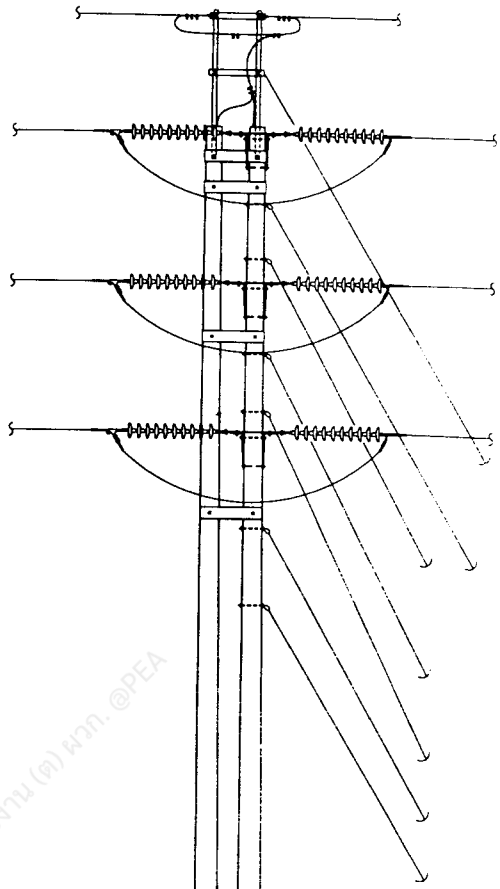


อดิวิทย์ ทองสุข พง.3 ศนร. กฟส.อล. กฟน.กบ. กฟต.2 สายงาน (ค) ผวก. @PEA

กองมาตรฐานระบบไฟฟ้า ฝ่ายมาตรฐานและความปลอดภัย	การไฟฟ้าส่วนภูมิภาค	ใช้แทนแบบ ..... ถูกแทนโดยแบบ .....
ผู้เขียน สมชาย ..... ผู้สำรวจ ..... วิศวกร ..... หัวหน้าแผนก ..... ผู้อำนวยการกอง ..... ผู้อำนวยการฝ่าย	ผู้ว่าการ ..... แทน	เขียนเสร็จวันที่ 15 ต.ค. 44 แก้แบบวันที่ ..... มิติเป็น มิลลิเมตร มาตราส่วน 1 : 125
	115 kV วงจรคู่ สายไฟฟ้าคู่ โครงสร้างเสาช่วงระยะไม่เกิน 150 ม. แบบ DD-LS-1	
รองผู้ว่าการวางแผน และพัฒนาระบบไฟฟ้า	115 kV DOUBLE CIRCUIT DOUBLE CONDUCTOR SPAN ≤150 m STRUCTURE TYPE DD-LS-1	แบบเลขที่ SA1-015/44014 แผ่นที่ 1 ของจำนวน 6 แผ่น


การประกอบเลขที่
ASSEMBLY NO. 5360

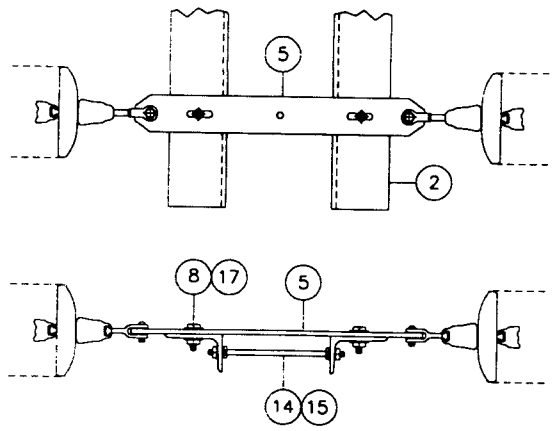


รายละเอียด A
DETAIL A

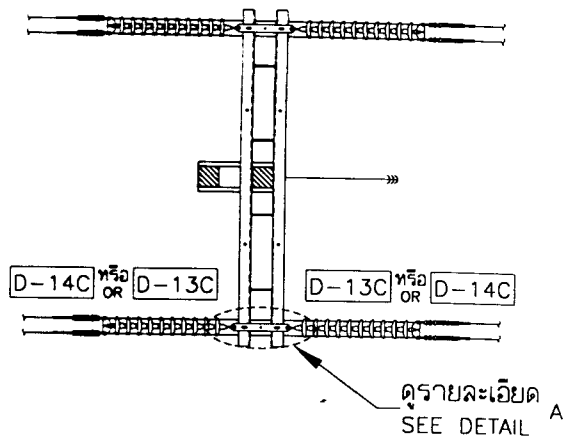


รูปตัด A-A
SECTION A-A

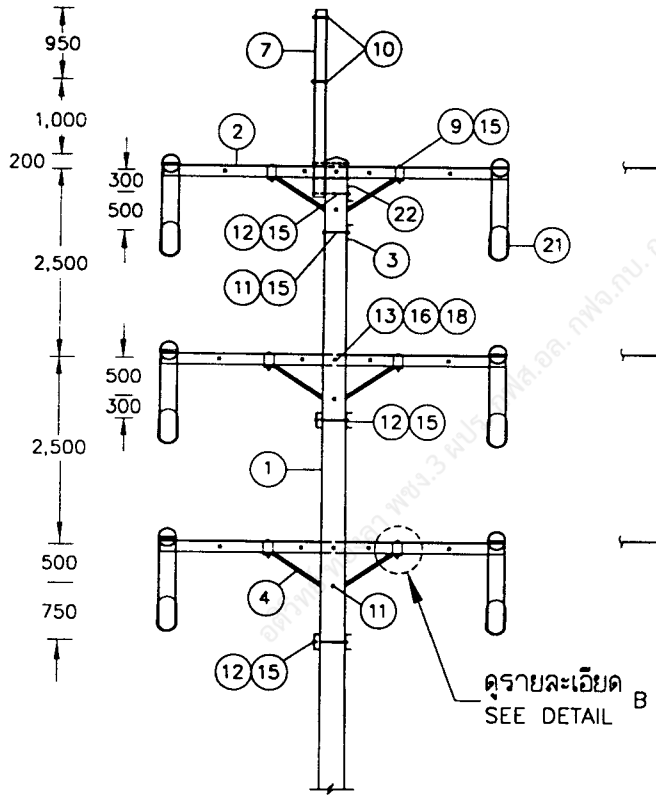

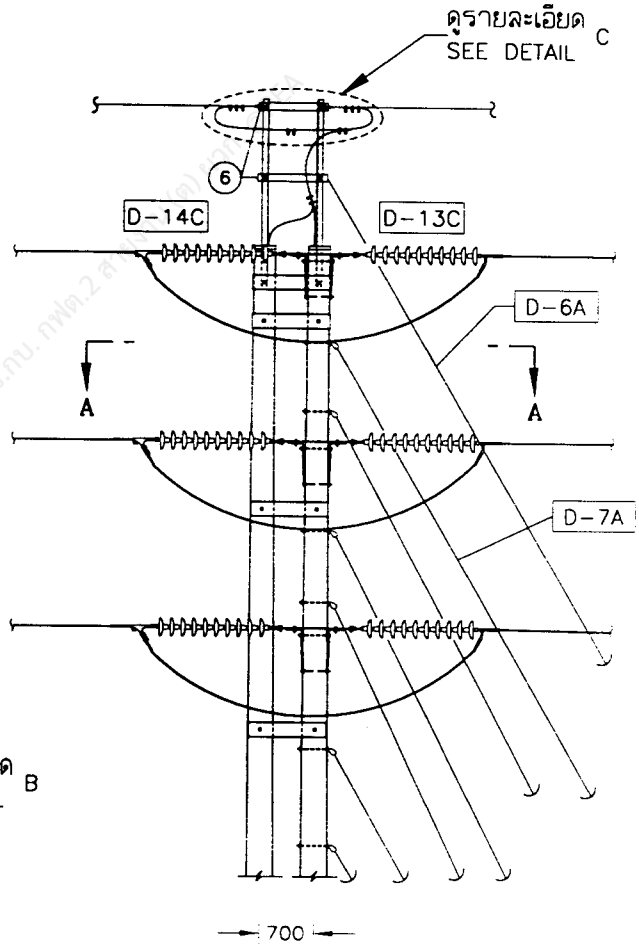


กองมาตรฐานระบบไฟฟ้า ฝ่ายมาตรฐานและความปลอดภัย	การไฟฟ้าส่วนภูมิภาค	ใช้แทนแบบ ..... ถูกแทนโดยแบบ .....
ผู้เขียน สมชาย ผู้สำรวจ ..... วิศวกร ..... หัวหน้าแผนก ..... ผู้อำนวยการกอง ..... ผู้อำนวยการฝ่าย	ผู้ว่าการ ..... 115 kV วงจรคู่ สายไฟฟ้าคู่ โครงสร้างเสาช่วงระยะไม่เกิน 150 ม. แบบ DD-LS-1	เขียนเสร็จวันที่ 15 ต.ค. 44 แก้แบบวันที่ ..... มิติเป็น มิลลิเมตร มาตราส่วน 1 : 100
รองผู้ว่าการวางแผน และพัฒนาระบบไฟฟ้า	115 kV DOUBLE CIRCUIT DOUBLE CONDUCTOR SPAN ≤150 m STRUCTURE TYPE DD-LS-1	แบบเลขที่ SA1-015/44014 แผ่นที่ 2 ของจำนวน 6 แผ่น


การประกอบเลขที่ ASSEMBLY NO. 5360

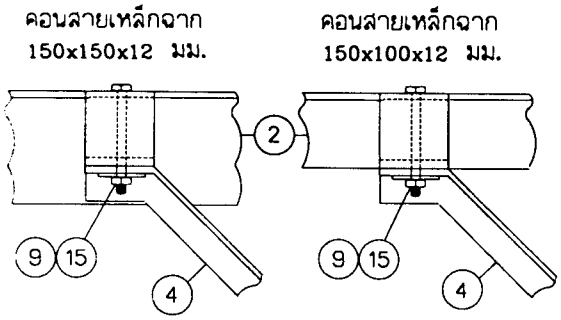


รายละเอียด B
DETAIL B

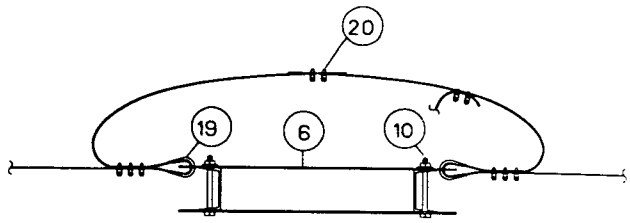


รายละเอียด C
DETAIL C

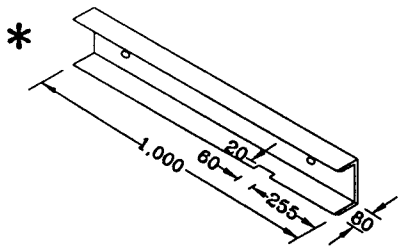

วัสดุลำดับที่ ITEM. NO. (22)

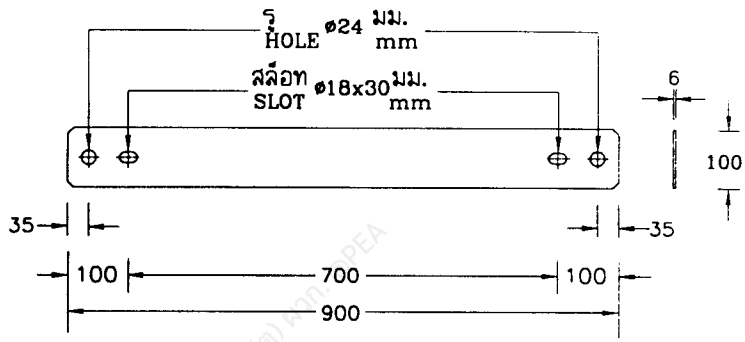

วัสดุลำดับที่ ITEM. NO. (6)

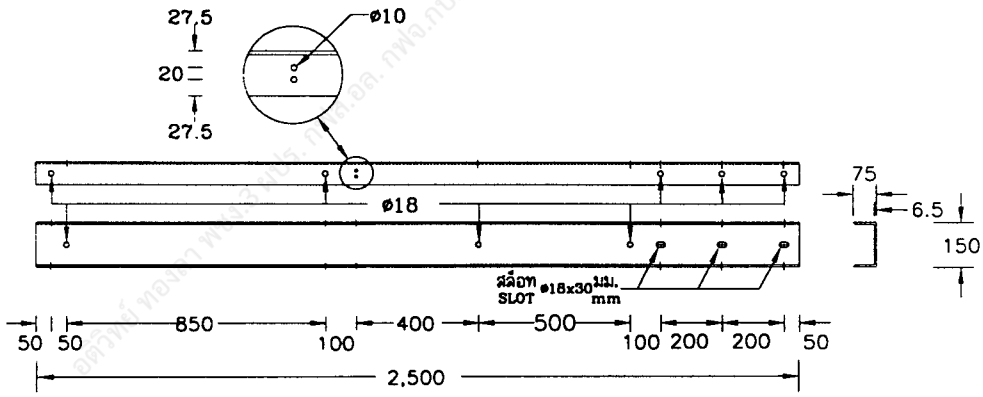


วัสดุลำดับที่ ITEM. NO. (7)

* ดัดแปลงเพิ่มเติมจากวัสดุเลขที่ 01000400 และใช้ SPRAY ZINC พ่นทับร่องที่บาก
MADE FROM MAT. NO. 01000400 AND SPRAY ZINC AT DITCH

กองมาตรฐานระบบไฟฟ้า ฝ่ายมาตรฐานและความปลอดภัย	การไฟฟ้าส่วนภูมิภาค	ใช้แทนแบบ ..... ถูกแทนโดยแบบ .....
ผู้เขียน สมชาย ..... ผู้สำรวจ ..... วิศวกร ..... หัวหน้าแผนก ..... ผู้อำนวยการกอง ..... ผู้อำนวยการฝ่าย	ผู้ว่าการ ..... แทน	เขียนเสร็จวันที่ 15 ต.ค. 44 แก้แบบวันที่ ..... มิติเป็น มิลลิเมตร มาตราส่วน .....
รองผู้ว่าการวางแผน และพัฒนาระบบไฟฟ้า	115 kV วงจรคู่ สายไฟฟ้าคู่ โครงสร้างเสาช่วงระยะไม่เกิน 150 ม. แบบ DD-LS-1	
	115 kV DOUBLE CIRCUIT DOUBLE CONDUCTOR SPAN ≤150 m STRUCTURE TYPE DD-LS-1	แบบเลขที่ SA1-015/44014 แผ่นที่ 3 ของจำนวน 6 แผ่น

การประกอบเลขที่ ASSEMBLY NO.	5360

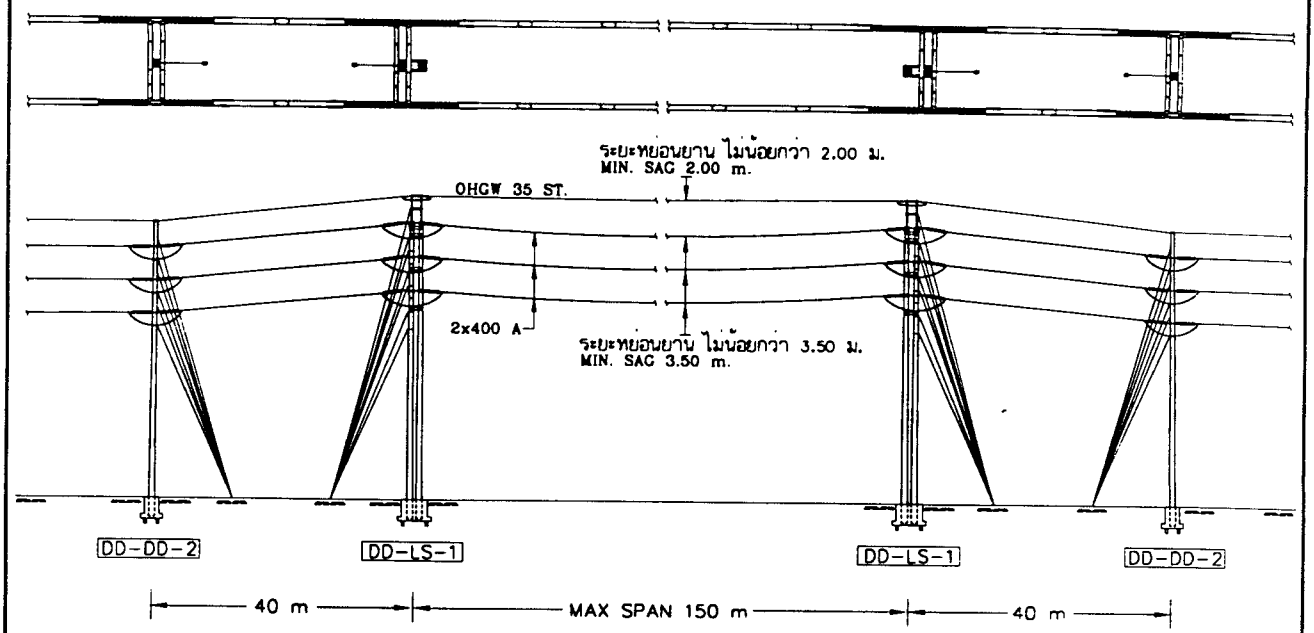

ข้อกำหนดใช้งาน

แบบมาตรฐานนี้ สามารถนำไปใช้ได้ในกรณีดังต่อไปนี้ :-

1. กรณีแม่น้ำนั้นมีสะพานข้ามแม่น้ำขนานไปกับแนวสายส่งและระยะห่างตามแนวระดับระหว่างสายไฟฟ้ากับขอบสะพานไม่น้อยกว่า 4.5 ม. ที่ระยะหย่อนยานสายสูงสุดสายไฟฟ้าเส้นล่างสุดต้องมีระยะห่างในแนวดิ่งจากส่วนสูงสุดของท้องคานสะพานไม่น้อยกว่า 3.9 ม.
2. กรณีแม่น้ำนั้นไม่มีสะพานข้ามแม่น้ำ และเรือที่สัญจรผ่านมีความสูงไม่เกิน 7 ม.
3. ในกรณีก่อสร้างข้ามทางรถไฟ ฯลฯ ให้พิจารณาระยะห่างความปลอดภัยตามแบบมาตรฐาน เลขที่ SA1-015/17068 (การประกอบเลขที่ 9301)
4. หากพิจารณาตรวจสอบสถานที่แล้วไม่เป็นไปตามข้อกำหนดดังกล่าวข้างต้น ต้องพิจารณาออกแบบเฉพาะใหม่เป็นแห่งๆ ไป

RECOMMENDATION

THESE DRAWINGS CAN BE USED IN THE FOLLOWING CASE :

1. THERE IS A BRIDGE PARALLEL THE 115 kV LINE AND THE HORIZONTAL CLEARANCE BETWEEN CONDUCTOR AND THE EDGE OF BRIDGE IS NOT LESS THAN 4.5 m, THE LOWEST CONDUCTOR AT MAXIMUM SAG SHALL HAVE VERTICAL CLEARANCE FROM THE HIGHEST POINT ON BOTTOM OF THE BRIDGE BEAM NOT LESS THAN 3.9 m
2. THERE IS NO BRIDGE AND THE HEIGHT OF PASSING BOATS ARE NOT MORE THAN 7 m
3. IN CASE LINES ARE ABOVE THE RAILWAYS .etc., MINIMUM CLEARANCES IN SHALL BE CONSIDED DWG.NO. S02-015/17068 (ASSEMBLY NO. 9301)
4. OTHER CASES, NEW DESIGN IS NEEDED .

กองมาตรฐานระบบไฟฟ้า ฝ่ายมาตรฐานและความปลอดภัย	การไฟฟ้าส่วนภูมิภาค	ใช้แทนแบบ ..... ถูกแทนโดยแบบ .....
ผู้เขียน สมชาย..... ผู้สำรวจ..... วิศวกร..... หัวหน้าแผนก..... ผู้อำนวยการกอง..... ผู้อำนวยการฝ่าย.....	ผู้ว่าการ ..... แทน.....	เขียนเสร็จวันที่ 15 ต.ค. 44 แก้แบบวันที่ ..... มิติเป็น ..... มาตราส่วน .....
รองผู้ว่าการวางแผน และพัฒนาระบบไฟฟ้า	115 kV วงจรคู่ สายไฟฟ้าคู่ โครงสร้างเสาช่วงระยะไม่เกิน 150 ม. แบบ DD-LS-1	
	115 kV DOUBLE CIRCUIT DOUBLE CONDUCTOR SPAN ≤150 m STRUCTURE TYPE DD-LS-1	แบบเลขที่ SA1-015/44014 แผ่นที่ 4 ของจำนวน 6 แผ่น

การประกอบเลขที่ ASSEMBLY NO. 5360

บัญชีวัสดุ
BILL OF MATERIAL

ลำดับที่ ITEM	รายละเอียด DESCRIPTION	จำนวน REQ'D	วัสดุเลขที่ MAT. NO.
1	เสาคอนกรีต 22 ม. POLE, CONCRETE, 22 m LONG	2	00010011
2	คอนสายแบบเหล็กฉาก ขนาด 150x100x12 มม. ยาว 4.50 ม. หรือขนาด 150x150x12 มม. ยาว 4.50 ม. CROSSARM,STEEL ANGLE,150x100x12 mm.,4.50 m LONG or STEEL ANGLE, 150x150x12 mm., 4.50 m LONG	6	00120002
3	เหล็กรูปรางน้ำ ขนาด 200x80x7.5 มม. ยาว 1,000 มม. STEEL CHANNEL, 200x80x7.5 mm 1,000 mm LONG	5	01000400
4	เหล็กฉากรับคอนสาย ขนาด 50x50x6 มม. ช่วงกว้าง 1,800 มม. ดรอพ 450 มม. BRACE, ANGLE STEEL 50x50x6 mm, 1,800 mm WIDE ,450 mm DROP	6	01200007
5	แผ่นเหล็กยึนสองปลาย ขนาด 12x100x760 มม. PLATE,STEEL,DOUBLE ARMING,12x100x760 mm	6	01030102
6	แผ่นเหล็ก ขนาด 6x100 มม. ยาว 900 มม. PLATE,STEEL, 6x100 mm, 900 mm LONG	4	–
7	เหล็กรูปรางน้ำรับสายล่อฟ้า ขนาด 150x75x6.5 มม. ยาว 2,500 มม. OVERHEAD GROUND WIRE STEEL CHANNEL, 150x75x6.5 mm 2,500 mm LONG	2	–
8	สลักเกลียว M16x75 มม. พร้อมแหวนกลม 2 อัน BOLT, MACHINE, M16x75 mm COMPLETE WITH 2 ROUND WASHERS	12	01110400
9	สลักเกลียว M16x170 มม. BOLT, MACHINE M16x170 mm	12	01110201
10	สลักเกลียว M16x200 มม. BOLT, MACHINE M16x200 mm	4	01110202
11	สลักเกลียว M16x350 มม. BOLT, MACHINE M16x350 mm	5	01110205
12	สลักเกลียว M16x450 มม. BOLT, MACHINE M16x450 mm	8	01110207
13	สลักเกลียว M20x350 มม. BOLT, MACHINE M20x350 mm	3	01110300
14	สลักเกลียวตลอด M16x400 มม. BOLT, DOUBLE ARMING, M16x400 mm	12	01120000
15	แหวนสี่เหลี่ยมแบน 52x52x4.5 มม. รู ø18 มม. มอก. 258 WASHER, SQUARE, FLAT, 52x52x4.5 mm, HOLE ø18 mm, TIS 258	73	01180100
16	แหวนสี่เหลี่ยมแบน 62x62x6 มม. รู ø22 มม. มอก. 258 WASHER, SQUARE, FLAT, 62x62x6 mm, HOLE ø22 mm, TIS 258	3	01180101
17	แหวนสปริง M16 ประเภทใช้งานทั่วไป มอก. 259 WASHER, LOCK, M16 GENERAL PURPOSE, TIS 259	12	01180301
18	แหวนสปริง M 20 มอก. 259 WASHER, LOCK, SPRING, SIZE 20 mm, GENERAL PURPOSE, TIS 259	3	01180302
19	กายทิมเบิ้ล THIMBLE, GUY	3	01210304
20	ยูแคล้มป์ สลัก 1 ตัว เอ็ม 8 CLAMP, SINGLE U-BOLT, M. 8	14	01230000

กองมาตรฐานระบบไฟฟ้า
ฝ่ายมาตรฐานและความปลอดภัย

ผู้เขียน สมชาย
ผู้สำรวจ
วิศวกร
หัวหน้าแผนก
ผู้อำนวยการกอง
ผู้อำนวยการฝ่าย

รองผู้ว่าการวางแผน และพัฒนาระบบไฟฟ้า

การไฟฟ้าส่วนภูมิภาค

ผู้ว่าการ

115 kV วงจรคู่ สายไฟฟ้าคู่
โครงสร้างเสาช่วงระยะไม่เกิน 150 ม.
แบบ DD-LS-1

115 kV DOUBLE CIRCUIT DOUBLE CONDUCTOR
SPAN ≤150 m STRUCTURE
TYPE DD-LS-1

ใช้แทนแบบ .....
ถูกแทนโดยแบบ .....
เขียนเสร็จวันที่ 15 ต.ค. 44
แก้แบบวันที่ .....
มิติเป็น .....
มาตราส่วน .....

แบบเลขที่ SA1-015/44014
แผ่นที่ 5 ของจำนวน 6 แผ่น

การประกอบเลขที่ ASSEMBLY NO. 5360

บัญชีวัสดุ BILL OF MATERIAL

ลำดับที่ ITEM	รายละเอียด DESCRIPTION	จำนวน REQ'D	วัสดุเลขที่ MAT. NO.
21	ปริฟอร์มแยกสาย สำหรับสายอะลูมิเนียม 400 ต.มม. SPACER,HELICAL ROD,PREFORMED,FOR AL 400 sq.mm.	6	02240000
22	เหล็กรูปรางน้ำ ขนาด 200x80x7.5 มม. ยาว 1,000 ม. STEEL CHANNEL, 200x80x7.5 mm 1,000 mm LONG	1	-

แบบอ้างอิง REFERANCE DRAWING			การประกอบเลขที่ ASSEMBLY NO.
D-13C	การประกอบลูกถ้วยแขวน SUSPENSION INSULATOR ASSEMBLY	6	5607
D-14C	การประกอบลูกถ้วยแขวน SUSPENSION INSULATOR ASSEMBLY	6	5608
D-6A	การประกอบยึดโยงลวดเหล็กตีเกลียว 50 ต.มม. STEEL STRANDED WIRE 50 mm², GUY ASSEMBLY	1	5636 หรือ or 5637
D-7A	การประกอบยึดโยงลวดเหล็กตีเกลียว 95 ต.มม. STEEL STRANDED WIRE 95 mm², GUY ASSEMBLY	6	5638 หรือ or 5639
D-9A	สมอบกคอนกรีต CONCRETE ANCHOR	1	5659 B หรือ or 5659 D
D-10B	ฐานรากเสา POLE FOUNDATION	1	5687 C หรือ or 5687 E หรือ or 5687 H หรือ or 5687 J

กองมาตรฐานระบบไฟฟ้า ฝ่ายมาตรฐานและความปลอดภัย	การไฟฟ้าส่วนภูมิภาค	ใช้แทนแบบ ..... ถูกแทนโดยแบบ .....
ผู้เขียน ...สมชาย..... ผู้สำรวจ..... วิศวกร..... หัวหน้าแผนก..... ผู้อำนวยการกอง..... ผู้อำนวยการฝ่าย.....	ผู้ว่าการ...[illegible]...แทน	เขียนเสร็จวันที่ 15 ต.ค. 44 แก้แบบวันที่ ..... มิติเป็น ...-..... มาตราส่วน ...-.....
รองผู้ว่าการวางแผน และพัฒนาระบบไฟฟ้า .....[illegible].....	115 kV วงจรคู่ สายไฟฟ้าคู่ โครงสร้างเสาช่วงระยะไม่เกิน 150 ม. แบบ DD-LS-1	
	115 kV DOUBLE CIRCUIT DOUBLE CONDUCTOR SPAN ≤150 m STRUCTURE TYPE DD-LS-1	แบบเลขที่ SA1-015/44014 แผ่นที่ 6 ของจำนวน 6 แผ่น