การประกอบเลขที่
ASSEMBLY NO. 0103

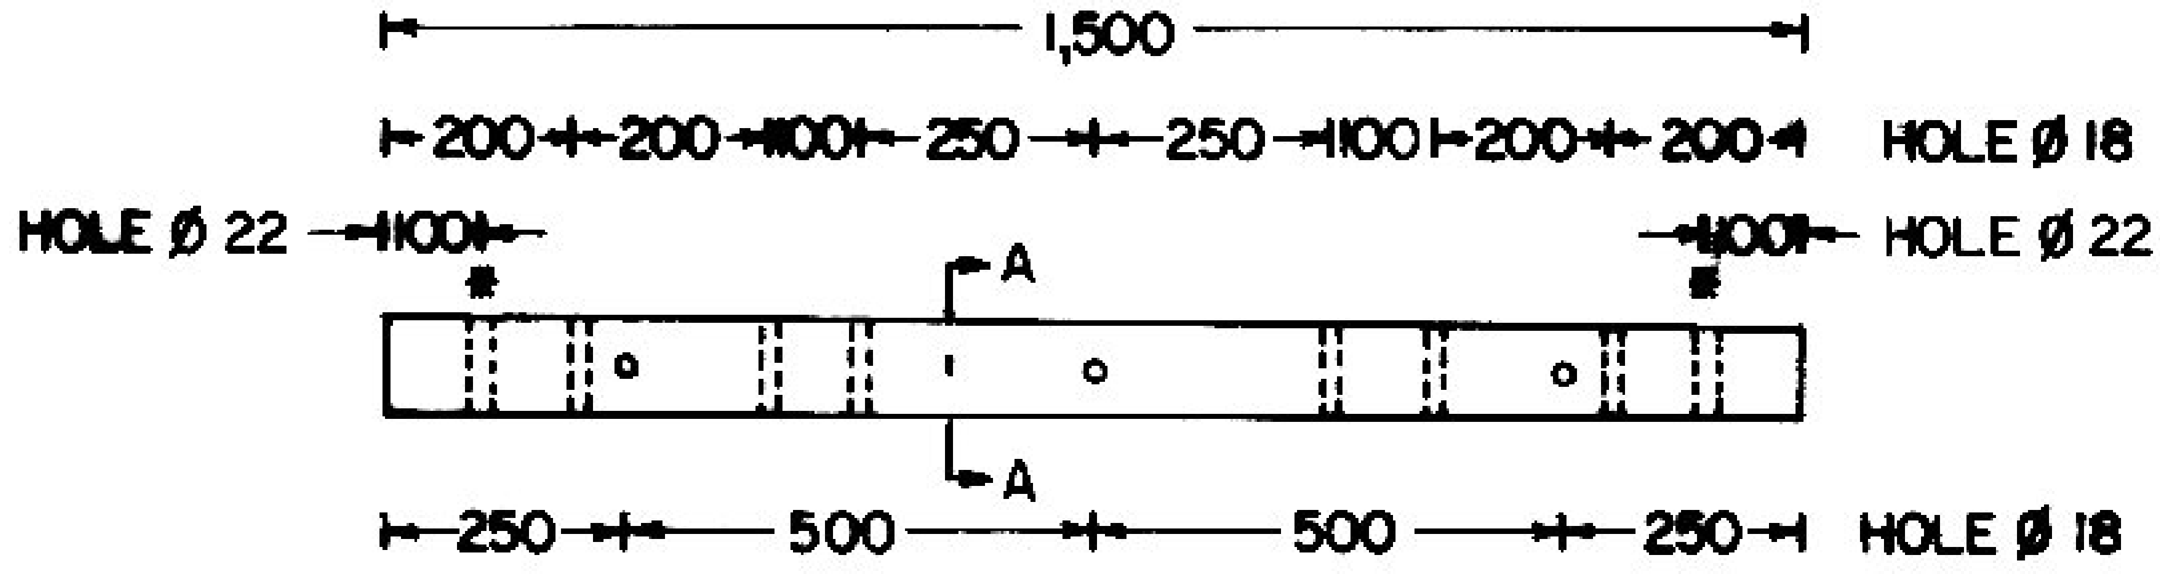

WORKING MOMENT 225 kg – m SAFETY FACTOR = 3

WEIGHT ≃ 36 kg

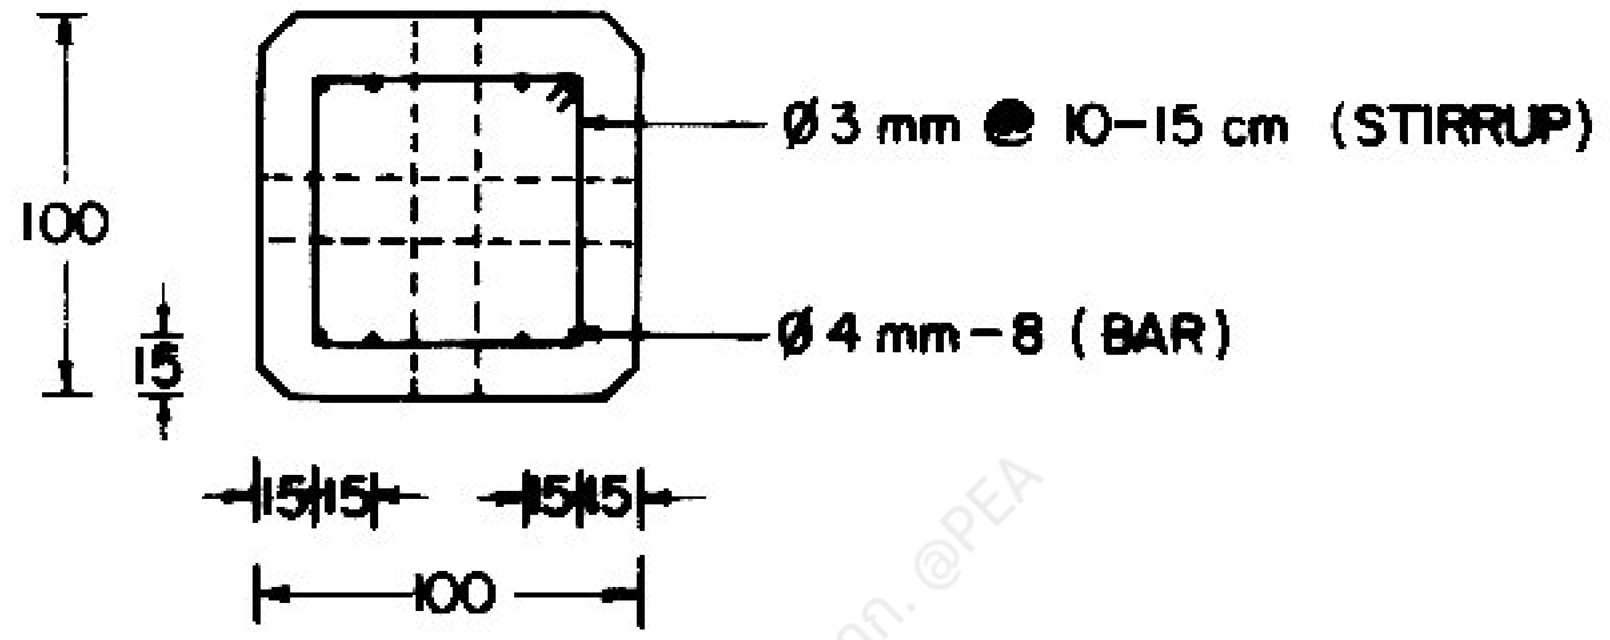

รูปตัด
SECTION A–A

คอน คอนกรีตอัดแรง 100 X 100 X 1,500 มม.

1 ใช้เป็นคอนสำหรับติดตั้งฟิวส์สวิตช์แรงต่ำ รายละเอียดการติดตั้ง ดูแบบเลขที่ SAI-015/22012 (การประกอบเลขที่ 0406)

2 ใช้เป็นคอนสำหรับติดตั้งเคเบิลอากาศ 2 วงจร รายละเอียดการติดตั้ง ดูแบบเลขที่ SAI-015/21036, SAI-015/21041 (การประกอบเลขที่ 2307, 2308) (ใช้คอน คอร. แทนไม้คอน)

3 ใช้เป็นคอนสำหรับติดตั้งลูกถ้วยก้านตรง ระบบ 1 เฟส 19 kV รายละเอียดการติดตั้ง ดูแบบเลขที่ SAI-015/29023 (การประกอบเลขที่ 3308)

PRESTRESSED CONCRETE CROSSARM, 100X100 X 1,500 mm

1 FOR MOUNTING L.T. FUSE SWITCH. DETAIL OF INSTALLATION SEE DWG. NO. SAI-015/22012

2 FOR 2 CIRCUITS AERIAL CABLE INSTALLATION. DETAIL OF INSTALLATION SEE DWG. NO. SAI-015/21036, SAI-015/21041 (USE PRESTRESSED CONCRETE CROSSARM INSTEAD OF WOOD CROSSARM)

3 FOR 1 PHASE 19 kV SYSTEM, AS CROSSARM OF PIN TYPE INSULATOR DETAIL OF INSTALLATION SEE DWG. NO. SAI-015/29023 (ASSEMBLY NO. 3308)

กองเสาและไม้คอน
ฝ่ายก่อสร้าง

ผู้เขียน ...
ผู้ตรวจ ...
วิศวกร ...
หัวหน้าแผนก ...
หัวหน้ากอง ...
ผู้อำนวยการฝ่าย ...
รองผู้ว่าการฝ่ายเทคนิค

การไฟฟ้าส่วนภูมิภาค

ผู้ว่าการ ...

คอน คอนกรีตอัดแรง 100X100X1,500 มม.

PRESTRESSED CONCRETE CROSSARM, 100X100X1,500 mm

ใช้แทนแบบ ...
ถูกแทนโดยแบบ ...
เขียนเสร็จวันที่ 8 ก.พ. 22
แก้แบบวันที่ 9 พ.ย. 30
มิติเป็น มม.
มาตราส่วน 1 : 5 , 1 : 20

แบบเลขที่ KDO-015/[illegible]
แผ่นที่ 1 ของจำนวน 1 แผ่น