

การประกอบเลขที่ ASSEMBLY NO.	0809

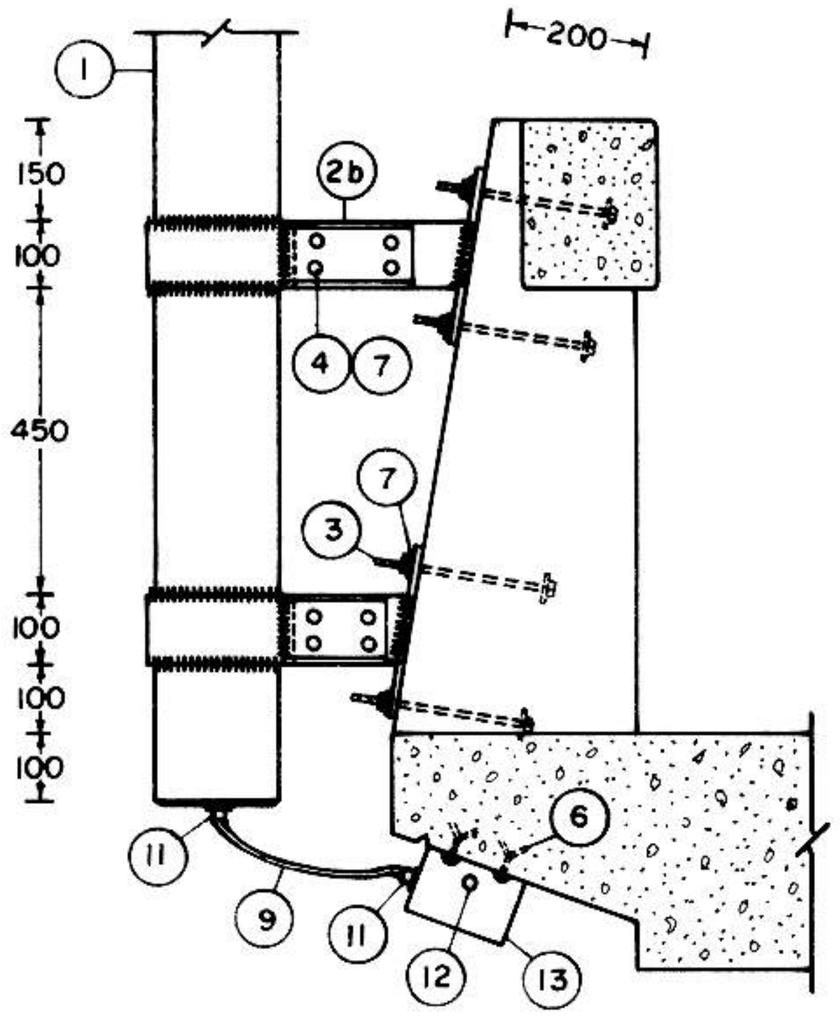

แบบที่ 1 กรณีราวสะพานลาดเอียง
TYPE 1 CASE : SLOPING EXISTING BRIDGE

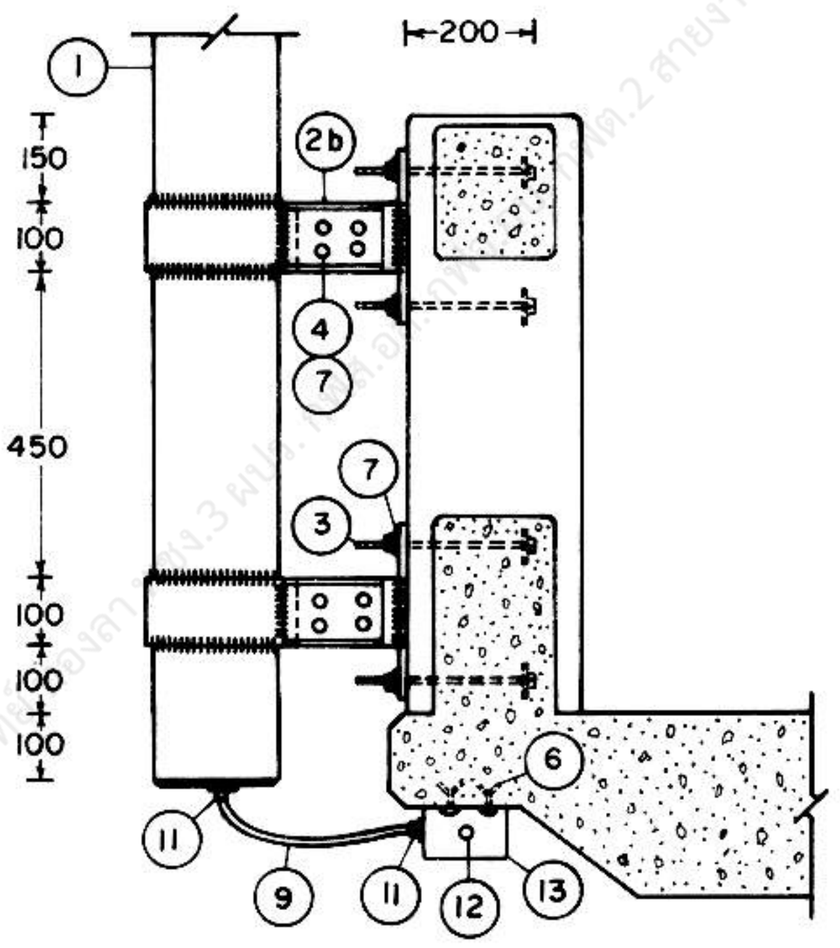


แบบที่ 2 กรณีราวสะพานตั้งฉาก
TYPE 2 CASE: PERPENDICULARITY EXISTING BRIDGE


กองวิศวกรรมไฟฟ้าและเครื่องกล ฝ่ายวิศวกรรม	การไฟฟ้าส่วนภูมิภาค	ใช้แทนแบบ ถูกแทนโดยแบบ เขียนเสร็จวันที่ 15 ก.พ. 23 แก้แบบวันที่ มิติเป็น มม. มาตราส่วน 1 : 20
ผู้เขียน ผู้สำรวจ วิศวกร หัวหน้าแผนก หัวหน้ากอง ผู้อำนวยการฝ่าย	ผู้ว่าการ การติดตั้งไฟฟ้าแสงสว่างบนสะพาน	
รองผู้ว่าการฝ่ายเทคนิค	BRIDGE LIGHTING INSTALLATION	แบบเลขที่ SAI-015/23038 แผ่นที่ 1 ของจำนวน 3 แผ่น

4 เม.ย. 2523

การประกอบเลขที่ 0809
ASSEMBLY NO.

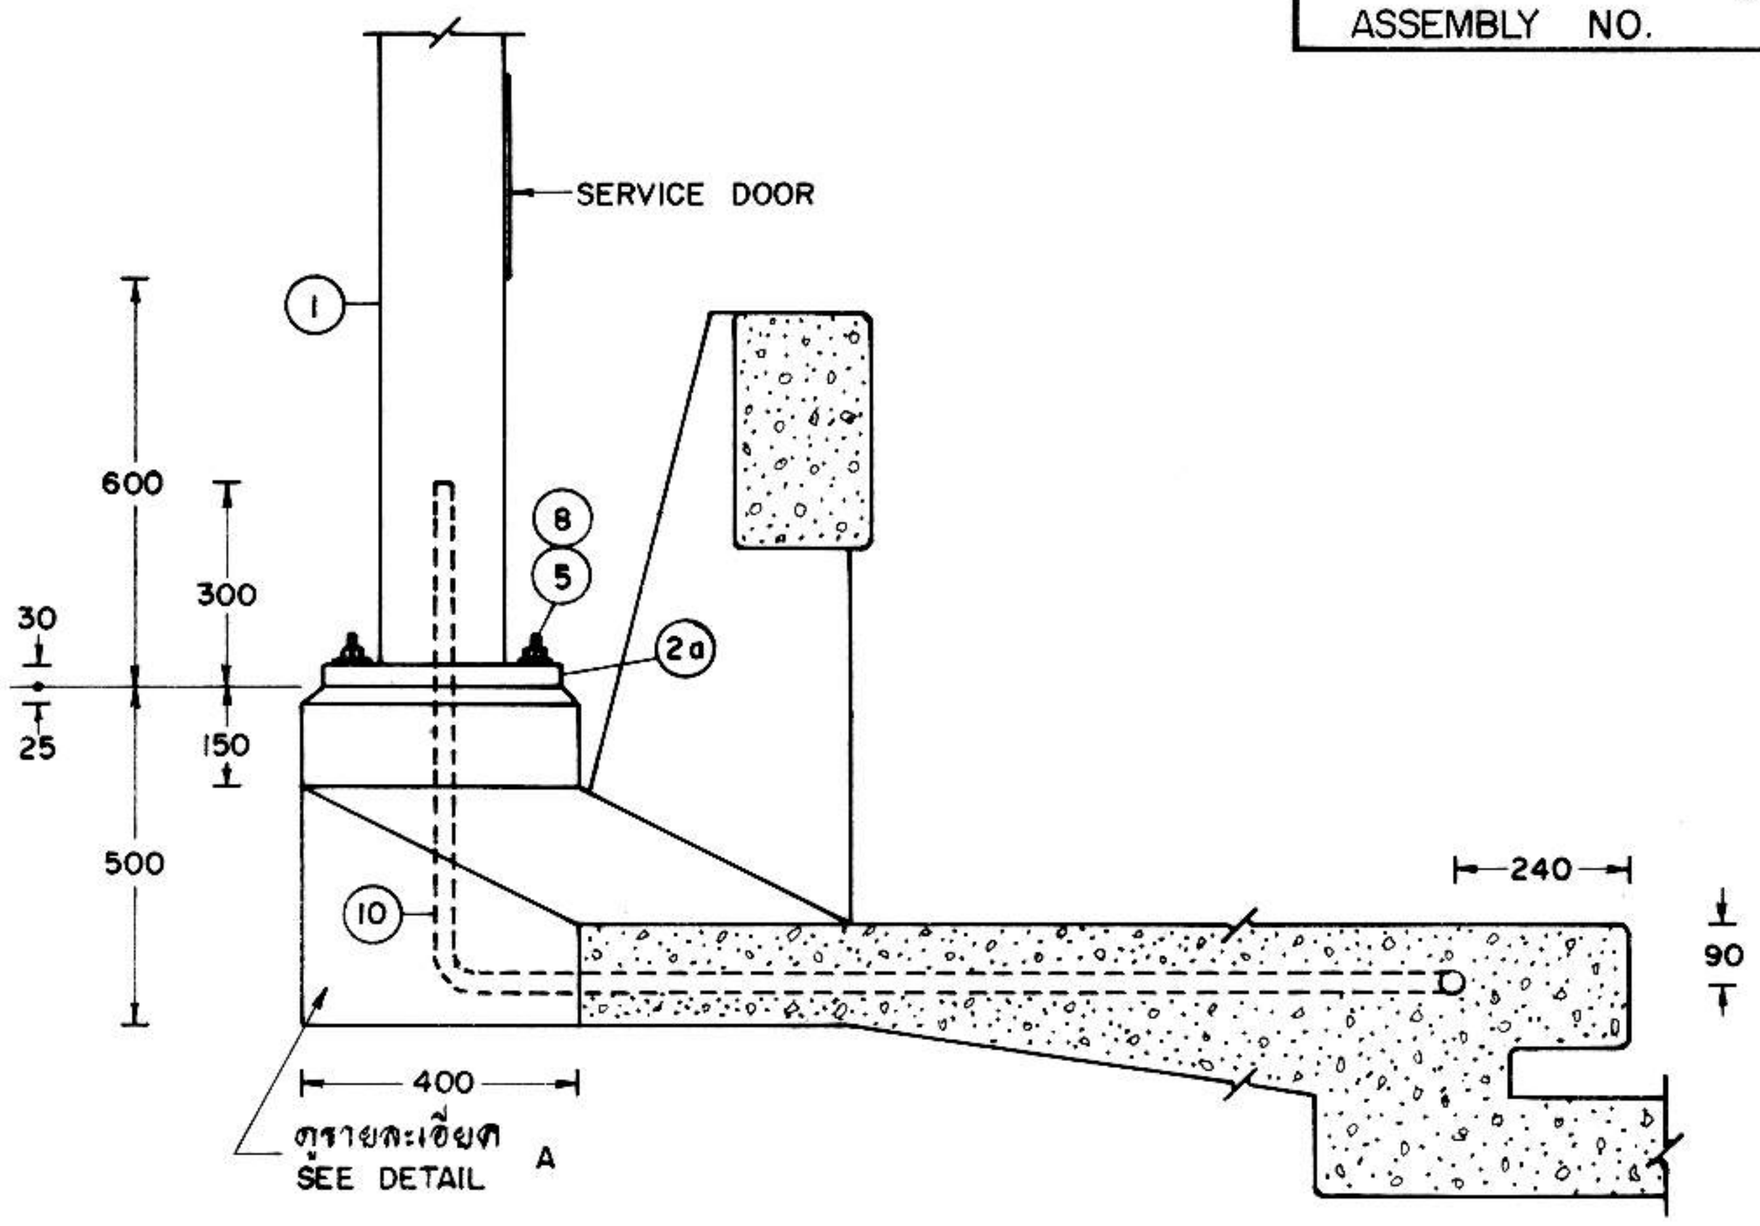

แบบที่ 3 กรณีที่สะพานสร้างฐานคอนกรีตไว้สำหรับติดตั้งเสาไฟฟ้าแสงสว่าง
TYPE 3 CASE: FIXING OF LIGHTING POLE ON PROVIDE CONCRETE BASE

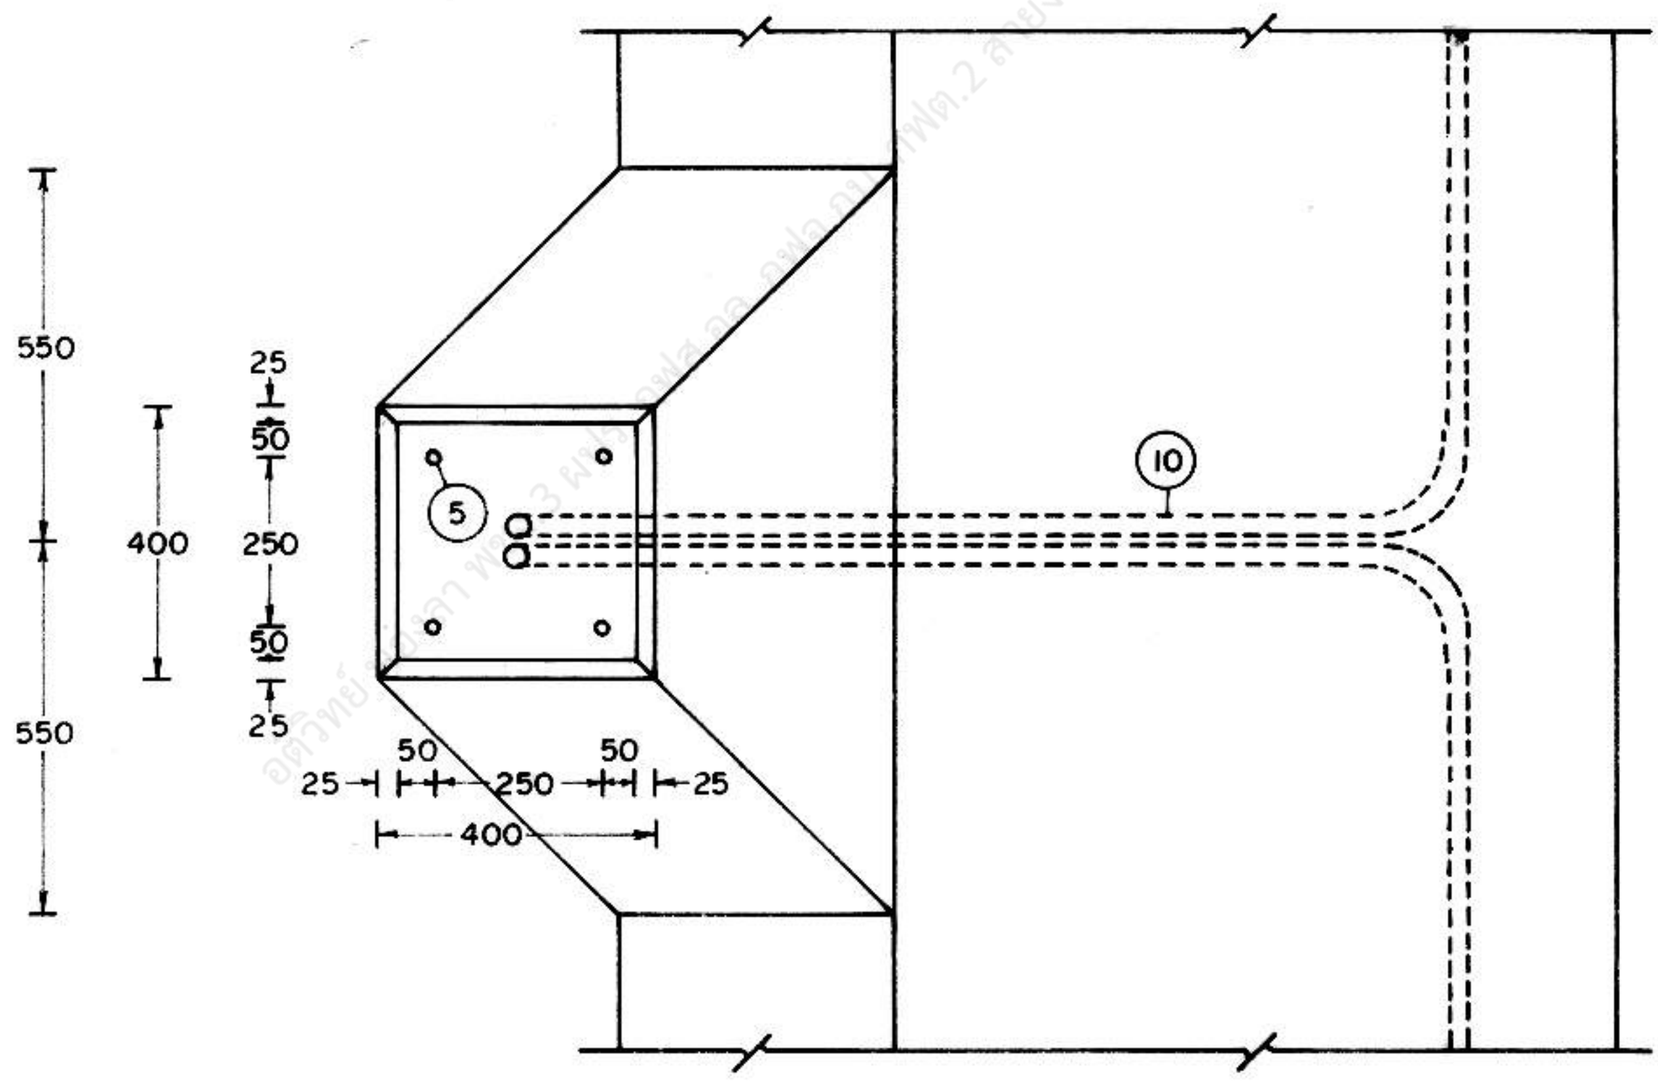

รายละเอียด A
DETIL A

กองวิศวกรรมไฟฟ้าและเครื่องกล ฝ่ายวิศวกรรม	การไฟฟ้าส่วนภูมิภาค	ใช้แทนแผน ถูกแทนโดยแผน
ผู้เขียน ผู้สำรวจ วิศวกร หัวหน้าแผนก หัวหน้ากอง ผู้อำนวยการฝ่าย	ผู้ว่าการ 8 เม.ย. 23	เขียนเสร็จวันที่ 15 ก.พ. 23 แก้แบบวันที่ มิติเป็น มม. มาตราส่วน 1 : 20
รองผู้ว่าการฝ่ายเทคนิค 6 เม.ย. 2523	การติดตั้งไฟฟ้าแสงสว่างบนสะพาน BRIDGE LIGHTING INSTALLATION	แผนเลขที่ SAI-015/23038 แผ่นที่ 2 ของจำนวน 3 แผ่น

การประกอบเลขที่ ASSEMBLY NO. 0809

บัญชีวัสดุ
BILL OF MATERIAL

ลำดับที่ ITEM	รายละเอียด DESCRIPTION	จำนวน REQ'D 1	2	3	วัสดุเลขที่ MAT. NO.
1 *	เสาไฟเหล็กทรงกระบอกปลายเรียว พร้อมกิ่งโคมไฟ และดวงโคม ขนาดความสูงตามกิ่งโคมไฟตามต้องการ (7.5-9 ม.) TAPERED STEEL LIGHTING POLE, COMPLETE WITH BRACKET AND LUMINAIRE, MOUNTING HEIGHT AS REQUIRED (7.5-9 m)	1	1	1	—
2a	แผ่นเหล็ก ขนาด 350 X 350 X 30 มม. STEEL, BASE PLATE, SIZE 350 X 350 X 30 mm	-	-	1	—
2b	จาจับเสาไฟฟ้าแสงสว่างยึดกับราวสะพาน FIXING OF LIGHTING POLE ON EXISTING BRIDGE	2	2	-	—
3	สลักเกลียว M 16 X 250 มม. BOLT, MACHINE, M 16 X 250 mm	8	8	-	01110203
4	สลักเกลียว M 16 X 50 มม. BOLT, MACHINE, M 16 X 50 mm	8	8	-	—
5	สลักเกลียวแบบก้านงอ M 24 X 650 มม. (1" Ø) BOLT, ANCHOR, M 24 X 650 mm (1" Ø)	-	-	4	—
6	สลักเกลียว AY ปลั๊ก (แบบเปลือกหอยมาน) ขนาดตามต้องการ BOLT, AY PLUG (EXPANSION SHIELD) SIZE AS REQUIRED	2	2	-	—
7	แหวนสปริง M 16 มอก. 259 WASHER, LOCK, M 16 TIS 259	32	32	-	01180301
8	แหวนสปริง M 24 มอก. 259 WASHER, LOCK, M 24 TIS 259	-	-	4	01180303
9	ท่ออ่อน (ตัดงอได้) สำหรับเดินสายไฟ ชนิดกันน้ำ ขนาดตามต้องการ FLEXIBLE CONDUIT, RAINTIGHT, SIZE AS REQUIRED			-	—
10	ท่อเหล็กสำหรับเดินสายไฟ ขนาดตามต้องการ RIGID STEEL CONDUIT, SIZE AS REQUIRED				—
11	ข้อต่อสำหรับท่ออ่อน (ในการเดินสายไฟ) ชนิดกันน้ำ ขนาดตามต้องการ CONNECTOR FOR FLEXIBLE CONDUIT, RAINTIGHT, SIZE AS REQUIRED	2	2	-	—
12	ข้อต่อสำหรับท่อเหล็ก (ในการเดินสายไฟ) ชนิดกันน้ำ ขนาดตามต้องการ CONNECTOR FOR RIGID STEEL CONDUIT, RAINTIGHT, SIZE AS REQUIRED	2	2	-	—
13	กล่องต่อสาย ขนาดตามต้องการ JUNCTION BOX, SIZE AS REQUIRED	1	1	-	—

* สำหรับแบบที่ 1 และแบบที่ 2 SERVICE DOOR ควรอยู่สูงจากฐานเสาไฟประมาณ 1-1.1 เมตร
FOR TYPE 1 AND TYPE 2 SERVICE DOOR SHOULD BE 1-1.1 METER ABOVE THE BASE OF POLE.

กองวิศวกรรมไฟฟ้าและเครื่องกล ฝ่ายวิศวกรรม	การไฟฟ้าส่วนภูมิภาค	ใช้แทนแบบ ถูกแทนโดยแบบ เขียนเสร็จวันที่ 15 ก.พ. 23 แก้แบบวันที่ มิติเป็น มาตราส่วน
ผู้เขียน ผู้สำรวจ วิศวกร หัวหน้าแผนก หัวหน้ากอง ผู้อำนวยการฝ่าย	ผู้ว่าการ 8 เม.ย. 23	
รองผู้ว่าการฝ่ายเทคนิค 4 เม.ย. 2523	การติดตั้งไฟฟ้าแสงสว่างบนสะพาน BRIDGE LIGHTING INSTALLATION	แบบเลขที่ SAI-015/23038 แผ่นที่ 3 ของจำนวน 3 แผ่น