

การประกอบเลขที่ ASSEMBLY NO. **3302**

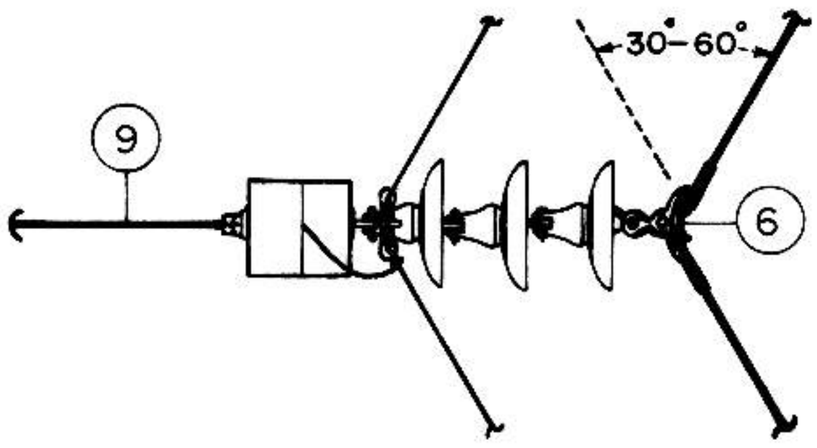

ดูข้อแนะนำในการก่อสร้างระบบจำหน่าย 1 เฟส 19 เควี แบบเลขที่ S02-015/20016

SEE CONSTRUCTION SUGGESTION OF 1-PHASE 19 kV SYSTEM DWG. NO. S02-015/20016

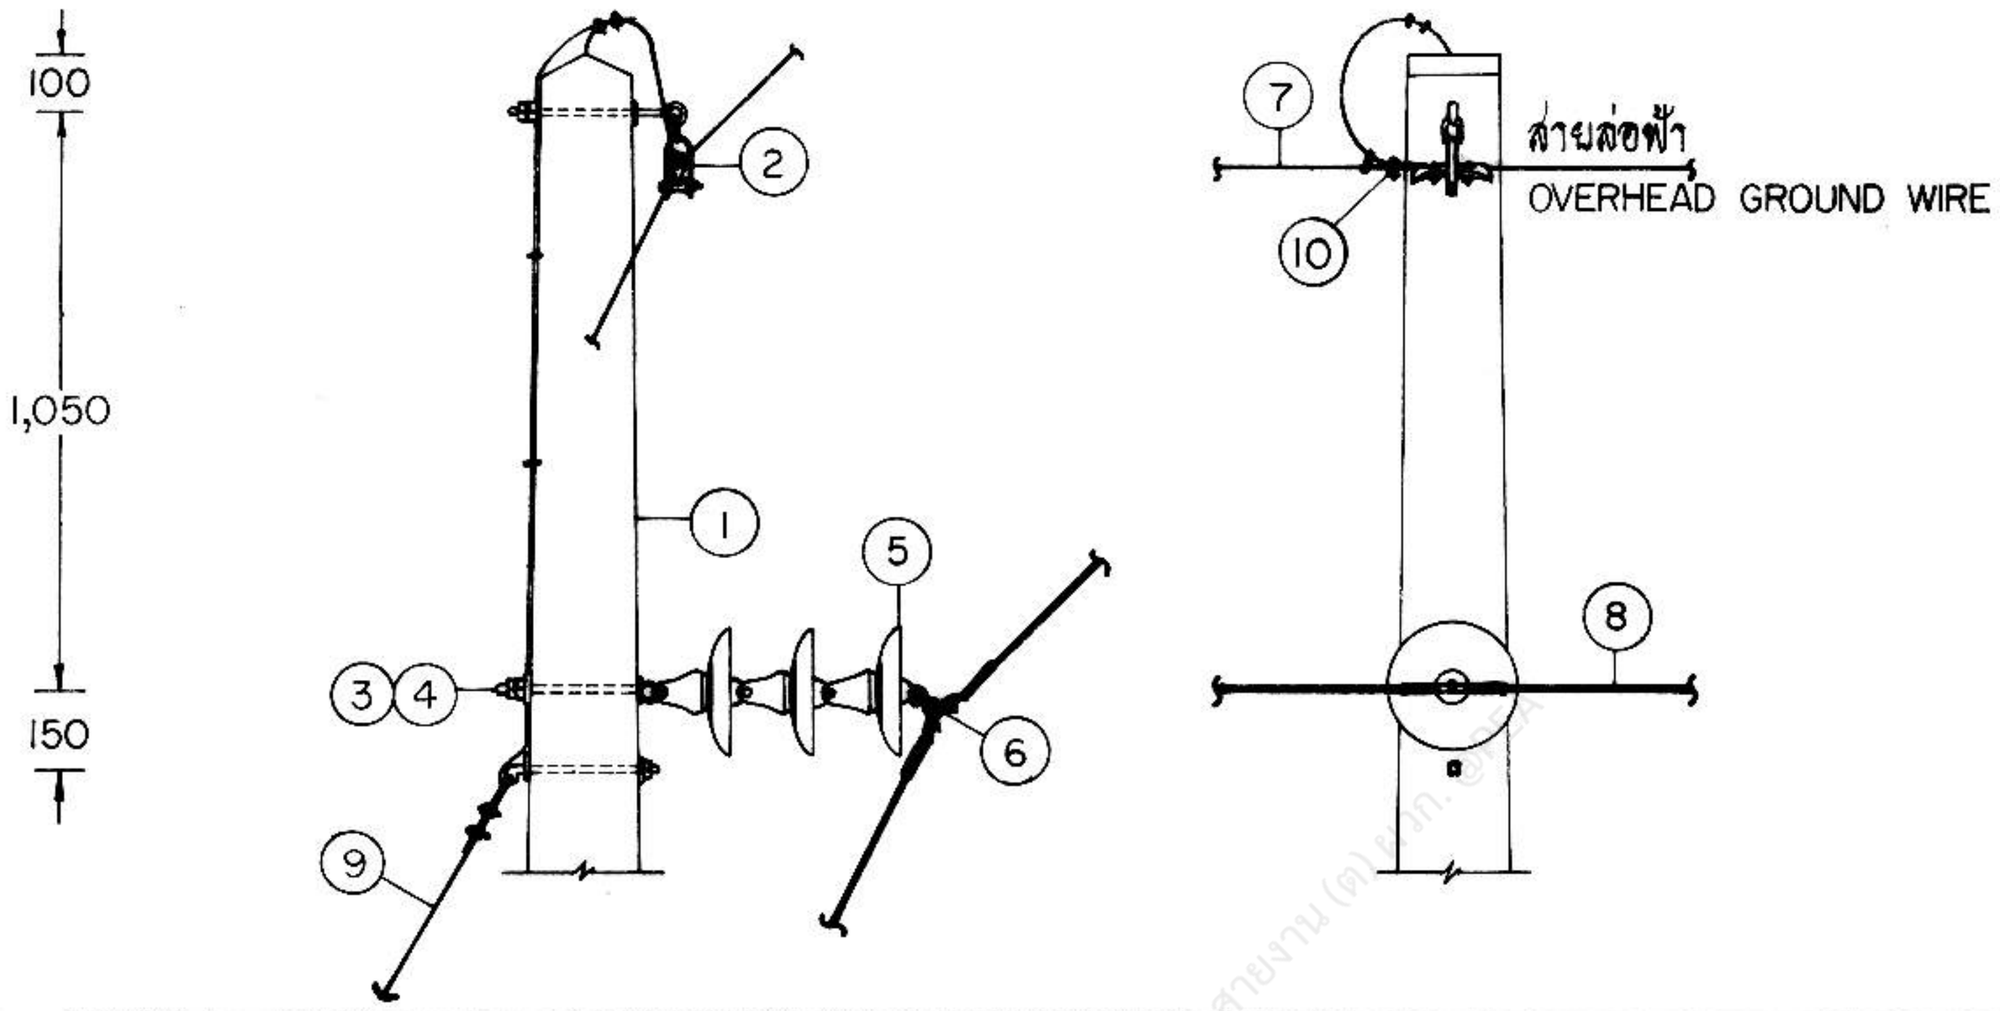

บัญชีวัสดุ
BILL OF MATERIAL

ลำดับที่ ITEM	รายละเอียด DESCRIPTION	จำนวน REQ'D	วัสดุเลขที่ MAT. NO.
1	เสาคอนกรีต ขนาด 12 ม. (สำหรับระบบ 33 kV) CONCRETE POLE 12 m LONG (FOR 33 kV SYSTEM)	1	00010004 (0034)
2	กราวด์วายร์แคล้มป์ สำหรับเสาคอนกรีต GROUND WIRE SUPPORT AND CLAMP, FOR CONCRETE POLE	1	01230201 (0298)
3	สลักห่วงกลม M 16 X 250 มม. BOLT, ROUND EYE M 16 X 250 mm	1	01140002 (0254)
4	แหวนสี่เหลี่ยมแผน 52X52X4.5 มม. รู Ø 18 มม. มอก. 258 WASHER, SQUARE, FLAT 52X52X4.5 mm HOLE Ø 18 mm TIS 258	2	01180100 (0355)
5	ลูกถ้วยแขวน มอก.354 แบบ ค (แบบ 52-4) INSULATOR, SUSPENSION TYPE, TIS 354 TYPE C (CLASS 52-4)	3	03020002 (0415)
6	ซัซเพนชั่นแคล้มป์ แบบเคลวิส์ อลูมิเนียม 35-70 ต.มม. CLAMP, SUSPENSION, CLEVIS TYPE, Al 35-70 mm^2	1	03120100 (0292)
7	ลวดเหล็กตีเกลียว 25 ต.มม. มอก. 404 WIRE, STEEL STRANDED 25 mm^2 TIS 404		01100002 (0181)
8	สายอะลูมิเนียมแกนเหล็ก หรือ อะลูมิเนียมอัลลอย 35-50 ต.มม. CONDUCTOR, ACSR OR ALUMINIUM-ALLOY 35-50 mm^2		02020001-2 02030001-2
9	สายยึดโยงระบบ 33 kV พร้อมสมอบกครบชุด GY-32 ANCHOR GUY FOR 33 kV SYSTEM GY-32	1	——
10	ยูแคล้มป์ สลัก 1 ตัว M 8 (ไวร์โรป คลิ๊ฟ) CLAMP, SINGLE U-BOLT, M 8 (WIRE ROPE CLIP)	2	01230000 (0165)

กองวิศวกรรม

ผู้เขียน
ผู้สำรวจ
วิศวกร
หัวหน้าแผนก
หัวหน้ากอง

รองผู้ว่าการฝ่ายเทคนิค

การไฟฟ้าส่วนภูมิภาค

ผู้ว่าการ

การประกอบลูกถ้วยแขวนกับเสาคอนกรีต
ระบบ 1 เฟส 19 kV
สำหรับทางโค้ง 30°-60°

SUSPENSION INSULATOR ASSEMBLY ON CONCRETE POLE
1-PHASE 19 kV SYSTEM
ANGLE STRUCTURE 30°-60°

ใช้แทนแบบ
ถูกแทนโดยแบบ
เขียนเสร็จวันที่ 23 ม.ค. 20
แก้แบบวันที่
มิติเป็น มม.
มาตราส่วน 1:25
แบบเลขที่ S02-015/20013
แผ่นที่ 1 ของจำนวน 1 แผ่น