การประกอบเลขที่
ASSEMBLY NO. **5205A**

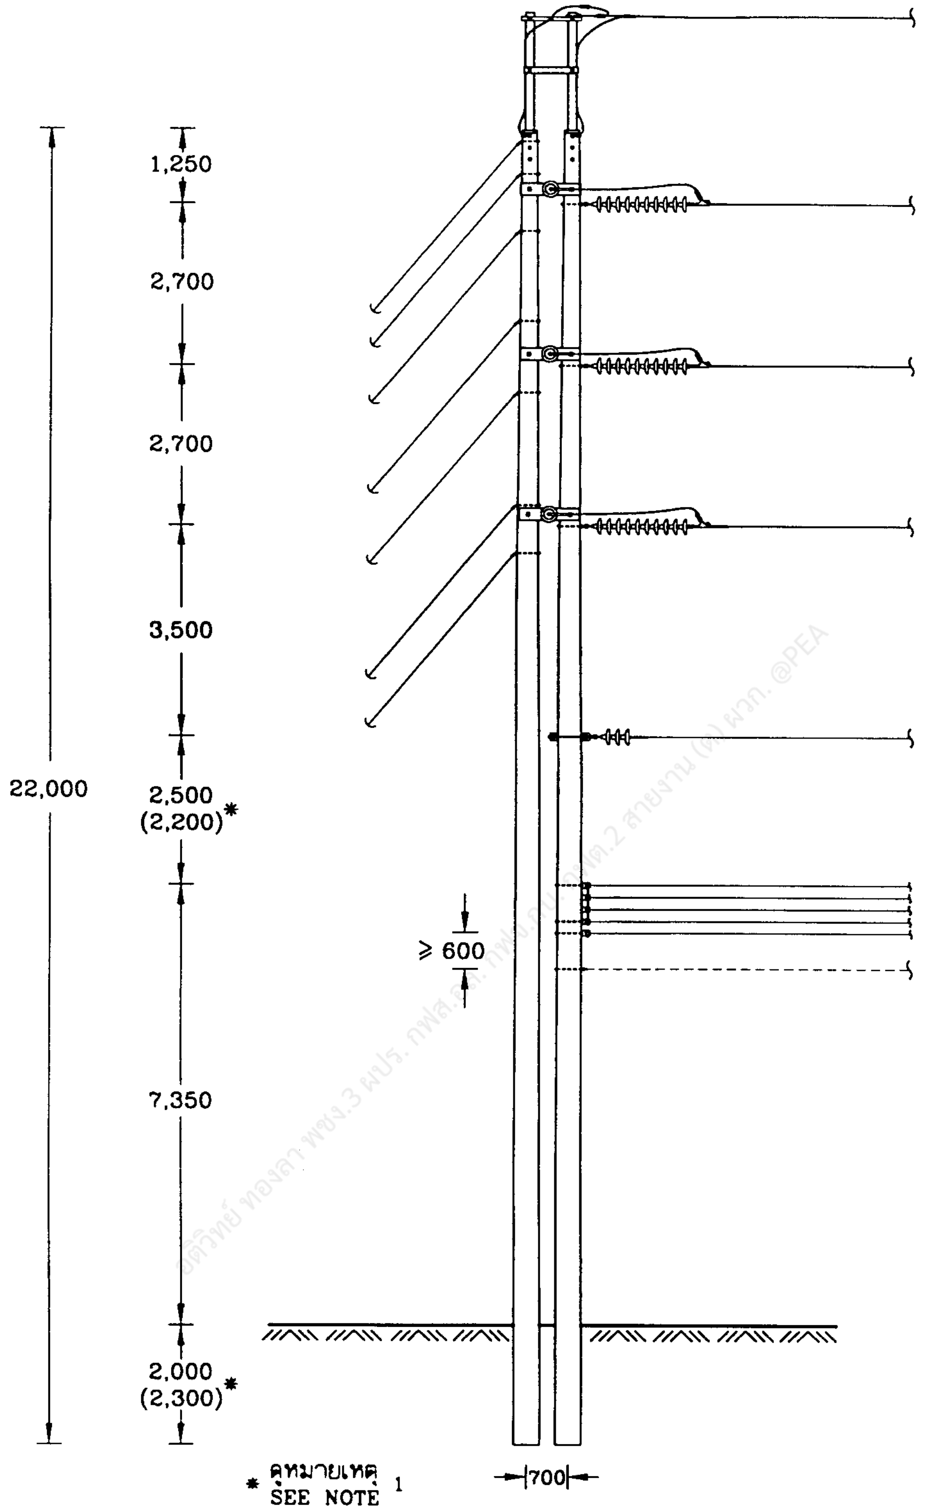

* ดูหมายเหตุ 1
SEE NOTE 1

อิศวิทย์ ทองลา พชง.3 ผปร. กฟส.อ. กฟน. ฝพต.2 สายงาน (ต) ผวก. @PEA

กองมาตรฐานระบบไฟฟ้า ฝ่ายมาตรฐานและความปลอดภัย	การไฟฟ้าส่วนภูมิภาค	ใช้แทนแบบ .... ถูกแทนโดยแบบ ....
ผู้เขียน ...สมชาย.......... ผู้สำรวจ .... วิศวกร .... หัวหน้าแผนก .... ผู้อำนวยการกอง .... ผู้อำนวยการฝ่าย	ผู้ว่าการ .... 115 kV วงจรเดี่ยว สายไฟฟ้าเดี่ยว 26 ก.ค. 2547 เสาคู่ (ชนิดมีกราวด์เพลทในเสา) สำหรับทางโค้ง 90° แบบ SS–LA–2	เขียนเสร็จวันที่ 2 มิ.ย. 2547 แก้แบบวันที่ .... มิติเป็น ..มิลลิเมตร....... มาตราส่วน ..1:125.......
รองผู้ว่าการฝ่ายวางแผนและพัฒนาระบบไฟฟ้า	115 kV SINGLE CIRCUIT SINGLE CONDUCTOR DOUBLE POLE (WITH GROUND PLATE IN POLE), 90° ANGLE STRUCTURE TYPE SS–LA–2	แบบเลขที่ SA1–015/47005 แผ่นที่ 1 ของจำนวน 4 แผ่น

2 6 ก.ค. 2547

การประกอบเลขที่ ASSEMBLY NO. 5205A

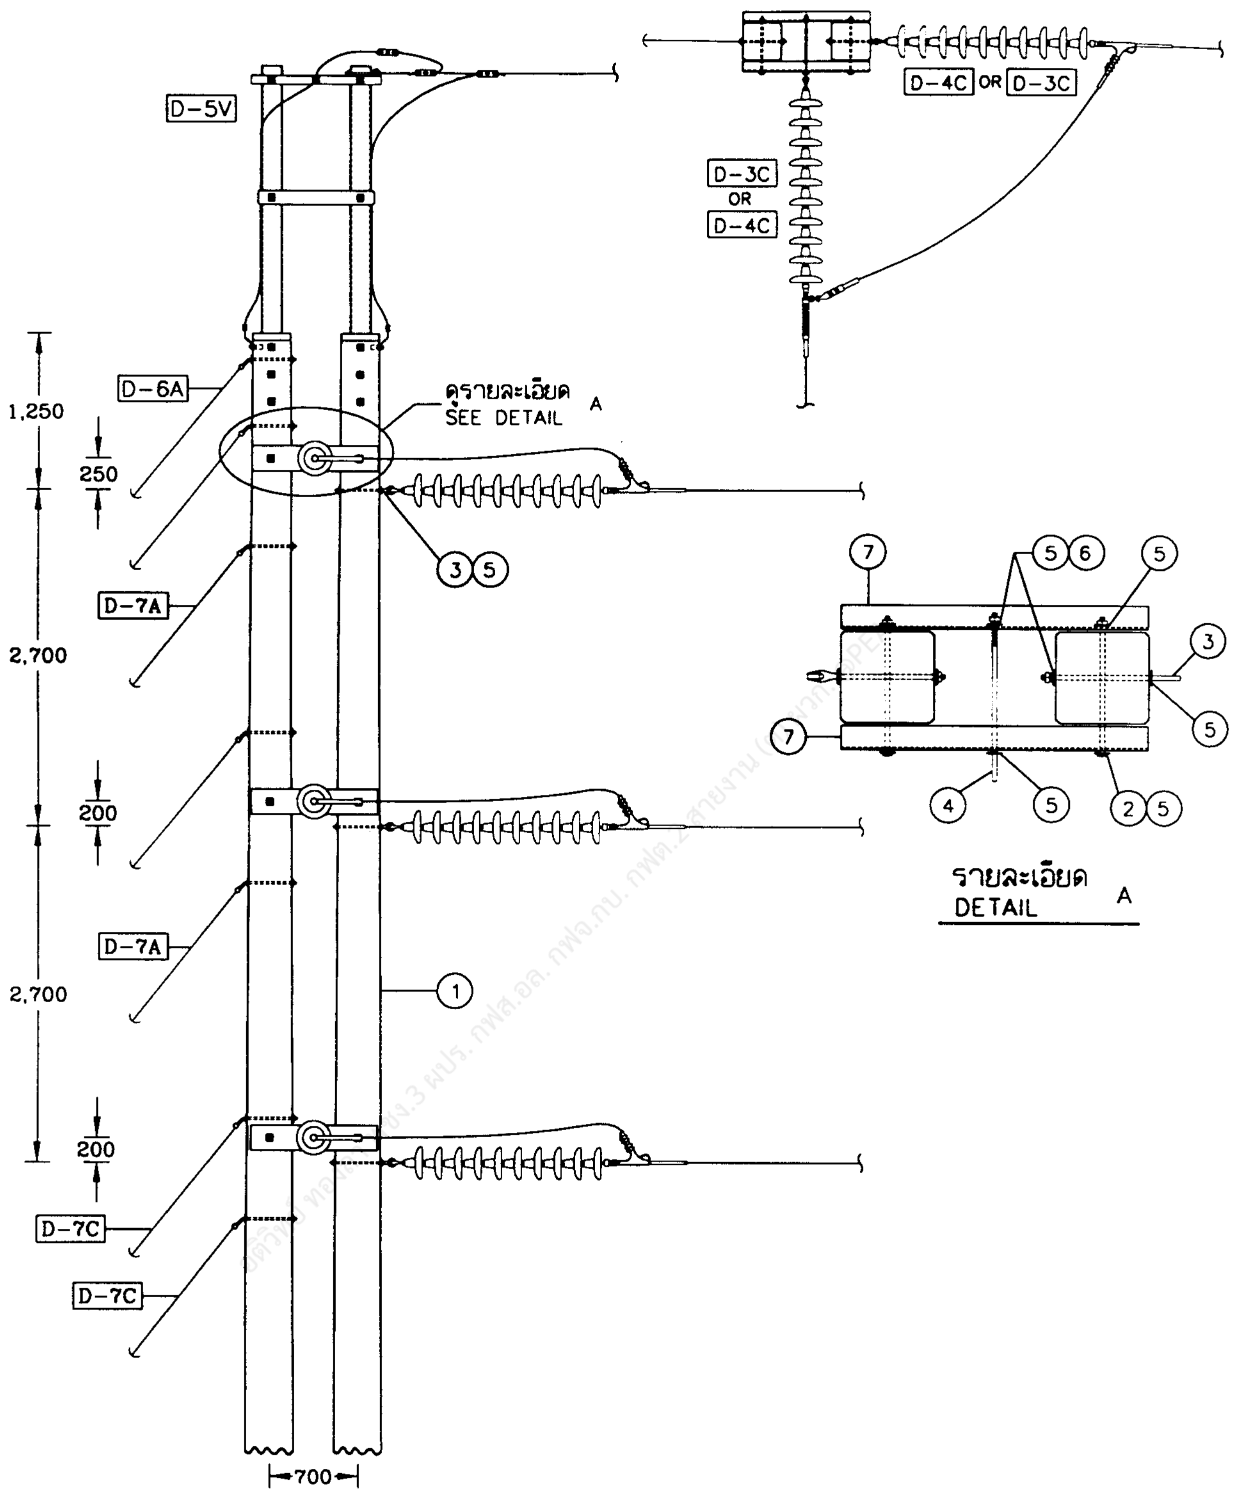

กองมาตรฐานระบบไฟฟ้า ฝ่ายมาตรฐานและความปลอดภัย	การไฟฟ้าส่วนภูมิภาค	ใช้แทนแบบ ....
ผู้เขียน ...สมชาย..........	ผู้ว่าการ........................	ถูกแทนโดยแบบ ....
ผู้สำรวจ....................		เขียนเสร็จวันที่ 2 มิ.ย. 2547
วิศวกร........	115 kV วงจรเดี่ยว สายไฟฟ้าเดี่ยว เสาคู่ (ชนิดมีกราวด์เพลทในเสา) สำหรับทางโค้ง 90 แบบ SS-LA-2	แก้แบบวันที่ ....
หัวหน้าแผนก........		มิติเป็น...มิลลิเมตร.......
ผู้อำนวยการกอง........		มาตราส่วน...1:60........
ผู้อำนวยการฝ่าย........		
รองผู้ว่าการฝ่ายวางแผนและพัฒนาระบบไฟฟ้า	115 kV SINGLE CIRCUIT SINGLE CONDUCTOR DOUBLE POLE (WITH GROUND PLATE IN POLE), 90° ANGLE STRUCTURE TYPE SS-LA-2	แบบเลขที่ SA1-015/47005 แผ่นที่ 2 ของจำนวน 4 แผ่น

26 ก.ค. 2547

26 ก.ค. 2547

การประกอบเลขที่
ASSEMBLY NO. 5205A

บัญชีวัสดุ
BILL OF MATERIAL

ลำดับที่ ITEM	รายละเอียด DESCRIPTION	จำนวน REQ.D	วัสดุเลขที่ MAT. NO.
1	เสา คอร. ยาว 22.00 ม. ชนิดมีกราวด์เพลทในเสา POLE, CONCRETE, 22.00 m LONG, WITH GROUND PLATE IN POLE	2	00010015
2	สลักเกลียว M 20x450 มม. BOLT, MACHINE, M 20x450 mm	6	01110302
3	สลักห่วงโอแวล M 20x350 มม. BOLT, OVAL EYE, M 20x350 mm	3	01150100
4	สลักห่วงโอแวล M 20x450 มม. BOLT, OVAL EYE, M 20x450 mm	3	01150101
5	แหวนสี่เหลี่ยมแบน 62x62x6 มม. รู ø22 มม. มอก.258 WASHER, SQUARE, FLAT 62x62x6 mm, HOLE ø22 mm, TIS 258	24	01180101
6	แหวนสปริง M 20 มอก. 259 WASHER, LOCK, M 20, TIS 259	6	01180302
7	เหล็กรูปรางน้ำ 200x80x7.5 มม. ยาว 1,000 มม. STEEL CHANNEL, 200x80x7.5 mm, 1,000 mm LONG	6	01000400

รายละเอียด
DETAIL

D-3C	การประกอบลูกถ้วยแขวน SUSPENSION INSULATOR ASSEMBLY	3	
D-4C	การประกอบลูกถ้วยแขวน SUSPENSION INSULATOR ASSEMBLY	3	
** D-5V	การประกอบสายล่อฟ้า OVERHEAD GROUND WIRE ASSEMBLY	1	
D-6A	การประกอบสายยึดโยงลวดเหล็กตีเกลียว 50 ต.มม. STEEL STRANDED WIRE 50 mm^2 GUY ASSEMBLY	1	
D-7A	การประกอบสายยึดโยงลวดเหล็กตีเกลียว 95 ต.มม. STEEL STRANDED WIRE 95 mm^2 GUY ASSEMBLY	4	
D-7C	การประกอบสายยึดโยงลวดเหล็กตีเกลียว 95 ต.มม. STEEL STRANDED WIRE 95 mm^2 GUY ASSEMBLY	2	
D-9A	สมอบกคอนกรีต CONCRETE ANCHOR	1	
D-10B	ฐานรากเสา POLE FOUNDATION	1	
D-25	การต่อลงดิน GROUNDING	1	

©PEA

กองมาตรฐานระบบไฟฟ้า
ฝ่ายมาตรฐานและความปลอดภัย

การไฟฟ้าส่วนภูมิภาค

ใช้แทนแบบ ....
ถูกแทนโดยแบบ ....

ผู้เขียน ...สมชาย...........
ผู้สำรวจ ....
วิศวกร ....
หัวหน้าแผนก ....
ผู้อำนวยการกอง ....
ผู้อำนวยการฝ่าย ....

ผู้ว่าการ ....

เขียนเสร็จวันที่ 2 มิ.ย. 2547
แก้แบบวันที่ ....
มิติเป็น ....
มาตราส่วน ....

115 kV วงจรเดี่ยว สายไฟฟ้าเดี่ยว
เสาคู่ (ชนิดมีกราวด์เพลทในเสา) สำหรับทางโค้ง 90°
แบบ SS-LA-2

26 ก.ค. 2547

รองผู้ว่าการฝ่ายวางแผนและพัฒนาระบบไฟฟ้า
....

115 kV SINGLE CIRCUIT SINGLE CONDUCTOR
DOUBLE POLE (WITH GROUND PLATE IN POLE), 90° ANGLE STRUCTURE
TYPE SS-LA-2

แบบเลขที่ SA1-015/47005
แผ่นที่ 3 ของจำนวน 4 แผ่น

26 ก.ค. 2547

การประกอบเลขที่
ASSEMBLY NO. 5205A

หมายเหตุ

1.* กรณีก่อสร้างในพื้นที่เขตทางหลวง ให้ใช้ค่าระยะห่างตามแนวดิ่งในวงเล็บ โดยดูรายละเอียดเพิ่มเติมในแบบเลขที่ SA1-015/43012 (การประกอบเลขที่ 5687)
2.** กรณีไม่มีสายยึดโยง ให้ใช้การประกอบสายล่อฟ้า แบบ D-5U แทน
3. ระยะห่างระหว่างช่วงเสาของโครงสร้างสายส่ง 115 kV โครงสร้างเสาสำหรับทางโค้ง 90° ให้ดูแบบเลขที่ SA1-015/47009 (การประกอบเลขที่ 5161)

NOTES

1.* IN CASE OF CONSTRUCTION IN HIGHWAY AREA, USE A VERTICAL CLEARANCE VALUE IN THE PARENTHESIS, FOR ADDITIONAL DETAIL, SEE DWG NO. SA1-015/43012 (ASSEMBLY NO. 5687) .
2.** IN CASE OF NO GUY, USE OVERHEAD GROUND WIRE ASSEMBLY TYPE D-5U .
3. SPAN LENGTHS FOR 115 kV CONSTRUCTION STRUCTURE, 90° ANGLE STRUCTURE, SEE DWG. NO. SA1-015/47009 (ASSEMBLY NO. 5161) .

อติวิทย์ ทองลา พชง.3 ผปร. กฟส.อล. กฟจ.กบ. กฟฉ.2 สายงาน (ต) ผวก. @PEA

กองมาตรฐานระบบไฟฟ้า
ฝ่ายมาตรฐานและความปลอดภัย

การไฟฟ้าส่วนภูมิภาค

ใช้แทนแบบ ....
ถูกแทนโดยแบบ ....

ผู้เขียน ...สมชาย...........
ผู้สำรวจ...................
วิศวกร...................
หัวหน้าแผนก...................
ผู้อำนวยการกอง...................
ผู้อำนวยการฝ่าย...................

ผู้ว่าการ..................................

เขียนเสร็จวันที่ 2 มิ.ย. 2547
แก้แบบวันที่ ....
มิติเป็น...................
มาตราส่วน...............

115 kV วงจรเดี่ยว สายไฟฟ้าเดี่ยว
เสาคู่ (ชนิดมีกราวด์เพลทในเสา) สำหรับทางโค้ง 90°
แบบ SS-LA-2

26 ก.ค. 2547

รองผู้ว่าการฝ่ายวางแผนและพัฒนาระบบไฟฟ้า
....

115 kV SINGLE CIRCUIT SINGLE CONDUCTOR
DOUBLE POLE (WITH GROUND PLATE IN POLE), 90° ANGLE STRUCTURE
TYPE SS-LA-2

แบบเลขที่ SA1-015/47005
แผ่นที่ 4 ของจำนวน 4 แผ่น

26 ก.ค. 2547