

การประกอบเลขที่ ASSEMBLY NO. 3303

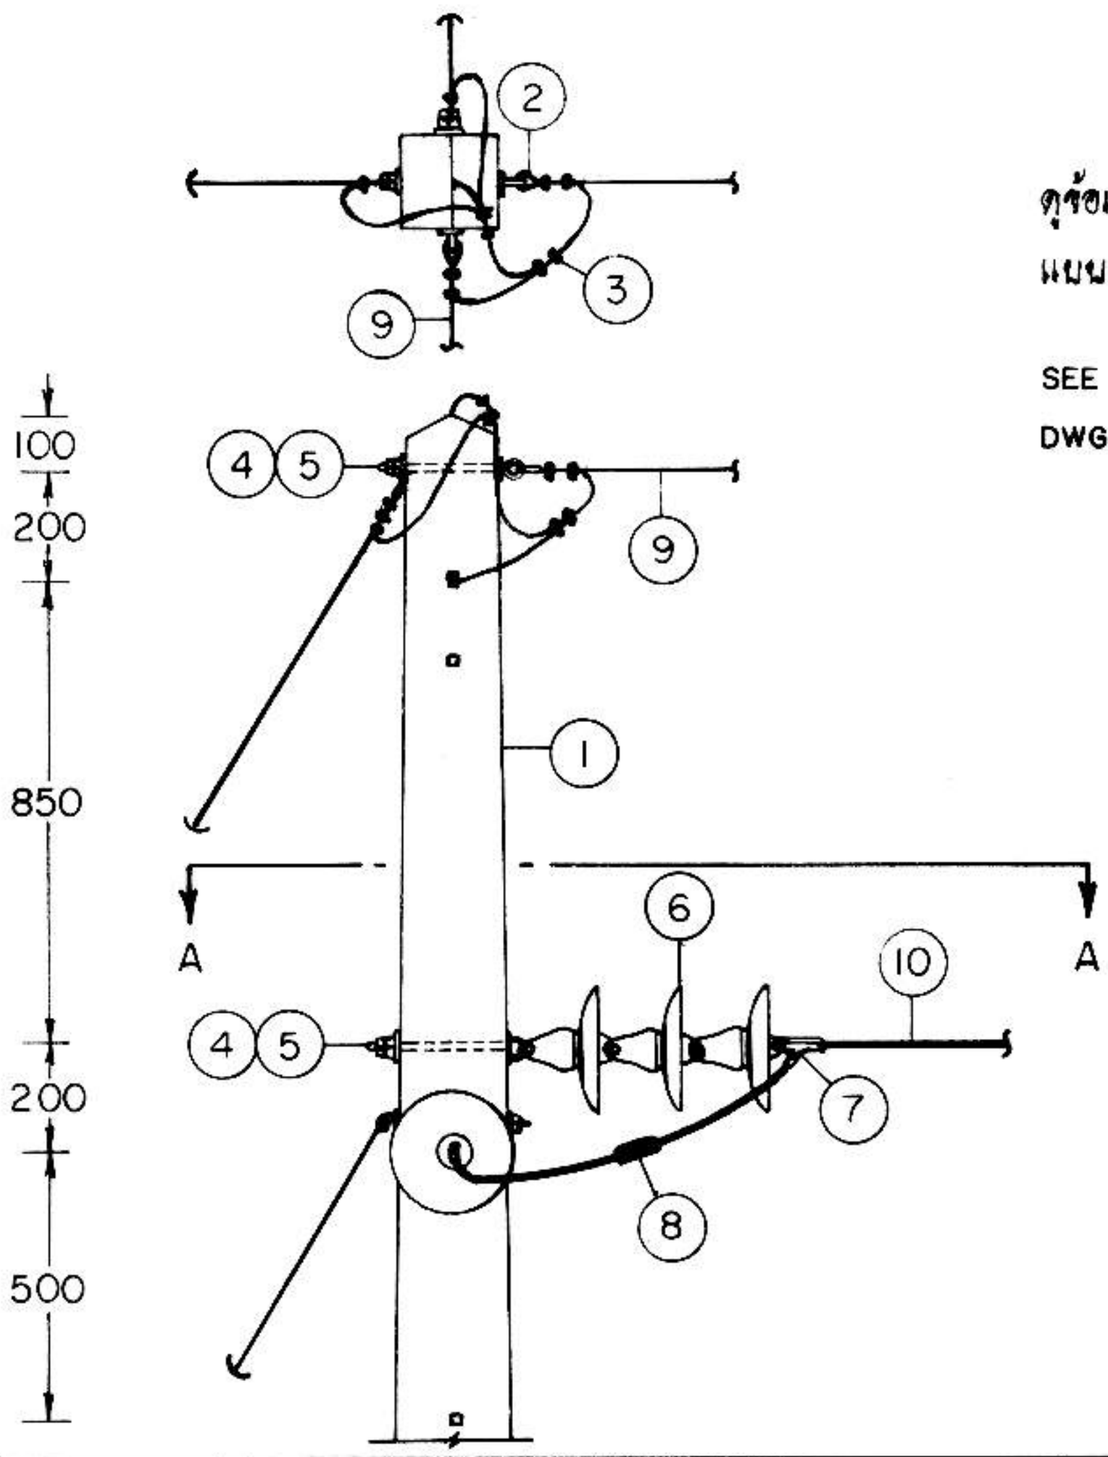

ดูข้อแนะนำในการก่อสร้างระบบจำหน่าย 1 เฟส 19 kV แบบเลขที่ S 02-015/20016

SEE CONSTRUCTION SUGGESTION OF 1-PHASE 19 kV SYSTEM DWG. NO. S02-015/20016

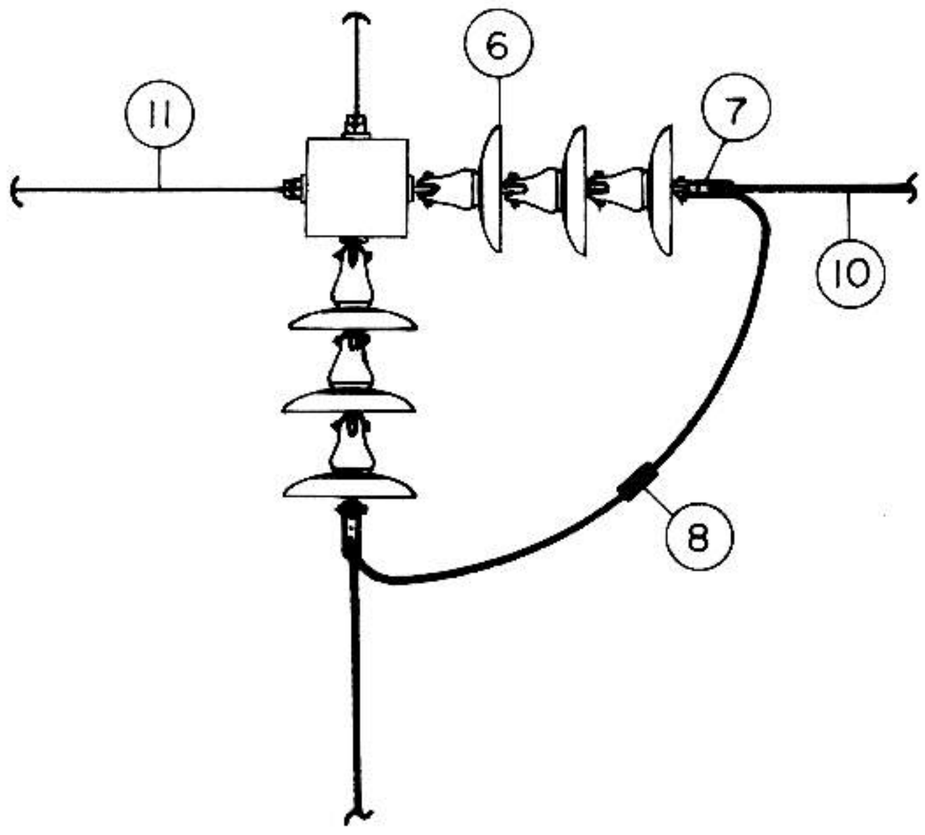

รูปตัด SECTION A-A

บัญชีวัสดุ BILL OF MATERIAL

ลำดับที่ ITEM	รายละเอียด DESCRIPTION	จำนวน REQ'D	วัสดุเลขที่ MAT. NO.
1	เสาคอนกรีต ขนาด 12 ม. (สำหรับระบบ 33 kV) CONCRETE POLE 12 m LONG (FOR 33 kV SYSTEM)	1	00010004 (0034)
2	กายทิมเบิ้ล สำหรับสายยึดโยงขนาด 50-95 ต.มม. THIMBLE, GUY, FOR STEEL WIRE 50-95 mm^2	2	01210304 (0150)
3	ยูแคล้มป์ สลัก 1 ตัว M 8 (ไวร์ โร้ป คลิ๊ฟ) CLAMP, SINGLE U-BOLT, M 8 (WIRE ROPE CLIP)	6	01230000 (0165)
4	สลักห่วงกลม M 16 X 250 มม. BOLT, ROUND EYE M 16 X 250 mm	4	01140002 (0254)
5	แหวนสี่เหลี่ยมแผ่น 52X52X4.5 มม. รู Ø 18 มม. มอก. 258 WASHER, SQUARE, FLAT 52X52X4.5 mm HOLE Ø 18 mm TIS 258	8	01180100 (0355)
6	ลูกถ้วยแขวน มอก.354 แบบ ง (แบบ 52-4) INSULATOR, SUSPENSION TYPE, TIS 354 TYPE D (CLASS 52-4)	6	03020002 (0415)
7	สเตรนแคล้มป์ สำหรับสายอะลูมิเนียม 35-70 ต.มม. อะลูมิเนียมแกนเหล็ก 35-50 ต.มม. CLAMP, STRAIN FOR Al 35-70 mm^2, ACSR 35-50 mm^2	2	03110000 or 03110100
8	หลอดต่อสายชนิดบีบไม่รับแรงดึง สายอะลูมิเนียม 35-50 ต.มม. อะลูมิเนียมแกนเหล็ก 35-50 ต.มม. CONNECTOR, SPLICE, COMPRESSION TYPE, TENSIONLESS Al 35-50 mm^2, ACSR 35-50 mm^2	1	02410001-2 02410101-2
9	ลวดเหล็กตีเกลียว 25 ต.มม. มอก. 404 WIRE, STEEL STRANDED 25 mm^2 TIS 404		01100002 (0181)
10	สายอะลูมิเนียมแกนเหล็ก หรือ อะลูมิเนียมอัลลอย 35-50 ต.มม. CONDUCTOR, ACSR OR ALUMINIUM-ALLOY 35-50 mm^2		02020001-2 or 02030001-2
11	สายยึดโยงระบบ 33 kV พร้อมสมอมกคว้านชุด GY-33 ANCHOR GUY FOR 33 kV SYSTEM GY-33	2	—

กองวิศวกรรม

ผู้เขียน
ผู้สำรวจ
วิศวกร
หัวหน้าแผนก
หัวหน้ากอง

รองผู้ว่าการฝ่ายเทคนิค

การไฟฟ้าส่วนภูมิภาค

ผู้ว่าการ

การประกอบลูกถ้วยแขวนกับเสาคอนกรีต
ระบบ 1 เฟส 19 kV
สำหรับทางโค้ง 60°-90°

SUSPENSION INSULATOR ASSEMBLY ON CONCRETE POLE
1-PHASE 19 kV SYSTEM
ANGLE STRUCTURE 60°-90°

ใช้แทนแบบ
ถูกแทนโดยแบบ
เขียนเสร็จวันที่ 23 ม.ค. 20
แก้แบบวันที่
มิติเป็น มม.
มาตราส่วน 1 : 25
แบบเลขที่ S 02-015/20014
แผ่นที่ 1 ของจำนวน 1 แผ่น