

การประกอบแบบที่ ASSEMBLY NO.	5275

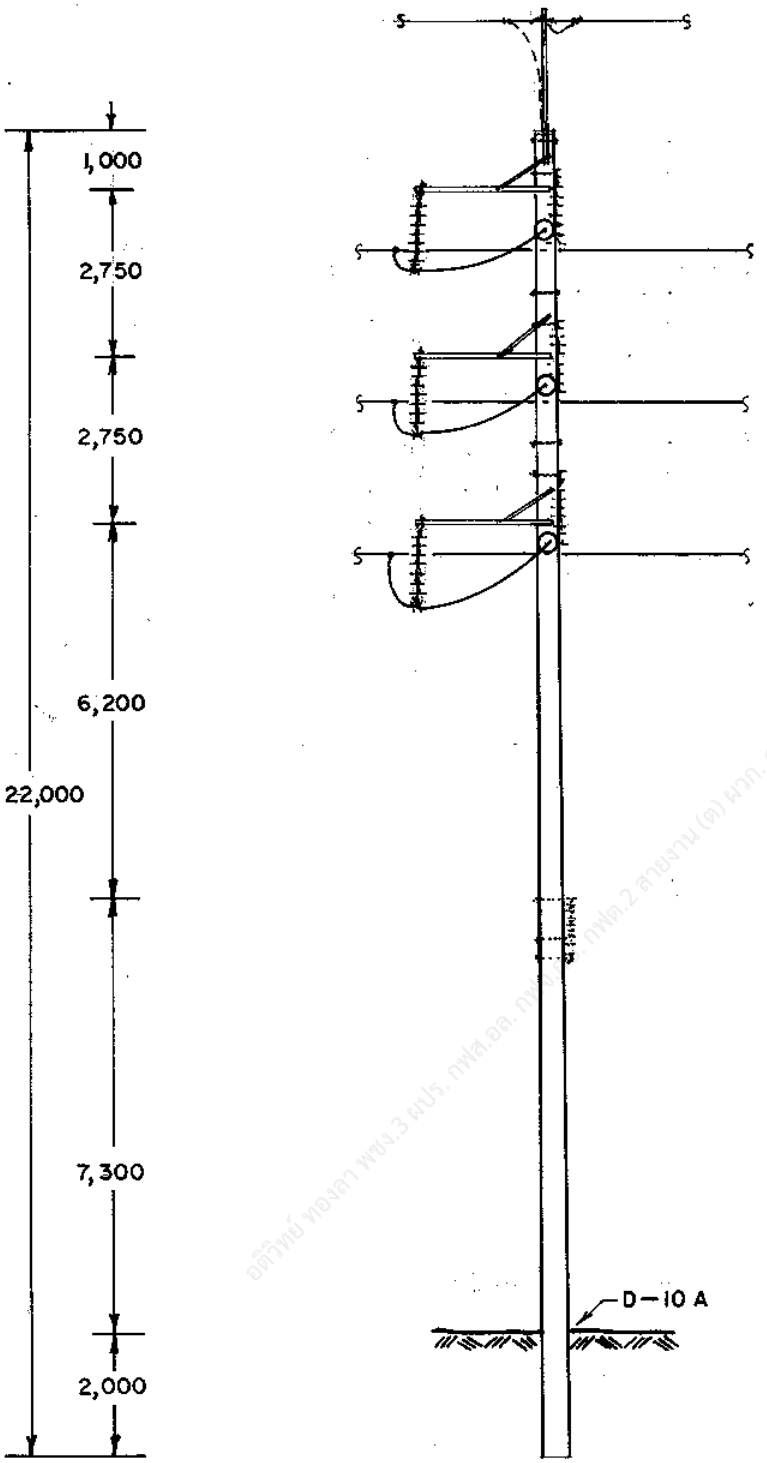

กองวิศวกรรมไฟฟ้าและเครื่องกล ฝ่ายวิศวกรรม	การไฟฟ้าส่วนภูมิภาค	ใช้แทนแบบ ถูกแทนโดยแบบ
ผู้เขียน ผู้ตรวจ วิศวกร หัวหน้าแผนก ผู้อำนวยการกอง ผู้อำนวยการฝ่าย	ผู้ว่าการ 115 kV วงจรเดี่ยว สายไฟฟ้าคู่ เสาต้นต่อแยกสาย แบบ SD-TL-4	เขียนเสร็จวันที่ 21 พ.ค. 40 แก้แบบวันที่ ตีเป็น มิลลิเมตร มาตราส่วน 1 : 125
รองผู้จ่าการเทคนิคและบริการ	115 kV SINGLE CIRCUIT DOUBLE CONDUCTOR FOR TAP LINE STRUCTURE TYPE SD-TL-4	แบบมาตรฐานที่ SAI-015/40014 แผ่นที่ 1 ของจำนวน 4 แผ่น

4 ส.ค. 2540

การประกอบลำดับที่ ASSEMBLY NO. 5275

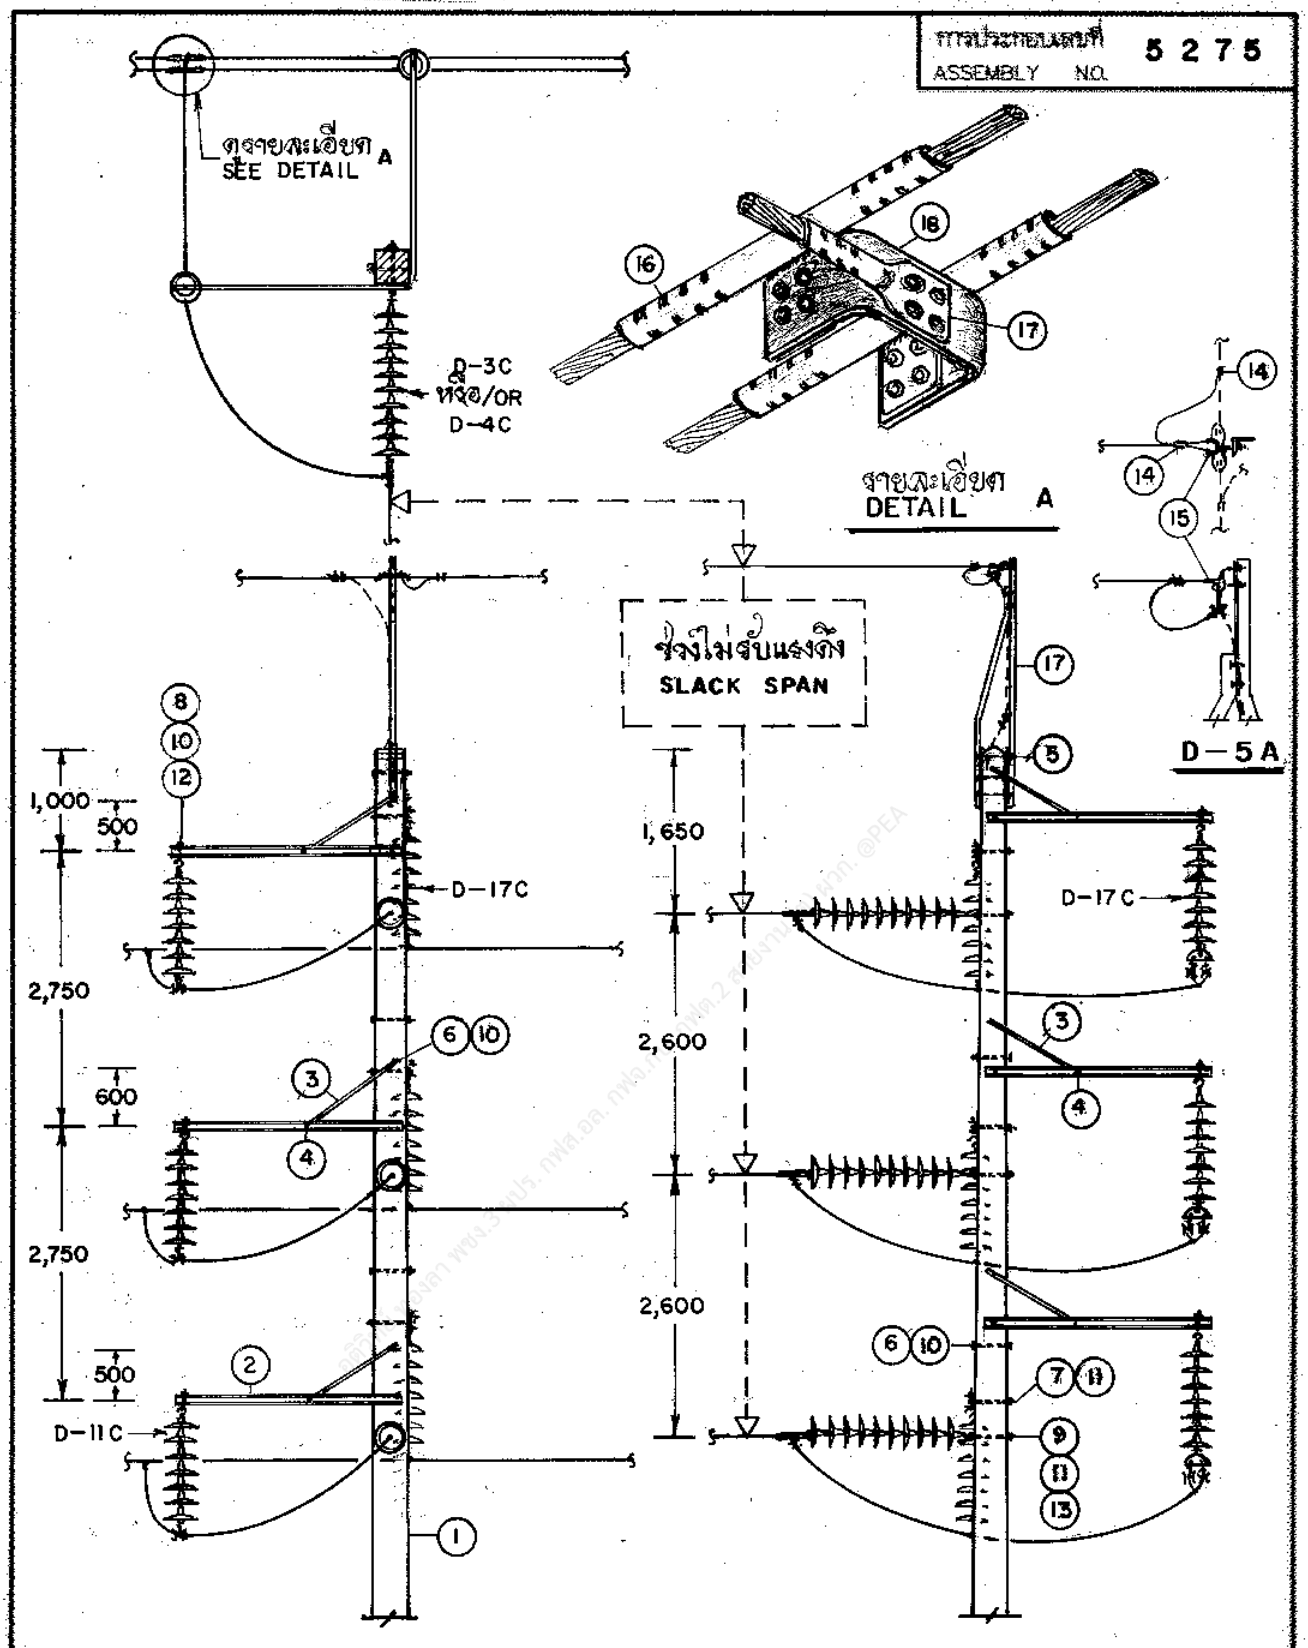

กองวิศวกรรมไฟฟ้าและเครื่องกล ฝ่ายวิศวกรรม	การไฟฟ้าส่วนภูมิภาค	ใช้แทนแบบ ถูกแทนโดยแบบ
ผู้เขียน ผู้ตรวจ วิศวกร หัวหน้าแผนก ผู้อำนวยการกอง ผู้อำนวยการฝ่าย	ผู้ว่าการ 4 ส.ค. 2540 115 kV วงจรเดี่ยว สายไฟฟ้าดู เสาต้นจ่อแยกสาย แบบ SD-TL-4	เขียนเสร็จวันที่ 21 พ.ค. 40 แก้แบบวันที่ รับเป็น มิลลิเมตร มาตราส่วน 1:75
รองผู้ว่าการวิศวกรรมและบริการ 4 ส.ค. 2540	115 kV SINGLE CIRCUIT DOUBLE CONDUCTOR FOR TAP LINE STRUCTURE TYPE SD-TL-4	แบบเลขที่ SAI-015/40014 แผ่นที่ 2 ของจำนวน 4 แผ่น

การประกอบเลขที่ ASSEMBLY NO. **5275**

บัญชีวัสดุ
BILL OF MATERIAL

ลำดับที่ ITEM	รายละเอียด DESCRIPTION	จำนวน/REQ'D I	II	วัสดุเลขที่ MAT. NO.
1	เสาคอนกรีต 22.0 ม. POLE, CONCRETE, 22.0 M LONG	1	–	00010011
2	คอนเหล็กแบบท้าวแขน ขนาด [100x50x5 มม. ยาว 2.25 ม. มอก.116 STEEL, ALLEY ARM, [100x50x5 mm, 2.25 M LONG, TIS 116	3	3	01000100
3	เหล็กประกับไม้คอน ขนาด 40x6 มม. ยาว 1,000 มม. BRACE, FLAT, FOR CROSSARM 40x6x1,000 mm	3	3	01200002
4	สลักเกลียวหัวหกเหลี่ยม M 16x75 มม. พร้อมแหวน BOLT, MACHINE, HEXAGON, M 16x75 mm COMP. WITH WASHER	3	3	01110400
5	สลักเกลียว M 16x300 มม. BOLT, MACHINE, M 16x300 mm	1	3	01110204
6	สลักเกลียว M 16x350 มม. BOLT, MACHINE, M 16x350 mm	2	2	01110205
7	สลักเกลียว M 20x350 มม. BOLT, MACHINE, M 20x350 mm	3	3	01110300
8	สลักห่วงโอเวล M 16x150 มม. BOLT, OVAL EYE, M 16x150 mm	3	3	01150000
9	สลักห่วงโอเวล M 20x350 มม. BOLT, OVAL EYE, M 20x350 mm	–	3	01150100
10	แหวนรองแบนเรียบ ประเภทจัตุรัสขนาดใหญ่ 52x52x4.5 มม. เส้นผ่านศูนย์กลางรู 18 มม. มอก.258 WASHER, PLAIN, SQUARE, LARGE 52x52x4.5 mm HOLE DIA. 18 mm TIS 258	9	9	01180100
11	แหวนรองแบนเรียบ ประเภทจัตุรัสขนาดใหญ่ 62x62x6 มม. เส้นผ่านศูนย์กลางรู 22 มม. มอก.258 WASHER, PLAIN, SQUARE, LARGE 62x62x6 mm HOLE DIA. 22 mm TIS 258	3	3	01180101
12	แหวนสปริง M 16 มอก. 259 WASHER, LOCK, M 16 TIS 259	3	3	01180301
13	แหวนสปริง M 20 มอก. 259 WASHER, LOCK, M 20 TIS 259	–	3	01180302
14	แคล้มป์โบ้สลัก 3 ตัว สำหรับลวดเหล็กตีเกลียว 35 ต.มม. CLAMP, TRIPLE BOLTS, FOR STEEL STRANDED WIRE 35 Sq.mm	–	2	01180303
15	กายทิมเบิล สำหรับลวดเหล็ก 35-50 ต.มม. หรือ 50-95 ต.มม. THIMBLE,GUY, FOR STEEL WIRE 35-50 Sq.mm OR 50-95 Sq.mm	–	2	หรือ 01210303 OR 01210304
16	คอนเนคเตอร์แบบ T ชนิดบีบ สำหรับสายอะลูมิเนียม 400 ต.มม. กับแผ่นรองชนิด 4 รู CONNECTOR, 2-PIECE COMPRESSION, T-TAP FOR AL CONDUCTOR 400 Sq.mm AND 4 HOLE NEMA PAD TAP	–	6	02500100
17	หางปลา เจาะรู 4 รู ตามมาตรฐาน NEMA สำหรับสายอะลูมิเนียม 400 ต.มม. TERMINAL, COMPRESSION, STRAIGHT PAD, NEMA 4-HOLE, FOR AL 400 Sq.mm	–	3	02420201
18	แผ่นอะลูมิเนียมรูปตัว U สำหรับต่อเชื่อมพร้อมสลักเกลียวและแหวน ALUMINIUM PAD COUPLER, U-SHAPE COMP. WITH BOLTS AND WASHERS	–	3	–
19	เหล็กฉากรับสายล่อฟ้าทางโค้ง 65 x 65 x 6 มม. ยาว 2,500 มม. STEEL ANGLE, OVERHEAD GROUND WIRE CORNER BAYONET 65x65x6 mm 2,500 mm LOHG	–	1	01180003

กองวิศวกรรมไฟฟ้าและเครื่องกล
ฝ่ายวิศวกรรม

การไฟฟ้าส่วนภูมิภาค

ผู้เขียน ..สมนึก สาครฯ.....
ผู้สำรวจ .....
วิศวกร .....
หัวหน้าแผนก .....
ผู้อำนวยการกอง .....
ผู้อำนวยการฝ่าย .....

ผู้ว่าการ .....
4 ส.ค. 2540

115 kV วงจรเดียว สายไฟฟ้าคู่
เสาต้นต่อแยกสาย
แบบ SD-TL-4

รองผู้ว่าการเทคนิคและบริการ
.....

115 kV SINGLE CIRCUIT DOUBLE CONDUCTOR
FOR TAP LINE STRUCTURE
TYPE SD-TL-4

ใช้แทนแบบ .....
ถูกแทนโดยแบบ .....
เขียนแล้วเสร็จวันที่ ..21. พค. 40..
แก้แบบวันที่ .....
มิติเป็น .....
มาตราส่วน .....

แบบเลขที่ SA1-015/40014
แผ่นที่ 3 ของจำนวน 4 แผ่น

4 ส.ค. 2540

การประกอบเลขที่ ASSEMBLY NO. 5275

ลำดับที่ ITEM	รายละเอียด DETAIL	จำนวน/REQ'D I	จำนวน/REQ'D II	
D-5A	การต่อสายล่อฟ้า OVERHEAD GROUND WIRE CONNECTION	–	1	
D-10A	ฐานรากเสา POLE FOUNDATION	1	–	
D-3C หรือ/OR D-4C	การประกอบลูกถ้วยแขวน SUSPENSION INSULATOR ASSEMBLY	–	3	
D-11C	การประกอบลูกถ้วยแขวน SUSPENSION INSULATOR ASSEMBLY	–	3	
D-17C	การประกอบลูกถ้วยแขวน SUSPENSION INSULATOR ASSEMBLY	3	–	

I. สำหรับโครงสร้างรับสายเมนไนไลน์
FOR MAIN LINE SUPPORTING STRUCTURE

II. สำหรับการต่อแยกสาย
FOR TAP LINE

หมายเหตุ 1. หากไนไลน์มีโครงสร้างเสารับสายเมนอยู่แล้วให้ใช้บัญชีวัสดุช่อง II เท่านั้น และมีการเปลี่ยนแปลงรายการตามตาราง A .
2. หากสายต่อแยกเป็นสายไฟฟ้าคู่ ให้เปลี่ยนแปลงตามตาราง B .

NOTES 1. IF IT HAD THE EXISTING POLE IN MAIN LINE, USED BILL OF MATERIAL IN REQ'D COLUMN II ONLY . AND SOME ITEMS SHALL BE CHANGED AS TABLE A .
2. IF TAP LINE IS DOUBLE CONDUCTOR, SOME ITEMS SHALL BE CHANGED AS TABLE B .

ตาราง TABLE A

เสาที่มีอยู่ EXISTING POLE	การเปลี่ยนแปลง /CHANGE: ยกเลิก /CANCEL	การเปลี่ยนแปลง /CHANGE: ลดจำนวน /REDUCE	หมายเหตุ NOTE
ทางตรง /TANGENT TG	–	รายการที่ 5 ITEM 3 ชุด SETS เหลือ TO 1 ชุด SETS	รื้อถอนเหล็กรับสายล่อฟ้าทางตรง (01010004) REMOVE OVERHEAD GROUND WIRE BAYONET (01010004)
ทางโค้ง /ANGLE SA	รายการที่ 5,19 ITEM	–	–

ตาราง TABLE B

	การเปลี่ยนแปลง /CHANGE: จาก /FROM	การเปลี่ยนแปลง /CHANGE: เป็น /TO	หมายเหตุ NOTE
ชุดประกอบลูกถ้วย INSULATOR ASSEMBLY	D-3C หรือ D-4C OR	D-13C หรือ D-14C OR	–
	D-11C	D-17C	–
รายการที่ 17 ITEM	3 ชุด SETS	6 ชุด SETS	–
รายการที่ 18 ITEM	3 ชุด SETS	–	–

กองวิศวกรรมไฟฟ้าและเครื่องกล ฝ่ายวิศวกรรม	การไฟฟ้าส่วนภูมิภาค	ใช้แทนแบบ .....
ผู้เขียน สมนึก สาคร	ผู้ว่าการ	ถูกแทนโดยแบบ .....
ผู้สำรวจ		เขียนเสร็จวันที่ 21 พ.ค. 40
วิศวกร	115 kV วงจรเดี่ยว สายไฟฟ้าคู่ 4 ส.ค. 2540	แก้แบบวันที่ .....
หัวหน้าแผนก	เสาต้นต่อแยกสาย	มิติเป็น .....
ผู้อำนวยการกอง	แบบ SD-TL-4	มาตราส่วน .....
ผู้อำนวยการฝ่าย		
รองผู้ว่าการเทคนิคและบริการ	115 kV SINGLE CIRCUIT DOUBLE CONDUCTOR FOR TAP LINE STRUCTURE TYPE SD-TL-4	แบบเลขที่ SA1-015/40014
		แผ่นที่ 4 ของจำนวน 4 แผ่น

4 ส.ค. 2540