
การประกอบเลขที่
ASSEMBLY NO. 5302

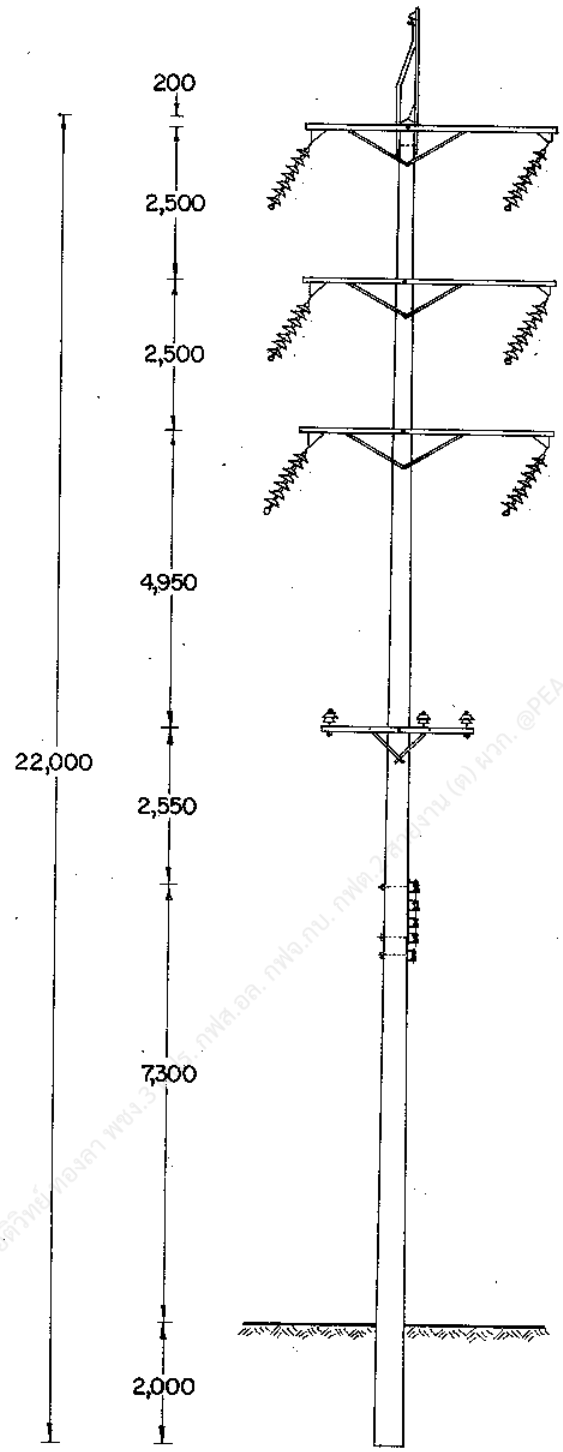

กองวิศวกรรมไฟฟ้าและเครื่องกล
ฝ่ายวิศวกรรม

ผู้เขียน
ผู้สำรวจ
วิศวกร
หัวหน้าแผนก
หัวหน้ากอง
ผู้อำนวยการฝ่าย

ของผู้ว่าการฝ่ายเทคนิค

การไฟฟ้าส่วนภูมิภาค

ผู้ว่าการ


115 kV วงจรคู่ สายไฟฟ้าเดี่ยว
เสาสำหรับทางโค้ง
แบบ DS-SA-1

23 115 kV DOUBLE CIRCUIT SINGLE CONDUCTOR
SMALL ANGLE STRUCTURE
TYPE DS-SA-1

ใช้เทพแบบ
ภูดแทนนี้โดยแบบ
เขียนเสร็จวันที่ 3 พ.ค. 23
แก้แบบครั้งที่
มิติเป็น มม.
มาตราส่วน 1 : 125

แบบเลขที่ SAI-015/23016
แผ่นที่ 1 จากจำนวน 3 แผ่น

การประกอบเลขที่ ASSEMBLY NO. 5302

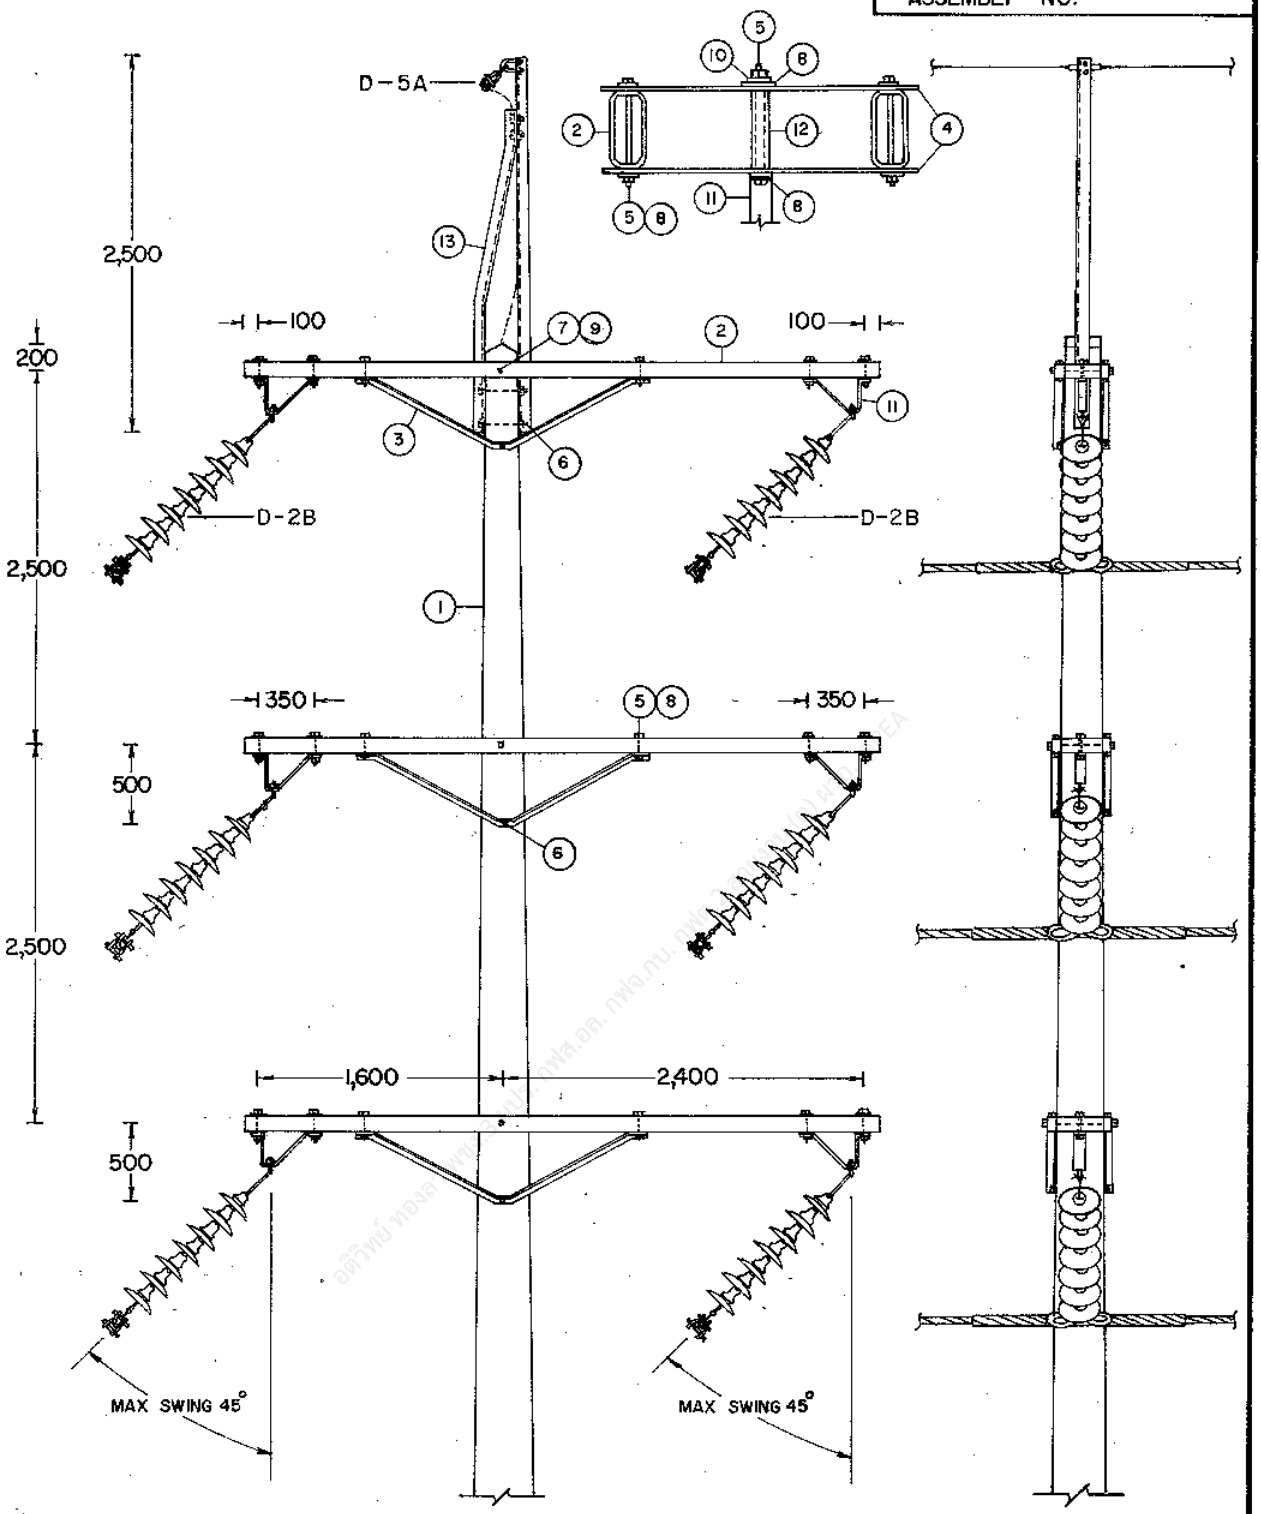

กองวิศวกรรมไฟฟ้าและเครื่องกล ฝ่ายวิศวกรรม	การไฟฟ้าส่วนภูมิภาค	ใช้แทนแบบ ถูกแทนโดยแบบ
ผู้เขียน ผู้สำรวจ วิศวกร หัวหน้าแผนก หัวหน้ากอง ผู้อำนวยการฝ่าย	ผู้ว่าการ 115 kV วงจรคู่ สายไฟฟ้าเดี่ยว เสาสำหรับทางโค้ง แบบ DS-SA-1	เริ่มใช้ครั้งที่ 3 ม.ค. 23 แก้แบบครั้งที่ มิติเป็น มม. มาตราส่วน 1 : 50
รองผู้ว่าการฝ่ายเทคนิค	115 kV DOUBLE CIRCUIT SINGLE CONDUCTOR SMALL ANGLE STRUCTURE TYPE DS-SA-1	แบบเลขที่ SAI-015/23016 แผ่นที่ 2 ของจำนวน 3 แผ่น

การประกอบเลขที่ ASSEMBLY NO. 5302

บัญชีวัสดุ
BILL OF MATERIAL

ลำดับที่ ITEM	รายละเอียด DESCRIPTION	จำนวน REQ'D	วัสดุเลขที่ MAT. NO.
1	เสาคอนกรีต 22 ม. POLE, CONCRETE 22 m LONG	1	00010011 (0041)
2	คอนสายแบบเหล็ก ขนาด 100 X 50 X 3.2 มม. ยาว 4.20 ม. CROSSARM, STEEL 100 X 50 X 3.2 mm, 4.20 m LONG	6	00120001 (0116)
3	เหล็กฉากรับคอนสาย ขนาด 50 X 50 X 6 มม. ช่วงกว้าง 1,800 มม. ดรอป 450 มม. BRACE, ANGLE STEEL 50 X 50 X 6 mm 1,800 mm WIDE 450 mm DROP	6	01200007 (0119)
4	เหล็กแผ่น ขนาด 6 X 100 X 450 มม. PLATE, STEEL 6 X 100 X 450 mm	24	01030002 (0143)
5	สลักเกลียว M 16 X 170 มม. BOLT, MACHINE, M 16 X 170 mm	48	01110201 (0221)
6	สลักเกลียว M 16 X 350 มม. BOLT, MACHINE, M 16 X 350 mm	6	01110205 (0225)
7	สลักเกลียว M 20 X 450 มม. BOLT, MACHINE, M 20 X 450 mm	3	01110302 (0234)
8	แหวนสี่เหลี่ยมแบน 52X52X4.5 มม. รู Ø 18 มม. มอก. 258 WASHER, SQUARE, FLAT 52X52X4.5 mm HOLE Ø 18 mm TIS 258	84	01180100 (0355)
9	แหวนสี่เหลี่ยมแบน 62 X 62 X 6 มม. รู Ø 22 มม. มอก. 258 WASHER, SQUARE, FLAT 62X62X6 mm HOLE Ø 22 mm TIS 258	6	01180101 (0356)
10	แหวนสปริง M 16 มอก. 259 WASHER, LOCK, M 16, TIS 259	12	01180301 (0365)
11	ที่แขวนลูกถ้วยทางโค้ง BRACKET, CORNER SUSPENSION	6	03140012 (0489)
12	ท่อเหล็ก ขื่อขนาด 20 มม. หนา 2.65 มม. ยาว 100 มม. PIPE, IRON DIA. 20 mm I.D., 2.65 mm THICKNESS, 100 mm LONG	12	01050000 (0905)
13	เหล็กฉากรับสายล่อฟ้าทางโค้ง OVERHEAD GROUND WIRE CORNER BAYONET	1	01010005 (0136)
	รายละเอียด **DETAIL**		
D-2B	การประกอบลูกถ้วยแขวน SUSPENSION INSULATOR ASSEMBLY	6	
D-5A	การต่อสายล่อฟ้า OVERHEAD GROUND WIRE CONNECTION	1	
D-10A	ฐานรากเสา POLE FOUNDATION	1	

กองวิศวกรรมไฟฟ้าและเครื่องกล
ฝ่ายวิศวกรรม

ผู้เขียน
ผู้สำรวจ
วิศวกร
หัวหน้าแผนก
หัวหน้ากอง
ผู้อำนวยการฝ่าย

รองผู้ว่าการฝ่ายเทคนิค

การไฟฟ้าส่วนภูมิภาค

ผู้ว่าการ 24 มี.ค. 23

115 kV วงจรคู่ สายไฟฟ้าเดี่ยว
เสาสี่ทางรับทางโค้ง
แบบ DS-SA-1

115 kV DOUBLE CIRCUIT SINGLE CONDUCTOR
SMALL ANGLE STRUCTURE
TYPE DS-SA-1

ใช้แทนแบบ
ถูกแทนโดยแบบ
เขียนเสร็จวันที่ 3 พ.ค. 23
แก้แบบวันที่
มิติเป็น
มาตราส่วน

แบบเลขที่ SAI-015/23016
แผ่นที่ 3 ของจำนวน 3 แผ่น

19 มี.ค. 2523