การประกอบเลขที่ ASSEMBLY NO. 3506

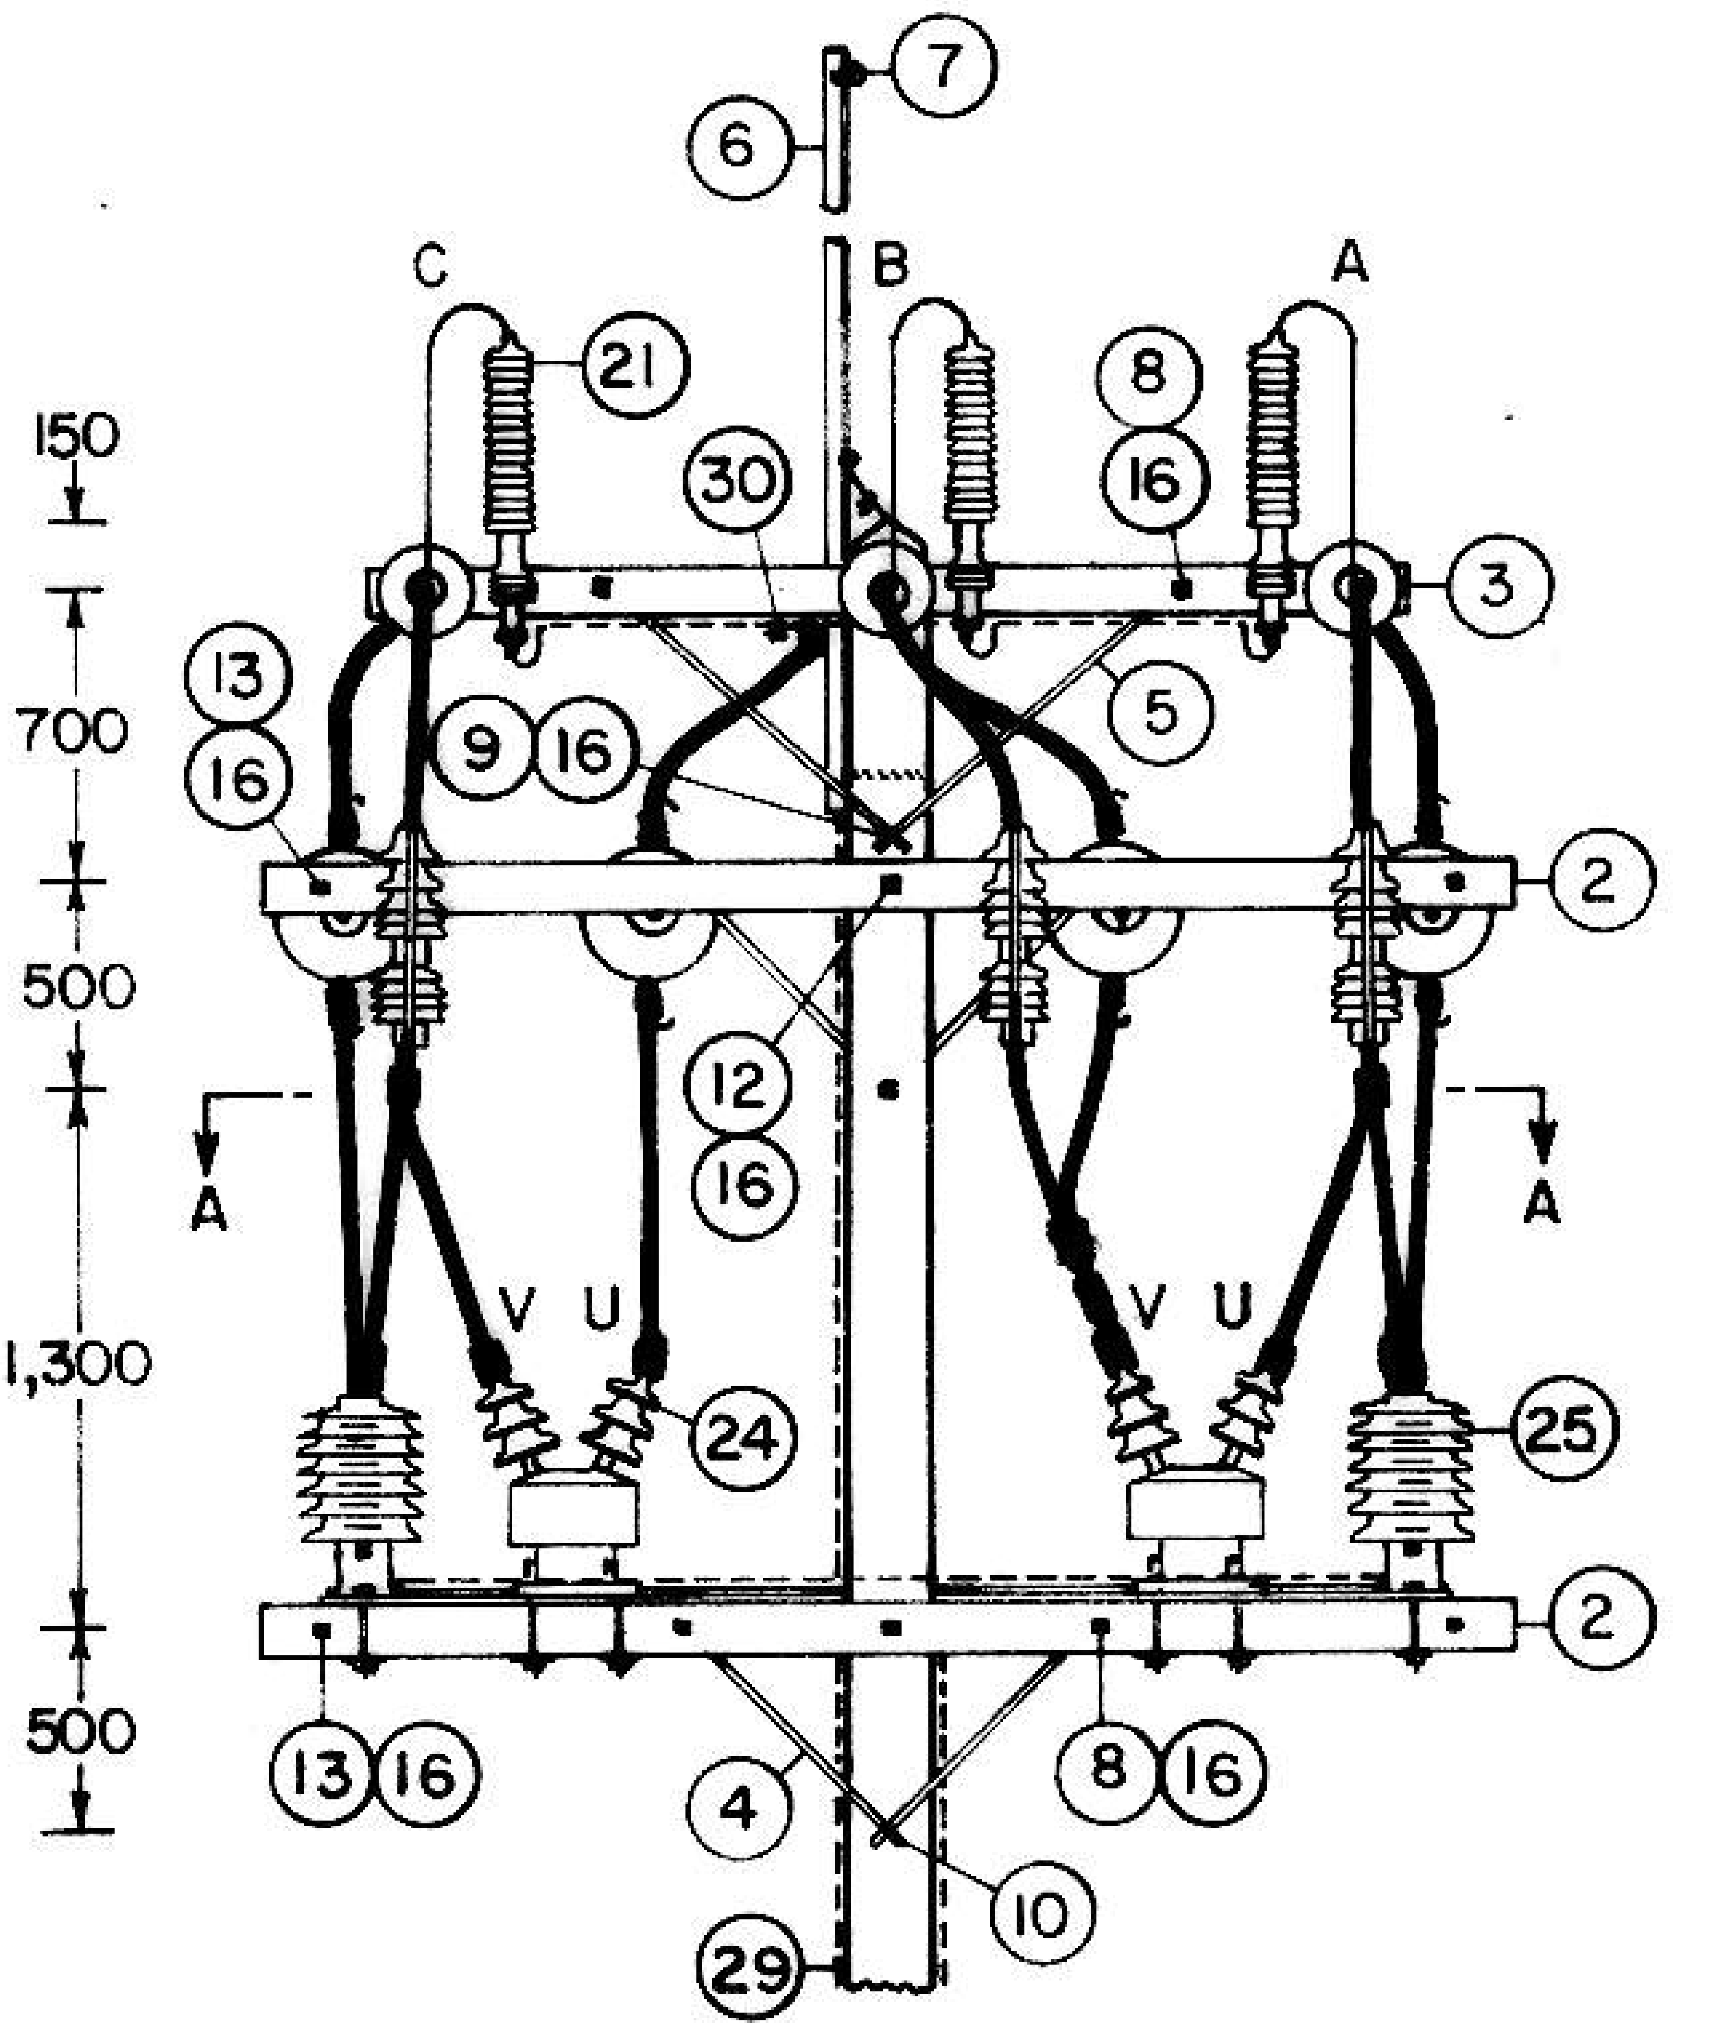

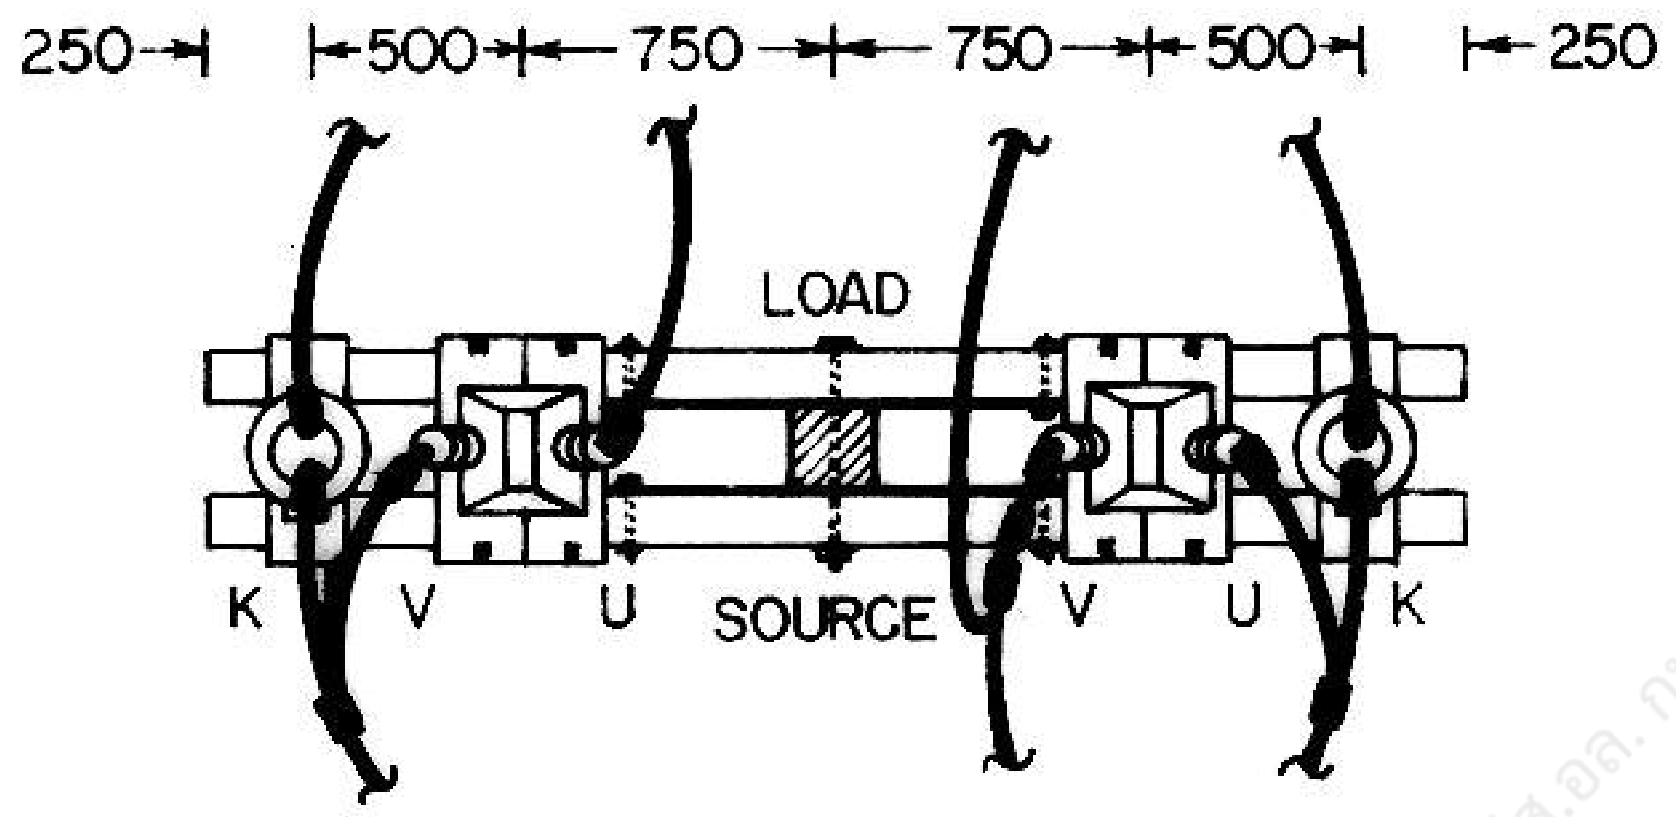

รูปตัด SECTION A – A

รายละเอียด DETAIL A

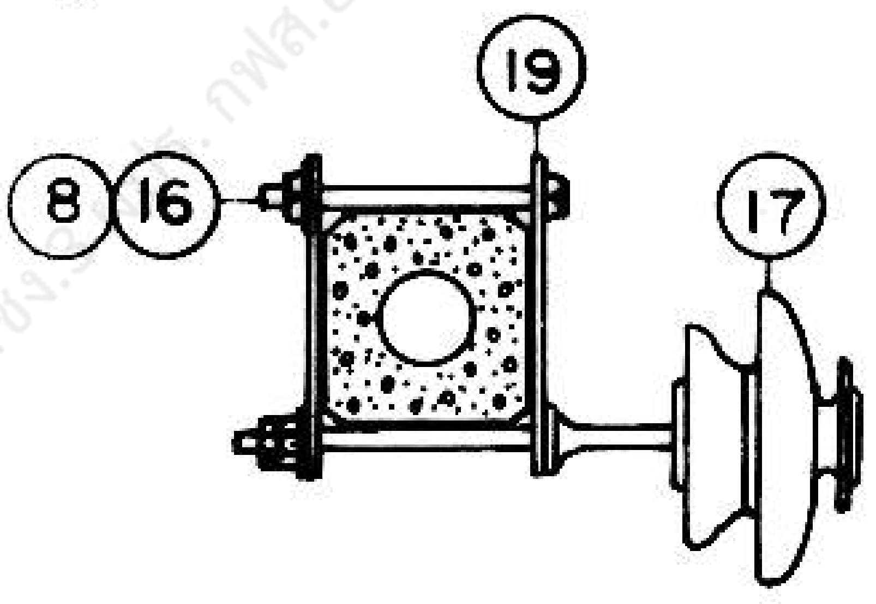

รายละเอียด DETAIL B

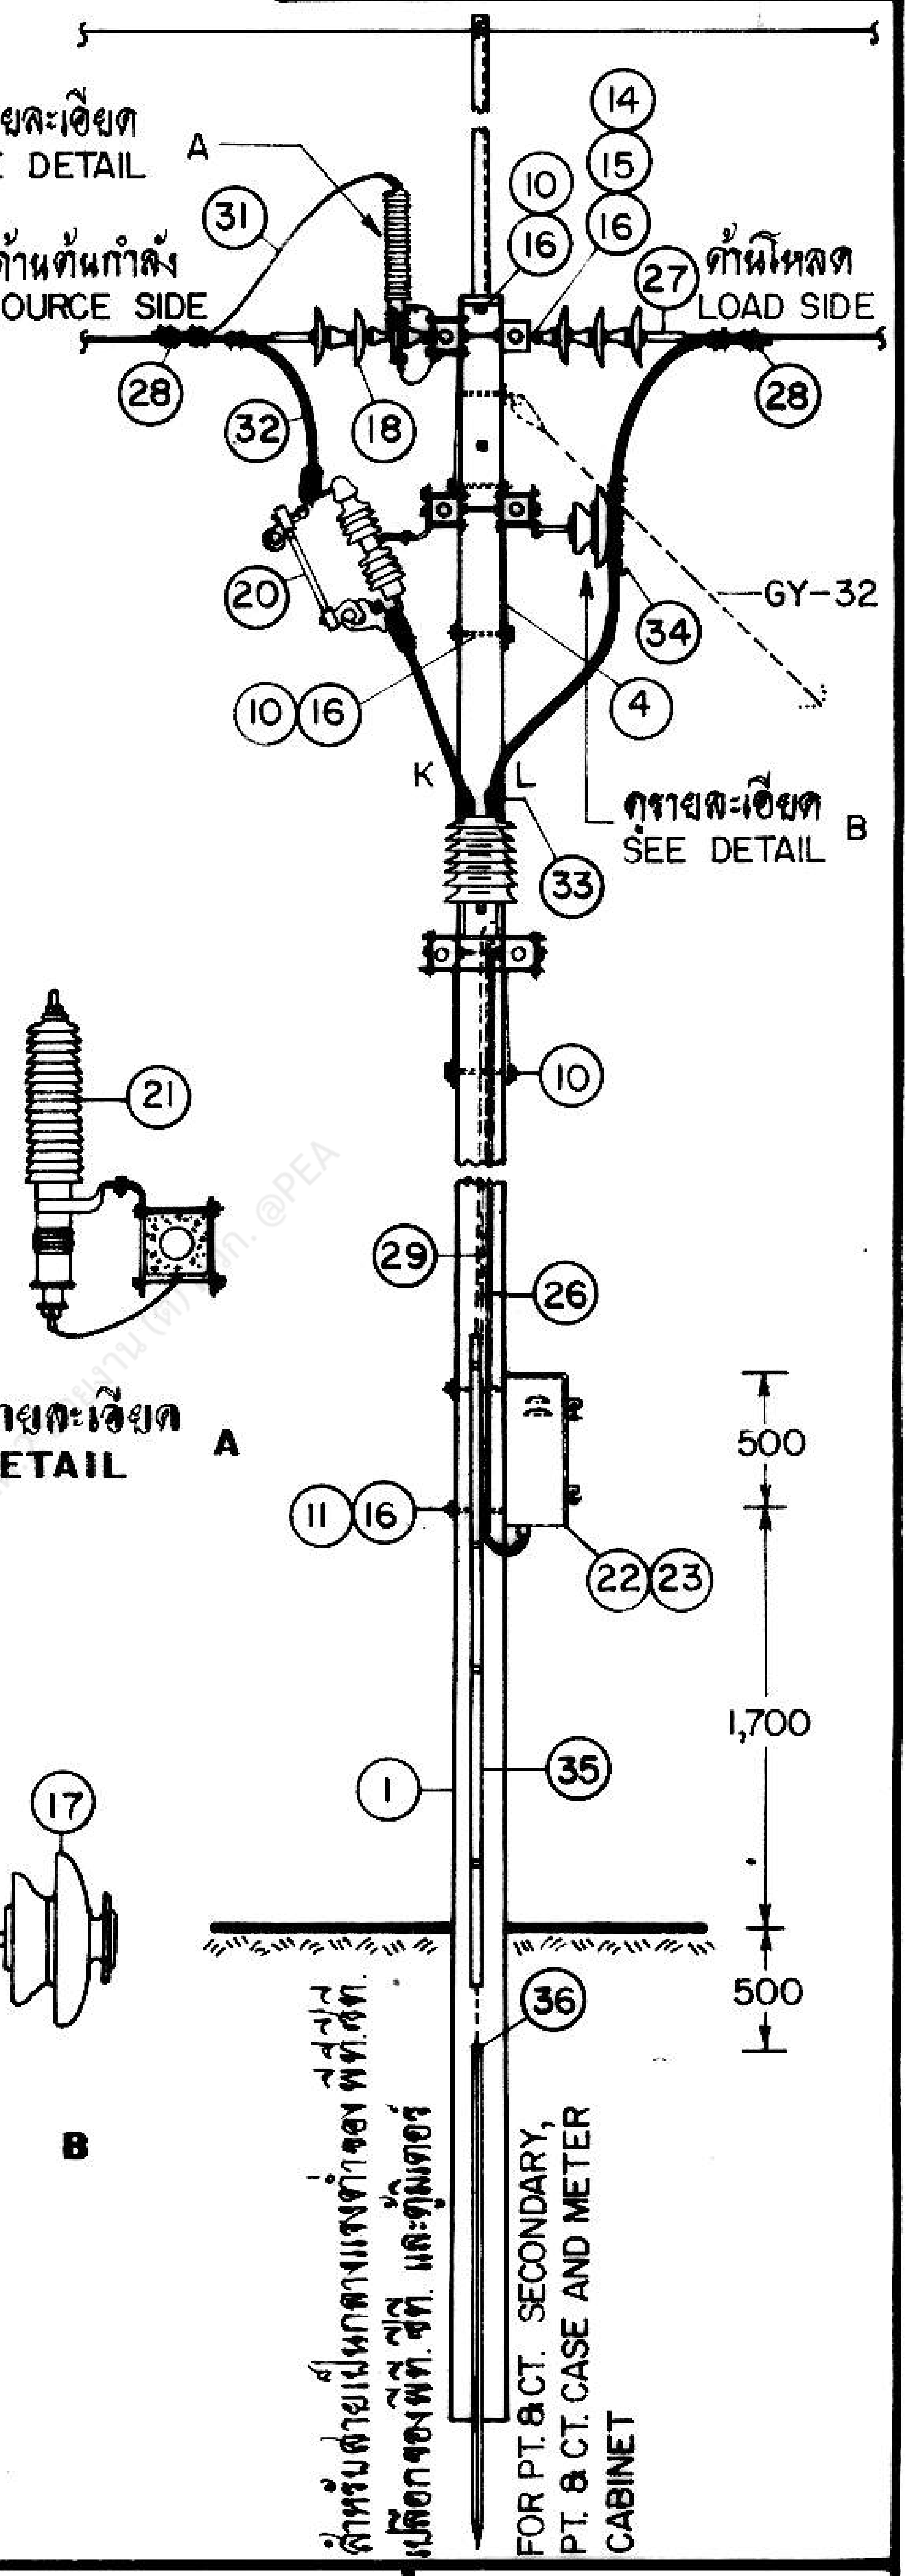

ดูรายละเอียด SEE DETAIL A
14
15
10
16
16
31
ด้านต้นกำลัง SOURCE SIDE
27
ด้านโหลด LOAD SIDE
28
32
18
28
20
GY-32
34
10
16
4
K
L
ดูรายละเอียด SEE DETAIL B
33
10
29
26
500
11
16
22
23
1,700
1
35
500
36
สำหรับสายเป็นกลางแรงต่ำของ พีที. ซีที. เปลือกของพีที. ซีที. และตู้มิเตอร์
FOR PT. & CT. SECONDARY, PT. & CT. CASE AND METER CABINET

สำหรับล่อฟ้าแรงสูง
FOR H.T. LIGHTNING ARRESTER

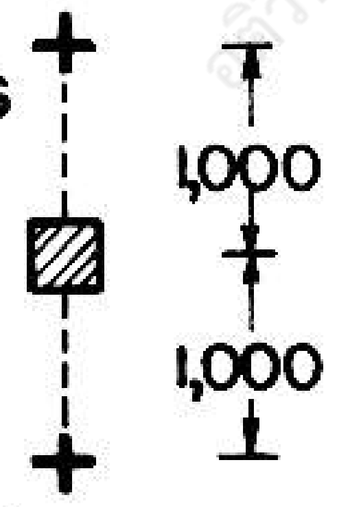

สำหรับสายเป็นกลางแรงต่ำของ พีที. ซีที. เปลือกของ พีที. ซีที. และตู้มิเตอร์
FOR PT. & CT. SECONDARY, PT. & CT. CASE AND METER CABINET

กฟส.อล. กฟจ.กบ. @PEA

กองวิศวกรรมไฟฟ้าและเครื่องกล
ฝ่ายวิศวกรรม

ผู้เขียน
ผู้ตรวจ
วิศวกร
หัวหน้าแผนก
ผู้อำนวยการกอง
ผู้อำนวยการฝ่าย
รองผู้ว่าการฝ่ายเทคนิค

การไฟฟ้าส่วนภูมิภาค

ผู้ว่าการ 17 มิ.ย. 29

การติดตั้งมิเตอร์ 3 เฟส 3 สาย ประกอบ พีที. และ ซีที. แรงสูง
ระบบ 33 kV

INSTALLATION OF 3-Ø, 3-W METER WITH PT. AND CT.
33 kV SYSTEM

ใช้แทนแบบ
ถูกแทนโดยแบบ
เขียนเสร็จวันที่ 16 เม.ย. 29
แก้แบบวันที่
มิติเป็น มม.
มาตราส่วน 1 : 50
แบบเลขที่ SAI-015/29005
แผ่นที่ 1 ของจำนวน 4 แผ่น

การประกอบเลขที่
ASSEMBLY NO. **3506**

วัสดุลำดับที่
MAT. ITEM ⑲

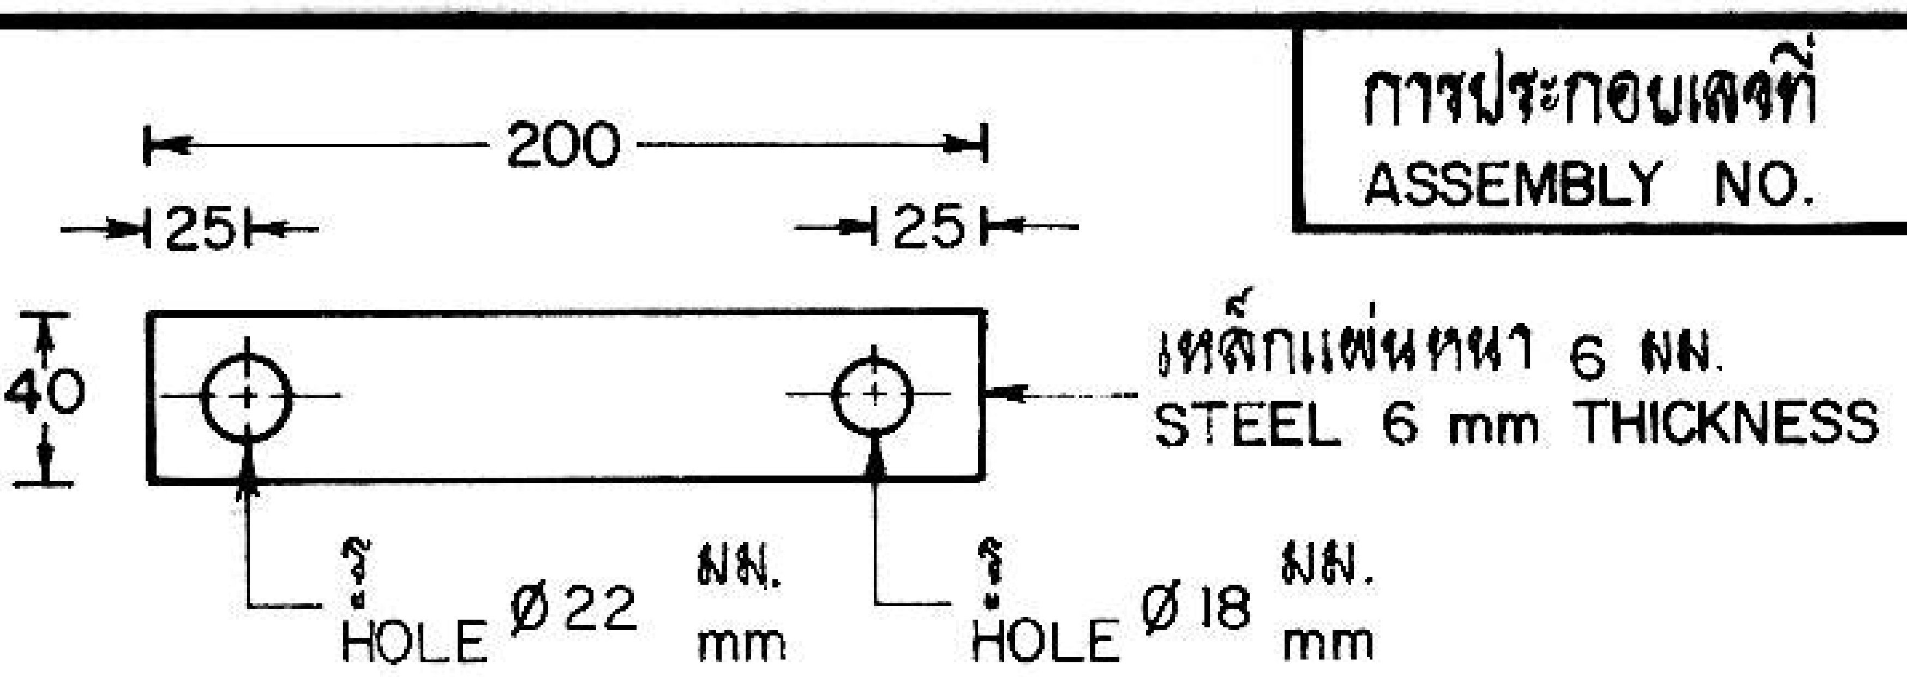

(ดัดแปลงใช้เหล็กประกับ วัสดุเลขที่ 01200002 ได้
MAY BE MADE OF BRACE MAT. NO. 01200002)

รายละเอียด C
DETAIL

บัญชีวัสดุ
BILL OF MATERIAL

ลำดับที่ ITEM	รายละเอียด DESCRIPTION	จำนวน REQ'D	วัสดุเลขที่ MAT. NO.
1	เสาคอนกรีต 12 ม. POLE, CONCRETE 12 m LONG	1	00010004
2	คอน คอร. สปัน ขนาด 120 X 120 X 3,000 มม. CROSSARM, SPUN, PRESTRESSED CONCRETE 120 X 120 X 3,000 mm	4	00110002
3	คอน คอร. สปัน (สำหรับเข้าปลายสาย) 120 X 120 X 2,500 มม. CROSSARM, SPUN, PRESTRESSED CONCRETE (FOR DEADENDING) 120 X 120 X 2,500 mm	2	00110004
4	เหล็กประกับคอนสาย 30 X 6 X 760 มม. BRACE, FLAT, FOR CROSSARM 30 X 6 X 760 mm	6	01200001
5	เหล็กประกับคอนสาย 40 X 6 X 1,000 มม. BRACE, FLAT, FOR CROSSARM 40 X 6 X 1,000 mm	2	01200002
6	เหล็กฉากรับสายล่อฟ้า OVERHEAD GROUND WIRE BAYONET	1	01010006
7	กราวด์วายแคล้มป์ แบบ J 1152 GROUND WIRE CLAMP, J 1152	1	01230205
8	สลักเกลียว 16 X 170 มม. BOLT, MACHINE, M 16 X 170 mm	12	01110201
9	สลักเกลียว M 16 X 200 มม. BOLT, MACHINE, M 16 X 200 mm	1	01110202
10	สลักเกลียว M 16 X 250 มม. BOLT, MACHINE, M 16 X 250 mm	4	01110203
11	สลักเกลียว M 16 X 300 มม. BOLT, MACHINE, M 16 X 300 mm	2	01110204
12	สลักเกลียว M 16 X 450 มม. BOLT, MACHINE, M 16 X 450 mm	2	01110207
13	สลักเกลียวตลอด M 16 X 500 มม. BOLT, DOUBLE ARMING, M 16 X 500 mm	4	01120002
14	สลักเกลียวหัวห่วงกลม M 16 X 450 มม. BOLT, DOUBLE ARMING, ROUND EYE, M 16 X 450 mm	3	01130001
15	นัทรูปห่วง M 16 DIN 582 NUT, EYE, M 16 DIN 582	3	01180001

พ.3 ผบร. กฟส.อต. กฟจ.กน. กฟต.2 (สายงาน (ต)) ผวก. @PEA

กองวิศวกรรมไฟฟ้าและเครื่องกล
ฝ่ายวิศวกรรม

ผู้เขียน
ผู้สำรวจ
วิศวกร
หัวหน้าแผนก
ผู้อำนวยการกอง
ผู้อำนวยการฝ่าย

รองผู้ว่าการฝ่ายเทคนิค

การไฟฟ้าส่วนภูมิภาค

ผู้ว่าการ 17 มิ.ย. 29

การติดตั้งมิเตอร์ 3 เฟส 3 สาย ประกอบ พีที. และซีที. แรงสูง
ระบบ 33 kV

INSTALLATION OF 3-Ø,3-W METER WITH PT. AND CT.
33 kV SYSTEM

ใช้แทนแบบ
ถูกแทนโดยแบบ
เขียนเสร็จวันที่ 16 เม.ย. 29
แก้แบบวันที่
มิติเป็น มม.
มาตราส่วน 1 : 5

แบบเลขที่ SAI-015/29005
แผ่นที่ 2 ของจำนวน 4 แผ่น

การประกอบเลขที่ ASSEMBLY NO. 3506

บัญชีวัสดุ
BILL OF MATERIAL

ลำดับที่ ITEM	รายละเอียด DESCRIPTION	จำนวน REQ'D	วัสดุเลขที่ MAT. NO.
16	แหวนสี่เหลี่ยมแบน 52 X 52 X 4.5 มม. รู Ø 18 มม. มอก. 258 WASHER, SQUARE, FLAT 52 X 52 X 4.5 mm HOLE Ø 18 mm TIS 258	50	01180100
17	ลูกถ้วยก้านตรง 33 kV มอก. 279 แบบ ค (แบบ 56-3) พร้อมก้าน INSULATOR, PIN TYPE, 33 kV TIS 279 TYPE C (CLASS 56-3) COMP. WITH PIN	4	03000002 03100001
18	ลูกถ้วยแขวน มอก. 354 แบบ ง (แบบ 52-4) INSULATOR, SUSPENSION TYPE, TIS 354 TYPE D (CLASS 52-4)	18	03020002
19	แผ่นเหล็ก 40 X 6 มม. ยาว 200 เจาะรูตามรายละเอียด C STEEL PLATE, 40 X 6 mm, 200 mm LONG, PUNCH HOLE AS DETAIL C	8	
20	ดรอพเอาต์ฟิวส์คัตเอาต์ หนึ่งอินซูเลเตอร์ 33 kV, 100 แอมป์ CUT-OUT, FUSE, OPEN TYPE, SINGLE INSULATOR, DROPOUT 33 kV, 100 A	3	04010100
21	ล่อฟ้าแรงสูง 30 kV, 5 กิโลแอมป์ LIGHTNING ARRESTER 30 kV, 5 kA	3	04000100
22	ดีมานด์มิเตอร์ ชนิดสะสม 3 เฟส 3 สาย 110 โวลต์ 5 แอมป์ DEMAND METER, CUMULATIVE, 3-PHASE, 3-WIRE, 110 V, 5 A	1	06000300
23	ตู้อะลูมิเนียมใช้ภายนอกอาคาร สำหรับดีมานด์มิเตอร์ พร้อมแป้นไม้ ALUMINIUM METER CABINET, OUTDOOR FOR 3-Ø DEMAND METER COMPLETE WITH WOOD PLATE	1	06100007
24	พีที. หนึ่งเฟสใช้นอกอาคาร 33,000-110 โวลต์ พร้อมอุปกรณ์ติดตั้ง TRANSFORMER, POTENTIAL, 1Ø, OUTDOOR, 33,000-110 V COMP. WITH MOUNTING ACCESS.	2	06020100
25	ซีที. ใช้นอกอาคาร 33 kV เรโชตามต้องการ พร้อมอุปกรณ์ติดตั้ง TRANSFORMER, CURRENT, 33 kV, RATIO AS REQUIRED COMP. WITH MOUNTING ACCESS.	2	06040101 - 06040106
26	คอนโทรลเคเบิล ขนาด 7 X 2.5 ต.มม. CONTROL CABLE, SIZE 7 X 2.5 mm^2	10 ม. m	02080402
27	สเตรนแคล้มป์สำหรับสายอะลูมิเนียม ขนาด 35-95 ต.มม. CLAMP, STRAIN, FOR Al SIZE 35-95 mm^2	6	03110000 - 03110001
28	พี.จี. คอนเนคเตอร์สลักคู่ สำหรับสายอะลูมิเนียม 35-95 ต.มม. CONNECTOR, PARALLEL GROOVE, DOUBLE BOLT, Al 35-95 mm^2	20	02300101 - 02300102
29	ลวดเหล็กตีเกลียว 50/7 ต.มม. มอก. 404 STEEL STRANDED WIRE 50/7 mm^2 TIS 404	28 ม. m	01100004
30	ยูแคล้มป์ สลักเดี่ยว M 8 CLAMP, SINGLE U-BOLT, M 8	7	01230000
31	สายอะลูมิเนียมเปลือย 35-95 ต.มม. มอก. 85 CONDUCTOR, Al, BARE 35-95 mm^2 TIS 85	4 ม. m	02010001 - 02010004
32	สายอะลูมิเนียมหุ้มฉนวนใช้ภายนอก 750 โวลต์ 75° ซ ขนาด 35-95 ต.มม. CONDUCTOR, INSULATED WEATHER-PROOF, 750 V, 75°C, Al 35-95 mm^2	23 ม. m	02070001 - 02070004
33	เทปพันเคเบิลอากาศแรงสูง ขนาด 3/4" X 30' ELECTRICAL SPLICING TAPE, FOR H.T. AERIAL CABLE, SIZE 3/4" X 30'	ม้วน roll	02180003
34	ลวดอะลูมิเนียมกลม ขนาด Ø 4 มม. TIE WIRE, Al Ø 4 mm LENGTH AS REQUIRED	ม. m	02200002

กองวิศวกรรมไฟฟ้าและเครื่องกล
ฝ่ายวิศวกรรม

ผู้เขียน
ผู้สำรวจ
วิศวกร
หัวหน้าแผนก
ผู้อำนวยการกอง
ผู้อำนวยการฝ่าย

รองผู้ว่าการฝ่ายเทคนิค

การไฟฟ้าส่วนภูมิภาค

ผู้ว่าการ 17 มิ.ย. 29

การติดตั้งมิเตอร์ 3 เฟส 3 สาย ประกอบ พีที. และซีที. แรงสูง
ระบบ 33 kV

INSTALLATION OF 3-Ø, 3-W METER WITH PT. AND CT.
33 kV SYSTEM

ใช้แทนแบบ
ถูกแทนโดยแบบ
เขียนเสร็จวันที่ 16 เม.ย. 29
แก้แบบวันที่
ผลิตเป็น
มาตราส่วน

แบบเลขที่ SAI-015/29005
แผ่นที่ 3 ของจำนวน 4 แผ่น

การประกอบเลขที่
ASSEMBLY NO. **3506**

บัญชีวัสดุ
BILL OF MATERIAL

ลำดับที่ ITEM	รายละเอียด DESCRIPTION	จำนวน REQ'D	วัสดุเลขที่ MAT. NO.
35	ท่อ PVC แข็ง ขนาด Ø 20 X 4,000 มม. พร้อมอุปกรณ์ยึด CONDUIT, PVC RIGID, Ø 20 X 4000 mm COMPLETE WITH FIXING ACCESSORIES	2	08040002
36	หลักดิน 60 X 60 X 5 มม. ยาว 2 ม. ROD, GROUND, 60 X 60 X 5 mm, 2 m LONG	2	01220002

	แบบอ้างอิง REFERENCE DRAWING	แบบเลขที่ DWG. NO.	การประกอบเลขที่ ASSEMBLY NO.
1	แผนผังการต่อมิเตอร์แรงสูง 3 เฟส 3 สาย 11–33 kV CONNECTION DIAGRAM OF 3-PHASE, 3-WIRES H.T. METER, 11–33 kV	S02-015/16005	**0506**
2	การต่อลงดินระบบแรงสูง และแรงต่ำ แผ่นที่ 15 และ 17 H.T. AND L.T. EARTHING SYSTEM, SHEET NO. 15 AND 17	S02-015/20039	**9701**
3	การประกอบสายดิน วิธียึดลวดเหล็ก GROUND LEAD ASSEMBLY, STEEL WIRE FITTING	S02-015/19166	**9703**
4	การประกอบที่ยึดท่อ PVC สำหรับสายดิน PVC PIPE FITTING ASSEMBLY FOR GROUND WIRE	S02-015/19128	**9704**

อดิวิทย์ ทองลา พชง.3 ผปร. กฟส.อล. กฟจ.กบ. กฟต.2 สายงาน (ต) ผวก. PEA

กองวิศวกรรมไฟฟ้าและเครื่องกล
ฝ่ายวิศวกรรม

ผู้เขียน
ผู้ตรวจ
วิศวกร
หัวหน้าแผนก
ผู้อำนวยการกอง
ผู้อำนวยการฝ่าย

รองผู้ว่าการฝ่ายเทคนิค

การไฟฟ้าส่วนภูมิภาค

ผู้ว่าการ 17 มิ.ย. 29

การติดตั้งมิเตอร์ 3 เฟส 3 สาย ประกอบ พีที. และซีที. แรงสูง
ระบบ 33 kV

INSTALLATION OF 3-Ø, 3-W METER WITH PT. AND CT.
33 kV SYSTEM

ใช้แทนแบบ
ถูกแทนโดยแบบ
เขียนเสร็จวันที่ 16 เม.ย. 29
แก้แบบวันที่
มิติเป็น
มาตราส่วน

แบบเลขที่ SAI–015/29005
แผ่นที่ 4 ของจำนวน 4 แผ่น