

การประกอบเลขที่ ASSEMBLY NO. 0550

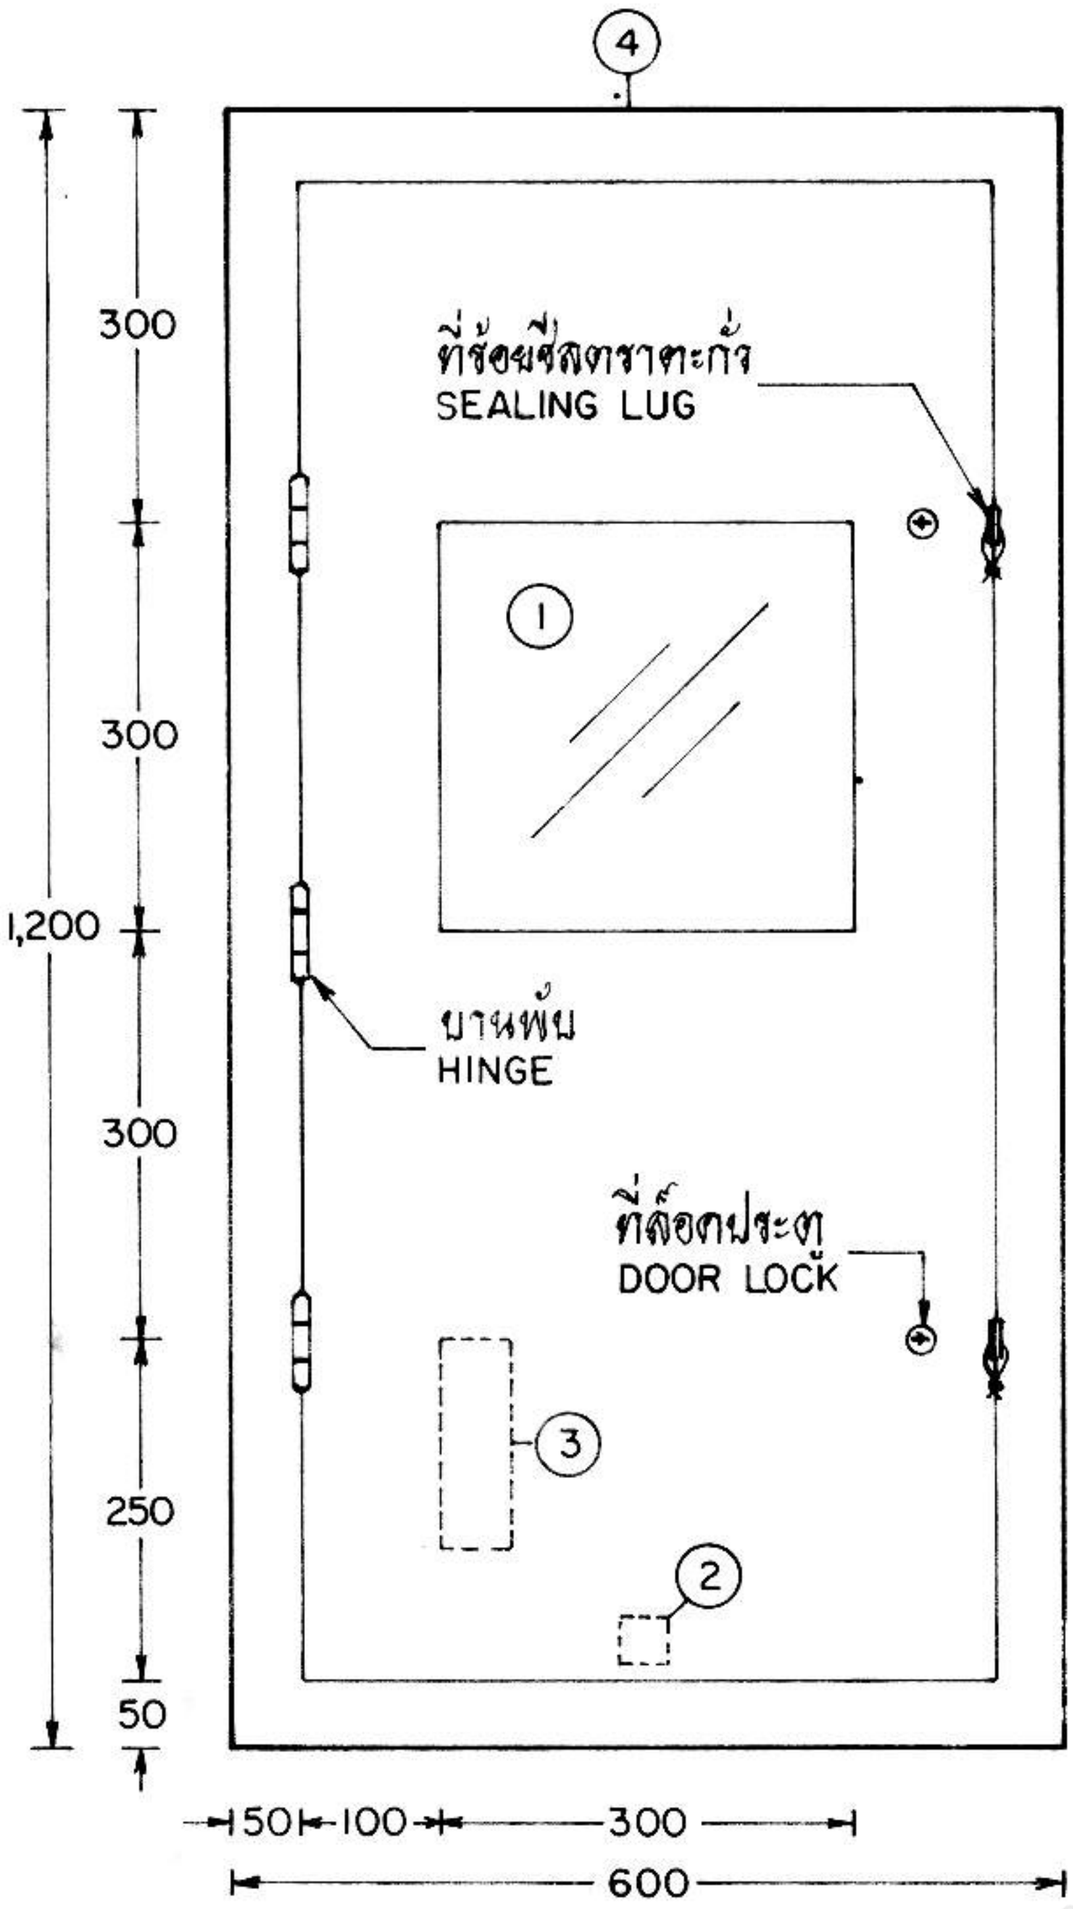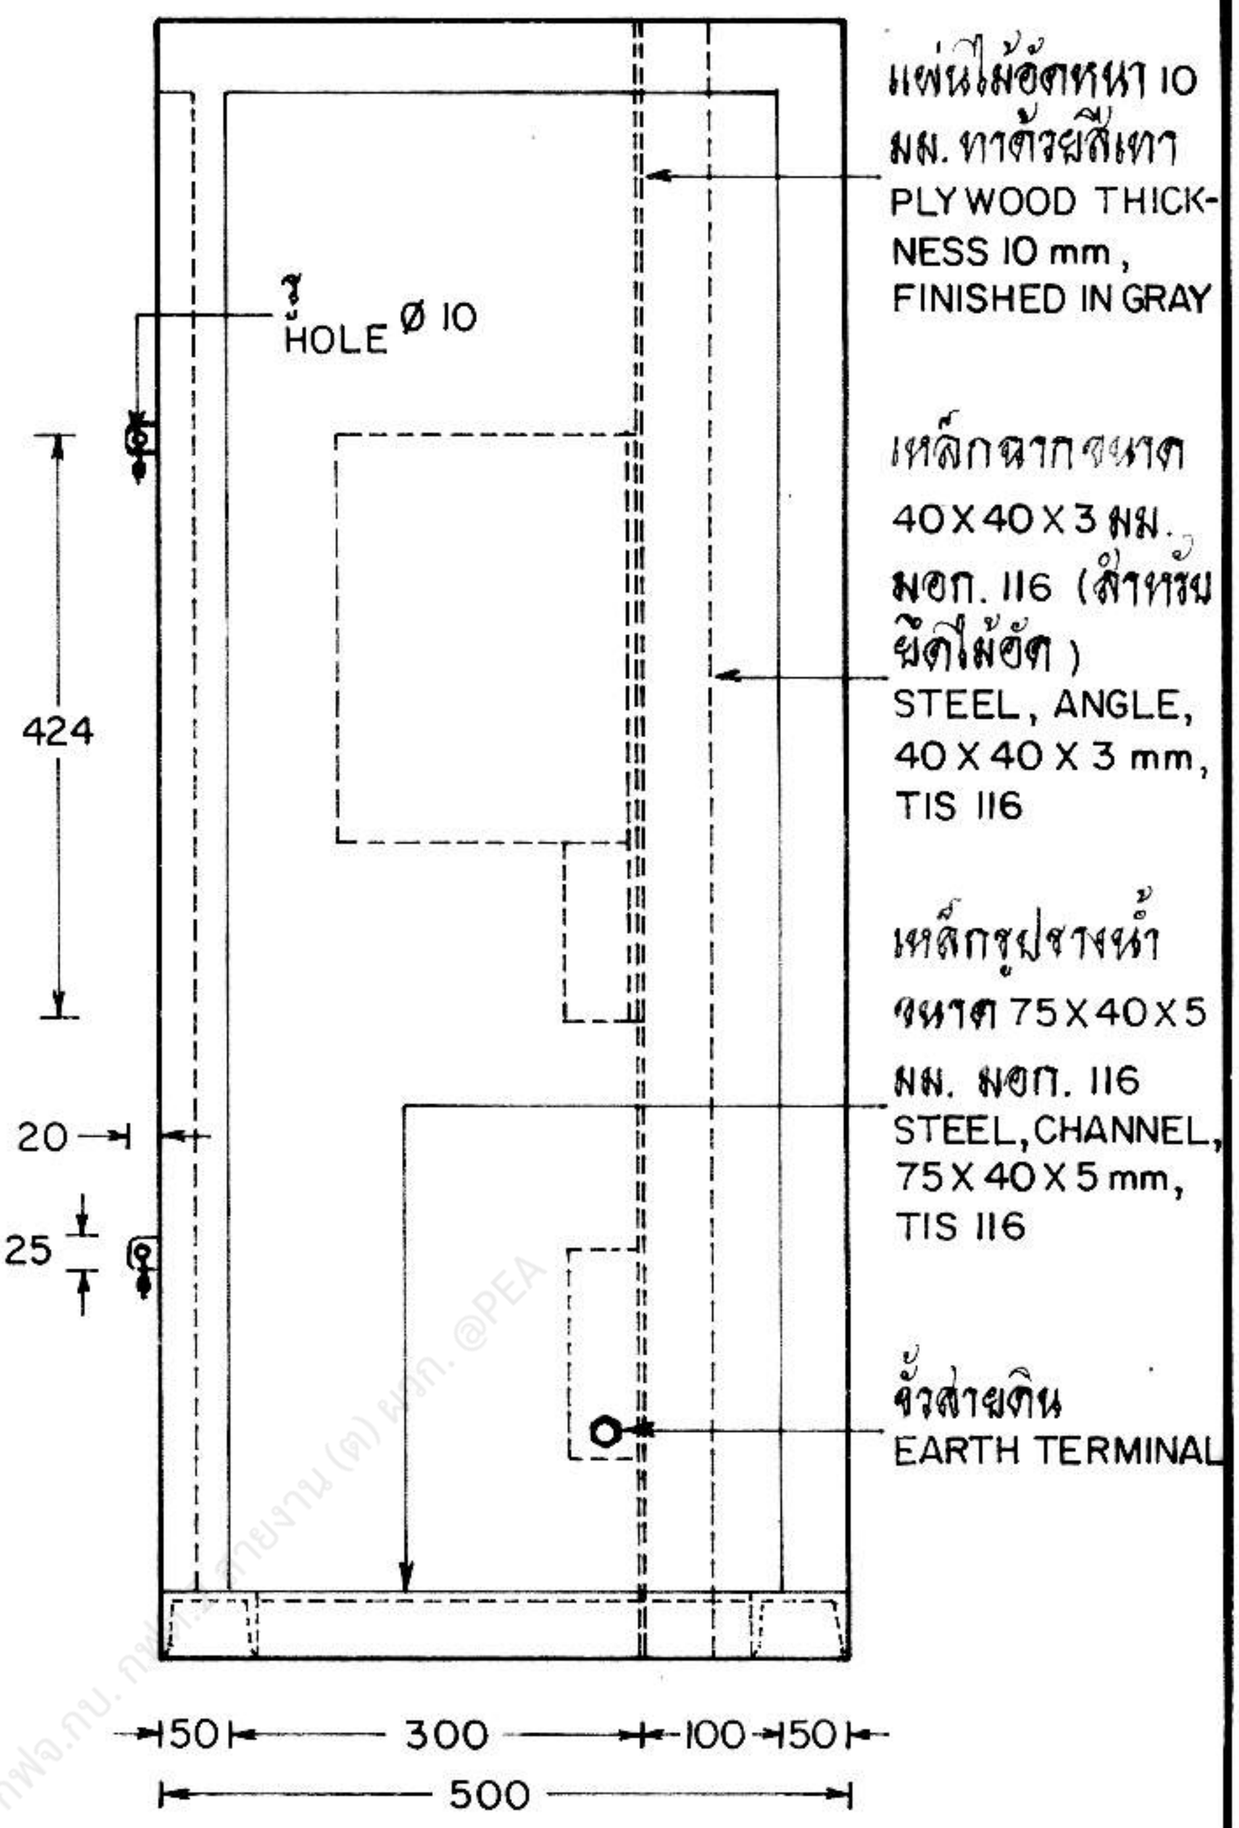


## รายละเอียด

1 กระจกใส หนา 5 มม.

2 ฐานฟิวส์ใช้ภายในอาคาร พร้อมคาร์ทริดจ์ฟิวส์ ขนาด 5 แอมป์

3 กล่องต่อสายไฟฟ้า 600 โวลต์ สำหรับสายทองแดง ขนาด 2.5 – 4 ต.มม. จำนวนไม่น้อยกว่า 12 ขั้ว

4 ตู้ทำด้วยแผ่นเหล็ก หนาอย่างน้อย 2 มม. พร้อมทั้งทาด้วยสีกันสนิม และทาทับด้วยสีเทา

## DETAILS

1 CLEAR GLASS THICKNESS 5 mm .

2 FUSE BASE, INDOOR TYPE, WITH 5 A CARTRIDGE FUSE .

3 TERMINAL BLOCK FOR COPPER CABLE 600 V SIZE 2.5 - 4 $mm^2$, NUMBER OF TERMINALS NOT LESS THAN 12 .

4 STEEL PLATE THICKNESS NOT LESS THAN 2 mm, PAINTED WITH ANTI – FEROUS COAT AND FINISHED IN GRAY .

| | | |
|---|---|---|
| กองวิศวกรรมไฟฟ้าและเครื่องกล<br>ฝ่ายวิศวกรรม | การไฟฟ้าส่วนภูมิภาค | ใช้แทนแผ่น .....<br>ถูกแทนโดยแผ่น .....<br>เขียนเสร็จวันที่ 19 ก.ค. 37 |
| ผู้เขียน .....<br>ผู้สำรวจ .....<br>วิศวกร .....<br>หัวหน้าแผนก .....<br>ผู้อำนวยการกอง .....<br>ผู้อำนวยการฝ่าย ..... | ผู้ว่าการ ..... 5 ส.ค 2537 ผวก.<br>ตู้ใส่เทเลเคาน์ติ้งอินสทรูเมนท์ | หน่วยงานที่ .....<br>มิติเป็น มิลลิเมตร<br>มาตราส่วน 1 : 10 |
| รองผู้ว่าการฝ่ายเทคนิค<br>4 ส.ค. 2537 | TELECOUNTING INSTRUMENT CABINET | แผนเลขที่ SA4-015/37022<br>แผ่นที่ 1 ของจำนวน 1 แผ่น |