
การประกอบเลขที่ ASSEMBLY NO. 3719

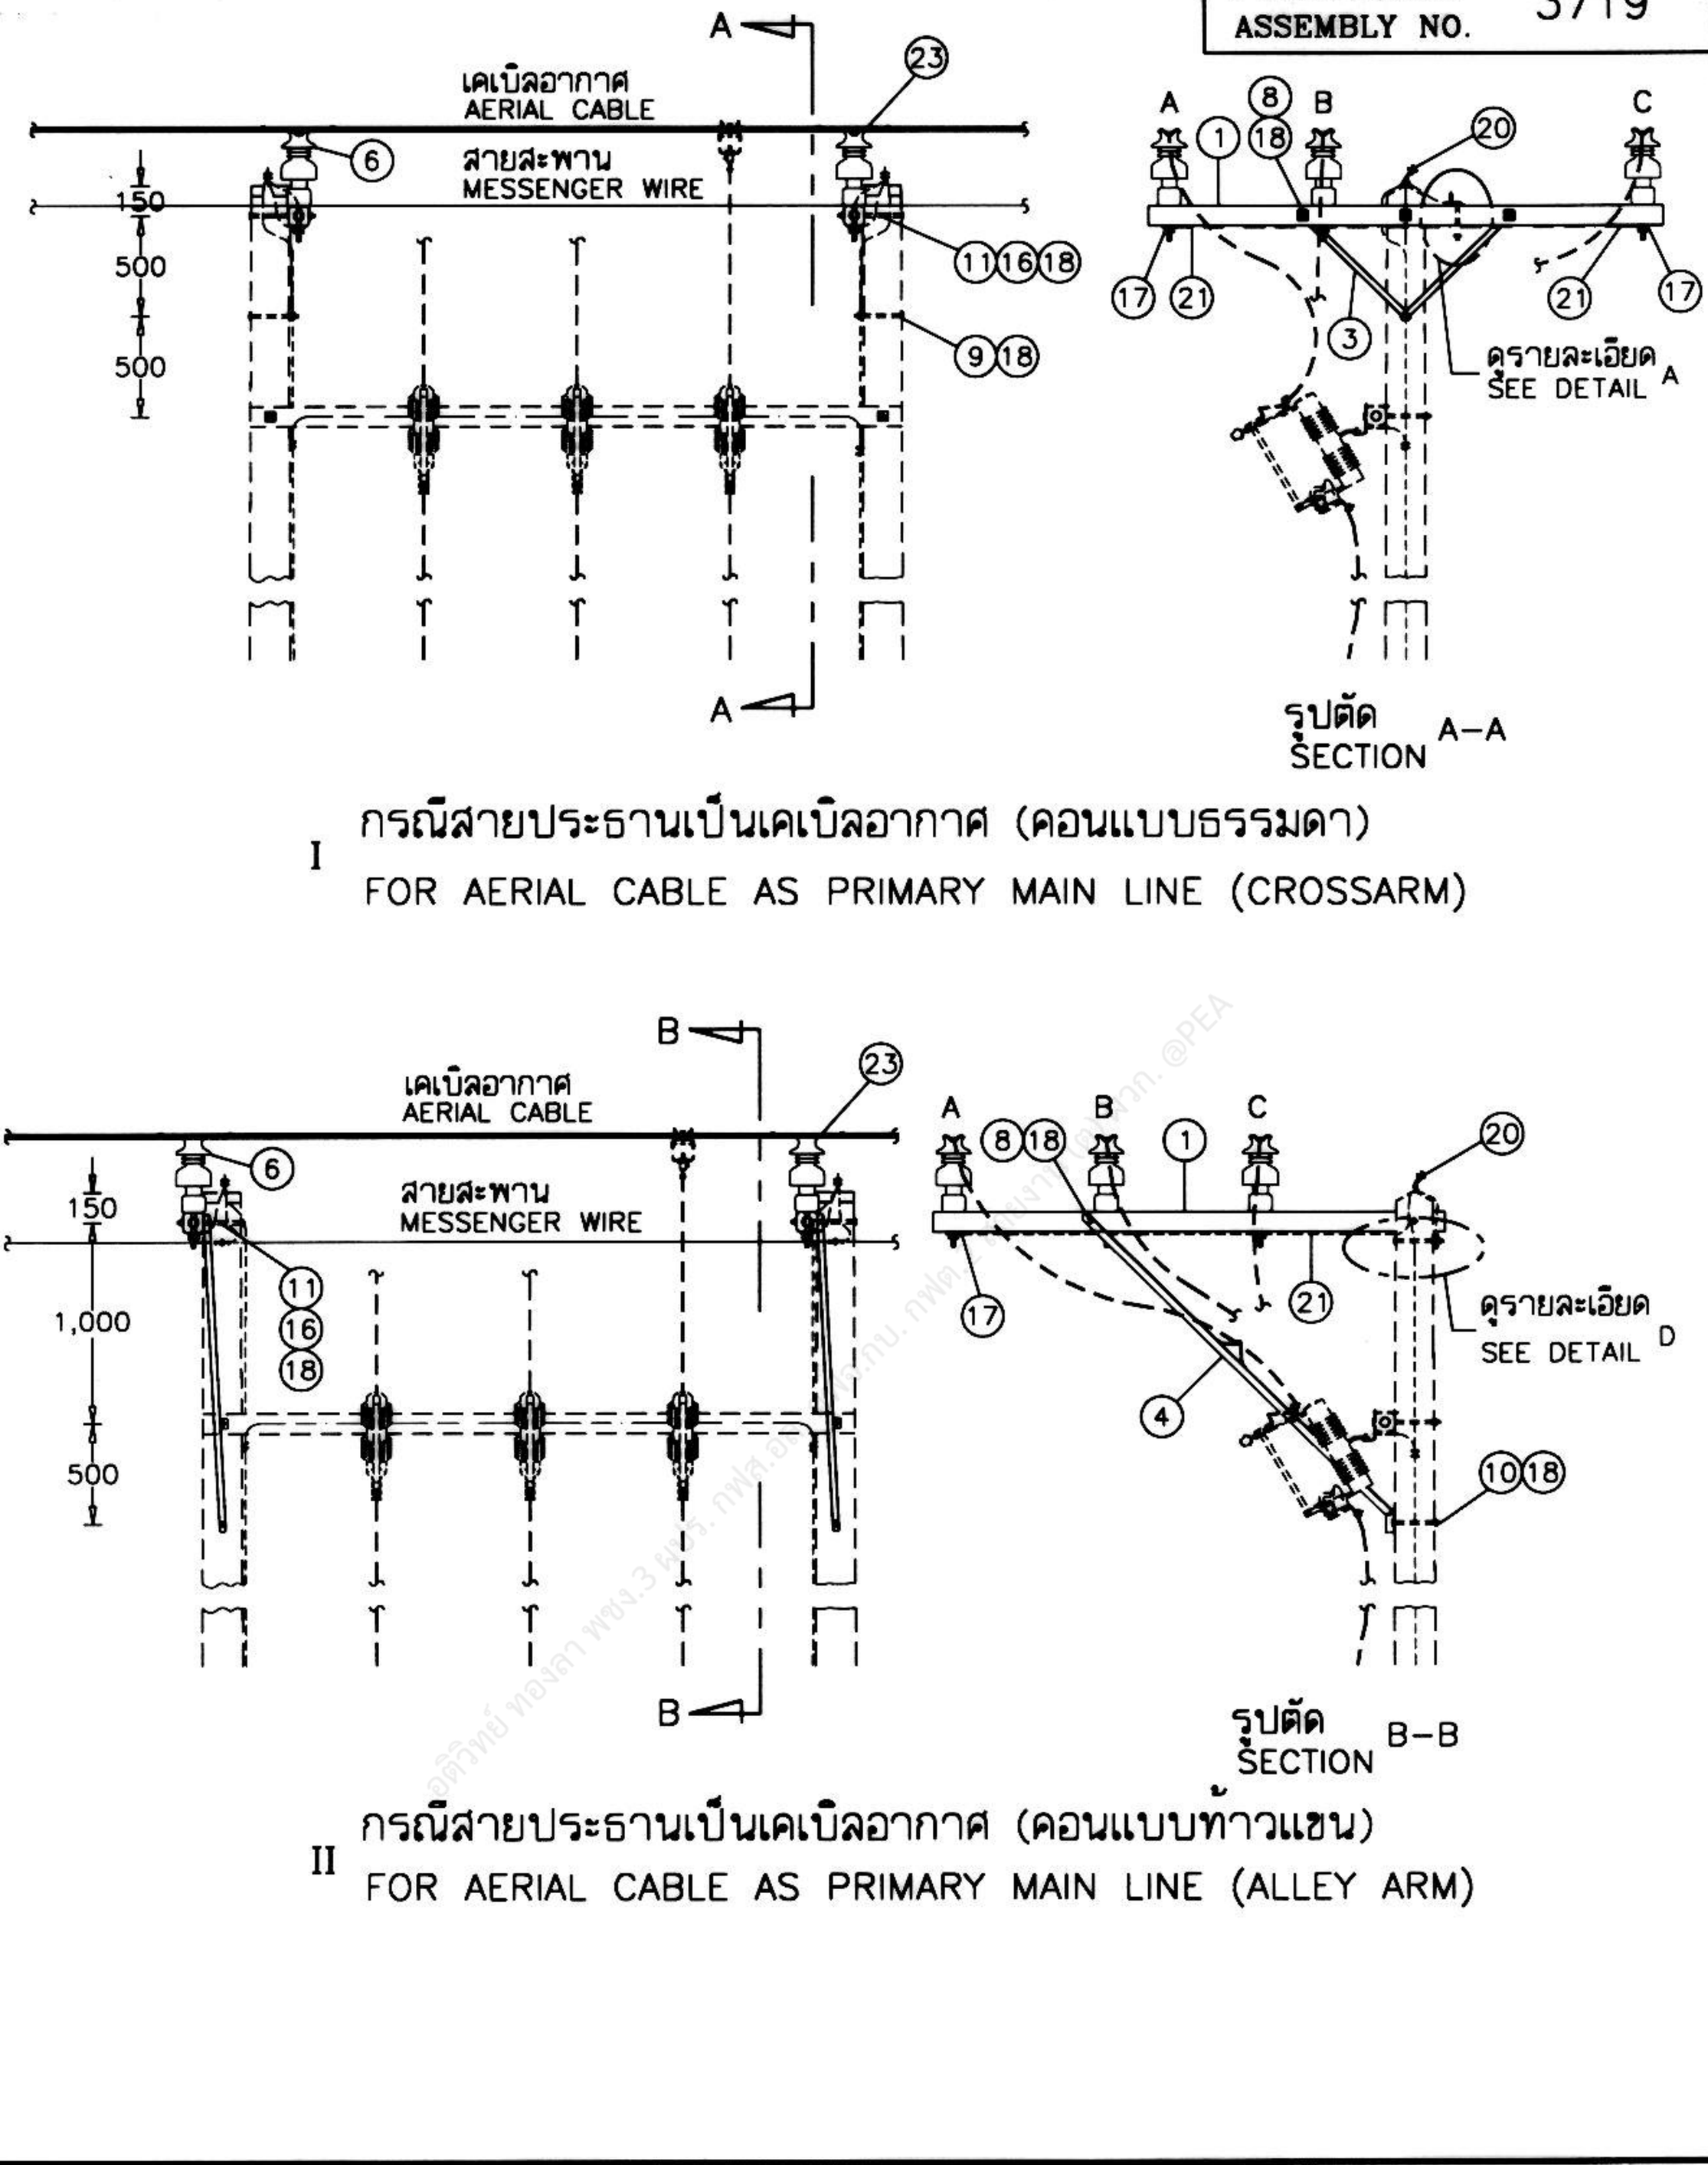

รูปตัด A–A
SECTION A–A


I กรณีสายประธานเป็นเคเบิลอากาศ (คอนแบบธรรมดา)
FOR AERIAL CABLE AS PRIMARY MAIN LINE (CROSSARM)

รูปตัด B–B
SECTION B–B


II กรณีสายประธานเป็นเคเบิลอากาศ (คอนแบบท้าวแขน)
FOR AERIAL CABLE AS PRIMARY MAIN LINE (ALLEY ARM)

กองมาตรฐานระบบไฟฟ้า ฝ่ายมาตรฐานและความปลอดภัย	การไฟฟ้าส่วนภูมิภาค	ใช้แทนแบบ .... SA1-015/21010, SA1-015/27015, SA1-015/31003, SA1-015/34032 ถูกแทนโดยแบบ .....
ผู้เขียน Supphakit Boonrung ผู้สำรวจ Supphakit Boonrung วิศวกร..... หัวหน้าแผนก..... ผู้อำนวยการกอง..... ผู้อำนวยการฝ่าย.....	ผู้ว่าการ..... - 9 W.A. 2544	เขียนเสร็จวันที่ 4 พ.ค. 2544 แก้แบบวันที่ ..... มิติเป็น มิลลิเมตร มาตราส่วน 1 : 50
รองผู้ว่าการวางแผนและพัฒนาระบบไฟฟ้า	การประกอบสายประธานบนนั่งร้านหม้อแปลง 3 เฟส ระบบ 33 kV MAIN LINE ASSEMBLY ON PLATFORM TRANSFORMER 3–PHASE, 33 kV	แบบเลขที่ SA4-015/44012 แผ่นที่ 1 ของจำนวน 11 แผ่น

การประกอบเลขที่ ASSEMBLY NO. 3719

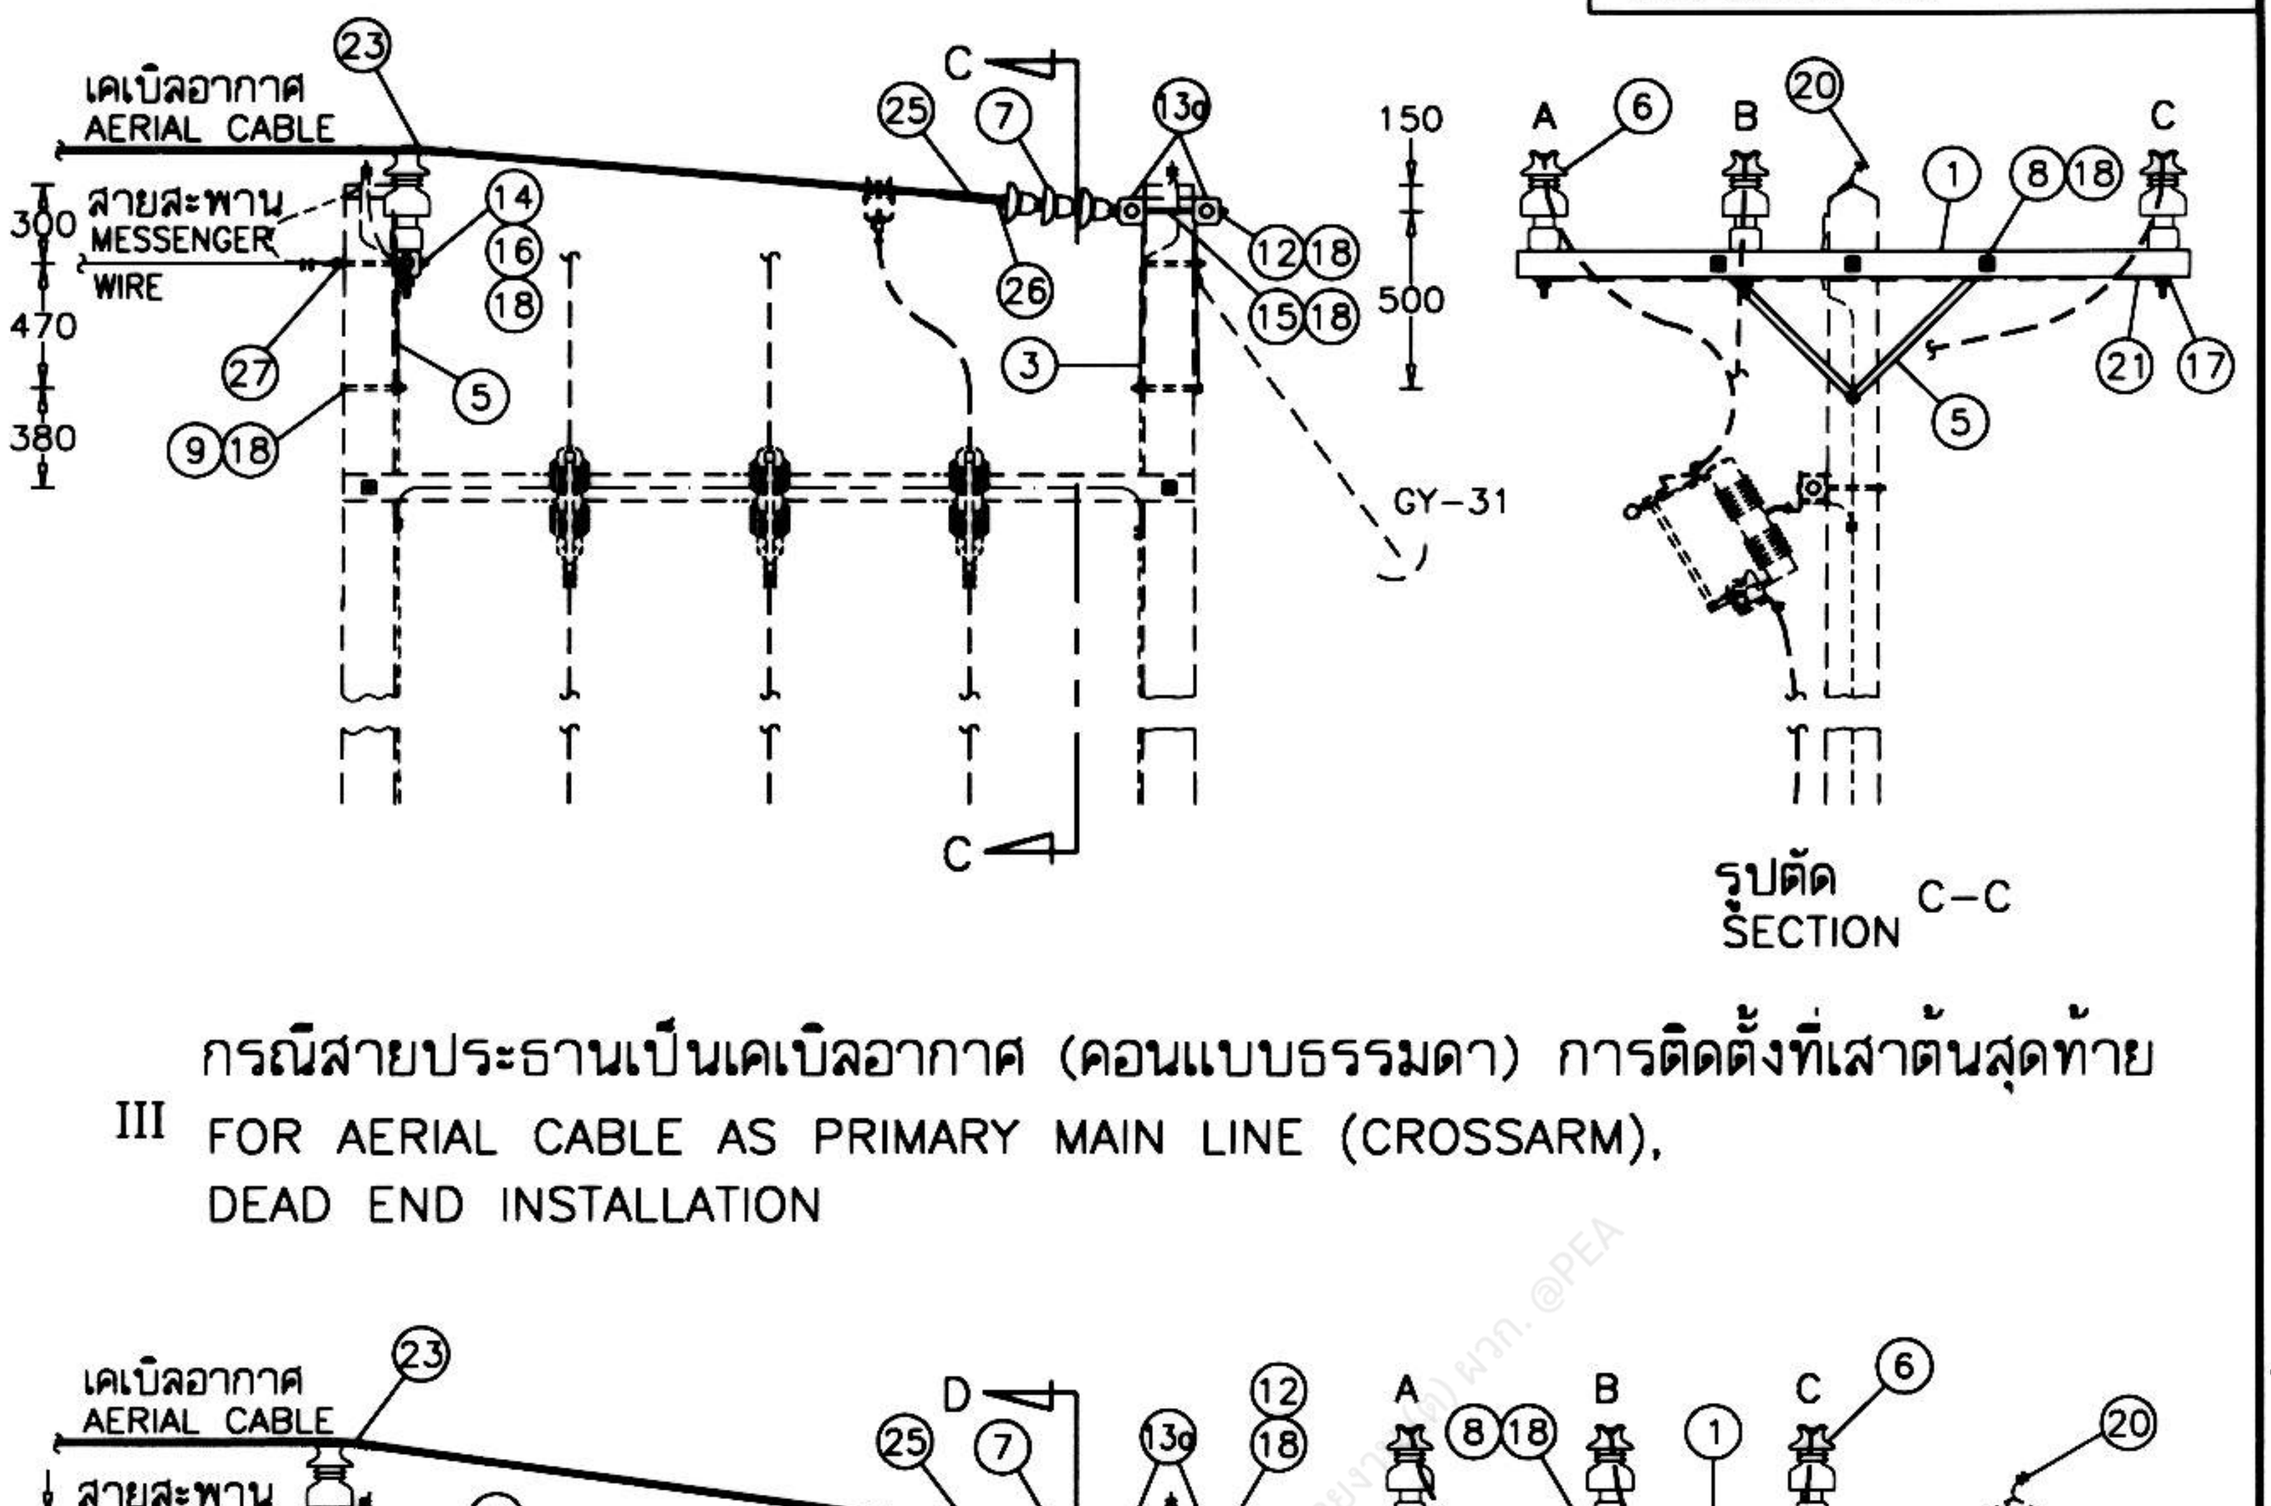

III กรณีสายประธานเป็นเคเบิลอากาศ (คอนแบบธรรมดา) การติดตั้งที่เสาต้นสุดท้าย
FOR AERIAL CABLE AS PRIMARY MAIN LINE (CROSSARM), DEAD END INSTALLATION

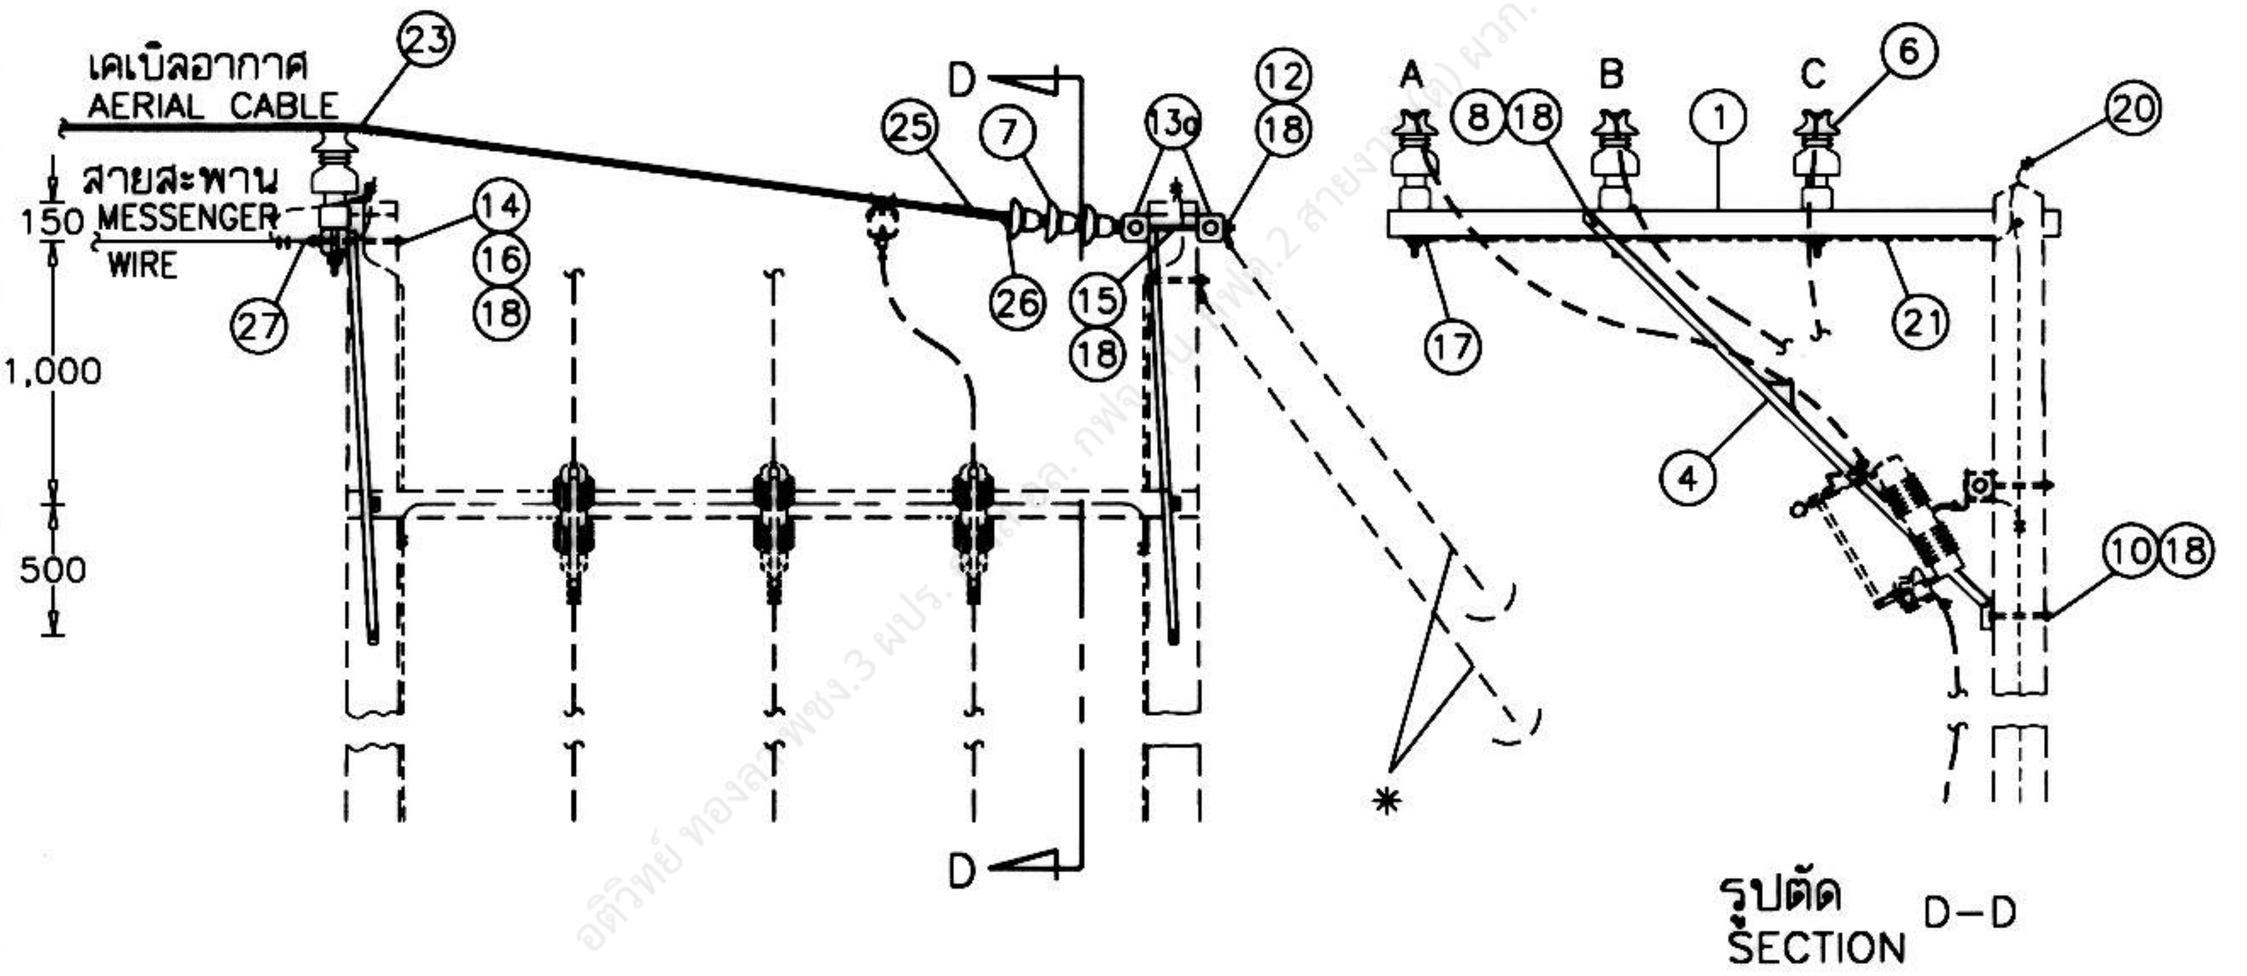


* การยึดโยงดูแบบเลขที่ SA4-015/39014 (การประกอบเลขที่ 3903 A)

IV กรณีสายประธานเป็นเคเบิลอากาศ (คอนแบบท้าวแขน) การติดตั้งที่เสาต้นสุดท้าย
FOR AERIAL CABLE AS PRIMARY MAIN LINE (ALLEY ARM), DEAD END INSTALLATION


กองมาตรฐานระบบไฟฟ้า ฝ่ายมาตรฐานและความปลอดภัย	การไฟฟ้าส่วนภูมิภาค	ใช้แทนแบบ .... SA1-015/21010, SA1-015/27015, SA1-015/31003, SA1-015/34032 ถูกแทนโดยแบบ ..... เขียนเสร็จวันที่ 4 พ.ค. 2544 แก้แบบวันที่ ..... มิติเป็น มิลลิเมตร มาตราส่วน 1 : 50
ผู้เขียน Supphakit Boonrung ผู้สำรวจ ..... วิศวกร ..... หัวหน้าแผนก ..... ผู้อำนวยการกอง ..... ผู้อำนวยการฝ่าย	ผู้ว่าการ ..... - 9 W.A. 2545	
รองผู้ว่าการวางแผนและพัฒนาระบบไฟฟ้า	การประกอบสายประธานบนนั่งร้านหม้อแปลง 3 เฟส ระบบ 33 kV MAIN LINE ASSEMBLY ON PLATFORM TRANSFORMER 3-PHASE, 33 kV	แบบเลขที่ SA4-015/44012 แผ่นที่ 2 ของจำนวน 11 แผ่น

การประกอบเลขที่ ASSEMBLY NO. 3719

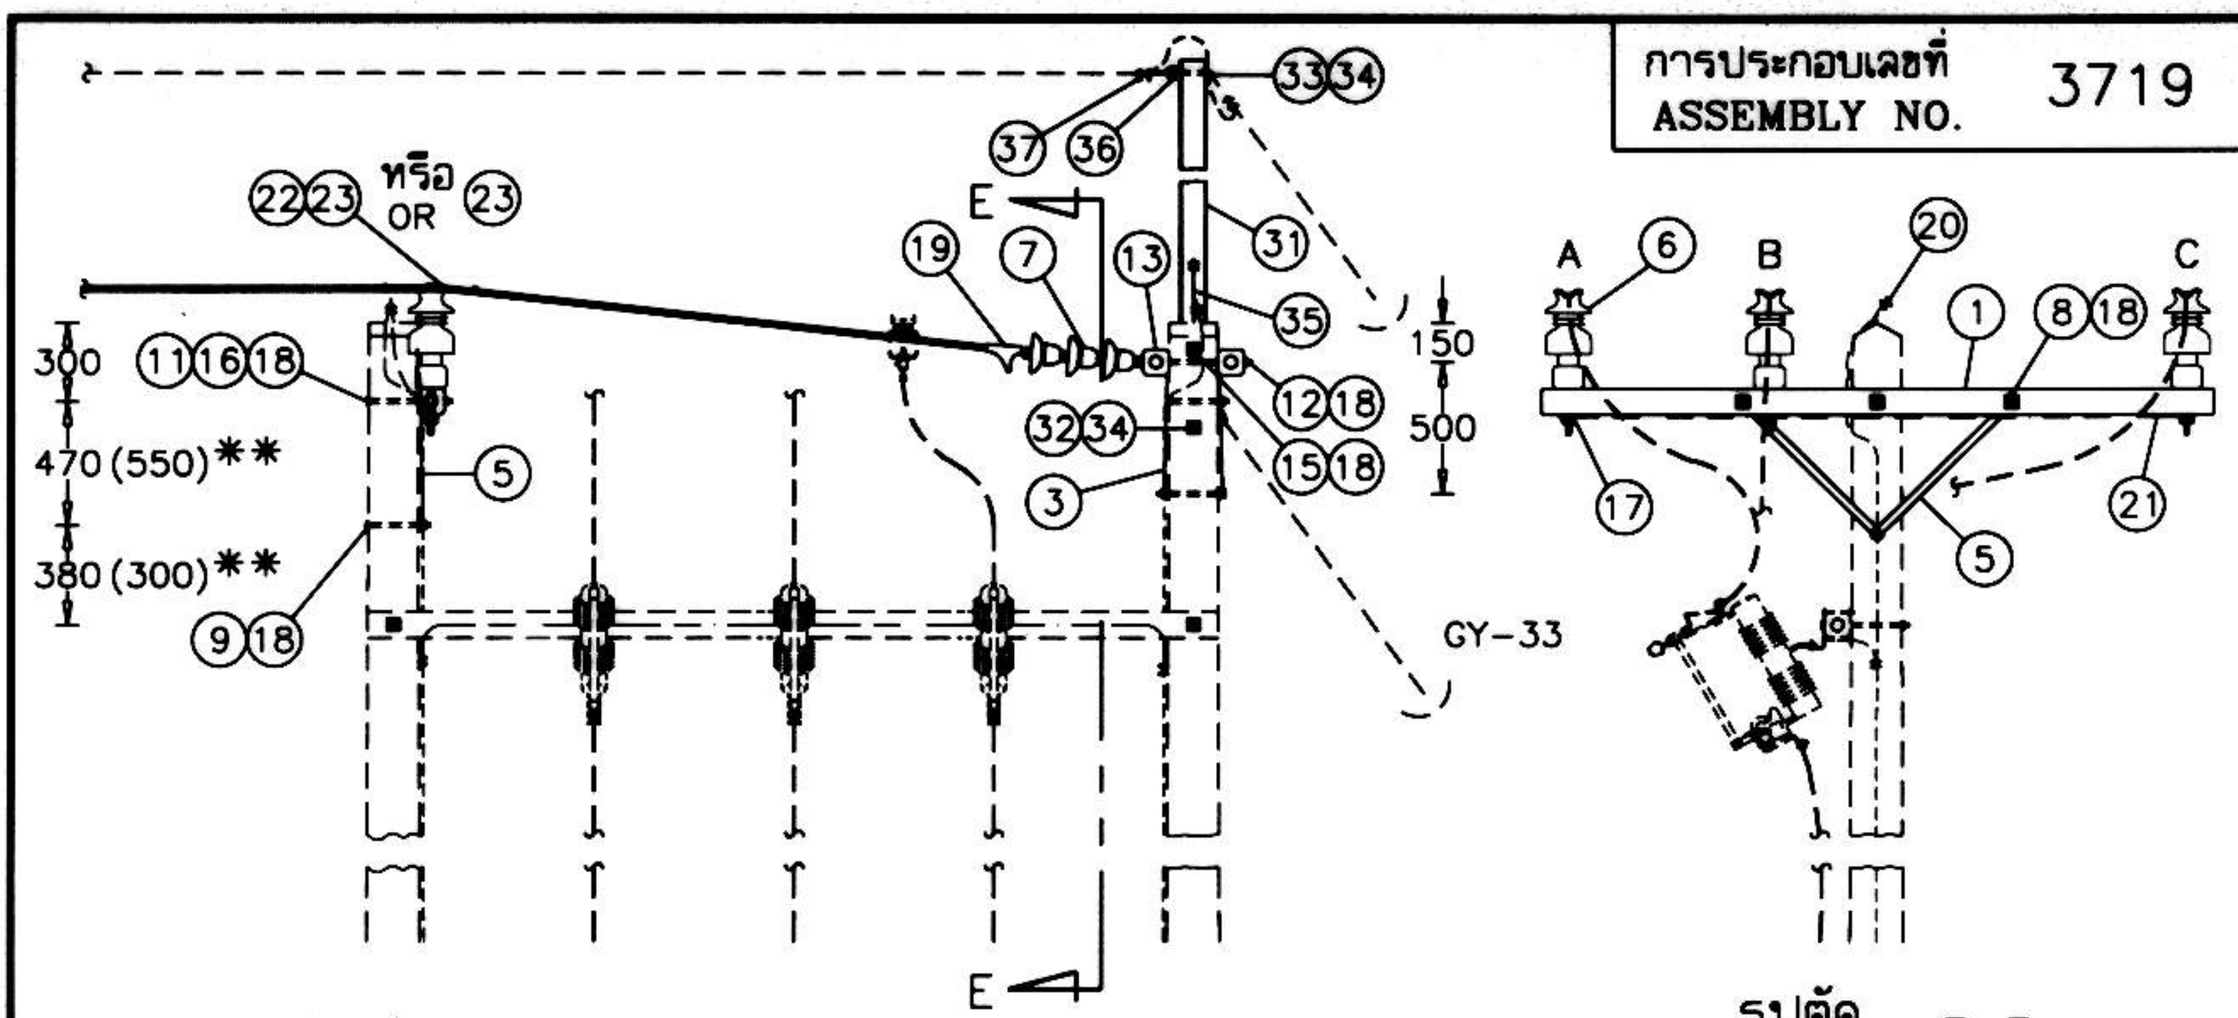

** สำหรับเหล็กประกับคอนขนาด 40x6x1,000 มม. (เจาะรูแบบพิเศษ)
FOR BRACE, FLAT FOR CROSS ARM, 40x6x1,000 mm (SPECIAL PUNCH)

V กรณีสายประธานเป็นอะลูมิเนียมเปลือย ทรือ สายอะลูมิเนียมหุ้มฉนวนแบบไม่เต็มพิกัด (คอนแบบธรรมดา) การติดตั้งที่เสาต้นสุดท้าย
FOR AI CONDUCTOR OR PIC AS PRIMARY MAIN LINE (CROSSARM), DEAD END INSTALLATION

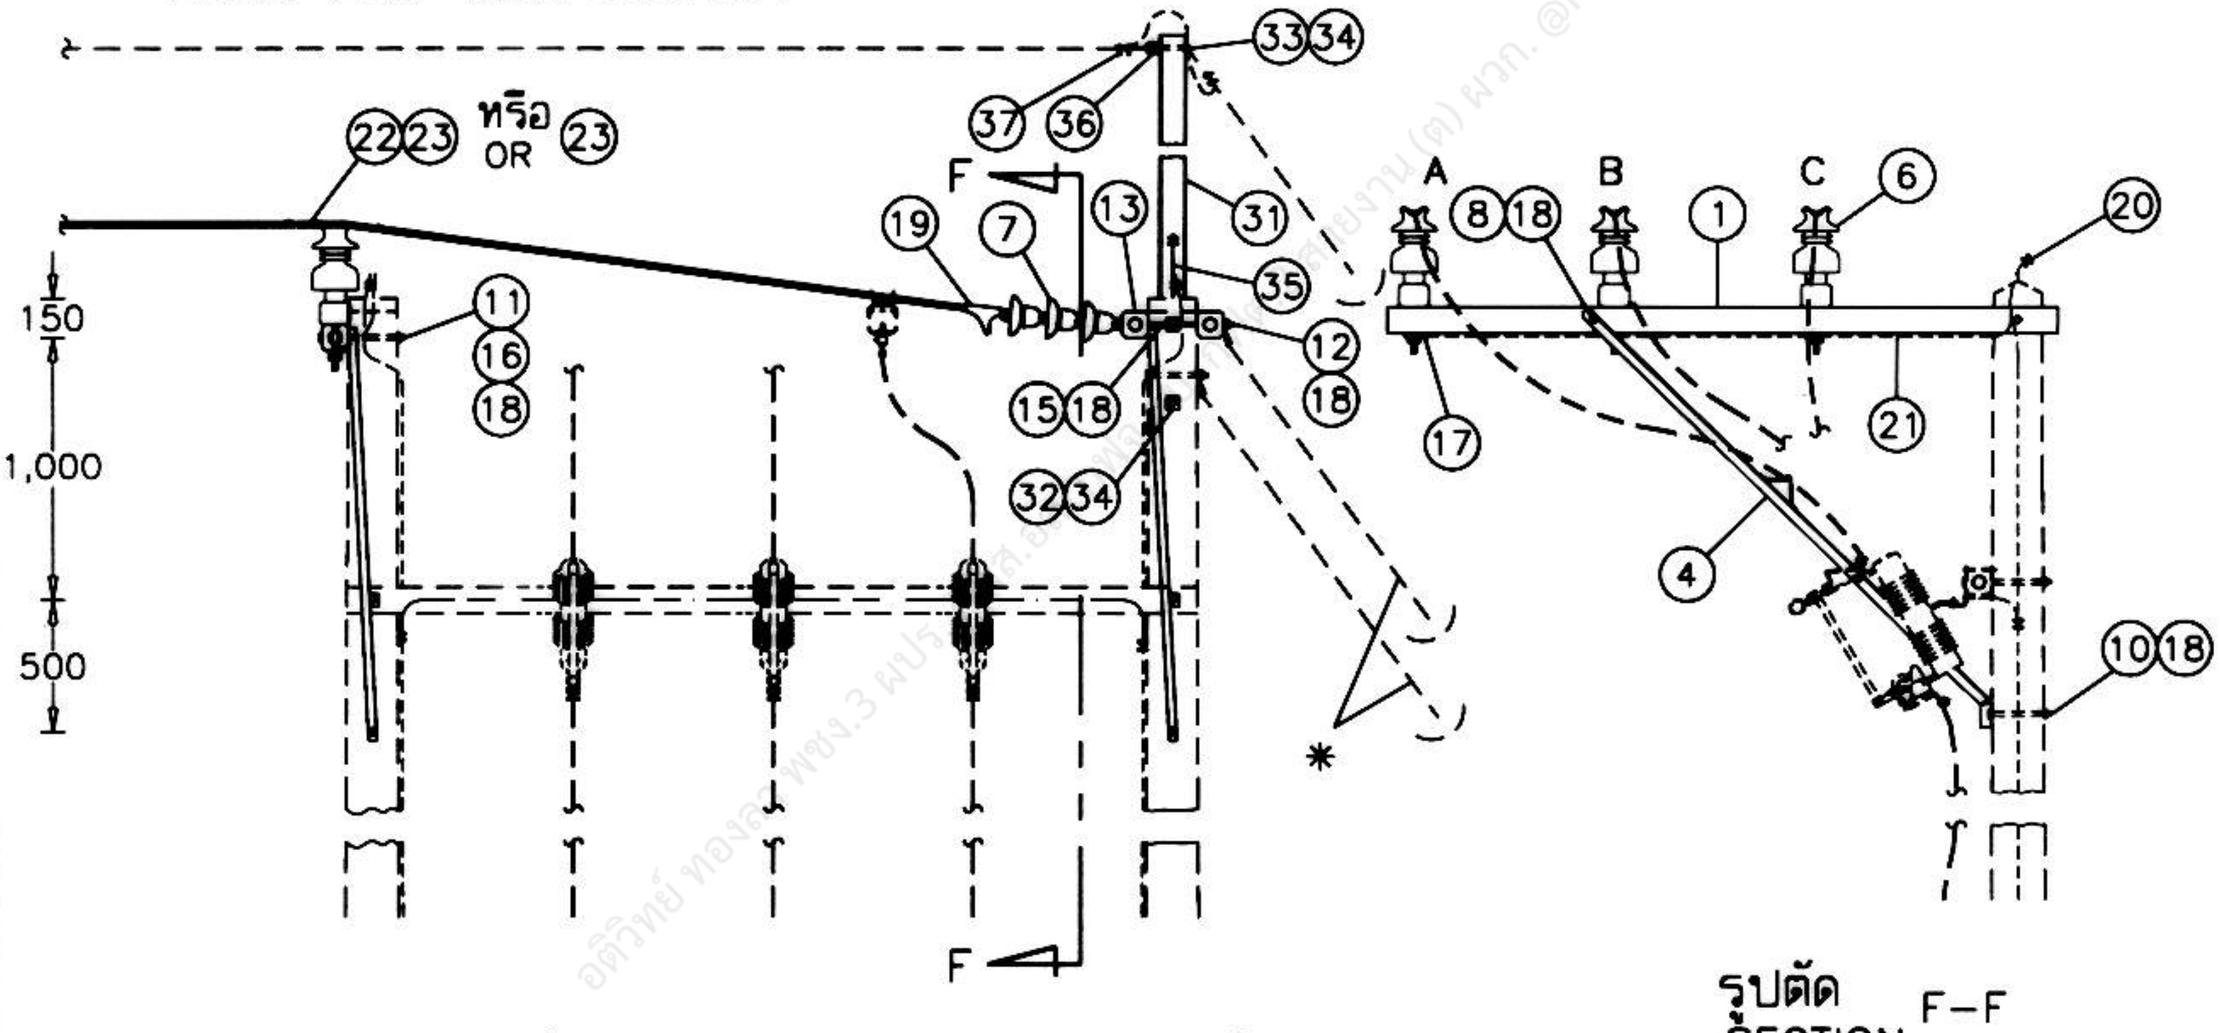



* การยึดโยงดูแบบเลขที่ SA4-015/39014 (การประกอบเลขที่ 3903 A)

VI กรณีสายประธานเป็นอะลูมิเนียมเปลือย ทรือ สายอะลูมิเนียมหุ้มฉนวนแบบไม่เต็มพิกัด (คอนแบบท้าวแขน) การติดตั้งที่เสาต้นสุดท้าย
FOR AI CONDUCTOR OR PIC AS PRIMARY MAIN LINE (ALLEY ARM), DEAD END INSTALLATION

กองมาตรฐานระบบไฟฟ้า ฝ่ายมาตรฐานและความปลอดภัย	การไฟฟ้าส่วนภูมิภาค	ใช้แทนแบบ SA1-015/21010, SA1-015/27015, SA1-015/31003, SA1-015/34032
ผู้เขียน Supphakit Boonruang ผู้สำรวจ ..... วิศวกร ..... หัวหน้าแผนก ..... ผู้อำนวยการกอง ..... ผู้อำนวยการฝ่าย	ผู้ว่าการ ..... 9 พ.ค. 2544	ถูกแทนโดยแบบ ..... เขียนเสร็จวันที่ 4 พ.ค. 2544 แก้แบบวันที่ ..... มิติเป็น มิลลิเมตร มาตราส่วน 1 : 50
รองผู้ว่าการวางแผนและพัฒนาระบบไฟฟ้า	การประกอบสายประธานบนนั่งร้านหม้อแปลง 3 เฟส ระบบ 33 kV MAIN LINE ASSEMBLY ON PLATFORM TRANSFORMER 3-PHASE, 33 kV	แบบเลขที่ SA4-015/44012 แผ่นที่ 3 ของจำนวน 11 แผ่น


การประกอบเลขที่ ASSEMBLY NO. 3719

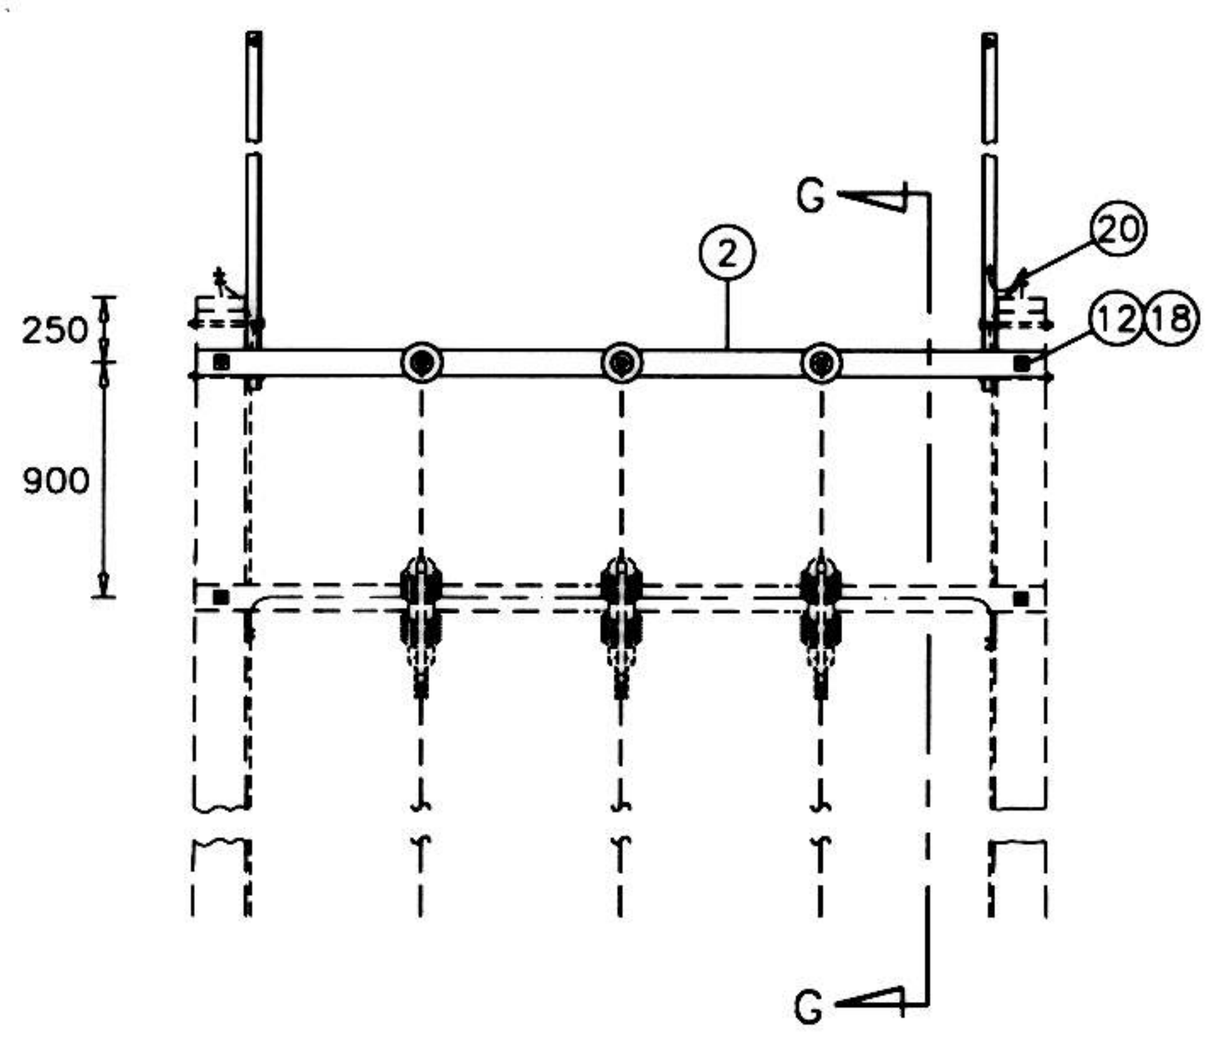

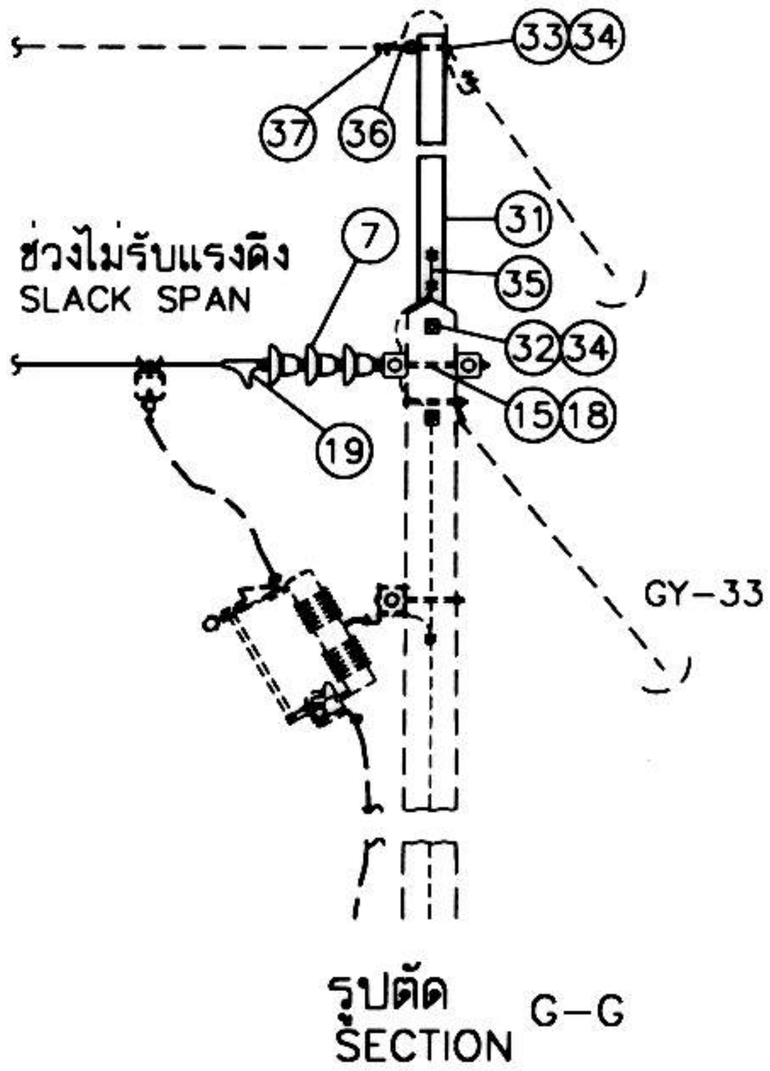


รูปตัด G–G
SECTION

กรณีนั่งร้านขวางแนวสายจำหน่าย การติดตั้งที่เสาต้นสุดท้าย
VII FOR PLACEMENT TRANSVERSE TO H.V. LINE DIRECTION, DEAD END INSTALLATION

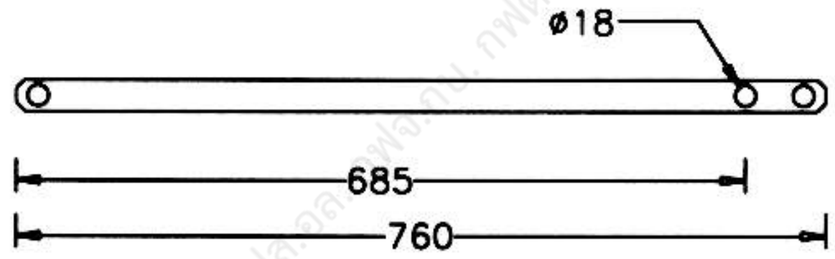


วัสดุลำดับที่ (5a)
MAT. ITEM

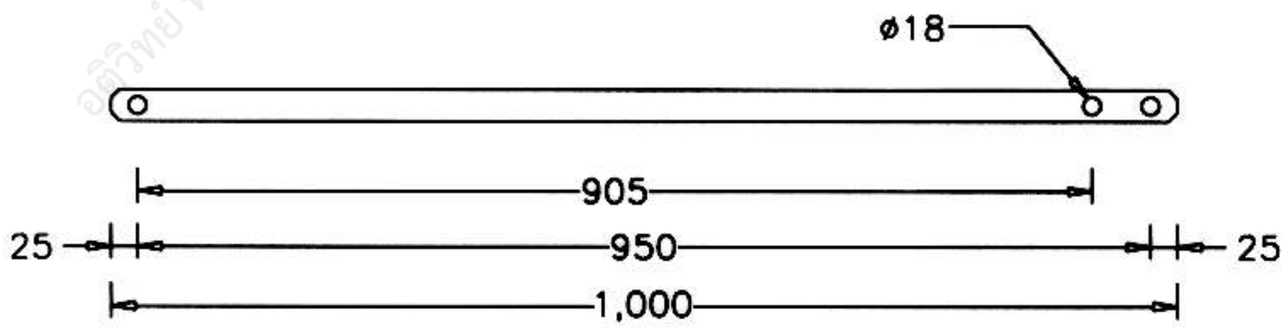


วัสดุลำดับที่ (5b)
MAT. ITEM

กองมาตรฐานระบบไฟฟ้า ฝ่ายมาตรฐานและความปลอดภัย	การไฟฟ้าส่วนภูมิภาค	ใช้แทนแบบ .... SA1-015/21010, SA1-015/27015, SA1-015/31003, SA1-015/34032 ถูกแทนโดยแบบ .....
ผู้เขียน Supphakit Boonruang ผู้สำรวจ Supphakit Boonruang วิศวกร ..... หัวหน้าแผนก ..... ผู้อำนวยการกอง ..... ผู้อำนวยการฝ่าย	ผู้ว่าการ ..... - 9 W.A. 2544	เขียนเสร็จวันที่ 4 พ.ค. 2544 แก้แบบวันที่ ..... มิติเป็น มิลลิเมตร มาตราส่วน 1 : 50
	การประกอบสายประธานบนนั่งร้านหม้อแปลง 3 เฟส ระบบ 33 kV	
รองผู้ว่าการวางแผนและพัฒนาระบบไฟฟ้า	MAIN LINE ASSEMBLY ON PLATFORM TRANSFORMER 3–PHASE, 33 kV	แบบเลขที่ SA4-015/44012 แผ่นที่ 4 ของจำนวน 11 แผ่น

การประกอบเลขที่ ASSEMBLY NO. 3719

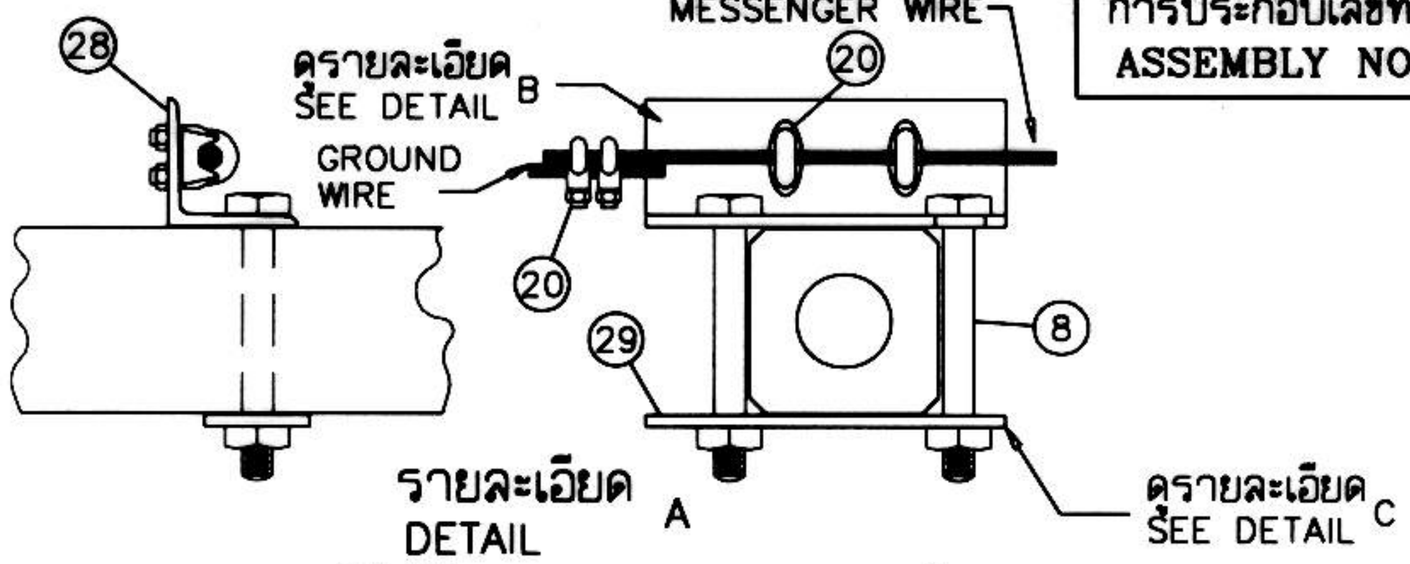


รายละเอียด A
DETAIL

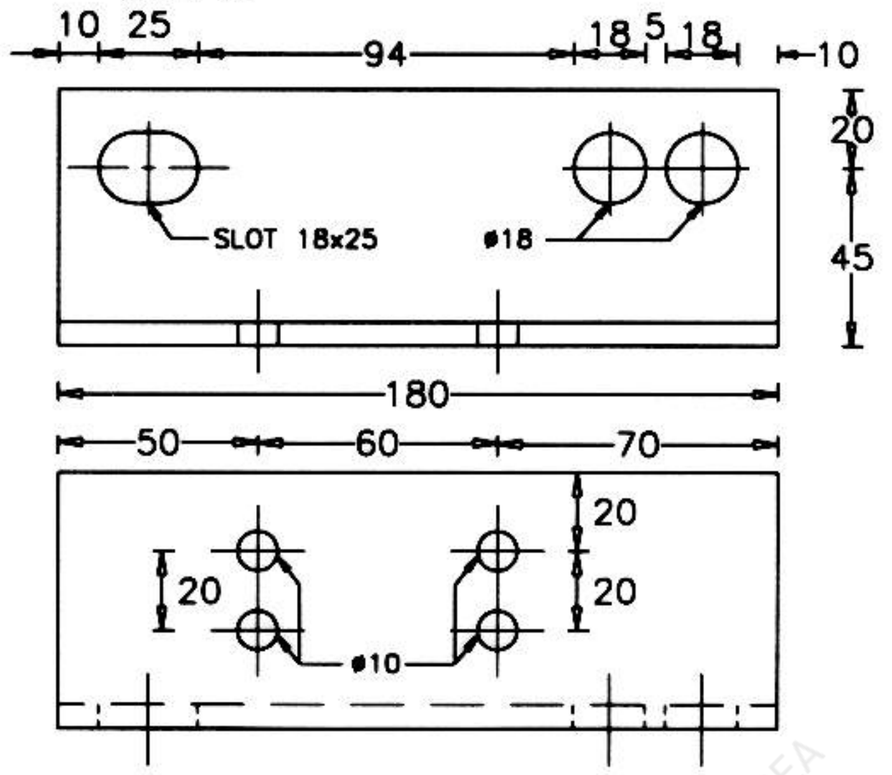


รายละเอียด B
DETAIL


เหล็กฉากขนาด 65x65x6 มม. ยาว 180 มม.
ANGLE, STEEL, 65x65x6 mm, 180 mm LONG
(อาจทำจากเหล็กฉากรับสายลอฟ้า วัสดุเลขที่ 01010002-5)
(MAY BE MADE FROM OHGW BAYONET, MAT.NO. 01010002-5)

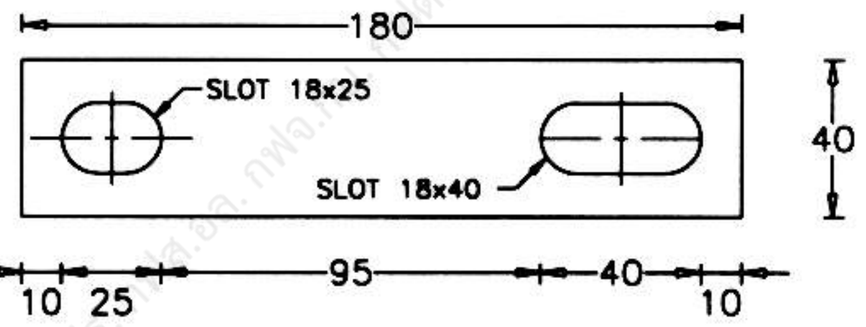

รายละเอียด C
DETAIL

แผ่นเหล็กขนาด 40x6 มม. ยาว 180 มม.
FLAT, STEEL, 40x6 mm, 180 mm LONG
(อาจทำจากเหล็กประกับคอน วัสดุเลขที่ 01200002)
(MAY BE MADE FROM BRACE, FLAT FOR CROSSARM, MAT.NO. 01200002)

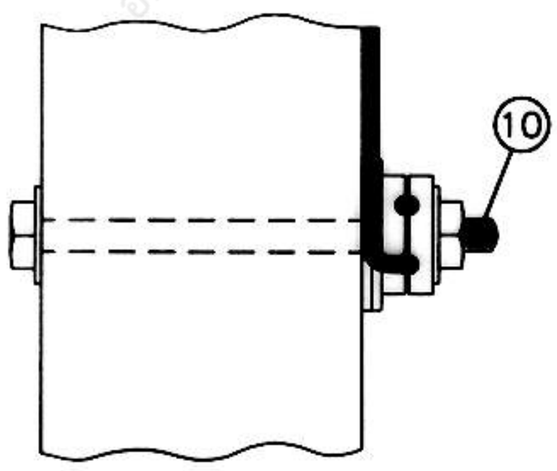

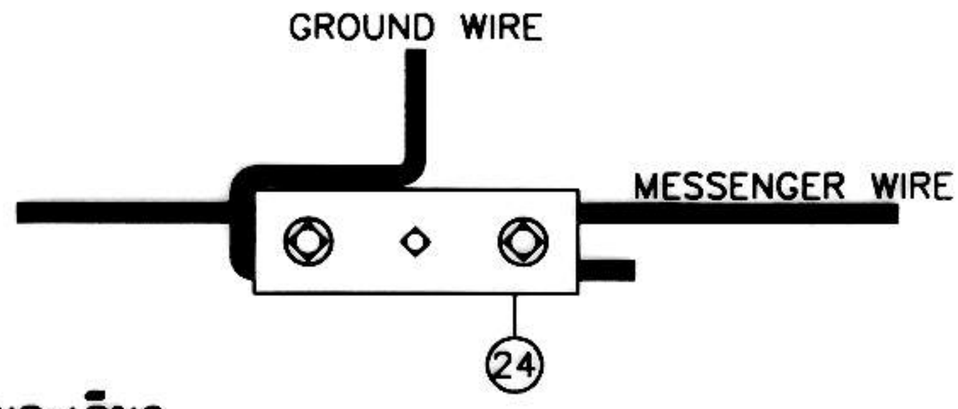

รายละเอียด D
DETAIL

กองมาตรฐานระบบไฟฟ้า ฝ่ายมาตรฐานและความปลอดภัย	การไฟฟ้าส่วนภูมิภาค	ใช้แทนแบบ .... SA1-015/21010, SA1-015/27015, SA1-015/31003, SA1-015/34032 ถูกแทนโดยแบบ .....
ผู้เขียน Supphakit Boonruang ผู้สำรวจ Supphakit Boonruang วิศวกร..... หัวหน้าแผนก..... ผู้อำนวยการกอง..... ผู้อำนวยการฝ่าย.....	ผู้ว่าการ..... 9 พ.ค. 2544	เขียนเสร็จวันที่ 4 พ.ค. 2544 แก้แบบวันที่ ..... มิติเป็น..... มาตราส่วน.....
	การประกอบสายประธานบนนั่งร้านหม้อแปลง 3 เฟส ระบบ 33 kV	
รองผู้ว่าการวางแผนและพัฒนาระบบไฟฟ้า	MAIN LINE ASSEMBLY ON PLATFORM TRANSFORMER 3-PHASE, 33 kV	แบบเลขที่ SA4-015/44012 แผ่นที่ 5 ของจำนวน 11 แผ่น

การประกอบเลขที่ ASSEMBLY NO. 3719

บัญชีวัสดุ
BILL OF MATERIAL

ลำดับที่ ITEM	รายละเอียด DESCRIPTION	จำนวน REQ'D I	II	III	IV	V	VI	VII	วัสดุเลขที่ MAT. NO.
A	การประกอบสายประธาน / MAIN LINE ASSEMBLY								
1a	คอน คอร. สปัน ขนาด 100x100x2,500 มม. CROSSARM, SPUN, PRESTRESSED CONCRETE, 100x100x2,500 mm	2	2	1	1	1	1	–	00110001
1b	คอน คอร. สปัน ขนาด 120x120x2,500 มม. CROSSARM, SPUN, PRESTRESSED CONCRETE, 120x120x2,500 mm	–	–	–	–	1	1	–	00110002
2	คาน คอร. สปัน ขนาด 100x100x3,200 มม. BEAM,SPUN PRESTRESSED CONCRETE, 100x100x3,200 mm	–	–	–	–	–	–	2	00210000
3a	เหล็กประกับคอน 30x6x760 มม. BRACE, FLAT FOR CROSSARM 30x6x760 mm	4	–	4	–	4	–	–	01200001
3b	เหล็กประกับคอน 40x6x1,000 มม. BRACE, FLAT FOR CROSSARM 40x6x1,000 mm	–	–	–	–	4	–	–	01200002
4a	เหล็กประกับคอนแบบท้าวแขน 40x40x5 มม. ยาว 2,120 มม. BRACE, ALLEY ARM, 40x40x5 mm, 2,120 mm LONG	–	2	–	2	–	2	–	01200004
4b	เหล็กประกับคอนแบบท้าวแขน 50x50x5 มม. ยาว 2,350 มม. BRACE, ALLEY ARM, 50x50x5 mm, 2,350 mm LONG	–	–	–	–	–	2	–	01200005
5a	เหล็กประกับคอน ขนาด 30x6x760 มม. (เจาะรูแบบพิเศษ) BRACE, FLAT FOR CROSSARM, 30x6x760 mm, (SPECIAL PUNCH)	–	–	2	–	2	–	–	01200001
5b	เหล็กประกับคอน ขนาด 40x6x1,000 (เจาะรูแบบพิเศษ) BRACE, FLAT FOR CROSSARM, 40x6x1,000 mm, (SPECIAL PUNCH)	–	–	–	–	2	–	–	01200001
6	ลูกถ้วยแท่งทรีอลูกถ้วยแท่งก้านตรง 33 kV ชนิดตามต้องการ INSULATOR, LINE POST TYPE OR PIN-POST TYPE, 33 kV, TYPE AS REQ.	6	6	3	3	3	3	–	03010003-4 03010103-4
7	ลูกถ้วยแขวน มอก. 354 แบบ ง. (แบบ 52-4) INSULATOR, SUSPENSION TYPE, TIS 354 TYPE D (CLASS 52-4)	–	–	9	9	9	9	9	03020002
8	สลักเกลียว M 16x130 มม. สำหรับ คอน คอร. สปัน ขนาด 100x100x2,500 มม. BOLT, MACHINE M 16x130 mm ; FOR CROSSARM, SPUN, PRESTRESSED CONCRETE, 100x100x2,500 mm	8	2	4	2	4	2	–	01110200
	สลักเกลียว M 16x170 มม. สำหรับ คอน คอร. สปัน ขนาด 120x120x2,500 มม. BOLT, MACHINE M 16x170 mm ; FOR CROSSARM, SPUN, PRESTRESSED CONCRETE, 120x120x2,500 mm								01110201
9	สลักเกลียว M 16x200 มม. สำหรับเสาคอนกรีต 12 ม. BOLT, MACHINE M 16x200 mm FOR 12 m CONCRETE POLE	2	–	2	–	2	–	–	01110202
	สลักเกลียว M 16x250 มม. สำหรับเสาคอนกรีต 12.20 ม. BOLT, MACHINE M 16x250 mm FOR 12.20 m CONCRETE POLE	2	–	2	–	2	–	–	01110203
10	สลักเกลียว M 16x250 มม. สำหรับเสาคอนกรีต 12 ม. BOLT, MACHINE M 16x250 mm FOR 12 m CONCRETE POLE	–	4	–	2	–	2	–	01110203
	สลักเกลียว M 16x300 มม. สำหรับเสาคอนกรีต 12.20 ม. BOLT, MACHINE M 16x300 mm FOR 12.20 m CONCRETE POLE	–	4	–	2	–	2	–	01110204

กองมาตรฐานระบบไฟฟ้า
ฝ่ายมาตรฐานและความปลอดภัย

ผู้เขียน Supphakit Boonruang
ผู้สำรวจ Supphakit Boonruang
วิศวกร .....
หัวหน้าแผนก .....
ผู้อำนวยการกอง .....
ผู้อำนวยการฝ่าย .....

รองผู้ว่าการวางแผน
และพัฒนาระบบไฟฟ้า
.....

การไฟฟ้าส่วนภูมิภาค

ผู้ว่าการ ..... - 9 พ.ค. 2544

การประกอบสายประธานบนนั่งร้านหม้อแปลง
3 เฟส ระบบ 33 kV

MAIN LINE ASSEMBLY ON PLATFORM TRANSFORMER
3-PHASE, 33 kV

ใช้แทนแบบ SA1-015/21010, SA1-015/27015, SA1-015/31003, SA1-015/34032
ถูกแทนโดยแบบ .....
เขียนเสร็จวันที่ 4 พ.ค. 2544
แก้แบบวันที่ .....
มิติเป็น .....
มาตราส่วน .....

แบบเลขที่ SA4-015/44012
แผ่นที่ 6 ของจำนวน 11 แผ่น

การประกอบเลขที่ ASSEMBLY NO. 3719

บัญชีวัสดุ
BILL OF MATERIAL

ลำดับที่ ITEM	รายละเอียด DESCRIPTION	จำนวน REQ'D I	II	III	IV	V	VI	VII	วัสดุเลขที่ MAT. NO.
A	การประกอบสายประธาน (ต่อ) / MAIN LINE ASSEMBLY (CONT.)								
11a	สลักเกลียว M 16x300 มม. สำหรับเสาคอนกรีต 12 ม. BOLT, MACHINE M 16x300 mm FOR 12 m CONCRETE POLE	2	2	–	–	1	1	–	01110204
	สลักเกลียว M 16x350 มม. สำหรับเสาคอนกรีต 12.20 ม. BOLT, MACHINE M 16x350 mm FOR 12.20 m CONCRETE POLE	2	2	–	–	1	1	–	01110205
11b	สลักเกลียว M 16x350 มม. สำหรับเสาคอนกรีต 12 ม. BOLT, MACHINE M 16x350 mm FOR 12 m CONCRETE POLE	–	–	–	–	1	1	–	01110205
	สลักเกลียว M 16x400 มม. สำหรับเสาคอนกรีต 12.20 ม. BOLT, MACHINE M 16x400 mm FOR 12.20 m CONCRETE POLE	–	–	–	–	1	1	–	01110206
12	สลักเกลียว M 16x450 มม. สำหรับเสาคอนกรีต 12 ม. BOLT, MACHINE M 16x450 mm FOR 12 m CONCRETE POLE	–	–	1	1	1	1	2	01110207
	สลักเกลียว M 16x500 มม. สำหรับเสาคอนกรีต 12.20 ม. BOLT, MACHINE M 16x500 mm FOR 12.20 m CONCRETE POLE	–	–	1	1	1	1	2	01110208
13a	คอน คอร. สปัน ขนาด 120x120x2,500 มม. CROSSARM, SPUN, PRESTRESSED CONCRETE, 120x120x2,500 mm	–	–	2	2	2	2	–	00110004
13b	คอน คอร. สปัน ขนาด 120x120x3,000 มม. CROSSARM, SPUN, PRESTRESSED CONCRETE, 120x120x3,000 mm	–	–	–	–	2	2	–	00110005
14	สลักเกลียว M 16x300 มม. พร้อมนัทรูปทวง M16 DIN 582 สำหรับเสาคอนกรีต 12 ม. BOLT, MACHINE M 16x300 mm WITH NUT, EYE M 16 DIN 582 FOR 12 m CONCRETE POLE	–	–	1	1	–	–	–	01110204 & 01180001
	สลักเกลียว M 16x350 มม. พร้อมนัทรูปทวง M16 DIN 582 สำหรับเสาคอนกรีต 12.20 ม. BOLT, MACHINE M 16x350 mm WITH NUT, EYE M 16 DIN 582 FOR 12.20 m CONCRETE POLE	–	–	1	1	–	–	–	01110205 & 01180001
15	สลักเกลียวท่วงกลม M 16x450 มม. สำหรับเสาคอนกรีต 12.00 ม. BOLT, DOUBLE ARMING,ROUND EYE, M 16x450 mm FOR 12 m CONCRETE POLE	–	–	3	3	3	3	3	01130001
	สลักเกลียวท่วงกลม M 16x500 มม. สำหรับเสาคอนกรีต 12.20 ม. BOLT, DOUBLE ARMING,ROUND EYE, M 16x500 mm FOR 12.20 m CONCRETE POLE	–	–	3	3	3	3	3	01130002
16	แหวนรองแบบสปริง M 16 มอก. 258 WASHER,LOCK, SPRING M 16 TIS 258	2	2	1	1	1	1	–	01180301
17	แหวนสี่เหลี่ยมโค้ง 60x60x5 มม. รู Ø 22 มม. WASHER, SQUARE, CURVE 60x60x5 mm, HOLE ø 22 mm	6	6	3	3	3	3	–	01180201
18	แหวนสี่เหลี่ยมแบน 52x52x4.5 มม. รู ø 18 มม. มอก. 258 WASHER, SQUARE, FLAT 52x52x4.5 mm HOLE ø18 mm TIS 258	19	19	22	19	19	19	16	01180100
19	สเตรนแคล้มป์ สำหรับสายอะลูมิเนียม สายอะลูมิเนียมเจือ และสายอะลูมิเนียมแกนเหล็ก ขนาดตามต้องการ CLAMP, STRAIN FOR Al, Al-ALLOY, AND ACSR, SIZE AS REQUIRED	–	–	–	–	3	3	3	03110000-4 03110101

กองมาตรฐานระบบไฟฟ้า
ฝ่ายมาตรฐานและความปลอดภัย

ผู้เขียน Supphakit Boonruang
ผู้สำรวจ Supphakit Boonruang
วิศวกร.....
หัวหน้าแผนก.....
ผู้อำนวยการกอง.....
ผู้อำนวยการฝ่าย.....

รองผู้ว่าการวางแผนและพัฒนาระบบไฟฟ้า
.....

การไฟฟ้าส่วนภูมิภาค

ผู้ว่าการ..... 9 พ.ค. 2544

การประกอบสายประธานบนนั่งร้านหม้อแปลง
3 เฟส ระบบ 33 kV

MAIN LINE ASSEMBLY ON PLATFORM TRANSFORMER
3-PHASE, 33 kV

ใช้แทนแบบ SA1-015/21010, SA1-015/27015, SA1-015/31003, SA1-015/34032
ถูกแทนโดยแบบ .....
เขียนเสร็จวันที่ 4 พ.ค. 2544
แก้แบบวันที่ .....
มิติเป็น.....
มาตราส่วน.....

แบบเลขที่ SA4-015/44012
แผ่นที่ 7 ของจำนวน 11 แผ่น

การประกอบเลขที่ ASSEMBLY NO. 3719

บัญชีวัสดุ
BILL OF MATERIAL

ลำดับที่ ITEM	รายละเอียด DESCRIPTION	จำนวน REQ'D I	II	III	IV	V	VI	VII	วัสดุเลขที่ MAT. NO.
A	การประกอบสายประธาน (ต่อ) / MAIN LINE ASSEMBLY (CONT.)								
20	ยูแคล้มป์ สลัก 1 ตัว M 8 CLAMP, SINGLE U-BOLT,M 8	14	14	6	6	4	4	4	01230000
21	ลวดเหล็กกลม Ø 4 มม. เส้นเดี่ยว (มอก. 71) น้ำหนักประมาณ 0.1 กก/ม. WIRE, STEEL SOLID DIA 4.0 mm (TIS.71), WEIGHT 0.1 kg/m	6 ม.	6 ม.	3 ม.	3 ม.	3 ม.	3 ม.	–	01100000
22	ลวดอะลูมิเนียมแบน 1x10 มม. ความยาวตามต้องการ ARMOUR TAPE, Al 1x10 mm, LENGTH AS REQUIRED	ม.	ม.	ม.	ม.	ม.	ม.	ม.	02200000
23	ลวดอะลูมิเนียมกลม ขนาด Ø 4 มม. ความยาวตามต้องการ TIE WIRE, Al ø 4 mm, LENGTH AS REQUIRED	ม.	ม.	ม.	ม.	ม.	ม.	ม.	02200002
24	แคล้มป์แขวนเคเบิล หรือกายแคล้มป์ สลัก 3 ตัว CLAMP, CABLE SUSPENSION OR CLAMP, GUY TRIPLE BOLT	–	2	–	–	–	–	–	02440100 02440102
25	ปรีฟอร์มเข้าปลายสายเคเบิลอากาศ 33 kV ขนาดตามต้องการ PREFORMED DEAD END, FOR AERIAL CABLE 33 kV, SIZE AS REQUIRED	–	–	3	3	–	–	–	02260104 02260200–1
26	ทิมเบิลเคลวิส สำหรับปรีฟอร์มเข้าปลายสาย CLEVIS, THIMBLE, FOR PREFORMED DEAD END	–	–	3	3	–	–	–	03140011
27	กายทิมเบิล สำหรับสายยิดโยง 50-95 ต.มม. THIMBLE,GUY, FOR STEEL WIRE 50–95 mm^2	–	–	1	1	–	–	–	01210304
28	เหล็กฉาก ขนาด 65x65x6 มม. ยาว 180 มม. ANGLE, STEEL, 65x65x6 mm, 180 mm LONG	2	–	–	–	–	–	–	
29	แผ่นเหล็ก ขนาด 40x6 มม. ยาว 180 มม. FLAT, STEEL, 40x6 mm, 180 mm LONG	2	–	–	–	–	–	–	
30									

อดิวิทย์ ทองลา พชง.3 ผปร. กฟส.อ.

กองมาตรฐานระบบไฟฟ้า
ฝ่ายมาตรฐานและความปลอดภัย

ผู้เขียน Suphakit Boonruang
ผู้สำรวจ Suphakit Boonruang
วิศวกร .....
หัวหน้าแผนก .....
ผู้อำนวยการกอง .....
ผู้อำนวยการฝ่าย .....

รองผู้ว่าการวางแผนและพัฒนาระบบไฟฟ้า
.....

การไฟฟ้าส่วนภูมิภาค

ผู้ว่าการ ..... – 9 พ.ค. 2544

การประกอบสายประธานบนนั่งร้านหม้อแปลง
3 เฟส ระบบ 33 kV

MAIN LINE ASSEMBLY ON PLATFORM TRANSFORMER
3–PHASE, 33 kV

ใช้แทนแบบ SA1-015/21010, SA1-015/27015, SA1-015/31003, SA1-015/34032
ถูกแทนโดยแบบ .....
เขียนเสร็จวันที่ 4 พ.ค. 2544
แก้แบบวันที่ .....
มิติเป็น .....
มาตราส่วน .....

แบบเลขที่ SA4-015/44012
แผ่นที่ 8 ของจำนวน 11 แผ่น

การประกอบเลขที่ ASSEMBLY NO. 3719

บัญชีวัสดุ
BILL OF MATERIAL

ลำดับที่ ITEM	รายละเอียด DESCRIPTION	จำนวน REQ'D I	II	III	IV	V	VI	VII	วัสดุเลขที่ MAT. NO.
B	การประกอบที่รับสายล่อฟ้า / OVERHEAD GROUND WIRE BAYONET ASSEMBLY								
31	เหล็กรูปรางน้ำรับสายล่อฟ้า ต้นเข้าปลายสาย ขนาด 100x50x5 มม. ยาว 2,250 มม. OVERHEAD GROUND WIRE DEAD END BAYONET, CHANNEL STEEL, 100x50x5 mm, 2,250 mm LONG	–	–	–	–	1	1	2	01000100
32	สลักเกลียว M 16x250 มม. BOLT, MACHINE M 16x250 mm	–	–	–	–	2	2	4	01110203
33	สลักห่วงกลม M 16x200 มม. BOLT, ROUND EYE, M 16x200 mm	–	–	–	–	1	1	2	01140001
34	แหวนสี่เหลี่ยมแบน 52x52x4.5 มม. รู ø 18 มม. มอก. 258 WASHER, SQUARE, FLAT 52x52x4.5 mm HOLE ø18 mm TIS 258	–	–	–	–	4	4	8	01180100
35	ลวดเหล็กตีเกลียว 25 ต.มม. มอก. 404 WIRE, STEEL STRANDED 25 mm² TIS 404	–	–	–	–	0.5 ม. m	0.5 ม. m	1 ม. m	01100002
36	กายทิมเบิล สำหรับสายยึดโยง 50–95 ต.มม. THIMBLE, GUY, FOR STEEL WIRE 50–95 mm²	–	–	–	–	1	1	2	01210304
37	ยูแคล้มป์ สลัก 1 ตัว M 8 (ไวร์ โร้ป คลิ้ฟ) CLAMP, SINGLE U-BOLT, M 8 (WIRE ROPE CLIP)	–	–	–	–	5	5	8	01230000

a สำหรับสายประธานเป็นเคเบิลอากาศ และสายอะลูมิเนียมทุ้มฉนวนแบบไม่เต็มพิกัด

b สำหรับสายประธานเป็นสายอะลูมิเนียมเปลือย

a FOR MAIN LINE AS AERIAL CABLE AND PIC.

b FOR MAIN LINE AS AI BARE CONDUCTOR.

	แบบอ้างอิง REFERENCE DRAWING	แบบเลขที่ DWG.No.	การประกอบเลขที่ ASSEMBLY No.
1	การติดตั้งหม้อแปลง 3 เฟส ระบบ 22 kV ขนาด 50–500 kVA บนนั่งร้าน 3–PHASE TRANSFORMER INSTALLATION 22 kV, 50–500 kVA ON PLATFORM	SA4–015/44011	3718
2	การติดตั้งเคเบิลอากาศระบบ 22 kV สำหรับเข้าปลายสายเสาต้นสุดท้าย AERIAL CABLE INSTALLATION, 22 kV FOR DEAD END POLE CONSTRUCTION	SA4–015/39014	3903 A
3	นั่งร้านหม้อแปลง การจัดวางตำแหน่งที่ตั้ง TRANSFORMER STATION, LOCATION OF STATION NETWORK	Z93/12015	8502
4	การใช้ลูกถ้วยยึดโยง STRAIN INSULATOR APPLICATION	SA1–015/20023	8408

กองมาตรฐานระบบไฟฟ้า
ฝ่ายมาตรฐานและความปลอดภัย

ผู้เขียน Supphakit Boonruang
ผู้สำรวจ Supphakit Boonruang
วิศวกร.....
หัวหน้าแผนก.....
ผู้อำนวยการกอง.....
ผู้อำนวยการฝ่าย.....

รองผู้ว่าการวางแผนและพัฒนาระบบไฟฟ้า
.....

การไฟฟ้าส่วนภูมิภาค

ผู้ว่าการ..... - 9 พ.ค. 2544

การประกอบสายประธานบนนั่งร้านหม้อแปลง
3 เฟส ระบบ 33 kV

MAIN LINE ASSEMBLY ON PLATFORM TRANSFORMER
3–PHASE, 33 kV

ใช้แทนแบบ SA1–015/21010, SA1–015/27015, SA1–015/31003, SA1–015/34032
ถูกแทนโดยแบบ .....
เขียนเสร็จวันที่ 4 พ.ค. 2544
แก้แบบวันที่ .....
มิติเป็น.....
มาตราส่วน.....

แบบเลขที่ SA4–015/44012
แผ่นที่ 9 ของจำนวน 11 แผ่น

การประกอบเลขที่ ASSEMBLY NO. 3719

ข้อแนะนำการใช้งาน
RECOMMENDATIONS

สายไฟฟ้า CONDUCTOR		เสาคอนกรีต 12 เมตร 12 m CONCRETE POLE			
		กรณีไม่มีสายยึดโยง WITHOUT GUY		กรณีมีสายยึดโยง WITH GUY	
ชนิด TYPE	ขนาด (ต.มม.) SIZE (mm^2)	ระยะระหว่างเสาสูงสุด (ม.) MAX. SPAN LENGTH (m)	ระยะหย่อนยานต่ำสุดของสายทุกเส้น (ม.) MAX. SAG OF ALL COND.(m)	ระยะระหว่างเสาสูงสุด (ม.) MAX. SPAN LENGTH (m)	ระยะหย่อนยานต่ำสุดของสายทุกเส้น (ม.) MAX. SAG OF ALL COND.(m)
อะลูมิเนียมเปลือย ALUMINIUM อะลูมิเนียมเจือ ALUMINIUM–ALLOY	50	50	1.0	–	–
	95, 120	40	1.0	80	1.2
	185	25	0.5	80	1.2
ทุ้มฉนวนแบบไม่เต็มพิกัด PIC	50	50	1.4	–	–
	95	40	1.2	–	–
	120, 185	20	0.4	40	0.7
เคเบิลอากาศ SAC	50, 95	20	0.4	40	1
	120, 185	20	0.5	40	1

อดิวิทย์ ทองลา พชง.3 ผปร. กฟส.อด. กฟจ.กบ. กฟภ.2 สายงาน (ค) ผกก. @PEA

กองมาตรฐานระบบไฟฟ้า
ฝ่ายมาตรฐานและความปลอดภัย

การไฟฟ้าส่วนภูมิภาค

ผู้เขียน Supphakit Boonruang
ผู้สำรวจ Supphakit Boonruang
วิศวกร.....
หัวหน้าแผนก.....
ผู้อำนวยการกอง.....
ผู้อำนวยการฝ่าย.....

ผู้ว่าการ..... 9 พ.ค. 2544

รองผู้ว่าการวางแผนและพัฒนาระบบไฟฟ้า
.....

การประกอบสายประธานบนนั่งร้านหม้อแปลง 3 เฟส ระบบ 33 kV

MAIN LINE ASSEMBLY ON PLATFORM TRANSFORMER
3–PHASE, 33 kV

ใช้แทนแบบ SA1-015/21010, SA1-015/27015, SA1-015/31003, SA1-015/34032
ถูกแทนโดยแบบ .....
เขียนเสร็จวันที่ 4 พ.ค. 2544
แก้แบบวันที่ .....
มิติเป็น.....
มาตราส่วน.....

แบบเลขที่ SA4-015/44012
แผ่นที่ 10 ของจำนวน 11 แผ่น

การประกอบเลขที่ ASSEMBLY NO. 3719

สายไพฟ้า CONDUCTOR		เสาคอนกรีต 12.20 เมตร 12.20 m CONCRETE POLE			
		กรณีไม่มีสายยึดโยง WITHOUT GUY		กรณีมีสายยึดโยง WITH GUY	
ชนิด TYPE	ขนาด (ต.มม.) SIZE (mm^2)	ระยะระหว่างเสาสูงสุด (ม.) MAX. SPAN LENGTH (m)	ระยะหย่อนยานต่ำสุดของสายทุกเส้น (ม.) MAX. SAG OF ALL COND.(m)	ระยะระหว่างเสาสูงสุด (ม.) MAX. SPAN LENGTH (m)	ระยะหย่อนยานต่ำสุดของสายทุกเส้น (ม.) MAX. SAG OF ALL COND.(m)
อะลูมิเนียมเปลือย ALUMINIUM อะลูมิเนียมเจือ ALUMINIUM-ALLOY	50	50	0.4	–	–
	95, 120	50	0.6	80	1.2
	185	50	1.0	80	1.2
หุ้มฉนวนแบบไม่เต็มพิกัด PIC	50	50	1.4	–	–
	95	40	0.5	–	–
	120, 185	40	0.7	–	–
เคเบิลอากาศ SAC	50, 95	40	0.8	–	–
	120, 185	40	1.0	–	–

อดิวัฒย์ ทองลา พชง.3 ผปร. กฟส.อด. กฟจ.กบ. กฟต.2 สายงาน (ค)ผวก. @PEA

กองมาตรฐานระบบไฟฟ้า
ฝ่ายมาตรฐานและความปลอดภัย

ผู้เขียน Supphakit Boonruang
ผู้สำรวจ Supphakit Boonruang
วิศวกร.....
หัวหน้าแผนก.....
ผู้อำนวยการกอง.....
ผู้อำนวยการฝ่าย.....

รองผู้ว่าการวางแผนและพัฒนาระบบไฟฟ้า
.....

การไฟฟ้าส่วนภูมิภาค

ผู้ว่าการ..... - 9 พ.ค. 2544

การประกอบสายประธานบนนั่งร้านหม้อแปลง
3 เฟส ระบบ 33 kV

MAIN LINE ASSEMBLY ON PLATFORM TRANSFORMER
3-PHASE, 33 kV

ใช้แทนแบบ SA1-015/21010, SA1-015/27015, SA1-015/31003, SA1-015/34032
ถูกแทนโดยแบบ .....
เขียนเสร็จวันที่ 4 พ.ค. 2544
แก้แบบวันที่ .....
มิติเป็น.....
มาตราส่วน.....

แบบเลขที่ SA4-015/44012
แผ่นที่ 1.1 ของจำนวน 1.1 แผ่น