การประกอบเลขที่ ASSEMBLY NO.	5 2 8 4

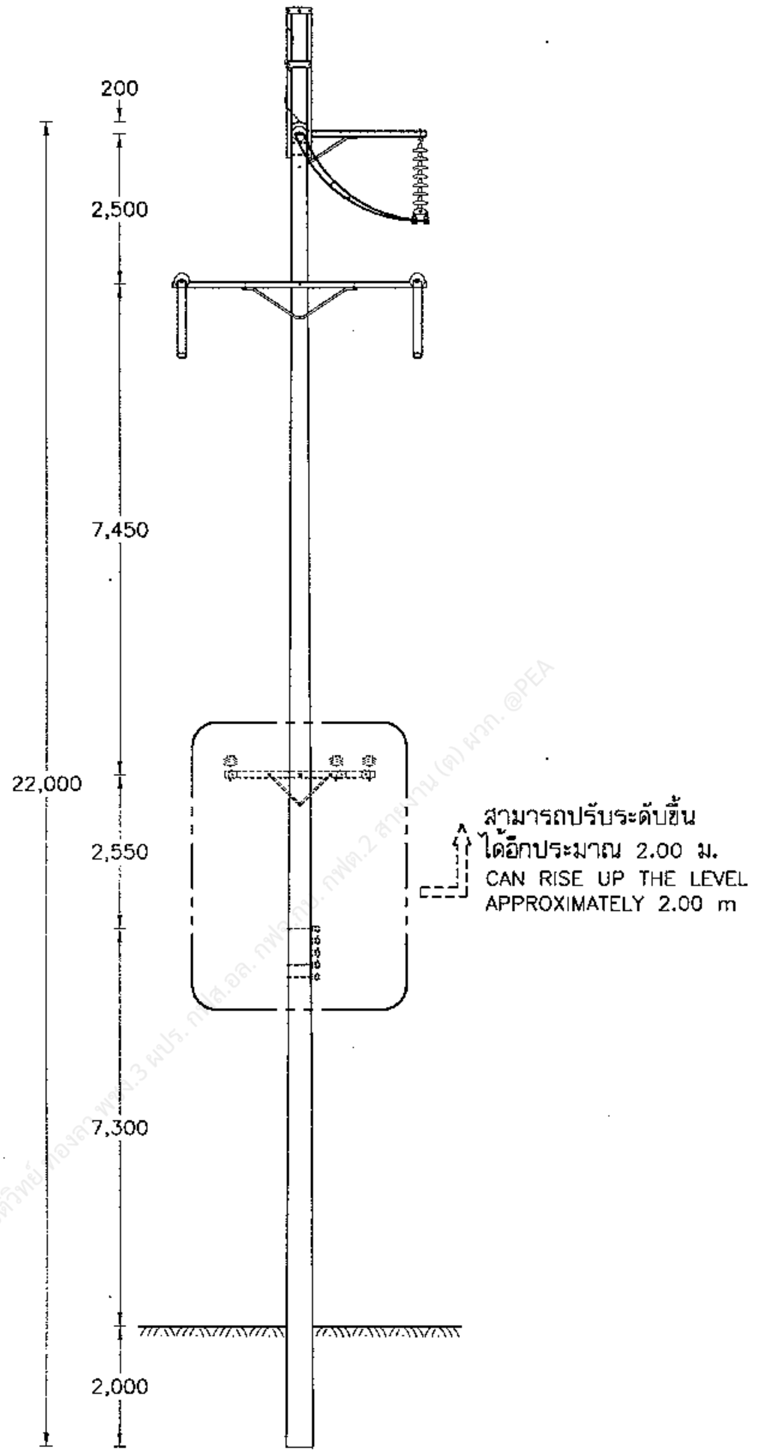

สามารถปรับระดับขึ้น
ได้อีกประมาณ 2.00 ม.
CAN RISE UP THE LEVEL
APPROXIMATELY 2.00 m

อติวิทย์ ทองลา พชง.3 ผปร. กฟส.อล. กฟฉ.2 สายงาน (ต) ผวก. @PEA

กองวิศวกรรมไฟฟ้าและเครื่องกล ฝ่ายวิศวกรรม	การไฟฟ้าส่วนภูมิภาค	ใช้แทนแบบ .... ถูกแทนโดยแบบ ....
ผู้เขียน Supphalit Boonsung ผู้สำรวจ.................. วิศวกร.................. หัวหน้าแผนก.......... (แทน) ผู้อำนวยการกอง.......... ผู้อำนวยการฝ่าย..........	ผู้ว่าการ.............................. 3 มี.ค. 2542 115 kV วงจรเดียว สายไฟฟ้าคู่ เสาเข้าปลายสายสองข้าง ก่อนเสาช่วงทางโค้ง แบบ SD–AS–6	เขียนเสร็จวันที่ 22 ก.พ. 2542 แก้แบบวันที่ .... มิติเป็น ..... มิลลิเมตร ..... มาตราส่วน ... 1 : 125 ....
รองผู้ว่าการเทคนิคและบริการ	115 kV SINGLE CIRCUIT, DOUBLE CONDUCTOR DOUBLE DEADEND STRUCTURE, ADJACENT POLE TO ANGLE TYPE SD–AS–6	แบบเลขที่ SA1–015/42006 แผ่นที่ 1 ของจำนวน 4 แผ่น

– 3 มี.ค. 2542

การประกอบเลขที่
ASSEMBLY NO. **5284**

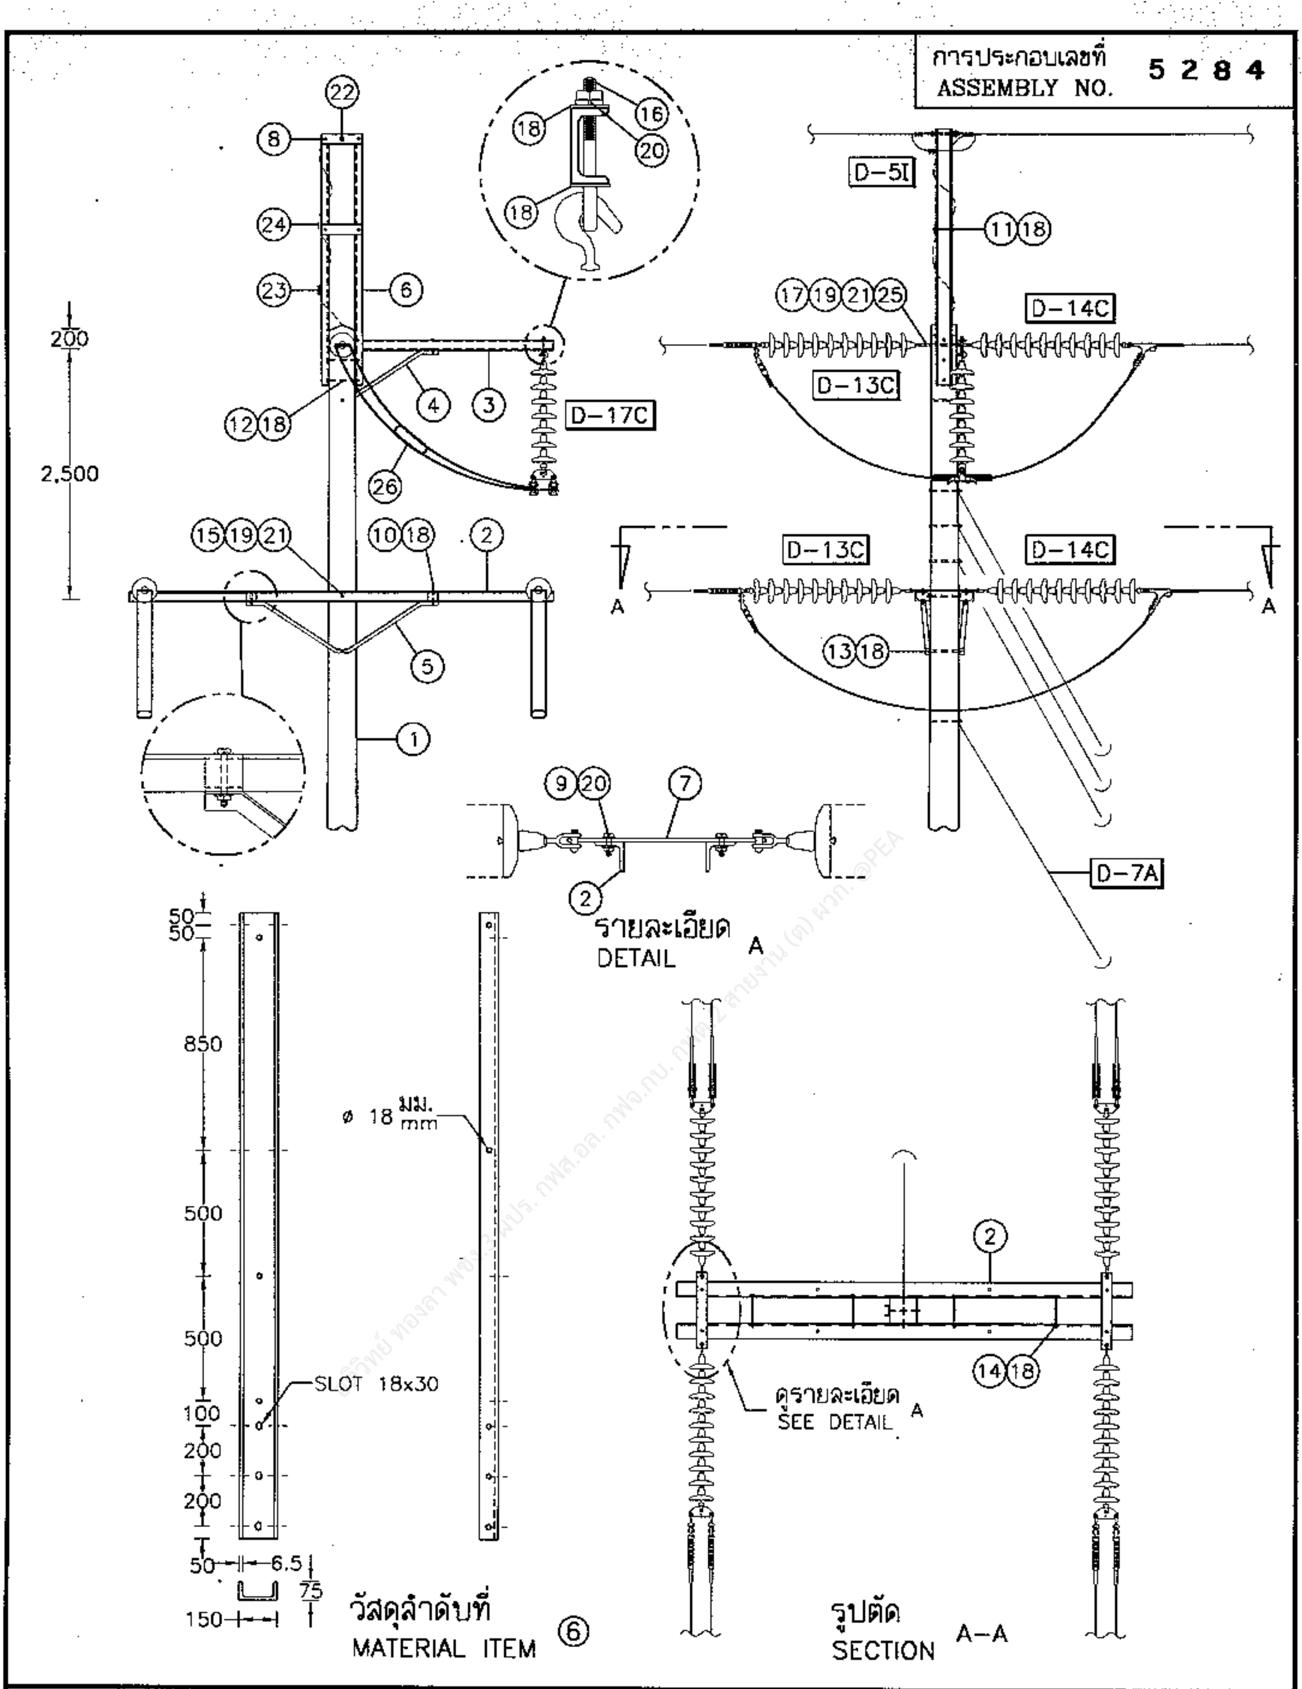

รายละเอียด
DETAIL A

วัสดุลำดับที่
MATERIAL ITEM ⑥

รูปตัด
SECTION A–A

ฉวีวิทย์ ทองลา พชอ.ผปบ. กฟส.อล. กฟจ.กบ. กฟฉ.2 สายงาน (ต) ผวก.@PEA

กองวิศวกรรมไฟฟ้าและเครื่องกล
ฝ่ายวิศวกรรม

การไฟฟ้าส่วนภูมิภาค

ใช้แทนแบบ ....
ถูกแทนโดยแบบ ....
เขียนเสร็จวันที่ 22 ก.พ. 2542

ผู้เขียน
ผู้สำรวจ......................
วิศวกร.......................
หัวหน้าแผนก.................
ผู้อำนวยการกอง..............
ผู้อำนวยการฝ่าย..............
รองผู้ว่าการเทคนิคและบริการ
....

ผู้ว่าการ - 3 มี.ค. 2542

แก้แบบวันที่ ....
มิติเป็น มิลลิเมตร
มาตราส่วน 1 : 75

115 kV วงจรเดี่ยว สายไฟฟ้าคู่
เสาเข้าปลายสายสองข้าง ก่อนเสาช่วงทางโค้ง
แบบ SD-AS-6

115 kV SINGLE CIRCUIT, DOUBLE CONDUCTOR
DOUBLE DEADEND STRUCTURE, ADJACENT POLE TO ANGLE
TYPE SD-AS-6

แบบเลขที่ SA1-015/42006
แผ่นที่ 2 ของจำนวน 4 แผ่น

- 3 มี.ค. 2542

การประกอบเลขที่ ASSEMBLY NO.	5 2 8 4

บัญชีวัสดุ
BILL OF MATERIAL

ลำดับที่ ITEM	รายละเอียด DESCRIPTION	จำนวน REQ'D	วัสดุเลขที่ MAT. NO.
1	เสาคอนกรีต 22 ม. POLE, CONCRETE 22 m LONG	1	00010011
2	คอนสายแบบเหล็กฉาก ขนาด 150x100x12 มม. ยาว 4.50 ม. CROSSARM, STEEL ANGLE 150x100x12 mm, 4.50 m LONG	2	00120001
3	คอนเหล็กแบบท้าวแขน ขนาด 100x50x5 มม. ยาว 2.25 ม. มอก 116 STEEL ALLEY ARM, 100x50x5 mm, 2.25 m LONG, TIS 116	1	01000100
4	เหล็กประกับคอน ขนาด 50x50x6 มม. ยาว 920 มม. BRACE, ANGLE STEEL 50x50x6 mm, 920 mm LONG	1	–
5	เหล็กฉากรับคอนสายขนาด 50x50x6 มม. ช่วงกว้าง 1,800 มม. ดรอพ 450 มม. BRACE, ANGLE STEEL 50x50x6 mm, 1,800 mm WIDE, 450 mm DROP	2	00120007
6	เหล็กรูปรางน้ำขนาด 150x75x6.5 มม. ยาว 2.50 ม. STEEL CHANNEL, 150x75x6.5 mm, 2.50 m LONG	2	–
7	แผ่นเหล็กยึดสองปลาย ขนาด 12x100x760 มม. PLATE, STEEL, DOUBLE ARMING 12x100x760 mm	2	01030102
8	แผ่นเหล็ก ขนาด 6x100x450 มม. PLATE, STEEL, 6x100x450 mm	4	01030002
9	สลักเกลียว M 16x75 มม. พร้อมแหวนกลม 2 อัน BOLT, MACHINE M 16x75 mm ; COMPLETE WITH 2 ROUND WASHER	4	01110400
10	สลักเกลียว M 16x170 มม. BOLT, MACHINE M 16x170 mm	5	01110201
11	สลักเกลียว M 16x200 มม. BOLT, MACHINE M 16x200 mm	4	01110202
12	สลักเกลียว M 16x300 มม. BOLT, MACHINE M 16x300 mm	3	01110204
13	สลักเกลียว M 16x350 มม. BOLT, MACHINE M 16x350 mm	2	01110205
14	สลักเกลียวตลอด M 16x400 มม. BOLT, DOUBLE ARMING, M 16x400 mm	4	01120000
15	สลักเกลียว M 20x350 มม. BOLT, MACHINE M 20x350 mm	1	01110300
16	สลักห่วงโอแวล M 16x150 มม. BOLT, OVAL EYE M 16x150 mm	1	01150000
17	สลักห่วงโอแวล M 20x350 มม. BOLT, OVAL EYE M 20x350 mm	1	01150100
18	แหวนสี่เหลี่ยมแบน 52x52x4.5 มม. รู ø18 มม. มอก. 258 WASHER, SQUARE FLAT 52x52x4.5 mm HOLE ø18 mm TIS 258	32	01180100
19	แหวนสี่เหลี่ยมแบน 62x62x6 มม. รู ø22 มม. มอก. 258 WASHER, SQUARE FLAT 62x62x6 mm HOLE ø22 mm TIS 258	2	01180101
20	แหวนสปริง M 16 มอก. 259 WASHER, LOCK M 16 TIS 259	5	01180301

กองวิศวกรรมไฟฟ้าและเครื่องกล ฝ่ายวิศวกรรม	การไฟฟ้าส่วนภูมิภาค	ใช้แทนแบบ .... ถูกแทนโดยแบบ ....
ผู้เขียน Supphakit Boonruang ผู้สำรวจ.................... วิศวกร.................... หัวหน้าแผนก.......(ทหม) ผู้อำนวยการกอง.................... ผู้อำนวยการฝ่าย.......สุวิน	ผู้ว่าการ - 3 ส.ค. 2542 115 kV วงจรเดี่ยว สายไฟฟ้าคู่ เสาเข้าปลายสายสองข้าง ก่อนเสาช่วงทางโค้ง แบบ SD-AS-6	เขียนเสร็จวันที่ 22 ก.พ. 2542 แก้แบบวันที่ .... มิติเป็น.................... มาตราส่วน....................
รองผู้ว่าการเทคนิคและบริการ	115 kV SINGLE CIRCUIT, DOUBLE CONDUCTOR DOUBLE DEADEND STRUCTURE, ADJACENT POLE TO ANGLE TYPE SD-AS-6	แบบเลขที่ SA1-015/42006 แผ่นที่ 3 ของจำนวน 4 แผ่น

- 3 ส.ค. 2542

การประกอบเลขที่ ASSEMBLY NO.	5 2 8 4

บัญชีวัสดุ
BILL OF MATERIAL

ลำดับที่ ITEM	รายละเอียด DESCRIPTION	จำนวน REQ'D	วัสดุเลขที่ MAT. NO.
21	แหวนสปริง M 20 WASHER, LOCK, M 20	2	01180302
22	ท่อเหล็ก ขนาด ø20 มม. ยาว 120 มม. PIPE, STEEL, ø20 mm, 120 mm LONG	1	01050001
23	แคล้มป์สลัก 3 ตัว สำหรับลวดเหล็กตีเกลียว 35 ต.มม. CLAMP, TRIPLE BOLTS, FOR STEEL STRANDED WIRE 35 mm^2	1	01230000
24	ลวดเหล็กตีเกลียว 35 ต.มม. ความยาวตามต้องการ STEEL STRANDED WIRE 35 mm^2, LENGTH AS REQUIRED	ม. m	01100003
25	อายเล็ท M 20 EYE LET, M 20	1	01180002
26	ปรีฟอร์มแยกสาย SPACER, HELICAL ROD, PREFORMED DEADEND	4	02240000

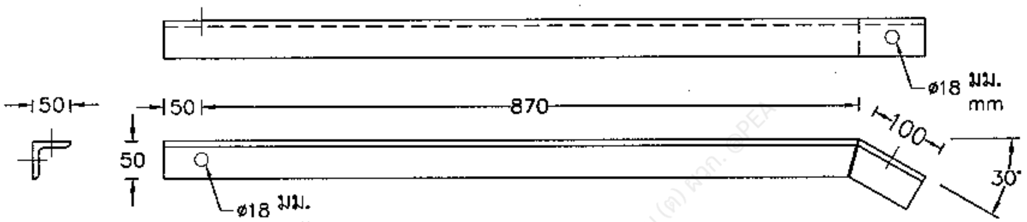

วัสดุลำดับที่ ④
MATERIAL ITEM

รายละเอียด
DETAIL

D-13C	การประกอบลูกถ้วยแขวน SUSPENSION INSULATOR ASSEMBLY	3	
D-14C	การประกอบลูกถ้วยแขวน SUSPENSION INSULATOR ASSEMBLY	3	
D-17C	การประกอบลูกถ้วยแขวน SUSPENSION INSULATOR ASSEMBLY	1	
D-5I	การต่อสายล่อฟ้า OVERHEAD GROUND WIRE CONNECTION	1	
D-7A	การประกอบสายยึดโยงลวดเหล็กตีเกลียว 95 ต.มม. STEEL STRANDED WIRE 95 mm^2 GUY ASSEMBLY	4	
* D-9B	สมอบกคอนกรีต CONCRETE ANCHOR	1	
* D-10A	ฐานรากเสา POLE FOUNDATION	1	

* สามารถเปลี่ยนได้ตามความเหมาะสม
CAN BE CHANGEDTO BE SUITABLE

กองวิศวกรรมไฟฟ้าและเครื่องกล ฝ่ายวิศวกรรม	การไฟฟ้าส่วนภูมิภาค	ใช้แทนแบบ .... ถูกแทนโดยแบบ ....
ผู้เขียน Supphalit Boonying ผู้สำรวจ .... วิศวกร .... หัวหน้าแผนก .... (ทน) ผู้อำนวยการกอง .... ผู้อำนวยการฝ่าย	ผู้ว่าการ - 3 ส.ค. 2542 115 kV วงจรเดี่ยว สายไฟฟ้าคู่ เสาเข้าปลายสายสองข้าง ก่อนเสาช่วงทางโค้ง แบบ SD-AS-6	เขียนเสร็จวันที่ 22 ก.พ. 2542 แก้แบบวันที่ .... มิติเป็น มิลลิเมตร มาตราส่วน 1 : 10
รองผู้ว่าการเทคนิคและบริการ	115 kV SINGLE CIRCUIT, DOUBLE CONDUCTOR DOUBLE DEADEND STRUCTURE, ADJACENT POLE TO ANGLE TYPE SD-AS-6	แบบเลขที่ SA1-015/42006 แผ่นที่ 4 ของจำนวน 4 แผ่น

- 3 ส.ค. 2542