
การประกอบเลขที่ ASSEMBLY NO. 0205


N – สายเป็นกลาง NEUTRAL LINE

A, B, C – สายเฟส PHASE LINE

L – สายดับไฟถนน STREET LIGHTING LINE

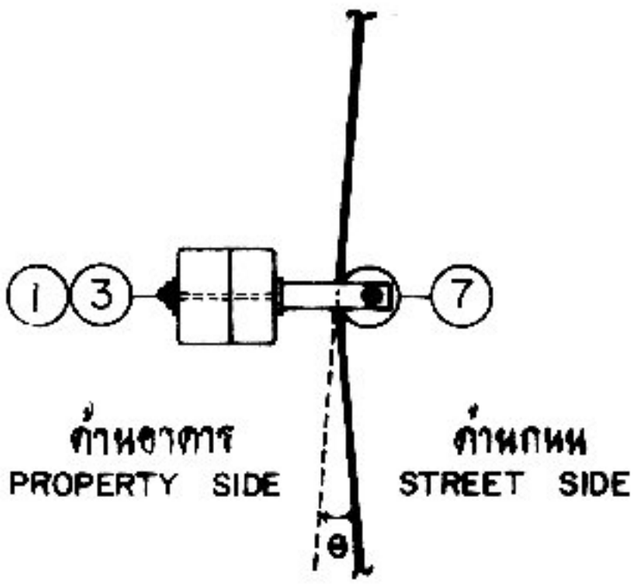


สำหรับทางตรง 0°-5° (θ)
FOR TANGENT STRUCTURE 0°-5° (θ)

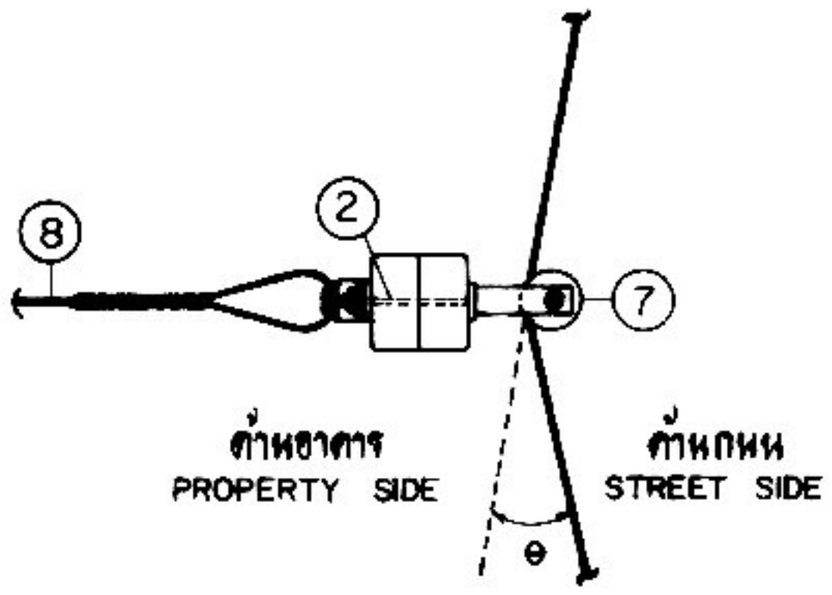

สำหรับทางโค้ง 5°-60° (θ)
FOR ANGLE STRUCTURE 5°-60° (θ)

ด้านบน
TOP VIEW

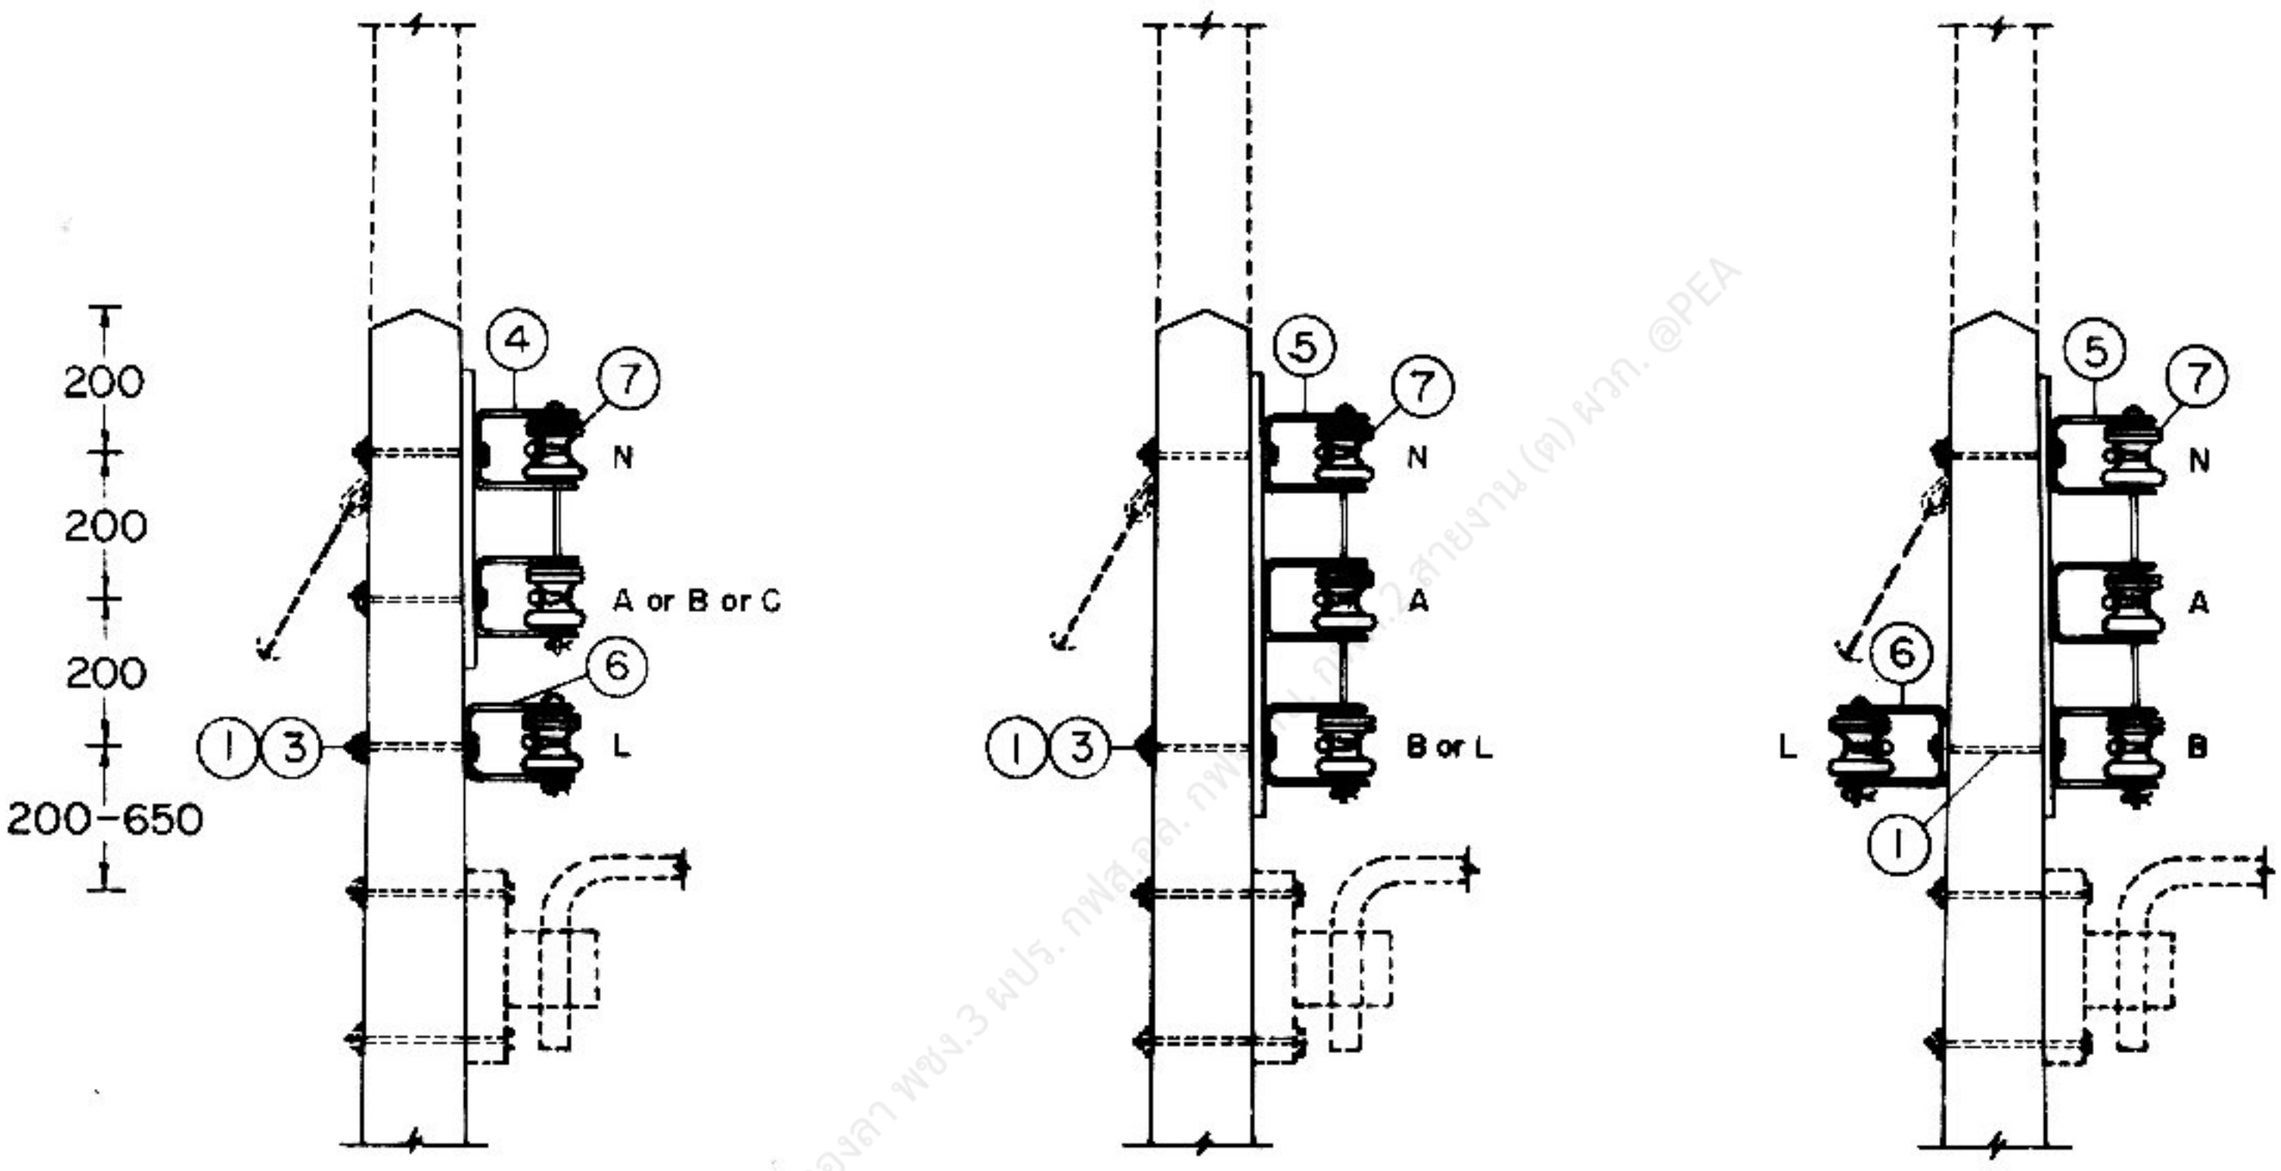

① แบบ 1 เฟส 2 สาย พร้อมสายดับไฟถนน
1-PHASE 2-WIRE INCLUDING STREET LIGHTING LINE

② แบบ 1 เฟส 2 สาย พร้อมสายดับไฟถนน หรือ แบบ 1 เฟส 3 สาย หรือ แบบ 2 เฟส 3 สาย
1-PHASE 2-WIRE INCLUDING STREET LIGHTING LINE OR 1-PHASE 3-WIRE OR 2-PHASE 3-WIRE

③ แบบ 1 เฟส 3 สาย พร้อมสายดับไฟถนน หรือ แบบ 2 เฟส 3 สาย พร้อมสายดับไฟถนน
1-PHASE 3-WIRE INCLUDING STREET LIGHTING LINE OR 2-PHASE 3-WIRE INCLUDING STREET LIGHTING LINE

อดิวิทย์ ทองดา พชง.3 ผปร. กฟส.สายงาน (ค) ผวก. @PEA

กองวิศวกรรมไฟฟ้าและเครื่องกล ฝ่ายวิศวกรรม	การไฟฟ้าส่วนภูมิภาค	ใช้แทนแบบ ถูกแทนโดยแบบ เขียนเสร็จวันที่ 12 มิ.ย. 21 แก้แบบวันที่ มิติเป็น mm. มาตราส่วน 1 : 20
ผู้เขียน ผู้สำรวจ วิศวกร หัวหน้าแผนก หัวหน้ากอง ผู้อำนวยการฝ่าย	ผู้ว่าการ 24 มิ.ย. 21	
รองผู้ว่าการฝ่ายเทคนิค 21 มิ.ย. 2521	การติดตั้งแร็คแขวงต่ำกันเสาคอนกรีต 8 ม. สำหรับทางตรง 0°-5° และ สำหรับทางโค้ง 5°-60° SECONDARY RACK INSTALLATION ON 8 m CONCRETE POLE FOR TANGENT STRUCTURE 0°-5° & ANGLE STRUCTURE 5°-60°	แบบเลขที่ SAI-015/21027 แผ่นที่ 1 ของจำนวน 2 แผ่น

การประกอบเลขที่ ASSEMBLY NO. 0205

บัญชีวัสดุ
BILL OF MATERIAL

ลำดับที่ ITEM	รายละเอียด DESCRIPTION	จำนวน REQUIRED 0°-5° 1	2	3	5°-60° 1	2	3	วัสดุเลขที่ MAT. NO.
1	สลักเกลียว M 16X170 มม. BOLT, MACHINE, M 16X170 mm	3	2	2	2	1	1	01110201
1a	สลักเกลียว M 16 X 250 มม. สำหรับเสาคอนกรีต 12 ม. BOLT, MACHINE, M 16 X 250 mm FOR 12 m CONCRETE POLE	3	2	2	2	1	1	01110203
2	สลักเกลียว M 16 X 200 มม. BOLT, MACHINE, M 16 X 200 mm	-	-	-	1	1	1	01110202
2a	สลักเกลียว M 16 X 300 มม. สำหรับเสาคอนกรีต 12 ม. BOLT, MACHINE, M 16 X 300 mm FOR 12 m CONCRETE POLE	-	-	-	1	1	1	01110204
3	แหวนสี่เหลี่ยมแบน 52 X 52 X 4.5 มมรู Ø 18 มม. มอก. 258 WASHER, SQUARE FLAT 52 X 52X 4.5 mm, HOLE Ø 18 mm TIS 258	3	2	1	2	1	-	01180100
4	แร็ค 2 X 200 มม. แบบหลังยื่น RACK, SECONDARY, MEDIUM PRESSED STEEL 2 X 200 mm EXT. BACK	1	-	-	1	-	-	03130000
5	แร็ค 3 X 200 มม. แบบหลังยื่น RACK, SECONDARY, MEDIUM PRESSED STEEL 3X 200 mm EXT. BACK	-	1	1	-	1	1	03130001
6	ที่จับลูกถ้วย สำหรับลูกถ้วย มอก. 227 (แบบ 53-2) CLEVIS, FLAT STEEL, FOR INSULATOR TIS 227 (CLASS 53-2)	1	-	1	1	-	1	03130100
7	ลูกถ้วยแกนต่ำ มอก. 227 แบบ ข (แบบ 53-2) INSULATOR, SPOOL TYPE, L.T. TIS 227 TYPE B (CLASS 53-2)	3	3	4	3	3	4	03030000
8	การประกอบสายยึดโยง GY-01 GUY ASSEMBLY GY-01	-	-	-	1	1	1	—
8a	การประกอบสายยึดโยง GY-02 สำหรับเสาคอนกรีต 12 ม. GUY ASSEMBLY GY-02 FOR 12 m CONCRETE POLE	-	-	-	1	1	1	—

อดิวัฒน์ ทองลา พชง.3 ผปร. กฟส.อด. กฟภ.

กองวิศวกรรมไฟฟ้าและเครื่องกล ฝ่ายวิศวกรรม	การไฟฟ้าส่วนภูมิภาค	ใช้แทนแบบ ถูกแทนโดยแบบ เขียนแบบเมื่อวันที่ 12 เม.ย. 21 แก้แบบวันที่ มิติเป็น มาตราส่วน
ผู้เขียน ผู้สำรวจ วิศวกร หัวหน้าแผนก หัวหน้ากอง ผู้อำนวยการฝ่าย	ผู้ว่าการ	
รองผู้ว่าการฝ่ายเทคนิค	การติดตั้งแร็คแรงต่ำกับเสาคอนกรีต 8 ม. สำหรับทางตรง 0°-5° และ สำหรับทางโค้ง 5°-60° SECONDARY RACK INSTALLATION ON 8 m CONCRETE POLE FOR TANGENT STRUCTURE 0°-5° & ANGLE STRUCTURE 5°-60°	แบบมาตรฐานที่ SAI-015/21027 แผ่นที่ 2 ของจำนวน 2 แผ่น