การประกอบเลขที่ 
ASSEMBLY NO. 3503

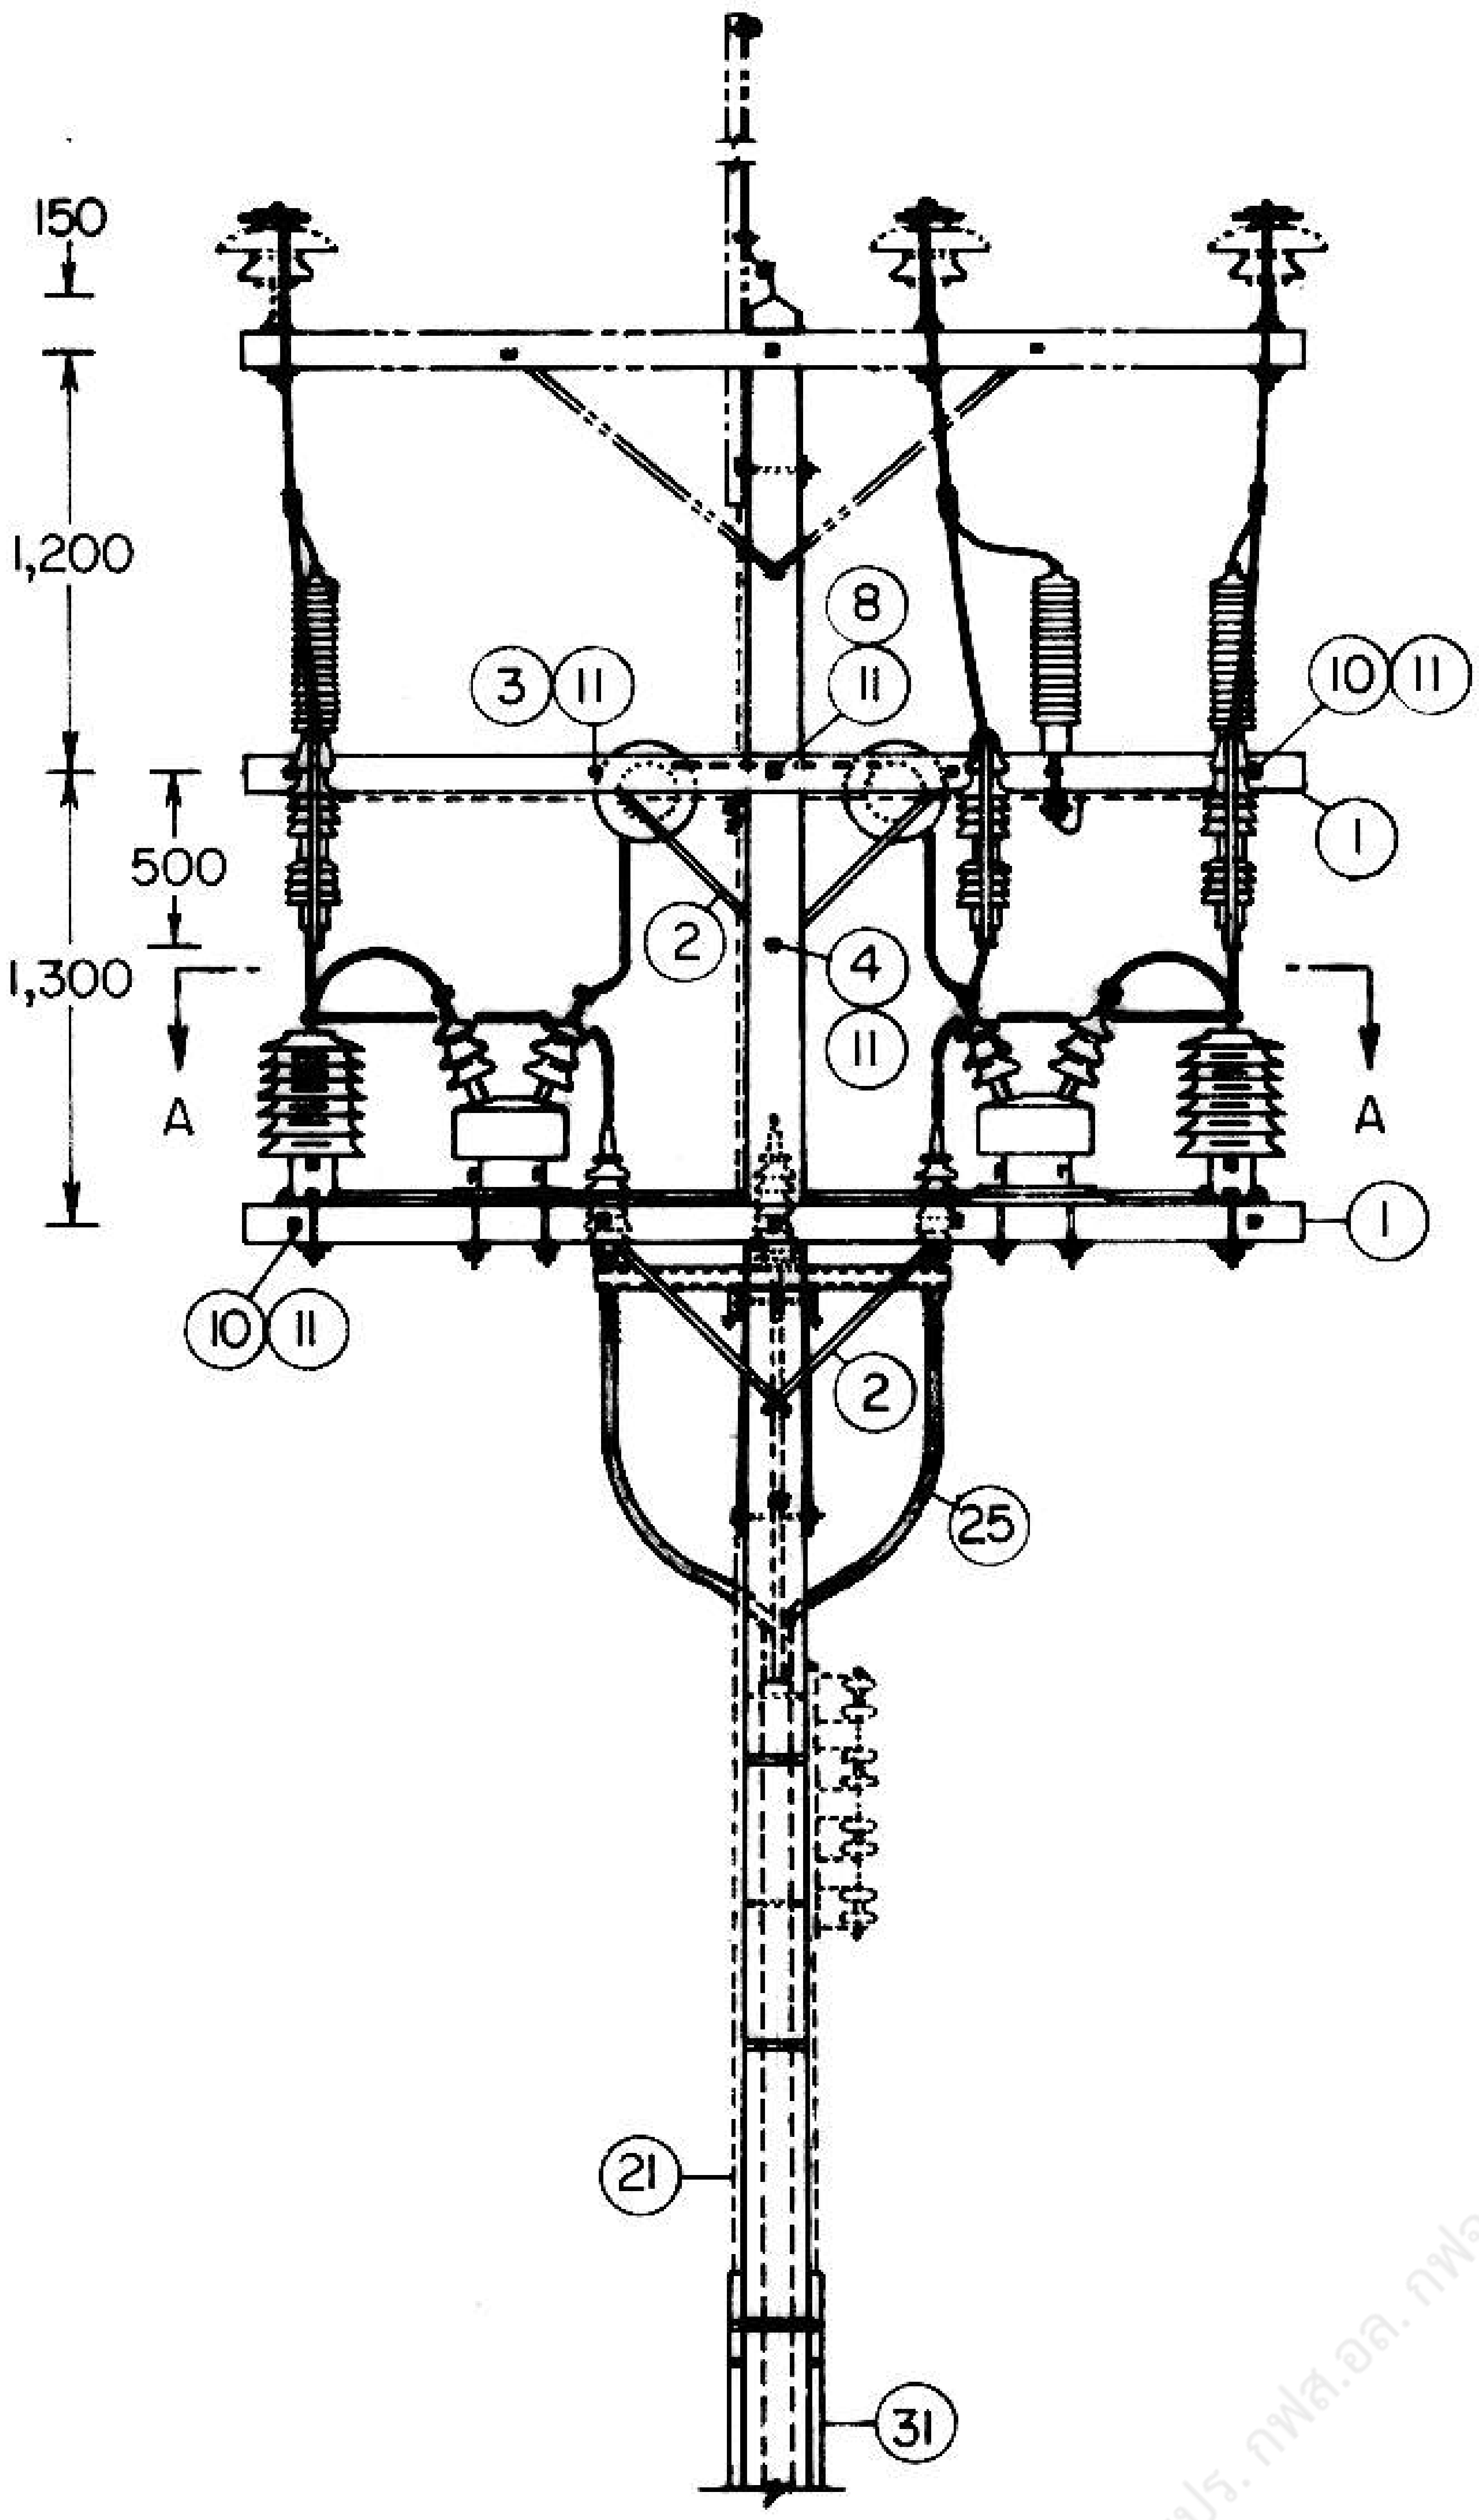

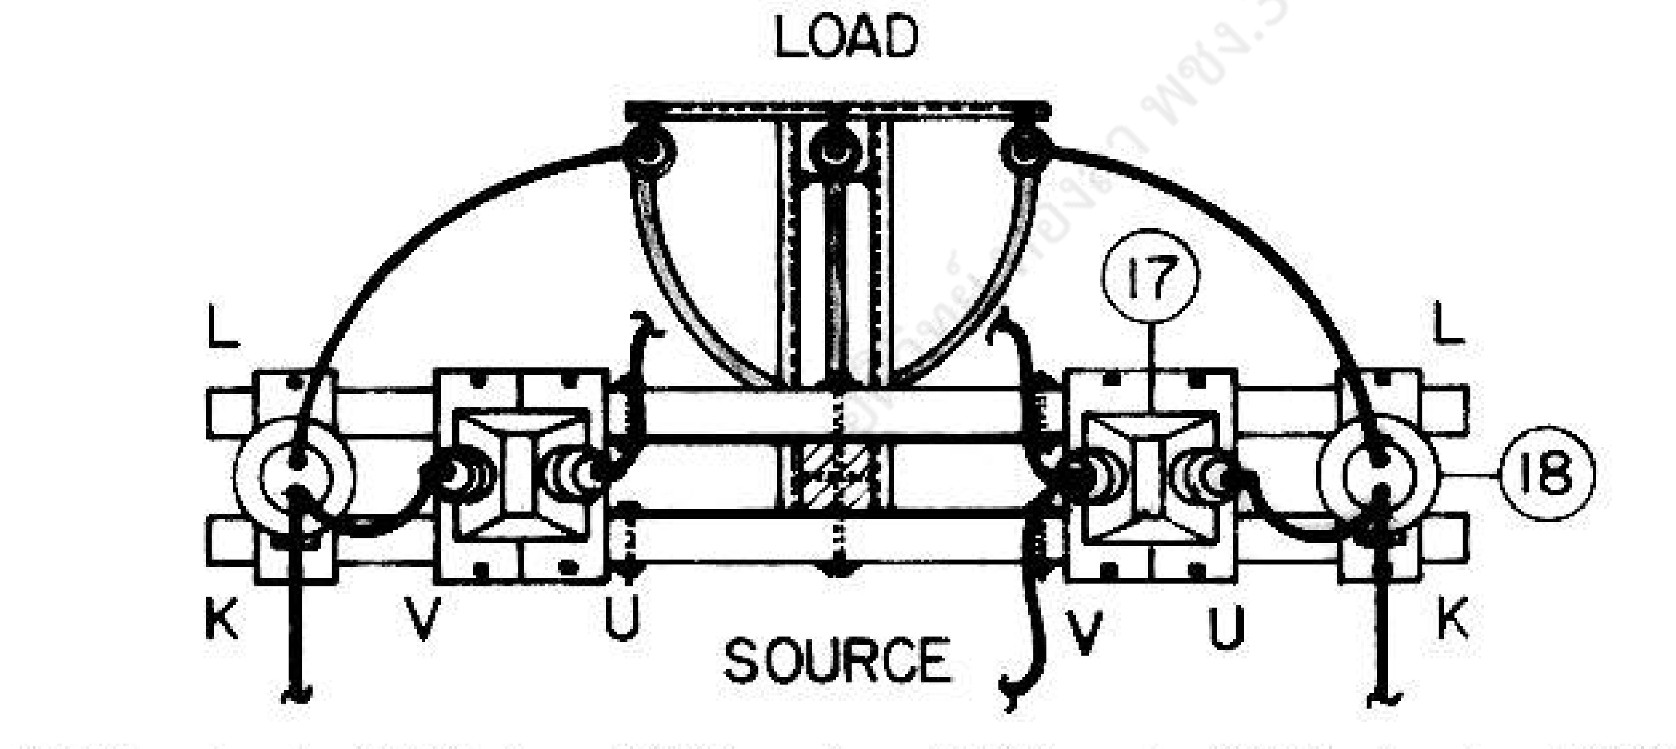

รูปตัด
SECTION A – A

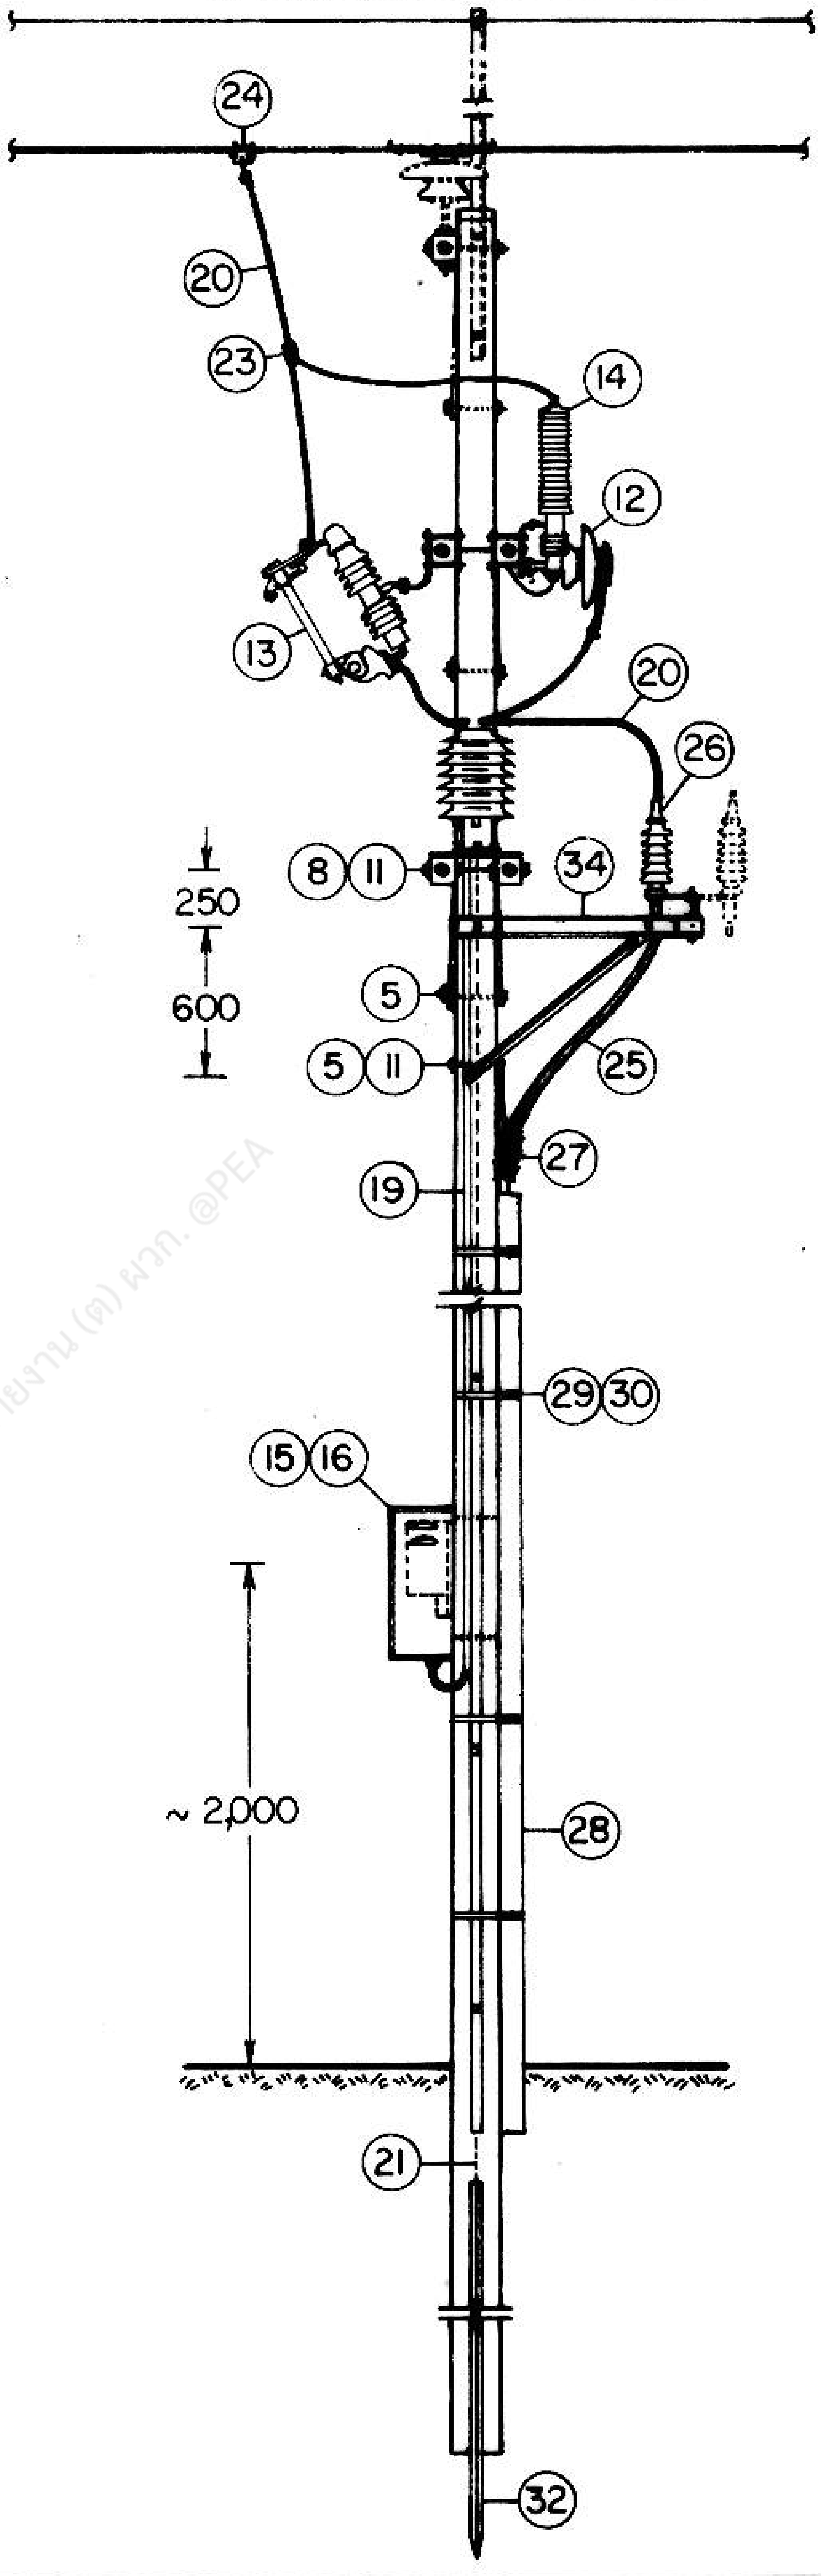

พชง.3 ผปร. กฟส.อล. กฟจ.กบ. กฟต.2 สายงาน (ต) ผวก. @PEA

กองวิศวกรรมไฟฟ้าและเครื่องกล
ฝ่ายวิศวกรรม

ผู้เขียน
ผู้สำรวจ
วิศวกร
หัวหน้าแผนก
ผู้อำนวยการกอง
ผู้อำนวยการฝ่าย

รองผู้ว่าการฝ่ายเทคนิค

## การไฟฟ้าส่วนภูมิภาค

ผู้ว่าการ 24.ส.ย.27

### การติดตั้ง พีที.และซีที. สำหรับมิเตอร์แรงสูง 33 kV
### จ่ายโหลดผ่านเคเบิลใต้ดิน
### ก ที่เสาในสายจำหน่าย (คอนสายแบบธรรมดา)

### PT. & CT. INSTALLATION FOR H.T. METER 33 kV
### UNDERGROUND LOAD
### A IN LINE POLE (CROSSARM)

ใช้แทนแบบ
ถูกแทนโดยแบบ
เขียนเสร็จวันที่ 17 ก.ย. 27
แก้แบบวันที่
มิติเป็น มม.
มาตราส่วน 1 : 50

แบบเลขที่ SAI-015/27017
แผ่นที่ 1 ของจำนวน 4 แผ่น

ก.ค. 2527

การประกอบเลขที่ 3503
ASSEMBLY NO.

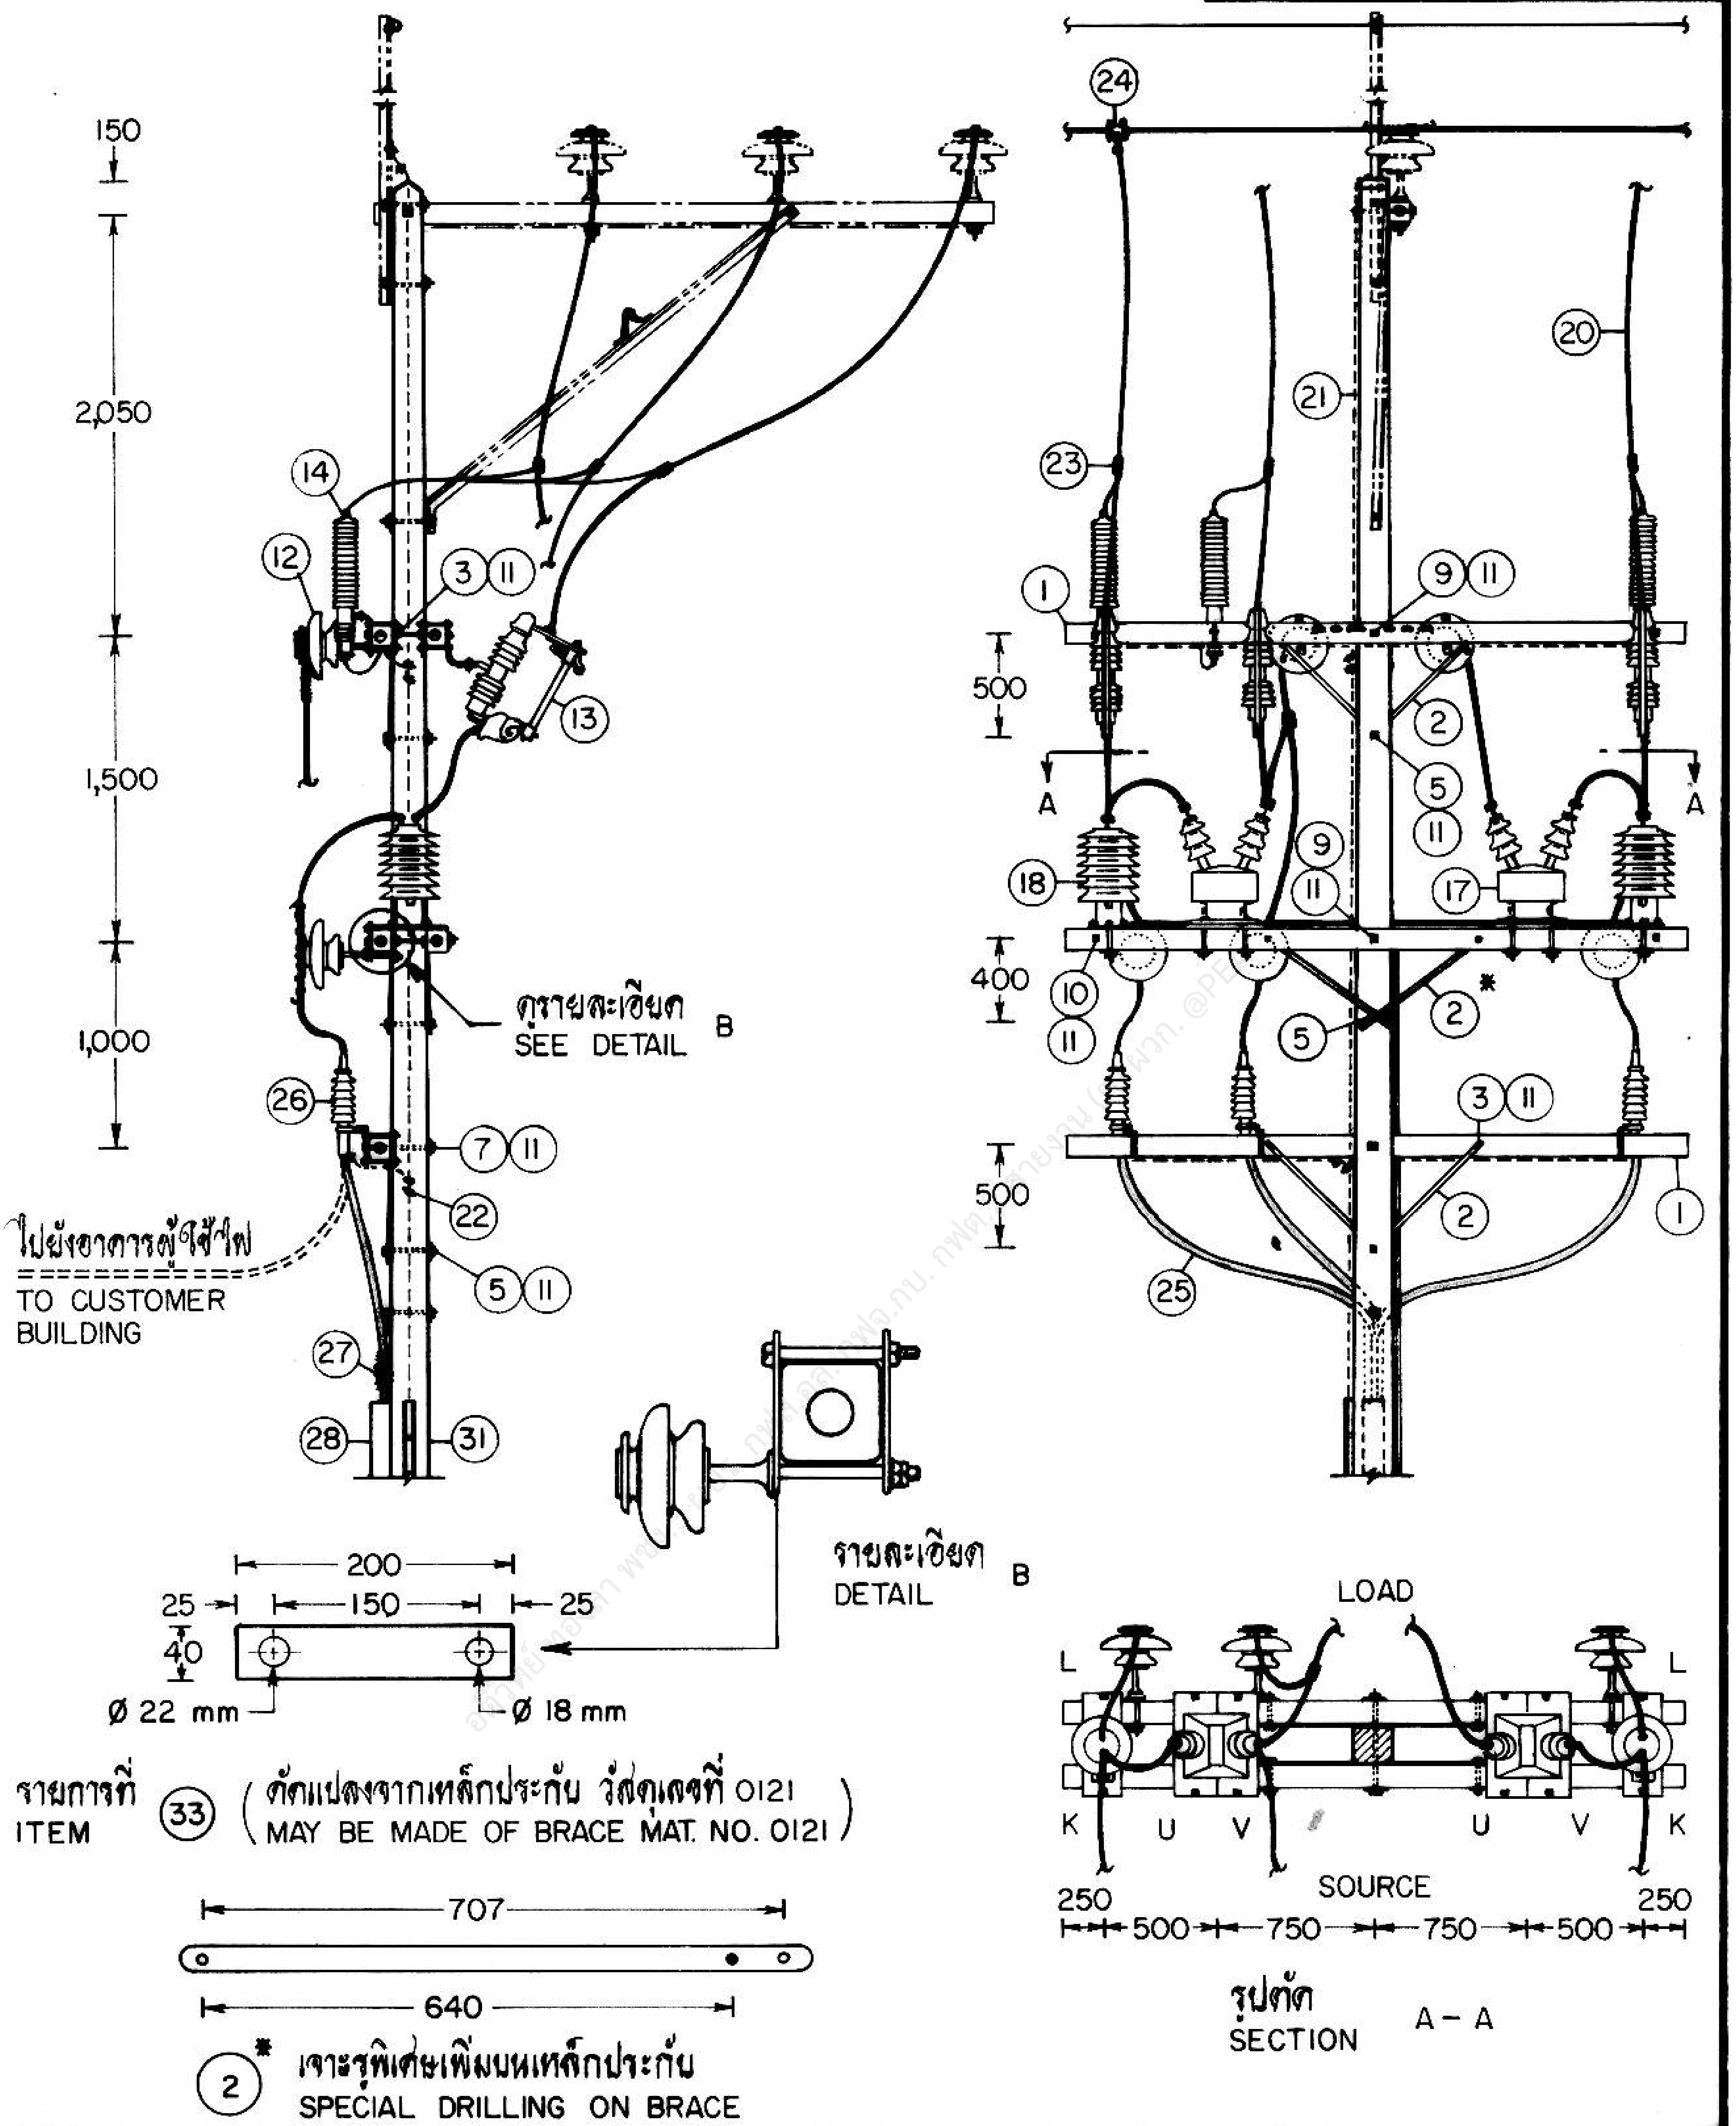

| | | |
|---|---|---|
| กองวิศวกรรมไฟฟ้าและเครื่องกล<br>ฝ่ายวิศวกรรม | การไฟฟ้าส่วนภูมิภาค | ใช้แทนแบบ<br>ถูกแทนโดยแบบ<br>เขียนเสร็จวันที่ 17 ก.ย. 27<br>แก้แบบวันที่ 2<br>มิติเป็น มม.<br>มาตราส่วน 1 : 50 |
| ผู้เขียน<br>ผู้สำรวจ<br>วิศวกร<br>หัวหน้าแผนก<br>ผู้อำนวยการกอง<br>ผู้อำนวยการฝ่าย | ผู้ว่าการ 24 ก.พ. 27<br>การติดตั้ง พีที. และซีที. สำหรับมิเตอร์แรงสูง 33 kV<br>จ่ายโหลดผ่านเคเบิลใต้ดิน<br>ข ที่เสาในสายจำหน่าย ( คอนสายแบบท้าวแขน ) | |
| รองผู้ว่าการฝ่ายเทคนิค | PT. & CT. INSTALLATION FOR H.T. METER 33 kV<br>UNDERGROUND LOAD<br>B IN LINE POLE ( ALLEY ARM ) | แบบเลขที่ SAI-015/27017<br>แผ่นที่ 2 จากจำนวน 4 แผ่น |

24 FEB. 2527

| | |
|---|---|
| การประกอบเลขที่<br>ASSEMBLY NO. | 3503 |

## บัญชีวัสดุ
## BILL OF MATERIAL

| ลำดับที่<br>ITEM | รายละเอียด<br>DESCRIPTION | จำนวน<br>REQ'D<br>ก/A | <br><br>ข/B | วัสดุเลขที่<br>MAT. NO. |
|---|---|---|---|---|
| 1 | คอน คอร. สปัน ขนาด 120 X 120 X 3,000 มม.<br>CROSSARM, SPUN PRESTRESSED CONCRETE, 120 X 120 X 3,000 mm | 4 | 5 | 00110002 |
| 2 | เหล็กประกับคอน ขนาด 30 X 6 X 760 มม.<br>BRACE, FLAT, FOR CROSSARM, 30 X 6 X 760 mm | 6 | 8 | 01200001 |
| 3 | สลักเกลียว M 16 X 170 มม.<br>BOLT, MACHINE, M 16 X 170 mm | 8 | 13 | 01110201 |
| 4 | สลักเกลียว M 16 X 200 มม.<br>BOLT, MACHINE, M 16 X 200 mm | 1 | – | 01110202 |
| 5 | สลักเกลียว M 16 X 250 มม.<br>BOLT, MACHINE, M 16 X 250 mm | 2 | 3 | 01110203 |
| 6 | สลักเกลียว M 16 X 300 มม.<br>BOLT, MACHINE, M 16 X 300 mm | 2 | 2 | 01110204 |
| 7 | สลักเกลียว M 16 X 400 มม.<br>BOLT, MACHINE, M 16 X 400 mm | – | 1 | 01110206 |
| 8 | สลักเกลียว M 16 X 450 มม.<br>BOLT, MACHINE, M 16 X 450 mm | 2 | – | 01110207 |
| 9 | สลักเกลียว M 16 X 500 มม.<br>BOLT, MACHINE, M 16 X 500 mm | – | 2 | 01110208 |
| 10 | สลักเกลียวตลอด M 16 X 500 มม.<br>BOLT, DOUBLE ARMING, M 16 X 500 mm | 4 | 4 | 01120002 |
| 11 | แหวนสี่เหลี่ยมแบน 52 X 52 X 4.5 มม. รู Ø 18 มม. มอก. 258<br>WASHER, SQUARE, FLAT, 52 X 52 X 4.5 mm HOLE Ø 18 mm TIS 258 | 32 | 37 | 01180100 |
| 12 | ลูกถ้วยก้านตรง 33 kV แบบ 56-3 มอก. 279 แบบ ค พร้อมก้าน<br>INSULATOR, PIN TYPE, 33 kV CLASS 56-3 TIS 279 TYPE C COMP. WITH PIN | 2 | 5 | 03000002<br>03100000 |
| 13 | ดรอพเอาต์ ฟิวส์คัตเอาต์ หนึ่งอินซูเลเตอร์ 33 kV 100 แอมป์<br>CUT-OUT, FUSE, OPEN TYPE, SINGLE INSULATOR, DROP-OUT 33 kV, 100 A | 3 | 3 | 04010100 |
| 14 | ล่อฟ้า 30 kV 5 กิโลแอมป์<br>LIGHTNING ARRESTER, 30 kV, 5 kA | 3 | 3 | 04000100 |
| 15 | ดีมานด์มิเตอร์ ชนิดสะสม 3 เฟส 3 สาย 110 โวลต์ 5 แอมป์<br>DEMAND METER, CUMULATIVE, 3-PHASE, 3-WIRE, 110 V, 5 A | 1 | 1 | 06000300 |
| 16 | ตู้ใส่มิเตอร์แรงสูง พร้อมแป้นไม้<br>METER CABINET FOR HIGH TENSION METER COMP. WITH METER PLATE | 1 | 1 | 06100007 |
| 17 | พี ที. หนึ่งเฟส ใช้นอกอาคาร 33,000–110 โวลต์ พร้อมอุปกรณ์ติดตั้ง<br>TRANSFORMER, POTENTIAL, 1Ø, OUTDOOR, 33,000–110 V, COMP. WITH MOUNTING ACCESS. | 2 | 2 | 06020100 |
| 18 | ซี ที. ใช้นอกอาคาร 33 kV เรโชตามต้องการ พร้อมอุปกรณ์ติดตั้ง<br>TRANSFORMER, CURRENT, OUTDOOR, 33 kV RATIO AS REQ'D COMP. WITH MOUNTING ACCESS. | 2 | 2 | 06040101<br>–<br>06040106 |
| 19 | คอนโทรลเคเบิล ขนาด 7 X 2.5 ต.มม.<br>CONTROL CABLE, SIZE 7 X 2.5 mm$^2$ | 10 ม./m | 10 ม./m | 02080402 |
| 20 | สายอะลูมิเนียม 35-95 ต.มม. ขนาดตามต้องการ มอก. 85<br>CONDUCTOR, Al 35-95 mm$^2$ SIZE AS REQUIRED TIS 85 | 15 ม./m | 24 ม./m | 02010001<br>–<br>02010004 |

| | | |
|---|---|---|
| กองวิศวกรรมไฟฟ้าและเครื่องกล<br>ฝ่ายวิศวกรรม | **การไฟฟ้าส่วนภูมิภาค** | ใช้แทนแบบ<br>ถูกแทนโดยแบบ |
| ผู้เขียน<br>ผู้สำรวจ<br>วิศวกร<br>หัวหน้าแผนก<br>ผู้อำนวยการกอง<br>ผู้อำนวยการฝ่าย | ผู้ว่าการ 24 ก.ย. 27 | เขียนเสร็จวันที่ 17 ก.ย. 27 |
| | การติดตั้ง พีที. และซีที. สำหรับมิเตอร์แรงสูง 33 kV<br>จ่ายโหลดผ่านเคเบิลใต้ดิน | แก้แบบวันที่<br>มิติเป็น<br>มาตราส่วน |
| รองผู้ว่าการฝ่ายเทคนิค | PT. & CT. INSTALLATION FOR H.T. METER 33 kV<br>UNDERGROUND LOAD | แบบเลขที่ SA1-015/27017<br>แผ่นที่ 3 ของจำนวน 4 แผ่น |

21 ก.ย. 2527

การประกอบเลขที่
ASSEMBLY NO. 3503

## บัญชีวัสดุ
## BILL OF MATERIAL

| ลำดับที่<br>ITEM | รายละเอียด<br>DESCRIPTION | จำนวน REQ'D<br>ก/A | <br>ข/B | วัสดุเลขที่<br>MAT. NO. |
|---|---|---|---|---|
| 21 | ลวดเหล็กตีเกลียว 50/7 ต.มม. มอก. 404<br>WIRE, STEEL STRANDED 50/7 $mm^2$ TIS 404 | 27 ม. m | 30 ม. m | 01100004 |
| 22 | ยูแคล้มป์ สลัก 1 ตัว M 8 (ไวร์โร้ปคลิ๊ฟ)<br>CLAMP, SINGLE U-BOLT, M8 ( WIRE ROPE CLIP ) | 11 | 13 | 01230000 |
| 23 | พี.จี. คอนเนคเตอร์ สลักคู่ สำหรับสายอะลูมิเนียม 25-95 ต.มม.<br>CONNECTOR, PARALLEL GROOVE, DOUBLE BOLT, Al 25-95 $mm^2$ | 7 | 7 | 02300102 |
| 24 | เบล (สเตอร์รัพ) แคล้มป์ และฮอทไลน์แคล้มป์ ขนาดตามต้องการ<br>CLAMP, BAIL ( STIRRUP) AND HOT LINE CLAMP SIZE AS REQUIRED | 3 | 3 | 02330000-1<br>02330100-1 |
| 25 | เคเบิลใต้ดินทองแดง 33 kV ขนาด และความยาวตามต้องการ<br>UNDERGROUND POWER CABLE, 33 kV, Cu SIZE AND LENGTH AS REQUIRED | ม. m | ม. m | |
| 26 | ชุดหัวเคเบิลใช้นอกอาคาร สำหรับสายเคเบิลใต้ดิน 33 kV ขนาดตามต้องการ<br>OUTDOOR CABLE TERMINATION KIT, 33 kV, SIZE AS REQUIRED | 3 | 3 | |
| 27 | ห่วงรองรับสายเคเบิลใต้ดิน ขนาดตามต้องการ<br>CABLE GRIP, SIZE AS REQUIRED | 1 | 1 | |
| 28 | ท่อร้อยสาย ผนังท่อหนา ขนาด 100 หรือ 150 มม. ยาว 3,000 มม. มอก. 770 พร้อมข้อต่อเกลียว และท่อโค้ง ความยาวตามต้องการ ( CONDUIT, STEEL, RIGID, SIZE 100 OR 150 mm, 3,000 mm LONG, TIS 770, COM. WITH COUPLING AND ELBOW COUPLING, LENGTH AS REQUIRED ) | | | 08050003<br>or<br>08050004 |
| 29 | เทปรัด 30 X 1.5 มม. รู Ø 10 มม.<br>PERFORATED TAPE 30 X 1.5 mm HOLE Ø 10 mm | 12 ม. m | 12 ม. m | 3921 |
| 30 | สลักเกลียว M 8 X 25 มม.<br>BOLT, MACHINE, M 8 X 25 mm | 10 | 10 | 01110000 |
| 31 | ท่อ PVC แข็ง ขนาด Ø 20 X 4,000 มม. มอก. 216<br>CONDUIT, RIGID PVC Ø 20 X 4,000 mm TIS. 216 | 2 | 2 | 08040002 |
| 32 | หลักดิน 60 X 60 X 5 มม. ยาว 2 ม.<br>ROD, GROUND, 60 X 60 X 5 mm, 2 m LONG | 2 | 2 | 01220002 |
| 33 | แผ่นเหล็ก ขนาด 40X6 มม. ยาว 200 มม. ใช้ยึดลูกถ้วยก้านตรงบนคอนคอนกรีต<br>STEEL PLATE 40X6 mm, 200 mm LONG FOR FIXING PIN INSULATOR ON CONCRETE CROSSARM | 4 | 10 | |
| 34 | ชุดโครงเหล็กสำหรับติดตั้งหัวสายเคเบิลใต้ดิน<br>SUPPORTING BRACKET FOR UNDERGROUND CABLE TERMINATOR | 1 ชุด set | – | |

| | แบบอ้างอิง<br>REFERENCE DRAWING | แบบเลขที่<br>DWG. NO. | การประกอบเลขที่<br>ASSEMBLY NO. |
|---|---|---|---|
| 1 | การต่อสายคอนโทรลเคเบิล<br>THE CONNECTION DIAGRAM OF CONTROL CABLE | S02-015/16005 | 0506 |
| 2 | การต่อลงดินระบบแรงสูง และแรงต่ำ<br>H.T. AND L.T. EARTHING | S02-015/20039 | 9701 |
| 3 | ชุดโครงเหล็กสำหรับติดตั้งหัวสายเคเบิลใต้ดิน<br>SUPPORTING BRACKET FOR UNDERGROUND CABLE TERMINATOR | SAI-015/27018 | 9566 |

กองวิศวกรรมไฟฟ้าและเครื่องกล
ฝ่ายวิศวกรรม

ผู้เขียน
ผู้สำรวจ
วิศวกร
หัวหน้าแผนก
ผู้อำนวยการกอง
ผู้อำนวยการฝ่าย

รองผู้ว่าการฝ่ายเทคนิค

# การไฟฟ้าส่วนภูมิภาค

ผู้ว่าการ 24.ก.ย.27

การติดตั้ง พีที. และซีที. สำหรับมิเตอร์แรงสูง 33 kV
จ่ายโหลดผ่านเคเบิลใต้ดิน

PT. & CT. INSTALLATION FOR H.T. METER 33 kV
UNDERGROUND LOAD

ใช้แทนแบบ
ถูกแทนโดยแบบ
เขียนเสร็จวันที่ 17 ก.ย. 27
แก้แบบวันที่
มิติเป็น
มาตราส่วน

แบบเลขที่ SAI-015/27017
แผ่นที่ 4 ของจำนวน 4 แผ่น

21 ก.ย.