การประกอบเลขที่
ASSEMBLY NO. 3403

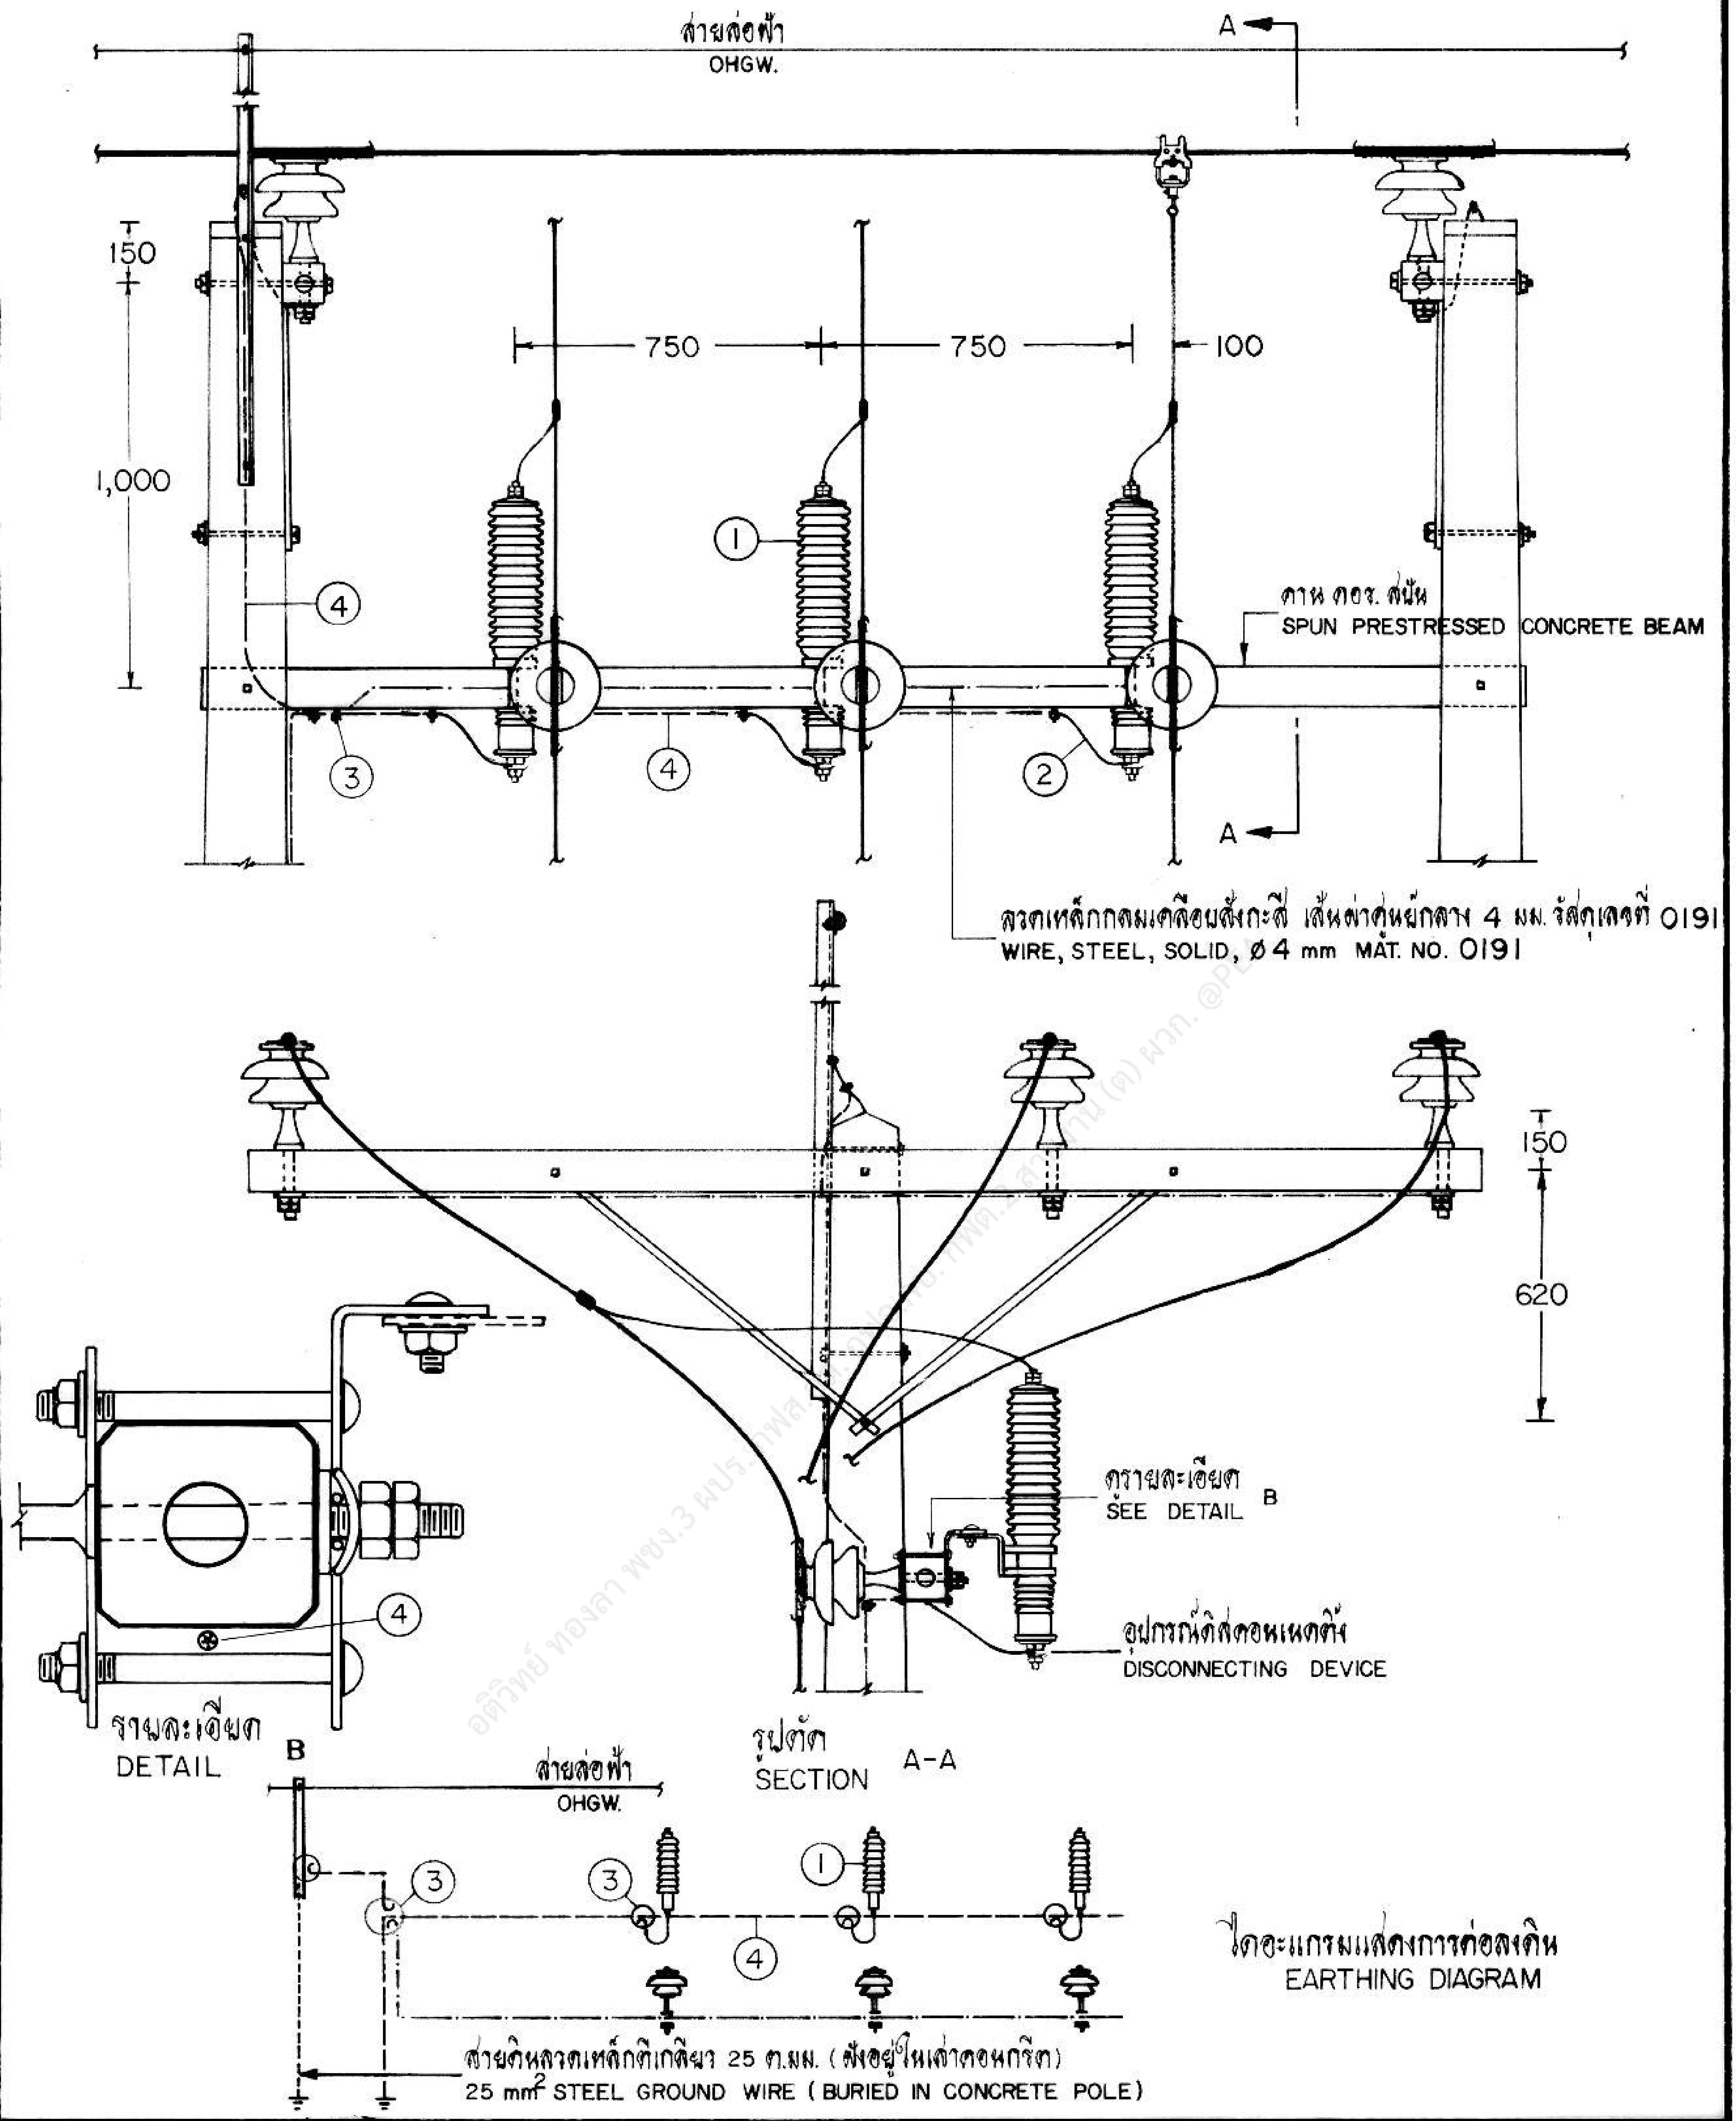
สายล่อฟ้า
OHGW.
A
150
1,000
750
750
100
①
②
③
④
คาน คอร. สปัน
SPUN PRESTRESSED CONCRETE BEAM
A
ลวดเหล็กกลมเคลือบสังกะสี เส้นผ่าศูนย์กลาง 4 มม. วัสดุเลขที่ 0191
WIRE, STEEL, SOLID, ⌀4 mm MAT. NO. 0191
150
620
ดรายละเอียด
SEE DETAIL B
อุปกรณ์ดิสคอนเนคติ้ง
DISCONNECTING DEVICE
รายละเอียด
DETAIL
B
รูปตัด
SECTION A-A
สายล่อฟ้า
OHGW.
ไดอะแกรมแสดงการต่อลงดิน
EARTHING DIAGRAM
สายดินลวดเหล็กตีเกลียว 25 ต.มม. (ฝังอยู่ในเสาคอนกรีต)
25 mm² STEEL GROUND WIRE (BURIED IN CONCRETE POLE)

กองวิศวกรรมไฟฟ้าและเครื่องกล
ฝ่ายวิศวกรรม

ผู้เขียน
ผู้สำรวจ
วิศวกร
หัวหน้าแผนก
หัวหน้ากอง
ผู้อำนวยการฝ่าย
รองผู้ว่าการฝ่ายเทคนิค

การไฟฟ้าส่วนภูมิภาค

ผู้ว่าการ

การติดตั้งล่อฟ้าแรงสูง พร้อมอุปกรณ์ดิสคอนเนคติ้ง
ระบบ 33 kV
ก ที่เสาต้นหม้อแปลง

33 kV LIGHTNING ARRESTER
COMPLETE WITH DISCONNECTING DEVICE INSTALLATION
A ON POLE AT TRANSFORMER STATION

ใช้แทนแบบ
ถูกแทนโดยแบบ
เขียนเสร็จวันที่ 21 มิ.ย. 21
แก้แบบวันที่ 24 ม.ค. 27
มิติเป็น มม.
มาตราส่วน 1 : 25
แบบเลขที่ SAI-015/21037
แผ่นที่ 1 จากจำนวน 3 แผ่น

การประกอบเลขที่
ASSEMBLY NO. 3403

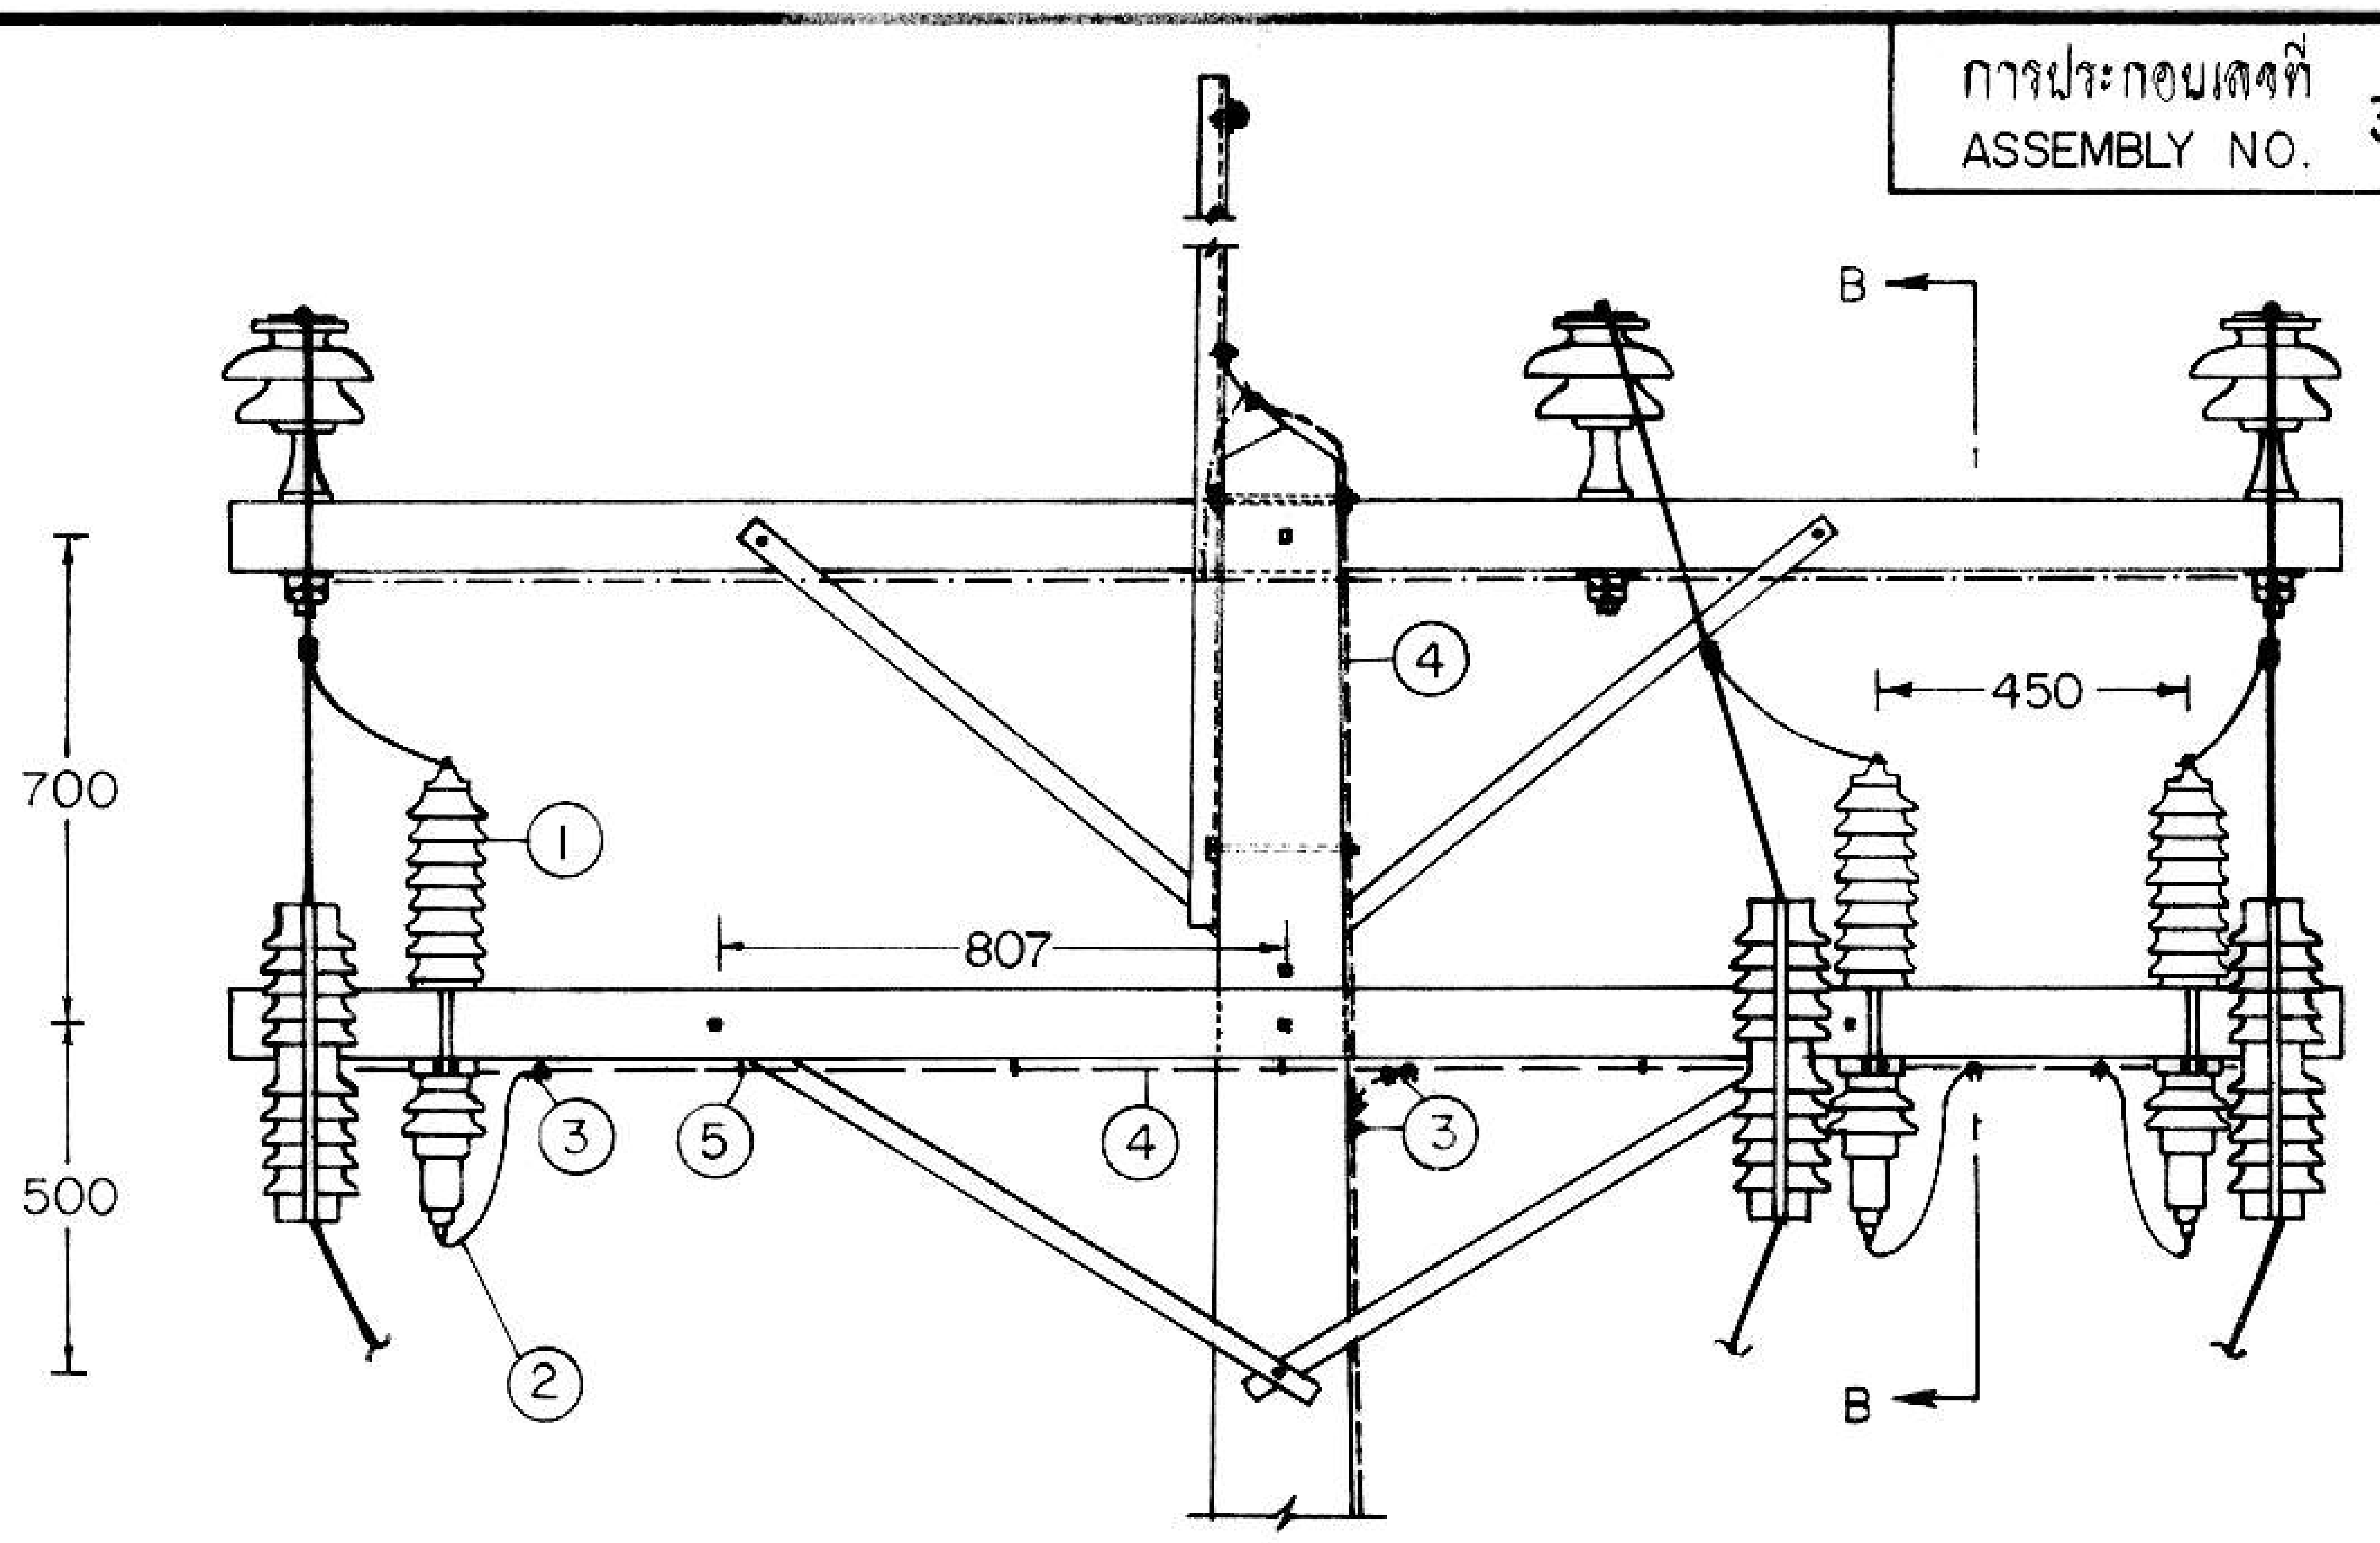
B
B
700
500
807
450
①
②
③
④
⑤

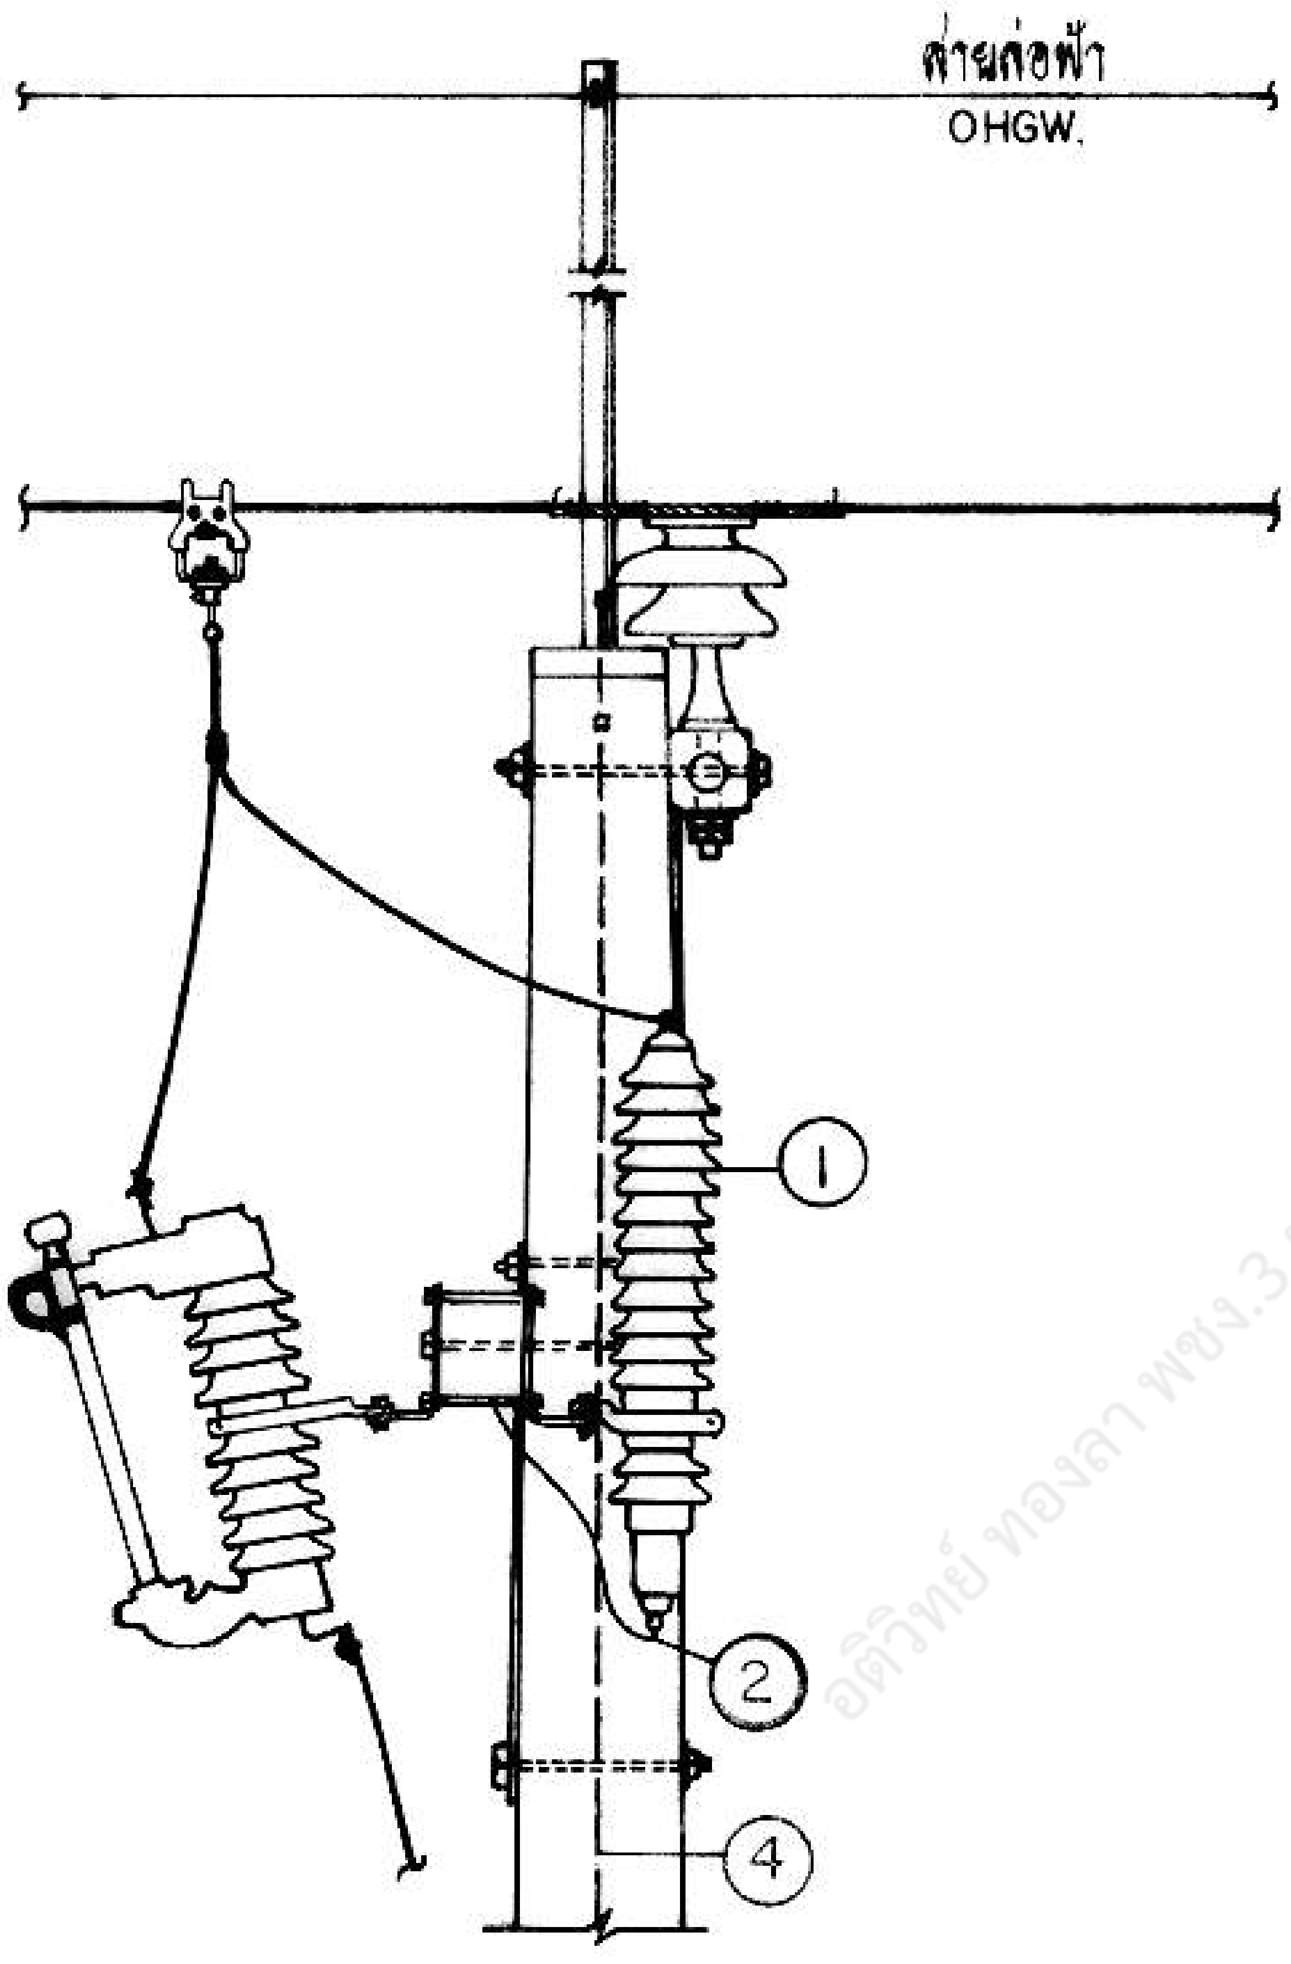
สายล่อฟ้า
OHGW.
①
②
④

รูปตัด
SECTION B-B

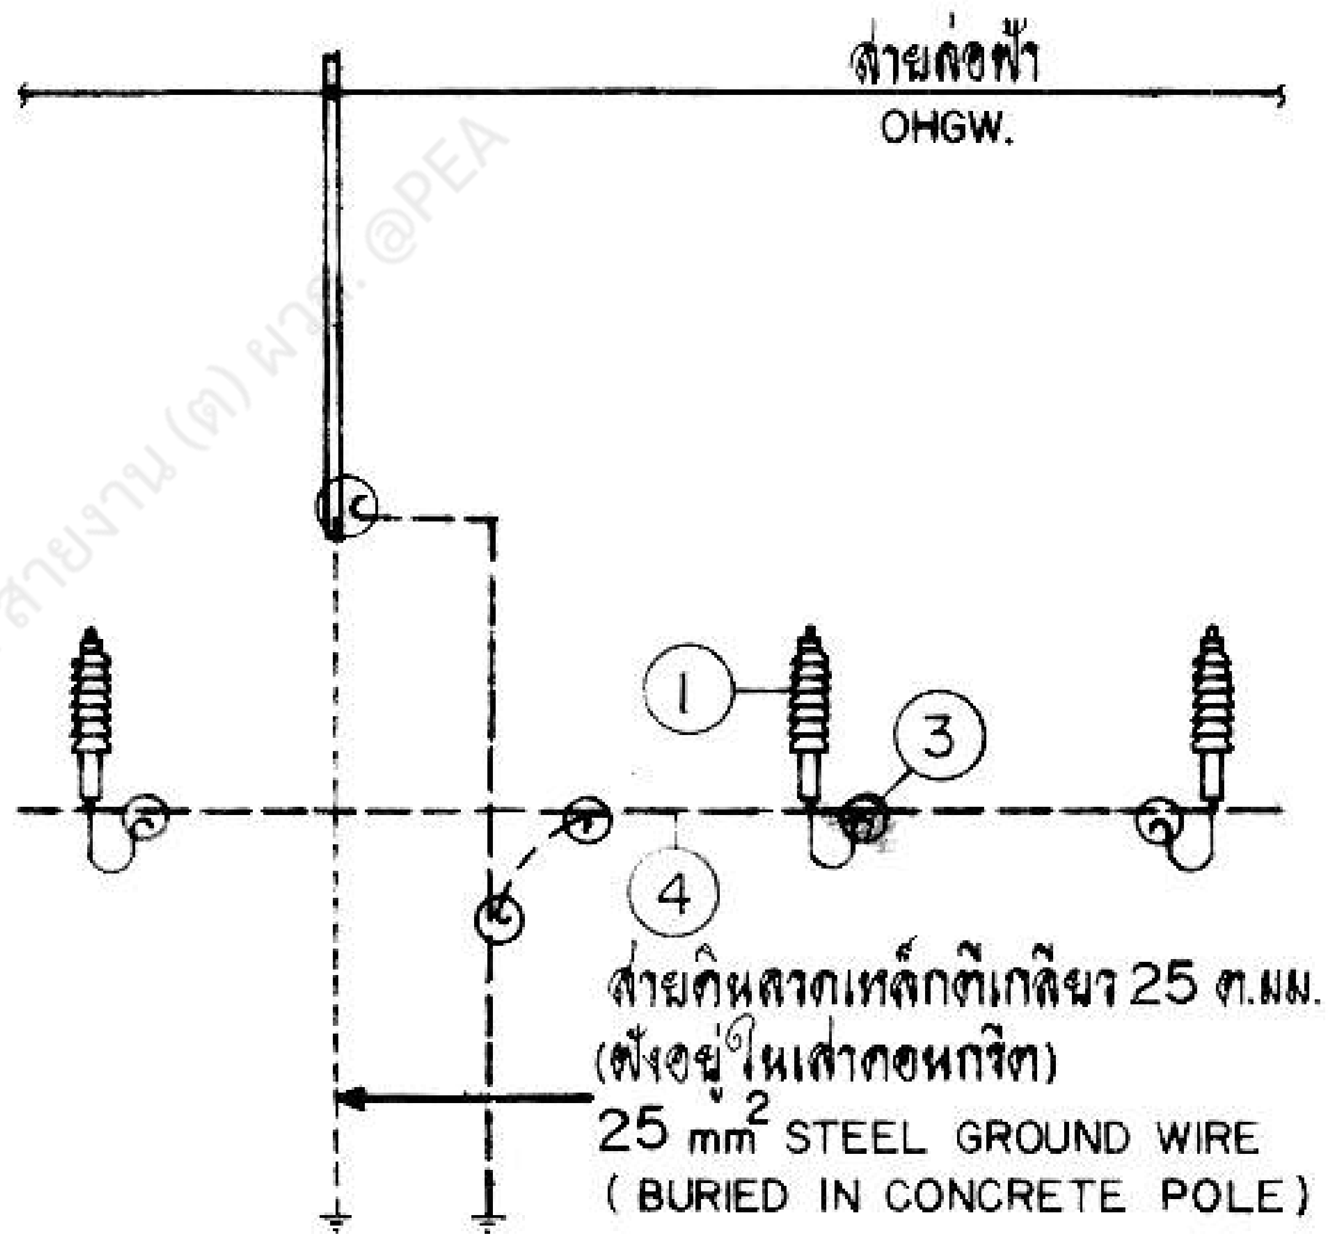
สายล่อฟ้า
OHGW.
①
③
④
สายดินลวดเหล็กตีเกลียว 25 ต.มม.
(ฝังอยู่ในเสาคอนกรีต)
25 mm² STEEL GROUND WIRE
(BURIED IN CONCRETE POLE)

ไดอะแกรมแสดงการต่อลงดิน
EARTHING DIAGRAM

อดิวิทย์ ทองลา พชง.3 ผบร. กฟส.อล. กฟจ.กบ. กฟต.2 สายงาน (ต) ผวก. @PEA

กองวิศวกรรมไฟฟ้าและเครื่องกล
ฝ่ายวิศวกรรม

ผู้เขียน
ผู้สำรวจ
วิศวกร
หัวหน้าแผนก
หัวหน้ากอง
ผู้อำนวยการฝ่าย

รองผู้ว่าการฝ่ายเทคนิค

การไฟฟ้าส่วนภูมิภาค

ผู้ว่าการ
14 ก.ค. 2521

การติดตั้งล่อฟ้าแรงสูง พร้อมอุปกรณ์ดิสคอนเนคติ้ง
ระบบ 33 kV
ข สำหรับป้องกันอุปกรณ์ไฟฟ้า

33 kV LIGHTNING ARRESTER
COMPLETE WITH DISCONNECTING DEVICE INSTALLATION
B FOR EQUIPMENT PROTECTION

ใช้แทนแบบ
ถูกแทนโดยแบบ
เขียนเสร็จวันที่ 21 มิ.ย. 21
แก้แบบวันที่
มิติเป็น มม.
มาตราส่วน 1 : 25

แบบเลขที่ SA1-015/21037
แผ่นที่ 2 ของจำนวน 3 แผ่น

การประกอบเลขที่
ASSEMBLY NO. 3403

บัญชีวัสดุ
BILL OF MATERIAL

ลำดับที่ ITEM	รายละเอียด DESCRIPTION	จำนวน REQ'D ก/A	 ข/B	วัสดุเลขที่ MAT NO.
1	ล่อฟ้าแรงสูง 30 kV, 5 กิโลแอมป์ พร้อมอุปกรณ์ดิสคอนเนคติ้ง และอุปกรณ์ติดตั้ง LIGHTNING ARRESTER, 30 kV, 5 kA COMP. WITH DISCONNECTING DEVICES AND MOUNTING ACCESS.	3	3	04000100
2	สายทองแดงตีเกลียวเปลือยอ่อน ขนาด 16 หรือ 25 ต.มม. CONDUCTOR, Cu STRANDED, FLEXIBLE, BARE 16 OR 25 mm^2	2 ม. m	2 ม. m	02000000 or 02000001
3	ยูแคล้มป์ สลัก 1 ตัว M 8 (ไวร์ โร้ป คลิ๊พ) CLAMP, SINGLE U-BOLT, M 8 (WIRE ROPE CLIP)	6	8	01230000
4	ลวดเหล็กตีเกลียว 50/7 ต.มม. มอก. 404 WIRE, STEEL STRANDED 50/7 mm^2 TIS 404	ม. m	ม. m	01100004
5	ตะปูส่องขาอาบสังกะสี สำหรับสายกลม 25-50 ต.มม. STAPLE, GALV. FOR ROUND CONDUCTOR 25-50 mm^2	–	7	01990003 01990004

หมายเหตุ

1. สำหรับล่อฟ้าแรงสูงที่จัดซื้อรุ่นใหม่ จะมีสายทองแดงอ่อนหุ้มฉนวน พร้อมคอนเนคเตอร์สำหรับต่อสายดินมาครบชุดแล้ว ให้ตัดรายการที่ 2 ออก และลดจำนวนรายการที่ 3 ลง 3 ชุด
2. สำหรับแบบ ก กรณีติดตั้งล่อฟ้าแรงสูงบนคานไม้เนื้อแข็ง ให้ยึดสายดินลวดเหล็กตีเกลียวด้วยตะปูส่องขาอาบสังกะสี ทุกระยะ 500 มม. และไม่ต้องต่อก้านลูกถ้วย และอุปกรณ์ที่ยึดล่อฟ้าด้วยลวดเหล็กกลม Ø 4 มม. ลงดิน
3. สายล่อฟ้าให้ต่อลงดินร่วมกับสายดินของล่อฟ้าแรงสูงด้วย เพื่อช่วยลดความต้านทานดินของสายดิน

NOTES

1. FOR NEW PURCHASE, A SET OF H.T. LIGHTNING ARRESTER SHALL BE COMPLETELY FURNISHED WITH DISCONNECTING DEVICE, FLEXIBLE Cu INSULATED EARTH LEAD, AND EARTH CONNECTOR: SO LEAVE OUT ITEM 2 AND REDUCE THE QUANTITY OF ITEM 3 TO 3 SETS.
2. FOR DESIGN A, IN CASE OF H.T. LIGHTNING ARRESTER INSTALLATION ON HARDWOOD BEAM, EARTH LEAD WIRE, STEEL STRANDED SHALL BE FIXED WITH STAPLE AT 500 mm INTERVALS. INSULATOR PIN AND MOUNTING BRACKET SHALL NOT BE BONDED TO GROUND BY Ø 4 mm SOLID STEEL WIRE.
3. THE OVERHEAD GROUND WIRE SHALL BE CONNECTED TO GROUND LEAD OF H.T. LIGHTNING ARRESTER IN ORDER TO REDUCE THE EARTH ELECTRODE RESISTANCE.

กองวิศวกรรมไฟฟ้าและเครื่องกล
ฝ่ายวิศวกรรม

ผู้เขียน
ผู้ตรวจ
วิศวกร
หัวหน้าแผนก
หัวหน้ากอง
ผู้อำนวยการฝ่าย

รองผู้ว่าการฝ่ายเทคนิค

การไฟฟ้าส่วนภูมิภาค

ผู้ว่าการ
14 ก.ค. 2521

การติดตั้งล่อฟ้าแรงสูง พร้อมอุปกรณ์ดิสคอนเนคติ้ง
ระบบ 33 kV

33 kV LIGHTNING ARRESTER
COMPLETE WITH DISCONNECTING DEVICE INSTALLATION

ใช้แทนแบบ
ถูกแทนโดยแบบ
เขียนเสร็จวันที่ 21 มิ.ย. 21
แก้แบบครั้งที่
มิติเป็น
มาตราส่วน

แบบเลขที่ SAI-015/21037
แผ่นที่ 3 ของจำนวน 3 แผ่น