การประกอบเลขที่ ASSEMBLY NO. 5226

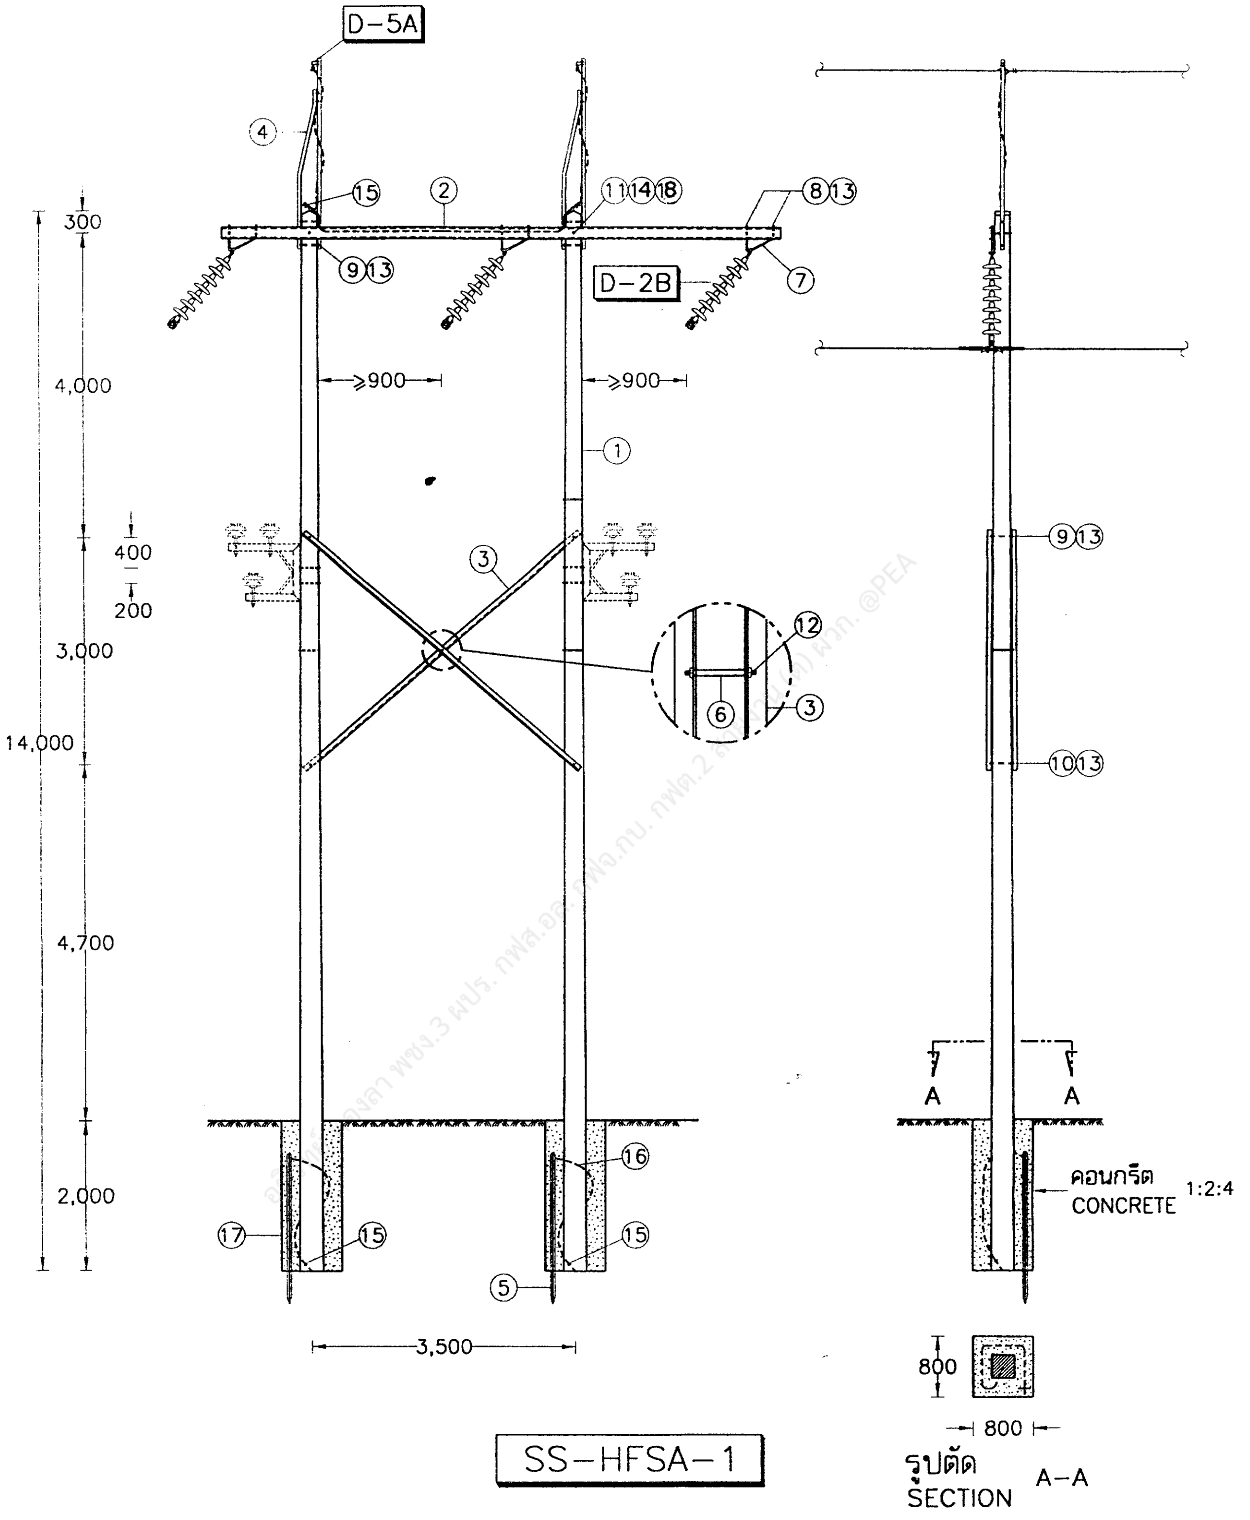

กองวิศวกรรมไฟฟ้าและเครื่องกล
ฝ่ายวิศวกรรม

การไฟฟ้าส่วนภูมิภาค

ใช้แทนแบบ ....
ถูกแทนโดยแบบ ....

ผู้เขียน Sippthalat Bamrung
ผู้สำรวจ..................
วิศวกร.......................
หัวหน้าแผนก..................
ผู้อำนวยการกอง...............
ผู้อำนวยการฝ่าย..............

ผู้ว่าการ.............................23 ธ.ค. 2541

เขียนเสร็จวันที่ 14 ต.ค. 2541
แก้แบบวันที่ ....
มิติเป็น มิลลิเมตร
มาตราส่วน 1 : 100

แบบโครงสร้างสายส่ง 115 kV วงจรเดี่ยว สายไฟฟ้าเดี่ยว เสาคู่สำหรับทางโค้งแบบ H-FRAME ใช้เสาขนาด 14 ม. แบบ SS-HFSA-1

รองผู้ว่าการเทคนิคและบริการ
....

115 kV LINE STRUCTURE CONSTRUCTION, SINGLE CIRCUIT SINGLE CONDUCTOR, H-FRAME ANGLE STRUCTURE, 14 m POLE TYPE SS-HFSA-1

แบบเลขที่ SA1-015/41021
แผ่นที่ 1 ของจำนวน 3 แผ่น

23 ธ.ค. 2541

การประกอบเลขที่
ASSEMBLY NO. **5 2 2 6**

บัญชีวัสดุ
BILL OF MATERIAL

ลำดับที่ ITEM	รายละเอียด DESCRIPTION	จำนวน REQ'D	วัสดุเลขที่ MAT. NO.
1	เสาคอนกรีต 14 เมตร POLE, CONCRETE, 14 m LONG	2	00010006
2	เหล็กรูปรางน้ำ ขนาด 150x75x6.5 มม. ยาว 7.40 ม. (ดูรายละเอียด A) STEEL CHANNEL 150x75x6.5 mm, 7.40 m LONG (SEE DETAIL A)	1	–
3	เหล็กฉาก ขนาด 75x75x6 มม. ยาว 4.83 ม. (ดูรายละเอียด B) STEEL ANGLE 75x75x6 mm, 4.83 m LONG (SEE DETAIL B)	2	–
4	เหล็กฉากรับสายล่อฟ้าทางโค้ง ขนาด 65x65x6 มม. ยาว 2.50 ม. มอก. 116 OVERHEAD GROUND WIRE CORNER BAYONET, 65x65x6 mm, 2.50 m LONG TIS 116	2	01010005
5	หลักดิน ขนาด 60x60x5 มม. ยาว 2 ม. ROD, GROUND, 60x60x5 mm, 2 m LONG	2	01220002
6	ท่อเหล็ก ขนาด 20 มม. หนา 2.65 มม. ยาว 220 มม. PIPE, IRON DIA. 20 mm ID, 2.65 mm THICKNESS, 220 mm LONG	1	–
7	ที่แขวนลูกถ้วยทางโค้ง BRACKET, CORNER SUSPENSION	3	03140012
8	สลักเกลียว M 16x200 มม. BOLT, MACHINE, M 16x200 mm	6	01110202
9	สลักเกลียว M 16x250 มม. BOLT, MACHINE, M 16x250 mm	6	01110203
10	สลักเกลียว M 16x300 มม. BOLT, MACHINE, M 16x300 mm	2	01110204
11	สลักเกลียว M 20x250 มม. BOLT, MACHINE, M 20x250 mm	2	–
12	สลักเกลียวตลอด M 16x400 มม. BOLT, DOUBLE ARMING, M 16x400 mm	1	01120000
13	แหวนสี่เหลี่ยมแบน 52x52x4.5 มม. รู ø18 มม. มอก. 258 WASHER, SQUARE, FLAT 52x52x4.5 mm, HOLE ø18 mm TIS 258	28	01180100
14	แหวนสปริง M 20 มอก. 259 WASHER, LOCK, M 20 TIS 259	2	01180302
15	ยูแคล้มป์สลัก 1 ตัว M 8 CLAMP, SINGLE U-BOLT, M 8	12	01230000
16	ลวดเหล็กตีเกลียว 50 ต.มม. WIRE, STEEL STRANDED 50 mm^2	15 ม. m	01100004
17	คอนกรีต 1 : 2 : 4 CONCRETE 1 : 2 : 4	1.8 ม.^{3} m^3	–
18	แหวนสี่เหลี่ยมแบน 62x62x6 มม. รู ø 22 มม. มอก. 258 WASHER, SQUARE, FLAT 62x62x6 mm, HOLE ø 22 mm TIS 258	4	01180101

กองวิศวกรรมไฟฟ้าและเครื่องกล
ฝ่ายวิศวกรรม

การไฟฟ้าส่วนภูมิภาค

ใช้แทนแบบ ....
ถูกแทนโดยแบบ ....

ผู้เขียน Suphachit Boonruang
ผู้สำรวจ ....
วิศวกร ....
หัวหน้าแผนก ....
ผู้อำนวยการกอง ....
ผู้อำนวยการฝ่าย ....

ผู้ว่าการ .... 23 ธ.ค. 2541

เขียนเสร็จวันที่ 14 ต.ค. 2541
แก้แบบวันที่ ....
มิติเป็น ....
มาตราส่วน ....

แบบโครงสร้างสายส่ง 115 kV วงจรเดี่ยว สายไฟฟ้าเดี่ยว
เสาคู่สำหรับทางโค้งแบบ H-FRAME ใช้เสาขนาด 14 ม.
แบบ SS-HFSA-1

115 kV LINE STRUCTURE CONSTRUCTION, SINGLE CIRCUIT
SINGLE CONDUCTOR, H-FRAME ANGLE STRUCTURE, 14 m POLE
TYPE SS-HFSA-1

รองผู้ว่าการเทคนิคและบริการ
....

แบบเลขที่ SA1-015/41021
แผ่นที่ 2 ของจำนวน 3 แผ่น

23 ธ.ค. 2541

กฟส.อล. กฟจ.กน. กฟต.2 สายงาน (ต) ผวก. @PEA

การประกอบเลขที่
ASSEMBLY NO. **5 2 2 6**

รายละเอียด DETAIL			
D-2B	การประกอบลูกถ้วยแขวน SUSPENSION INSULATOR ASSEMBLY	3	
D-5A	การต่อสายล่อฟ้า OVERHEAD GROUND WIRE CONNECTION	2	

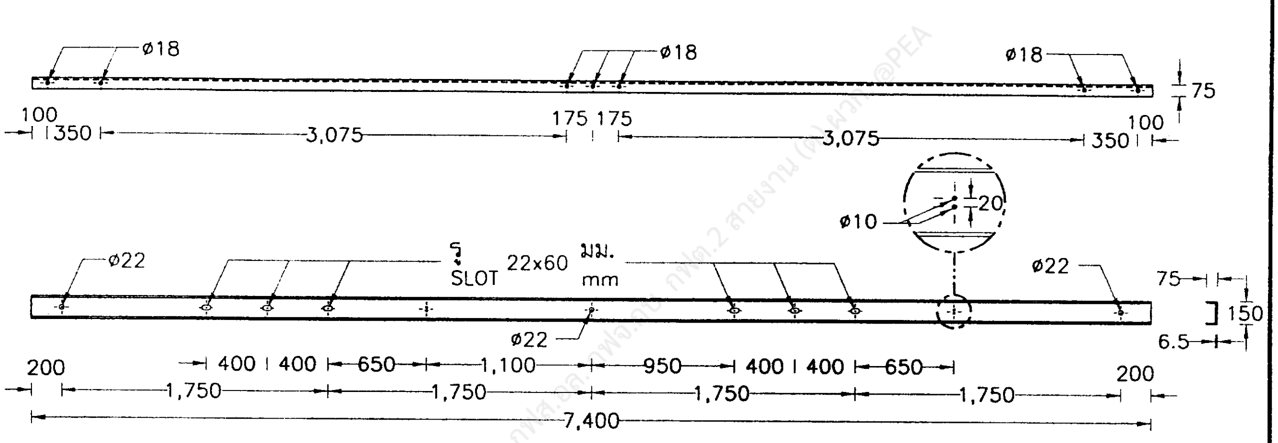

รายละเอียด **A**
DETAIL

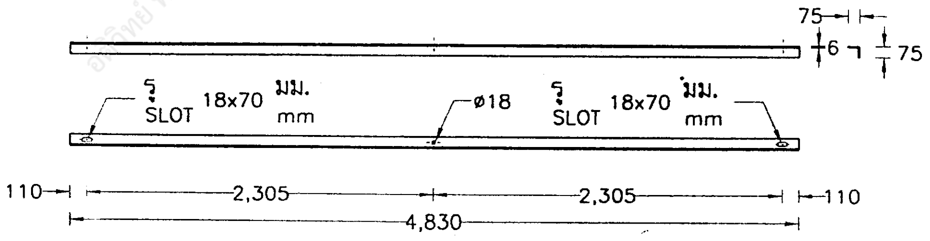

รายละเอียด **B**
DETAIL

อภิสิทธิ์ ทองลา พชง.3 ผปร. กฟส.อล. กฟจ.อด. กฟต.2 สายงาน (ต) ผวก. @PEA

กองวิศวกรรมไฟฟ้าและเครื่องกล ฝ่ายวิศวกรรม	การไฟฟ้าส่วนภูมิภาค	ใช้แทนแบบ .... ถูกแทนโดยแบบ .... เขียนเสร็จวันที่ 14 ต.ค. 2541
ผู้เขียน Suppakit Boonrueng ผู้สำรวจ .... วิศวกร .... หัวหน้าแผนก .... ผู้อำนวยการกอง .... ผู้อำนวยการฝ่าย	ผู้ว่าการ .... 23 ธ.ค. 2541 แบบโครงสร้างสายส่ง 115 kV วงจรเดี่ยว สายไฟฟ้าเดี่ยว เสาคู่สำหรับทางโค้งแบบ H-FRAME ใช้เสาขนาด 14 ม. แบบ SS-HFSA-1	แก้แบบวันที่ .... มิติเป็น มิลลิเมตร มาตราส่วน 1 : 50
รองผู้ว่าการเทคนิคและบริการ	115 kV LINE STRUCTURE CONSTRUCTION, SINGLE CIRCUIT SINGLE CONDUCTOR, H-FRAME ANGLE STRUCTURE, 14 m POLE TYPE SS-HFSA-1	แบบเลขที่ SA1-015/41021 แผ่นที่ 3 ของจำนวน 3 แผ่น

23 ธ.ค. 2541