การประกอบเลขที่ 7907
ASSEMBLY NO. 5452

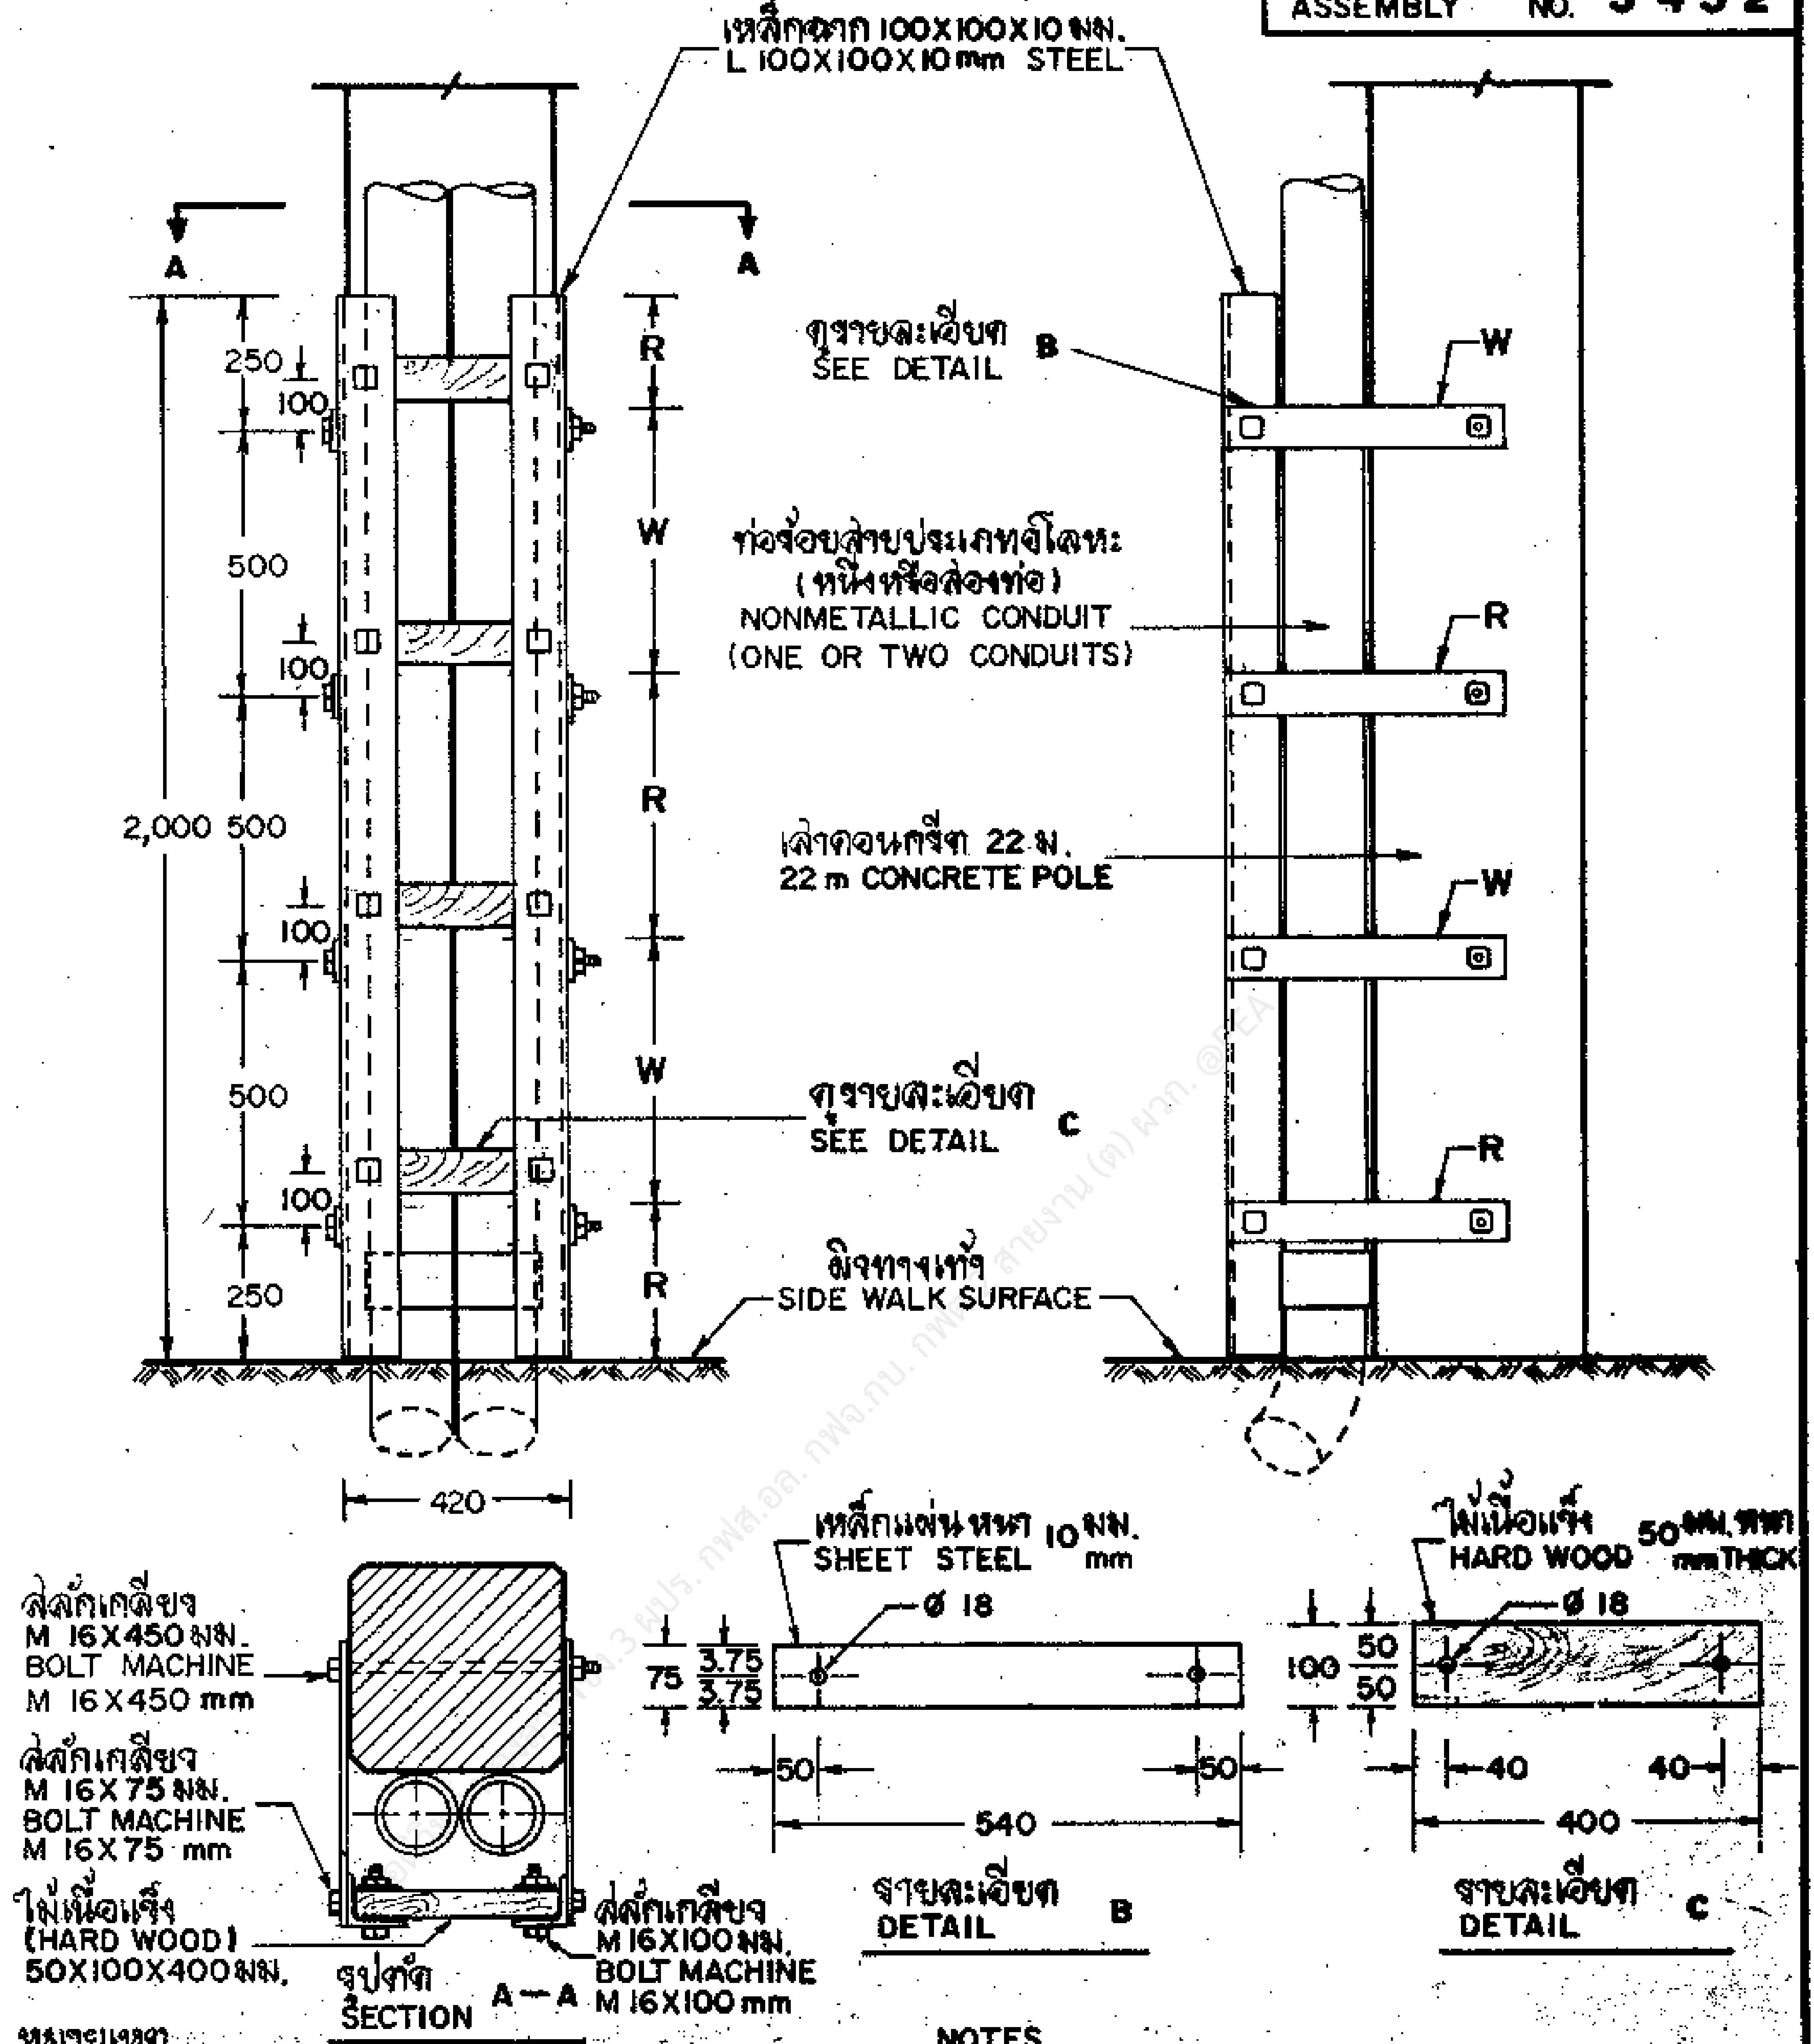

หมายเหตุ

1. "R" และ "W" เป็นช่วงให้ทาสี แดง และ ขาว ตามลำดับ บนโครงกั้น
2. โครงกั้น สามารถติดตั้งได้ทั้งทิศเดียวกัน และทิศทางข้ามกับการจราจร แต่ทั่วไปนิยมติดตั้งในทิศทางข้ามกับการจราจร

NOTES

1. "R" AND "W" INDICATE PARTS OF STEEL GUARD PAINTED IN RED AND WHITE RESPECTIVELY .
2. AWAY OR AGAINST TRAFFIC CONSTRUCTION SHALL BE SELECTED AS SUITABLY, BUT AWAY TRAFFIC CONSTRUCTION IS GENERALLY PREFERABLE .

กองวิศวกรรมไฟฟ้าและเครื่องกล ฝ่ายวิศวกรรม	# การไฟฟ้าส่วนภูมิภาค	ใช้แทนแบบ ถูกแทนที่โดยแบบ
ผู้เขียน สมพงษ์ ผู้สำรวจ วิศวกร หัวหน้าแผนก ผู้อำนวยการกอง ผู้อำนวยการฝ่าย	ผู้ว่าการ 23 ส.ค. 34 การติดตั้งโครงกั้น (สำหรับท่อร้อยสายขึ้นเสาระบบ 69 kV, 115 kV) เสาคอนกรีต 22 ม.	เริ่มแต่วันที่ 9 ต.ค. 34 แก้ไขแล้วที่ มิติเป็น มิลลิเมตร มาตราส่วน 1 : 12.5, 1 : 20
รองผู้ว่าการฝ่ายเทคนิค	GUARD CONSTRUCTION (FOR 69 kV, 115 kV RISER POLE) 22 m CONCRETE POLE	แบบเลขที่ SAI-015/34031 แผ่นที่ 1 ของจำนวน 1 แผ่น

23 ส.ค. 2534