การประกอบเลขที่
ASSEMBLY NO. **3508**

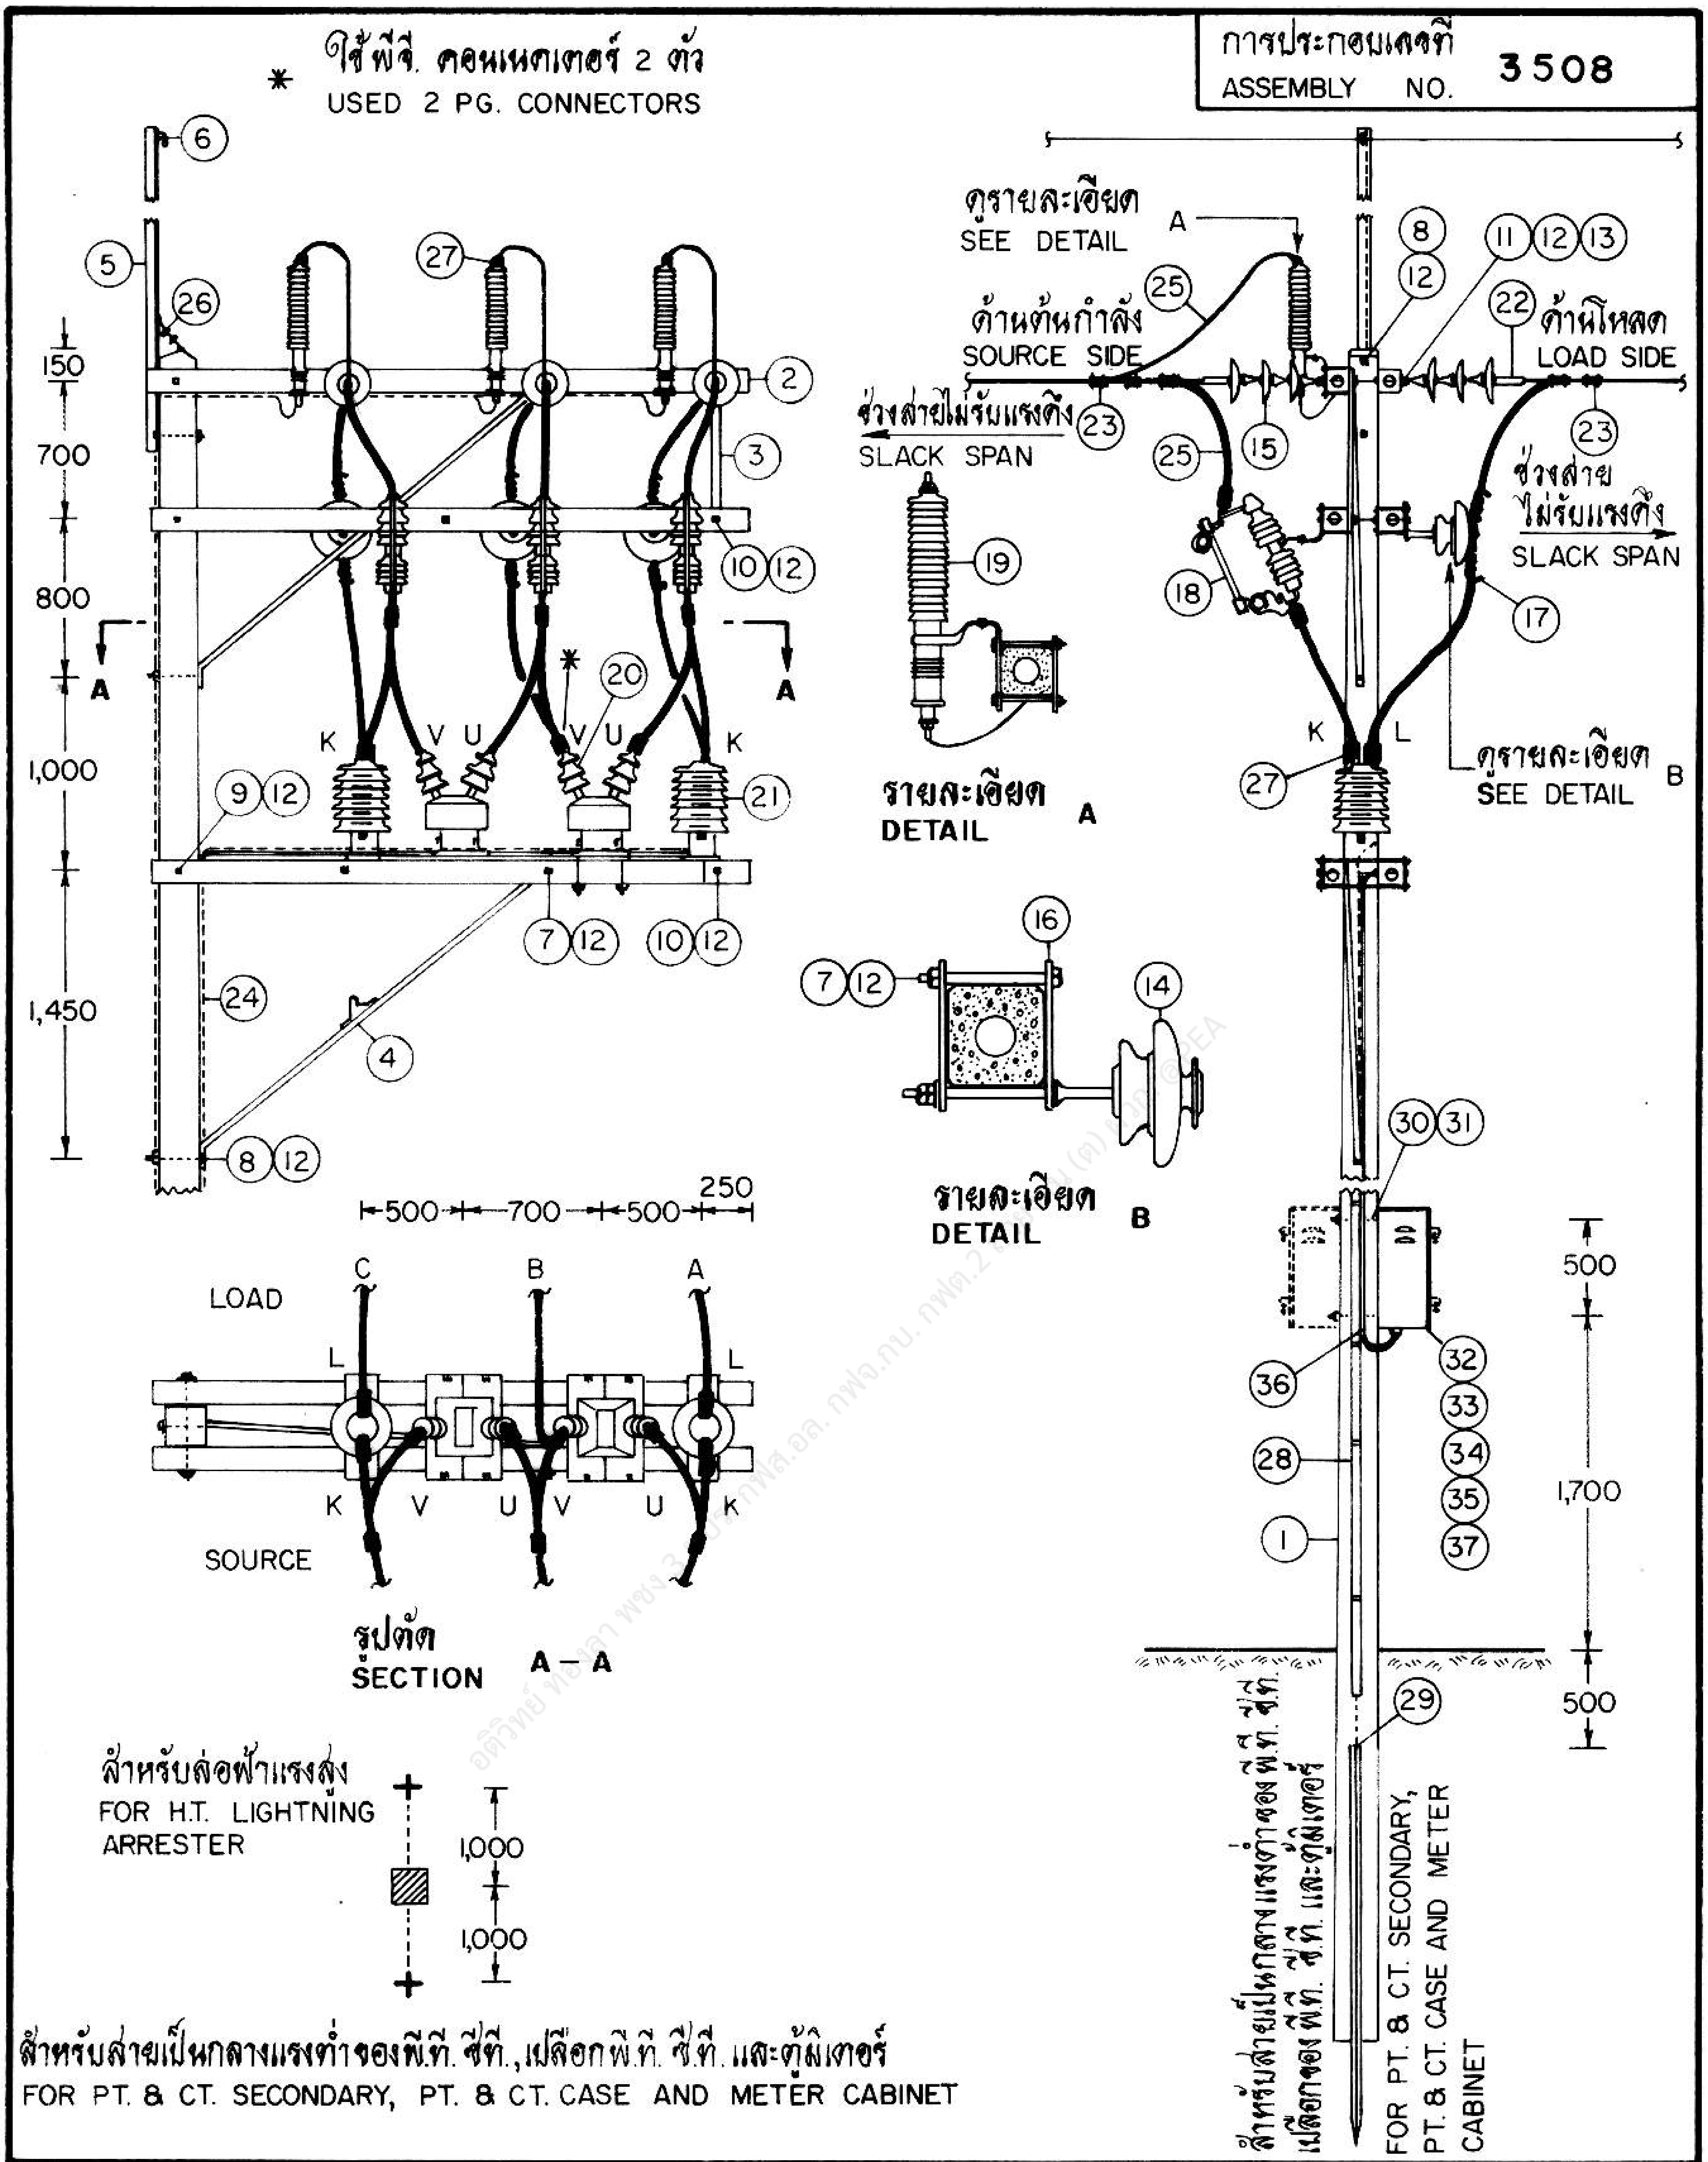

รายละเอียด
DETAIL A

รายละเอียด
DETAIL B

รูปตัด
SECTION A – A

สำหรับสายเป็นกลางแรงต่ำของพี.ที. ซี.ที., เปลือกพี.ที. ซี.ที. และตู้มิเตอร์
FOR PT. & CT. SECONDARY, PT. & CT. CASE AND METER CABINET

กองวิศวกรรมไฟฟ้าและเครื่องกล ฝ่ายวิศวกรรม	# การไฟฟ้าส่วนภูมิภาค	ใช้แทนแบบ ถูกแทนโดยแบบ
ผู้เขียน ผู้สำรวจ วิศวกร หัวหน้าแผนก ผู้อำนวยการกอง ผู้อำนวยการฝ่าย	ผู้ว่าการ (แทน) 17 มิย. 2535 การติดตั้งมิเตอร์ 3 เฟส 3 สาย 33 kV ประกอบพี.ที. และซี.ที. (กรณีประกอบคอนแขนท้าวแขน)	เขียนเสร็จวันที่ 2 มค. 35 แก้แผ่นที่ มิติเป็น มิลลิเมตร มาตราส่วน 1 : 50
รองผู้ว่าการฝ่ายเทคนิค	INSTALLATION OF 33 kV, 3-Ø, 3-W, METER WITH P.T. & C.T. (ALLEY ARM)	แผนเลขที่ SAI-015/35001 แผ่นที่ 1 ของจำนวน 5 แผ่น

16

การประกอบเลขที่
ASSEMBLY NO. **3508**

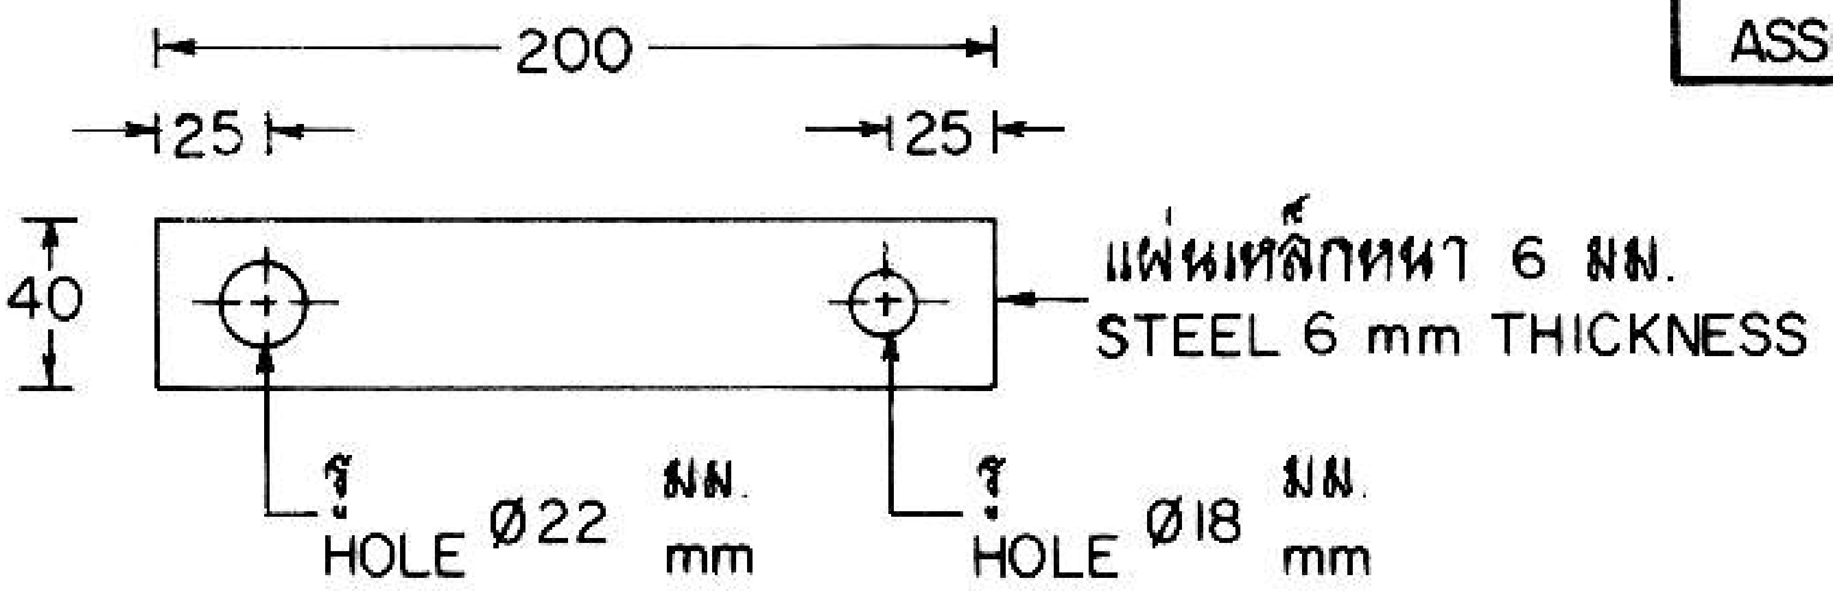

วัสดุลำดับที่ ⑯
MAT ITEM

(อาจทำจากเหล็กประกับ วัสดุเลขที่ 01200002 ได้
MAY BE MADE OF BRACE MAT. NO. 01200002)

รายละเอียด
DETAIL C

บัญชีวัสดุสำหรับการประกอบคอน, สายไฟฟ้า, อุปกรณ์ป้องกัน, พี.ที. และซี.ที.
BILL OF MATERIAL FOR CROSSARMS, CONDUCTORS, PROTECTIVE EQUIPMENTS, P.T. AND C.T. ASSEMBLY

ลำดับที่ ITEM	รายละเอียด DESCRIPTION	จำนวน REQ'D	วัสดุเลขที่ MAT. NO.
1	เสาคอนกรีต 12 ม. POLE, CONCRETE, 12 m LONG	1	00010004
2	คอน คอร. สปัน ขนาด 120 X 120 X 3,000 มม. CROSSARM, SPUN, PRESTRESSED CONCRETE, 120 X 120 X 3,000 mm	6	00110002
3	เหล็กประกับคอน 30 X 6 X 760 มม. BRACE, FLAT, FOR CROSSARM, 30 X 6 X 760 mm	1	01200001
4	เหล็กประกับคอนแบบท้าวแขน 50 X 50 X 5 มม. ยาว 2,350 มม. BRACE, ALLEY ARM, 50 X 50 X 5 mm, 2,350 mm LONG	2	01200005
5	เหล็กฉากรับสายล่อฟ้า OVERHEAD GROUND WIRE BAYONET	1	01010006 or 01010003
6	กราวด์วายแคล้มป์ แบบ J 1152 GROUND WIRE CLAMP, J 1152	1	01230205
7	สลักเกลียว M 16 X 170 มม. BOLT, MACHINE, M 16 X 170 mm	4	01110201
8	สลักเกลียว M 16 X 250 มม. BOLT, MACHINE, M 16 X 250 mm	4	01110203
9	สลักเกลียว M 16 X 450 มม. BOLT, MACHINE, M 16 X 450 mm	3	01110207
10	สลักเกลียวตลอด M 16 X 500 มม. BOLT, DOUBLE ARMING, M 16 X 500 mm	4	01120002
11	สลักเกลียวห่วงกลม M 16 X 450 มม. BOLT, DOUBLE ARMING, ROUND EYE, M 16 X 450 mm	3	01130002
12	แหวนสี่เหลี่ยมแบน 52 X 52 X 4.5 มม. รู Ø 18 มม. มอก. 258 WASHER, SQUARE, FLAT, 52 X 52 X 4.5 mm, HOLE Ø 18 mm, TIS 258	39	01180100
13	นัทรูปห่วง M 16 DIN 582 NUT, EYE, M 16, DIN 582	3	01180001
14	ลูกถ้วยก้านตรง 33 kV มอก. 279 แบบ ค (แบบ 56-3);พร้อมก้าน INSULATOR, PIN TYPE, 33 kV, TIS 279, TYPE C (CLASS 56-3);COMP. WITH PIN	3	03000002 03100001

3 ผปร. กฟส.อล. กฟจ.กบ. กฟต.2 สายงาน (ต) ผวก. @PEA

กองวิศวกรรมไฟฟ้าและเครื่องกล
ฝ่ายวิศวกรรม

ผู้เขียน
ผู้สำรวจ
วิศวกร
หัวหน้าแผนก
ผู้อำนวยการกอง
ผู้อำนวยการฝ่าย

รองผู้ว่าการฝ่ายเทคนิค

การไฟฟ้าส่วนภูมิภาค

ผู้ว่าการ (แทน) 17 ต.ย. 2535

การติดตั้งมิเตอร์ 3 เฟส 3 สาย 33 kV ประกอบ พี.ที. และซี.ที.
(กรณีประกอบคอนแบบท้าวแขน)

INSTALLATION OF 33 kV, 3-Ø, 3-W, METER WITH P.T. & C.T.
(ALLEY ARM)

ใช้แทนแบบ
ถูกแทนโดยแบบ
เขียนเสร็จวันที่ 2 ม.ค. 35
แก้แบบวันที่
มิติเป็น มิลลิเมตร
มาตราส่วน 1 : 5
แบบเลขที่ SAI-015/35001
แผ่นที่ 2 ของจำนวน 5 แผ่น

16

การประกอบเลขที่
ASSEMBLY NO. 3508

บัญชีวัสดุสำหรับการประกอบคอน, สายไฟฟ้า, อุปกรณ์ป้องกัน, พี.ที. และซี.ที.
BILL OF MATERIAL FOR CROSSARMS, CONDUCTORS, PROTECTIVE EQUIPMENTS, P.T. AND C.T. ASSEMBLY

ลำดับที่ ITEM	รายละเอียด DESCRIPTION	จำนวน REQ'D	วัสดุเลขที่ MAT. NO.
15	ลูกถ้วยแขวน มอก. 354 แบบ ง (แบบ 52-4) INSULATOR, SUSPENSION TYPE, TIS 354, TYPE D (CLASS 52-4)	18	03020002
16	แผ่นเหล็ก 40 X 6 มม. ยาว 200 มม. เจาะรูตามรายละเอียด C STEEL PLATE, 40 X 6 mm, 200 mm LONG; PUNCH HOLE AS DETAIL C	6	——
17	ลวดอะลูมิเนียมกลม Ø 4 มม. ความยาวตามต้องการ TIE WIRE, Al, Ø 4 mm, LENGTH AS REQUIRED	ม. m	02200002
18	ดรอพเอาท์ ฟิวส์คัทเอาท์ หนึ่งอินซูเลเตอร์ 33 kV, 100 A CUTOUT, FUSE, OPEN TYPE, SINGLE INSULATOR, DROPOUT, 33 kV, 100 A	3	04010100
19	ล่อฟ้าแรงสูง 30 kV, 5 kA LIGHTNING ARRESTER, 30 kV, 5 kA	3	04000100
20	พี.ที. หนึ่งเฟส ใช้นอกอาคาร 33,000-110 V พร้อมอุปกรณ์ติดตั้ง TRANSFORMER, POTENTIAL, 1-Ø, OUTDOOR, 33,000-110 V; COMP. WITH MOUNTING ACCESS.	2	06020100
21	ซี.ที. ใช้นอกอาคาร 33 kV เรโชตามต้องการ พร้อมอุปกรณ์ติดตั้ง TRANSFORMER, CURRENT, 33 kV, RATIO AS REQUIRED; COMP. WITH MOUNTING ACCESS.	2	06040101- 06040104
22	สเตรนแคล้มป์ สำหรับสายอะลูมิเนียม ขนาดตามต้องการ CLAMP, STRAIN, FOR Al, SIZE AS REQUIRED	6	03110000- 03110101
23	พีจี. คอนเนคเตอร์ สลักคู่ สำหรับสายอะลูมิเนียม ขนาดตามต้องการ CONNECTOR, PARALLEL GROOVE, Al; SIZE AS REQUIRED	20	02300102- 02300103
24	ลวดเหล็กตีเกลียว 50/7 ต.มม. มอก. 404 STEEL STRANDED WIRE, 50/7 mm^2; TIS 404	28 ม. m	01100004
25	สายอะลูมิเนียมหุ้มฉนวน ใช้ภายนอก 750 V, 75°C ขนาด 35-95 ต.มม. CONDUCTOR, INSULATED, WEATHER-PROOF, 750 V, 75°C, Al, 35-95 mm^2	21 ม. m	02070001 or 02070004
26	ยูแคล้มป์ สลัก 1 ตัว M 8 CLAMP, SINGLE U-BOLT, M 8	7	01230000
27	เทปพันเคเบิลอากาศแรงสูง ขนาด 3/4" X 30' ELECTRICAL, SPLICING TAPE, FOR H.T. AERIAL CABLE, SIZE 3/4" X 30'	ม้วน roll	02180003
28	ท่อ PVC แข็ง ขนาด Ø 20 X 2,500-4,000 มม. พร้อมอุปกรณ์ยึด CONDUIT, PVC RIGID, Ø 20 X 2,500-4,000 mm; COMP. WITH FIXING ACCESS.	2	08040002 or 08040001
29	หลักดิน 60 X 60 X 5 มม. ยาว 2 ม. ROD, GROUND, 60 X 60 X 5 mm, 2 m LONG	2	01220002

กองวิศวกรรมไฟฟ้าและเครื่องกล
ฝ่ายวิศวกรรม

ผู้เขียน
ผู้สำรวจ
วิศวกร
หัวหน้าแผนก
ผู้อำนวยการกอง
ผู้อำนวยการฝ่าย

รองผู้ว่าการฝ่ายเทคนิค

การไฟฟ้าส่วนภูมิภาค

ผู้ว่าการ (แทน)

17 มิ.ย. 2535

การติดตั้งมิเตอร์ 3 เฟส 3 สาย 33 kV ประกอบพี.ที. และซี.ที.
(กรณีประกอบคอนแบบท้าวแขน)

INSTALLATION OF 33 kV, 3-Ø, 3-W, METER WITH P.T. & C.T.
(ALLEY ARM)

ใช้แทนแบบ
ถูกแทนโดยแบบ
เขียนเสร็จวันที่ 2 ม.ค. 35
แก้แบบวันที่
มิติเป็น
มาตราส่วน

แบบเลขที่ SAI-015/35001
แผ่นที่ 3 ของจำนวน 5 แผ่น

16

การประกอบเลขที่
ASSEMBLY NO. 3508

บัญชีวัสดุสำหรับการประกอบมิเตอร์
BILL OF MATERIAL FOR METER ASSEMBLY

ลำดับที่ ITEM	รายละเอียด DESCRIPTION	จำนวน REQ'D I	II	III	วัสดุเลขที่ MAT. NO.
30	สลักเกลียว M 16 X 300 มม. BOLT, MACHINE, M 16 X 300 mm	2	2	2	01110204
31	แหวนสี่เหลี่ยมแบน 52 X 52 X 4.5 มม. รู Ø 18 มม. มอก. 258 WASHER, SQUARE, FLAT, 52 X 52 X 4.5 mm, HOLE Ø 18 mm, TIS 258	4	4	4	01180100
32	ตู้ใส่มิเตอร์แรงสูง พร้อมแป้นไม้ ALUMINIUM METER CABINET, FOR H.T. METER ; COMP. WITH METER PLATE	1	2	2	06100008 06100001
33	ดีมานด์มิเตอร์ ชนิดสะสม 3 เฟส 3 สาย 110 โวลต์ 5 แอมป์ DEMAND METER, CUMULATIVE, 3-PHASE, 3-WIRE, 110 V, 5 A	1	–	1	06000300
34	ดีมานด์มิเตอร์ ชนิดสะสม แบบวัดค่า 2 อัตรา 3 เฟส 3 สาย 110 โวลต์ 5 แอมป์ DEMAND METER, CUMULATIVE, TWO-RATE TARIFF, 3-PHASE, 3-WIRE, 110 V, 5 A	–	1	–	4069
35	วาร์อาวร์มิเตอร์ 3 เฟส 3 สาย 110 โวลต์ 5 แอมป์ METER, VAR-HOUR, 3-PHASE, 3-WIRE, 110 V, 5 A	–	–	1	06000400
36	คอนโทรลเคเบิล ขนาด 7 X 2.5 ต.มม. CONTROL CABLE, SIZE 7 X 2.5 mm^2	10 ม. m	13 ม. m	13 ม. m	02080402
37	ตะปูเกลียว ชุบโครเมียม ขนาด 15-20 มม. SCREW, CHOME-PLATED, SIZE 15-20 mm	3	6	6	

หมายเหตุ

บัญชีวัสดุสำหรับการประกอบมิเตอร์ :—

สดมภ์ I : สำหรับการติดตั้งดีมานด์มิเตอร์

สดมภ์ II : สำหรับการติดตั้งดีมานด์มิเตอร์แบบวัดค่า 2 อัตรา

สดมภ์ III : สำหรับการติดตั้งดีมานด์มิเตอร์และ วาร์อาวร์มิเตอร์ร่วมกัน

NOTES

BILL OF MATERIAL FOR METER ASSEMBLY :—

COLUMN I : FOR DEMAND METER INSTALLATION,

COLUMN II : FOR TWO-RATE-TARIFF DEMAND METER INSTALLATION,

COLUMN III : FOR DEMAND METER AND VAR-HOUR METER COMBINDED INSTALLATION .

กองวิศวกรรมไฟฟ้าและเครื่องกล
ฝ่ายวิศวกรรม

ผู้เขียน
ผู้สำรวจ
วิศวกร สมพร
หัวหน้าแผนก
ผู้อำนวยการกอง
ผู้อำนวยการฝ่าย

รองผู้ว่าการฝ่ายเทคนิค

การไฟฟ้าส่วนภูมิภาค

ผู้ว่าการ (แทน) 17 มิ.ย. 2535

การติดตั้งมิเตอร์ 3 เฟส 3 สาย 33 kV ประกอบ พี.ที และ ซี.ที.
(กรณีประกอบคอนแบบท้าวแขน)

INSTALLATION OF 33 kV, 3-Ø, 3-W, METER WITH P.T. & C.T.
(ALLEY ARM)

ใช้แทนแบบ
ถูกแทนโดยแบบ
เขียนเสร็จวันที่ 2 ม.ค. 35
แก้แบบวันที่
มิติเป็น
มาตราส่วน

แบบเลขที่ SAI-015/35001
แผ่นที่ 4 ของจำนวน 5 แผ่น

16 มิ.ย. 2535

การประกอบเลขที่ ASSEMBLY NO.	3508

	แบบอ้างอิง REFERENCE DRAWING	แบบเลขที่ DWG. NO.	การประกอบเลขที่ ASSEMBLY NO.
1	รหัสสีของคอนโทรลเคเบิล สำหรับมิเตอร์แรงสูง 11 - 33 kV COLOUR CODE OF CONTROL CABLE, FOR 11-33 kV H.T. METER	S02-015/16015	0506
2	แผนผังการต่อมิเตอร์แรงสูง 3 เฟส 3 สาย แบบวัดค่า 2 อัตรา ระบบ 22-33 kV CONNECTION DIAGRAM OF 3-PHASE, 3-WIRE H.T. METER, TWO-RATE TARIFF, 22-33 kV SYSTEM	SA1-015/28005	0533
3	แผนผังการต่อมิเตอร์แรงสูง 3 เฟส 3 สาย กรณีติดตั้งกิโลวัตต์-ชั่วโมงมิเตอร์ ร่วมกับ กิโลวาร์-ชั่วโมงมิเตอร์ ระบบ 22-33 kV CONNECTION DIAGRAM OF 3-PHASE, 3-WIRE H.T. METER, kWh AND kVar METERS COMBINATION, 22-33 kV SYSTEM	SA1-015/28018	0538
4	การต่อลงดินระบบแรงสูง และแรงต่ำ แผ่นที่ 15 และ 17 H.T. AND L.T. EARTHING SYSTEM, SHEET NOS. 15 AND 17	S02-015/20039	9701
5	การประกอบสายดิน วิธียึดลวดเหล็ก GROUND LEAD ASSEMBLY, STEEL WIRE FITTING	S02-015/19166 SA1-015/31012	9703 9703A
6	การประกอบที่ยึดท่อ PVC สำหรับสายดิน PVC PIPE FITTING ASSEMBLY, FOR GROUND WIRE	S02-015/19128 SA1-015/31013	9704 9704A
7	การติดตั้งบัคอาร์ม (แบบท้าวแขน) 33 kV 33 kV BUCKARM (ALLEY ARM) INSTALLATION	SA1-015/35508	3810
8	การติดตั้งอุปกรณ์ที่เสาเข้าปลายสายแบบท้าวแขน DEADEND CONSTRUCTION ON ALLEY ARM	SA1-015/35009	3811

พชง.3 ผปร. กฟส.อล. กฟจ.กบ. กฟต.2 สายงาน (ต) ผวก. @PEA

คำเตือน

ในการติดตั้งตู้ใส่มิเตอร์ ให้ดำเนินการตามมาตรการ และวิธีปฏิบัติเกี่ยวกับการละเมิดสิทธิการใช้ไฟฟ้า โดยการเอียงมิเตอร์ ตามบันทึกที่ มต. 2145 ลว. 31 พ.ค. 2528 (อนุมัติ ผวก. ลว. 28 พ.ค. 2528) ดังนี้ :

(1) การยึดแป้นไม้ของมิเตอร์ และตู้ใส่มิเตอร์ ให้ยึดด้วยสลักเกลียว 2 ชุด โดยให้หัวของสลักเกลียวอยู่ในตู้

(2) ให้เจาะรูร้อยลวด ตีตราตะกั่วที่ปลายสลัก ตามข้อ (1) ทั้ง 2 ชุด

(3) ให้ร้อยลวดตีตราตะกั่วที่ฝาตู้ใส่มิเตอร์ ทั้ง 2 ชุด

กองวิศวกรรมไฟฟ้าและเครื่องกล ฝ่ายวิศวกรรม	การไฟฟ้าส่วนภูมิภาค	ใช้แทนแบบ .... ถูกแทนโดยแบบ ....
ผู้เขียน .... ผู้สำรวจ .... วิศวกร .... หัวหน้าแผนก .... ผู้อำนวยการกอง .... ผู้อำนวยการฝ่าย	ผู้ว่าการ .... 17 มิ.ย. 2535	เขียนเสร็จวันที่ 2 ม.ค. 35 แก้แบบวันที่ .... พิมพ์เป็น .... มาตราส่วน ....
	การติดตั้งมิเตอร์ 3 เฟส 3 สาย 33 kV ประกอบพี.ที. และซี.ที. (กรณีประกอบคอนแบบท้าวแขน)	
รองผู้ว่าการฝ่ายเทคนิค	INSTALLATION OF 33 kV, 3-Ø, 3-W, METER WITH P.T. & C.T. (ALLEY ARM)	แบบเลขที่ SA1-015/35001 แผ่นที่ 5 ของจำนวน 5 แผ่น

16