การประกอบเลขที่
ASSEMBLY NO. 0811

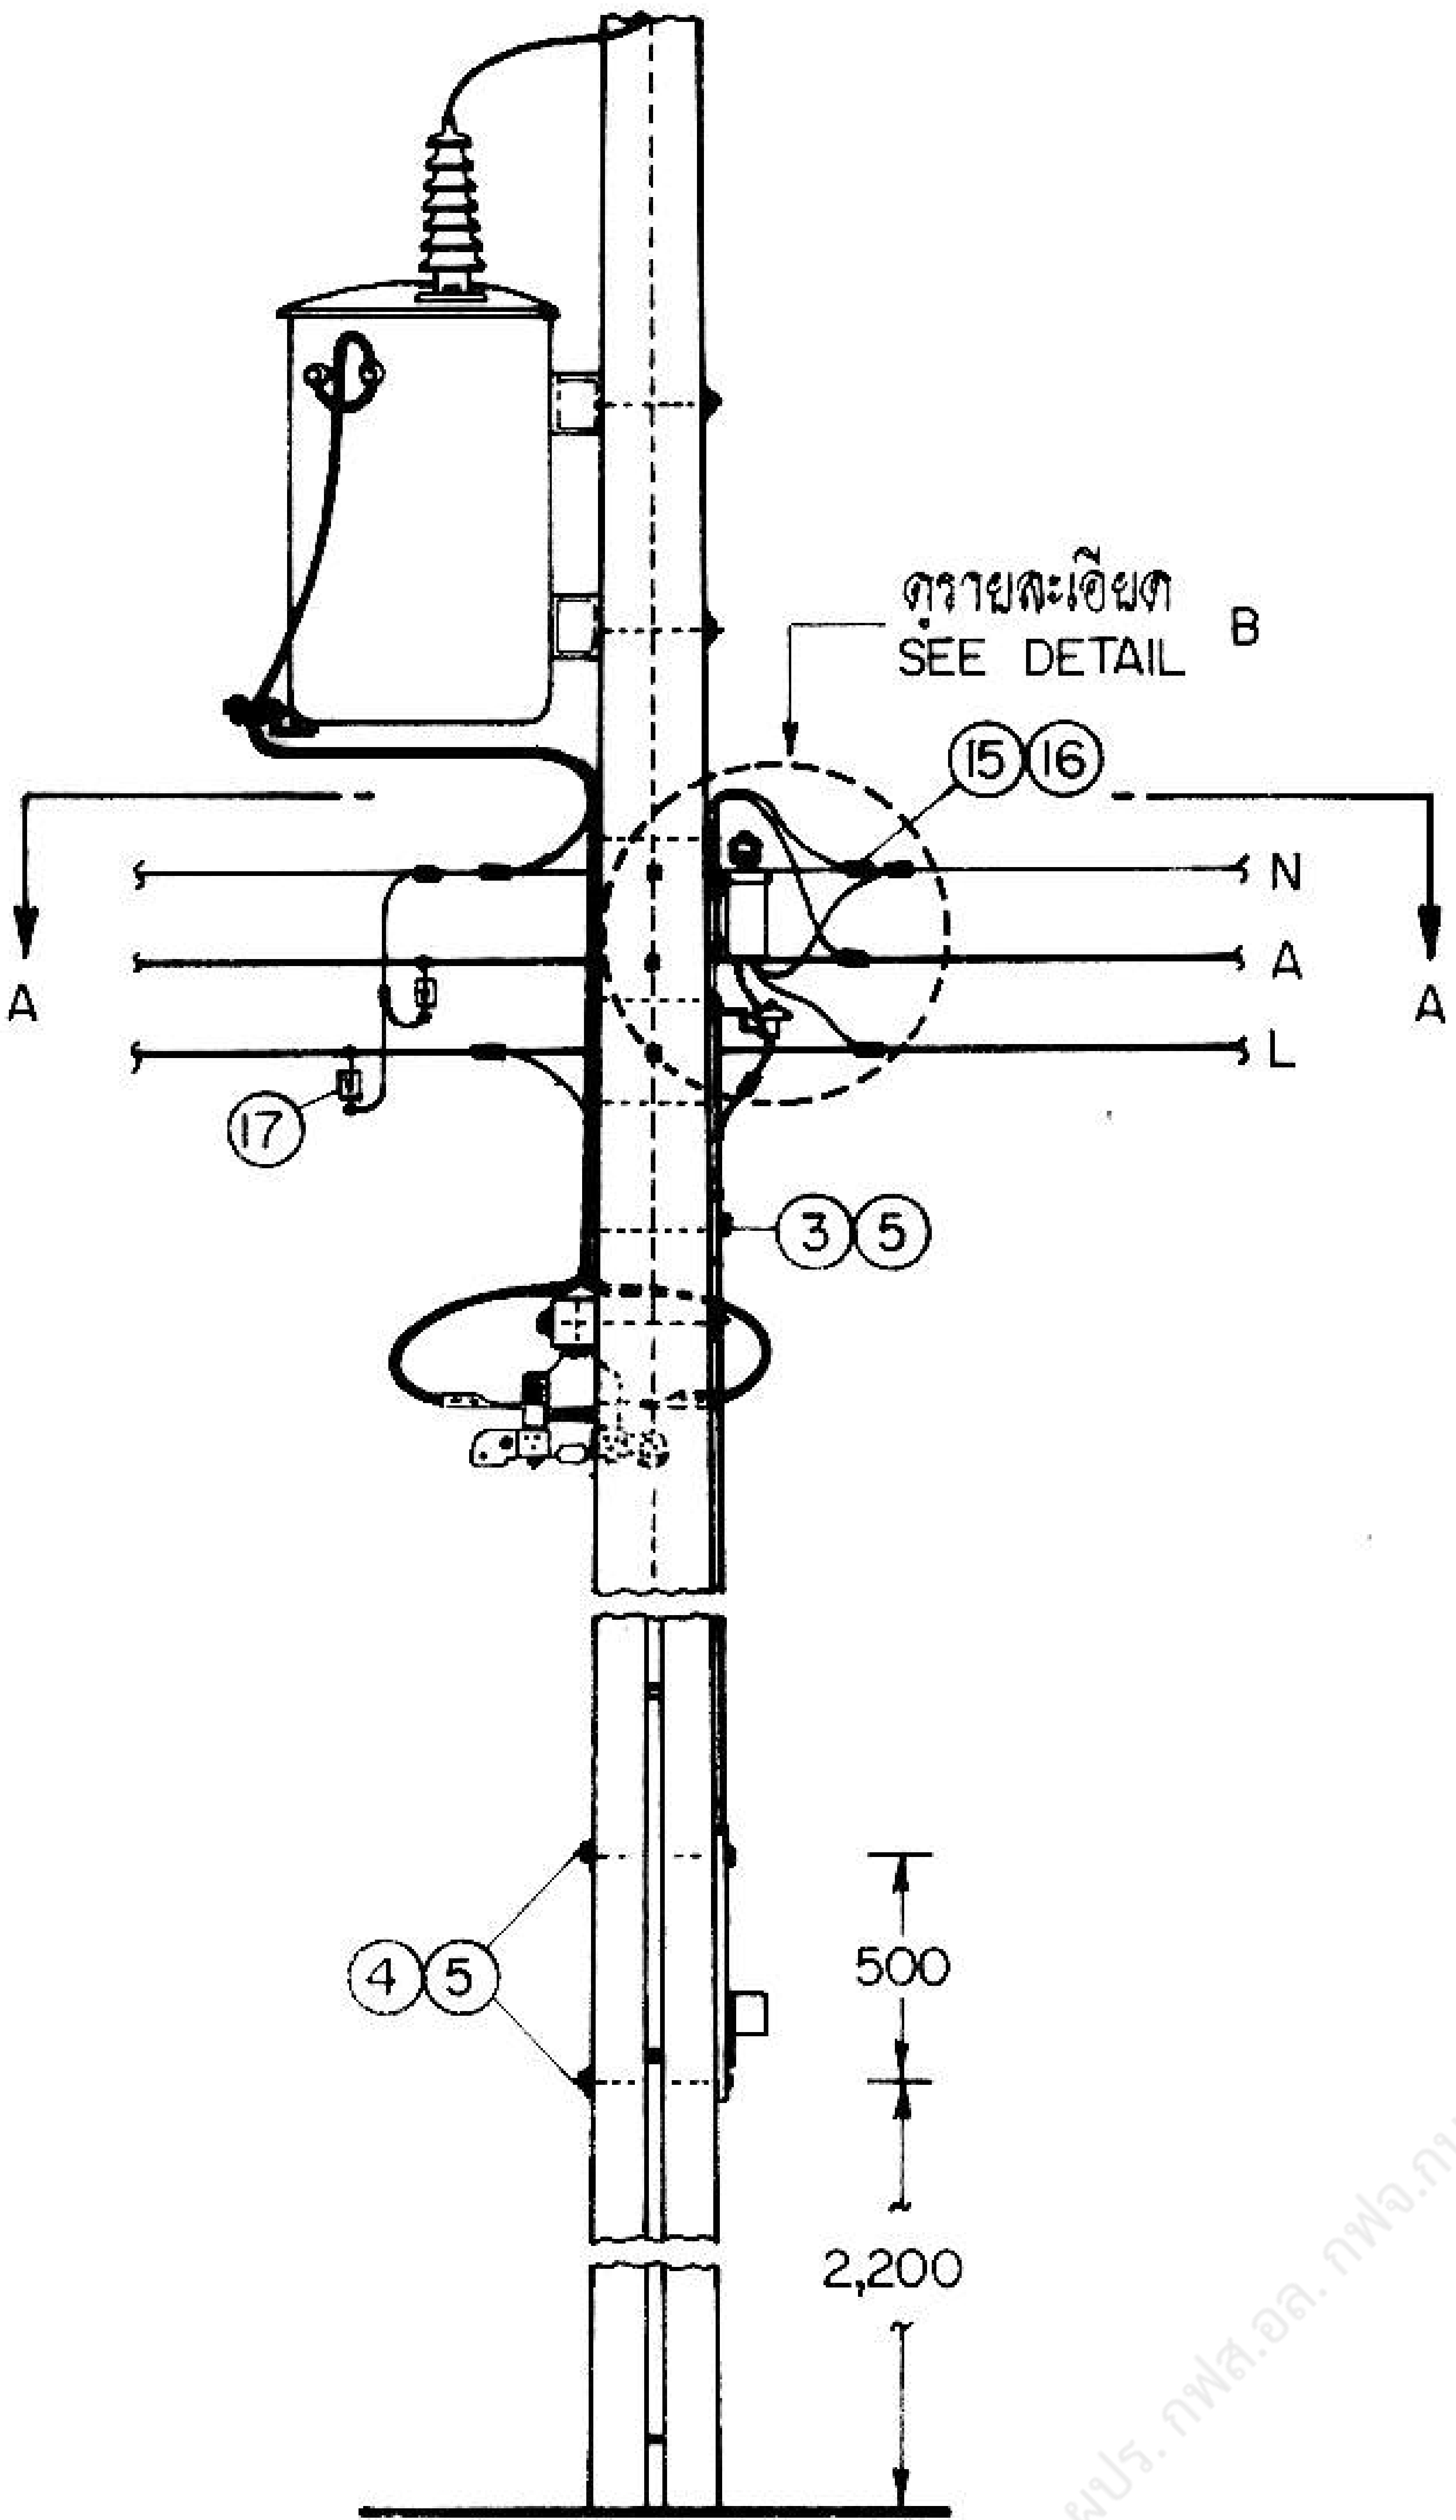

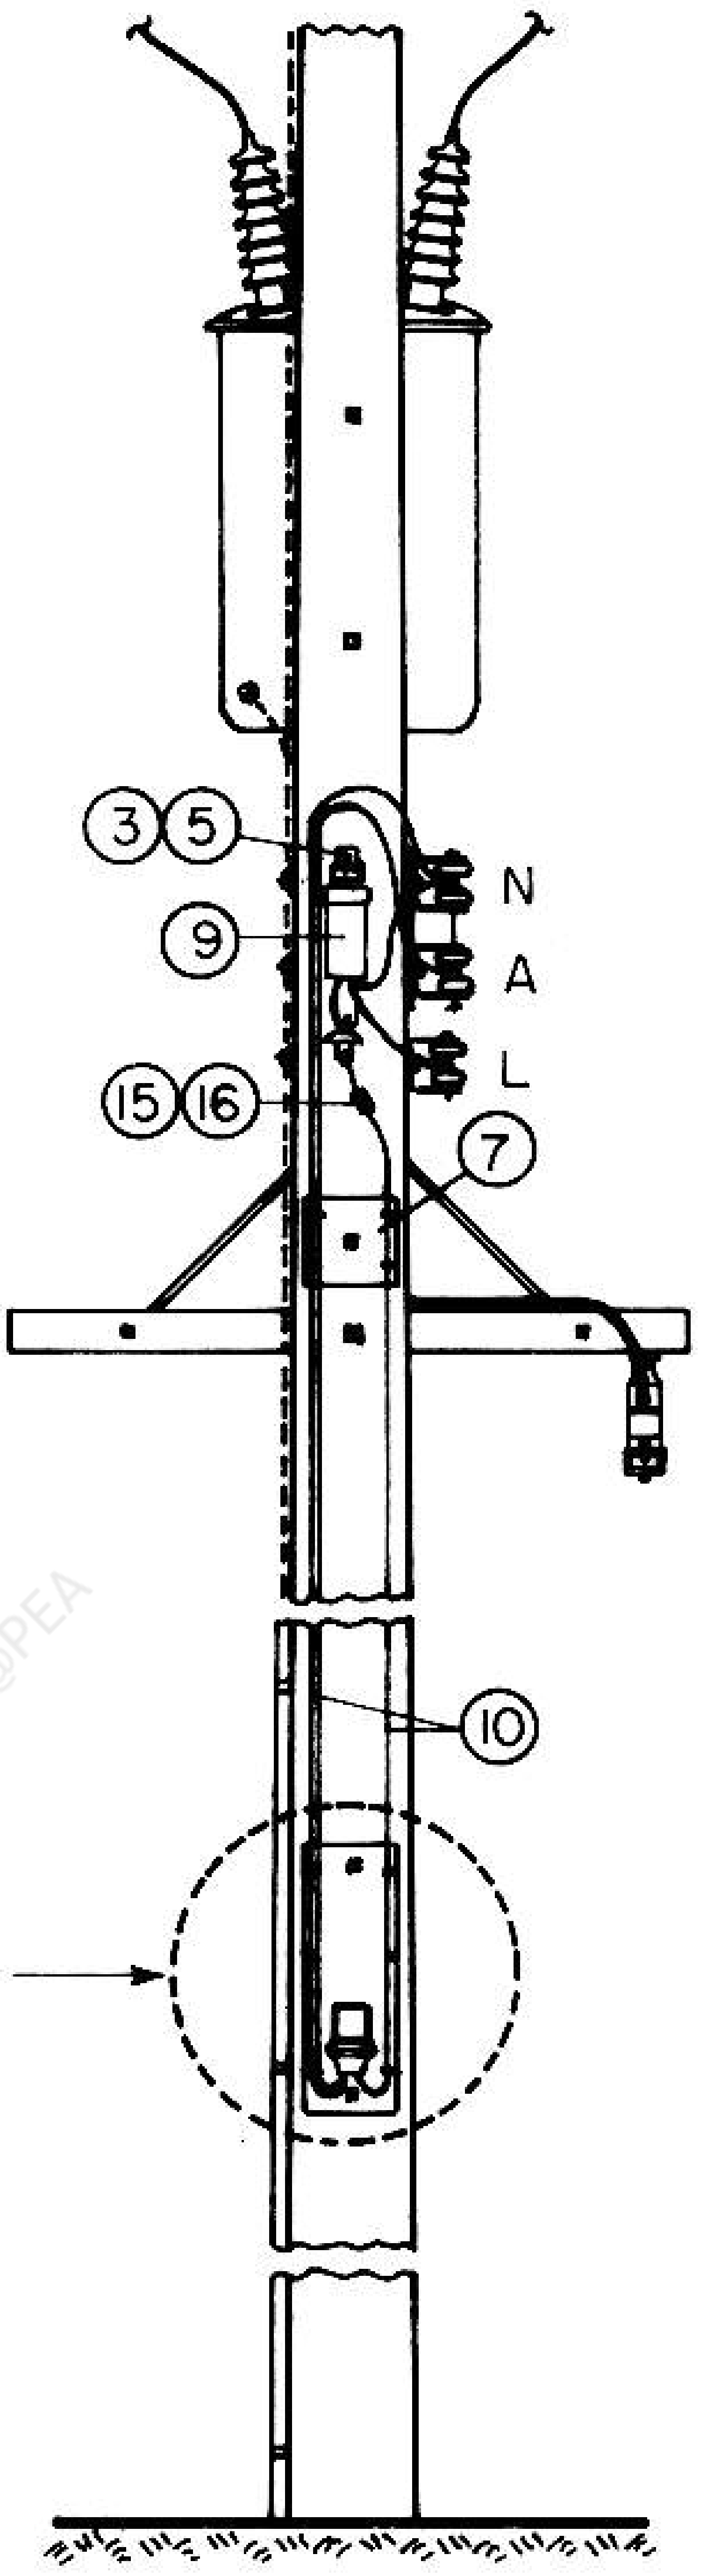

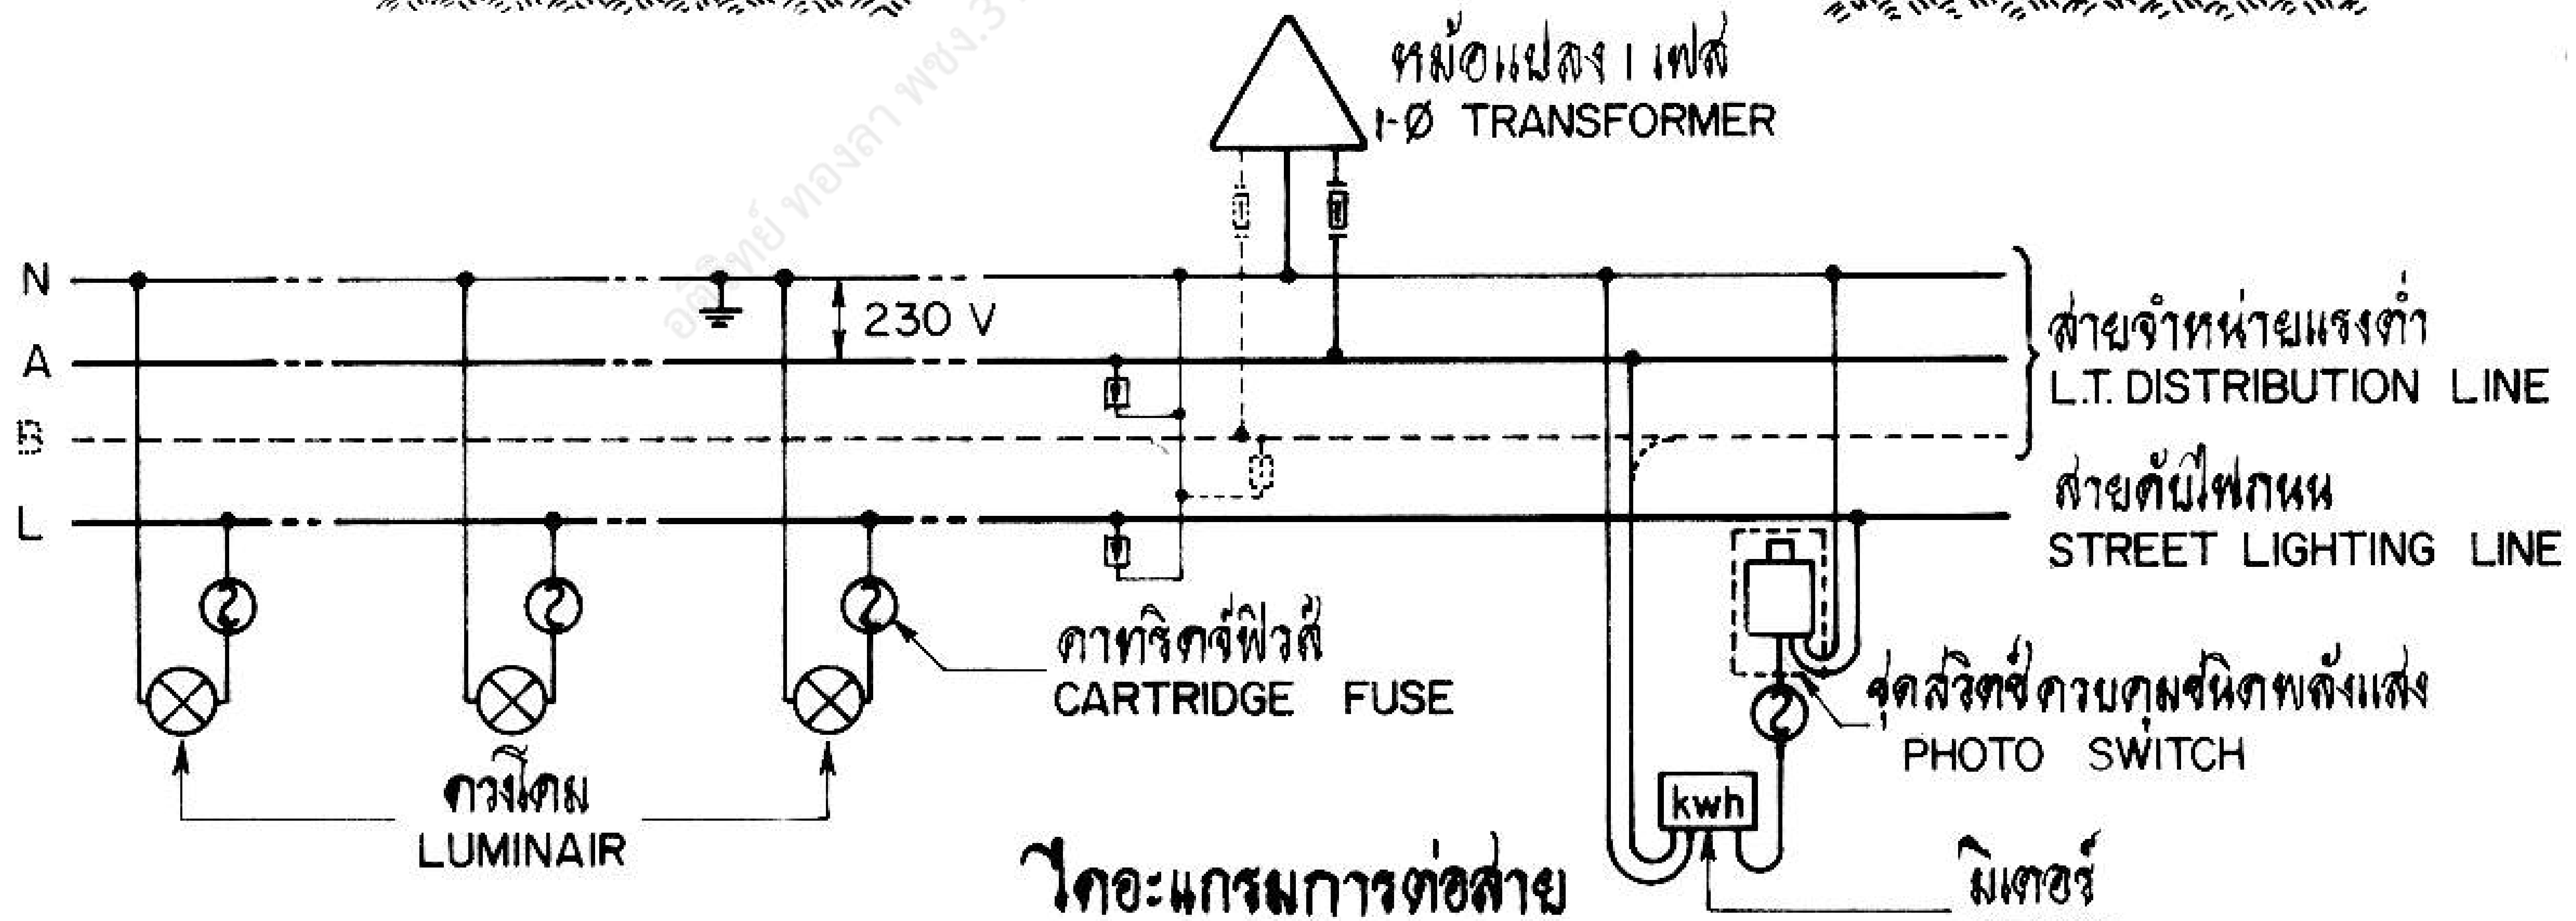

ไดอะแกรมการต่อสาย
WIRING DIAGRAM

[illegible] ทองลา พชง.3 ผปร. กฟส.อล. กฟจ.กบ. กฟต[illegible]งาน (ต) ผวก. @PEA

กองวิศวกรรมไฟฟ้าและเครื่องกล
ฝ่ายวิศวกรรม

ผู้เขียน Mont ...
ผู้สำรวจ........
วิศวกร ....
หัวหน้าแผนก........
ผู้อำนวยการกอง........
ผู้อำนวยการฝ่าย........
รองผู้ว่าการฝ่ายเทคนิค........

การไฟฟ้าส่วนภูมิภาค

ผู้ว่าการ........
5 เม.ย. 2528

การติดตั้งชุดสวิตซ์ควบคุมชนิดพลังแสงสำหรับเปิด-ปิด วงจรไฟถนน
ก ที่เสาต้นติดตั้งหม้อแปลงแบบแขวน

PHOTO SWITCH INSTALLATION IN STREET LIGHTING CIRCUIT
A ON SINGLE PHASE TRANSFORMER POLE

ใช้แทนแบบ........
ถูกแทนโดยแบบ........
เขียนเสร็จวันที่ 27 มี.ค. 28
แก้แบบวันที่........
มิติเป็น มม.
มาตราส่วน 1 : 50
แบบเลขที่ SAI-015/28009
แผ่นที่ 1 ของจำนวน 6 แผ่น

การประกอบเลขที่
ASSEMBLY NO. 0811

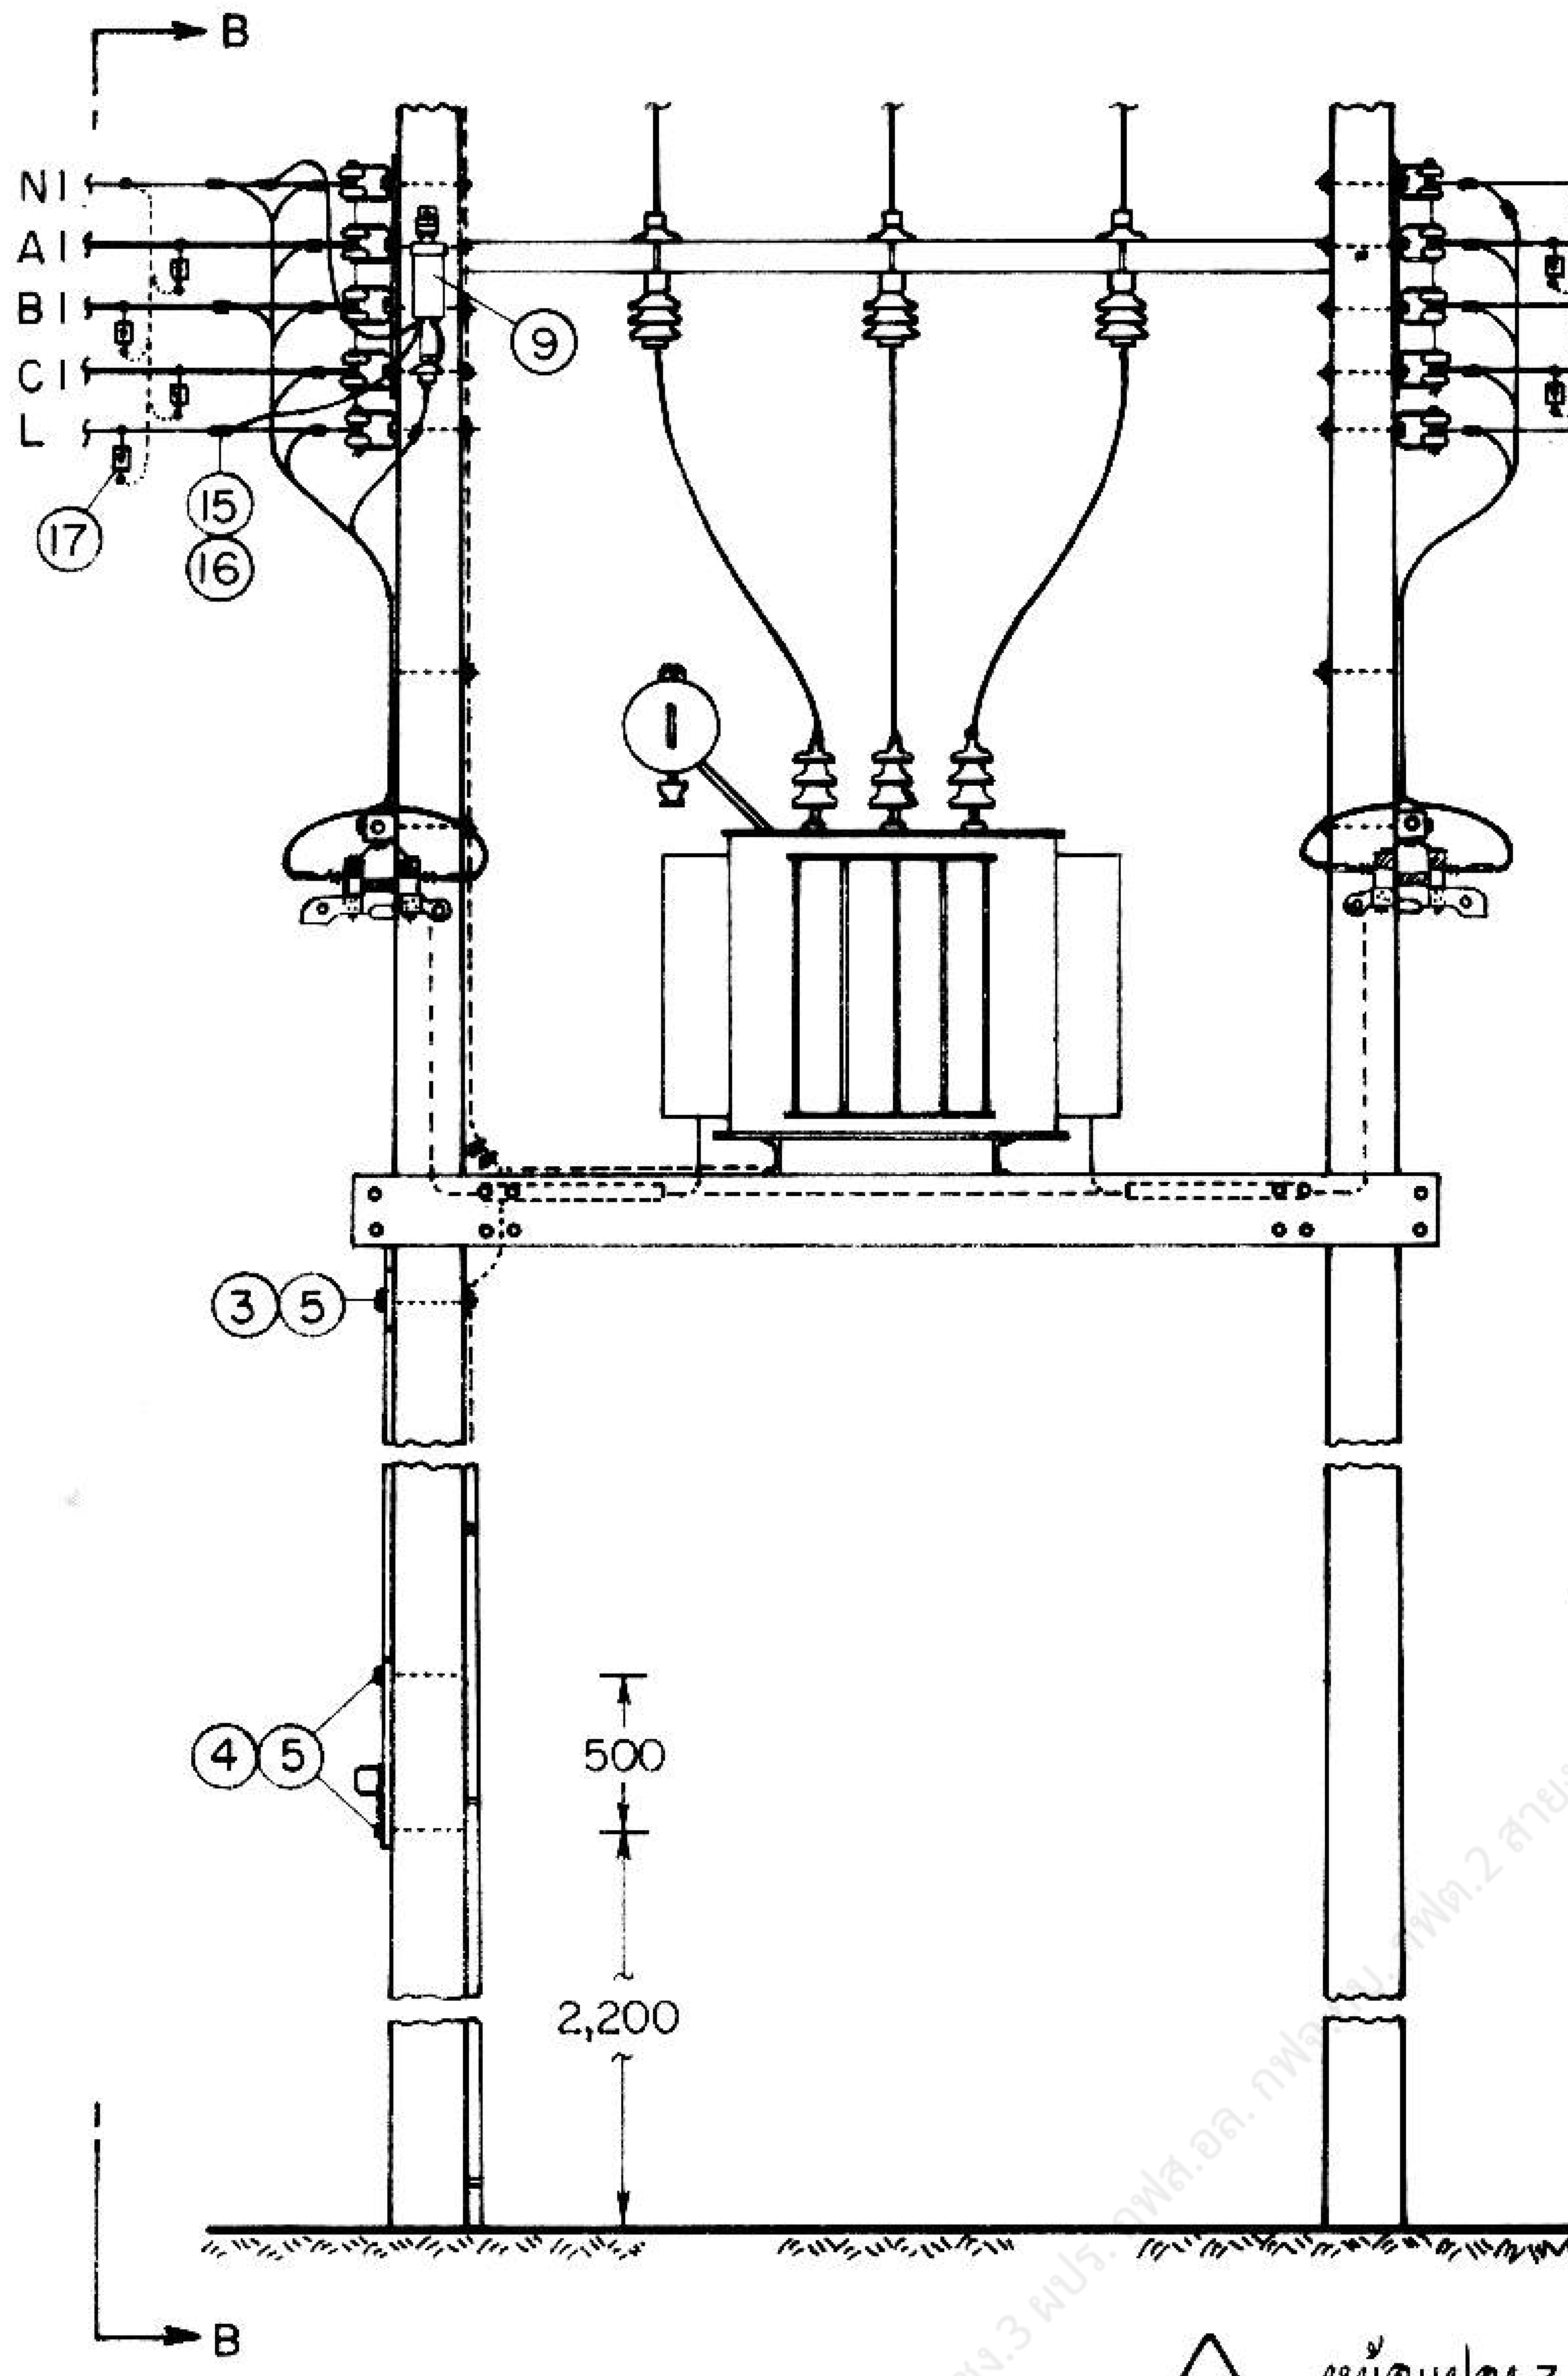

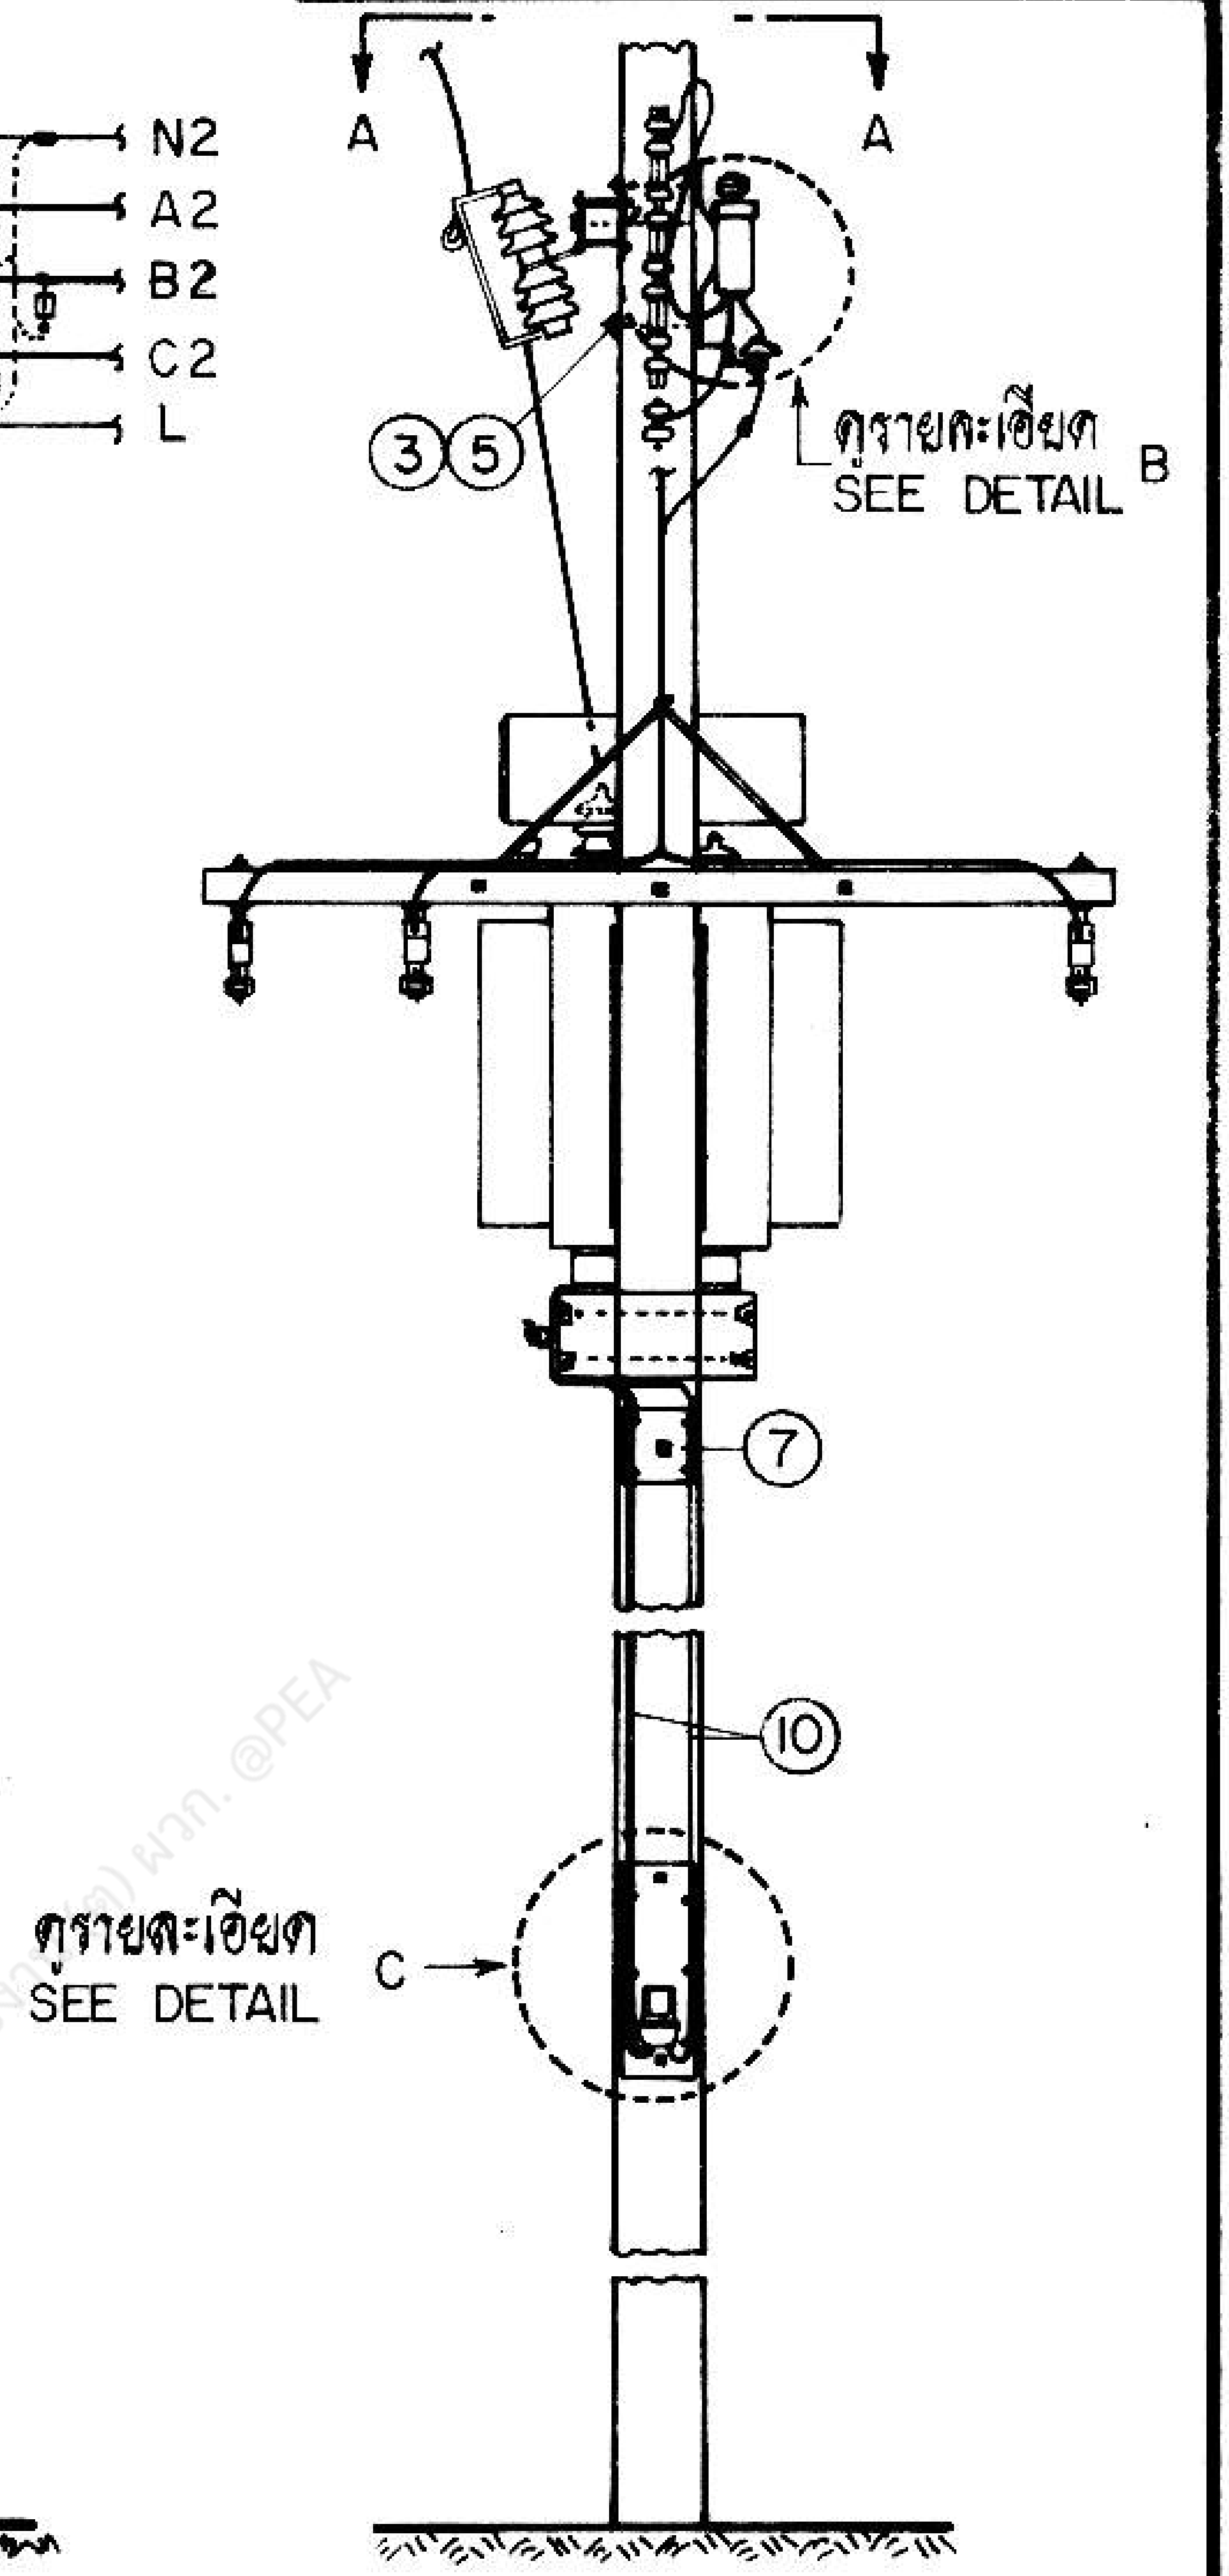

รูปตัด
SECTION B-B

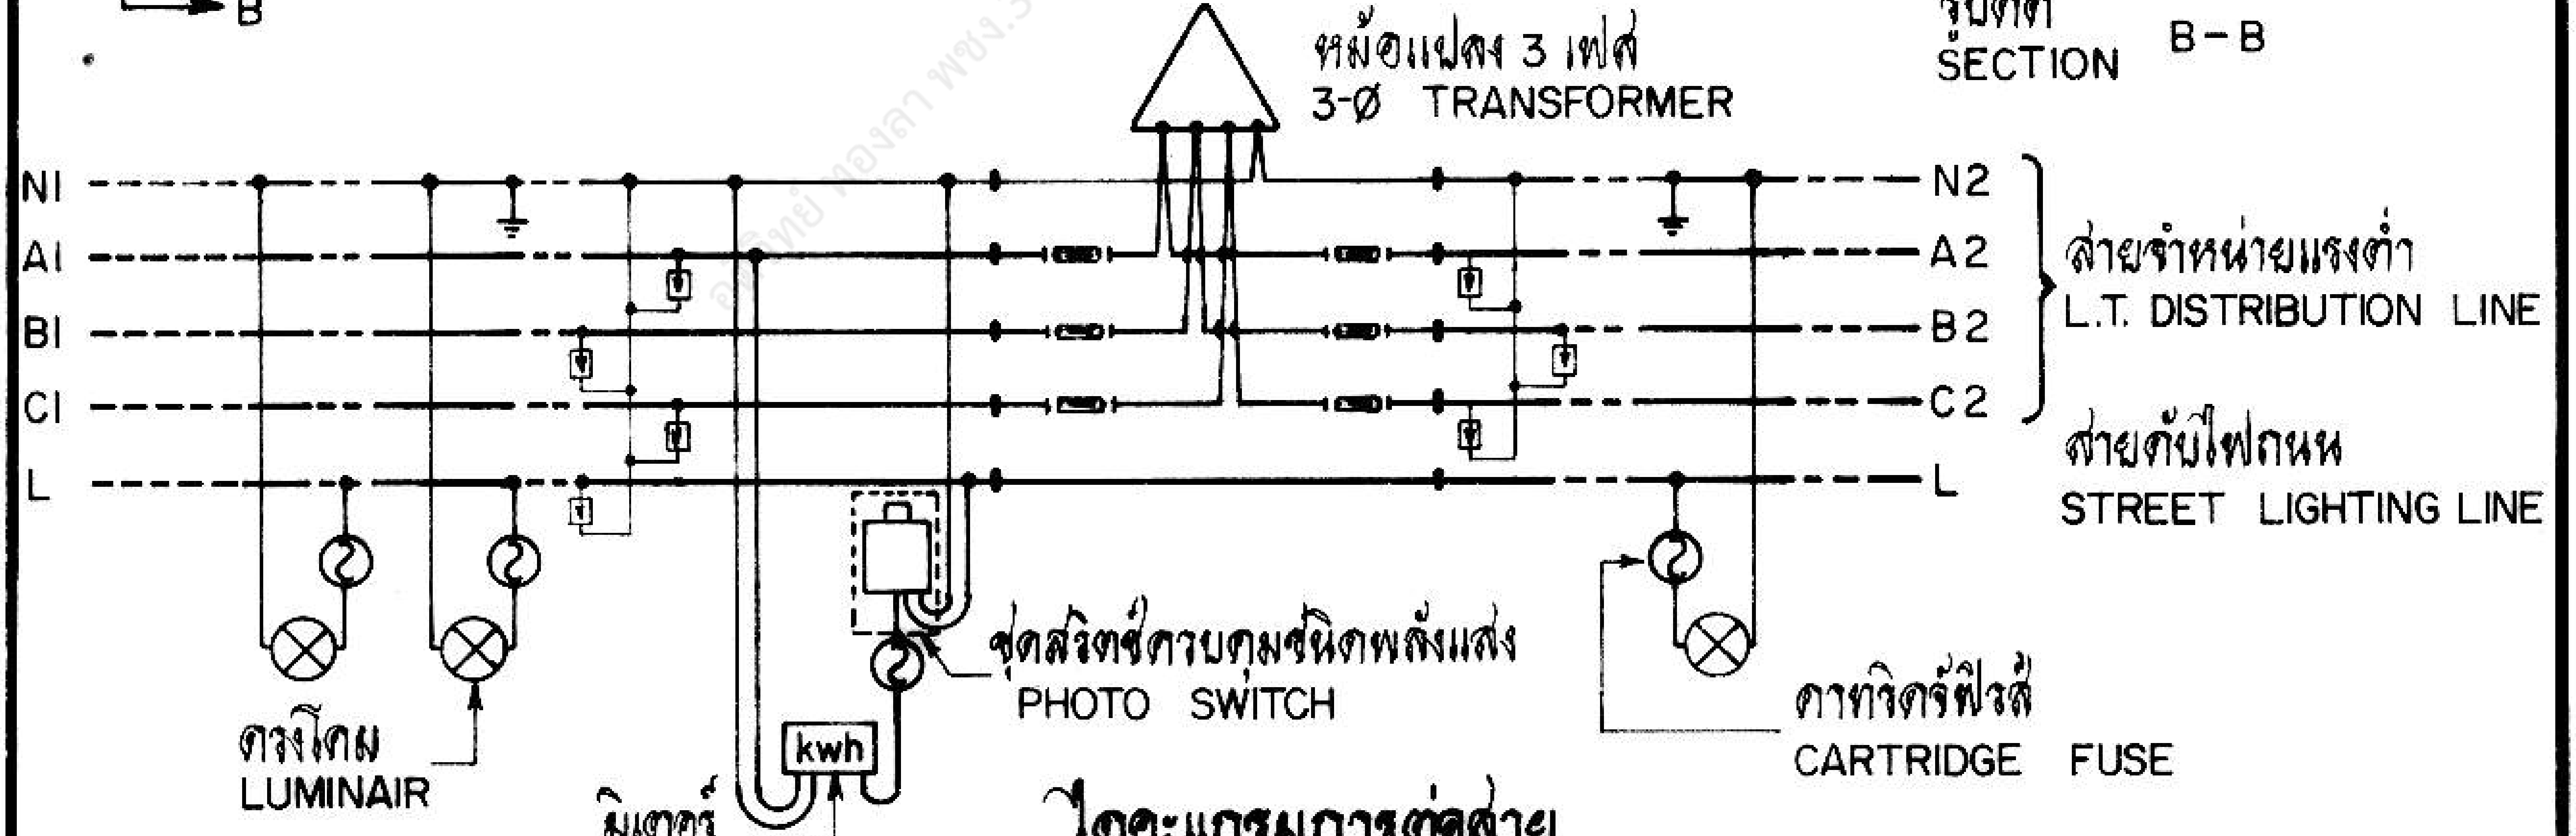

ไดอะแกรมการต่อสาย
WIRING DIAGRAM

กองวิศวกรรมไฟฟ้าและเครื่องกล
ฝ่ายวิศวกรรม

การไฟฟ้าส่วนภูมิภาค

ผู้เขียน
ผู้สำรวจ
วิศวกร
หัวหน้าแผนก
ผู้อำนวยการกอง
ผู้อำนวยการฝ่าย

ของผู้ว่าการฝ่ายเทคนิค

ผู้ว่าการ 5 เมย 2528

การติดตั้งชุดสวิตช์ควบคุมชนิดพลังแสงสำหรับเปิด-ปิด วงจรไฟถนน
ฃ ที่เสาต้นนั่งร้านหม้อแปลง

PHOTO SWITCH INSTALLATION IN STREET LIGHTING CIRCUIT
B ON THREE PHASE TRANSFORMER POLE

ใช้แทนแบบ
ถูกแทนโดยแบบ
เขียนเสร็จวันที่ 27 มี.ค. 28
แก้แบบวันที่
มิติเป็น มม.
มาตราส่วน 1 : 50

แบบเลขที่ SAI-015/28009
แผ่นที่ 2 ของจำนวน 6 แผ่น

การประกอบเลขที่ 0811
ASSEMBLY NO.

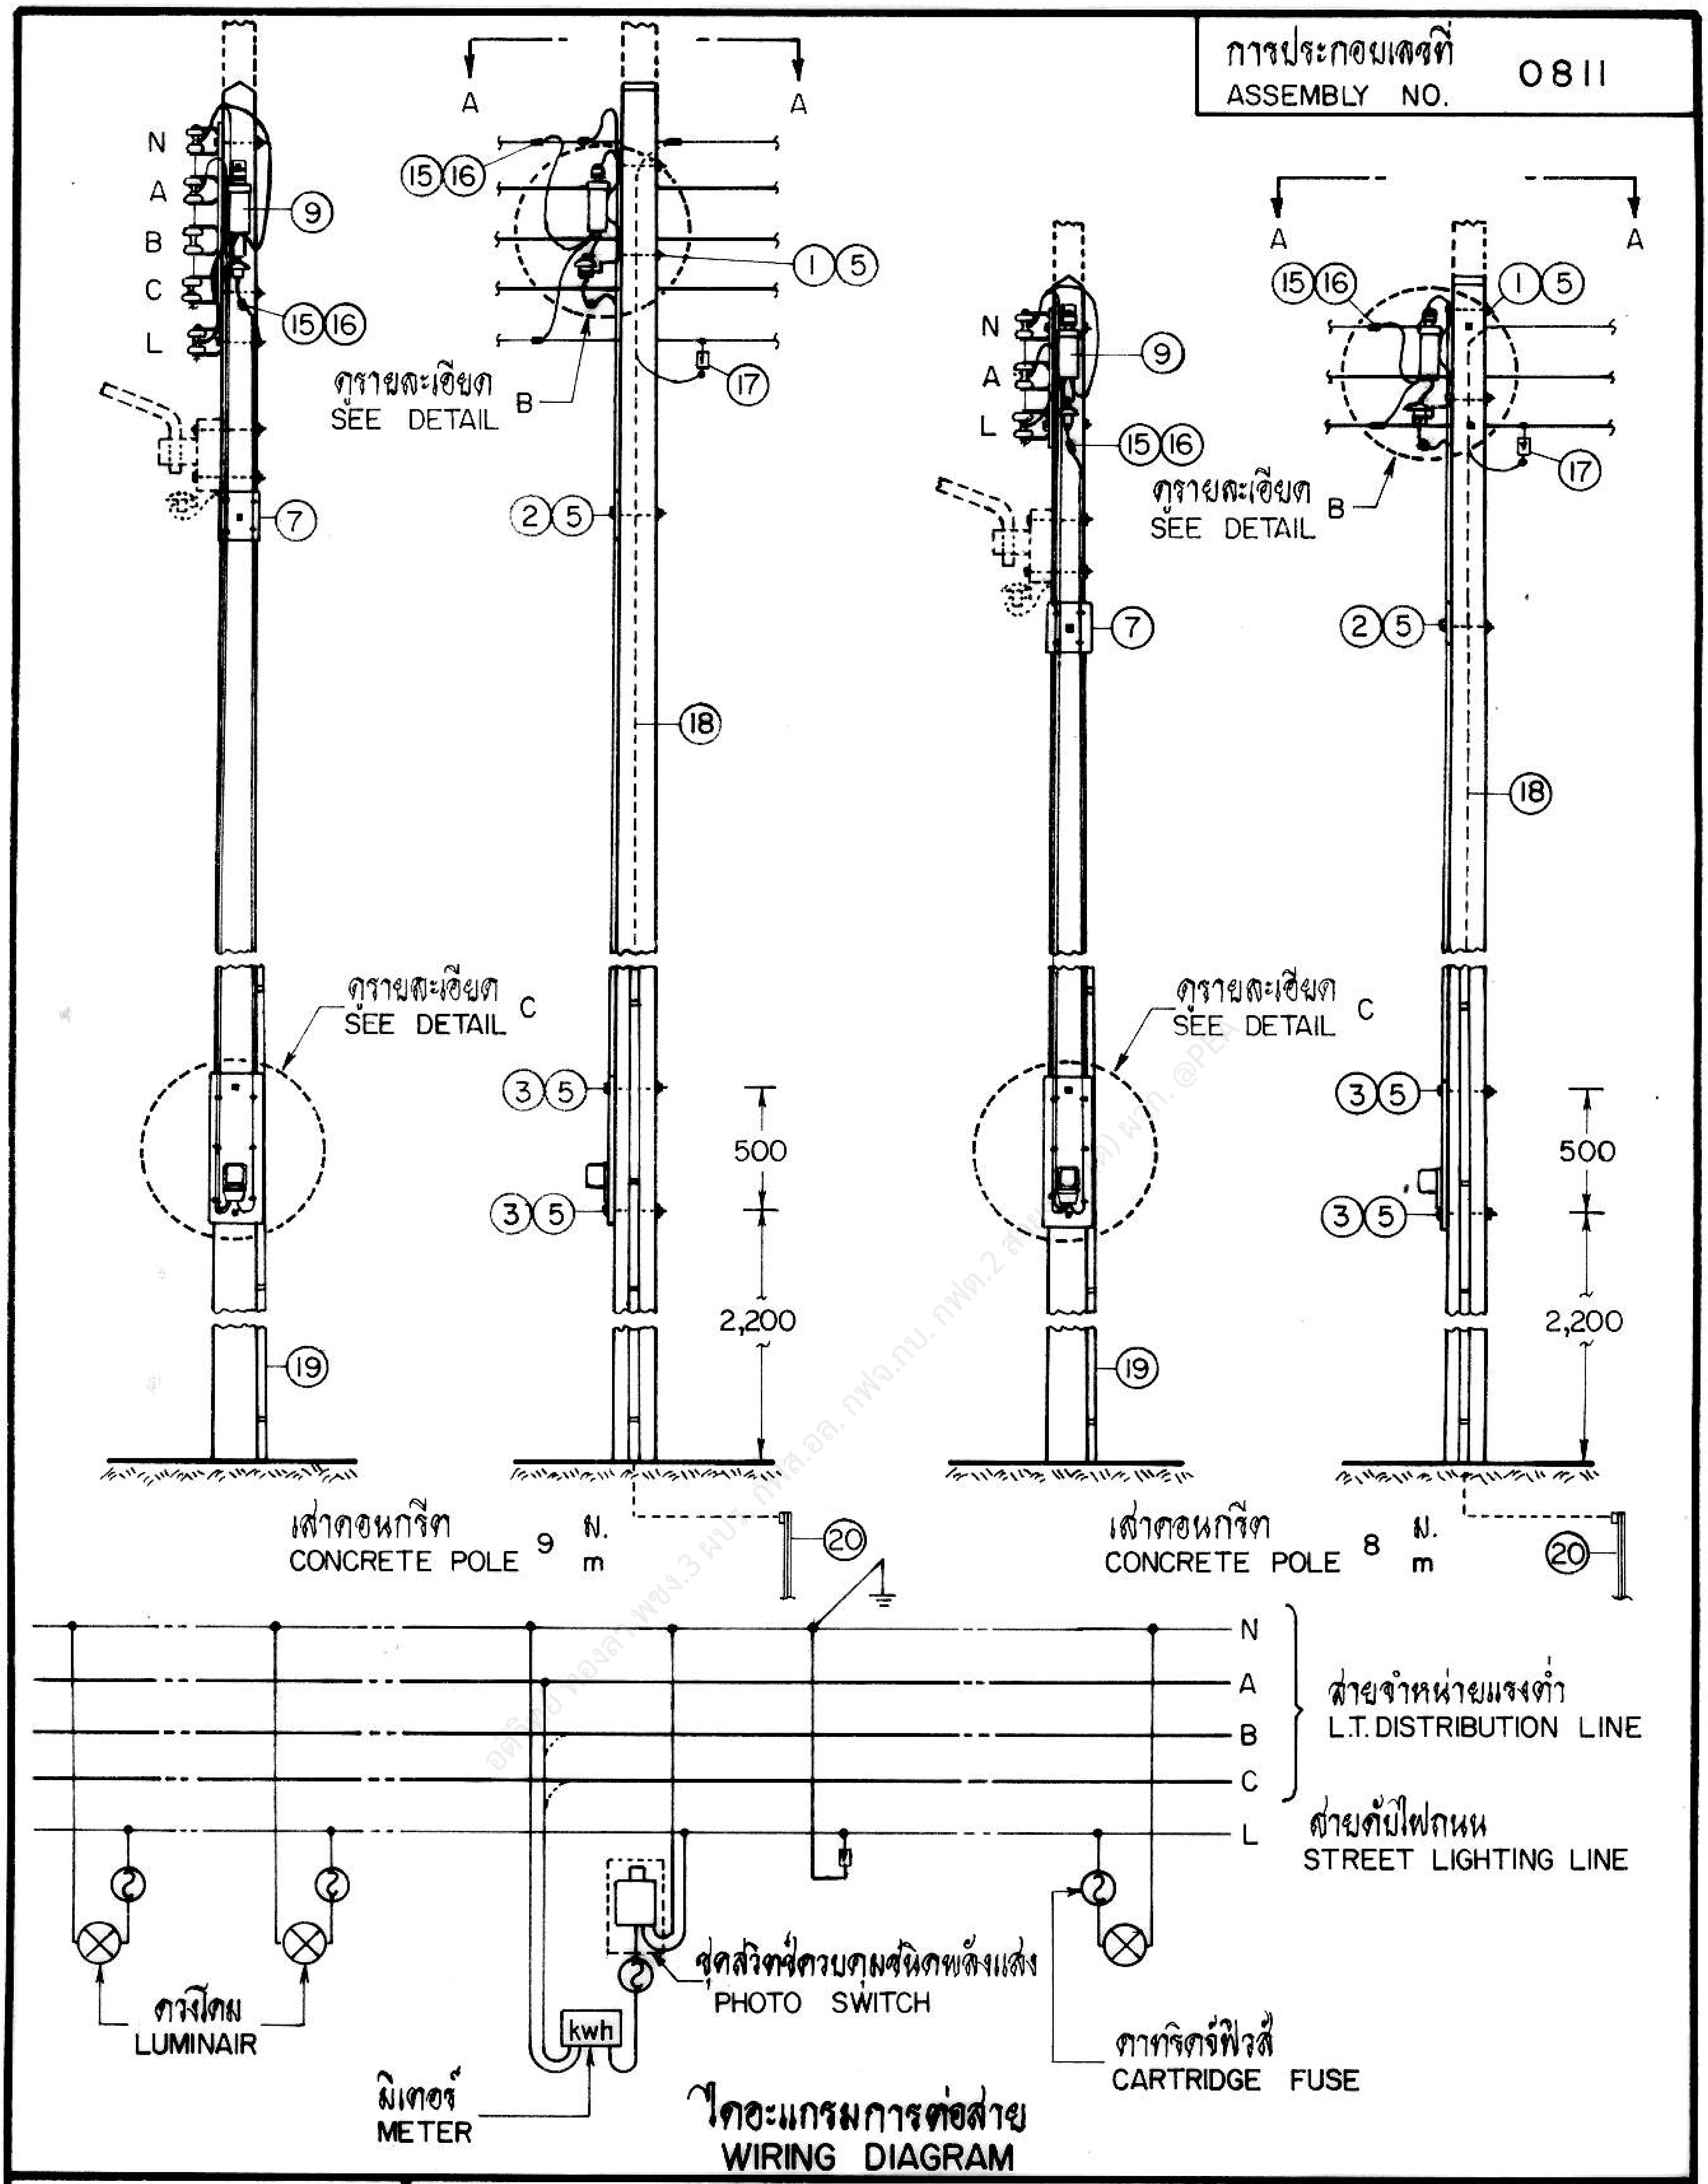

ไดอะแกรมการต่อสาย
WIRING DIAGRAM

กองวิศวกรรมไฟฟ้า และเครื่องกล ฝ่ายวิศวกรรม	**การไฟฟ้าส่วนภูมิภาค**	ใช้แทนแบบ........ ถูกแทนโดยแบบ........
ผู้เขียน........ ผู้สำรวจ........ วิศวกร........ หัวหน้าแผนก........ ผู้อำนวยการกอง........ ผู้อำนวยการฝ่าย........	ผู้ว่าการ........ 5 เม.ย. 2528 การติดตั้งชุดสวิตช์ควบคุมชนิดพลังแสงสำหรับเปิด-ปิด วงจรไฟถนน ค ที่เสาต้นในไลน์ระบบจำหน่ายแรงต่ำ	เขียนเสร็จวันที่ 27 มี.ค. 28 แก้แบบวันที่........ มิติเป็น มม. มาตราส่วน 1 : 50
รองผู้ว่าการฝ่ายเทคนิค........	PHOTO SWITCH INSTALLATION IN STREET LIGHTING CIRCUIT C ON THE POLE IN L.T. DISTRIBUTION LINE	แบบเลขที่ SAI-015/28009 แผ่นที่ 3 ของจำนวน 6 แผ่น

การประกอบเลขที่ ASSEMBLY NO.	0811

ชุดสวิตช์ควบคุมชนิดพลังแสง ให้ติดตั้งได้ที่ ตำแหน่ง 1 หรือ 2 ตามความเหมาะสม
PHOTO SWITCH CAN BE INSTALLED SUITABLY AT POSITION 1 OR 2

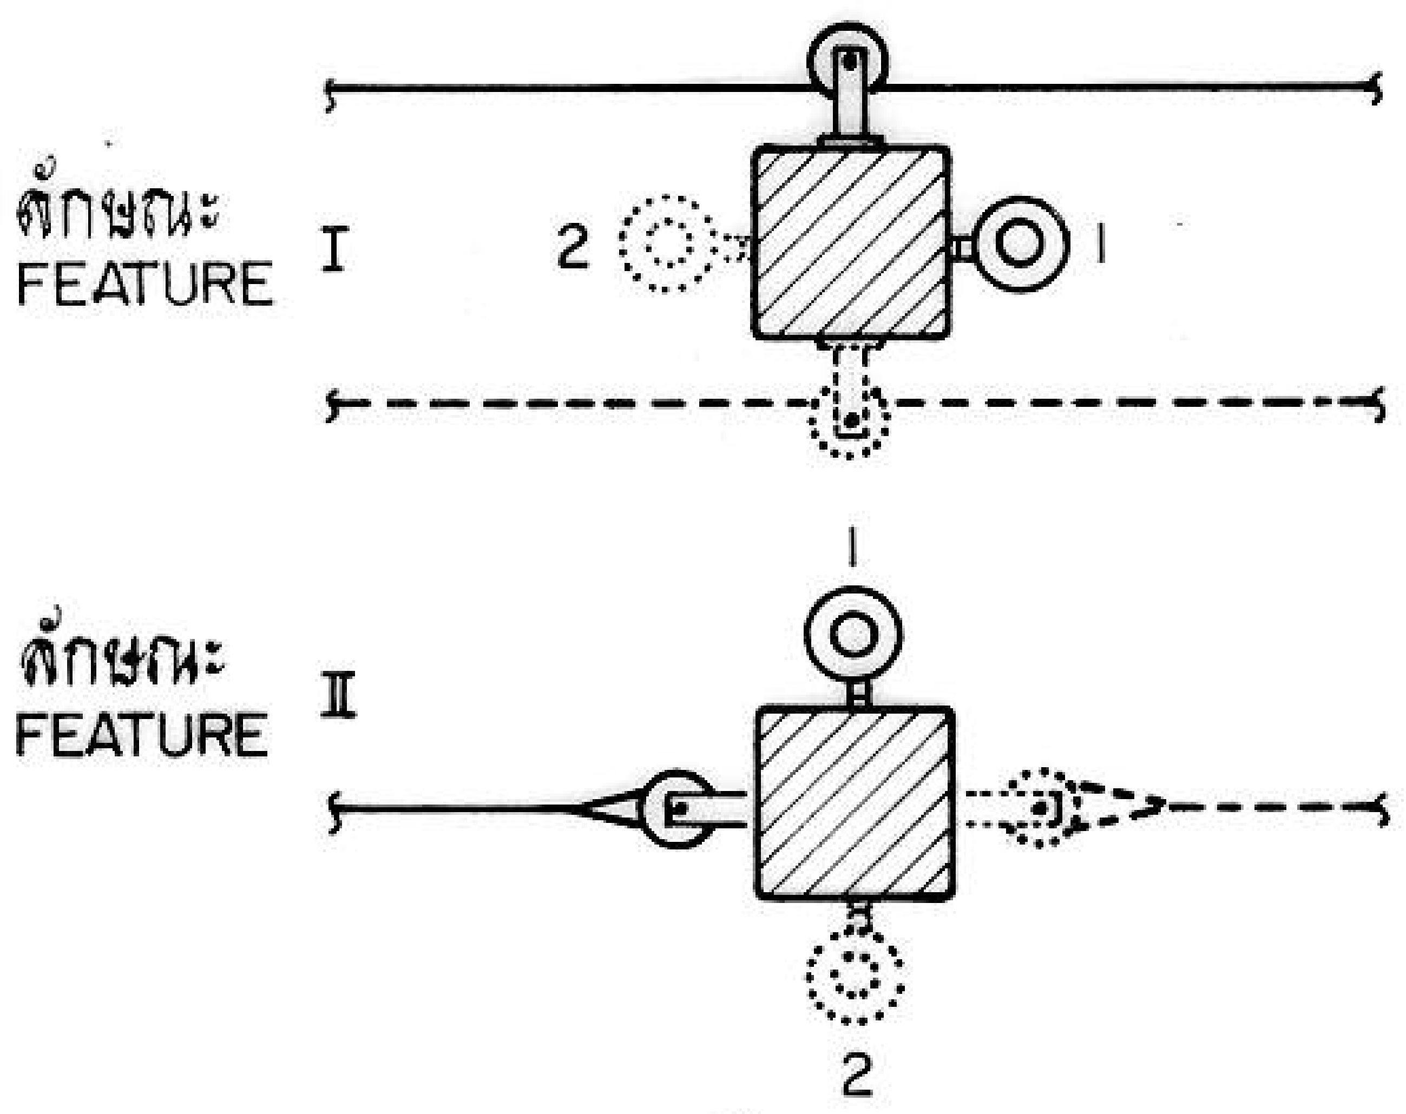

รูปตัด SECTION A-A

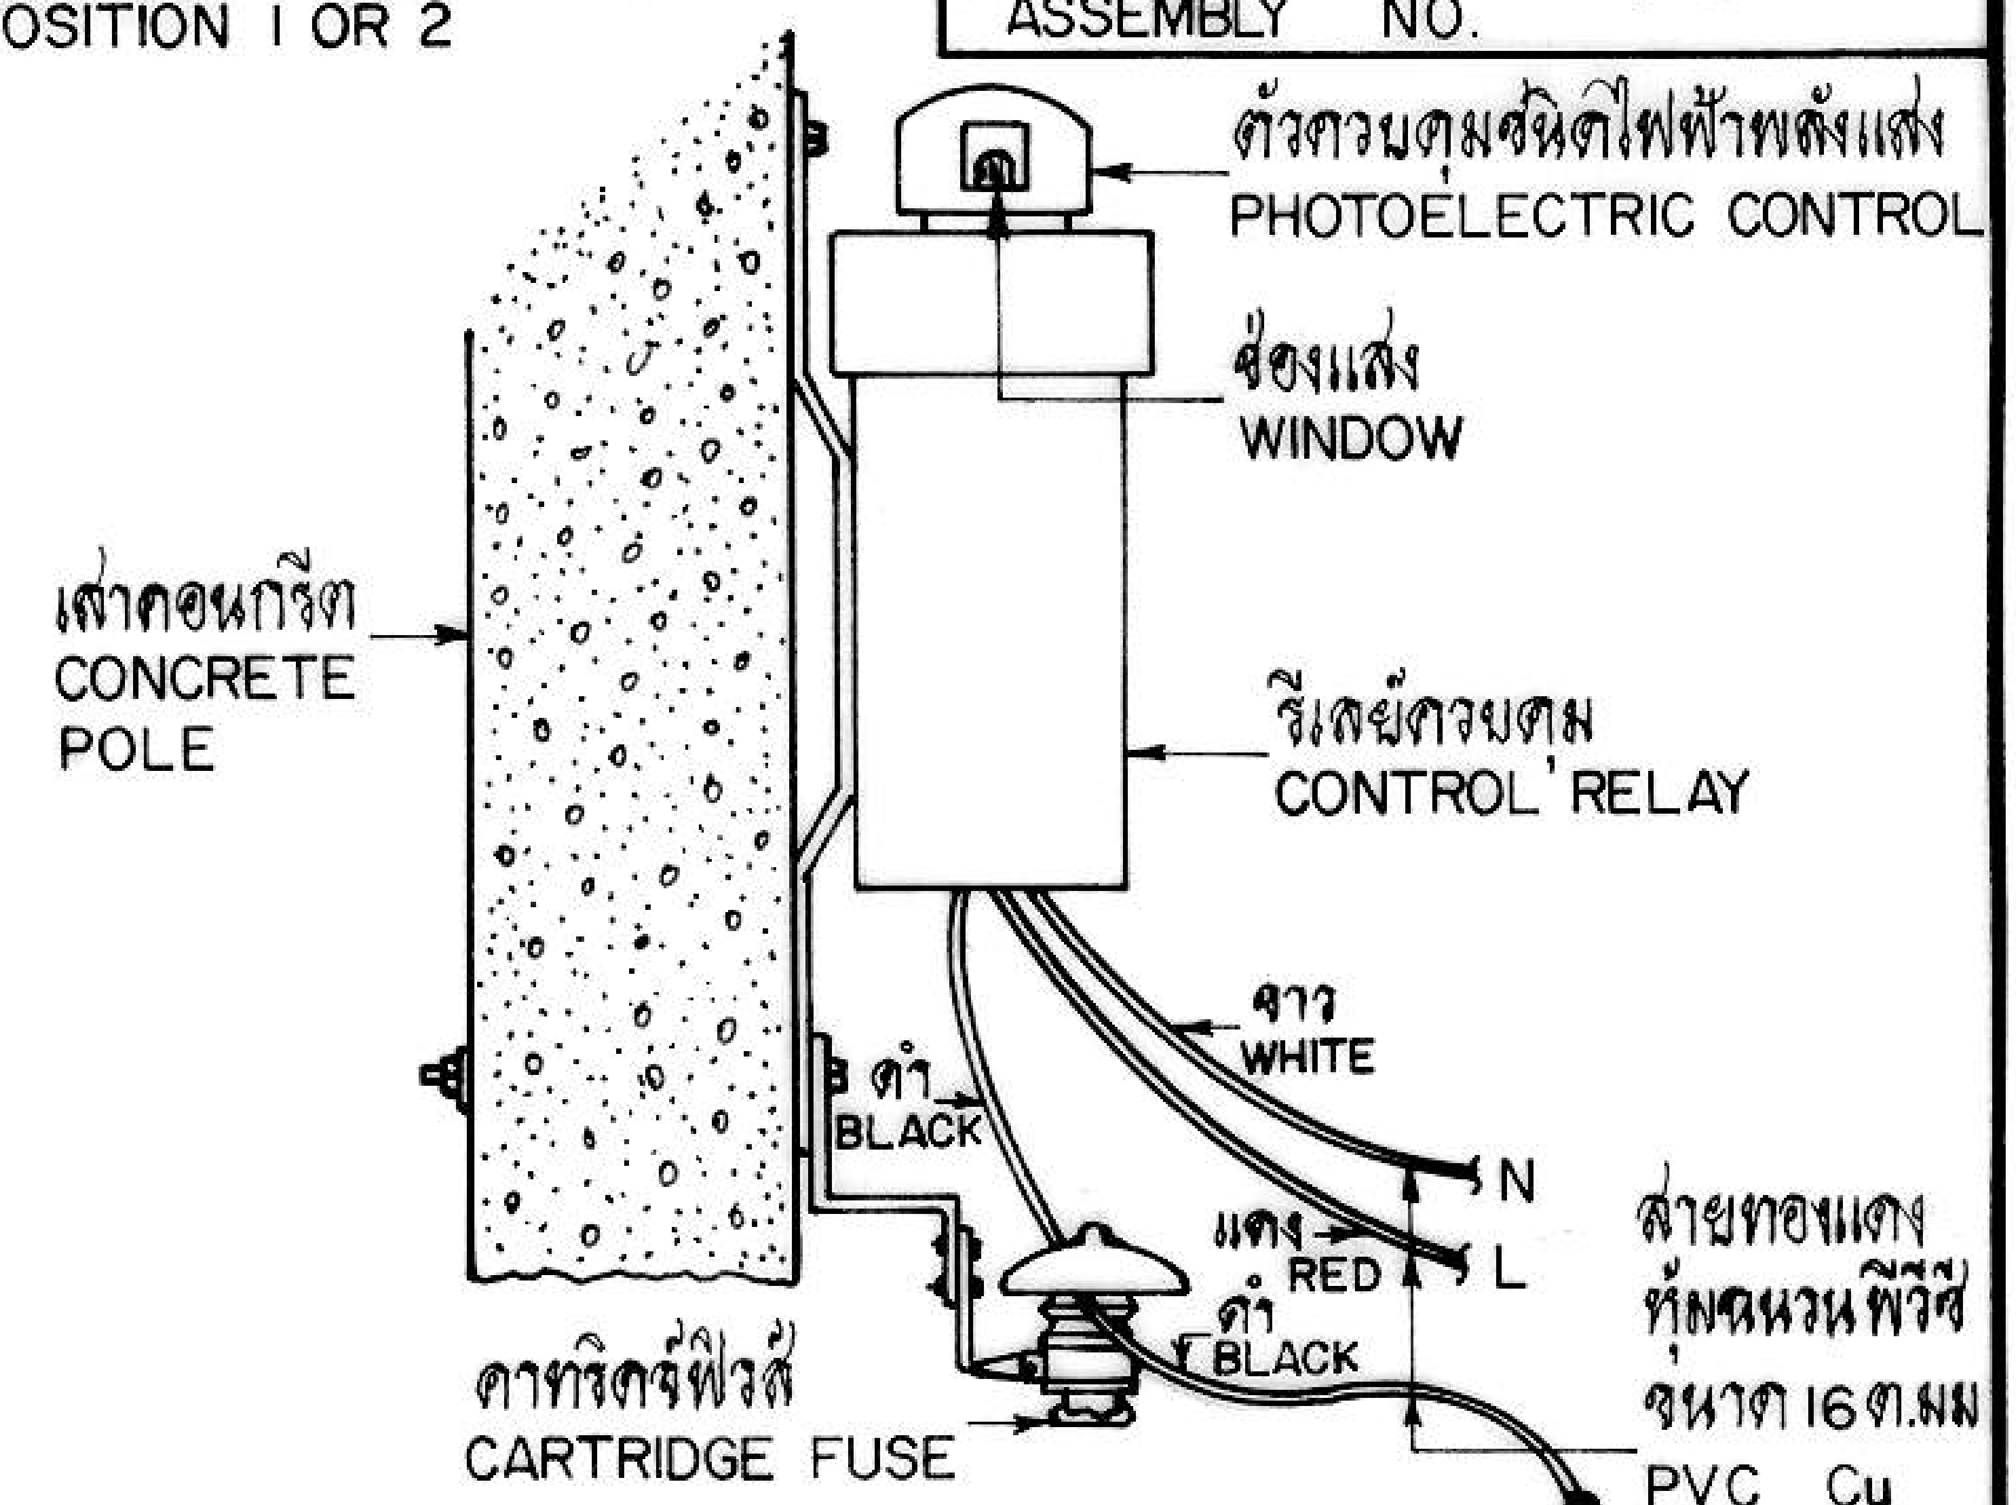

รายละเอียด DETAIL B

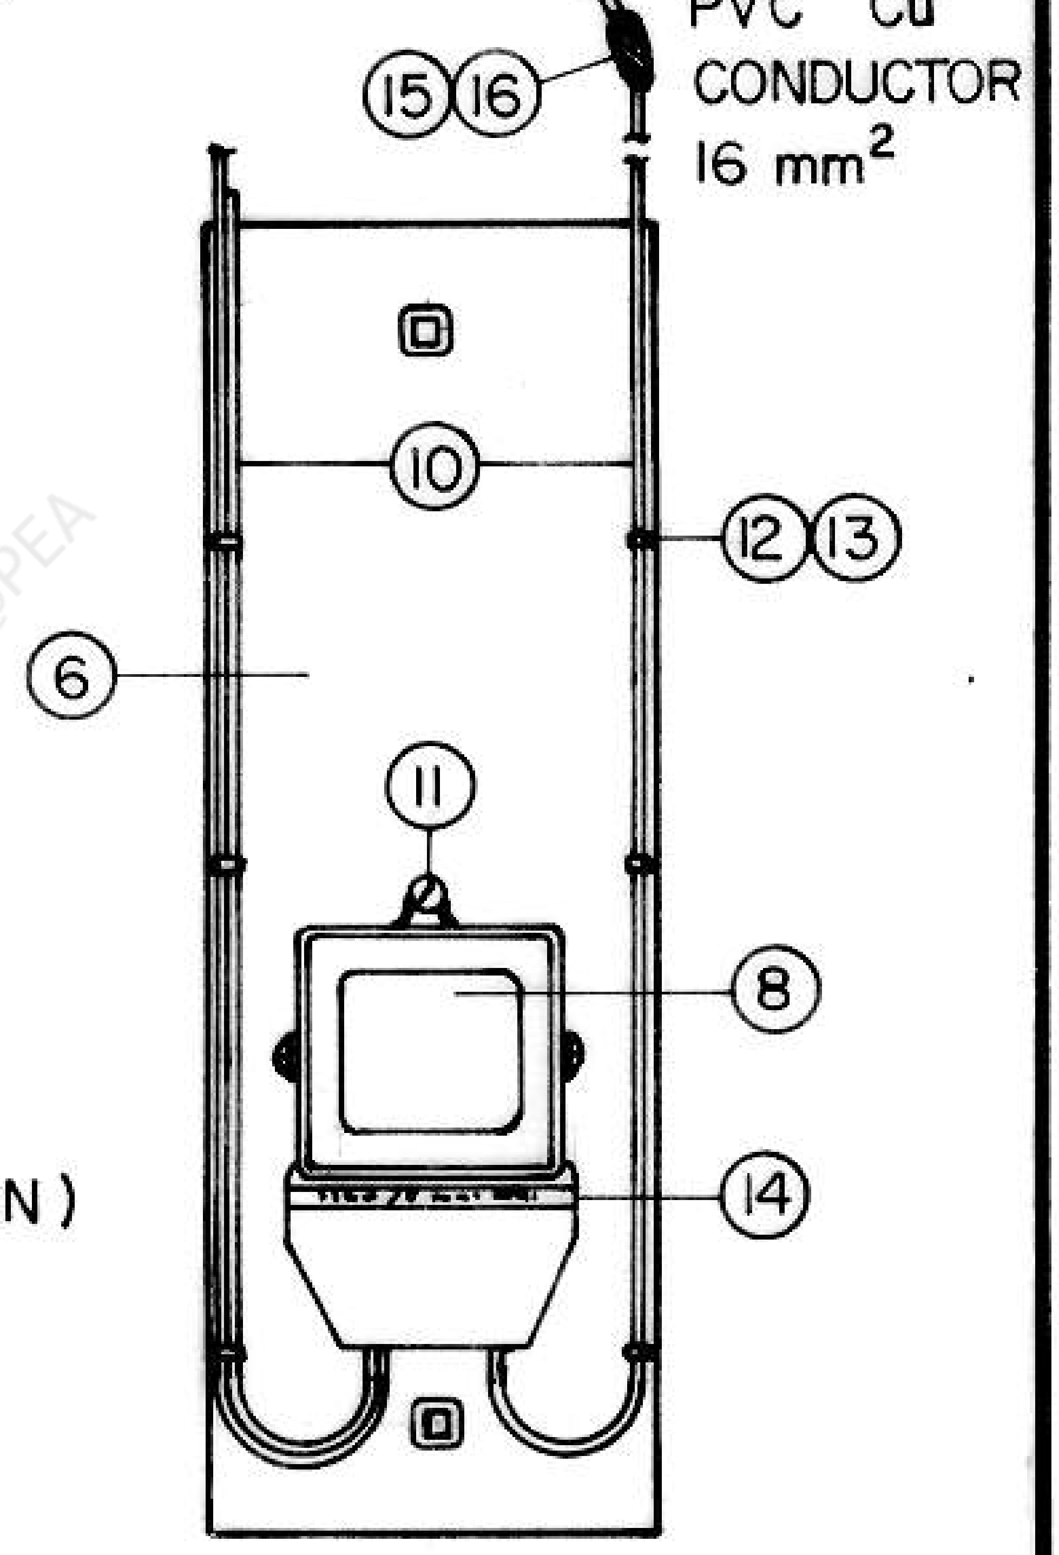

รายละเอียด DETAIL C

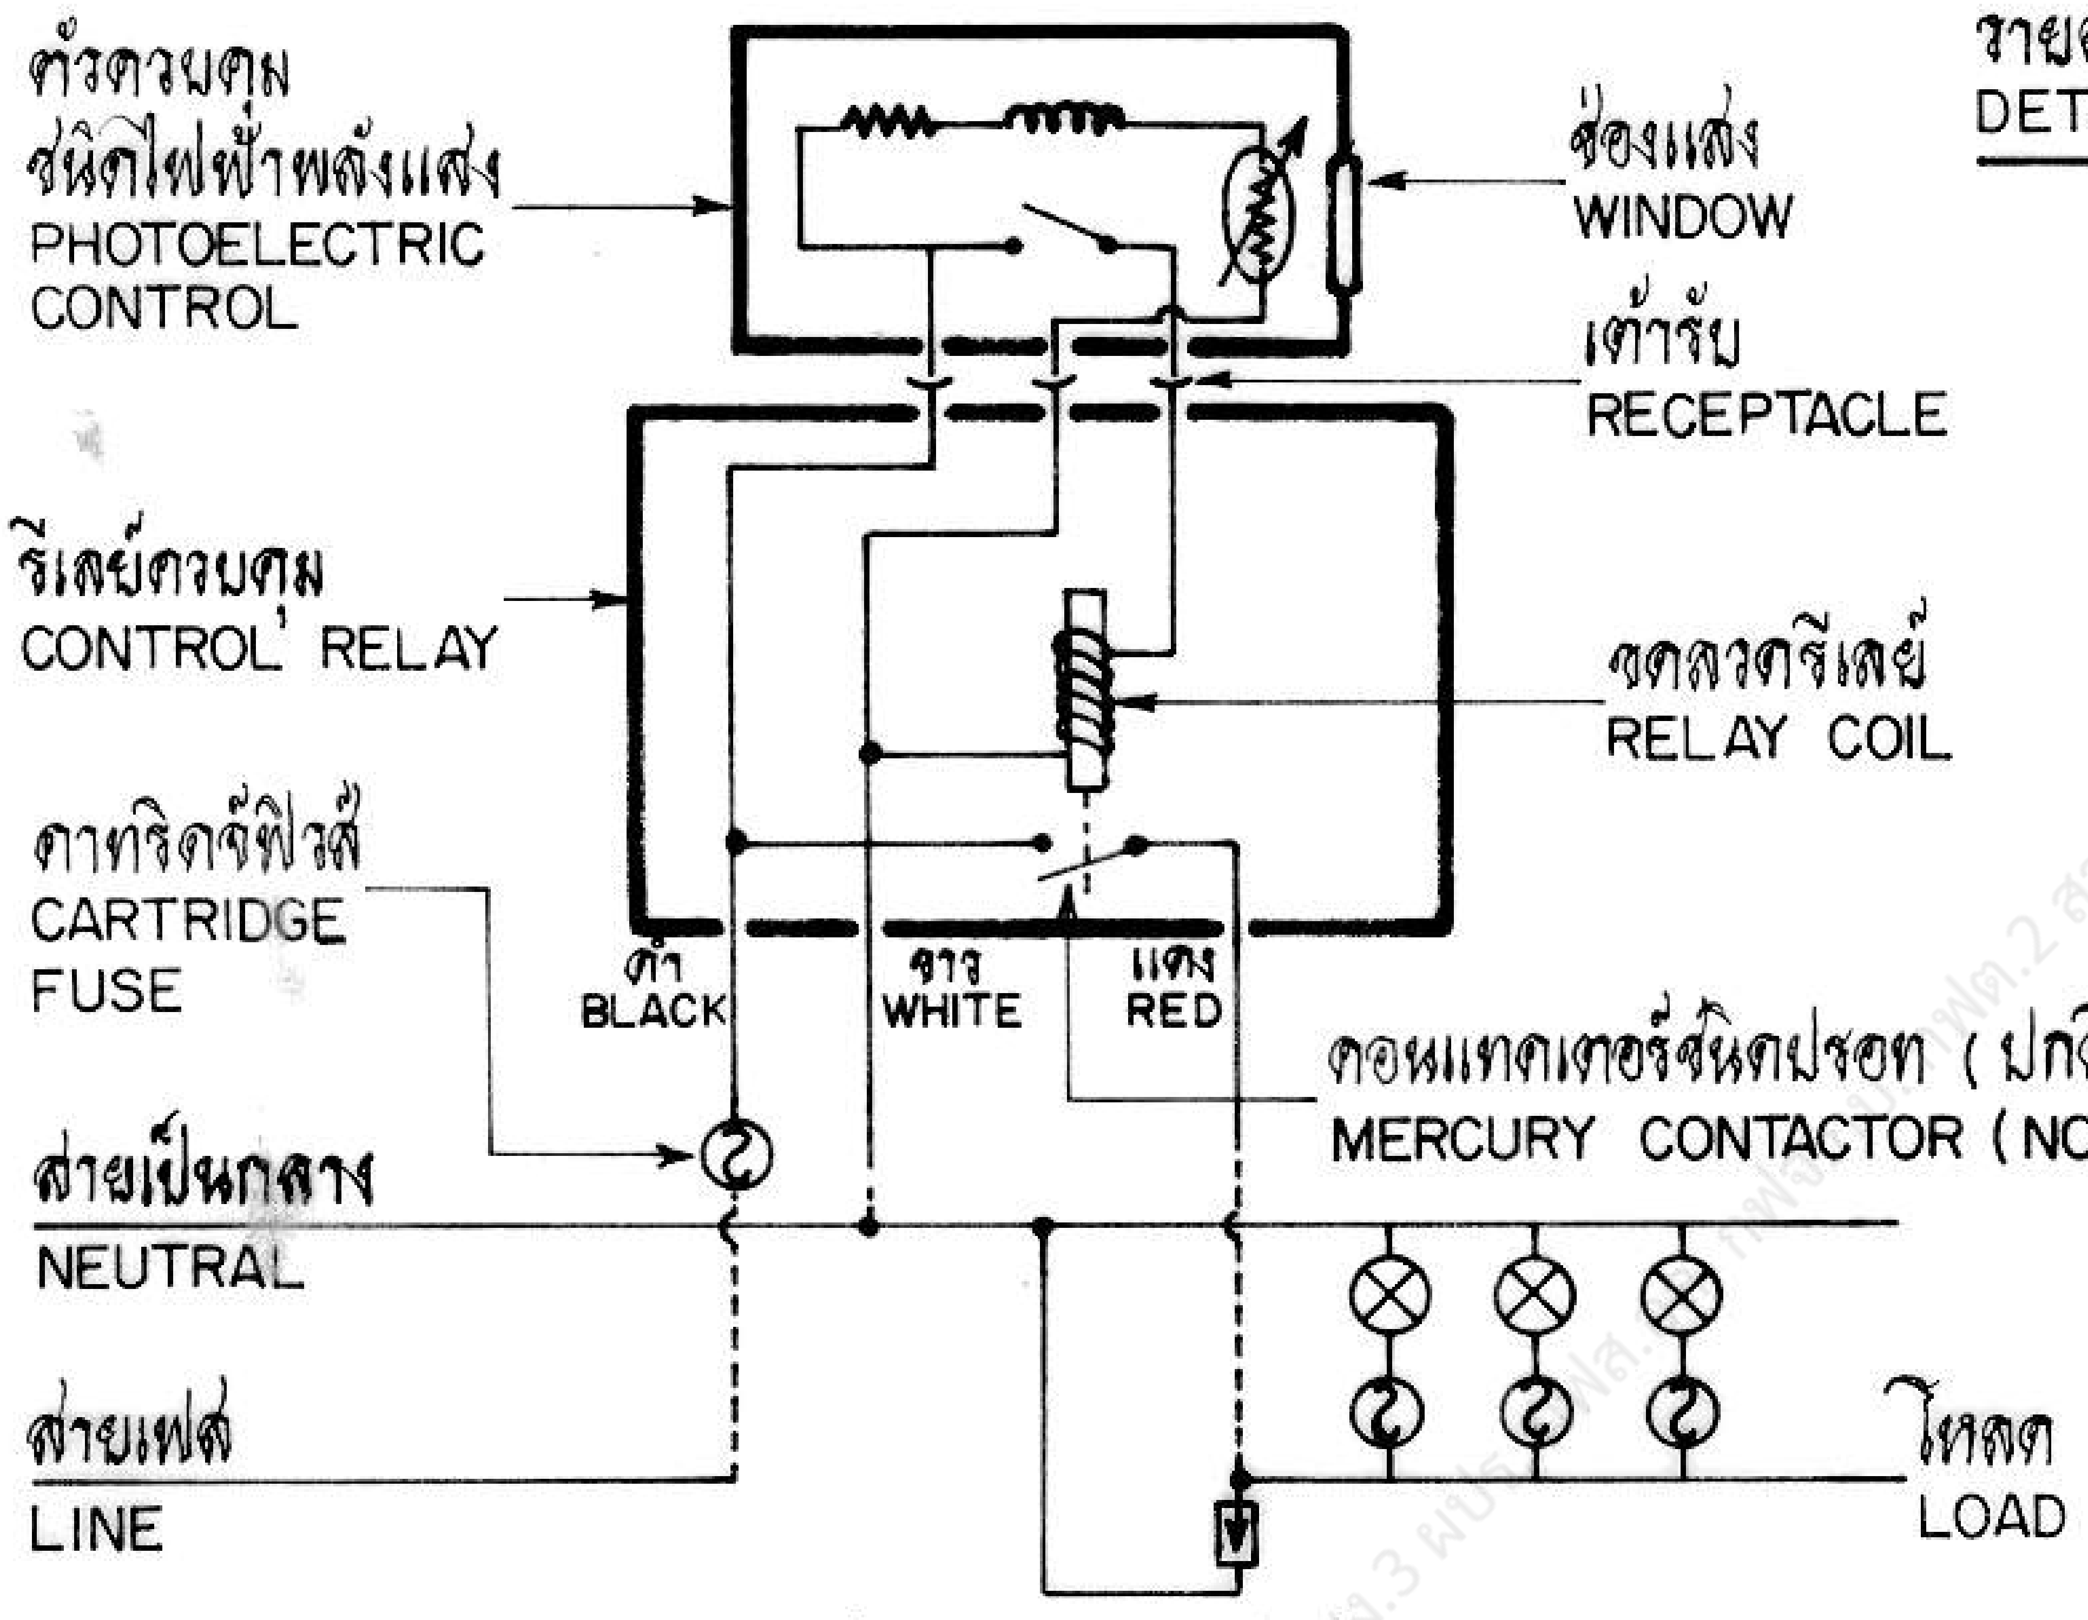

* ไดอะแกรมการต่อสาย
WIRING DIAGRAM

ข้อแนะนำการติดตั้งตัวควบคุมชนิดไฟฟ้าพลังแสง

การติดตั้งชุดสวิตช์ควบคุมชนิดพลังแสง ให้พยายามหันช่องแสงไปทางทิศเหนือให้มากที่สุด และหลีกเลี่ยงไม่ให้มีสิ่งกีดขวางปิดหน้าช่องแสง อันจะทำให้การทำงานควบคุมการ ปิด-เปิด วงจรไฟถนน เกิดคลาดเคลื่อนไป

* ไดอะแกรมที่แสดงการต่อสายในแบบนี้ ชุดควบคุมแบบสวิตช์ควบคุมชนิดพลังแสงประกอบด้วย

1. รีเลย์ควบคุม **ผลิตภัณฑ์** H-B
2. **ตัวควบคุมชนิดไฟฟ้าพลังแสง ผลิตภัณฑ์** RIPLEY.

กองวิศวกรรมไฟฟ้า และเครื่องกล ฝ่ายวิศวกรรม	**การไฟฟ้าส่วนภูมิภาค**	ใช้แทนแบบ.......... ถูกแทนโดยแบบ..........
ผู้เขียน.......... ผู้สำรวจ.......... วิศวกร.....ช.ค..... หัวหน้าแผนก.......... ผู้อำนวยการกอง.......... ผู้อำนวยการฝ่าย..........	ผู้ว่าการ.......... -5 เม.ย. 2528 การติดตั้งชุดสวิตช์ควบคุมชนิดพลังแสงสำหรับเปิด-ปิด วงจรไฟถนน	เขียนเสร็จวันที่ 27 มี.ค. 28 แก้แบบวันที่.......... มิติเป็น.......... มาตราส่วน..........
รองผู้ว่าการฝ่ายเทคนิค	PHOTO SWITCH INSTALLATION IN STREET LIGHTING CIRCUIT	แบบเลขที่ SAI-015/28009 แผ่นที่ 4 ของจำนวน 6 แผ่น

-5 เม.ย. 2528

การประกอบเลขที่
ASSEMBLY NO. 0811

บัญชีวัสดุ
BILL OF MATERIAL

ลำดับที่ ITEM	รายละเอียด DESCRIPTION	จำนวน REQ'D ก/A	ข/B	ค/C	วัสดุเลขที่ MAT. NO.
1	สลักเกลียว M 16 X 170 มม. BOLT, MACHINE, M 16 X 170 mm	–	–	2	01110201
2	สลักเกลียว M 16 X 200 มม. BOLT, MACHINE, M 16 X 200 mm	–	–	1	01110202
3	สลักเกลียว M 16 X 250 มม. BOLT, MACHINE, M 16 X 250 mm	3	3	2	01110203
4	สลักเกลียว M 16 X 300 มม. BOLT, MACHINE, M 16 X 300 mm	2	2	–	01110204
5	แหวนสี่เหลี่ยมแบน 52 X 52 X 4.5 มม. รู Ø 18 มม. มอก. 258 WASHER, SQUARE, FLAT, 52 X 52 X 4.5 mm, HOLE Ø 18 mm, TIS 258	8	8	8	01180100
6	แป้นไม้รองมิเตอร์ไสแล้ว ขนาด 60 X 20 X 2 ซม. METER, PLATE (HARD WOOD), SURFACE FINISHED, SIZE 60 X 20 X 2 cm	1	1	1	
7	แป้นไม้สำหรับยึดสายเข้า และออกจากมิเตอร์ไสแล้ว ขนาด 20 X 20 X 2 ซม. CABLE, PLATE (HARD WOOD), SURFACE FINISHED, SIZE 20 X 20 X 2 cm	1	1	1	
8	วัตต์ฮาวร์มิเตอร์ 1 เฟส 2 สาย 220 โวลต์ 20(40) แอมป์ ใช้ภายนอก METER, WATTHOUR, SINGLE-PHASE, 2-WIRE, 220 V, 20 (40) A, WEATHER PROOF	1	1	1	06000003
9	ชุดควบคุมวงจรไฟถนนแบบสวิตช์ควบคุมชนิดพลังแสง วงจรเดี่ยว สำหรับระบบ 220 โวลต์ ขนาด 30 แอมป์ (แบบใช้ภายนอก) ประกอบด้วย STREET LIGHTING CONTROL SET, PHOTO SWITCH TYPE, SINGLE CIRCUIT, FOR 220 V, 30 A (OUTDOOR TYPE), CONSIST OF – ตัวควบคุมชนิดไฟฟ้าพลังแสง (1 อัน วัสดุเลขที่ 07030205) PHOTOELECTRIC CONTROL – รีเลย์ควบคุมใช้คอนแทคเตอร์ปรอท 1 เฟส 220 โวลต์ โหลด 30 แอมป์ (1 อัน วัสดุเลขที่ 07030206) CONTROL RELAY, MERCURY CONTACTOR, 1-Ø, 220V, LOAD RATING 30 A – ฐานฟิวส์ สำหรับ ดี-คาทริดจ์ฟิวส์ 500 โวลต์ 63 แอมป์ (1 อัน วัสดุเลขที่ 07030001) FUSE, FITTING FOR D-CARTRIDGE, 500 V, 63 A – ดี-คาทริดจ์ฟิวส์ ขนาด 500 โวลต์ 35 แอมป์ (1 อัน วัสดุเลขที่ 07030002) D-CARTRIDGE FUSE, 500 V, 35 A	1 ชุด set	1 ชุด set	1 ชุด set	
10	สายอะลูมิเนียมหุ้มฉนวน PVC 750 โวลต์ 75°C 25 ต.มม. มอก. 293 CABLE, Al PVC INSULATED, 750 V, 75°C, 25 mm² TIS 293	20 ม. m	20 ม. m	20 ม. m	02070000
11	ตะปูเกลียวชุบโครเมียม ขนาด 15-20 ต.มม. SCREW, CHROME PLATED, SIZE 15-20 mm	3	3	3	
12	ตะปูหัวกลมแบนยาว 15-20 มม. Ø 1.00 มม. มอก. 113 NAIL, ROUND, MILD STEEL WIRE 15-20 mm LONG Ø 1.00 mm TIS 113	9	9	9	
13	เข็มขัดรัดสาย (ทำด้วยลวดอะลูมิเนียมแบน 1 X 10 มม.) CABLE STRAP (MADE OF ARMOUR TAPE 1 X 10 mm)				
14	หมายเลขผู้ใช้ไฟ (ทำด้วยแผ่นอะลูมิเนียม 15 X 100 มม. หนา 0.5 มม.) NUMBER OF CUSTOMER (MADE OF ALUMINIUM PLATE 15 X 100 mm, 0.5 mm THICKNESS)	1	1	1	
15	คอนเนคเตอร์ชนิดบีบ แบบ H สำหรับสายอะลูมิเนียม ขนาดตามต้องการ CONNECTOR, COMPRESSIONS, H-TYPE, FOR Al CONDUCTOR, SIZE AS REQUIRED	5	5	5	02320003 - 02320002

กองวิศวกรรมไฟฟ้าและเครื่องกล
ฝ่ายวิศวกรรม

การไฟฟ้าส่วนภูมิภาค

ผู้เขียน
ผู้สำรวจ
วิศวกร
หัวหน้าแผนก
ผู้อำนวยการกอง
ผู้อำนวยการฝ่าย

ผู้ว่าการ

5 เม.ย. 2528

การติดตั้งชุดสวิตช์ควบคุมชนิดพลังแสงสำหรับเปิด-ปิด วงจรไฟถนน

รองผู้ว่าการฝ่ายเทคนิค

PHOTO SWITCH INSTALLATION IN STREET LIGHTING CIRCUIT

ใช้แทนแบบ
ถูกแทนโดยแบบ
เขียนเสร็จวันที่ 27 มี.ค. 28
แก้แบบวันที่
มิติเป็น
มาตราส่วน
แบบเลขที่ SAI-015/28009
แผ่นที่ 5 ของจำนวน 6 แผ่น

5 เม.ย. 2528

การประกอบเลขที่ ASSEMBLY NO. 0811

บัญชีวัสดุ
BILL OF MATERIAL

ลำดับที่ ITEM	รายละเอียด DESCRIPTION	จำนวน REQ'D			วัสดุเลขที่ MAT. NO.
		ก/A	ข/B	ค/C	
16	PVC เทป กว้าง 19 มม. (ใช้ความยาว 2 ม. ต่อ 1 จุด) มอก. 386 PVC TAPE, 19 mm WIDE (2 m LONG PER POINT) TIS 386				02180001 or 02180002
17	ล่อฟ้า 250-500 โวลต์ 2.5-5 กิโลแอมป์ LIGHTNING ARRESTER, 250-500 VOLT, 2.5-5 kA	1	1	1	04000300
18	ลวดเหล็กตีเกลียว 50/7 ต.มม. มอก. 404 WIRE, STEEL STRANDED, 50/7 mm², TIS 404	–	–	20 ม./m	01100004
19	ท่อ PVC แข็ง ขนาด 20 X 4,000 มม. มอก. 216 พร้อมอุปกรณ์ยึด CONDUIT, PVC, RIGID, 20 X 4,000 mm, TIS. 216, COMP. WITH FIXING ACCESSORY	–	–	1	08040002
20	**หลักดิน** 60 X 60 X 5 มม. ยาว 2 ม. ROD, GROUND, 60 X 60 X 5 mm, 2 m LONG	–	–	1	01220002

หมายเหตุ

1. ในกรณีติดตั้งหม้อแปลงเฉพาะเพื่อจ่ายไฟให้กับวงจรไฟถนน **ให้ติดตั้งฟิวส์สวิตช์**แรงต่ำป้องกันวงจรไฟถนนที่เสาต้นหม้อแปลง (ดังรายละเอียด รูป ก)
2. สำหรับระบบจำหน่ายที่มีระบบไฟถนนติดตั้งอยู่สมบูรณ์แล้ว ต่อมามีการติดตั้งหม้อแปลงเสริมเพิ่มในสายระบบจำหน่ายช่วงดังกล่าว ให้คงระบบไฟถนนของเดิมไว้ โดยไม่ต้องติดตั้งชุดควบคุมวงจรไฟถนนเพิ่มใหม่**ที่หม้อแปลงเสริมและให้ต่อใช้สายเป็นกลางแรงต่ำของหม้อแปลงทั้งสองเครื่องร่วมกัน** (ดังรายละเอียด รูป ข)
3. **จำนวนดวงโคม และขนาดฟิวส์** ใช้ขนาดเดียวกับของสวิตช์เวลาที่กำหนดไว้ในแบบเลขที่ SAI-015/23039 (การประกอบเลขที่ 0807)

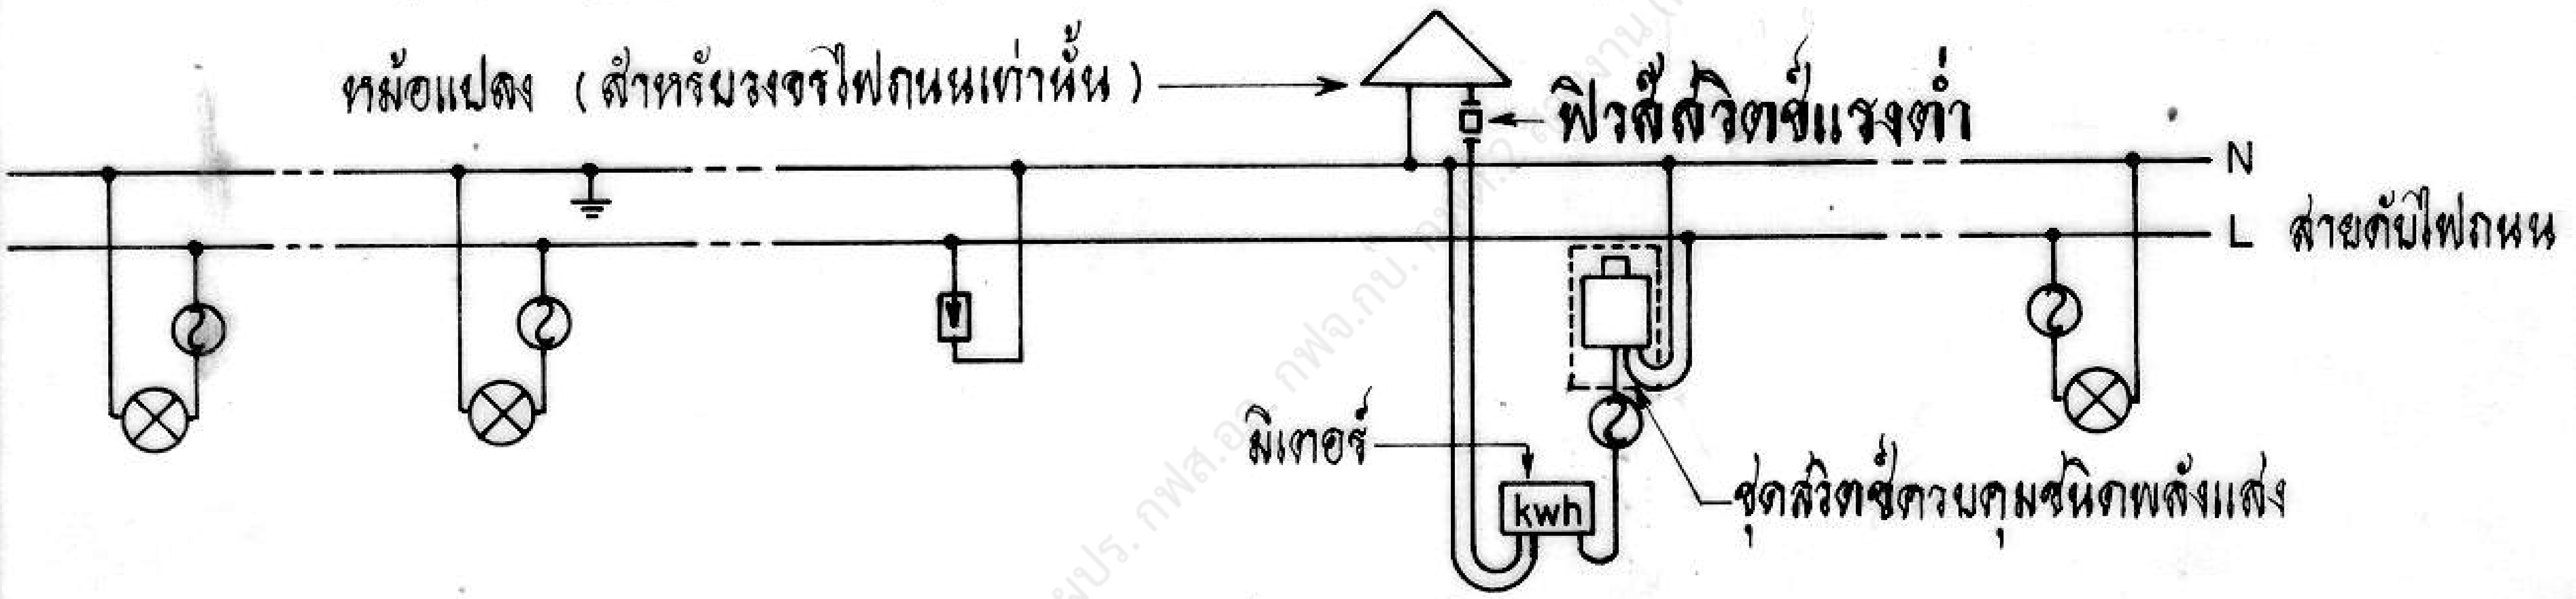
หม้อแปลง (สำหรับวงจรไฟถนนเท่านั้น)
ฟิวส์สวิตช์แรงต่ำ
N
L สายดับไฟถนน
มิเตอร์
kwh
ชุดสวิตช์ควบคุมชนิดพลังแสง

รูป ก

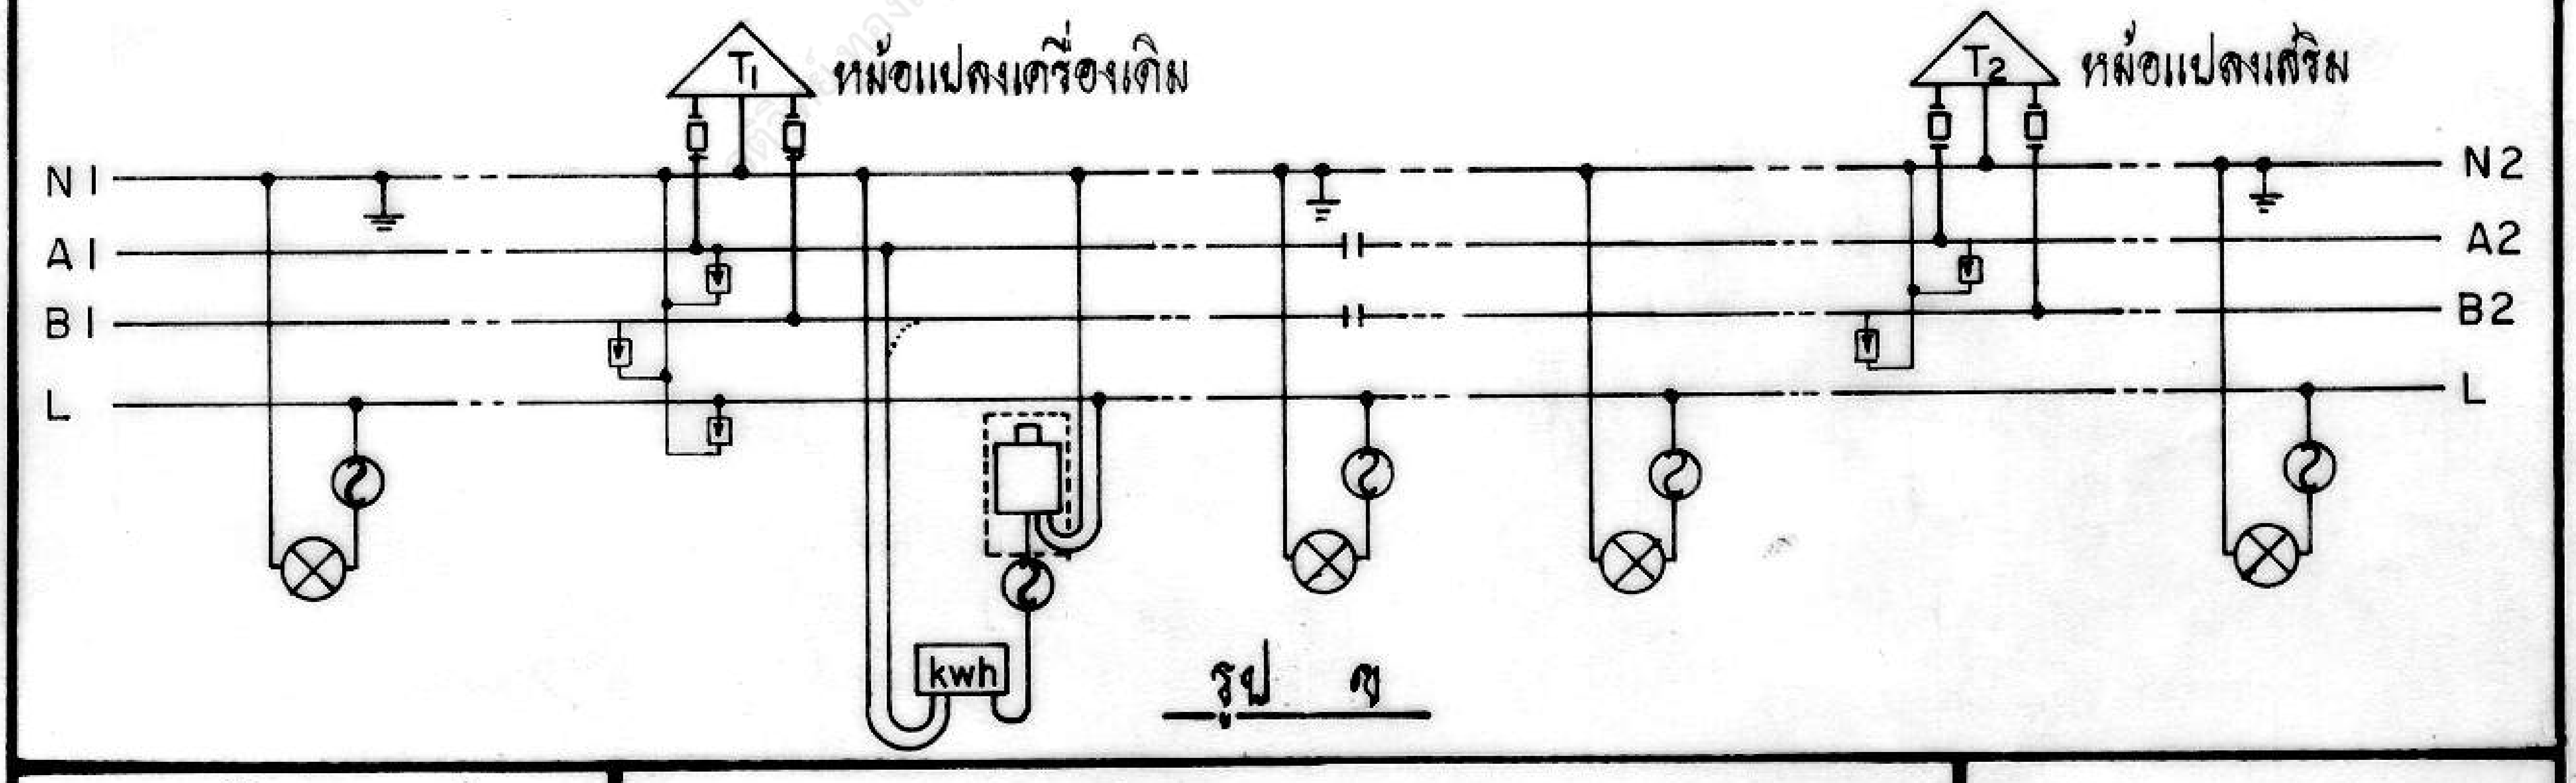

รูป ข

กองวิศวกรรมไฟฟ้าและเครื่องกล ฝ่ายวิศวกรรม	**การไฟฟ้าส่วนภูมิภาค**	ใช้แทนแบบ..........
ผู้เขียน.......... ผู้สำรวจ.......... วิศวกร.......... หัวหน้าแผนก.......... ผู้อำนวยการกอง.......... ผู้อำนวยการฝ่าย..........	ผู้ว่าการ..........	ถูกแทนโดยแบบ.......... เขียนเสร็จวันที่ 27 มี.ค. 28 แก้แบบวันที่.......... ลิขิตเป็น.......... มาตราส่วน..........
	– 5 เม.ย. 2528 การติดตั้งชุดสวิตช์ควบคุมชนิดพลังแสงสำหรับเปิด-ปิด วงจรไฟถนน	
รองผู้ว่าการฝ่ายเทคนิค..........	PHOTO SWITCH INSTALLATION IN STREET LIGHTING CIRCUIT	แบบเลขที่ SAI-015/28009 แผ่นที่ 6 ของจำนวน 6 แผ่น

– 5 เม.ย. 2528