การประกอบเลขที่ ASSEMBLY NO.	0103

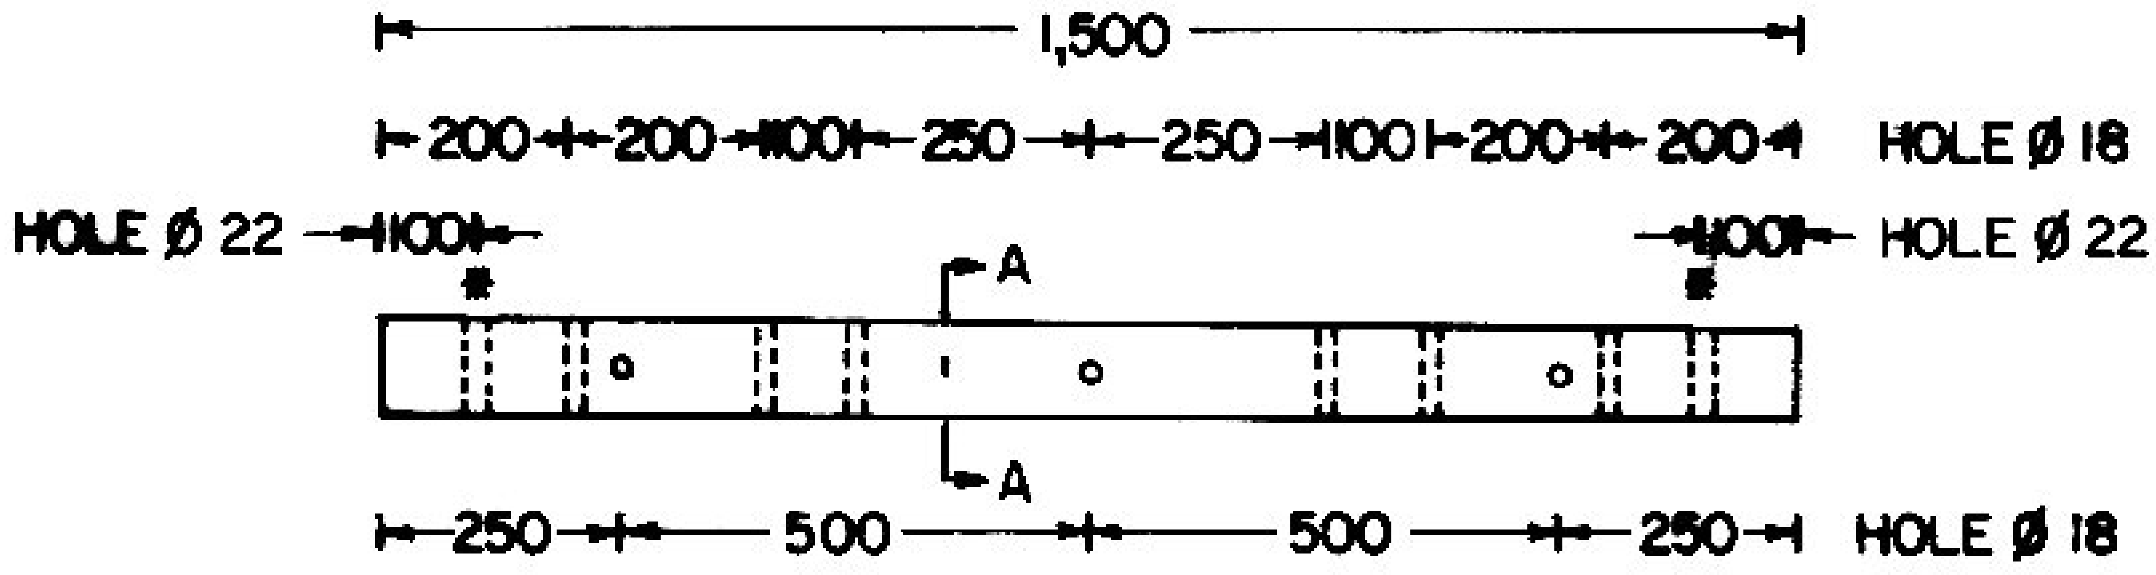
1,500
200
200
100
250
250
100
200
200
HOLE Ø 18
HOLE Ø 22
100
A
A
100
HOLE Ø 22
250
500
500
250
HOLE Ø 18

WORKING MOMENT 225 kg - m SAFETY FACTOR = 3

WEIGHT ≃ 36 kg

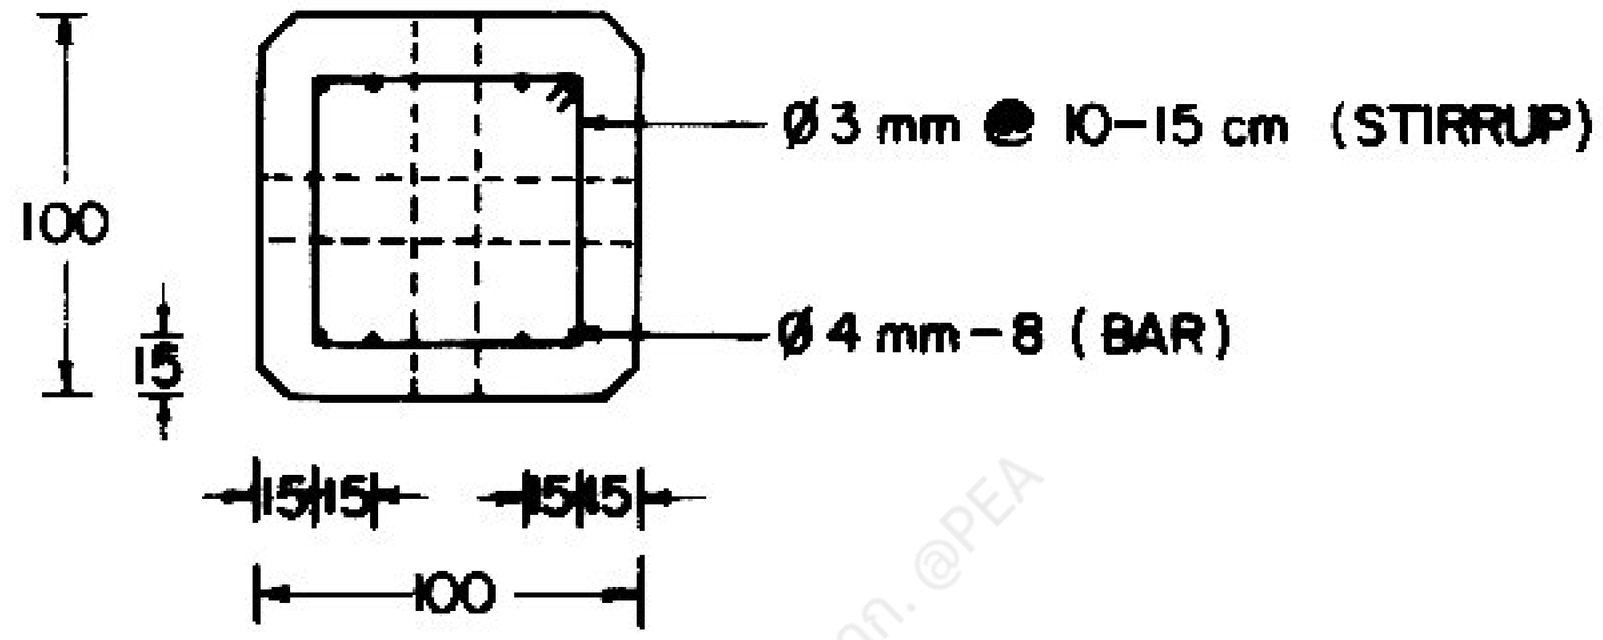
100
15
Ø 3 mm @ 10-15 cm (STIRRUP)
Ø 4 mm - 8 (BAR)
15 15
15 15
100

รูปตัด
SECTION **A-A**

คอน คอนกรีตอัดแรง 100 X 100 X 1,500 มม.

1 ใช้เป็นคอนสำหรับติดตั้งฟิวส์สวิตช์แรงต่ำ รายละเอียดการติดตั้ง ดูแบบเลขที่ SAI-015/22012 (การประกอบเลขที่ 0406)

2 ใช้เป็นคอนสำหรับติดตั้งเคเบิลอากาศ 2 วงจร รายละเอียดการติดตั้ง ดูแบบเลขที่ SAI-015/21036, SAI-015/21041 (การประกอบเลขที่ 2307, 2308) (ใช้คอน คอร. แทนไม้คอน)

3 ใช้เป็นคอนสำหรับติดตั้งลูกถ้วยก้านตรง ระบบ 1 เฟส 19 kV รายละเอียดการติดตั้ง ดูแบบเลขที่ SAI-015/29023 (การประกอบเลขที่ 3308)

PRESTRESSED CONCRETE CROSSARM, 100X100X1,500 mm

1 FOR MOUNTING L.T. FUSE SWITCH. DETAIL OF INSTALLATION SEE DWG. NO. SAI-015/22012

2 FOR 2 CIRCUITS AERIAL CABLE INSTALLATION. DETAIL OF INSTALLATION SEE DWG. NO. SAI-015/21036, SAI-015/21041 (USE PRESTRESSED CONCRETE CROSSARM INSTEAD OF WOOD CROSSARM)

3 FOR 1 PHASE 19 kV SYSTEM, AS CROSSARM OF PIN TYPE INSULATOR DETAIL OF INSTALLATION SEE DWG. NO. SAI-015/29023 (ASSEMBLY NO. 3308)

กองเสาและไม้คอน ฝ่ายก่อสร้าง	การไฟฟ้าส่วนภูมิภาค	ใช้แทนแบบ ถูกแทนโดยแบบ
ผู้เขียน ผู้ตรวจ วิศวกร หัวหน้าแผนก หัวหน้ากอง ผู้อำนวยการฝ่าย	ผู้ว่าการ	เขียนเสร็จวันที่ 8 ก.พ. 22 แก้แบบวันที่ 9 พ.ย. 30
	คอน คอนกรีตอัดแรง 100X100X1,500 มม.	มิติเป็น มม. มาตราส่วน 1:5, 1:20
รองผู้ว่าการฝ่ายเทคนิค	PRESTRESSED CONCRETE CROSSARM, 100X100X1,500 mm	แบบเลขที่ KDO-015/22009 แผ่นที่ 1 ของจำนวน 1 แผ่น