การประกอบเลขที่
ASSEMBLY NO. **3233**

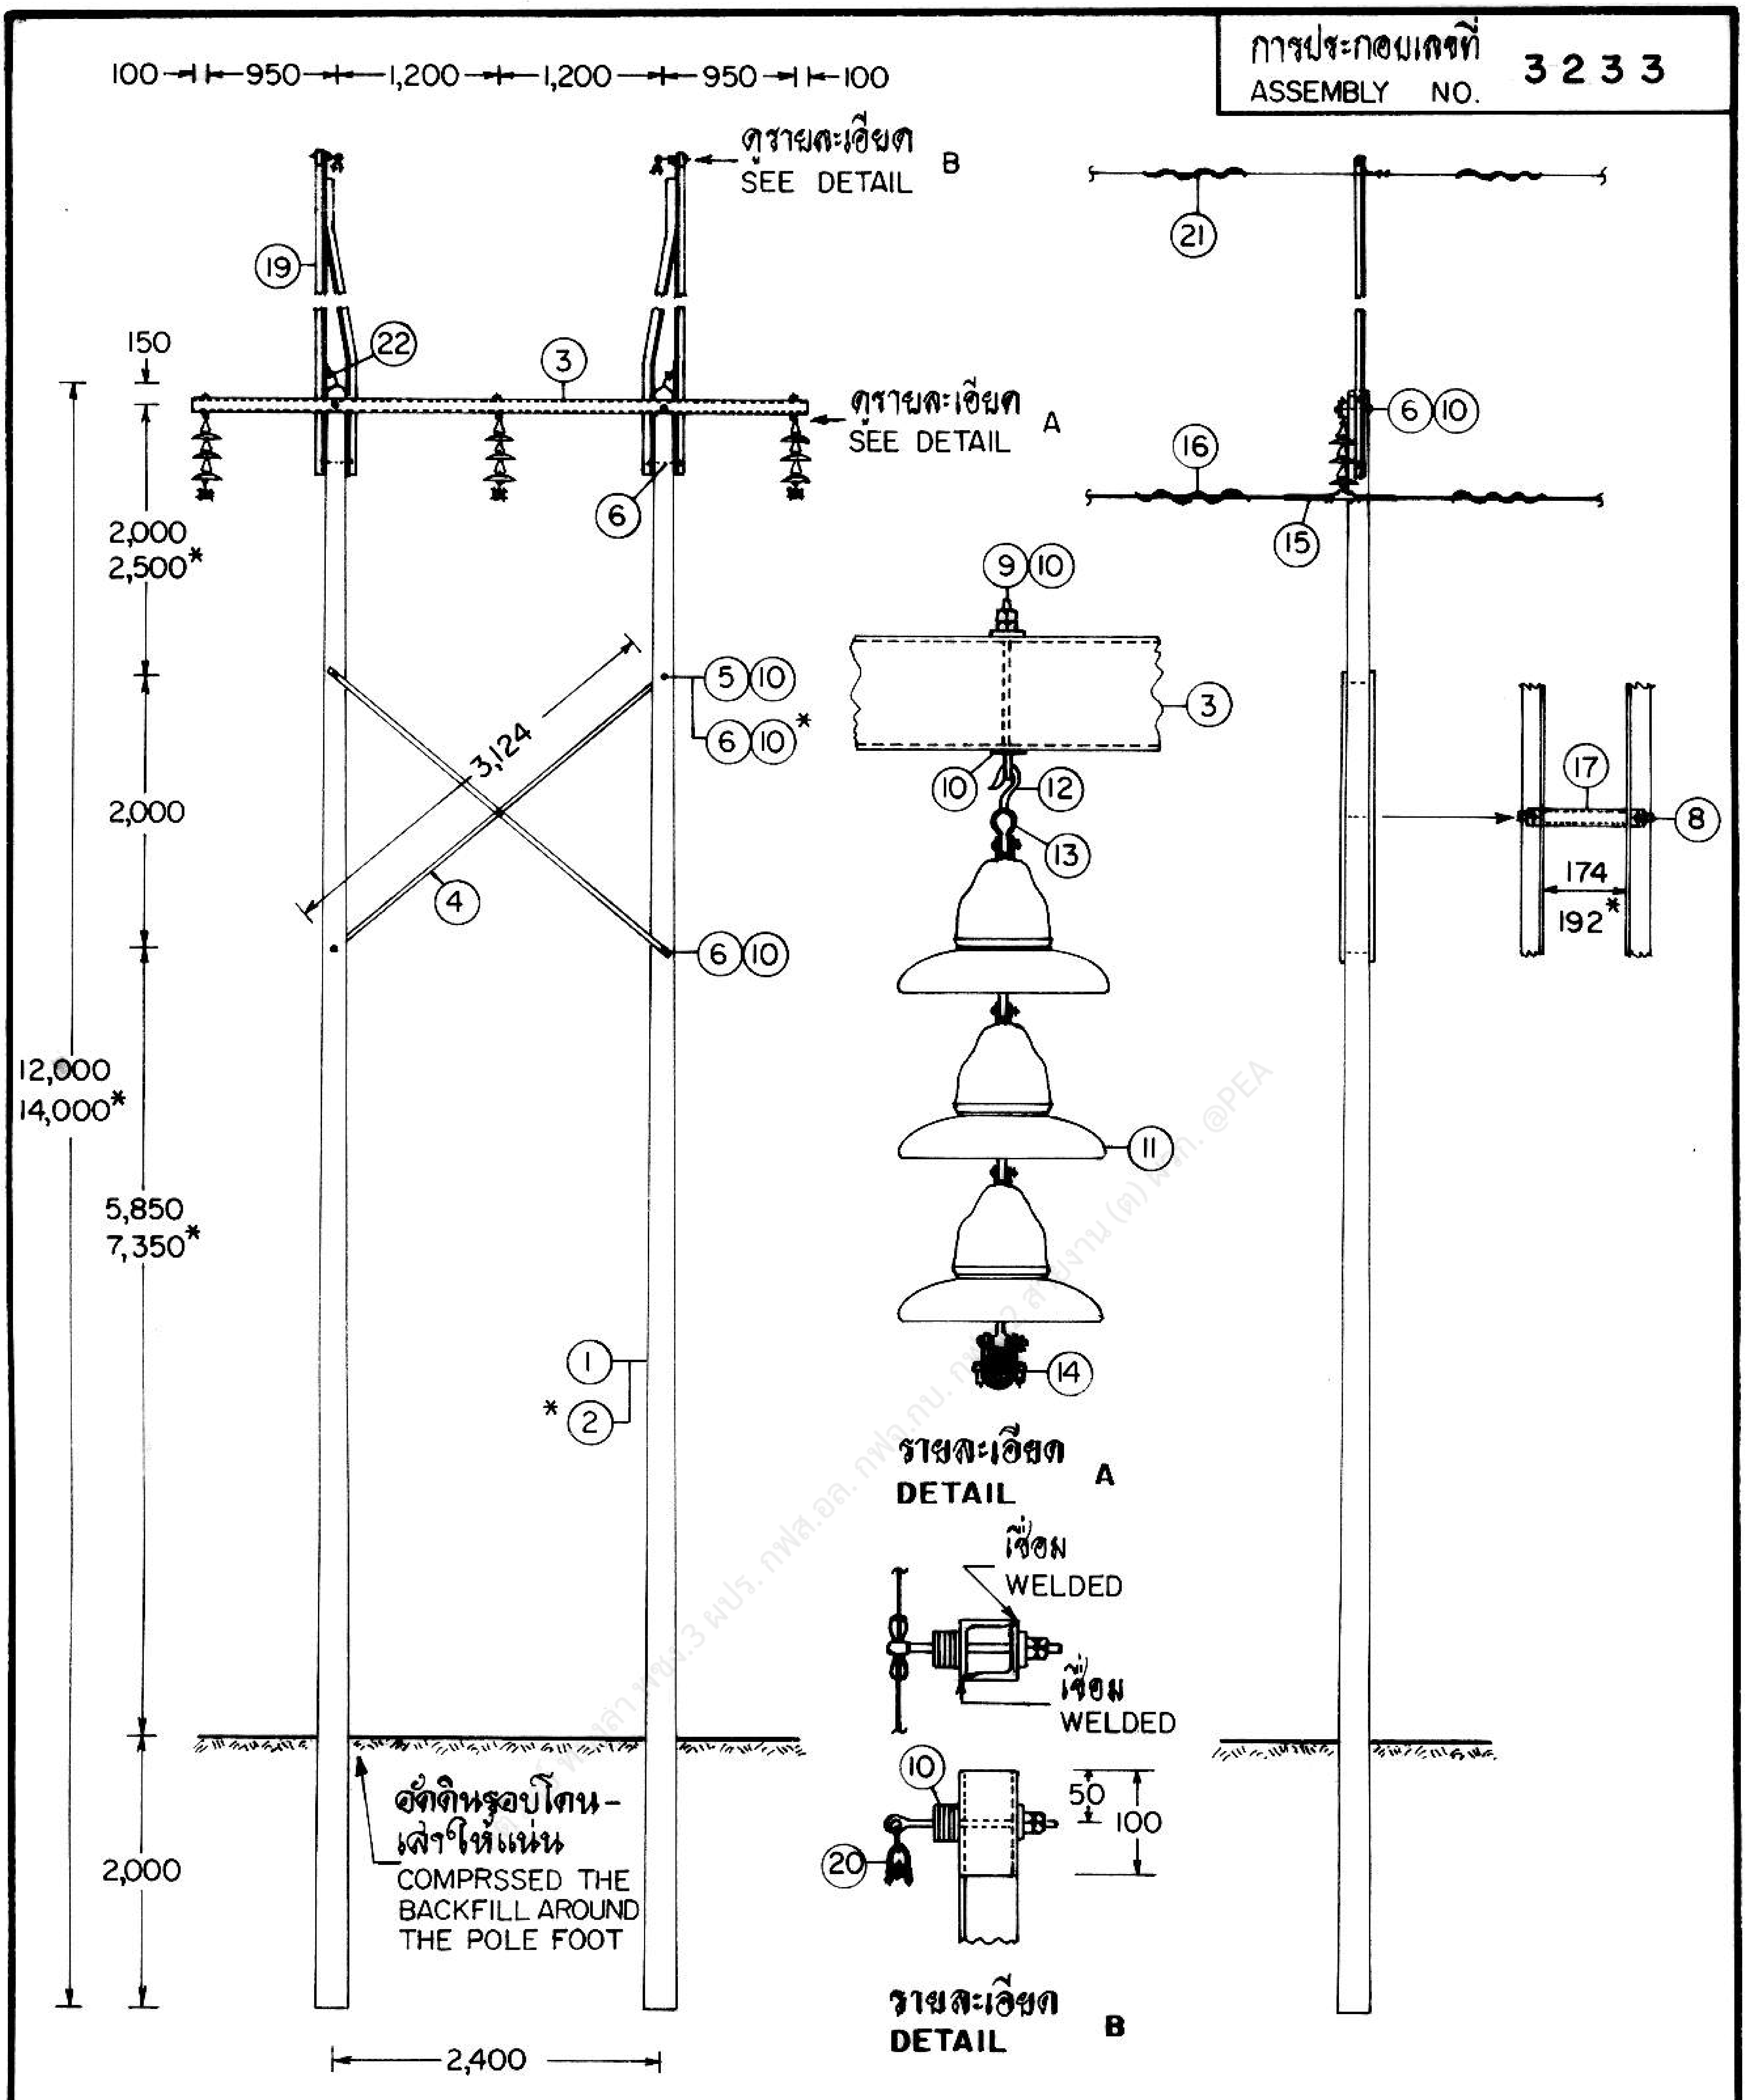

* สำหรับเสา 14 ม.
FOR 14 m POLE

กองวิศวกรรมไฟฟ้าและเครื่องกล
ฝ่ายวิศวกรรม

ผู้เขียน
ผู้สำรวจ
วิศวกร
หัวหน้าแผนก
ผู้อำนวยการกอง
ผู้อำนวยการฝ่าย

รองผู้ว่าการฝ่ายเทคนิค

# การไฟฟ้าส่วนภูมิภาค

ผู้ว่าการ 16 ก.ย. 34

โครงสร้างเสาคู่ สำหรับแขวนสายไฟฟ้า ระบบ 33 kV
ช่วงเสา 120 - 200 ม.
มุม 0°-5°

33 kV, H-FRAME SUSPENSION STRUCTURE
SPAN 120-200 m
LINE ANGLE 0°-5°

ใช้แทนแบบ
ถูกแทนโดยแบบ
เขียนเสร็จวันที่ 19 ส.ค. 34
แก้แบบวันที่
มิติเป็น มิลลิเมตร
มาตราส่วน 1:75

แบบเลขที่ SAI-015/34019
แผ่นที่ 1 จากจำนวน 3 แผ่น

12 ก.ย. 2534

การประกอบเลขที่
ASSEMBLY NO. **3233**

## บัญชีวัสดุ
## BILL OF MATERIAL

| ลำดับที่ ITEM | รายละเอียด DESCRIPTION | จำนวน REQ'D I | จำนวน REQ'D II | วัสดุเลขที่ MAT. NO. |
|---|---|---|---|---|
| 1 | เสาคอนกรีต 12 ม.<br>POLE, CONCRETE, 12 m LONG | 2 | – | 00010003<br>(0033) |
| 2 | เสาคอนกรีต 14 ม.<br>POLE, CONCRETE, 14 m LONG | – | 2 | 00010005<br>(0035) |
| 3 | เหล็กรูปรางน้ำ ขนาด 100 X 50 X 5 มม. ยาว 4.50 ม. ( มอก. 116)<br>STEEL, CHANNEL, 100 X 50 X 5 mm, 4.50 m LONG ( TIS 116) | 1 | 1 | (0198) |
| 4 | เหล็กฉาก ขนาด 75 X 75 X 6 มม. ยาว 3.50 ม. ( มอก. 116 )<br>STEEL, ANGLE, 75 X 75 X 6 mm, 3.50 m LONG ( TIS 116 ) | 2 | 2 | 01010100<br>(0123) |
| 5 | สลักเกลียว M 16 X 200 มม.<br>BOLT, MACHINE, M 16 X 200 mm | 2 | – | 01110202<br>(0222) |
| 6 | สลักเกลียว M 16 X 250 มม.<br>BOLT, MACHINE, M 16 X 250 mm | 8 | 10 | 01110203<br>(0223) |
| 7 | สลักเกลียว M 16 X 300 มม.<br>BOLT, MACHINE, M 16 X 300 mm | – | – | 01110204<br>(0224) |
| 8 | สลักเกลียวตลอด M 16 X 400 มม.<br>BOLT, DOUBLE ARMING, M 16 X 400 mm | 1 | 1 | 01110302<br>(0234) |
| 9 | สลักห่วงโอแวล M 16 X 150 มม.<br>BOLT, OVAL EYE, M 16 X 150 mm | 3 | 3 | 01150000<br>(0257) |
| 10 | แหวนสี่เหลี่ยมแบน 52 X 52 X 4.5 มม. รู Ø 18 มม. มอก. 258<br>WASHER, SQUARE, FLAT, 52 X 52 X 4.5 mm, HOLE Ø 18 mm, TIS 258 | 22 | 22 | 01180100<br>(0355) |
| 11 | ลูกถ้วยแขวน มอก. 354 แบบ ง ( แบบ 52-4 )<br>INSULATOR, SUSPENSION TYPE, TIS 354, TYPE D ( CLASS 52-4 ) | 9 | 9 | 03020002<br>(0415) |
| 12 | ข้อต่อแขวนแบบหัวกลม ANSI แบบ B<br>BALL-HOOK, ANSI, TYPE B | 3 | 3 | 03140002<br>(0483) |
| 13 | ข้อต่อแบบ ซ็อคเก็ต-อาย ANSI แบบ B<br>SOCKET-EYE, ANSI, TYPE B | 3 | 3 | 03140003<br>(0484) |
| 14 | ซัซเพนชั่นแคล้มป์ แบบ เคลวิส ขนาดตามต้องการ<br>CLAMP, SUSPENSION, CLEVIS TYPE; SIZE AS REQUIRED | 3 | 3 | 03120101<br>(0293) |
| 15 | ปรีฟอร์มอาร์เมอร์ร็อด<br>ARMOR ROD, PREFORMED | 3 | 3 | 02220104 –<br>02220107 |
| 16 | ไวเบรชั่นแดมเปอร์ แบบสไปแรล สำหรับสายอะลูมิเนียมเปลือย สายอะลูมิเนียมแกนเหล็ก และสายอะลูมิเนียมเจือ<br>VIBRATION DAMPER, SPIRAL, FOR Al, ACSR, AND ALUMINIUM ALLOY CONDUCTOR | 6 | 6 | 02200101 –<br>02200103 |
| 17 | ท่อเหล็ก ช่องขนาด 20 มม. หนา 2.65 มม. ความยาวตามต้องการ<br>PIPE, IRON, DIA. 20 mm I.D., 2.65 mm THICKNESS ; LENGTH AS REQUIRED | 1 | 1 | — |
| 18 | คอนกรีต 1 : 3 : 5<br>CONCRETE 1 : 3 : 5 | 2.5 ม.$^3$<br>m$^3$ | 2.5 ม.$^3$<br>m$^3$ | — |
| 19 | เหล็กฉากรับสายล่อฟ้าทางโค้ง ขนาด 65 X 65 X 6 มม.<br>OVERHEAD GROUND WIRE CORNER BAYONET, ANGLE STEEL, 65 X 65 X 6 mm | 2 | 2 | 01010007 or<br>01010002 |
| 20 | กราวด์วายร์แคล้มป์ สำหรับคอนไม้<br>GROUND WIRE SUPPORT AND CLAMP, FOR WOOD BAYONET | 2 | 2 | 01130001<br>(0247) |
| 21 | ไวเบรชั่นแดมเปอร์ แบบสไปแรล สำหรับลวดเหล็กตีเกลียว 25 ต.มม.<br>VIBRATION DAMPER, SPIRAL, FOR 25 mm$^2$ STEEL STRANDED WIRE | 4 | 4 | 02200100<br>(0903) |
| 22 | ยูแคล้มป์ สลัก 1 ตัว M 8<br>CLAMP, SINGLE U-BOLT, M 8 | 8 | 8 | 01230000<br>(0165) |

กองวิศวกรรมไฟฟ้าและเครื่องกล
ฝ่ายวิศวกรรม

ผู้เขียน
ผู้สำรวจ
วิศวกร สมพร
หัวหน้าแผนก
ผู้อำนวยการกอง
ผู้อำนวยการฝ่าย

รองผู้ว่าการฝ่ายเทคนิค

# การไฟฟ้าส่วนภูมิภาค

ผู้ว่าการ 16 ก.ย. 34

โครงสร้างเสาคู่ สำหรับแขวนสายไฟฟ้า ระบบ 33 kV
ช่วงเสา 120 – 200 ม.
มุม 0° – 5°

33 kV, H-FRAME SUSPENSION STRUCTURE
SPAN 120 – 200 m
LINE ANGLE 0° – 5°

ใช้แทนแบบ
ถูกแทนโดยแบบ
เขียนเสร็จวันที่ 19 ส.ค. 34
แก้แบบวันที่
มิติเป็น
มาตราส่วน

แบบเลขที่ SAI-015/34019
แผ่นที่ 2 ของจำนวน 3 แผ่น

12 ก.ย. 2534

การประกอบเลขที่
ASSEMBLY NO. **3233**

## ข้อกำหนด

**REGULATIONS**

| ชนิดและขนาดของสายไฟฟ้า ต.มม. TYPE AND SIZE OF CONDUCTOR $mm^2$ | ระยะระหว่างเสาสูงสุด ม. MAXIMUM SPAN LENGTH m | ระยะหย่อนยานต่ำสุดของสายไฟฟ้าทุกเส้น ม. MINIMUM SAG OF ALL CONDUCTORS m |
|---|---|---|
| ACSR 95/15 | 200 | 3.00 |
| ACSR 120/20 | | 4.00 |
| ACSR 185/30 | | 6.00 |
| AA 95 | | 3.00 |
| AA 120 | | 3.00 |
| AA 185 | | 4.00 |

### หมายเหตุ

1. จำนวนในบัญชีวัสดุ :
   สดมภ์ I สำหรับเสาคอนกรีต 12 ม.
   สดมภ์ II สำหรับเสาคอนกรีต 14 ม.
2. ACSR หมายถึงสายอะลูมิเนียมแกนเหล็ก

   AA หมายถึงสายอะลูมิเนียมเจือ
3. เสาต้นที่ปักอยู่ในบริเวณที่เป็นดินอ่อน ( ดินเหนียว, ดินเลน ) หรือดินแข็งปานกลาง (ดินปนทราย) ให้เทคอนกรีตหุ้มโคนเสา ลึก 2.00 ม. จากระดับผิวดิน ขนาดหน้าตัด 0.80 X 0.80 ม.

### NOTES

1. REQ'D IN BILL OF MATERIAL :
   COLUMN I, FOR 12 m CONCRETE POLE.
   COLUMN II, FOR 14 m CONCRETE POLE.
2. ACSR IS ALUMINIUM CONDUCTOR, STEEL REINFORCED.

   AA IS ALL ALUMINIUM ALLOY CONDUCTOR.
3. THE POLE FOOT SHALL BE COVERED WITH CONCRETE 2.00 m DEPTH, CROSS-SECTION 0.80 X 0.80 m, IF IT IS SET IN POOR SOIL ( MARCHY SOIL, OR CLAY ) OR NORMAL SOIL ( SANDY CLAY ).

อดิวิทย์ ทองลา พชง.3 ผปร. กฟจ. กฟต.2 @PEA

กองวิศวกรรมไฟฟ้าและเครื่องกล
ฝ่ายวิศวกรรม

ผู้เขียน
ผู้สำรวจ
วิศวกร
หัวหน้าแผนก
ผู้อำนวยการกอง
ผู้อำนวยการฝ่าย

รองผู้ว่าการฝ่ายเทคนิค

## การไฟฟ้าส่วนภูมิภาค

ผู้ว่าการ 16 ก.ย. 34

โครงสร้างเสาคู่ สำหรับแขวนสายไฟฟ้า ระบบ 33 kV
ช่วงเสา 120 - 200 ม.
มุม 0° - 5°

33 kV, H-FRAME SUSPENSION STRUCTURE
SPAN 120 - 200 m
LINE ANGLE 0° - 5°

ใช้แทนแผน
ถูกแทนโดยแผน
เขียนเสร็จวันที่ 19 ส.ค. 34
แก้แผนวันที่
มิติเป็น
มาตราส่วน

แผนเลขที่ SAI-015/34019
แผ่นที่ 3 ของจำนวน 3 แผ่น

12 ก.ย. 2534