การประกอบเลขที่
ASSEMBLY NO. **5404**

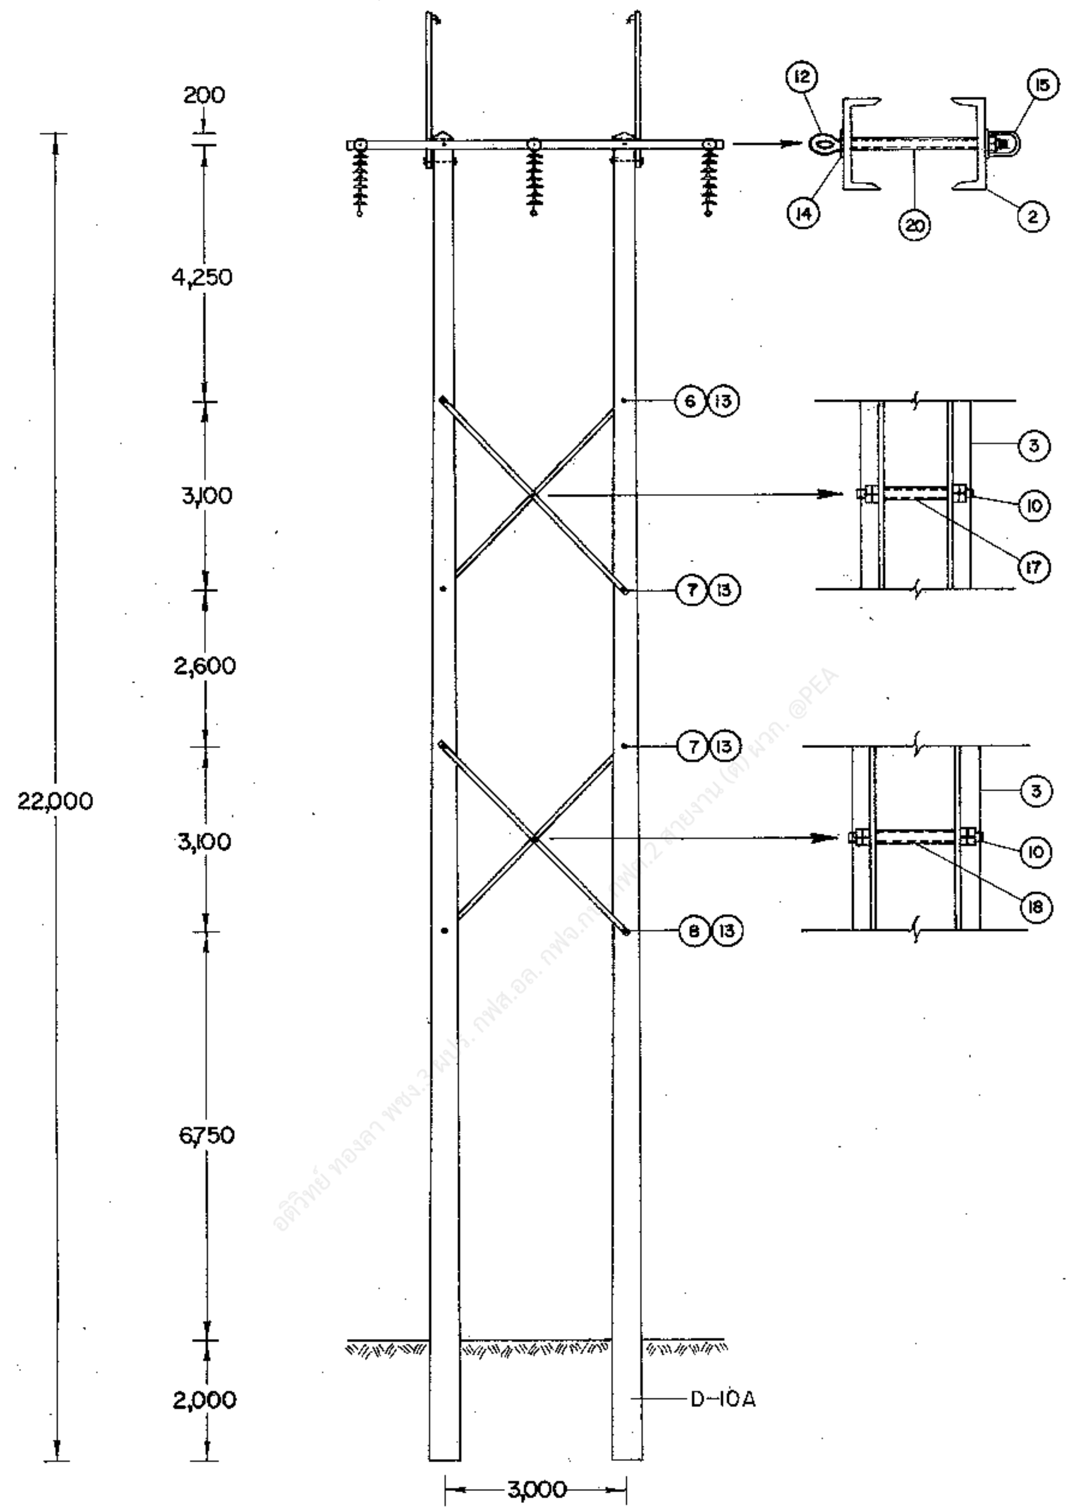

อดิวิทย์ ทองลา พชง.3 ผปฟ. กฟส.อล. กฟน.2 สายงาน (ต) ผวก. @PEA

กองวิศวกรรมไฟฟ้าและเครื่องกล ฝ่ายวิศวกรรม	**การไฟฟ้าส่วนภูมิภาค**	ใช้แทนแบบ.......... ถูกแทนโดยแบบ..........
ผู้เขียน.......... ผู้สำรวจ.......... วิศวกร.......... หัวหน้าแผนก.......... หัวหน้ากอง.......... ผู้อำนวยการฝ่าย..........	ผู้ว่าการ.......... 24 มี.ค. 23 115 kV วงจรเดี่ยว สายไฟฟ้าเดี่ยว เสาคู่แบบ H-FRAME ใช้เสายาว 22 ม. แบบ SS-HF-1	เขียนเสร็จวันที่ 4 ม.ค. 23 แก้แบบวันที่.......... มิติเป็น มม. มาตราส่วน 1 : 125
รองผู้ว่าการฝ่ายเทคนิค	115 kV SINGLE CIRCUIT SINGLE CONDUCTOR H-FRAME STRUCTURE 22 m POLE TYPE SS-HF-1	แบบเลขที่ SAL-015/23022 แผ่นที่ 1 ของจำนวน 4 แผ่น

มี.ค. 2523

การประกอบเลขที่ ASSEMBLY NO. 5404

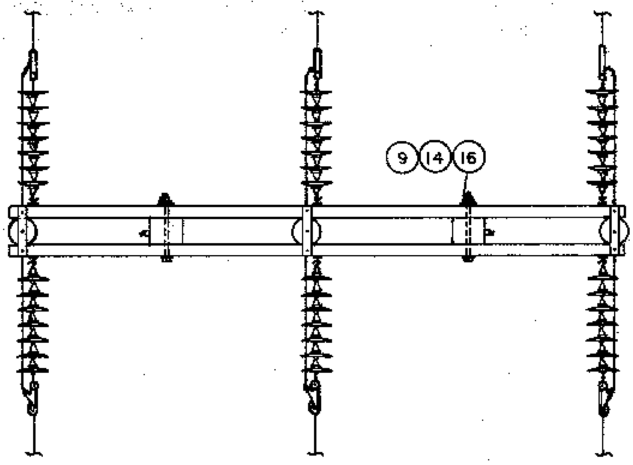

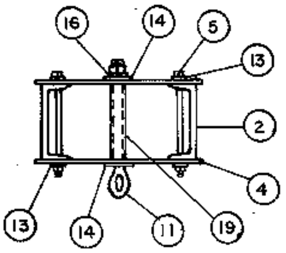

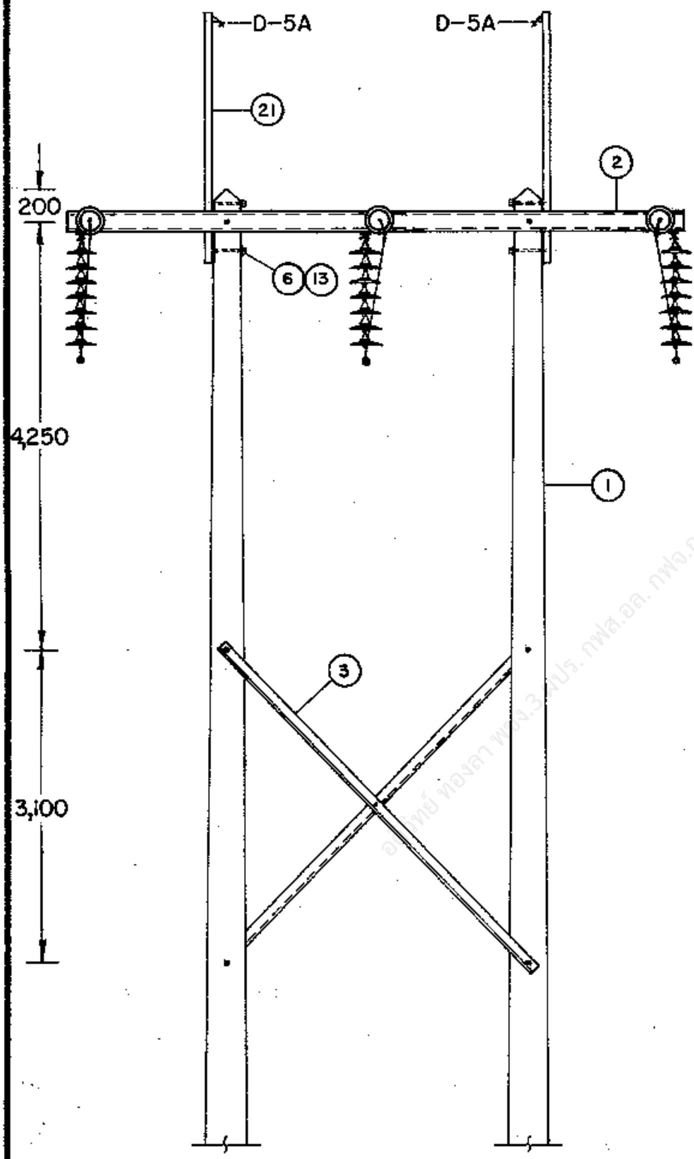

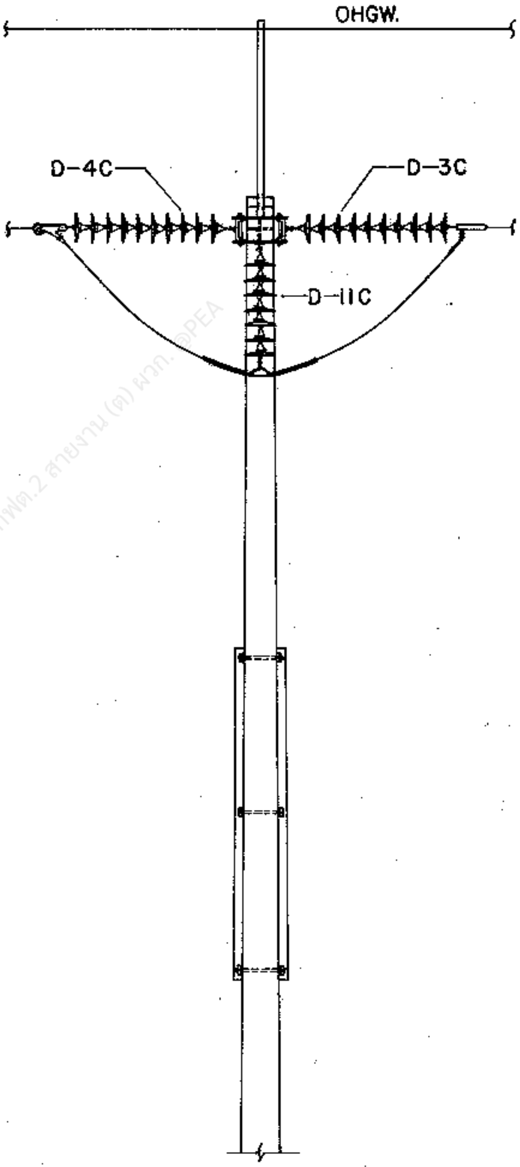

[illegible] ทองลา พคง.3 ผปร. กฟส.อล. กฟจ.กบ. กฟต.2 สายงาน (ต) ผวก. @PEA

กองวิศวกรรมไฟฟ้าและเครื่องกล ฝ่ายวิศวกรรม	การไฟฟ้าส่วนภูมิภาค	ใช้แทนแบบ........ ถูกแทนโดยแบบ........ เขียนเสร็จวันที่ 4 ม.ค. 23 แก้แบบวันที่........ คิดเป็น มม. มาตราส่วน 1 : 75
ผู้เขียน........ ผู้สำรวจ........ วิศวกร........ หัวหน้าแผนก........ หัวหน้ากอง........ ผู้อำนวยการฝ่าย........	ผู้ว่าการ........ 24 มี.ค. 23 115 kV วงจรเดี่ยว สายไฟฟ้าเดี่ยว เสาคู่แบบ H-FRAME ใช้เสาขนาด 22 ม. แบบ SS-HF-1	
รองผู้ว่าการฝ่ายเทคนิค........	115 kV SINGLE CIRCUIT SINGLE CONDUCTOR H-FRAME STRUCTURE 22 m POLE TYPE SS-HF-1	แบบเลขที่ SAI-015/23022 แผ่นที่ 2 ของจำนวน 4 แผ่น

1 ตุ.ค. 2523

การประกอบเลขที่
ASSEMBLY NO. **5404**

บัญชีวัสดุ
BILL OF MATERIAL

ลำดับที่ ITEM	รายละเอียด DESCRIPTION	จำนวน REQ'D	วัสดุเลขที่ MAT. NO.
1	เสาคอนกรีต 22 ม. POLE, CONCRETE 22 m LONG	2	00010011 (0041)
2	เหล็กรูปรางน้ำ ขนาด 200X80X7.5 มม. ยาว 6.00 ม. (ดูรายละเอียด A) STEEL CHANNEL 200X80X7.5 mm, 6.00 m LONG (SEE DETAIL A)	2	01000401 (2676)
3	เหล็กฉาก ขนาด 75X75X6 มม. ยาว 4.50 ม. (ดูรายละเอียด B) STEEL ANGLE 75X75X6 mm, 4.50 m LONG (SEE DETAIL B)	4	01010102 (2678)
4	แผ่นเหล็ก ขนาด 6X100X450 มม. (เจาะรูกึ่งกลางให้เป็นขนาด Ø 22 มม.) PLATE, STEEL 6X100X450 mm (DRILLING THE CENTER HOLE Ø 22 mm)	6	01030002 (0143)
5	สลักเกลียว M 16 X 250 มม. BOLT, MACHINE, M 16 X 250 mm	6	01110203 (0223)
6	สลักเกลียว M 16 X 350 มม. BOLT, MACHINE, M 16 X 350 mm	6	01110205 (0225)
7	สลักเกลียว M 16 X 400 มม. BOLT, MACHINE, M 16 X 400 mm	4	01110206 (0226)
8	สลักเกลียว M 16 X 450 มม. BOLT, MACHINE, M 16 X 450 mm	2	01110207 (0227)
9	สลักเกลียว M 20 X 450 มม. BOLT, MACHINE, M 20 X 450 mm	2	01110302 (0234)
10	สลักเกลียวตลอด M 16 X 400 มม. BOLT, DOUBLE ARMING M 16 X 400 mm	2	01120000 (0243)
11	สลักห่วงโอแวล M 20 X 350 มม. BOLT, OVAL EYE M 20 X 350 mm	3	01150100 (0260)
12	สลักห่วงโอแวล M 20 X 450 มม. BOLT, OVAL EYE M 20 X 450 mm	3	01150101 (0261)
13	แหวนสี่เหลี่ยมแบน 52X52X4.5 มม. รู Ø 18 มม. มอก. 258 WASHER, SQUARE, FLAT 52X52X4.5 mm HOLE Ø 18 mm TIS 258	24	01180100 (0355)
14	แหวนสี่เหลี่ยมแบน **62X62X6** มม. รู Ø 22 มม. **มอก. 258** WASHER, SQUARE, FLAT **62X62X6** mm HOLE Ø 22 mm **TIS 258**	16	01180101 (0356)
15	อายเล็ท สำหรับสลักเกลียว M 20 EYELET FOR BOLT M 20	3	01180002 (0346)
16	แหวนสปริง M 20 **มอก. 259** WASHER, LOCK, M 20, **TIS 259**	5	01180302 (0366)
17	ท่อเหล็ก ชื่อขนาด 20 มม. หนา 2.65 มม. ยาว 300 มม. PIPE, IRON DIA. 20 mm ID, 2.65 mm THICKNESS, 300 mm LONG	1	—
18	ท่อเหล็ก ชื่อขนาด 20 มม. หนา 2.65 มม. ยาว 350 มม. PIPE, IRON DIA. 20 mm ID, 2.65 mm THICKNESS, 350 mm LONG	1	—
19	ท่อเหล็ก ชื่อขนาด 25 มม. หนา 3.25 มม. ยาว 200 มม. PIPE, IRON DIA. 25 mm ID, 3.25 mm THICKNESS, 200 mm LONG	3	—
20	ท่อเหล็ก ชื่อขนาด 25 มม. หนา 3.25 มม. ยาว 300 มม. PIPE, IRON DIA. 25 mm ID, 3.25 mm THICKNESS, 300 mm LONG	3	—
21	เหล็กฉากรับสายล่อฟ้าทางตรง ยาว 2.50 ม. OVERHEAD GROUND WIRE BAYONET 2.50 m LONG	~~1~~ 2	01010004 (0135)

กองวิศวกรรมไฟฟ้าและเครื่องกล
ฝ่ายวิศวกรรม
ผู้เขียน
ผู้สำรวจ
วิศวกร
หัวหน้าแผนก
หัวหน้ากอง
ผู้อำนวยการฝ่าย
รองผู้ว่าการฝ่ายเทคนิค

การไฟฟ้าส่วนภูมิภาค

ผู้ว่าการ .... 24 มี.ค. 23

115 kV วงจรเดี่ยว สายไฟฟ้าเดี่ยว
เสาคู่แบบ H-FRAME ใช้เสาขนาด 22 ม.
แบบ SS-HF-1

115 kV SINGLE CIRCUIT SINGLE CONDUCTOR
H-FRAME STRUCTURE 22 m POLE
TYPE SS-HF-1

ใช้แทนแบบ........
ถูกแทนโดยแบบ........
เขียนเสร็จวันที่ 4 ม.ค. 23
แก้แบบวันที่........
มิติเป็น........
มาตราส่วน........
แบบเลขที่ SAI-015/23022
แผ่นที่ 3 ของจำนวน 4 แผ่น

1 9 มี.ค. 2523

การประกอบเลขที่ ASSEMBLY NO. **5404**

บัญชีวัสดุ
BILL OF MATERIAL

ลำดับที่ ITEM	รายละเอียด DESCRIPTION	จำนวน REQ'D	วัสดุเลขที่ MAT. NO.
D-3C	การประกอบลูกถ้วยแขวน SUSPENSION INSULATOR ASSEMBLY	3	
D-4C	การประกอบลูกถ้วยแขวน SUSPENSION INSULATOR ASSEMBLY	3	
D-11C	การประกอบลูกถ้วยแขวน SUSPENSION INSULATOR ASSEMBLY	3	
D-5A	การต่อสายล่อฟ้า OVER HEAD GROUND WIRE CONNECTION	2	
D-10A	ฐานรากเสา POLE FOUNDATION	2	

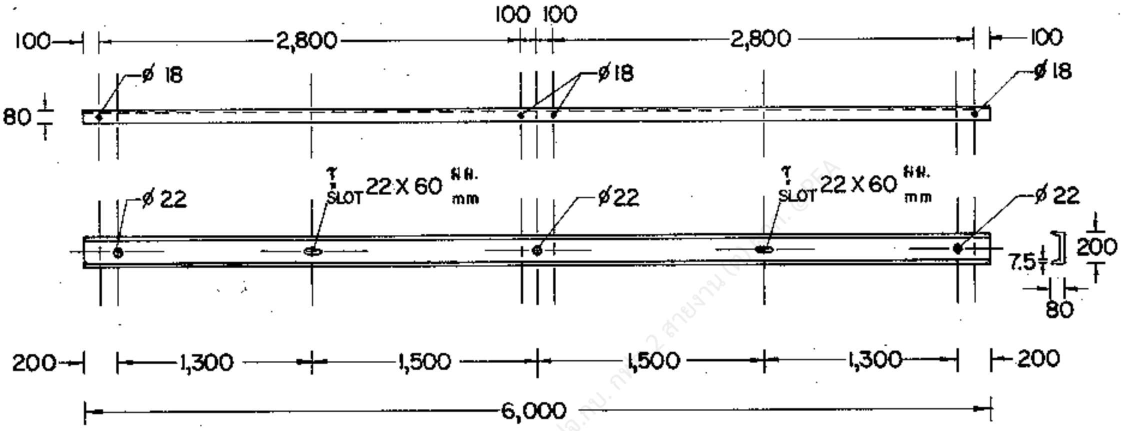

รายละเอียด A
DETAIL

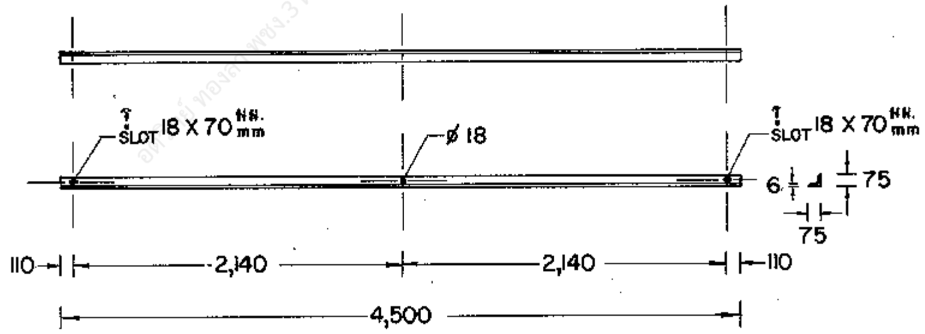

รายละเอียด B
DETAIL

กองวิศวกรรมไฟฟ้าและเครื่องกล ฝ่ายวิศวกรรม	**การไฟฟ้าส่วนภูมิภาค**	ใช้แทนแบบ.......... ถูกแทนโดยแบบ.......... เขียนเสร็จวันที่ 4 ม.ค.23
ผู้เขียน.......... ผู้ตรวจ.......... วิศวกร.......... หัวหน้าแผนก.......... หัวหน้ากอง.......... ผู้อำนวยการฝ่าย..........	ผู้ว่าการ.......... 24 มี.ค. 23 115 kV วงจรเดี่ยว สายไฟฟ้าเดี่ยว เสาคู่แบบ H-FRAME ใช้เสาขนาด 22 ม. แบบ SS-HF-1	แก้แบบวันที่.......... มิติเป็น มม. มาตราส่วน 1 : 50
รองผู้ว่าการฝ่ายเทคนิค	115 kV SINGLE CIRCUIT SINGLE CONDUCTOR H-FRAME STRUCTURE 22 m POLE TYPE SS-HF-1	แบบเลขที่ SAI-015/23022 แผ่นที่ 4 ของจำนวน 4 แผ่น